
DRESSING ROOM — SHELL AND LAYOUT

PLAN · COPIED FROM THE OWNER'S SKETCH — NOT YET A SITE MEASUREMENT

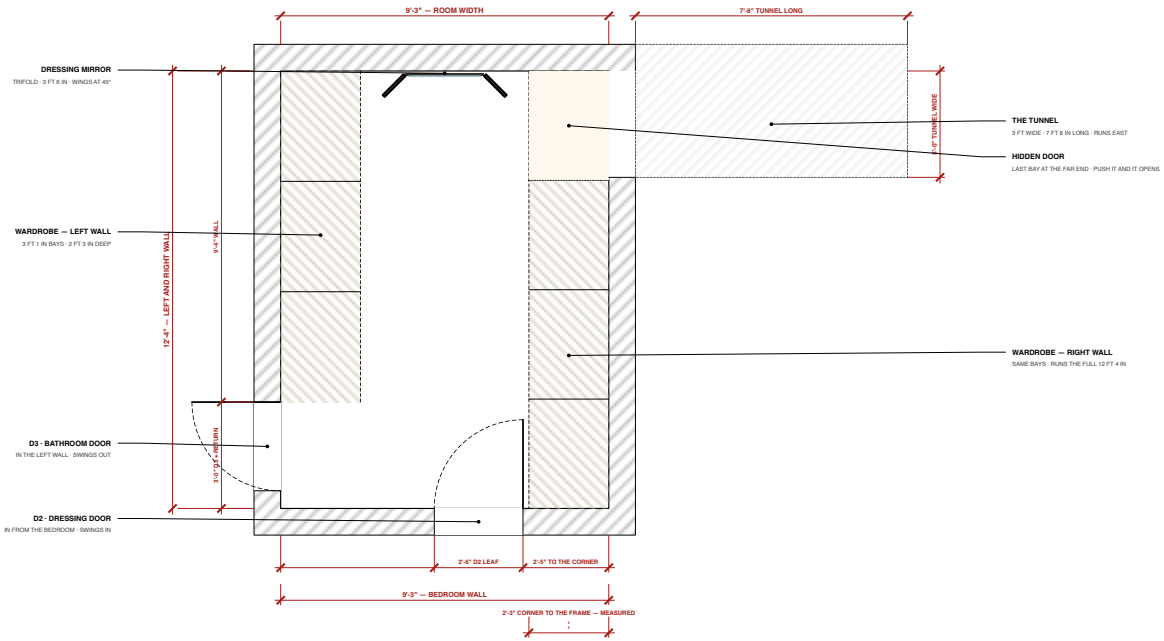

NOTES

REVISION 4

Third pass, and this one copies the sketch rather than interpreting it. The two earlier drawings both had the shape wrong; everything below is read straight off the owner's own clean drawing.

The BEDROOM wall is the bottom wall here, 9 ft 3 in, and it carries D2, the existing dressing door in from the bedroom, 2 ft 3 in from the right-hand corner to the door FRAME — measured 1¼" Sept on both sides of the wall, and the figure that now governs. The sketch's 2 ft 0 in is superseded.

The BATHROOM door, D3, is in the LEFT wall, at the bedroom end — not in the bedroom wall. The sketch runs 9 ft 4 in of wall down from the far corner and then opens the door.

The TUNNEL runs EAST, straight out of the far end of the right wall, 3 ft wide and 7 ft 8 in long, its far side flush with the far wall. The hidden door is the last wardrobe bay in front of it: built and shelved like every other bay, so from the room it reads as one more cupboard.

Ceiling 9 ft 1 in, plain, over the left and right sides — the same height as the main room. A domed centre rises to 10 ft 0 in, so the wardrobes are capped at 9 ft 0 in, clear under it.

SETTLED — D2 sits 2 ft 3 in from the corner to its frame (1¼" Sept), leaf 2 ft 6 in. That closes this sheet against AST-DR-000 and AST-DR-007: this room's right-hand corner and the bedroom's bed-wall corner are the same corner. Walls are taken at 9 in throughout. See AST-DR-024.

OPEN — D3 is 2 ft 6 in frame to frame (2 ft 3 in leaf, 1" Sept), but the sketch's 9 ft 4 in against 12 ft 4 in leaves 3 ft 0 in — so a 6 in return is shown into the corner. To confirm.

OPEN — the wardrobes are 2 ft 3 in deep and D2's frame is now 2 ft 3 in off that corner (1¼" Sept): the right-hand run's face lands flush on the frame, no clearance. Trim the end bay or check on site.

OPEN — the left run is drawn stopping at D3. Whether it ends there or returns over the door is not decided.

OPEN — where the tunnel leads, and what is at its far end.

OPEN — the dome's own shape: how far along the room it runs, and its profile.

The mirror is the confirmed trifold, 3 ft 6 in across with its wings at 45° — see AST-DR-027.

A STUDY IN TEAK

Particulars of the room

DRESSING ROOM

Shell and layout · third pass


SCALE	DATE
1:35 @ A3	16.10.2026
REV	DWG
4 — the dressing door at the owner's 27 Sept tape: 2 ft 3 in leaf, 2 ft 3 in of wall to the corner	AST-DR-023


PROJECT	SHEET	SCALE	DATE	REV	DRAWING
A Study in Teak — Dressing Room	**General arrangement — the whole sheet** each view follows at its own scale, pages 2 to 3	NTS	16.10.2026	4	**AST-DR-023 · 1 of 3**

ALL DIMENSIONS IN FEET & INCHES. PRINT ON A4 AT 100% / "ACTUAL SIZE" — NOT "FIT TO PAGE" — AND CHECK THE SCALE BAR. DO NOT SCALE; WORK TO FIGURED DIMENSIONS. VERIFY ON SITE.

DRESSING ROOM — SHELL AND LAYOUT

SCALE 1:48 (¼" = 1'-0") @ A4 · PLAN · COPIED FROM THE OWNER'S SKETCH — NOT YET A SITE MEASUREMENT

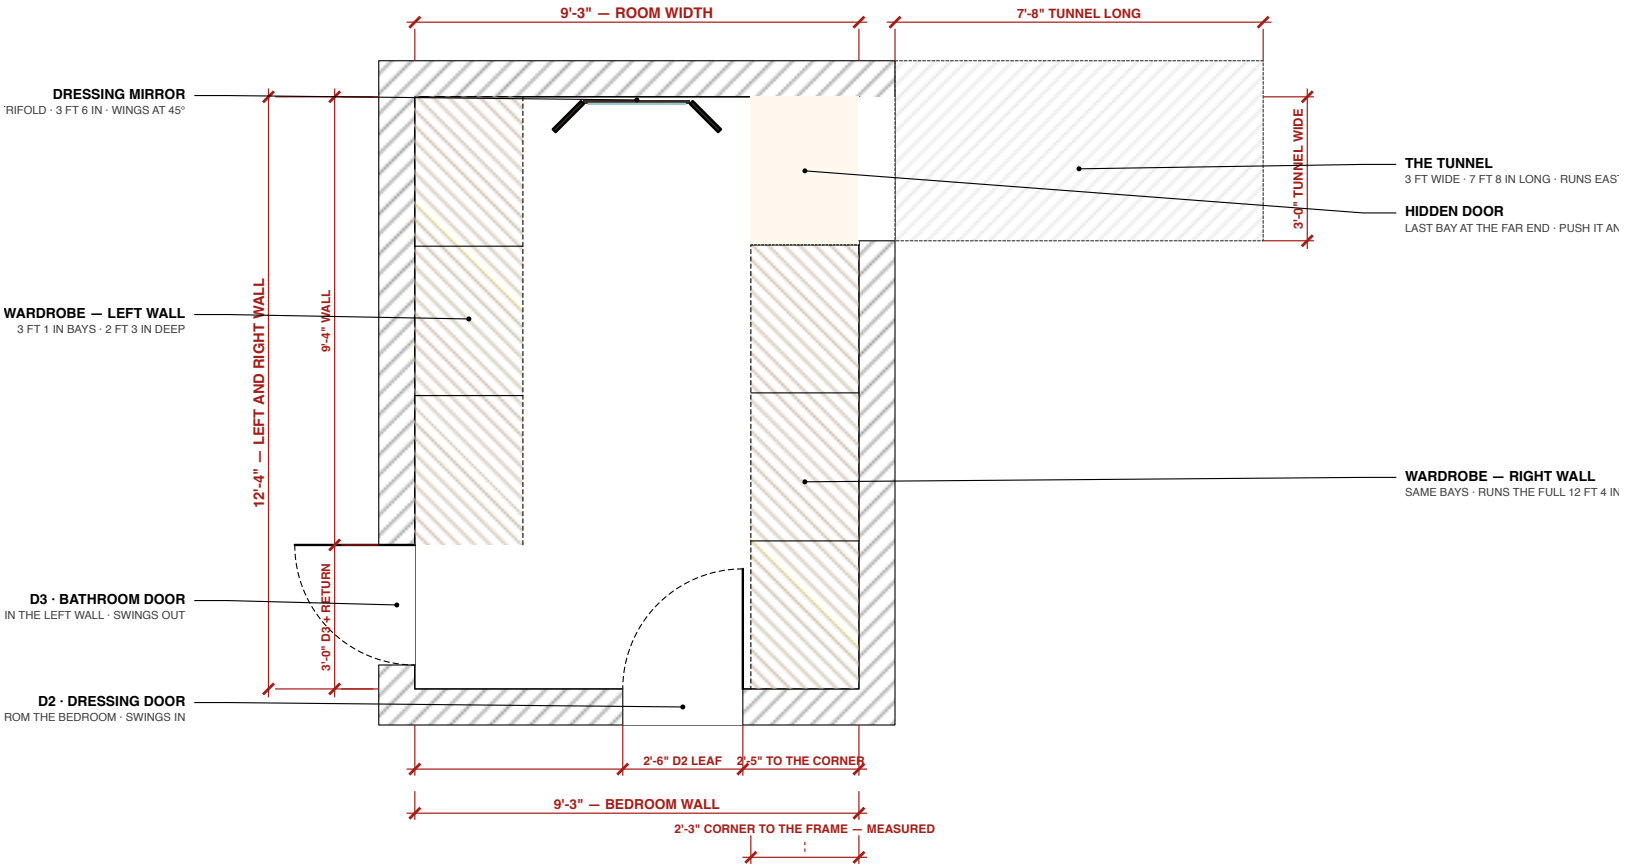

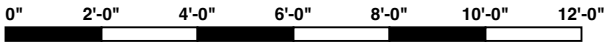

PROJECT	SHEET	SCALE	DATE	REV	DRAWING
A Study in Teak — Dressing Room	**Dressing room — shell and layout** Shell and layout · third pass	1:48 @ A4	16.10.2026	4	**AST-DR-023 · 2 of 3**

ALL DIMENSIONS IN FEET & INCHES. PRINT ON A4 AT 100% / "ACTUAL SIZE" — NOT "FIT TO PAGE" — AND CHECK THE SCALE BAR. DO NOT SCALE; WORK TO FIGURED DIMENSIONS. VERIFY ON SITE.

NOTES

REVISION 4

Third pass, and this one copies the sketch rather than interpreting it. The two earlier drawings both had the shape wrong; everything below is read straight off the owner's own clean drawing.

The BEDROOM wall is the bottom wall here, 9 ft 3 in, and it carries D2, the existing dressing door in from the bedroom, 2 ft 3 in from the right-hand corner to the door FRAME — measured 1⅛" Sept on both sides of the wall, and the figure that now governs. The sketch's 2 ft 0 in is superseded.

The BATHROOM door, D3, is in the LEFT wall, at the bedroom end — not in the bedroom wall. The sketch runs 9 ft 4 in of wall down from the far corner and then opens the door.

The TUNNEL runs EAST, straight out of the far end of the right wall, 3 ft wide and 7 ft 8 in long, its far side flush with the far wall. The hidden door is the last wardrobe bay in front of it: built and shelved like every other bay, so from the room it reads as one more cupboard.

Ceiling 9 ft 1 in, plain, over the left and right sides — the same height as the main room. A domed centre rises to 10 ft 0 in, so the wardrobes are capped at 9 ft 0 in, clear under it.

SETTLED — D2 sits 2 ft 3 in from the corner to its frame (1⅛" Sept), l

this sheet against AST-DR-000 and AST-DR-007: this room's right-ha

bed-wall corner are the same corner. Walls are taken at 9 in throughc

OPEN — D3 is 2 ft 6 in frame to frame (2 ft 3 in leaf, 1" Sept), but the

12 ft 4 in leaves 3 ft 0 in — so a 6 in return is shown into the corner. T

OPEN — the wardrobes are 2 ft 3 in deep and D2's frame is now 2 ft 3

the right-hand run's face lands flush on the frame, no clearance. Trim

OPEN — the left run is drawn stopping at D3. Whether it ends there c

is not decided.

OPEN — where the tunnel leads, and what is at its far end.

OPEN — the dome's own shape: how far along the room it runs, and

The mirror is the confirmed trifold, 3 ft 6 in across with its wings at 4

PROJECT	SHEET	SCALE	DATE	REV	DRAWING
A Study in Teak — Dressing Room	**Notes** Shell and layout · third pass	NTS	16.10.2026	4	**AST-DR-023 · 3 of 3**

ALL DIMENSIONS IN FEET & INCHES. PRINT ON A4 AT 100% / "ACTUAL SIZE" — NOT "FIT TO PAGE" — AND CHECK THE SCALE BAR. DO NOT SCALE; WORK TO FIGURED DIMENSIONS. VERIFY ON SITE.