
## DRESSING ROOM — SHELL AND LAYOUT

PLAN · COPIED FROM THE OWNER'S SKETCH — NOT YET A SITE MEASUREMENT

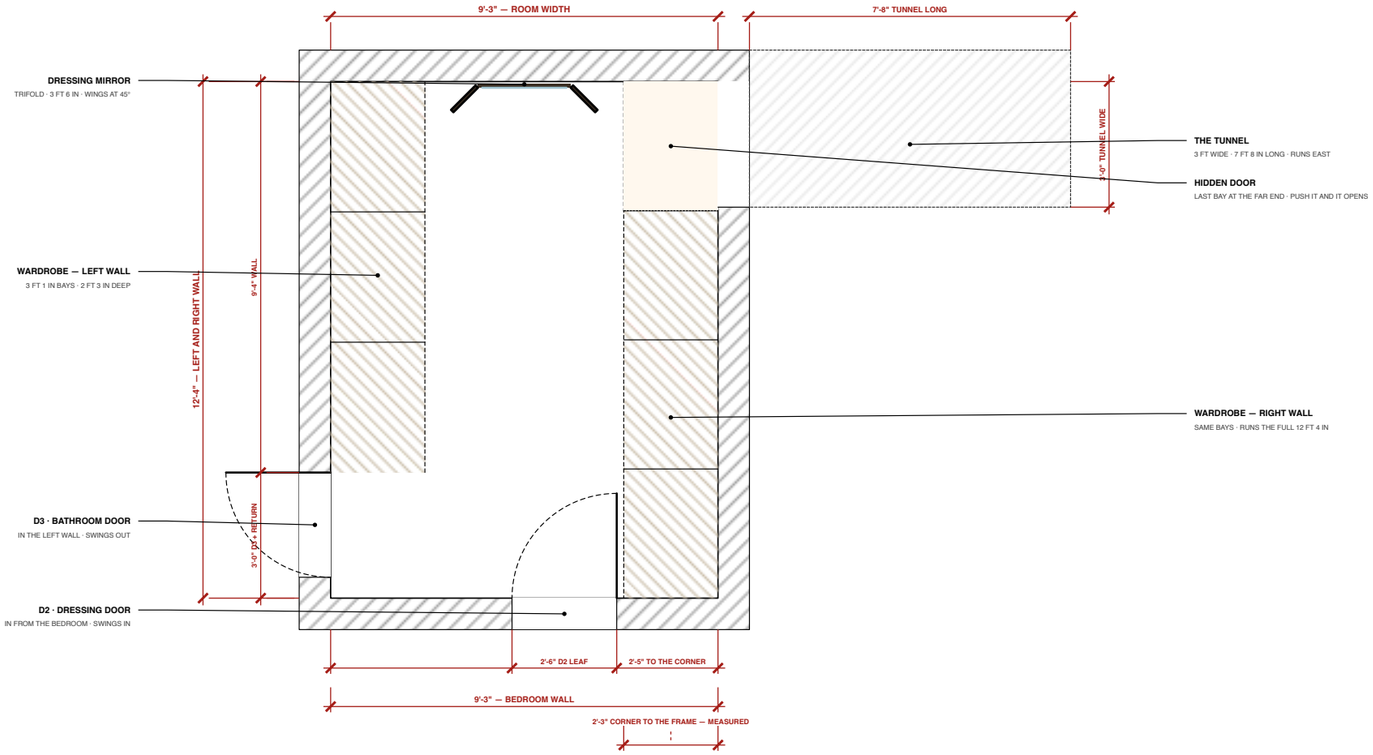


## NOTES

REVISION 4

Third pass, and this one copies the sketch rather than interpreting it. The two earlier drawings both had the shape wrong; everything below is read straight off the owner's own clean drawing.

The BEDROOM wall is the bottom wall here, 9 ft 3 in, and it carries D2, the existing dressing door in from the bedroom, 2 ft 3 in from the right-hand corner to the door FRAME — measured 1¼" Sept on both sides of the wall, and the figure that now governs. The sketch's 2 ft 0 in is superseded.

The BATHROOM door, D3, is in the LEFT wall, at the bedroom end — not in the bedroom wall. The sketch runs 9 ft 4 in of wall down from the far corner and then opens the door.

The TUNNEL runs EAST, straight out of the far end of the right wall, 3 ft wide and 7 ft 8 in long, its far side flush with the far wall. The hidden door is the last wardrobe bay in front of it: built and shelved like every other bay, so from the room it reads as one more cupboard.

Ceiling 9 ft 1 in, plain, over the left and right sides — the same height as the main room. A domed centre rises to 10 ft 0 in, so the wardrobes are capped at 9 ft 0 in, clear under it.

SETTLED — D2 sits 2 ft 3 in from the corner to its frame (1¼" Sept), leaf 2 ft 6 in. That closes this sheet against AST-DR-000 and AST-DR-007: this room's right-hand corner and the bedroom's bed-wall corner are the same corner. Walls are taken at 9 in throughout. See AST-DR-024.

OPEN — D3 is 2 ft 6 in frame to frame (2 ft 3 in leaf, 1" Sept), but the sketch's 9 ft 4 in against 12 ft 4 in leaves 3 ft 0 in — so a 6 in return is shown into the corner. To confirm.

OPEN — the wardrobes are 2 ft 3 in deep and D2's frame is now 2 ft 3 in off that corner (1¼" Sept): the right-hand run's face lands flush on the frame, no clearance. Trim the end bay or check on site.

OPEN — the left run is drawn stopping at D3. Whether it ends there or returns over the door is not decided.

OPEN — where the tunnel leads, and what is at its far end.

OPEN — the dome's own shape: how far along the room it runs, and its profile.

The mirror is the confirmed trifold, 3 ft 6 in across with its wings at 45° — see AST-DR-027.

**A STUDY IN TEAK**

Particulars of the room

**DRESSING ROOM**

Shell and layout · third pass


| SCALE | DATE |
|---|---|
| 1:35 @ A3 | 16.10.2026 |
| REV | DWG |
| 4 — the dressing door at the owner's 27 Sept tape: 2 ft 6 in leaf, 2 ft 3 in of wall to the corner | AST-DR-023 |

| PROJECT | SHEET | SCALE | DATE | REV | DRAWING |
|---|---|---|---|---|---|
| A Study in Teak — Dressing Room | **General arrangement — the whole sheet**<br>each view follows at its own scale, pages 2 to 3 | NTS | 16.10.2026 | 4 | **AST-DR-023 · 1 of 3** |

ALL DIMENSIONS IN FEET & INCHES. PRINT ON A3 AT 100% / "ACTUAL SIZE" — NOT "FIT TO PAGE" — AND CHECK THE SCALE BAR. DO NOT SCALE; WORK TO FIGURED DIMENSIONS. VERIFY ON SITE.

## DRESSING ROOM — SHELL AND LAYOUT

SCALE 1:30 @ A3 · PLAN · COPIED FROM THE OWNER'S SKETCH — NOT YET A SITE MEASUREMENT

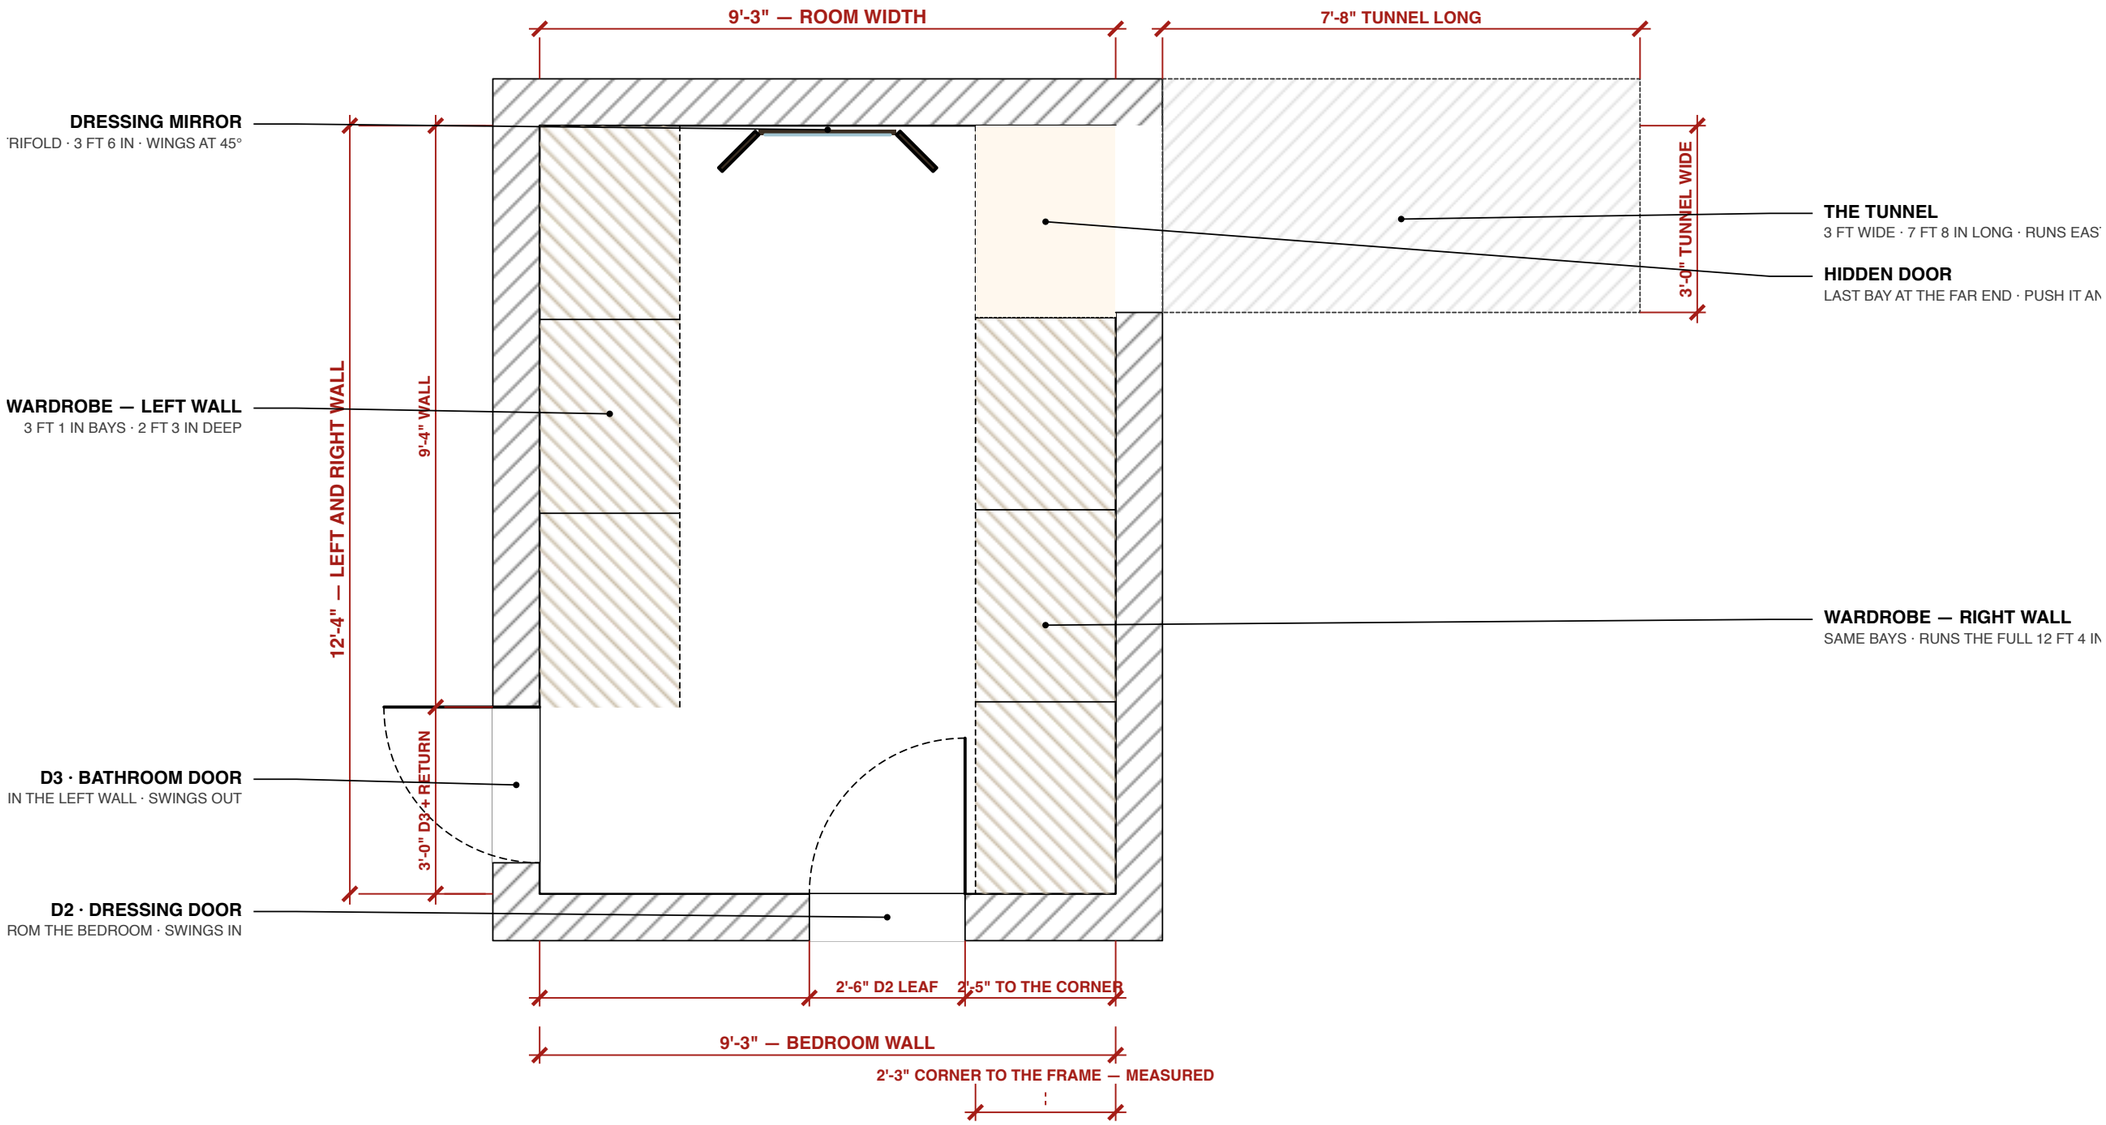


| PROJECT | SHEET | SCALE | DATE | REV | DRAWING |
|---|---|---|---|---|---|
| A Study in Teak — Dressing Room | **Dressing room — shell and layout**<br>Shell and layout · third pass | 1:30 @ A3 | 16.10.2026 | 4 | **AST-DR-023 · 2 of 3** |

ALL DIMENSIONS IN FEET & INCHES. PRINT ON A3 AT 100% / "ACTUAL SIZE" — NOT "FIT TO PAGE" — AND CHECK THE SCALE BAR. DO NOT SCALE; WORK TO FIGURED DIMENSIONS. VERIFY ON SITE.

# NOTES

REVISION 4

Third pass, and this one copies the sketch rather than interpreting it. The two earlier drawings both had the shape wrong; everything below is read straight off the owner's own clean drawing.

The BEDROOM wall is the bottom wall here, 9 ft 3 in, and it carries D2, the existing dressing door in from the bedroom, 2 ft 3 in from the right-hand corner to the door FRAME — measured 1⅛" Sept on both sides of the wall, and the figure that now governs. The sketch's 2 ft 0 in is superseded.

The BATHROOM door, D3, is in the LEFT wall, at the bedroom end — not in the bedroom wall. The sketch runs 9 ft 4 in of wall down from the far corner and then opens the door.

The TUNNEL runs EAST, straight out of the far end of the right wall, 3 ft wide and 7 ft 8 in long, its far side flush with the far wall. The hidden door is the last wardrobe bay in front of it: built and shelved like every other bay, so from the room it reads as one more cupboard.

Ceiling 9 ft 1 in, plain, over the left and right sides — the same height as the main room. A domed centre rises to 10 ft 0 in, so the wardrobes are capped at 9 ft 0 in, clear under it.

SETTLED — D2 sits 2 ft 3 in from the corner to its frame (1⅛" Sept), leaf 2 ft (

this sheet against AST-DR-000 and AST-DR-007: this room's right-hand corne

bed-wall corner are the same corner. Walls are taken at 9 in throughout. See

OPEN — D3 is 2 ft 6 in frame to frame (2 ft 3 in leaf, 1" Sept), but the sketch's

12 ft 4 in leaves 3 ft 0 in — so a 6 in return is shown into the corner. To confi

OPEN — the wardrobes are 2 ft 3 in deep and D2's frame is now 2 ft 3 in off t

the right-hand run's face lands flush on the frame, no clearance. Trim the en

OPEN — the left run is drawn stopping at D3. Whether it ends there or return

is not decided.

OPEN — where the tunnel leads, and what is at its far end.

OPEN — the dome's own shape: how far along the room it runs, and its profi

The mirror is the confirmed trifold, 3 ft 6 in across with its wings at 45° — se

| PROJECT | SHEET | SCALE | DATE | REV | DRAWING |
|---|---|---|---|---|---|
| A Study in Teak — Dressing Room | **Notes**<br>Shell and layout · third pass | NTS | 16.10.2026 | 4 | **AST-DR-023 · 3 of 3** |

ALL DIMENSIONS IN FEET & INCHES. PRINT ON A3 AT 100% / “ACTUAL SIZE” — NOT “FIT TO PAGE” — AND CHECK THE SCALE BAR. DO NOT SCALE; WORK TO FIGURED DIMENSIONS. VERIFY ON SITE.