

ELEVATION — RIGHT WALL

SEEN FROM THE ROOM · STUDY WALL ON THE LEFT · OPTION C

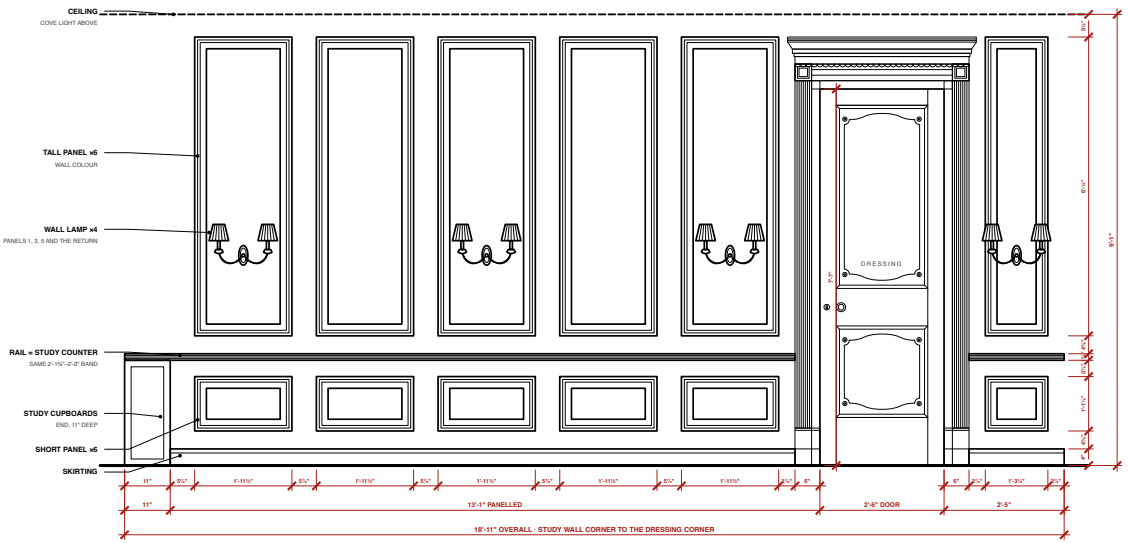


SECTION A–A

THROUGH PANEL 1

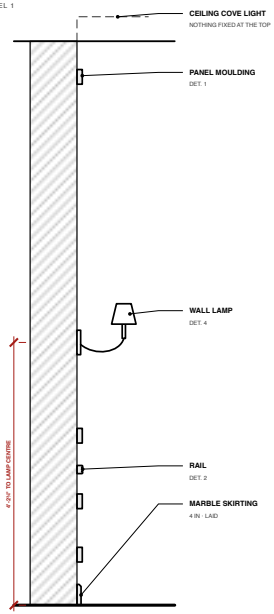

PLAN

CUT AT 3'-3¾" · ROOM BELOW, WALL ABOVE

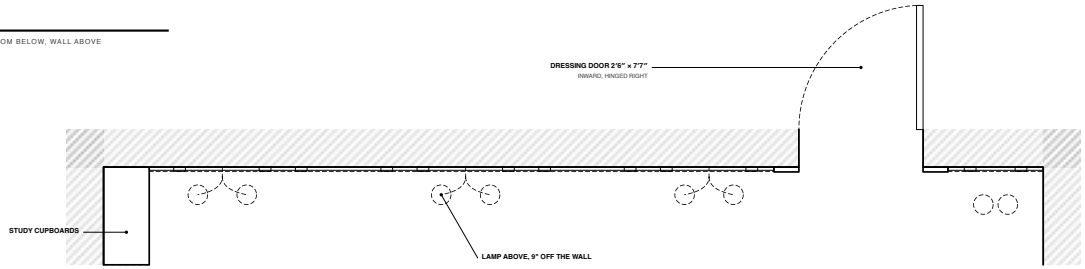

NOTES

REVISION 20

Option C: 5 equal panels, lamps in 1, 3, 5 and the return.

One narrow panel on the wall past the door.

Moulding, rail and skirting painted the wall colour.

SELECTED after four schemes: the rail is the study counter band carried round the corner, and it dies into the casing.


Skirting is white marble, 4 in, already laid.

Casing 2 in lining + 4 in moulding = 6 in, 3'-6" overall; crown at 8 ft 8 in, and the tall panels stop on that line, not the leaf head at 7 ft 7 in.

Dressing door (1¾" Sept tape): leaf 2 ft 6 in, 2 ft 10 in with frame; 2 ft 3 in of wall to the corner. OPEN: the frame lands 13 ft 10 from the study corner, 4 in off the 13 ft 6 taped on ½" Sept.

1 · PANEL MOULDING


SECTION · THE OWNER'S LAYERED PROFILE

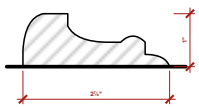

WALL FACE BELOW · MITRED CORNERS

2 · RAIL


SECTION

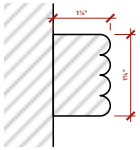

MATCHES THE COUNTER EDGE

3 · SKIRTING


MARBLE · SECTION

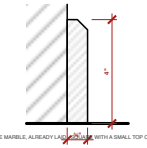

WHITE MARBLE, ALREADY LAID · 4 IN WITH A SMALL TOP CHAMFER

4 · WALL LAMP

ELEVATION · ×4

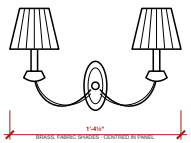

BRASS, FABRIC SHADES · CENTRED IN PANEL

A STUDY IN TEAK

Particulars of the room

RIGHT WALL — PANEL MOULDING

Elevation · Plan · Section · Details


SCALE	DATE
AS NOTED @ A3	16.10.2026
REV	DWG
20 — the drawing does not set the reveal to 6" (kept taper 2 ft 6 in lead, 2 ft 10 in with frame, 2 ft 3 in of wall to the corner	AST-DR-007

PROJECT	SHEET	SCALE	DATE	REV	DRAWING
A Study in Teak — Right Wall — Panel Mou…	**General arrangement — the whole sheet** each view follows at its own scale, pages 2 to 9	NTS	16.10.2026	20	**AST-DR-007 · 1 of 9**

ALL DIMENSIONS IN FEET & INCHES. PRINT ON A4 AT 100% / "ACTUAL SIZE" — NOT "FIT TO PAGE" — AND CHECK THE SCALE BAR. DO NOT SCALE; WORK TO FIGURED DIMENSIONS. VERIFY ON SITE.

ELEVATION — RIGHT WALL

SCALE 1:30 @ A4 · SEEN FROM THE ROOM · STUDY WALL ON THE LEFT · OPTION C

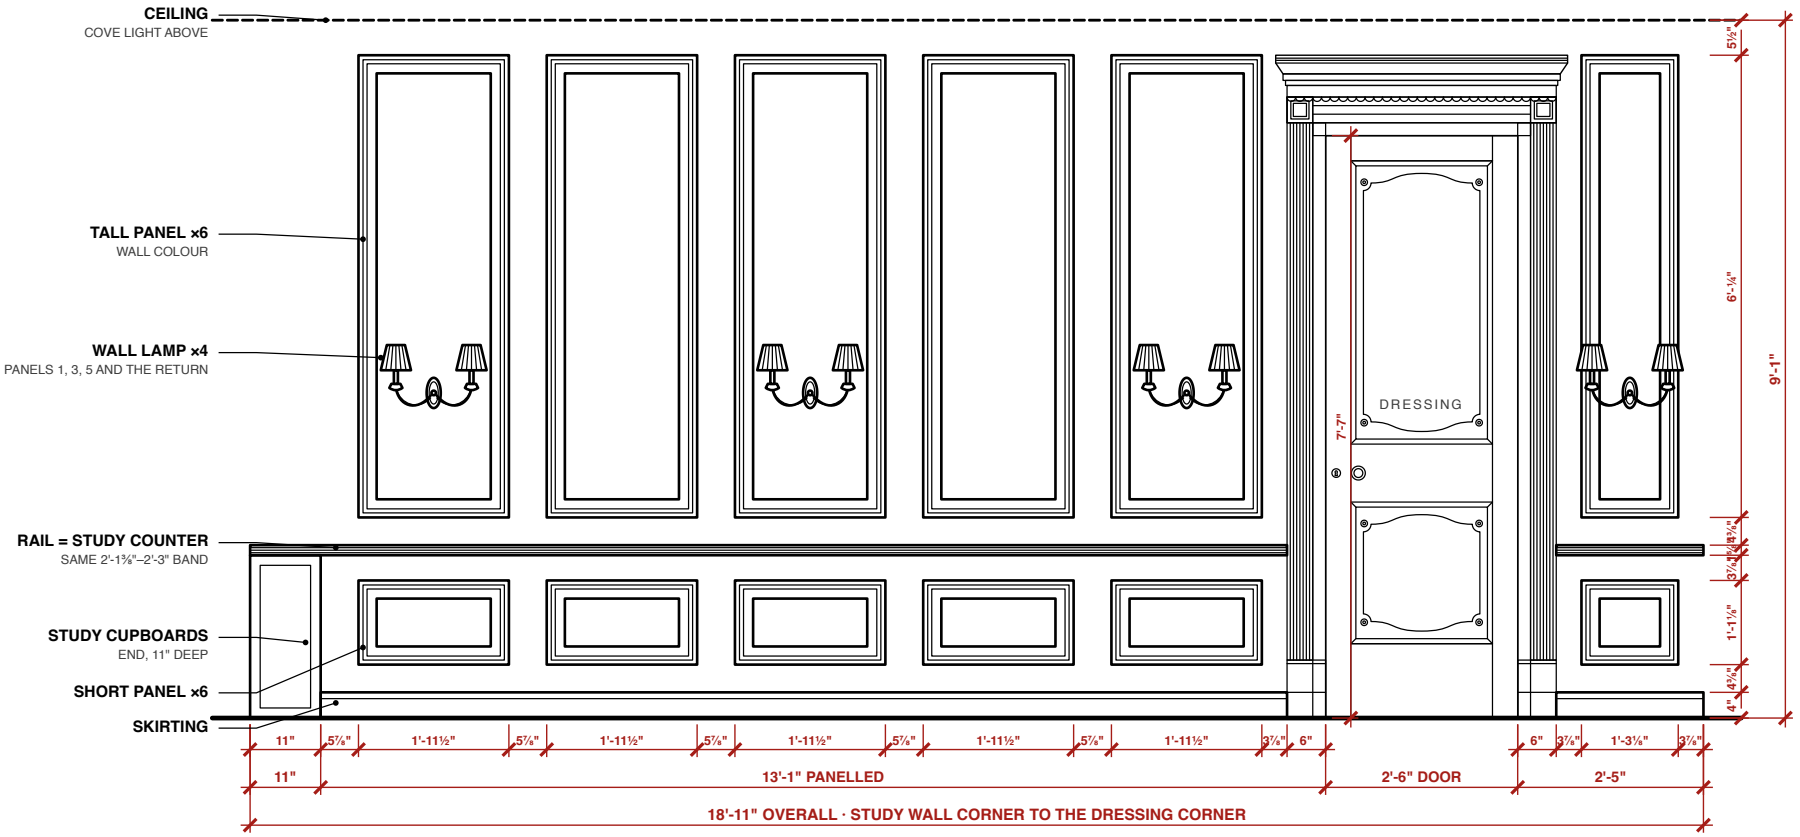


0" 1'-0" 2'-0" 3'-0" 4'-0" 5'-0" 6'-0"


PROJECT	SHEET	SCALE	DATE	REV	DRAWING
A Study in Teak — Right Wall — Panel Mou…	**Elevation — right wall** Elevation · Plan · Section · Details	1:30 @ A4	16.10.2026	20	**AST-DR-007 · 2 of 9**

ALL DIMENSIONS IN FEET & INCHES. PRINT ON A4 AT 100% / "ACTUAL SIZE" — NOT "FIT TO PAGE" — AND CHECK THE SCALE BAR. DO NOT SCALE; WORK TO FIGURED DIMENSIONS. VERIFY ON SITE.

SECTION A–A

SCALE 1:24 (½" = 1'-0") @ A4 · THROUGH PANEL 1

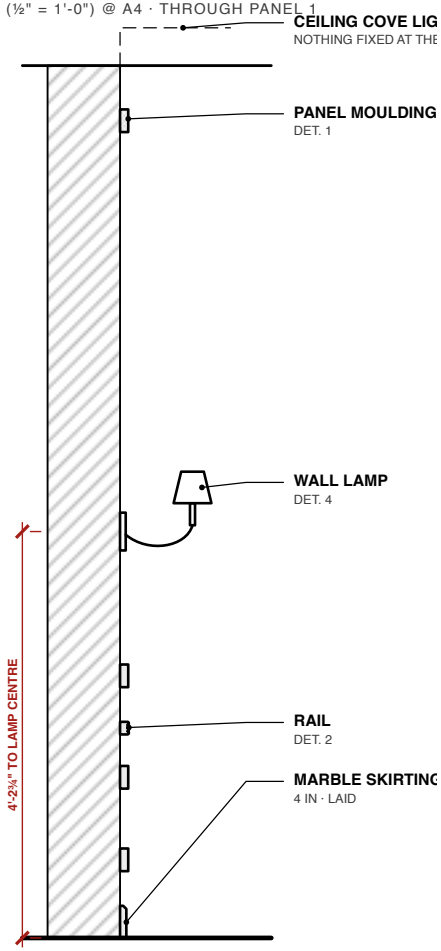

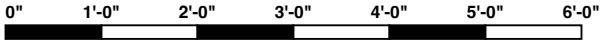



PROJECT	SHEET	SCALE	DATE	REV	DRAWING
A Study in Teak — Right Wall — Panel Mou…	**Section A–A** Elevation · Plan · Section · Details	1:24 @ A4	16.10.2026	20	**AST-DR-007 · 3 of 9**

ALL DIMENSIONS IN FEET & INCHES. PRINT ON A4 AT 100% / "ACTUAL SIZE" — NOT "FIT TO PAGE" — AND CHECK THE SCALE BAR. DO NOT SCALE; WORK TO FIGURED DIMENSIONS. VERIFY ON SITE.

PLAN

SCALE 1:30 @ A4 · CUT AT 3'-3⅜" · ROOM BELOW, WALL ABOVE

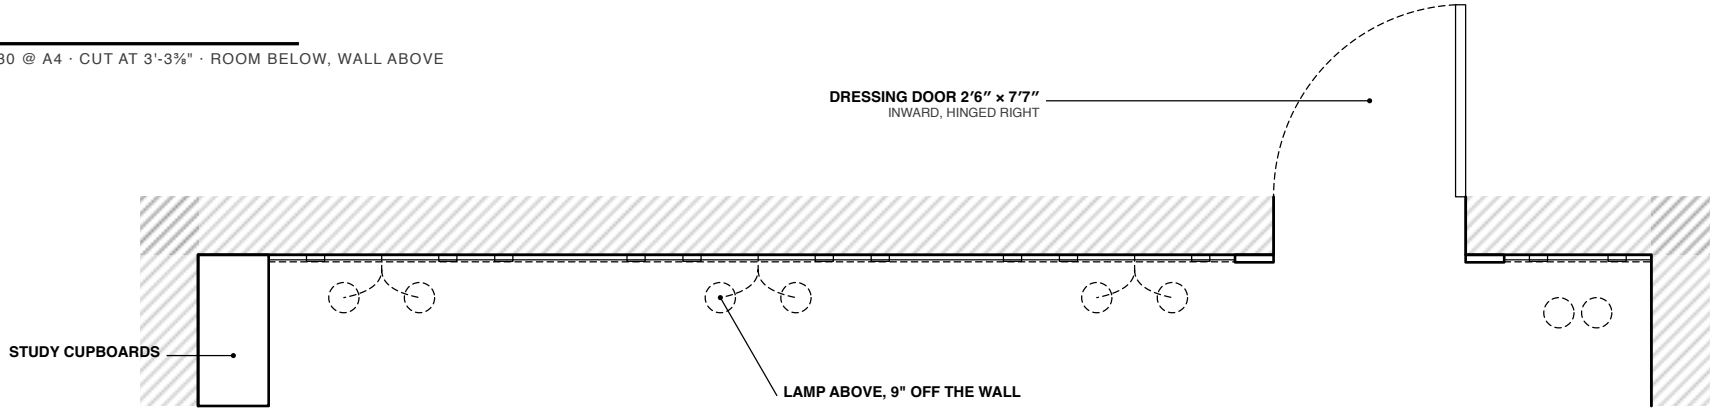

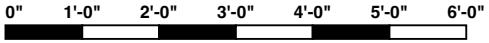

PROJECT	SHEET	SCALE	DATE	REV	DRAWING
A Study in Teak — Right Wall — Panel Mou…	**Plan** Elevation · Plan · Section · Details	1:30 @ A4	16.10.2026	20	**AST-DR-007 · 4 of 9**

ALL DIMENSIONS IN FEET & INCHES. PRINT ON A4 AT 100% / "ACTUAL SIZE" — NOT "FIT TO PAGE" — AND CHECK THE SCALE BAR. DO NOT SCALE; WORK TO FIGURED DIMENSIONS. VERIFY ON SITE.

NOTES

REVISION 20

Option C: 5 equal panels, lamps in 1, 3, 5 and the return.

One narrow panel on the wall past the door.

Moulding, rail and skirting painted the wall colour.

SELECTED after four schemes: the rail is the study counter

band carried round the corner, and it dies into the casing.

Skirting is white marble, 4 in, already laid.

Casing 2 in lining + 4 in moulding = 6 in, 3'-6" overall;

crown at 8 ft 8 in, and the tall panels stop on that

line, not the leaf head at 7 ft 7 in.

Dressing door (1⅛" Sept tape): leaf 2 ft 6 in, 2 ft 10 in with frame

2 ft 3 in of wall to the corner. OPEN: the frame lands 13 ft 10


from the study corner, 4 in off the 13 ft 6 taped on ¾" Sept.

PROJECT	SHEET	SCALE	DATE	REV	DRAWING
A Study in Teak — Right Wall — Panel Mou…	**Notes** Elevation · Plan · Section · Details	NTS	16.10.2026	20	**AST-DR-007 · 5 of 9**


ALL DIMENSIONS IN FEET & INCHES. PRINT ON A4 AT 100% / "ACTUAL SIZE" — NOT "FIT TO PAGE" — AND CHECK THE SCALE BAR. DO NOT SCALE; WORK TO FIGURED DIMENSIONS. VERIFY ON SITE.

1 · PANEL MOULDING

SCALE 1:1 (FULL SIZE) @ A4 · SECTION · THE OWNER'S LAYER

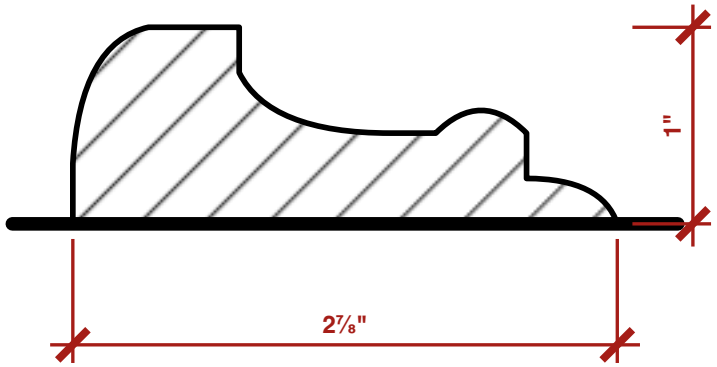

WALL FACE BELOW · MITRED CORNERS

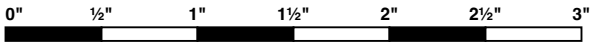


PROJECT	SHEET	SCALE	DATE	REV	DRAWING
A Study in Teak — Right Wall — Panel Mou…	**1 · panel moulding** Elevation · Plan · Section · Details	1:1 @ A4	16.10.2026	20	**AST-DR-007 · 6 of 9**

ALL DIMENSIONS IN FEET & INCHES. PRINT ON A4 AT 100% / "ACTUAL SIZE" — NOT "FIT TO PAGE" — AND CHECK THE SCALE BAR. DO NOT SCALE; WORK TO FIGURED DIMENSIONS. VERIFY ON SITE.

2 · RAIL

SCALE 1:1 (FULL SIZE) @ A4 · SEC

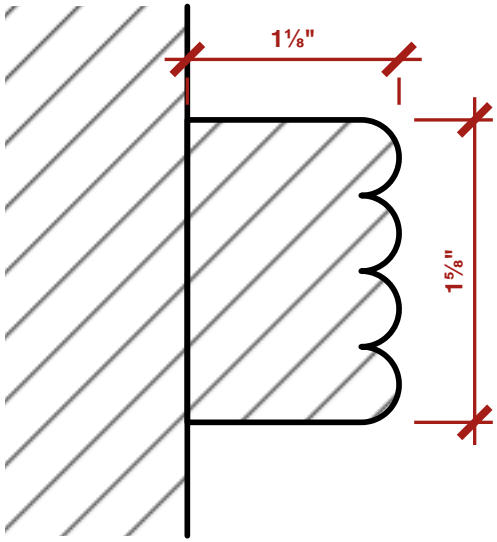

MATCHES THE COUNTER EDGE


0" ½" 1" 1½" 2" 2½" 3"

PROJECT	SHEET	SCALE	DATE	REV	DRAWING
A Study in Teak — Right Wall — Panel Mou…	**2 · rail** Elevation · Plan · Section · Details	1:1 @ A4	16.10.2026	20	**AST-DR-007 · 7 of 9**


ALL DIMENSIONS IN FEET & INCHES. PRINT ON A4 AT 100% / "ACTUAL SIZE" — NOT "FIT TO PAGE" — AND CHECK THE SCALE BAR. DO NOT SCALE; WORK TO FIGURED DIMENSIONS. VERIFY ON SITE.

3 · SKIRTING

SCALE 1:2 (6" = 1'-0") @ A4 · MARBLE · SECTION

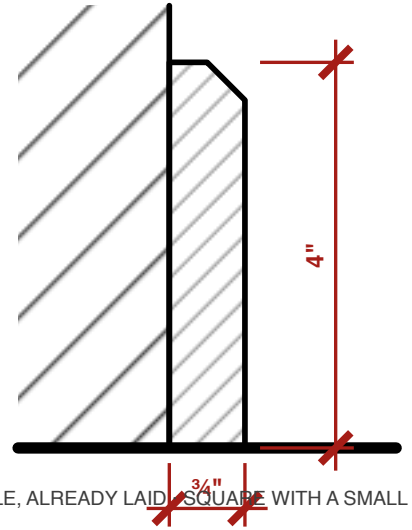

WHITE MARBLE, ALREADY LAID · SQUARE WITH A SMALL TOP CHAMFER

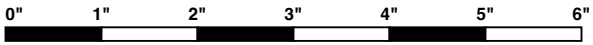


PROJECT	SHEET	SCALE	DATE	REV	DRAWING
A Study in Teak — Right Wall — Panel Mou…	**3 · skirting** Elevation · Plan · Section · Details	1:2 @ A4	16.10.2026	20	**AST-DR-007 · 8 of 9**

ALL DIMENSIONS IN FEET & INCHES. PRINT ON A4 AT 100% / "ACTUAL SIZE" — NOT "FIT TO PAGE" — AND CHECK THE SCALE BAR. DO NOT SCALE; WORK TO FIGURED DIMENSIONS. VERIFY ON SITE.

4 · WALL LAMP

SCALE 1:4 (3" = 1'-0") @ A4 · ELEVATION · ×4

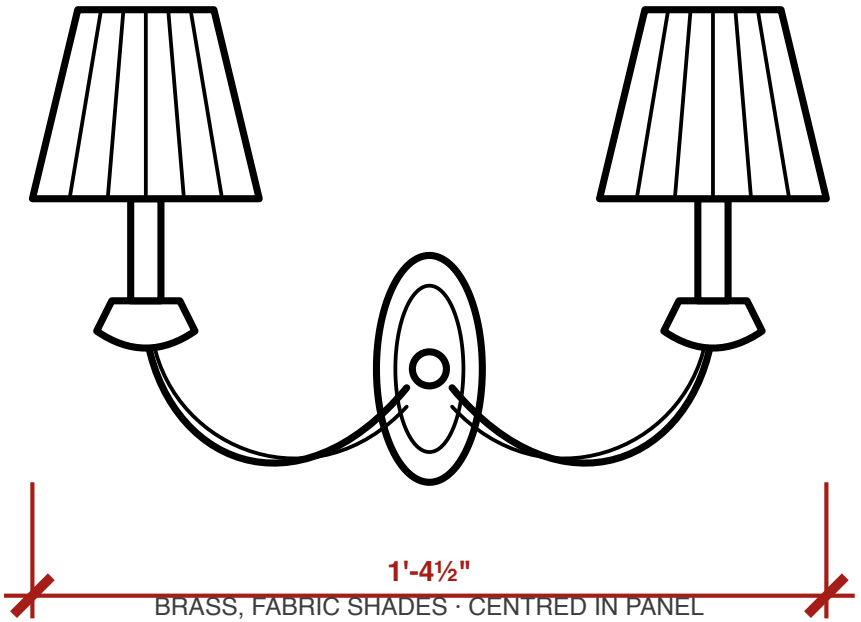

BRASS, FABRIC SHADES · CENTRED IN PANEL

0" 2" 4" 6" 8" 10" 1'-0"

PROJECT	SHEET	SCALE	DATE	REV	DRAWING
A Study in Teak — Right Wall — Panel Mou…	**4 · wall lamp** Elevation · Plan · Section · Details	1:4 @ A4	16.10.2026	20	**AST-DR-007 · 9 of 9**

ALL DIMENSIONS IN FEET & INCHES. PRINT ON A4 AT 100% / "ACTUAL SIZE" — NOT "FIT TO PAGE" — AND CHECK THE SCALE BAR. DO NOT SCALE; WORK TO FIGURED DIMENSIONS. VERIFY ON SITE.