

ELEVATION — STUDY WALL, WITH THE ARCHES

SEEN FROM THE ROOM · CURTAINS NOT DRAWN

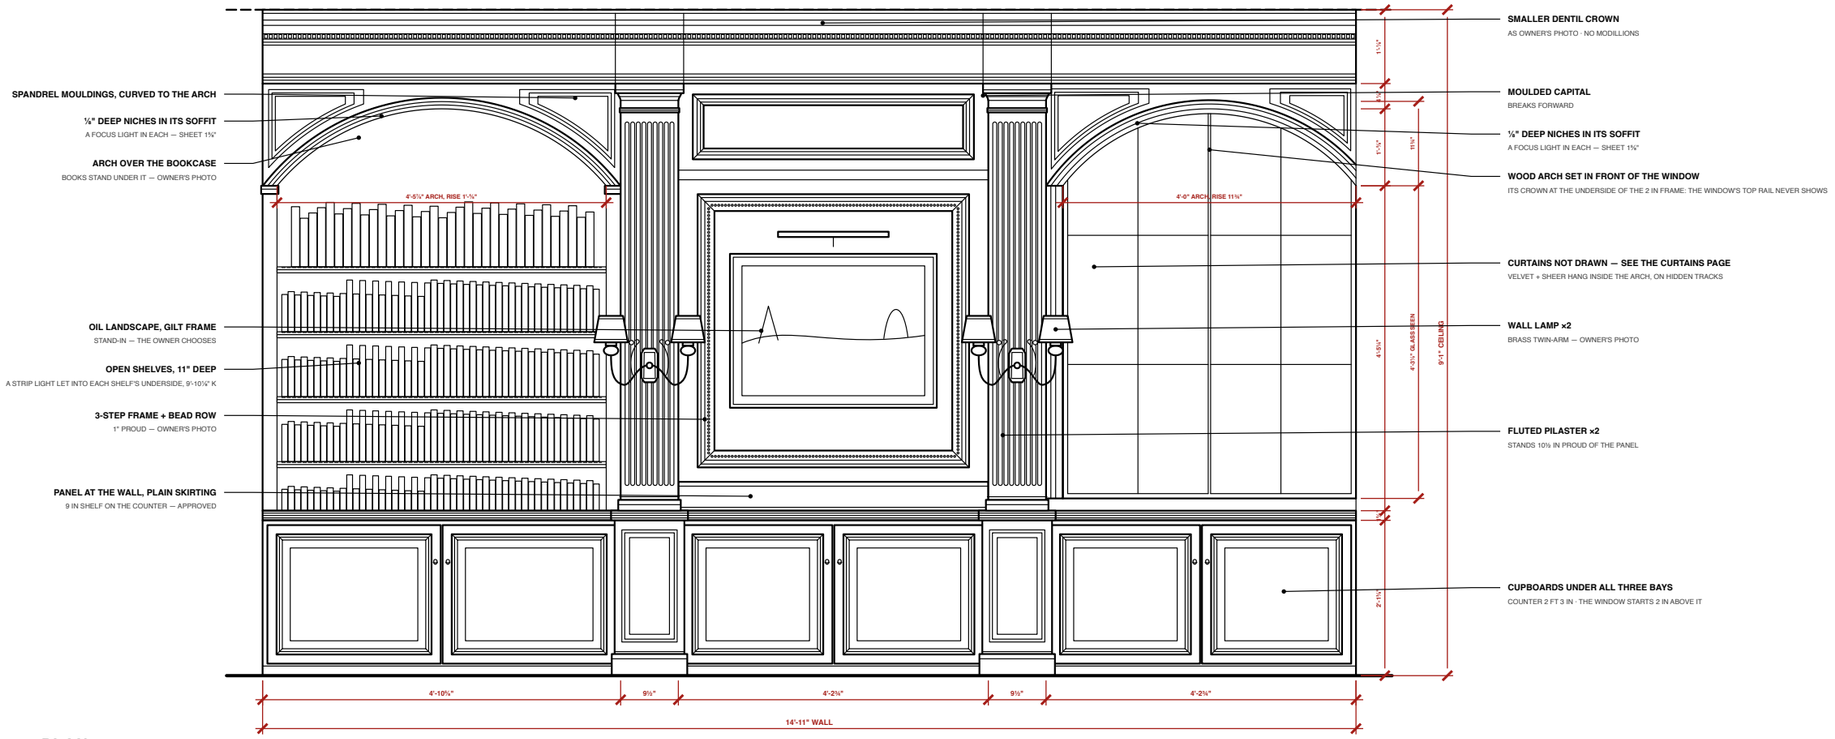

PLAN

CUT AT 3'-11¼" · WALL AT THE TOP · OVERHEAD AND BELOW DASHED

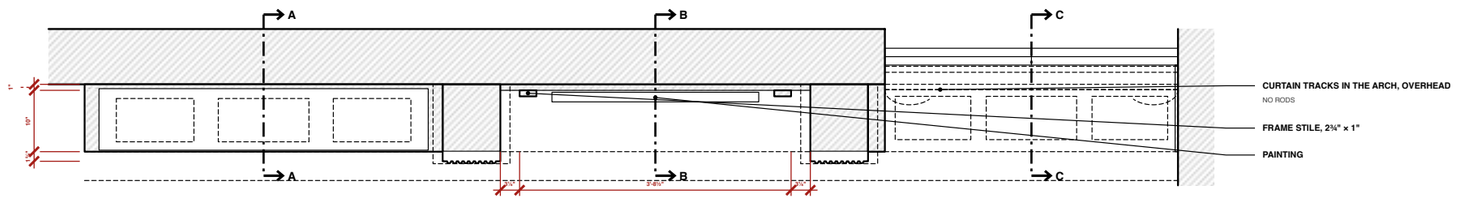

NOTES

REVISION 4

Owner's second scheme (7 Oct). Arches over the bookcase and the window, three deep rectangular niches cut into each arch's underside — a focus light in each (8 Oct) — and spandrel mouldings curved to follow the arch. The window's glass is unchanged: the wood arch is a veneered panel set in front of the window's top: its crown sits at the underside of the window's 2 in top rail, so the window's top rail is hidden and only glass shows; both arches spring at one line. Curtains not drawn.

Centre: the panel goes back to the wall plane, so the counter is a 9 in shelf and the pilasters stand 10⅛ in proud (approved).

Mouldings, crown and lamp from the owner's photos. Sections: AST-DR-042. Details: AST-DR-043.

A STUDY IN TEAK

Particulars of the room

STUDY WALL — WITH ARCHES

Elevation · Plan


SCALE	DATE
1:20 @ A3	09.10.2026
REV	DWG
	AST-DR-040

PROJECT	SHEET	SCALE	DATE	REV	DRAWING
A Study in Teak — Study Wall — With Arches	**General arrangement — the whole sheet** each view follows at its own scale, pages 2 to 3	NTS	09.10.2026	4	**AST-DR-040 · 1 of 16**

ALL DIMENSIONS IN FEET & INCHES. PRINT ON A3 AT 100% / "ACTUAL SIZE" — NOT "FIT TO PAGE" — AND CHECK THE SCALE BAR. DO NOT SCALE; WORK TO FIGURED DIMENSIONS. VERIFY ON SITE.

PLAN

SCALE 1:20 @ A3 · CUT AT 3'-11¼" · WALL AT THE TOP · OVERHEAD AND BELOW DASHED

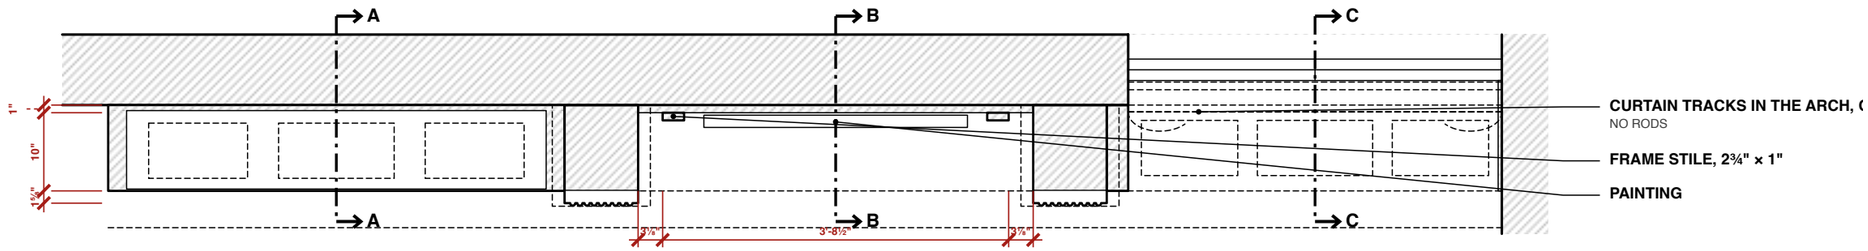

0" 1'-0" 2'-0" 3'-0" 4'-0" 5'-0" 6'-0"

PROJECT	SHEET	SCALE	DATE	REV	DRAWING
A Study in Teak — Study Wall — With Arches	**Plan** Elevation · Plan	1:20 @ A3	09.10.2026	4	**AST-DR-040 · 2 of 16**

ALL DIMENSIONS IN FEET & INCHES. PRINT ON A3 AT 100% / "ACTUAL SIZE" — NOT "FIT TO PAGE" — AND CHECK THE SCALE BAR. DO NOT SCALE; WORK TO FIGURED DIMENSIONS. VERIFY ON SITE.

NOTES

REVISION 4

Owner's second scheme (7 Oct). Arches over the bookcase and the window, three deep rectangular niches cut into each

arch's underside — a focus light in each (8 Oct) — and spandrel mouldings curved to follow the arch. The window's glass is unchanged: the wood arch

is a veneered panel set in front of the window's top: its crown sits at the underside of the window's 2 in top rail, so the window's top rail is hidden and only glass shows; both arches spring at one line. Curtai

Centre: the panel goes back to the wall plane, so the counter is a 9 in shelf and the pilasters stand 10½ in proud (approved).


Mouldings, crown and lamp from the owner's photos. Sections: AST-DR-042. Details: AST-DR-043.

PROJECT	SHEET	SCALE	DATE	REV	DRAWING
A Study in Teak — Study Wall — With Arches	**Notes** Elevation · Plan	NTS	09.10.2026	4	**AST-DR-040 · 3 of 16**

ALL DIMENSIONS IN FEET & INCHES. PRINT ON A3 AT 100% / “ACTUAL SIZE” — NOT “FIT TO PAGE” — AND CHECK THE SCALE BAR. DO NOT SCALE; WORK TO FIGURED DIMENSIONS. VERIFY ON SITE.


SECTION A–A

THROUGH THE BOOKCASE AT THE ARCH'S CROWN

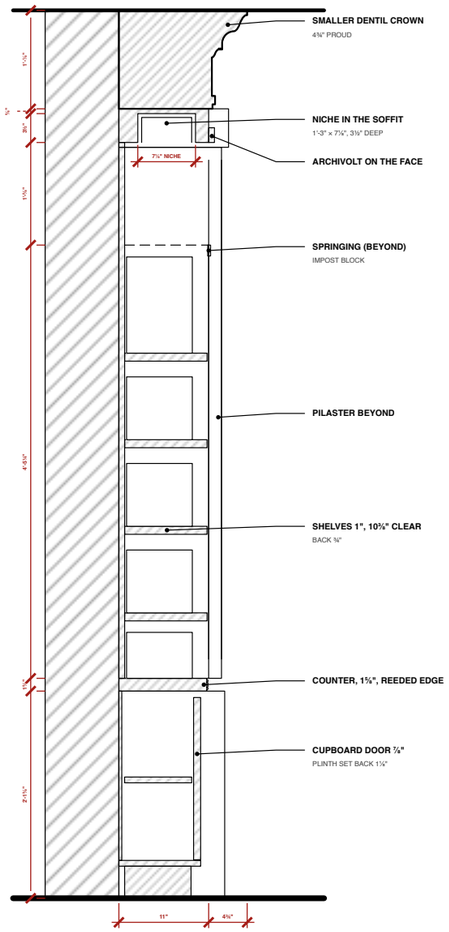


SECTION B–B

THROUGH THE CENTRE BAY AND PAINTING

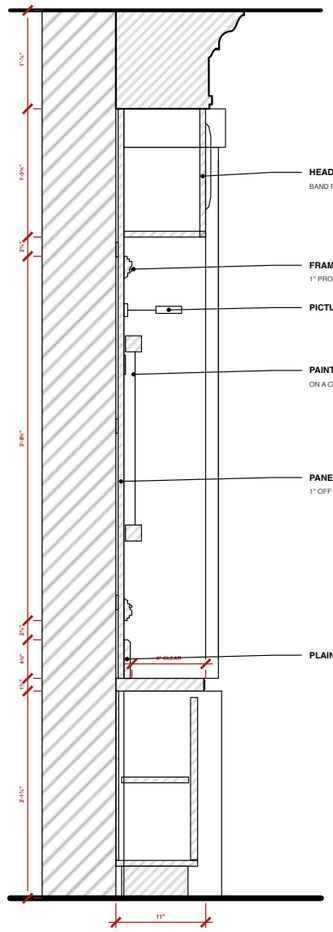

SECTION C–C

THROUGH THE WINDOW AT THE ARCH'S CROWN

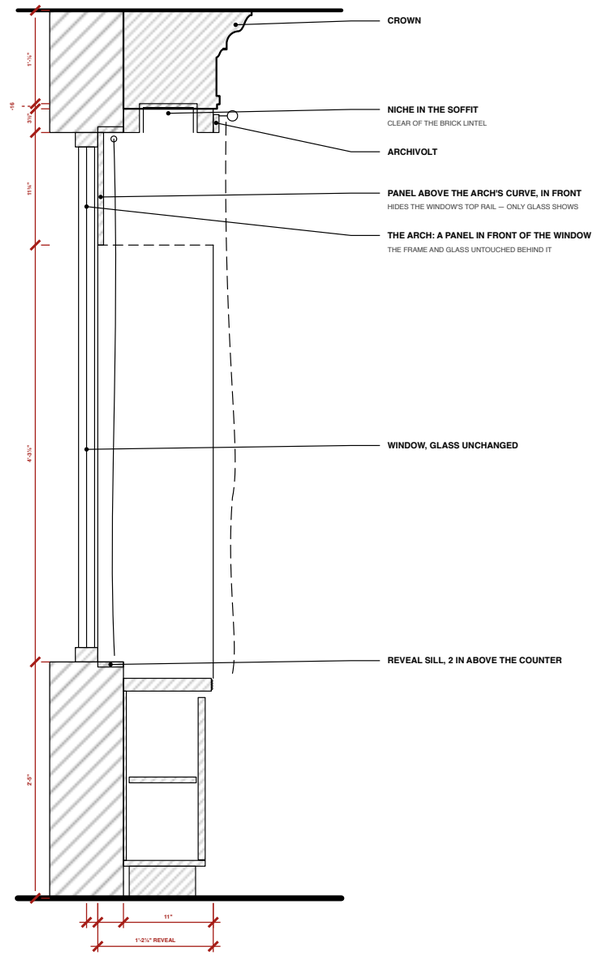

NOTES

REVISION 4

All three cut looking along the wall to the right (cut lines on AST-DR-040's plan). Each arch's head is a ply former, veneered; its three niches are boxes let into it, 3½" deep, lined in the same veneer, a small focus light (9'-10¼" K) in the middle of each. The window's niches stay in the timber, in front of the brick lintel. The window bay's panelling now runs at 11" like the rest, so the crown is one plane and the reveal ½" in.

Centre: panel at the wall plane, header at the cornice plane — the counter becomes a 9 in shelf under it. Details: AST-DR-043.

A STUDY IN TEAK

Particulars of the room

STUDY WALL — SECTIONS

A–A bookcase · B–B centre · C–C window


SCALE	DATE
1:15 @ A3	09.10.2026
REV	DWG
	AST-DR-042

PROJECT	SHEET	SCALE	DATE	REV	DRAWING
A Study in Teak — Study Wall — Sections	**General arrangement — the whole sheet** each view follows at its own scale, pages 5 to 7	NTS	09.10.2026	4	**AST-DR-042 · 4 of 16**

ALL DIMENSIONS IN FEET & INCHES. PRINT ON A3 AT 100% / "ACTUAL SIZE" — NOT "FIT TO PAGE" — AND CHECK THE SCALE BAR. DO NOT SCALE; WORK TO FIGURED DIMENSIONS. VERIFY ON SITE.

SECTION A–A

SCALE 1:15 @ A3 · THROUGH THE BOOKCASE AT THE ARCH'S CROWN

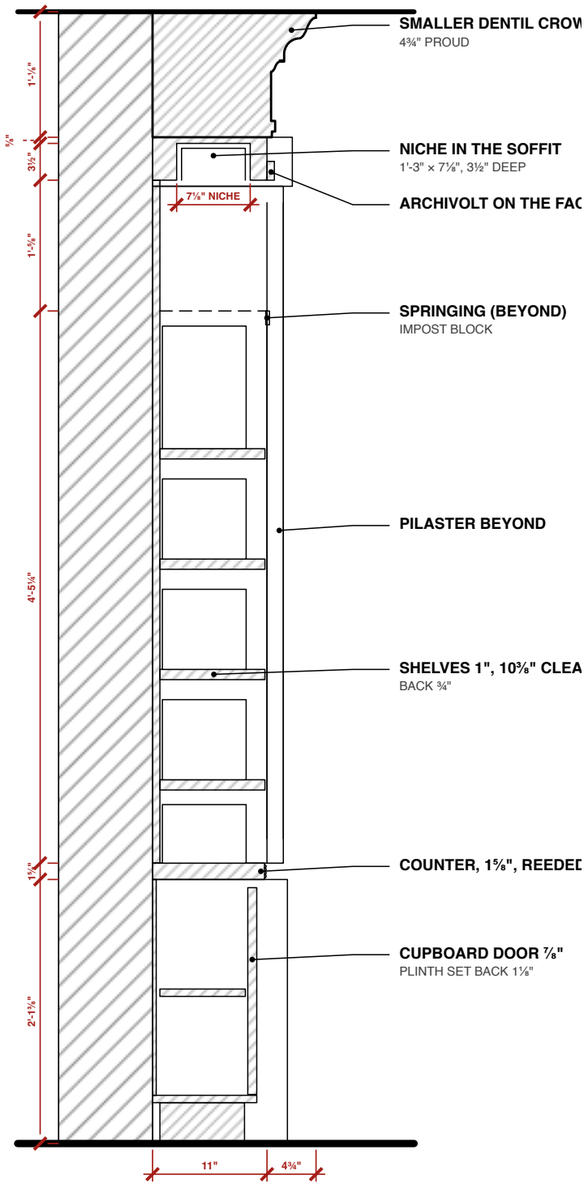


0" 6" 1'-0" 1'-6" 2'-0" 2'-6" 3'-0"

PROJECT	SHEET	SCALE	DATE	REV	DRAWING
A Study in Teak — Study Wall — Sections	**Section A–A** A–A bookcase · B–B centre · C–C window	1:15 @ A3	09.10.2026	4	**AST-DR-042 · 5 of 16**

ALL DIMENSIONS IN FEET & INCHES. PRINT ON A3 AT 100% / "ACTUAL SIZE" — NOT "FIT TO PAGE" — AND CHECK THE SCALE BAR. DO NOT SCALE; WORK TO FIGURED DIMENSIONS. VERIFY ON SITE.

SECTION B–B

SCALE 1:15 @ A3 · THROUGH THE CENTRE BAY AND PAINTING

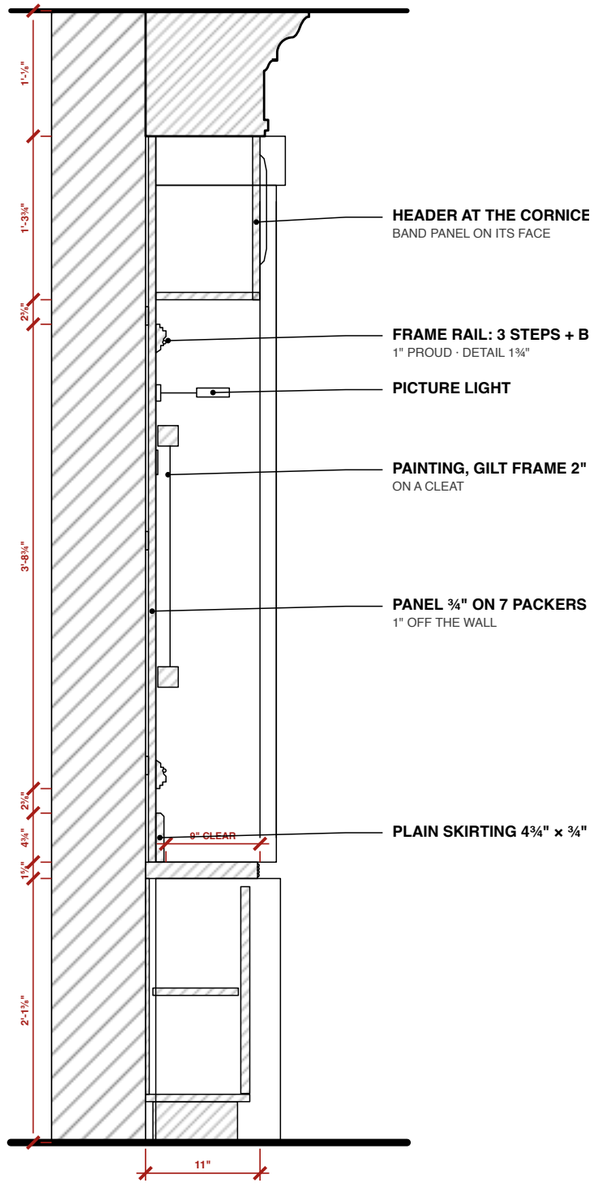

0" 6" 1'-0" 1'-6" 2'-0" 2'-6" 3'-0"

PROJECT	SHEET	SCALE	DATE	REV	DRAWING
A Study in Teak — Study Wall — Sections	**Section B–B** A–A bookcase · B–B centre · C–C window	1:15 @ A3	09.10.2026	4	**AST-DR-042 · 6 of 16**

ALL DIMENSIONS IN FEET & INCHES. PRINT ON A3 AT 100% / “ACTUAL SIZE” — NOT “FIT TO PAGE” — AND CHECK THE SCALE BAR. DO NOT SCALE; WORK TO FIGURED DIMENSIONS. VERIFY ON SITE.

NOTES

REVISION 4

All three cut looking along the wall to the right (cut lines on AST-DR-040's plan). Each arch's head is a ply former, veneered;

its three niches are boxes let into it, 3½" deep, lined in the same veneer, a small focus light (9'-10⅛" K) in the middle of each. The window's niches stay in the timber,

in front of the brick lintel. The window bay's panelling now runs at 11" like the rest, so the crown is one plane and the reveal ½" in.


Centre: panel at the wall plane, header at the cornice plane — the counter becomes a 9 in shelf under it. Details: AST-DR-043.

PROJECT	SHEET	SCALE	DATE	REV	DRAWING
A Study in Teak — Study Wall — Sections	**Notes** A–A bookcase · B–B centre · C–C window	NTS	09.10.2026	4	**AST-DR-042 · 7 of 16**

ALL DIMENSIONS IN FEET & INCHES. PRINT ON A3 AT 100% / “ACTUAL SIZE” — NOT “FIT TO PAGE” — AND CHECK THE SCALE BAR. DO NOT SCALE; WORK TO FIGURED DIMENSIONS. VERIFY ON SITE.


1 · BOOKCASE ARCH — ITS UNDERSIDE

LOOKING UP, UNROLLED FLAT · WALL AT THE TOP, ROOM BELOW

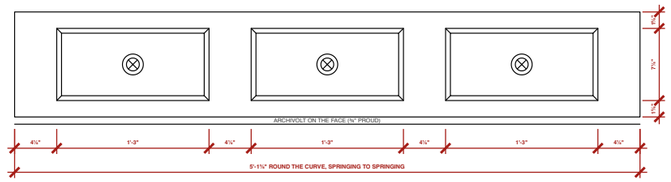


2 · WINDOW ARCH — ITS UNDERSIDE

LOOKING UP, UNROLLED FLAT

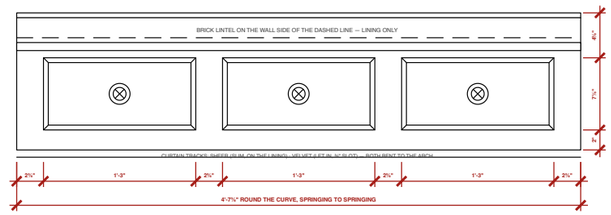


3 · A NICHE IN SECTION

ACROSS THE SOFFIT AT THE CROWN

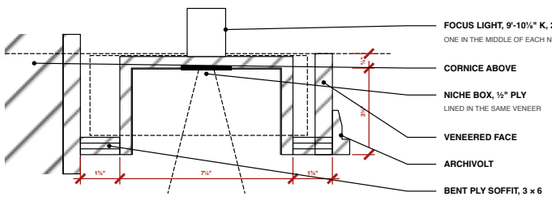


4 · THE CROWN

SECTION · OWNER'S PHOTO

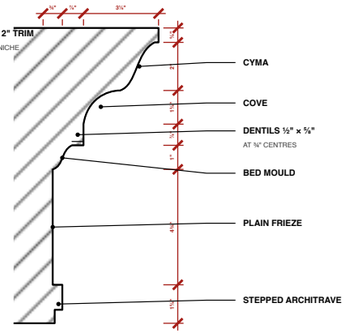


5 · THE PAINTING FRAME

SECTION + FACE · BEAD ROW, OWNER'S PHOTO

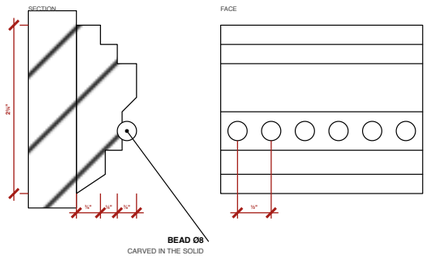

7 · SPANDREL MOULDING

SECTION

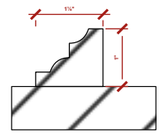


SPANDREL PANEL, VENEERED

STEPS AT ¼" AND 1¼", ROUND THE CURVE TOO

6 · SKIRTING + COUNTER

SECTION

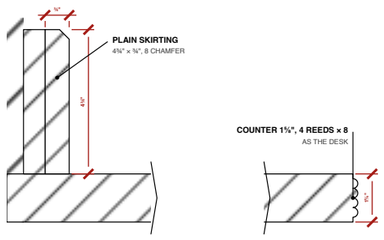

NOTES

REVISION 4

Details for AST-DR-040/042 (and 041/044 except the arches). Mouldings from the owner's photos; profiles to be mocked up full size

before cutting. Each niche has one small focus light, 9'-10¼" K, in the middle of its top (owner, 8 Oct). All timber in the room's teak veneer; no colour in this set.

A STUDY IN TEAK

Particulars of the room

STUDY WALL — DETAILS

Niches · crown · frame · skirting


SCALE	DATE
AS NOTED @ A3	**09.10.2026**
REV	DWG
2 — niche lights (owner, 8 Oct); niches for the arches only	**AST-DR-043**


PROJECT	SHEET	SCALE	DATE	REV	DRAWING
A Study in Teak — Study Wall — Details	**General arrangement — the whole sheet** each view follows at its own scale, pages 9 to 16	NTS	09.10.2026	2	**AST-DR-043 · 8 of 16**

ALL DIMENSIONS IN FEET & INCHES. PRINT ON A3 AT 100% / "ACTUAL SIZE" — NOT "FIT TO PAGE" — AND CHECK THE SCALE BAR. DO NOT SCALE; WORK TO FIGURED DIMENSIONS. VERIFY ON SITE.

1 · BOOKCASE ARCH — ITS UNDERSIDE

SCALE 1:5 @ A3 · LOOKING UP, UNROLLED FLAT · WALL AT THE TOP, ROOM BELOW

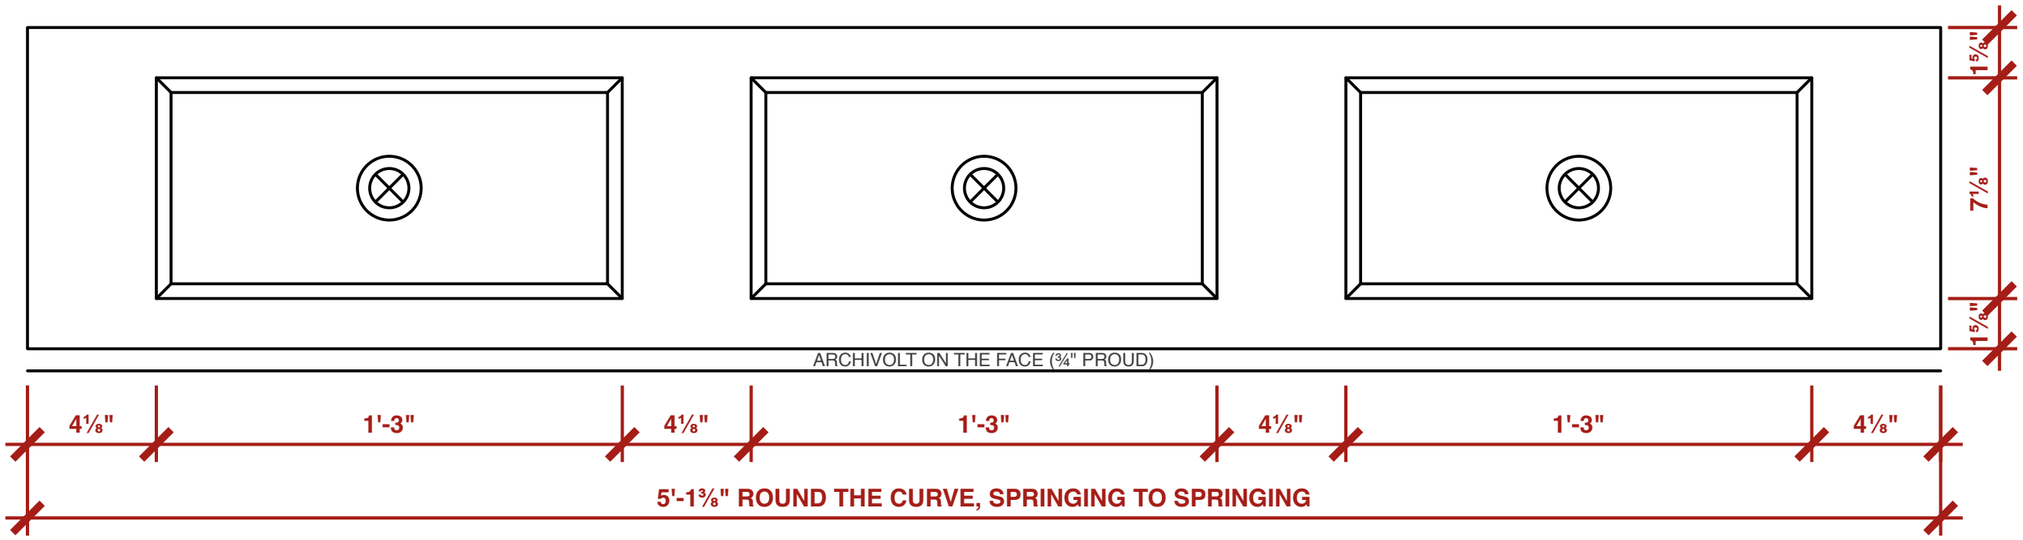

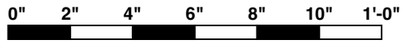


PROJECT	SHEET	SCALE	DATE	REV	DRAWING
A Study in Teak — Study Wall — Details	**1 · bookcase arch — its underside** Niches · crown · frame · skirting	1:5 @ A3	09.10.2026	2	**AST-DR-043 · 9 of 16**

ALL DIMENSIONS IN FEET & INCHES. PRINT ON A3 AT 100% / "ACTUAL SIZE" — NOT "FIT TO PAGE" — AND CHECK THE SCALE BAR. DO NOT SCALE; WORK TO FIGURED DIMENSIONS. VERIFY ON SITE.

2 · WINDOW ARCH — ITS UNDERSIDE

SCALE 1:5 @ A3 · LOOKING UP, UNROLLED FLAT

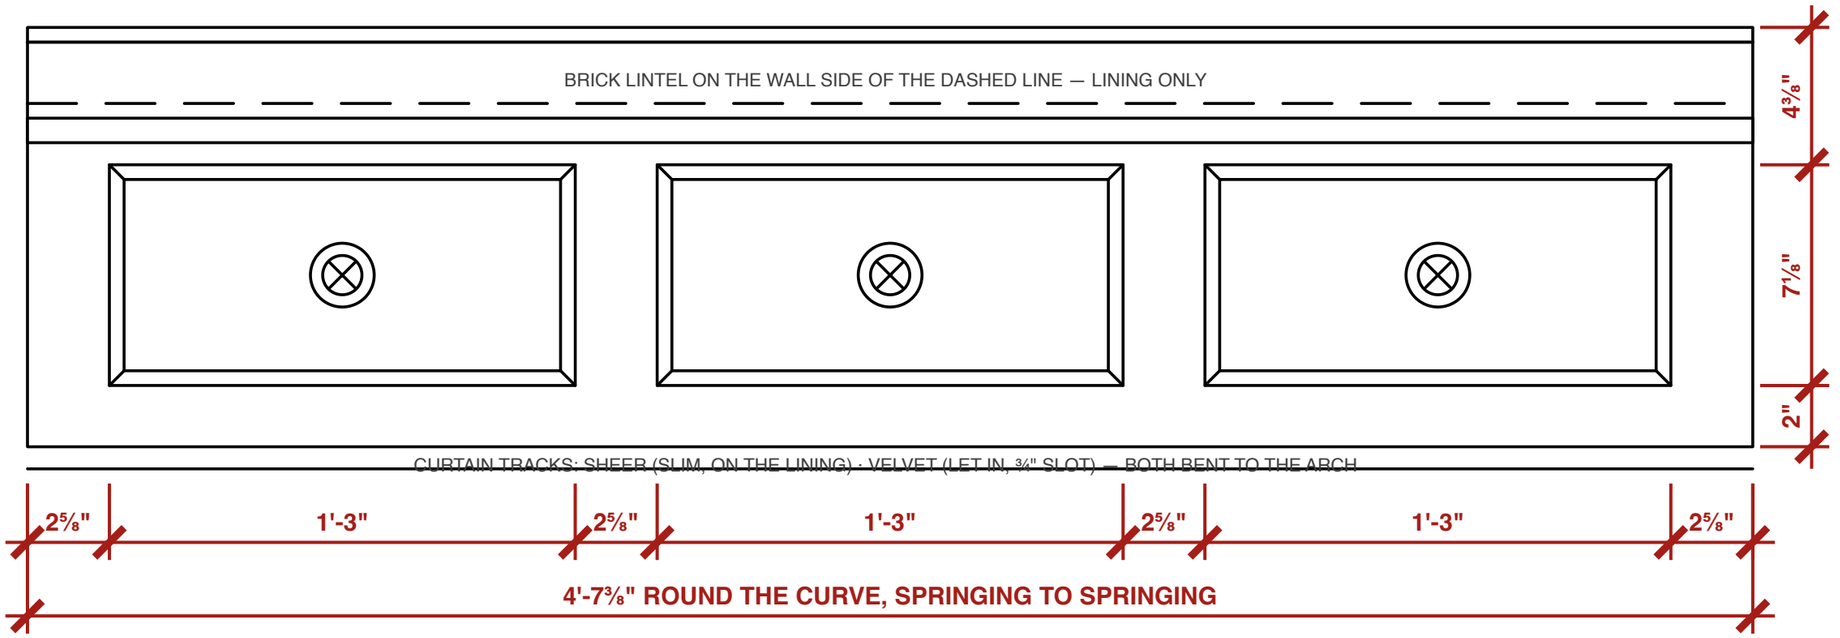


0" 2" 4" 6" 8" 10" 1'-0"

PROJECT	SHEET	SCALE	DATE	REV	DRAWING
A Study in Teak — Study Wall — Details	**2 · window arch — its underside** Niches · crown · frame · skirting	1:5 @ A3	09.10.2026	2	**AST-DR-043 · 10 of 16**

ALL DIMENSIONS IN FEET & INCHES. PRINT ON A3 AT 100% / "ACTUAL SIZE" — NOT "FIT TO PAGE" — AND CHECK THE SCALE BAR. DO NOT SCALE; WORK TO FIGURED DIMENSIONS. VERIFY ON SITE.

3 · A NICHE IN SECTION

SCALE 1:2 (6" = 1'-0") @ A3 · ACROSS THE SOFFIT AT THE CROWN

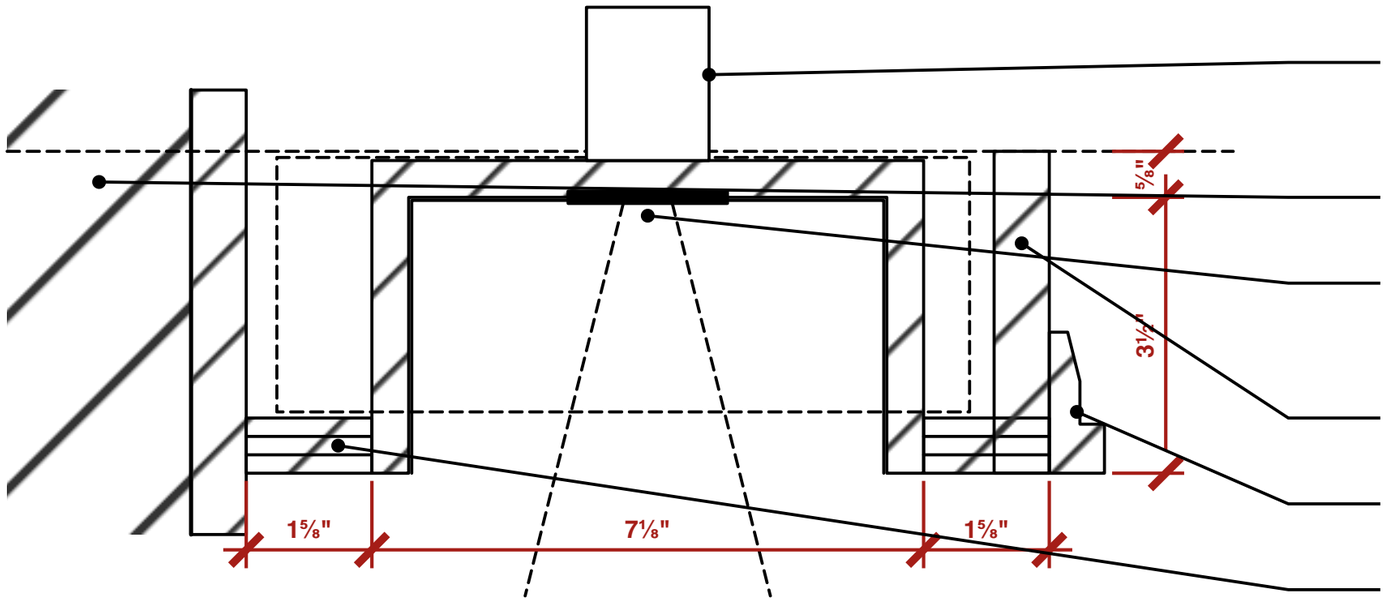



FOCUS LIGHT, 9'-10⅛" K, 2" TRIM
ONE IN THE MIDDLE OF EACH NICHE


CORNICE ABOVE

NICHE BOX, ½" PLY
LINED IN THE SAME VENEER

VENEERED FACE

ARCHIVOLT

BENT PLY SOFFIT, 3 × 6
ON CURVED RIBS (DASHED)

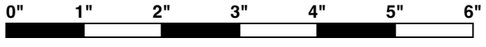


PROJECT	SHEET	SCALE	DATE	REV	DRAWING
A Study in Teak — Study Wall — Details	**3 · a niche in section** Niches · crown · frame · skirting	1:2 @ A3	09.10.2026	2	**AST-DR-043 · 11 of 16**

ALL DIMENSIONS IN FEET & INCHES. PRINT ON A3 AT 100% / "ACTUAL SIZE" — NOT "FIT TO PAGE" — AND CHECK THE SCALE BAR. DO NOT SCALE; WORK TO FIGURED DIMENSIONS. VERIFY ON SITE.

4 · THE CROWN

SCALE 1:2 (6" = 1'-0") @ A3 · SECTION · OWNER'S PHOTO

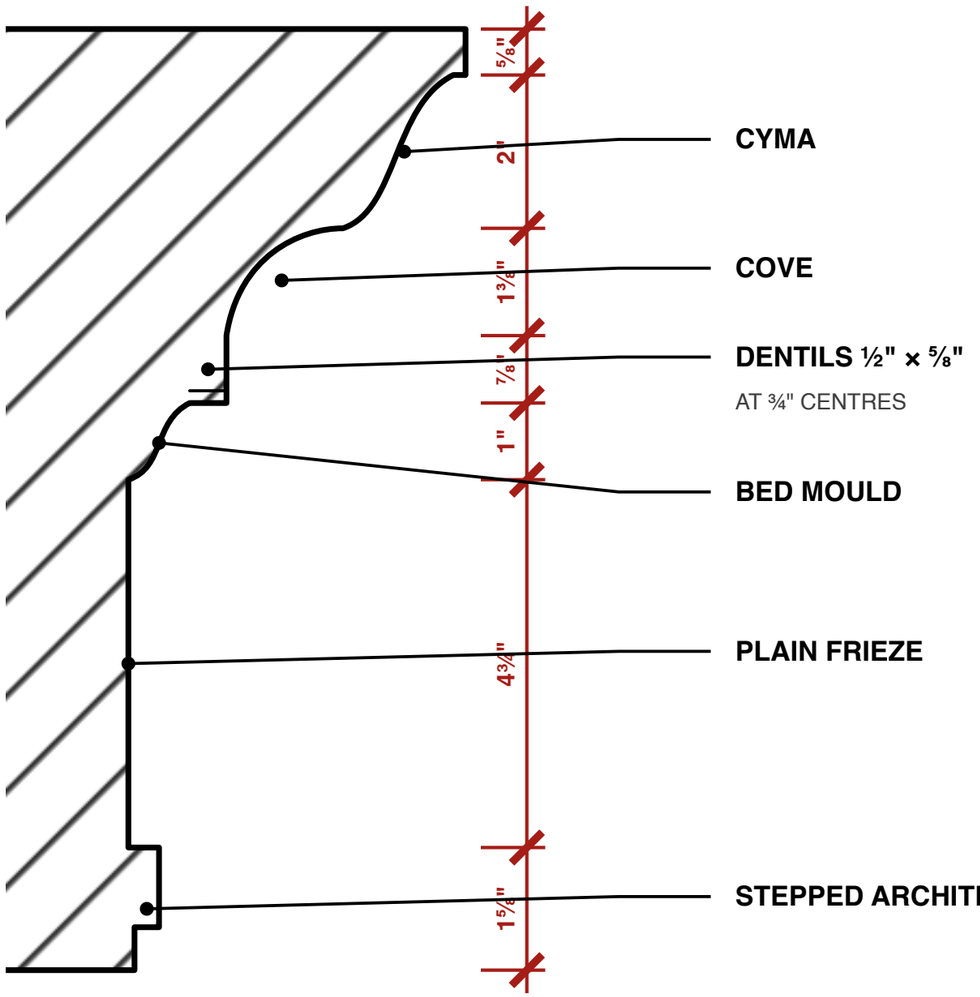




0" 1" 2" 3" 4" 5" 6"

PROJECT	SHEET	SCALE	DATE	REV	DRAWING
A Study in Teak — Study Wall — Details	**4 · the crown** Niches · crown · frame · skirting	1:2 @ A3	09.10.2026	2	**AST-DR-043 · 12 of 16**

ALL DIMENSIONS IN FEET & INCHES. PRINT ON A3 AT 100% / "ACTUAL SIZE" — NOT "FIT TO PAGE" — AND CHECK THE SCALE BAR. DO NOT SCALE; WORK TO FIGURED DIMENSIONS. VERIFY ON SITE.

5 · THE PAINTING FRAME

SCALE 1:1 (FULL SIZE) @ A3 · SECTION + FACE · BEAD ROW, OWNER'S PHOTO

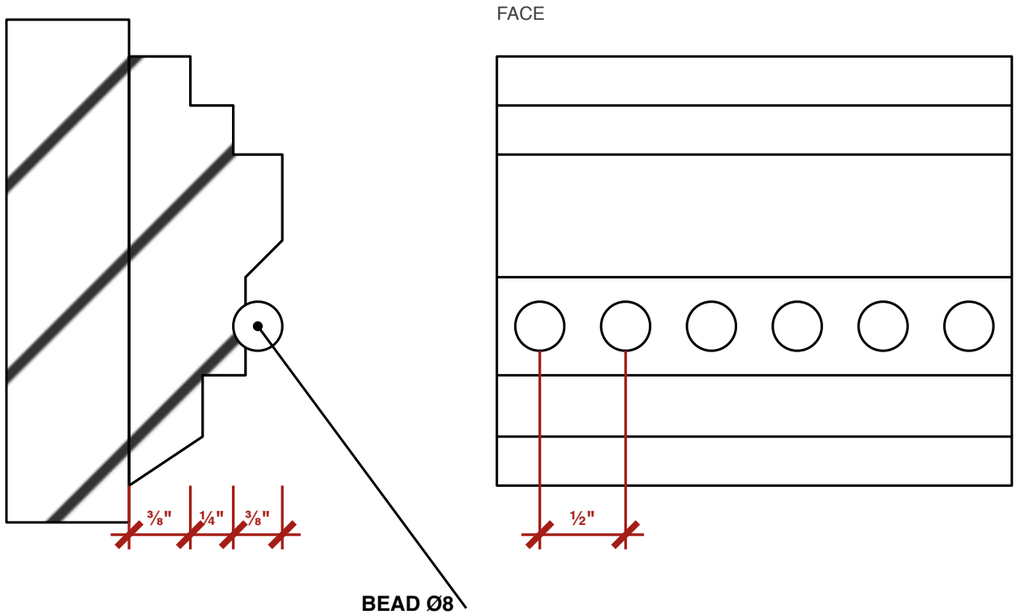

BEAD Ø8
CARVED IN THE SOLID

FACE


0" ½" 1" 1½" 2" 2½" 3"

PROJECT	SHEET	SCALE	DATE	REV	DRAWING
A Study in Teak — Study Wall — Details	**5 · the painting frame** Niches · crown · frame · skirting	1:1 @ A3	09.10.2026	2	**AST-DR-043 · 13 of 16**

ALL DIMENSIONS IN FEET & INCHES. PRINT ON A3 AT 100% / "ACTUAL SIZE" — NOT "FIT TO PAGE" — AND CHECK THE SCALE BAR. DO NOT SCALE; WORK TO FIGURED DIMENSIONS. VERIFY ON SITE.


7 · SPANDREL MOULDING

SCALE 1:1 (FULL SIZE) @ A3 · SECTION

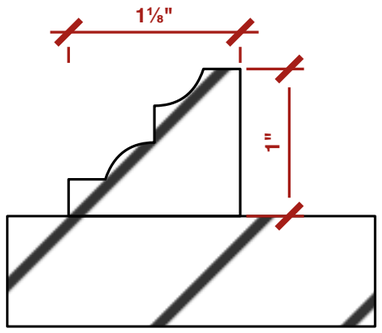

SPANDREL PANEL, VENEERED

STEPS AT ½" AND 1⅛", ROUND THE CURVE TOO

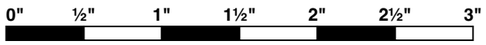


PROJECT	SHEET	SCALE	DATE	REV	DRAWING
A Study in Teak — Study Wall — Details	**7 · spandrel moulding** Niches · crown · frame · skirting	1:1 @ A3	09.10.2026	2	**AST-DR-043 · 14 of 16**


ALL DIMENSIONS IN FEET & INCHES. PRINT ON A3 AT 100% / "ACTUAL SIZE" — NOT "FIT TO PAGE" — AND CHECK THE SCALE BAR. DO NOT SCALE; WORK TO FIGURED DIMENSIONS. VERIFY ON SITE.

6 · SKIRTING + COUNTER

SCALE 1:2 (6" = 1'-0") @ A3 · SECTION

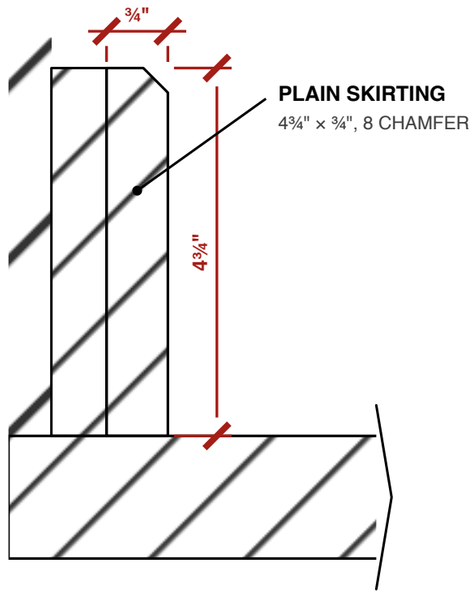

PLAIN SKIRTING
4¾" × ¾", 8 CHAMFER

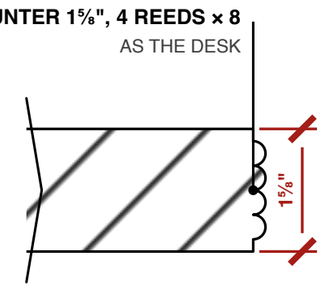

COUNTER 1⅝", 4 REEDS × 8
AS THE DESK

0" 1" 2" 3" 4" 5" 6"

PROJECT	SHEET	SCALE	DATE	REV	DRAWING
A Study in Teak — Study Wall — Details	**6 · skirting + counter** Niches · crown · frame · skirting	1:2 @ A3	09.10.2026	2	**AST-DR-043 · 15 of 16**

ALL DIMENSIONS IN FEET & INCHES. PRINT ON A3 AT 100% / "ACTUAL SIZE" — NOT "FIT TO PAGE" — AND CHECK THE SCALE BAR. DO NOT SCALE; WORK TO FIGURED DIMENSIONS. VERIFY ON SITE.

NOTES

REVISION 4

Details for AST-DR-040/042 (and 041/044 except the arches). Mouldings from the owner's photos; profiles to be mocked up full size

before cutting. Each niche has one small focus light, 9'-10⅛" K, in the middle of its top (owner, 8 Oct). All timber in the room's teak veneer; no colour in this set.

PROJECT	SHEET	SCALE	DATE	REV	DRAWING
A Study in Teak — Study Wall — Details	**Notes** Niches · crown · frame · skirting	NTS	09.10.2026	2	**AST-DR-043 · 16 of 16**

ALL DIMENSIONS IN FEET & INCHES. PRINT ON A3 AT 100% / “ACTUAL SIZE” — NOT “FIT TO PAGE” — AND CHECK THE SCALE BAR. DO NOT SCALE; WORK TO FIGURED DIMENSIONS. VERIFY ON SITE.