


THE ROOM AS BUILT

PLAN · SCALE 1:40 · SHELL ONLY, NO FURNITURE · CEILING 2769 (9 FT 1 IN) LEVEL THROUGHOUT

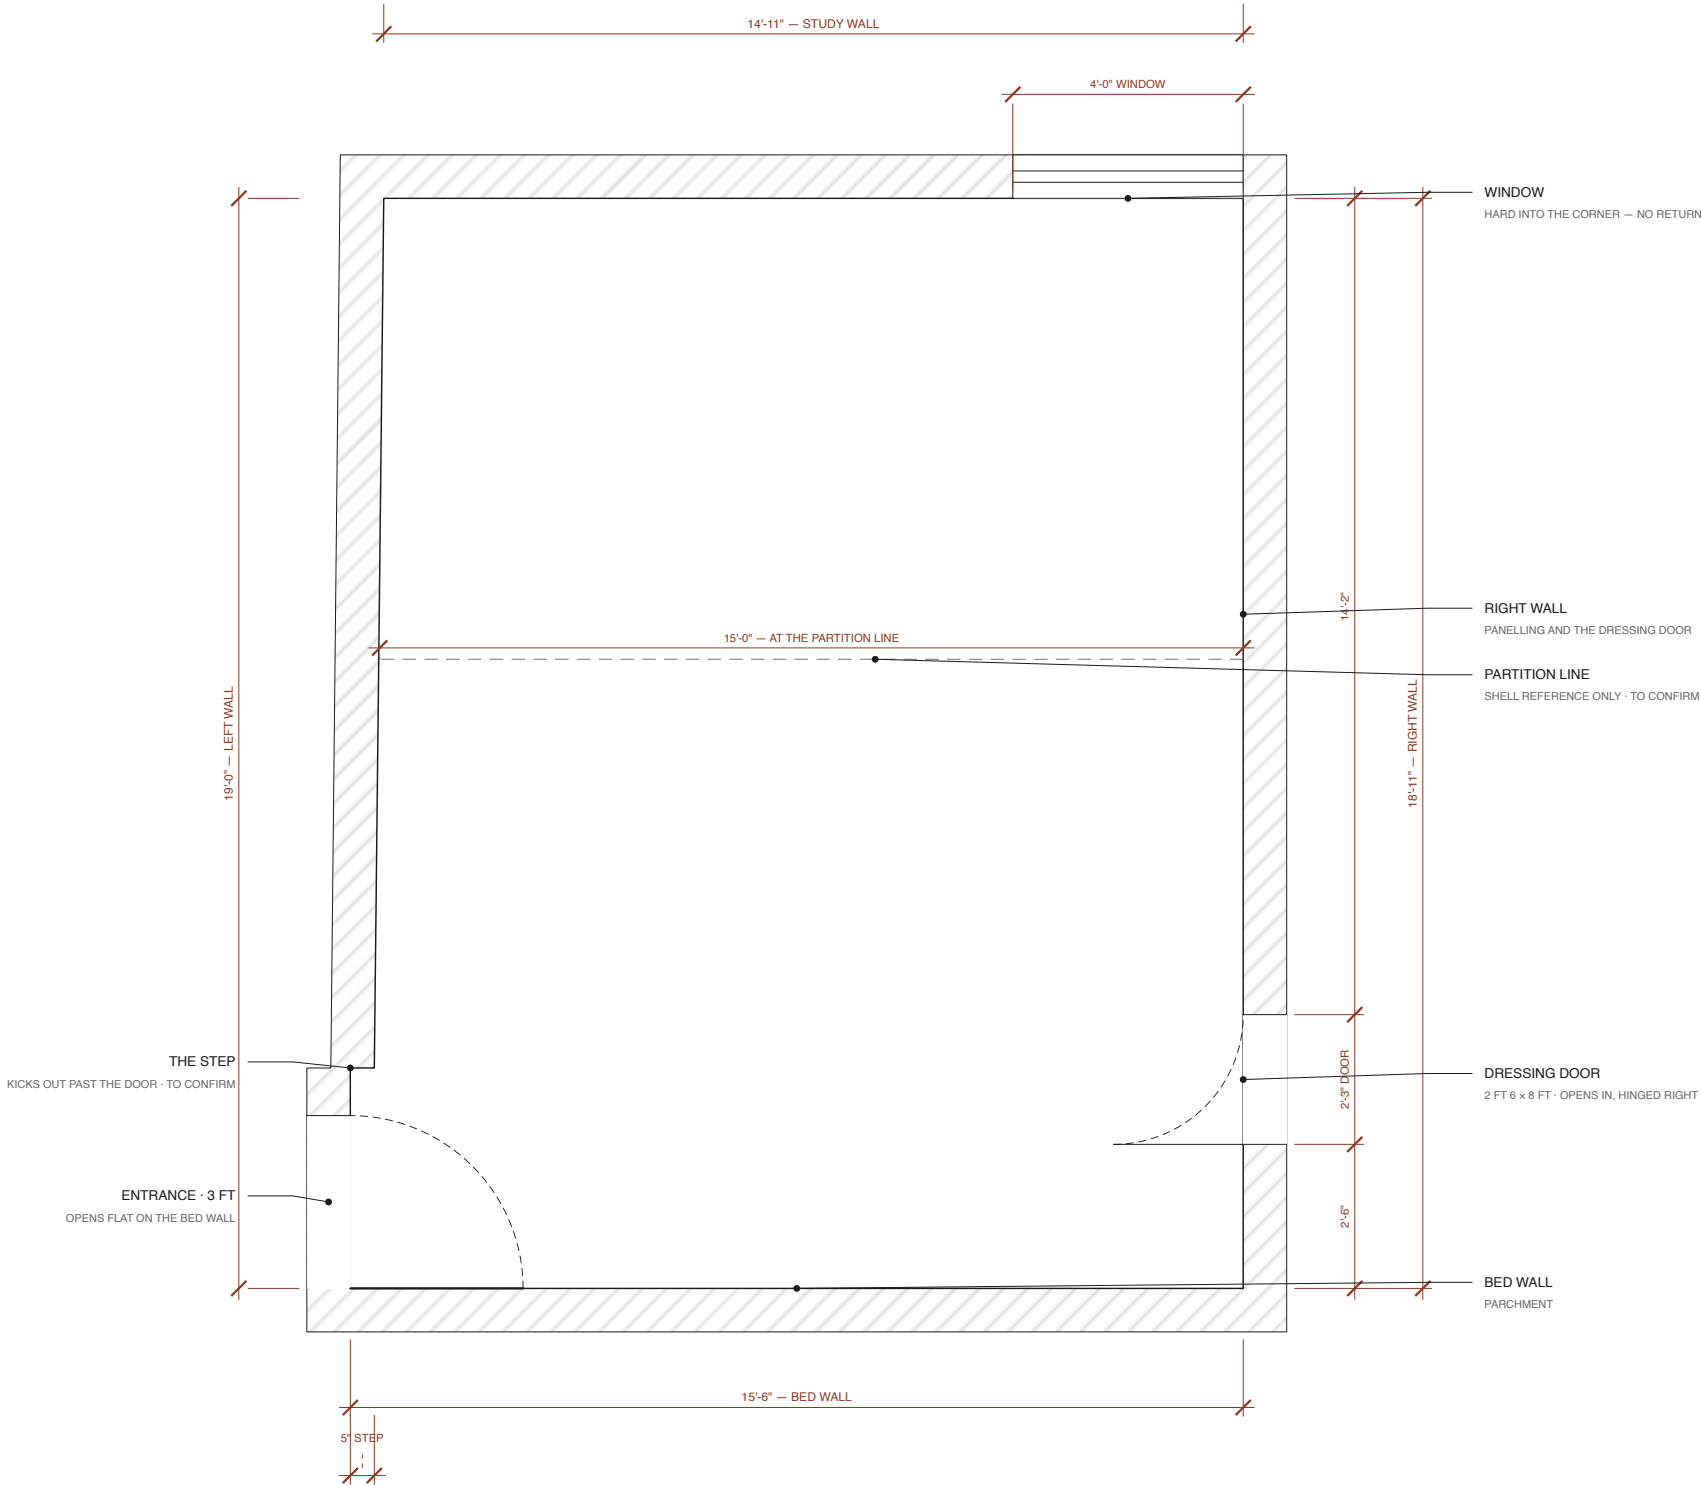

NOTES

REVISION 6

The room is not square. It widens about 2 in from the study wall to the bed wall — roughly half a degree.

Diagonals measured 24 ft 5 in and 23 ft 11 in.

Right wall — 13 ft 6 in to the door frame and 18 ft 11 in

overall are drawn exactly; the 3 ft frame and 2 ft 4 in return do not both fit with a 2 in lining. See AST-DR-007.

The right wall is taken as the straight reference; the left wall carries the splay and the step.

Ceiling 9 ft 1 in, level throughout. The main room ceiling is plain, so the splay never shows from above.

Floor, marble border and skirting are laid. Skirting runs on three walls only: bed, left and right.

Every fitted piece to be built 15–20 undersize and scribed on site to the wall it actually meets.

Furniture, partition and joinery are NOT shown.

Bathroom and dressing lie beyond the right wall — to come.

A STUDY IN TEAK

Particulars of the room

THE ROOM AS BUILT

Shell plan · measured on site

SCALE
1:40 @ A3


DATE
19.09.2026

REV
6 — the partition line at 11 ft from the bed wall, 8 ft from the study wall

DWG
AST-DR-000

D2 · D3


DRESSING AND BATHROOM · 2 FT 6 · AS AST-DR-009

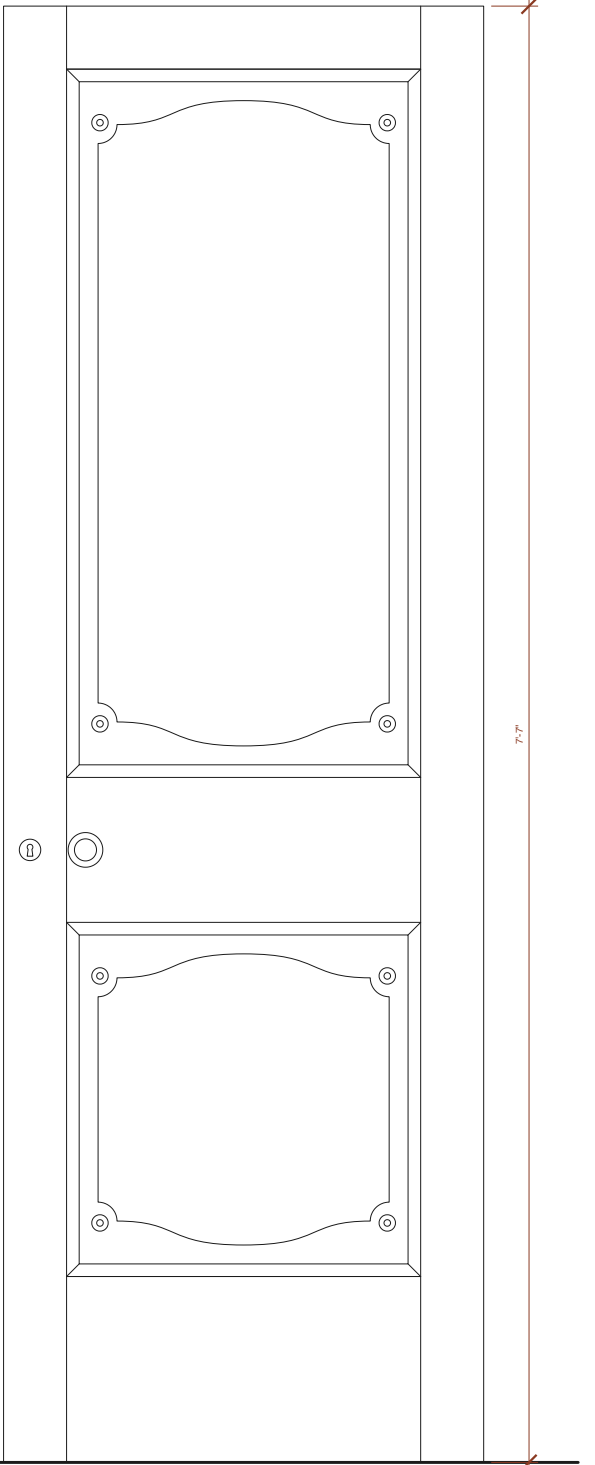

Both elevations are generated from the door sheets' own code, so the design cannot drift. Nothing on this sheet changes how the door LOOKS — only how it is made.


D1

MAIN DOOR · 3 FT · AS AST-DR-001

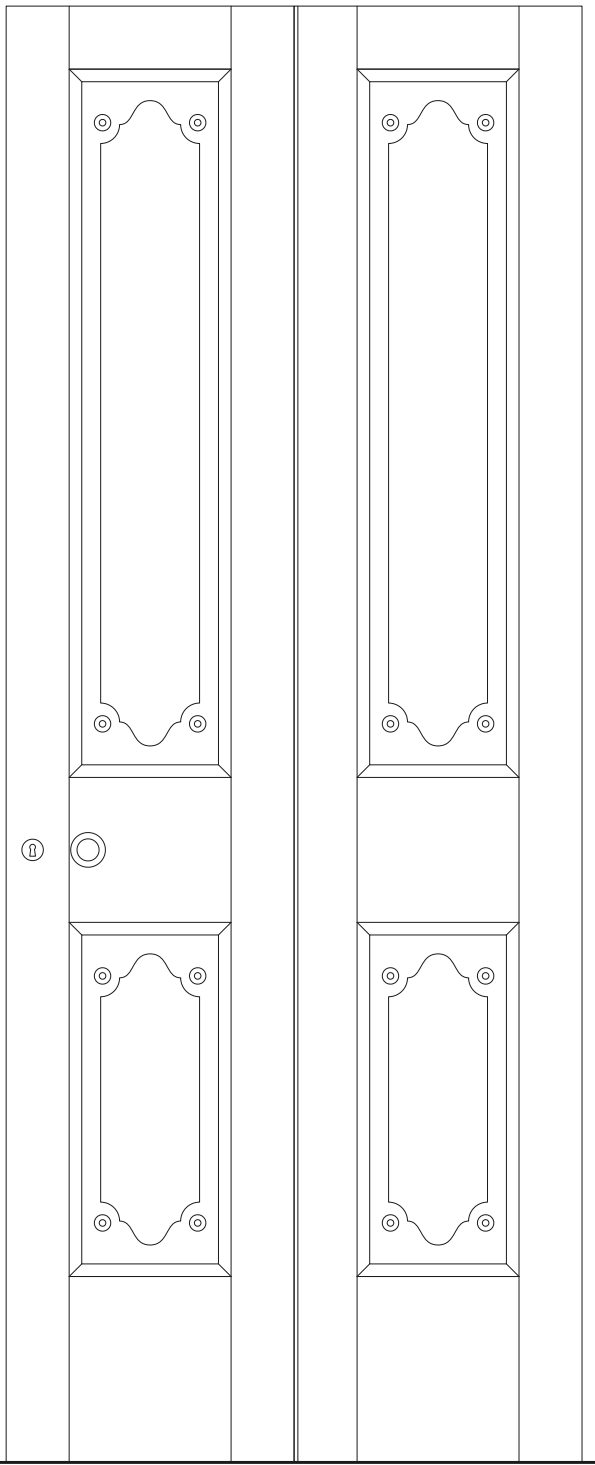

1 · THROUGH THE LEAF

SECTION ACROSS A PANEL · 1:2 · EVERY MEMBER PLANTED ON

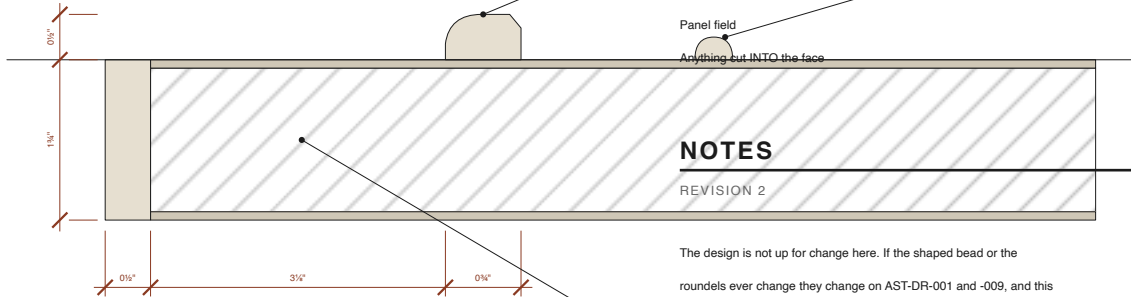

2 · WHAT CHANGES

THE SAME MEMBERS, MADE SEPARATELY AND GLUED ON

Panel field

was: sunk 13.5 into the solid
now: stays FLAT — the ovolo round it does the work
Ovolo sticking

was: worked on the stile edge
now: run as a separate 20 x 12 moulding, mitred on
Shaped bead

was: carved into the panel face
now: bandsawn to the curve in 10 x 6, planted on
Corner roundels

was: carved bosses
now: turned discs Ø26 x 5, glued on
The leaf

was: solid teak, 45
now: 38 blockboard, 12 lipping, veneer both sides

RELIEF

FACE OF THE VENEER = DATUM 0

Blockboard core	38
Veneer, each face	0.6
Solid lipping, four edges	12 WIDE
Leaf overall	45
Ovolo, planted	20 W · 12 OUT
Shaped bead, planted	10 W · 6 OUT
Roundel boss, glued on	Ø26 · 5 OUT
Panel field	FLAT · 0
Anything cut INTO the face	NONE

NOTES

REVISION 2

The design is not up for change here. If the shaped bead or the roundels ever change they change on AST-DR-001 and -009, and this sheet follows — it draws from the same code.

BLOCKBOARD CORE
Lipping is solid teak on all four edges so the leaf can be trimmed on site and the hinges and lock screw into wood, not into board.

Veneer both faces of the core and balance it: same thickness back and front, or the leaf will bow.

Ovolo, bead and bosses in solid teak, polished to match. They are small enough to take solid without moving, and they give a crisper arris than a cut face would.

Set the bead out from the panel opening, not from the leaf edge, so the four roundels land exactly on the corners of the curve.

OPEN — glue and pin, or glue only? Pins need filling and the filler shows through polish. Glue and cramp if the shop can.

A STUDY IN TEAK

Particulars of the room

DOORS — MADE IN VENEER

Same design · Planted mouldings · Construction only

SCALE

AS NOTED @ A3

DATE

23.09.2026

REV


2 — the design unchanged; only the construction differs

DWG

AST-DR-015


FRONT ELEVATION — D1

7 ft 7 in x 3 ft · PAIR OF LEAVES · SCALE 1:12

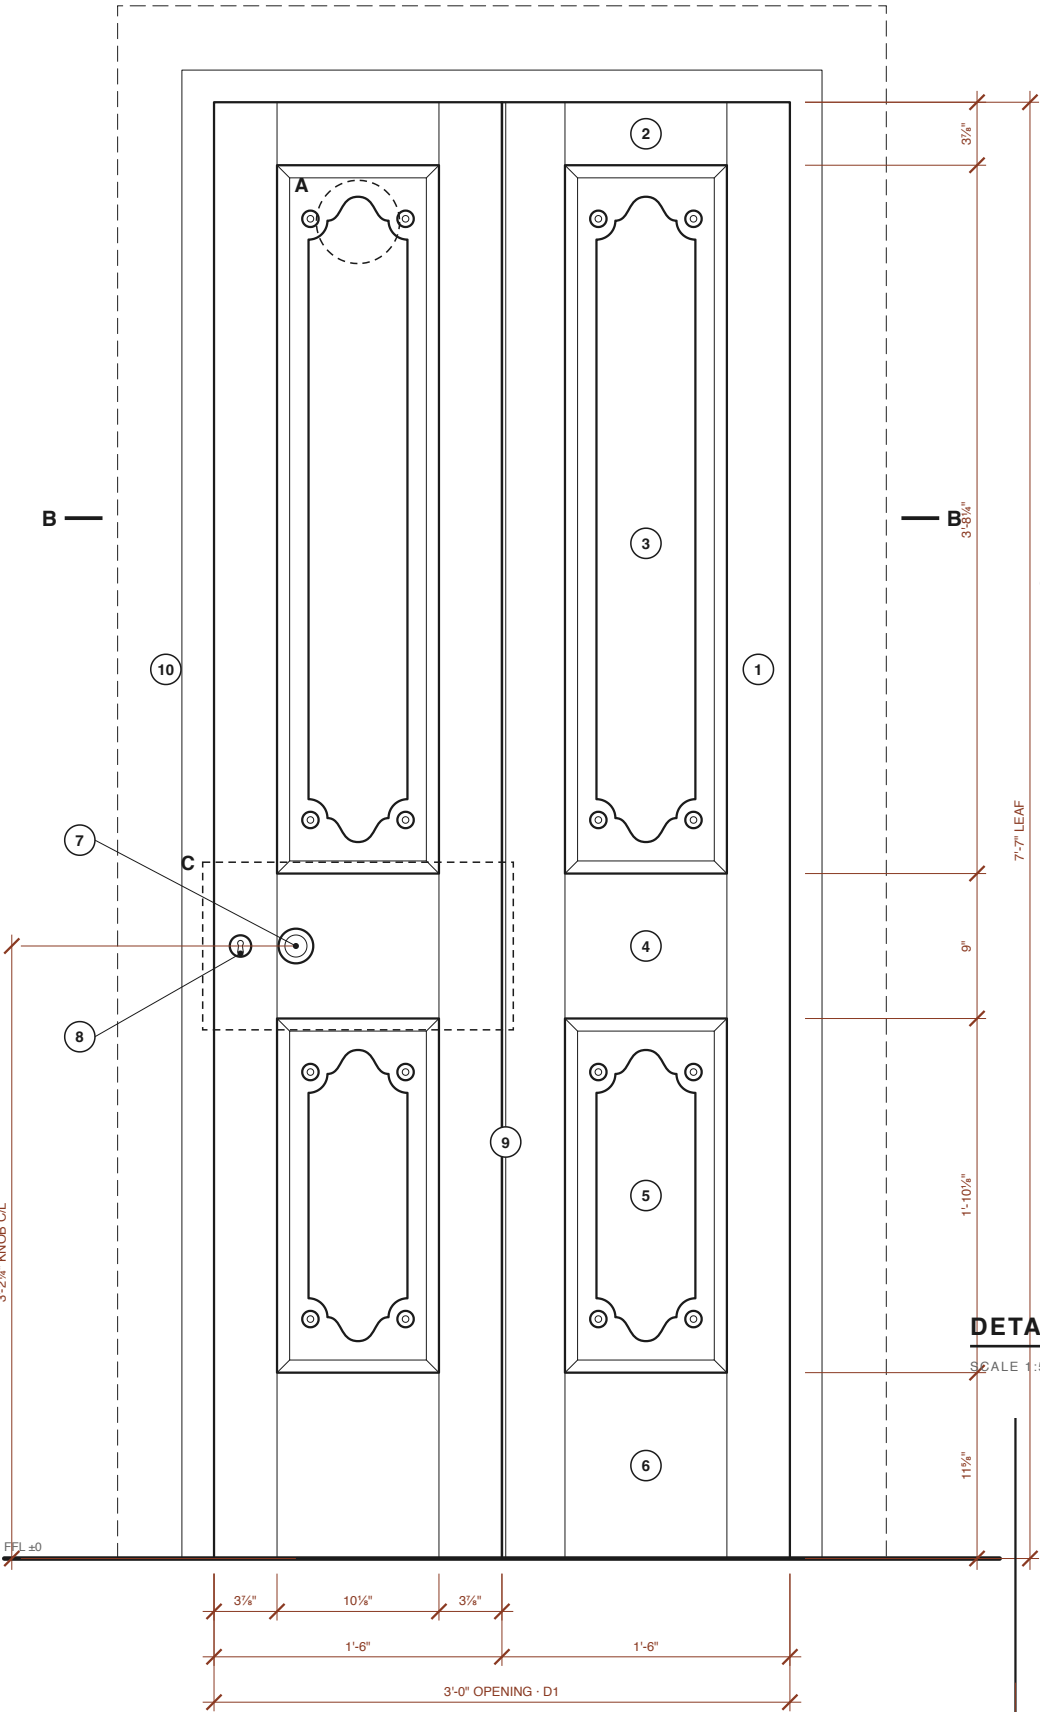


DETAIL A — PANEL HEAD

SCALE 1:2.5 · FOOT OF PANEL IS THE MIRROR

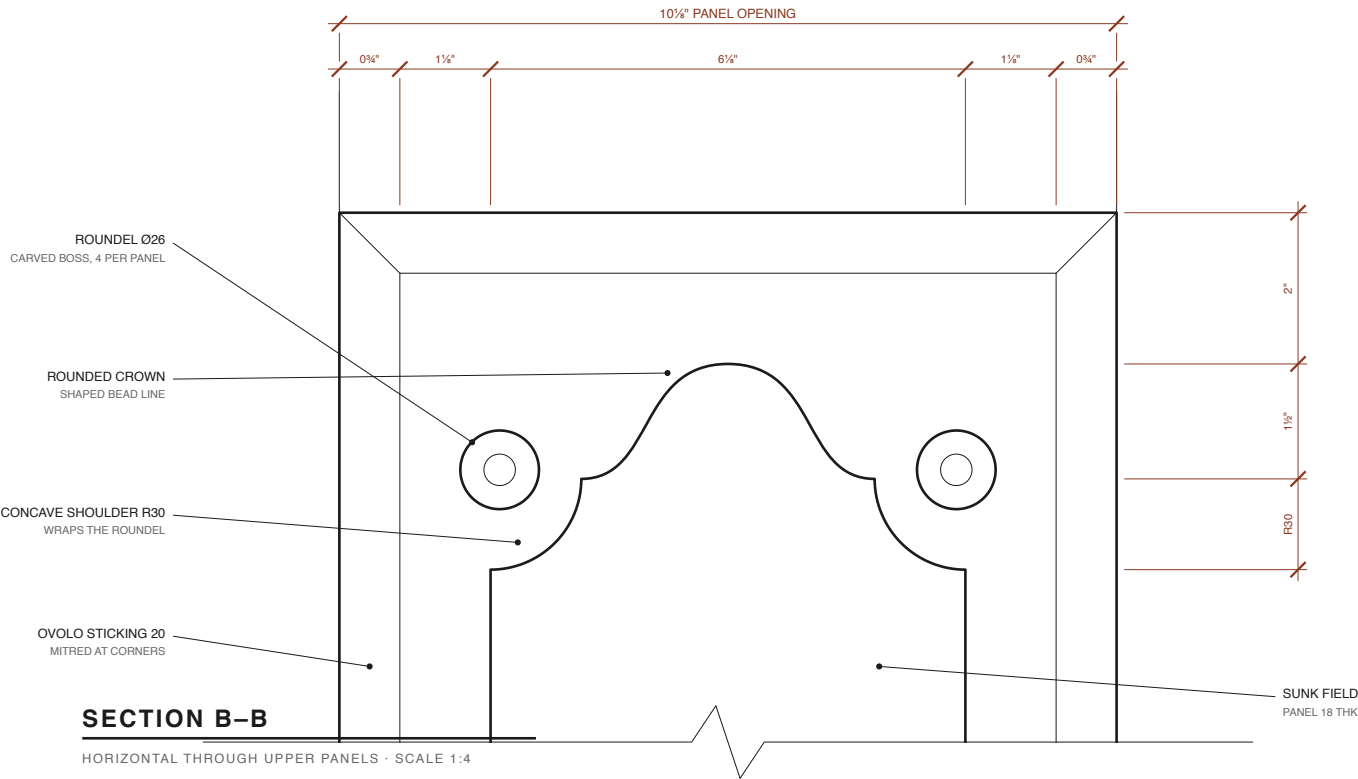


SECTION B-B

HORIZONTAL THROUGH UPPER PANELS · SCALE 1:4

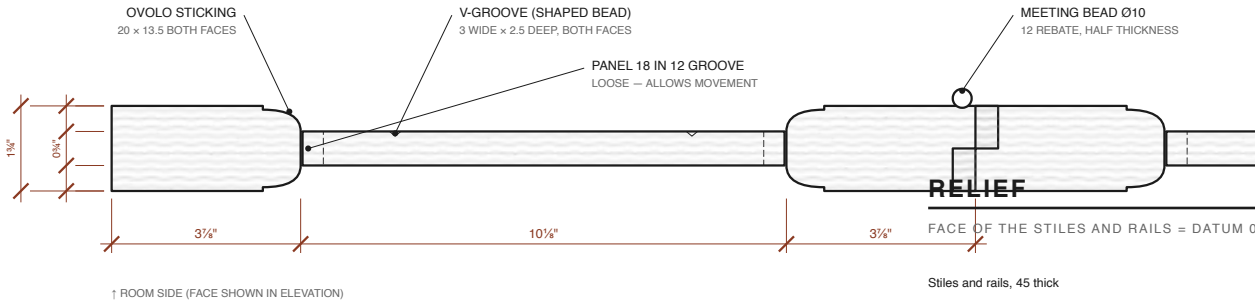

DETAIL C — LOCK RAIL

SCALE 1:5 · ACTIVE LEAF

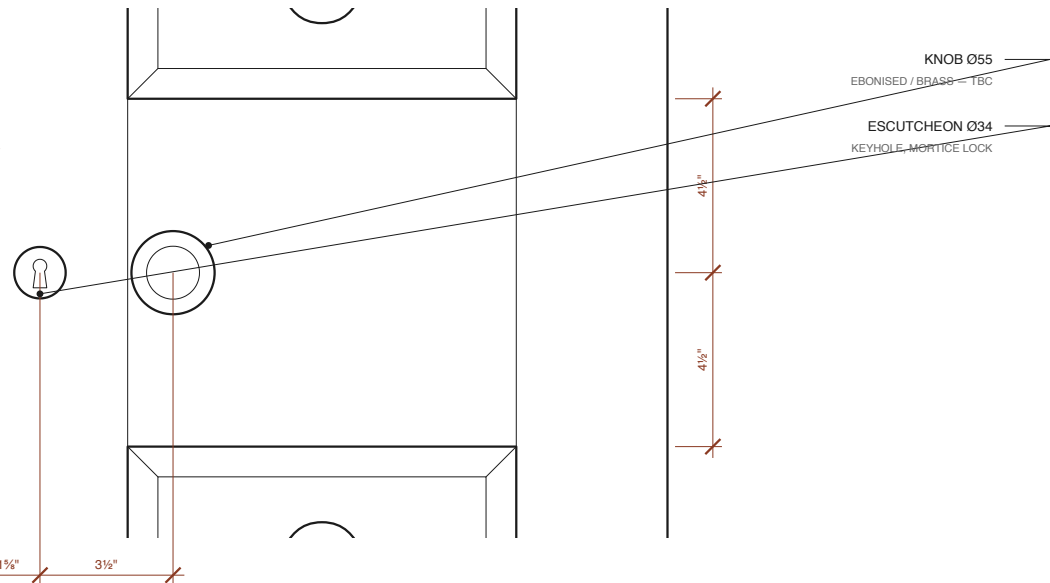

KEY

PARTS OF THE LEAF

- 1 Stile
- 2 Top rail
- 3 Upper panel — shaped bead, 4 roundels
- 4 Lock rail
- 5 Lower panel — same pattern
- 6 Bottom rail
- 7 Knob Ø55
- 8 Keyhole escutcheon
- 9 Meeting bead (pair only)
- 10 Architrave — to design

NOTES

READ BEFORE MAKING

Dimensions in feet and inches. Do not scale.

Proportions taken from a film-still reference;

leaf size, opening and thickness are ASSUMED.

Knob centre lands 958 above the floor — normal height.

D1 — MAIN DOOR, 7 ft 7 in x 3 ft.

Set out on the panel square. The 2 ft 6 leaf gives a

562 panel; the upper panel is two of those squares

(1124), the lower is one (562). Rails follow: top 100,

lock 230, bottom 295. Knob centre 972 above the floor.

Both widths take the identical rails and mouldings, so

only the panel width changes — here 257 per panel.

Solid teak frame. Veneer and polish per

Materials; polish to match the teak desk.

Casing: 2 in lining plus 4 in moulding over it, so the

moulding head sits 163 (6 in) above the leaf.

See AST-DR-011 (option A) and AST-DR-012 (option B).

Hinges and lock not yet designed.

A STUDY IN TEAK

Particulars of the room

DOOR D1 — 7 FT 7 IN x 3 FT

Elevation · Panel head · Section · Lock rail

SCALE

AS NOTED @ A3

REV

6 — set out on the panel square: upper two squares, lower one

DATE


17.09.2026

DWG

AST-DR-001


FRONT ELEVATION — D2 · D3

7 ft 7 in x 2 ft 6 in · SINGLE LEAF · SCALE 1:12

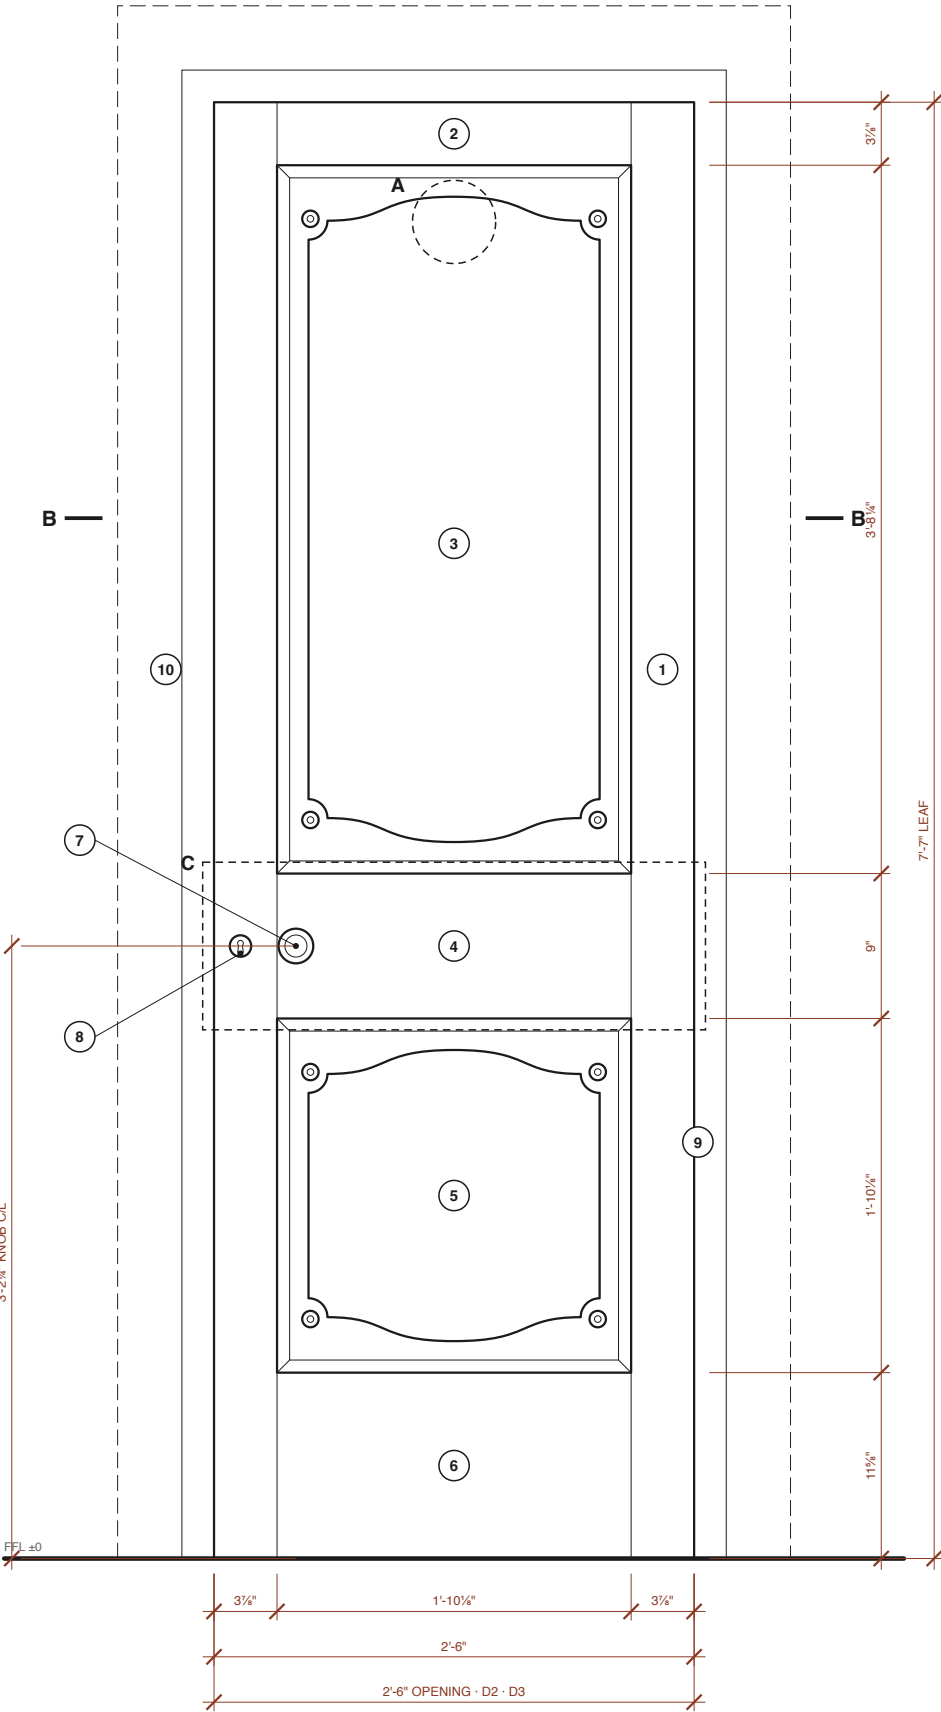


DETAIL A — PANEL HEAD

SCALE 1:5 · FOOT OF PANEL IS THE MIRROR

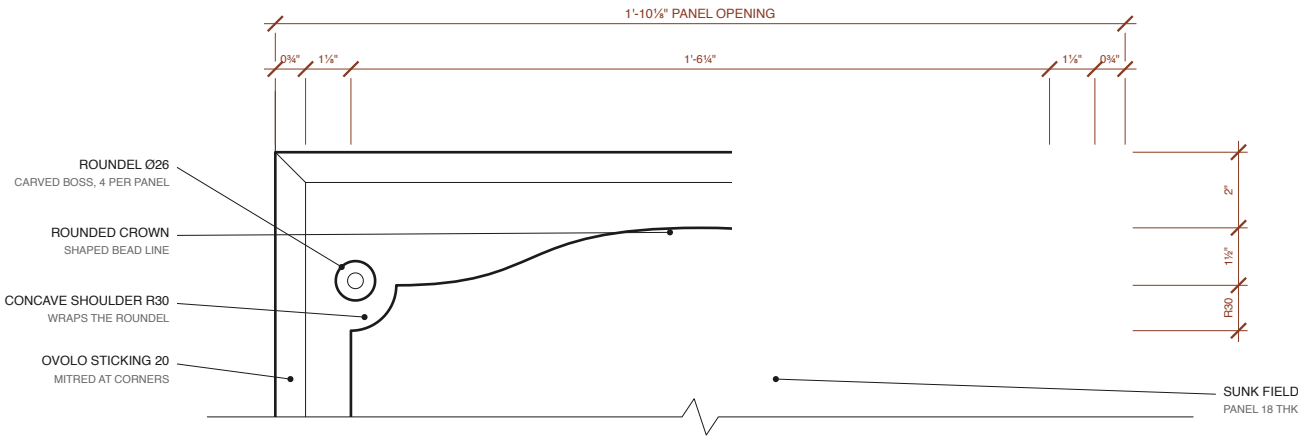


SECTION B-B

HORIZONTAL THROUGH UPPER PANELS · SCALE 1:6

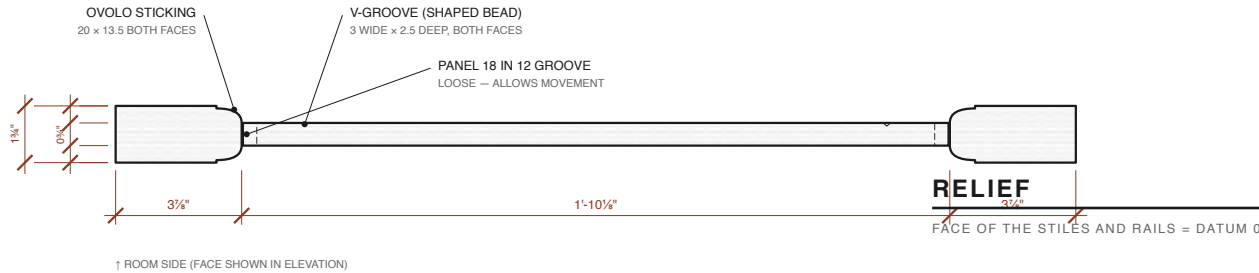

DETAIL C — LOCK RAIL

SCALE 1:8 · ACTIVE LEAF

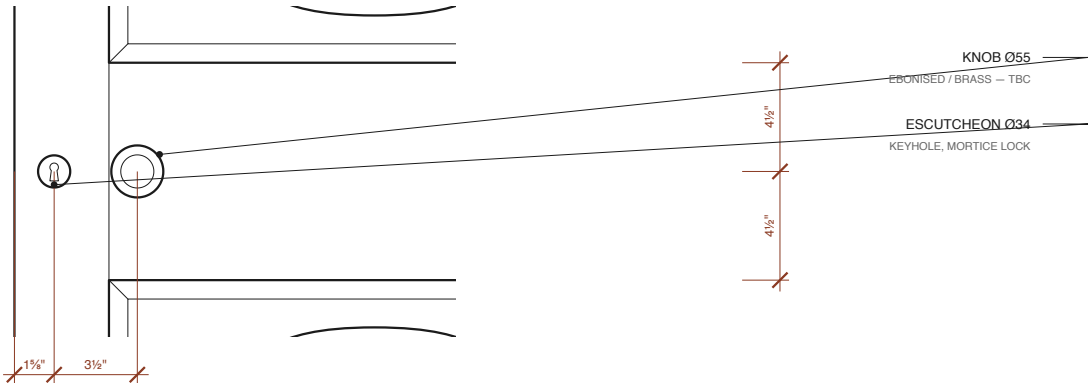

KEY

PARTS OF THE LEAF

- 1 Stile
- 2 Top rail
- 3 Upper panel — shaped bead, 4 roundels
- 4 Lock rail
- 5 Lower panel — same pattern
- 6 Bottom rail
- 7 Knob Ø55
- 8 Keyhole escutcheon
- 9 Meeting bead (pair only)
- 10 Architrave — to design

NOTES

READ BEFORE MAKING

Dimensions in feet and inches. Do not scale.

Proportions taken from a film-still reference;

leaf size, opening and thickness are ASSUMED.

Knob centre lands 958 above the floor — normal height.

D2 · D3 — DRESSING · BATHROOM, 7 ft 7 in x 2 ft 6 in.

Set out on the panel square. The 2 ft 6 leaf gives a

562 panel; the upper panel is two of those squares

(1124), the lower is one (562). Rails follow: top 100,

lock 230, bottom 295. Knob centre 972 above the floor.

Both widths take the identical rails and mouldings, so

only the panel width changes — here 562 per panel.

Solid teak frame. Veneer and polish per

Materials; polish to match the teak desk.

Casing: 2 in lining plus 4 in moulding over it, so the

moulding head sits 153 (6 in) above the leaf.

See AST-DR-011 (option A) and AST-DR-012 (option B).

Hinges and lock not yet designed.

A STUDY IN TEAK

Particulars of the room

DOOR D2 · D3 — 7 FT 7 IN x 2 FT 6 IN

Elevation · Panel head · Section · Lock rail

SCALE

AS NOTED @ A3

REV

6 — set out on the panel square: upper two squares, lower one

DATE


17.09.2026

DWG

AST-DR-009


DRESSING DOOR

D2 · 2 FT 6 · THE CARVED HEAD · 1:20

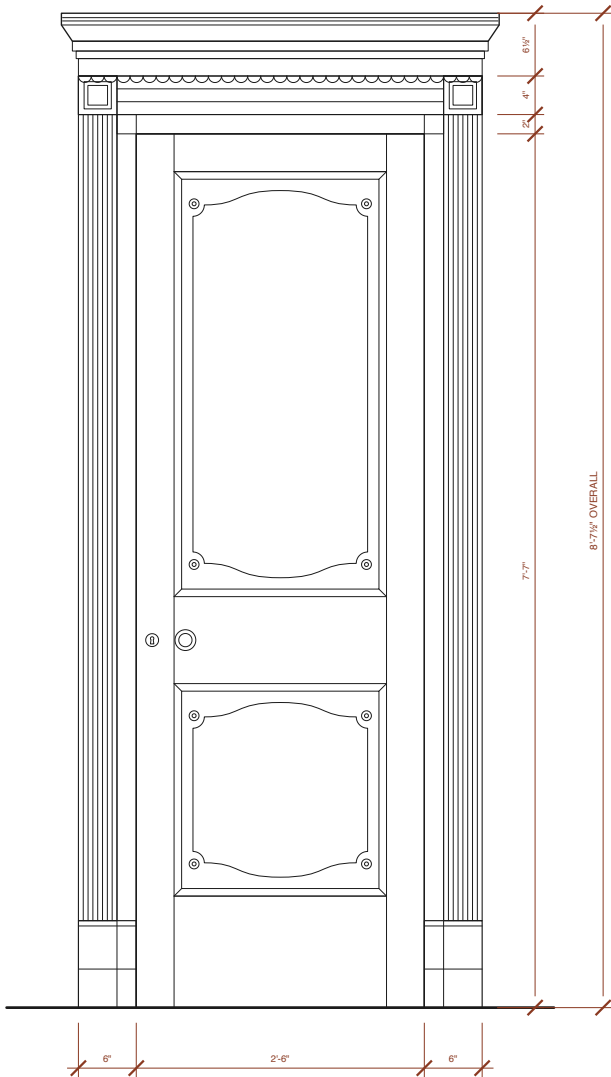


MAIN AND BATHROOM

D1 3 FT · D3 2 FT 6 · PLAIN CASING · 1:20

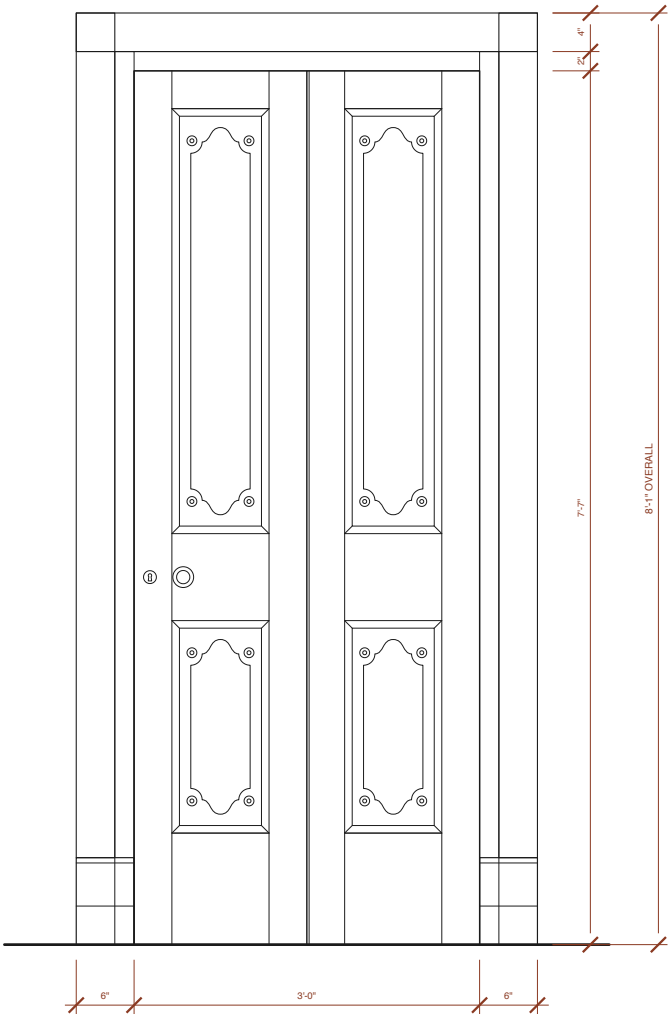


1 · THE HEAD

DRESSING DOOR · LEFT END · 1:4 · LINING, MOULDING, SCALLOPS, CROWN

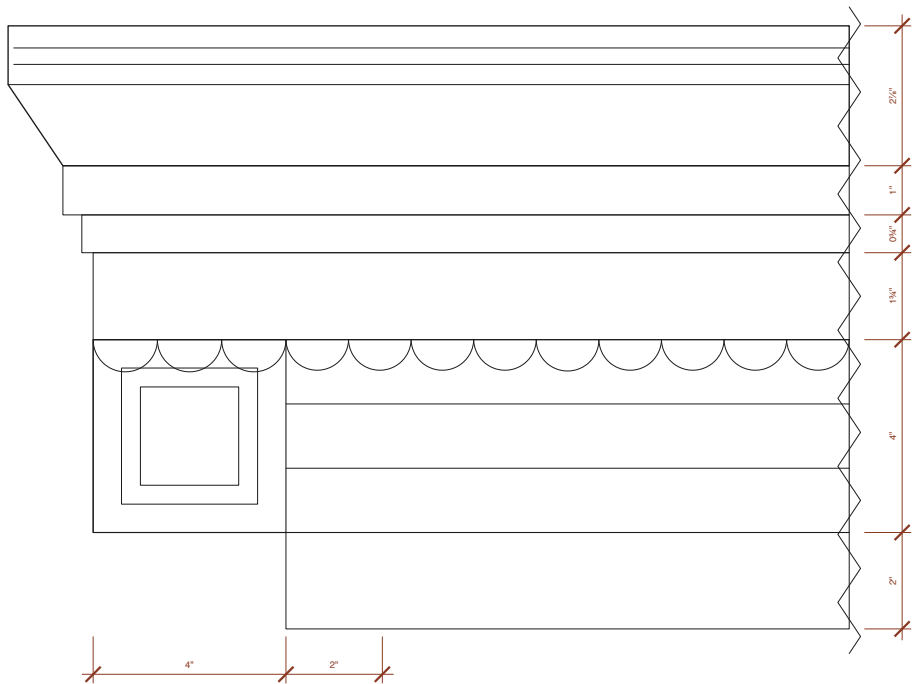


2 · SECTION

THROUGH THE HEAD · 1:4

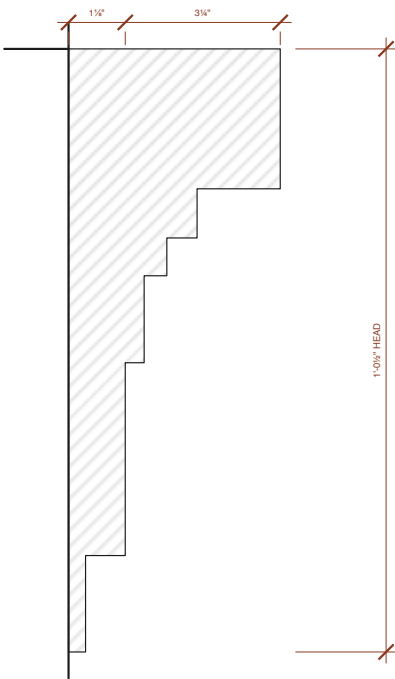


3 · JAMB

SECTION · 1:4 · 6 IN ON THE FACE

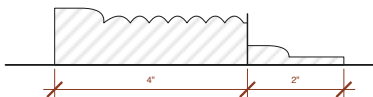

4 · PLINTH

AT THE FOOT · 1:10

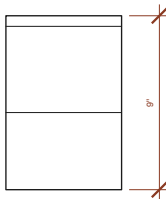

NOTES

REVISION 8

The lining is 2 in on the face. The moulding lays 4 in outside it, all round — so the jambs are 6 in wide, and over the opening the moulding head sits 6 in ABOVE the leaf, not on top of it.

The jambs are reeded. Across the head the moulding is STEPPED, not reeded — the reference has no reeding there.

A plinth block takes each jamb down over the marble skirting.

RELIEF

DATUM 0 = FACE OF THE PLASTER · LINING AND MOULDING ARE COMMON TO ALL THREE DOORS · THE REST IS THE DRESSING DOOR'S CARVED HEAD

Lining, 2 in on the face	6 OUT	Scallop course	40 OUT
Moulding, 4 in, reeded	30 OUT	Scallops, cut back from its face	5 IN
Reed grooves in the moulding face	3 IN	Small mouldings, over the scallops	52 AND 68 OUT
Corner block, flush with the moulding	30 OUT	Crown, the widest member	112 OUT
Its sunk panel, two steps	6 AND 10 IN	Plinth block, so the moulding dies on it	34 OUT

Above the moulding, and only above it: a course of scallops, two small mouldings, and a crown that mitres back at each end.

A 4 in square block at each corner, with a small sunk moulding inside it, ties head to jamb; the scallops run in three runs so a joint lands on each block edge. The crown lands at 2630 (8 ft 8 in).

The carved head is the DRESSING door's alone. Main and bathroom take the same lining and moulding, run straight across and stopped.

A STUDY IN TEAK

Particulars of the room

DOOR CASINGS

Carved head — dressing only · Plain elsewhere · Sections

SCALE
AS NOTED @ A3


DATE
19.09.2026

REV
8 — carved head: dressing door only

DWG
AST-DR-011

DRESSING DOOR

OPTION B · D2 · 2 FT 6 · THE CARVED HEAD · 1:20

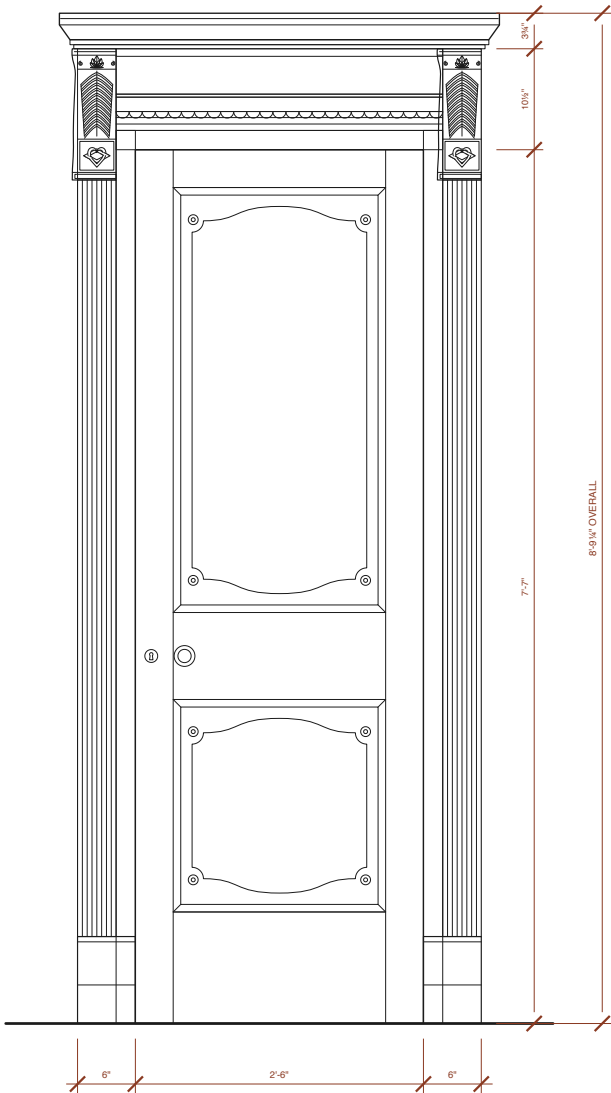

NOTES


OPTION B · REVISION 2

This is the alternative to AST-DR-011. Below the corbels the two are the same casing: a 2 in lining with a 4 in reeded moulding outside it, a plinth block at the foot, the same leaf.

What changes is the head. Option A closes the corner with a moulded square block. Option B carries it on a carved corbel and lets the architrave, scallops and frieze die into it.

MAIN AND BATHROOM


D1 3 FT · D3 2 FT 6 · PLAIN CASING · 1:20

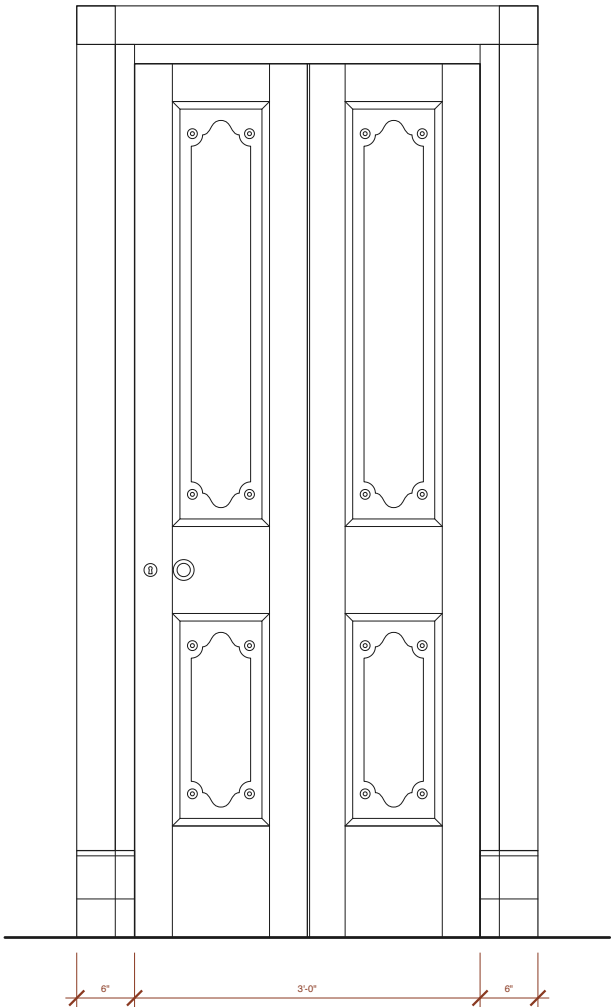

Each corbel is one piece, standing 14 proud of the casing on the wall side with a serpentine edge: a palmette under a small cap, eleven chevrons on a spine, and a shield knot woven through a lozenge at the foot. Dressing door only — the others go plain. The crown lands at 2672 — 3 in higher than Option A — leaving about 4 in of wall to the ceiling.


1 · THE CORBEL

ELEVATION · 1:2 · THE DRESSING DOOR ONLY

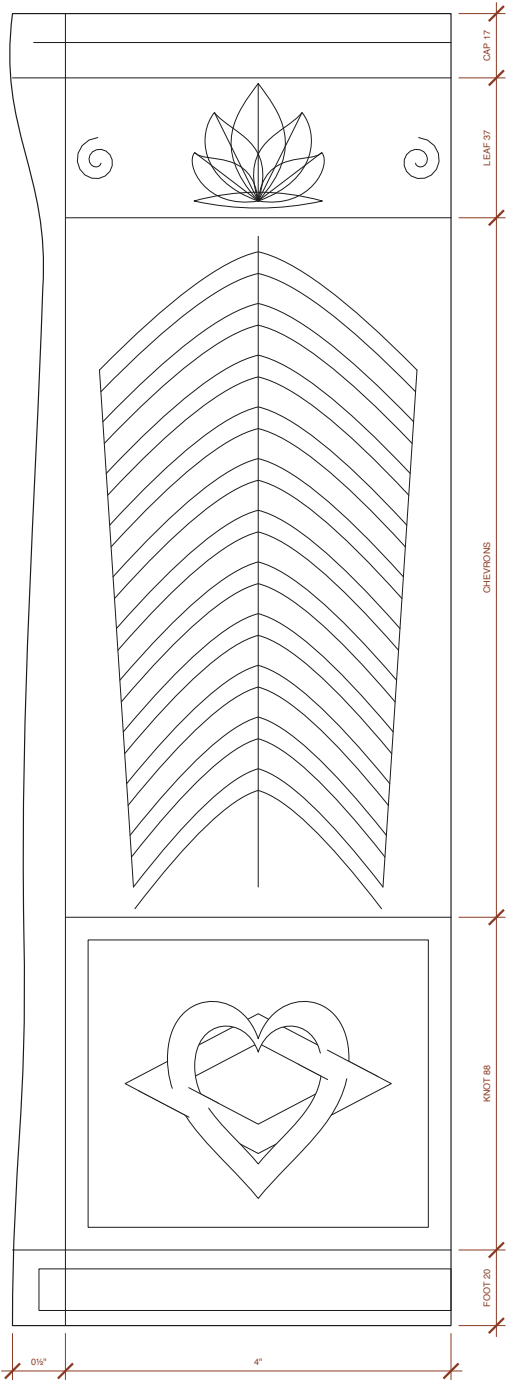


2 · THE LEAF

PALMETTE · 1:1.5

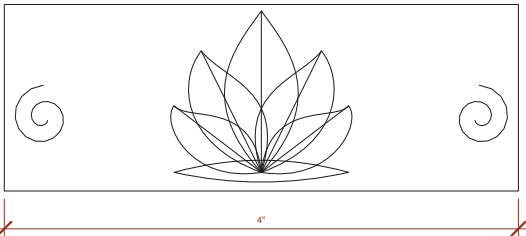


3 · THE KNOT

INTERLACE · 1:1.5

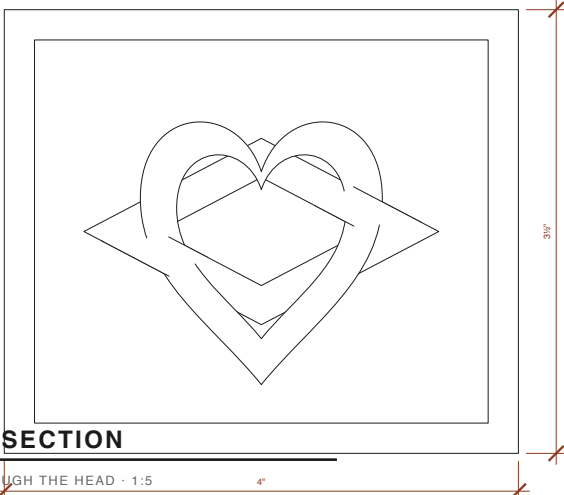

4 · SECTION

THROUGH THE HEAD · 1:5

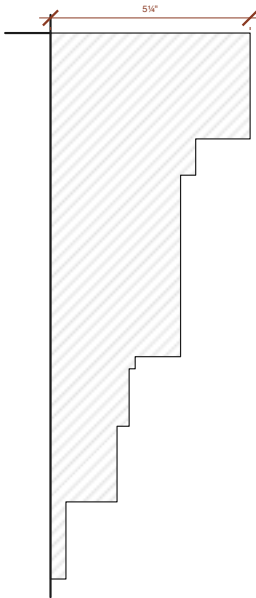

A STUDY IN TEAK

Particulars of the room

DOOR CASINGS — OPTION B

Carved corbels · Palmette · Chevrons · Knot

SCALE

AS NOTED @ A3

DATE

19.09.2026

REV


2 — carved head: dressing door only

DWG

AST-DR-012


FRONT ELEVATION

SCALE 1:20

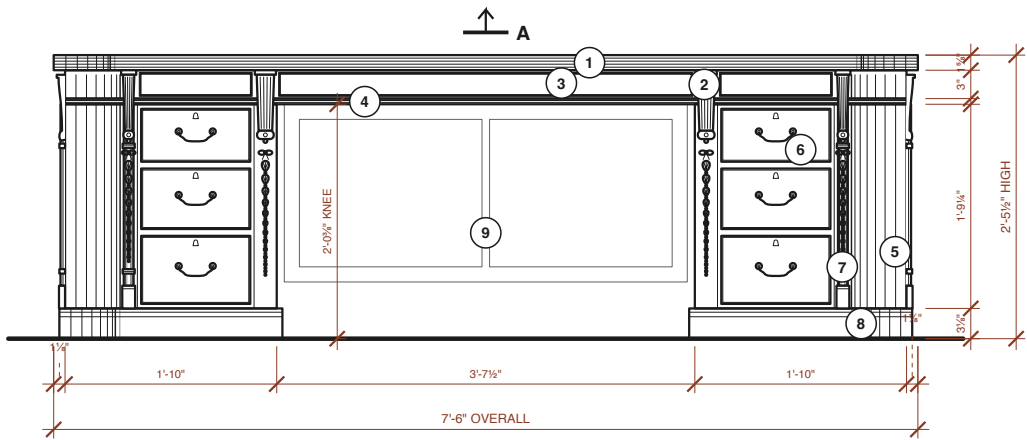


LEFT END ELEVATION

SCALE 1:20 · FRONT →

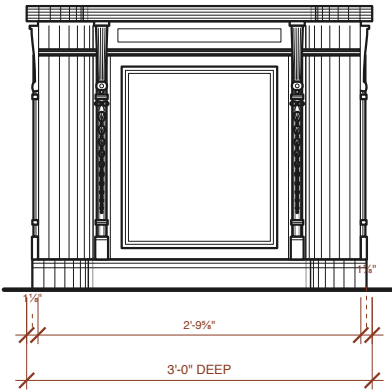


SECTION A-A

THROUGH KNEEHOLE · 1:12 · FRONT ←

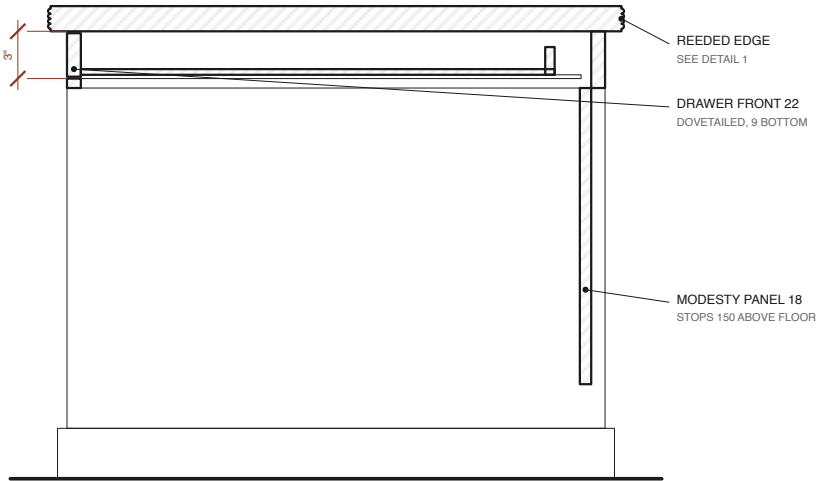


PLAN

SCALE 1:20 · FRONT AT BOTTOM

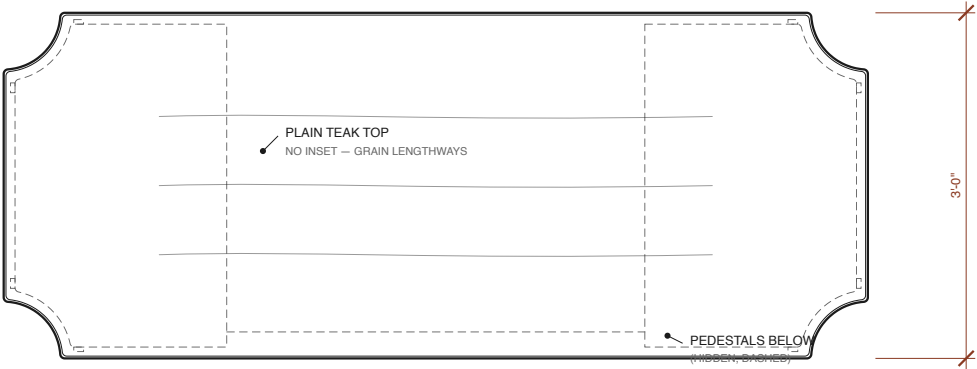


BACK ELEVATION

SCALE 1:20 · IF FREE-STANDING

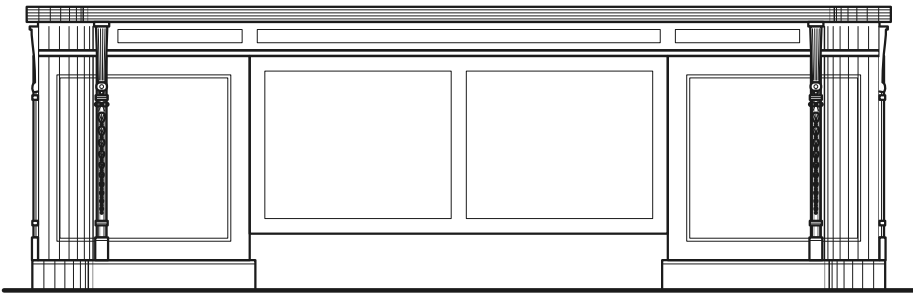

AXONOMETRIC

NOT TO SCALE · FROM FRONT RIGHT

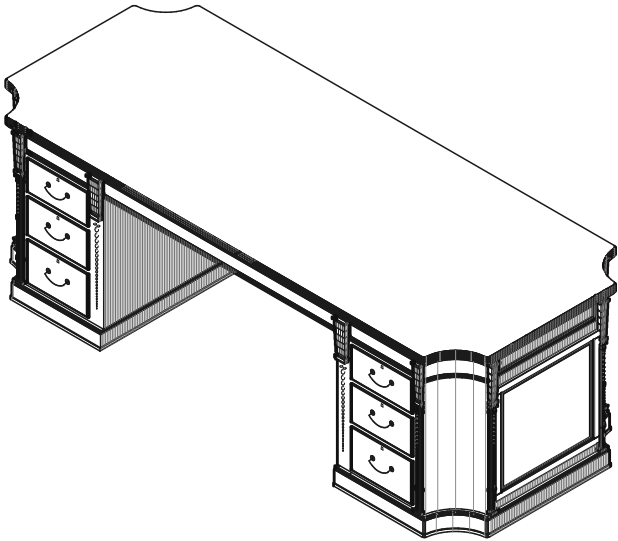

KEY

PARTS OF THE DESK

- 1 Top — plain teak, reeded edge
- 2 Reeded console bracket
- 3 Frieze drawer, push-to-open
- 4 Reeded rail
- 5 Hollow corner, moulding at each end of the curve
- 6 Pedestal — three drawers each side
- 7 Swan-neck handle + keyhole, every drawer
- 8 Moulded plinth
- 9 Modesty panel in kneehole

NOTES

READ BEFORE MAKING

Dimensions in feet and inches. Do not scale.
Length 7 ft 6 in and depth 3 ft confirmed.
Height 750 set for a 5 ft 9 in user.
Solid teak throughout; polish sets the room finish.
Three graduated drawers in each pedestal.
Hollowed corners; moulding strip at both curve ends.
Carving shown schematically — carver to work from reference and Details sheet.
A square-cornered version of this desk is drawn on AST-DR-028 for a carpenter who cannot make the hollows.
First-angle projection.

A STUDY IN TEAK

Particulars of the room

DESK — GENERAL ARRANGEMENT

Front · End · Section · Plan · Back · Axo

SCALE
AS NOTED @ A3


DATE
17.09.2026

REV
9 — plain teak top, gold on handles only

DWG
AST-DR-002


1 · TOP EDGE

SECTION · SCALE 1:1

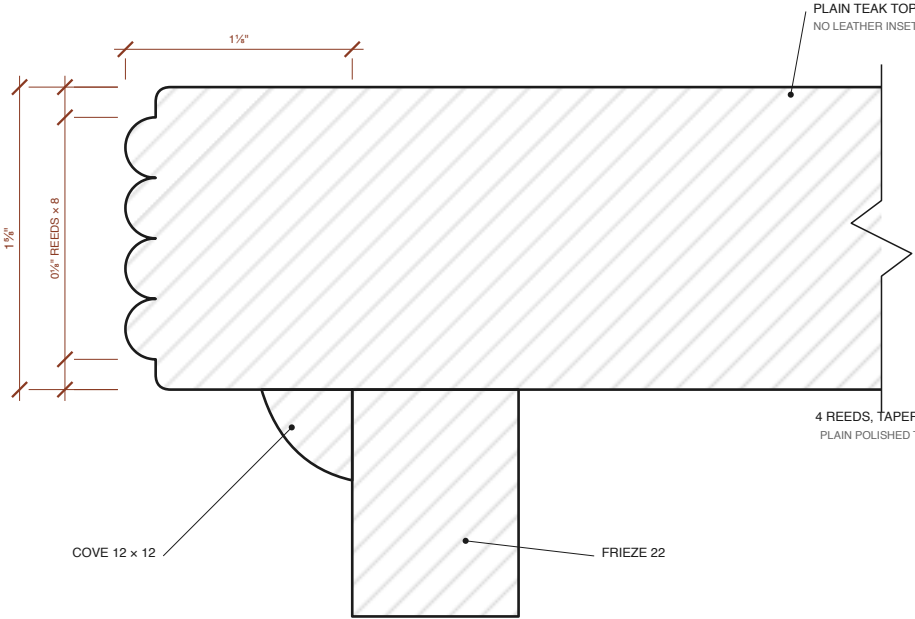


2 · DRAWER RAIL

SECTION · SCALE 1:1

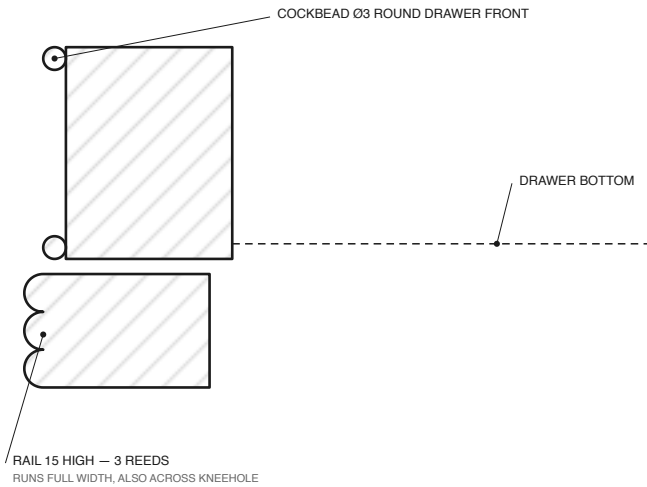


8 · CORNER — HOLLOW + END MOULDINGS

PLAN · SCALE 1:4 · ALL FOUR CORNERS · CURVES SHARE ONE CENTRE

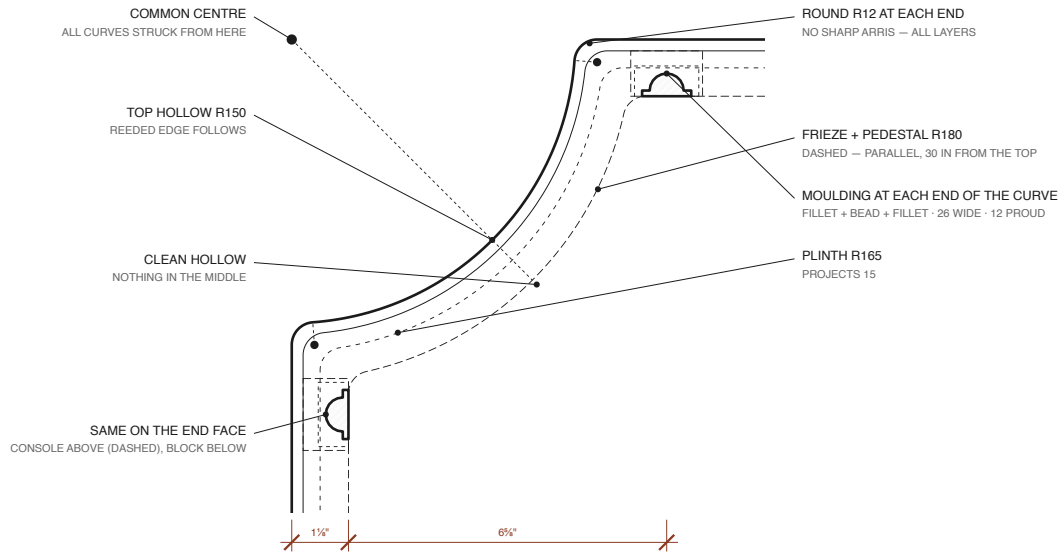


3 · CONSOLE BRACKET

FRONT + SIDE · 1:2.5 · 50 WIDE AT KNEEHOLE, 34 ON CORNERS

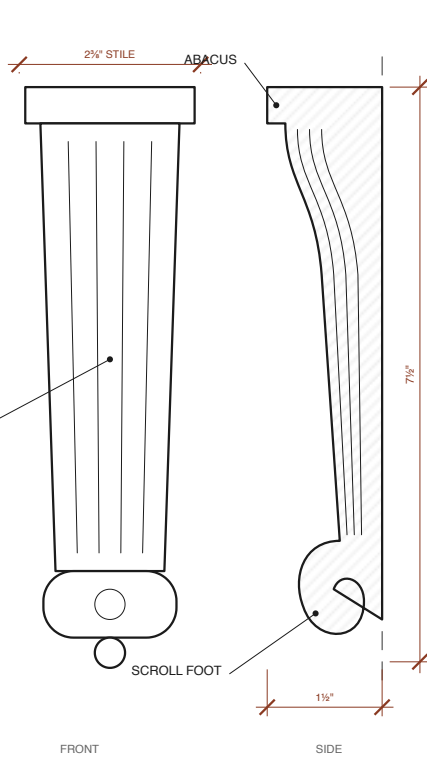


7 · PLINTH

SECTION · SCALE 1:2

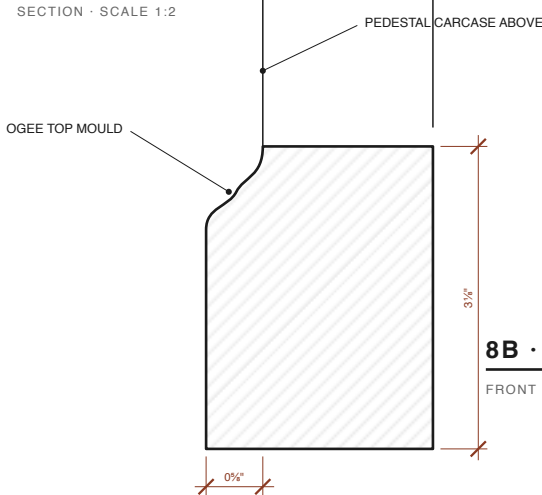


4 · CARVED DROP

KNEEHOLE STILE · SCALE 1:4

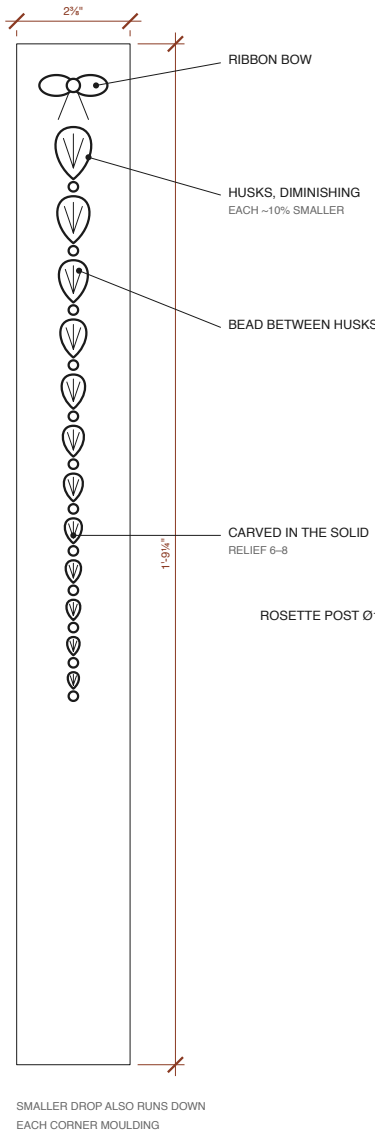


8B · CORNER ELEVATION

FRONT LEFT CORNER · SCALE 1:10

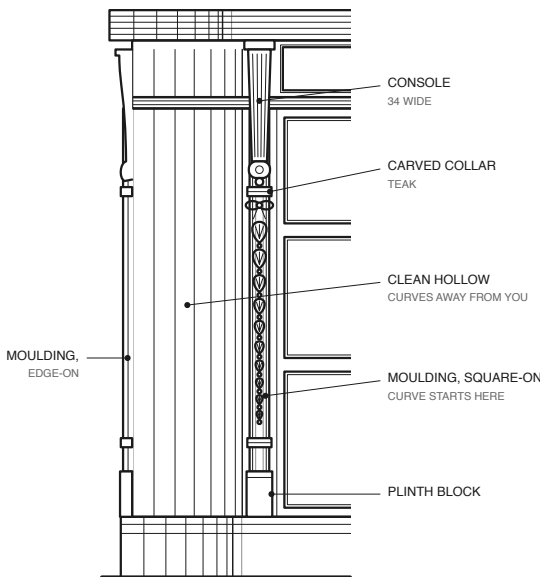


5 · PEDESTAL DRAWERS

RIGHT PEDESTAL FRONT · SCALE 1:10 · THREE EACH SIDE

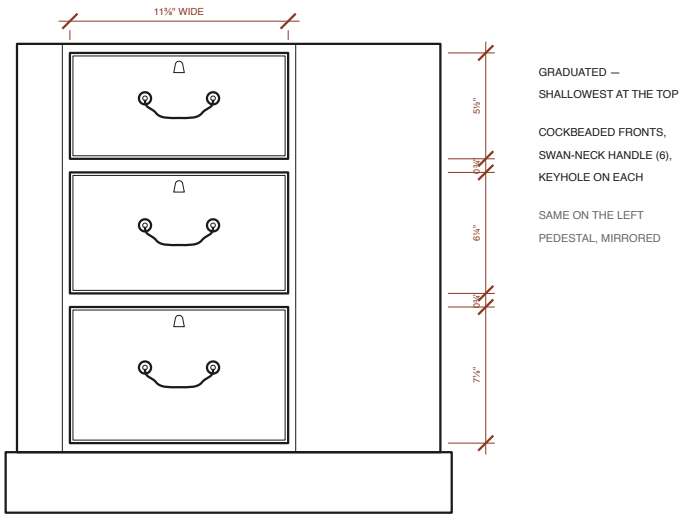

6 · DRAWER HANDLE

ELEVATION · SCALE 1:1

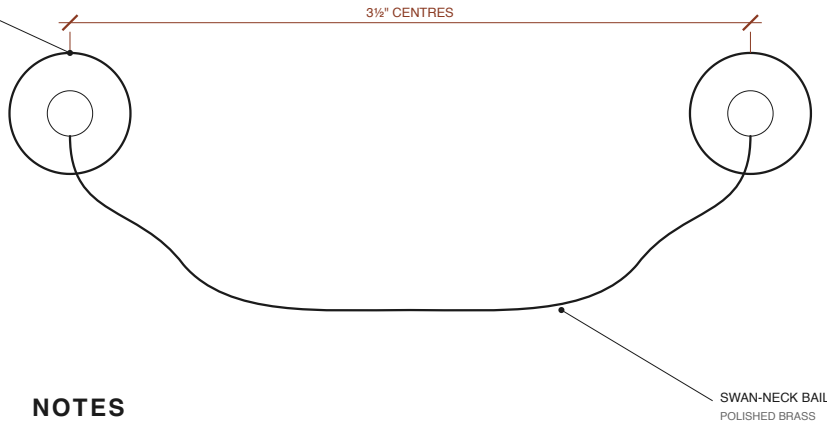

NOTES

DETAILS

Profiles are drawn from film stills and are indicative;

the joiner to prepare a full-size mock-up of 1, 2 and 7.

Carving (4, 5): carver to work from the reference photos;

sample one drop before carving the set.

Hardware (6): standard 90 mm swan-neck, solid brass.

Gold/brass on handles and ring pulls only; rest plain teak.

Corners: clean R150 hollow, moulding at both ends (8, 8B).

Cut a card template of the hollow to confirm.

A STUDY IN TEAK

Particulars of the room

DESK — DETAILS

Edge · Rail · Console · Drop · Ornament · Handle · Plinth · Corner

SCALE

AS NOTED @ A3

REV

9 — plain teak top, gold on handles only

DATE


17.09.2026

DWG

AST-DR-003

FROM THE FRONT RIGHT

AXONOMETRIC · APPROX 1:14 · HIDDEN LINES REMOVED · SHADED

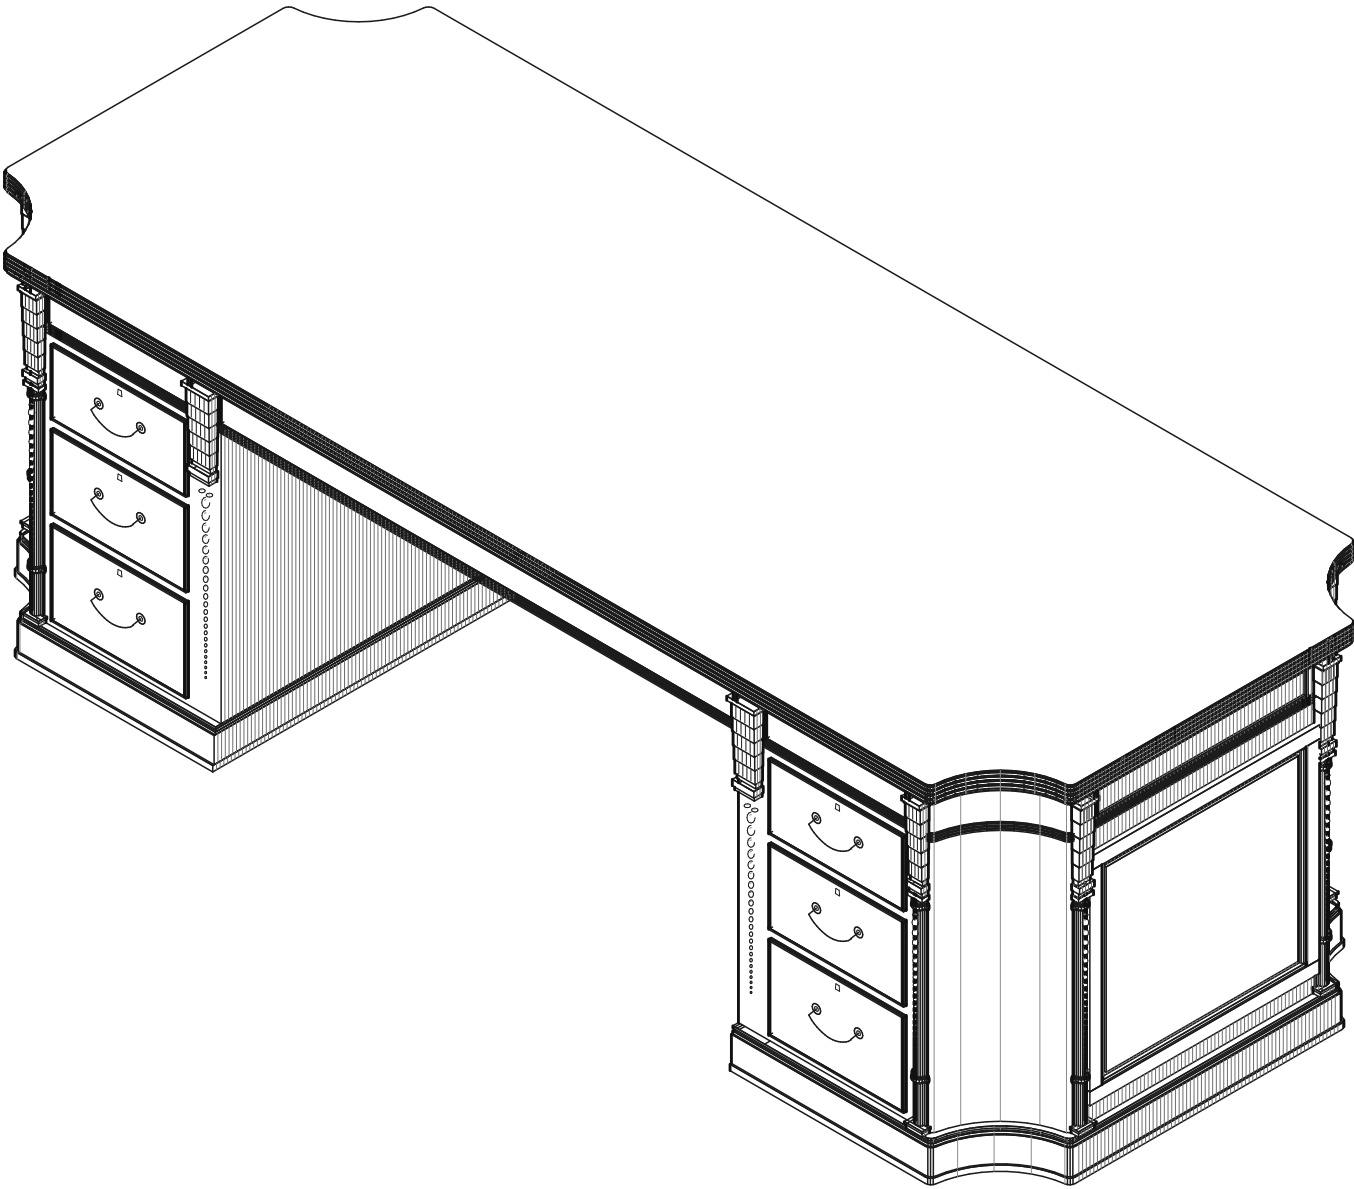


NOTES

3D VIEWS

Generated from the same geometry as the plan and elevations —
any change to sizes, hollows or mouldings updates every view.
Carving and handles shown simplified; see AST-DR-003.
Axonometric: measure along the three axes only.


FROM THE BACK LEFT

AXONOMETRIC · APPROX 1:29 · IF FREE-STANDING

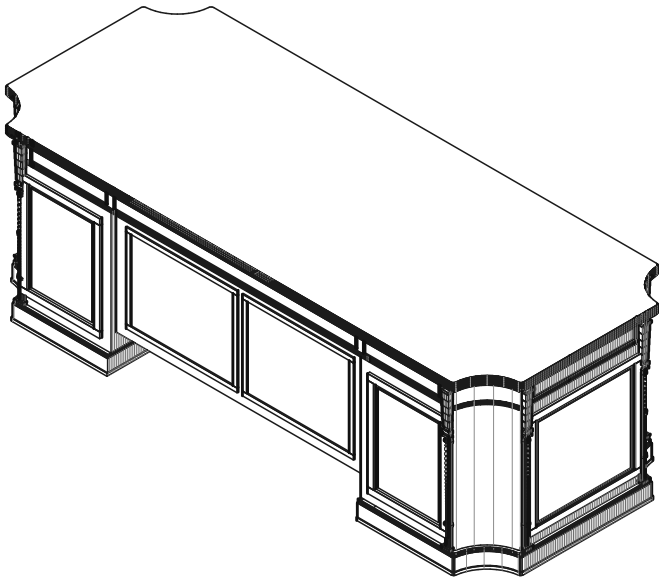

CORNER CLOSE-UP

FRONT RIGHT · APPROX 1:4 · HOLLOW, ROUNDS, END MOULDINGS, CONSOLES

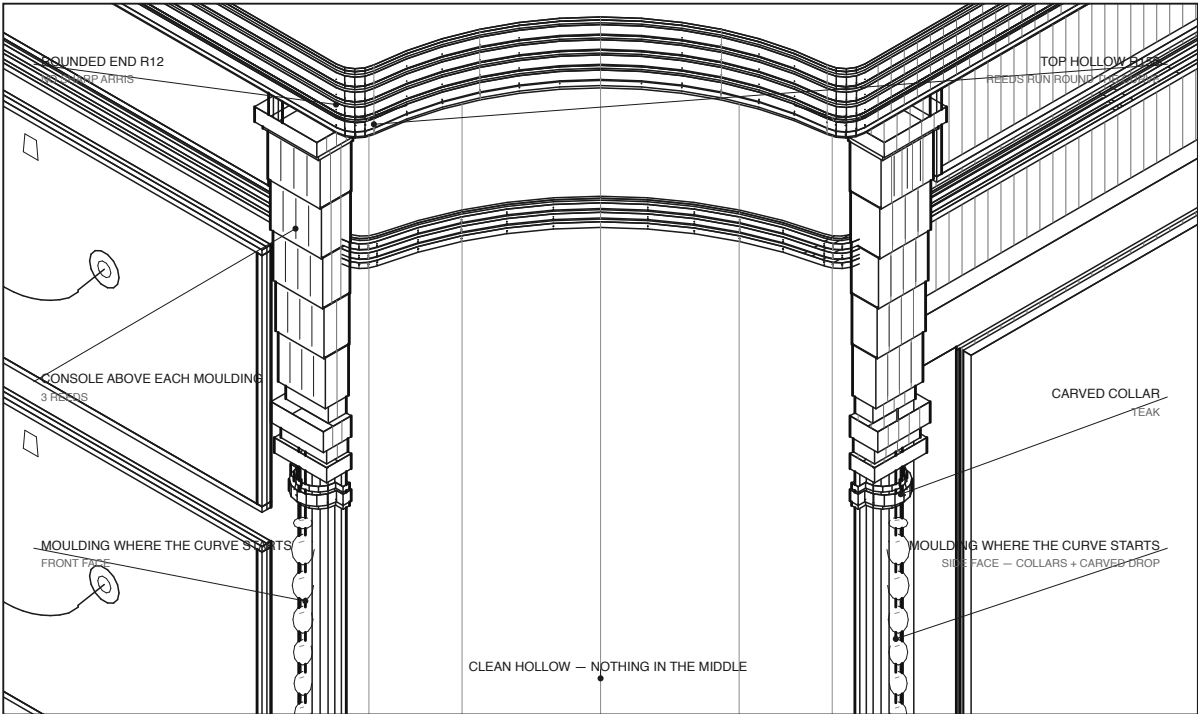

A STUDY IN TEAK

Particulars of the room

DESK — 3D VIEWS

Front right · Back left · Corner close-up

SCALE

AS NOTED @ A3

REV

9 — plain teak top, gold on handles only

DATE


17.09.2026

DWG

AST-DR-004


FRONT ELEVATION

SCALE 1:20

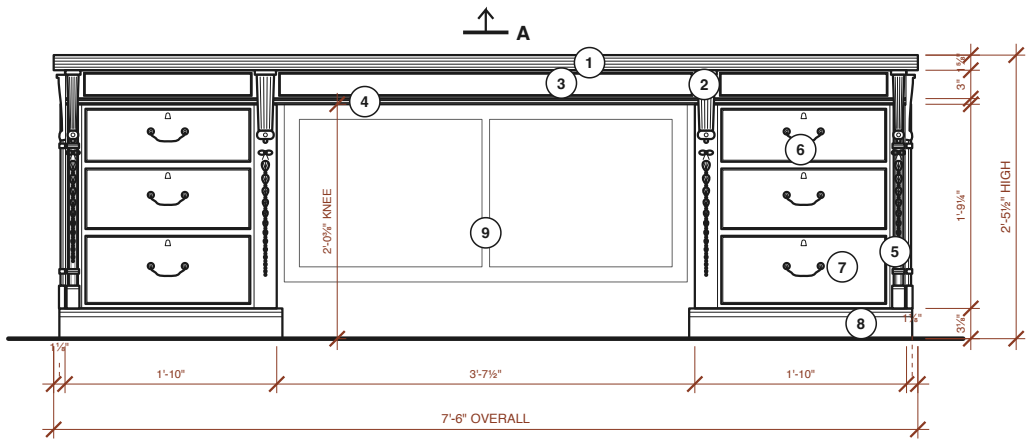


LEFT END ELEVATION

SCALE 1:20 · FRONT →

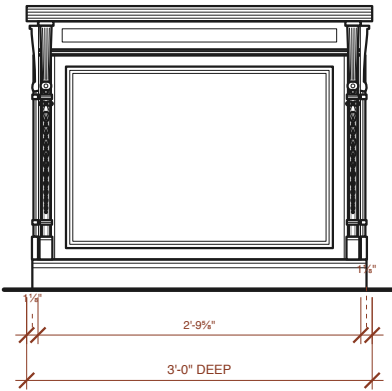


SECTION A-A

THROUGH KNEEHOLE · 1:12 · FRONT ←

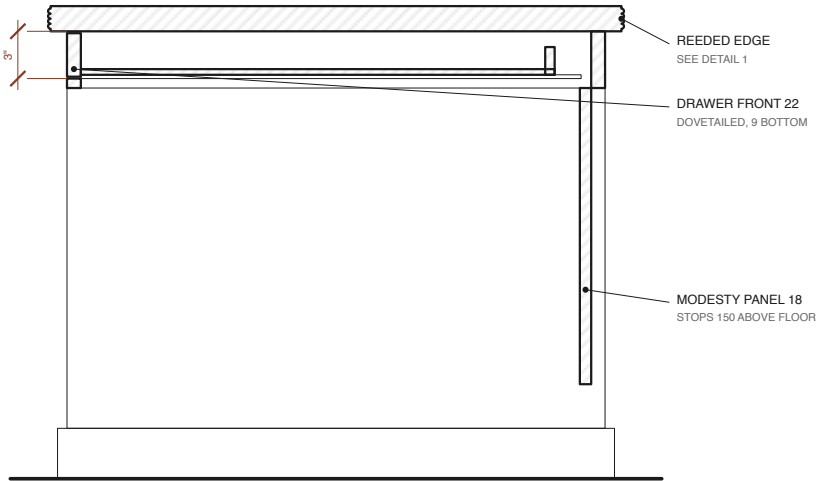


PLAN

SCALE 1:20 · FRONT AT BOTTOM

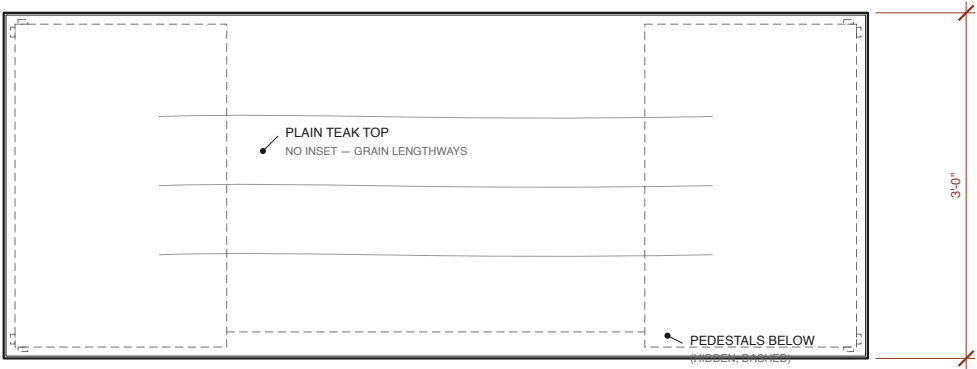


BACK ELEVATION

SCALE 1:20 · IF FREE-STANDING

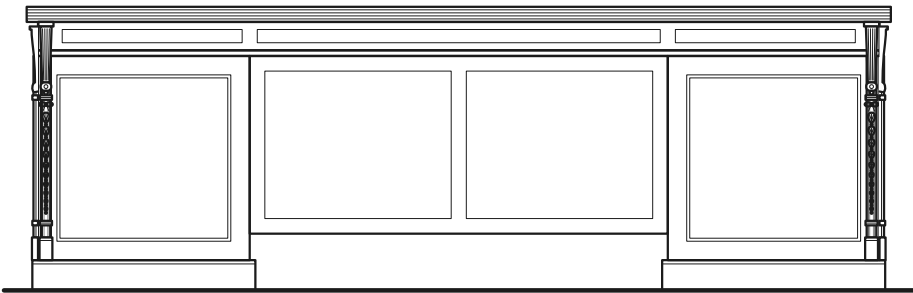

AXONOMETRIC

NOT TO SCALE · FROM FRONT RIGHT

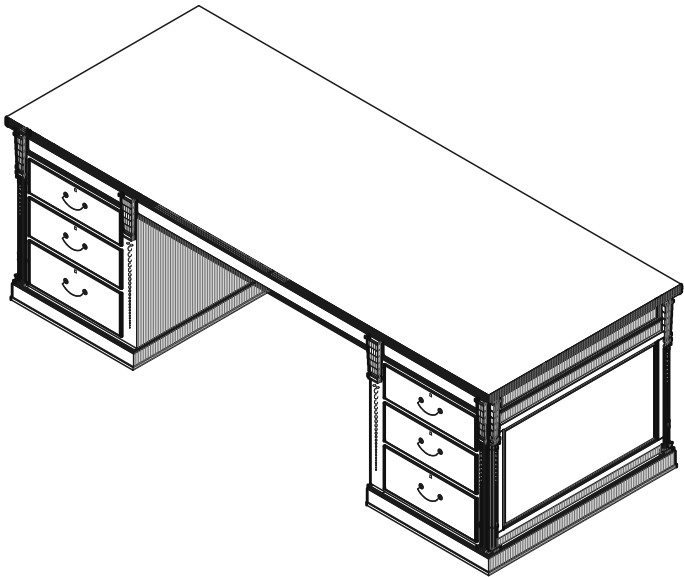

KEY

PARTS OF THE DESK

- 1 Top — plain teak, reeded edge
- 2 Reeded console bracket
- 3 Frieze drawer, push-to-open
- 4 Reeded rail
- 5 Square corner, moulding on each face at the corner
- 6 Pedestal — three drawers each side
- 7 Swan-neck handle + keyhole, every drawer
- 8 Moulded plinth
- 9 Modesty panel in kneehole

NOTES

READ BEFORE MAKING

Dimensions in feet and inches. Do not scale.

THE SQUARE-CORNERED DESK. Same size, same carcase, same carving and mouldings as AST-DR-002 — only the corners change: every layer turns a plain 90° corner instead of the R150 hollow.

The corner moulding (fillet + bead + fillet), its two collars, carved drop and console stand on each face just in from the corner — front face and end face.

Reeded edge, frieze drawers, rail, the three pedestal drawers each side and the plinth are unchanged.

First-angle projection.

A STUDY IN TEAK

Particulars of the room

DESK (SQUARE CORNERS) — GENERAL ARRANGEMENT

Front · End · Section · Plan · Back · Axo

SCALE
AS NOTED @ A3


DATE
30.09.2026

REV
1 — square corners, every detail kept

DWG
AST-DR-028


1 · TOP EDGE

SECTION · SCALE 1:1

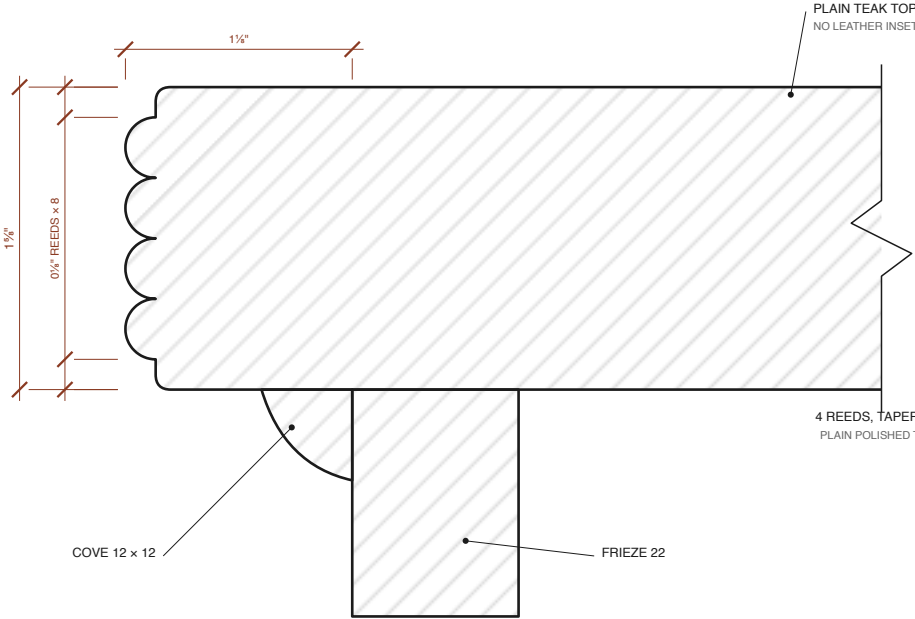


2 · DRAWER RAIL

SECTION · SCALE 1:1

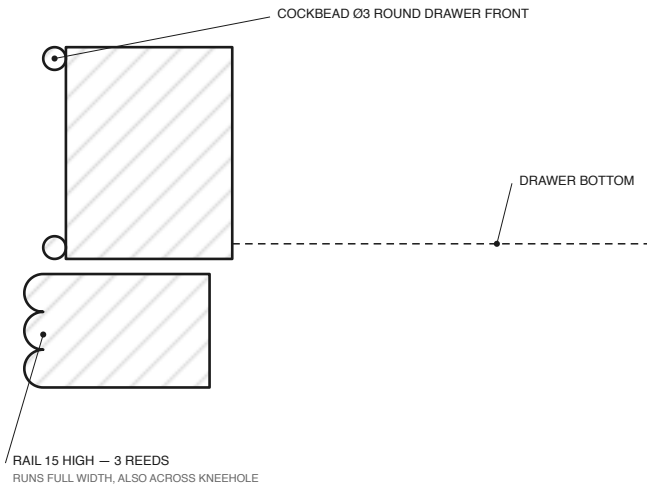


8 · CORNER — SQUARE + MOULDINGS

PLAN · SCALE 1:4 · ALL FOUR CORNERS · EVERY LAYER TURNS 90°

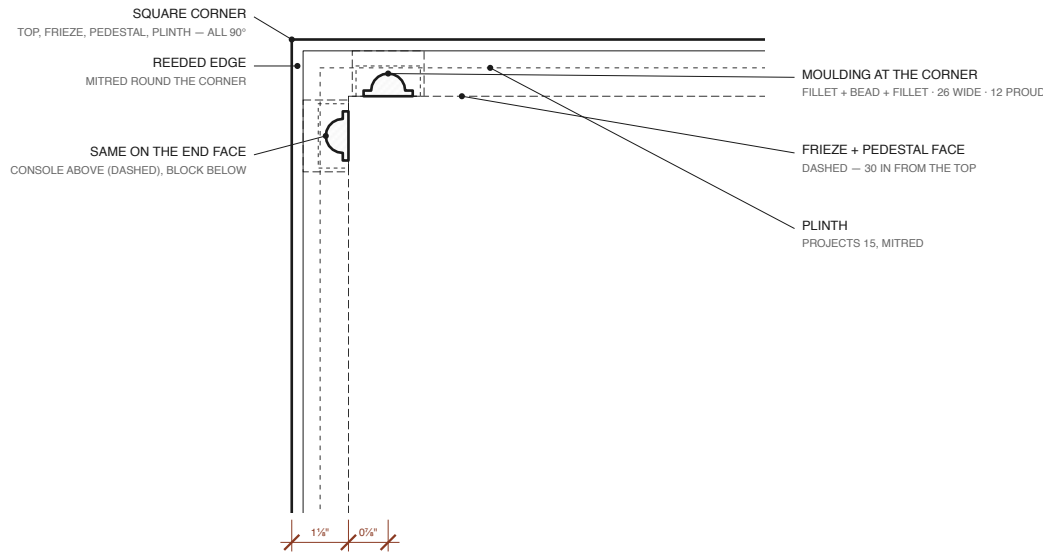


3 · CONSOLE BRACKET

FRONT + SIDE · 1:2.5 · 50 WIDE AT KNEEHOLE, 34 ON CORNERS

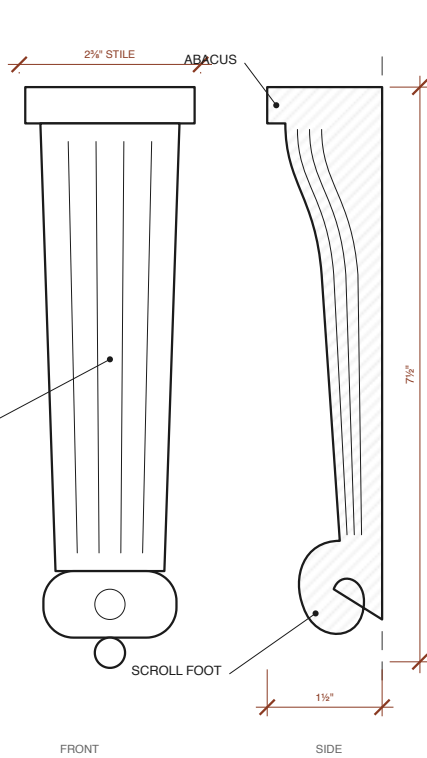


7 · PLINTH

SECTION · SCALE 1:2

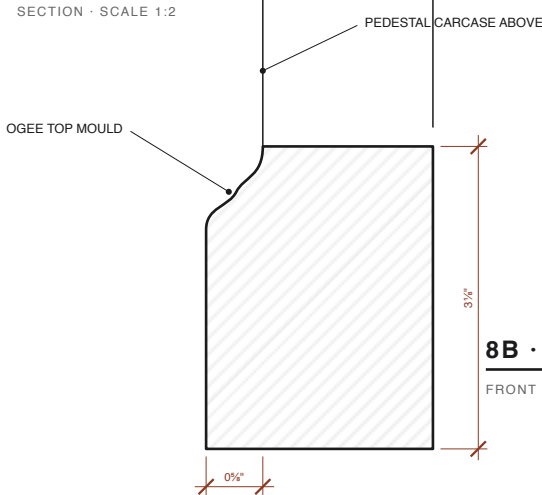


4 · CARVED DROP

KNEEHOLE STILE · SCALE 1:4

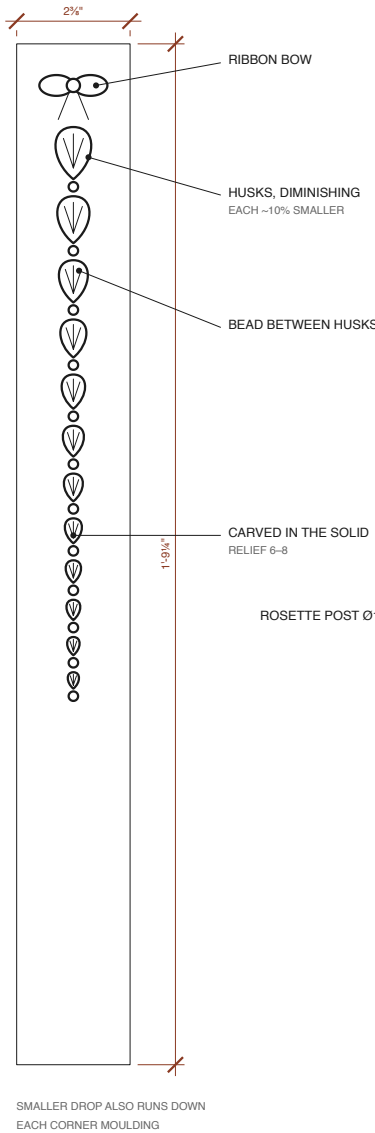


8B · CORNER ELEVATION

FRONT LEFT CORNER · SCALE 1:10 · SQUARE

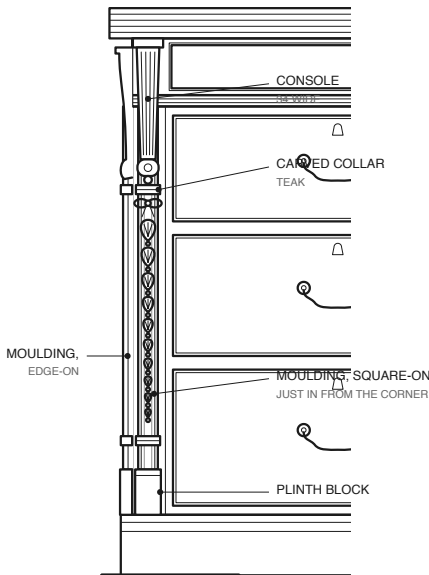


5 · PEDESTAL DRAWERS

RIGHT PEDESTAL FRONT · SCALE 1:10 · THREE EACH SIDE

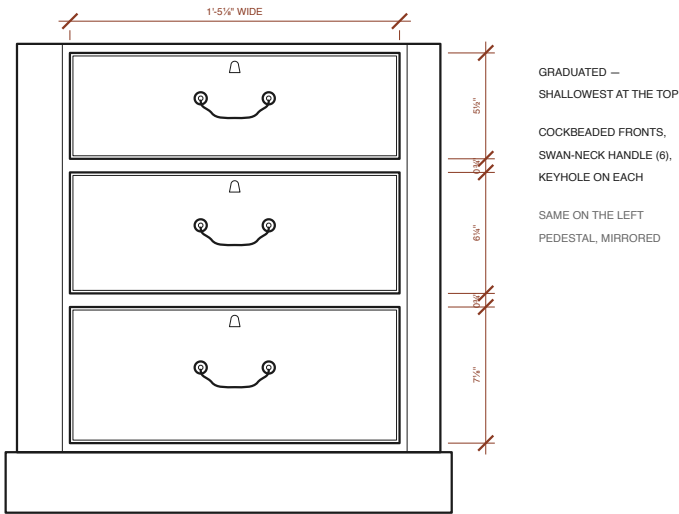

6 · DRAWER HANDLE

ELEVATION · SCALE 1:1

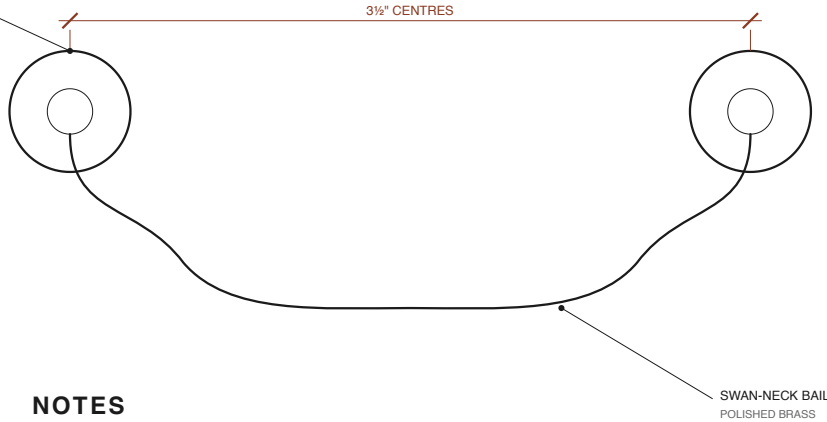

NOTES

DETAILS

Profiles are drawn from film stills and are indicative;

the joiner to prepare a full-size mock-up of 1, 2 and 7.

Carving (4, 5): carver to work from the reference photos;

sample one drop before carving the set.

Hardware (6): standard 90 mm swan-neck, solid brass.

Gold/brass on handles and ring pulls only; rest plain teak.

Corners: square, every layer mitred; moulding on each

face just in from the corner (8, 8B).

A STUDY IN TEAK

Particulars of the room

DESK (SQUARE CORNERS) — DETAILS

Edge · Rail · Console · Drop · Ornament · Handle · Plinth · Corner

SCALE

AS NOTED @ A3

DATE

30.09.2026

REV


1 — square corners, every detail kept

DWG

AST-DR-029

FROM THE FRONT RIGHT

AXONOMETRIC · APPROX 1:14 · HIDDEN LINES REMOVED · SHADED

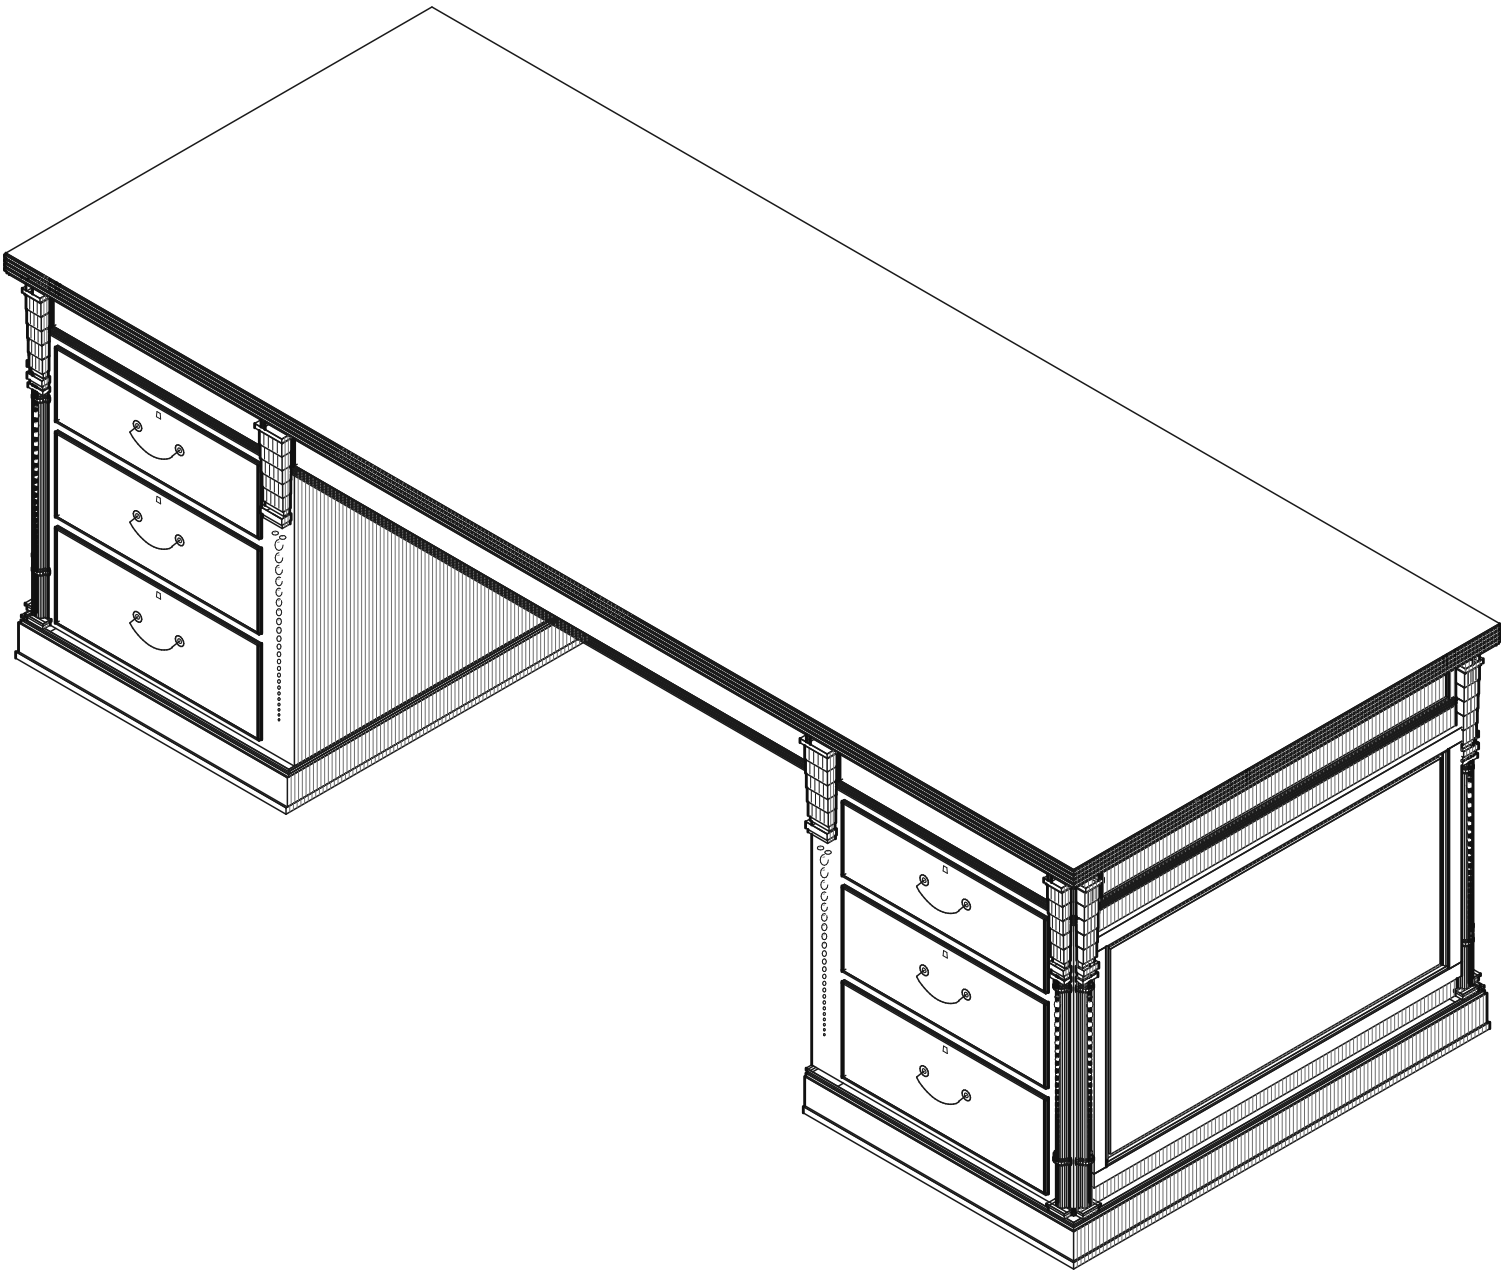


NOTES

3D VIEWS

Generated from the same geometry as the plan and elevations —
any change to sizes, hollows or mouldings updates every view.
Carving and handles shown simplified; see AST-DR-003.
Axonometric: measure along the three axes only.


FROM THE BACK LEFT

AXONOMETRIC · APPROX 1:29 · IF FREE-STANDING

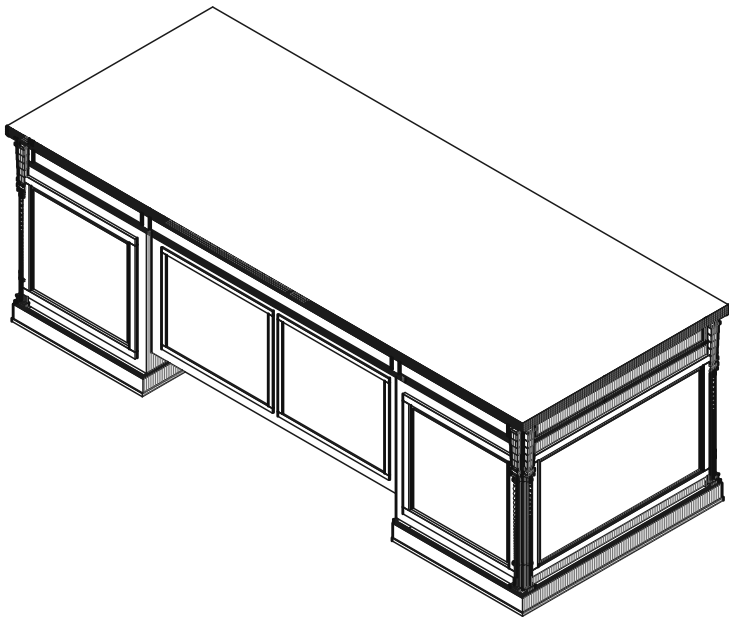

CORNER CLOSE-UP

FRONT RIGHT · APPROX 1:4 · SQUARE CORNER, MOULDINGS, CONSOLES

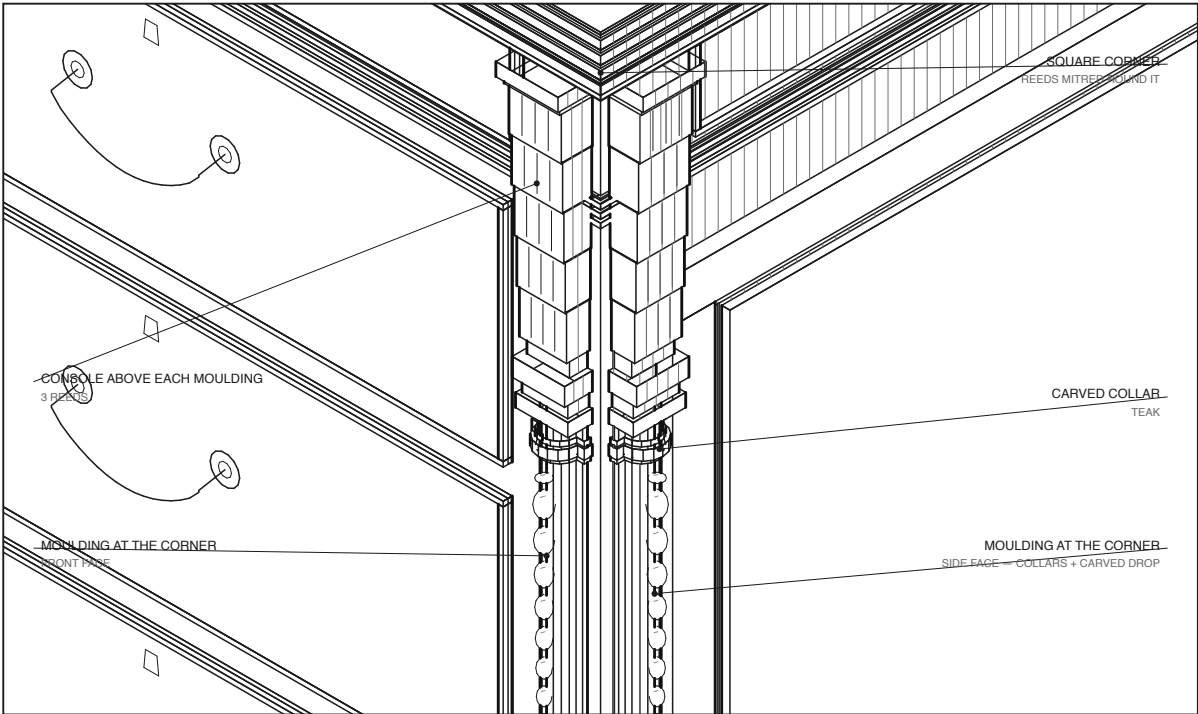

A STUDY IN TEAK

Particulars of the room

DESK (SQUARE CORNERS) — 3D VIEWS

Front right · Back left · Corner close-up

SCALE

AS NOTED @ A3

DATE

30.09.2026

REV


1 — square corners, every detail kept

DWG

AST-DR-030


ELEVATION — STUDY WALL

SCALE 1:25 · BOOKCASE · PANEL FOR PAINTING · WINDOW

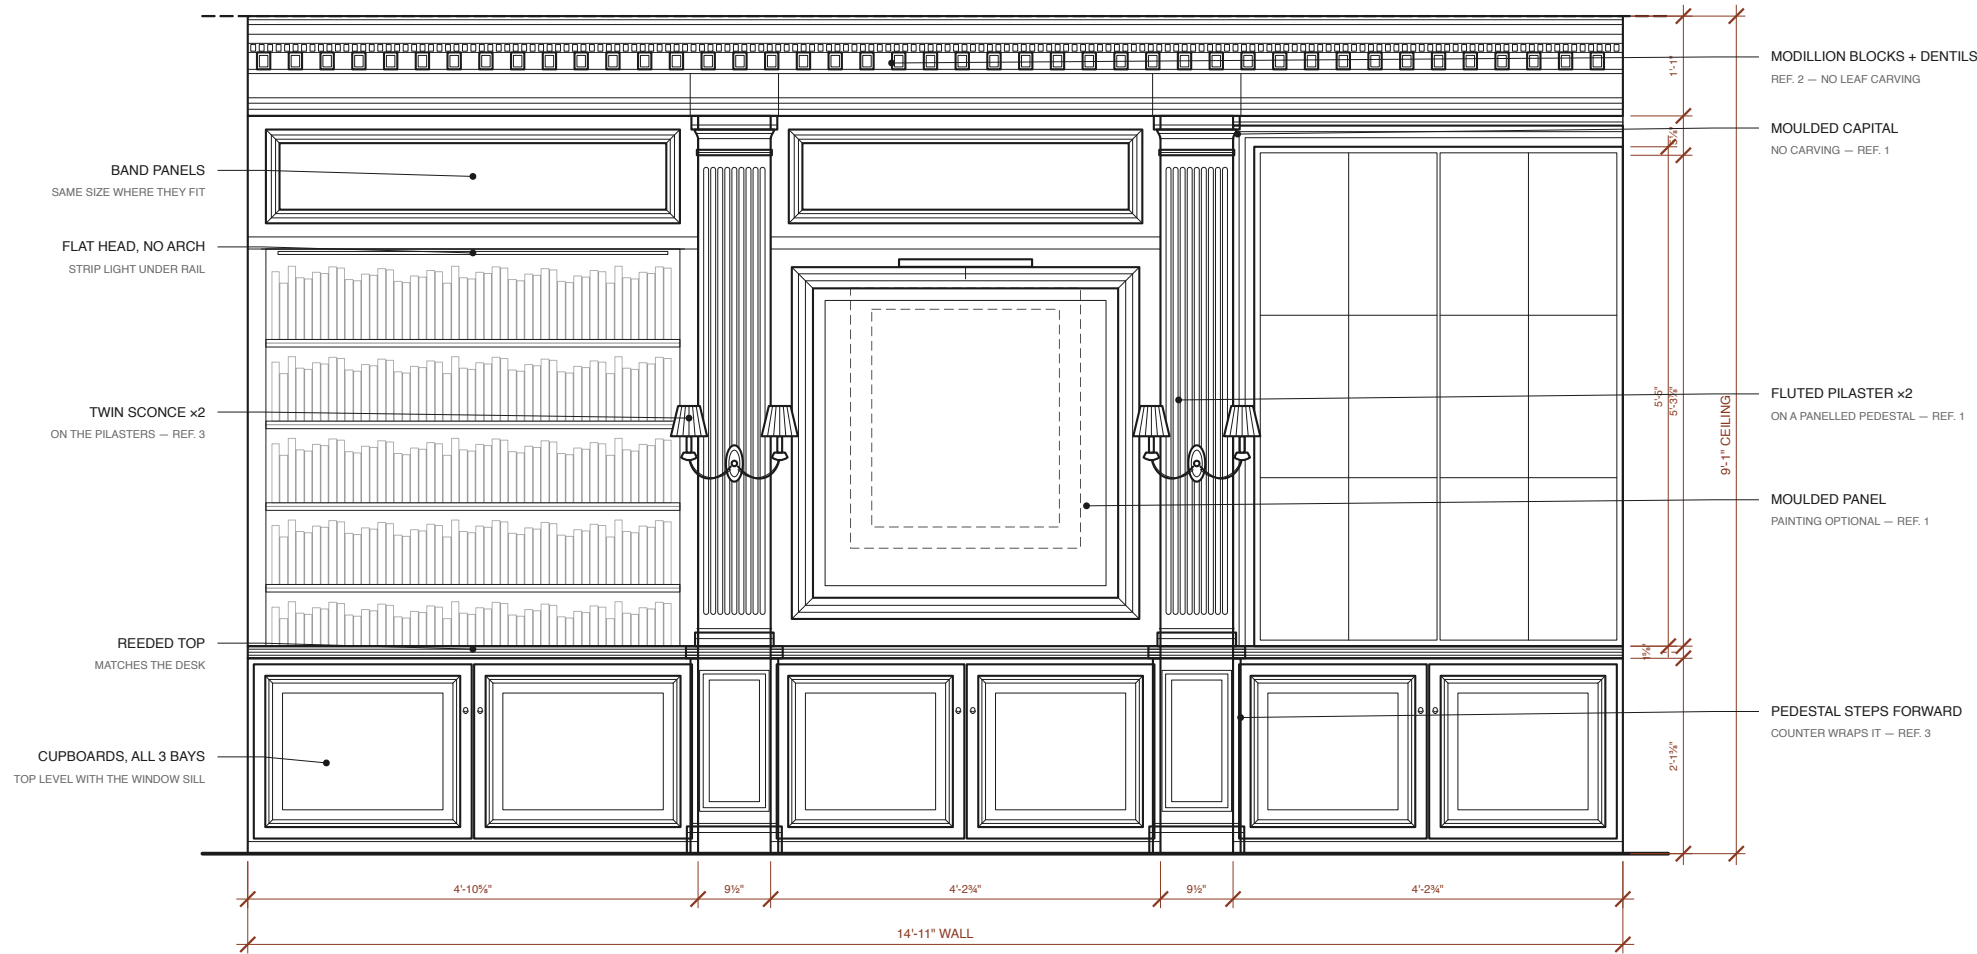


PLAN

CUT AT 1200 · SCALE 1:25 · ROOM BELOW, WALL ABOVE

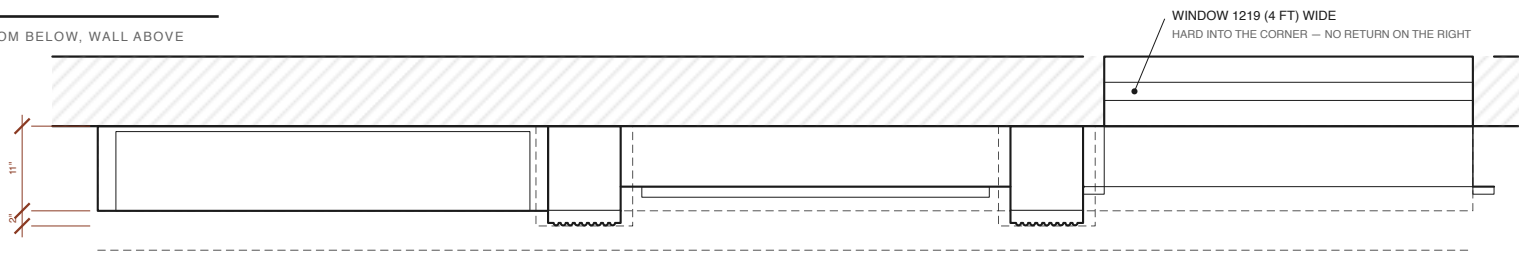

SECTION A-A

THROUGH BOOKCASE · 1:25

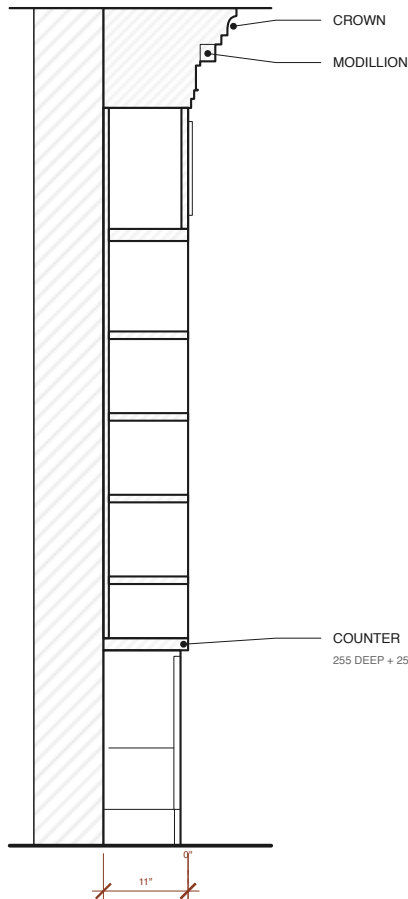

NOTES

REVISION 9

Wall 14 ft 11 in, ceiling 9 ft 1 in (measured).

Centre panel set equal to the window bay so the two pilasters frame a matched pair; the bookcase takes the remainder as the anchor at the end of the wall.

Window measured: 4 ft wide, 5 ft 5 in tall, hard into the right corner. Sill 2 ft 3 in (686) — CONFIRMED.

OPEN: sill 2 ft 3 + height 5 ft 5 + your 1 ft 3 to the ceiling makes 8 ft 11, two inches short of the 9 ft 1 ceiling. Sill and height are drawn as measured, so the head falls 1 ft 5 down, not 1 ft 3. Laser it.

Counter top is set to the sill at 686, so the two are one surface; this datum runs on round to the right wall rail.

Cupboards under all three bays. Gold on handles only.

A STUDY IN TEAK

Particulars of the room

STUDY WALL — GENERAL ARRANGEMENT

Elevation · Plan · Section

SCALE
AS NOTED @ A3


DATE
19.09.2026

REV
9 — sill datum confirmed at 686

DWG
AST-DR-005


1 · PILASTER

CAPITAL AND BASE · ELEVATION · SCALE 1:5 · REF. 1

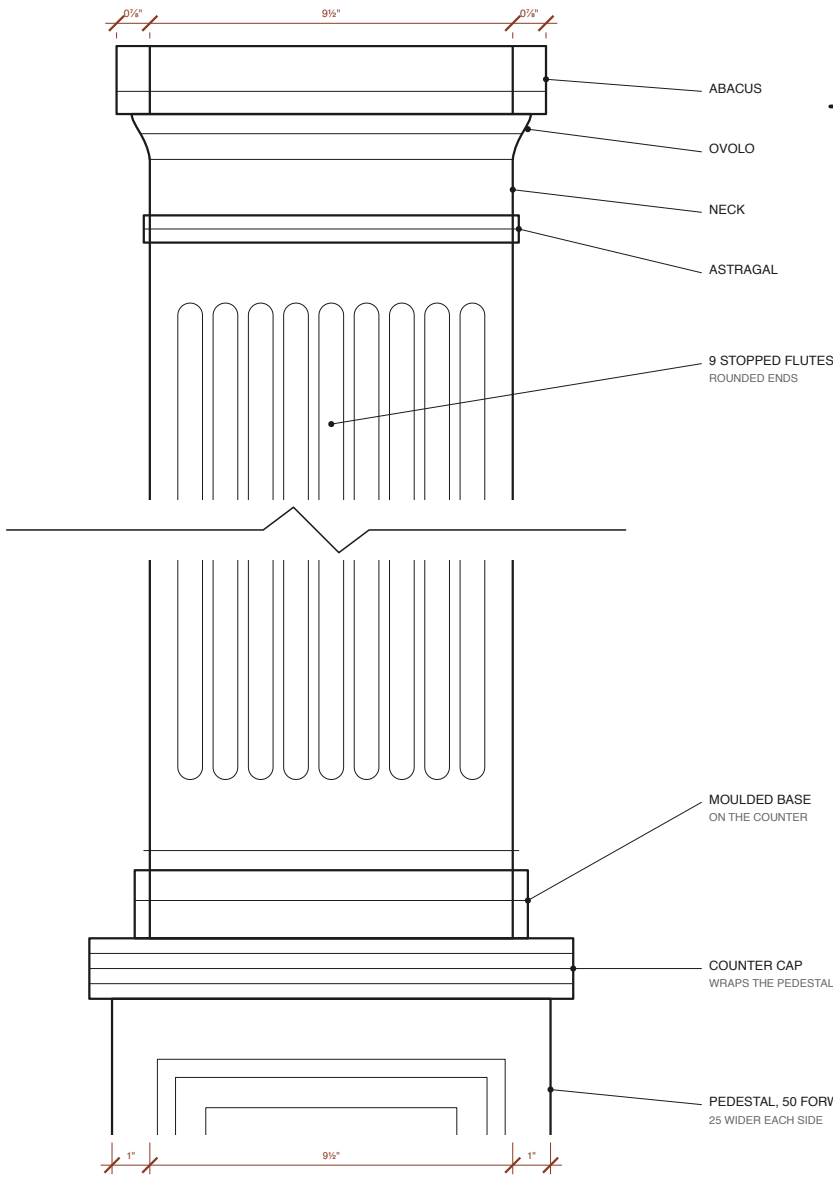


2 · PILASTER SECTION

PLAN · SCALE 1:2

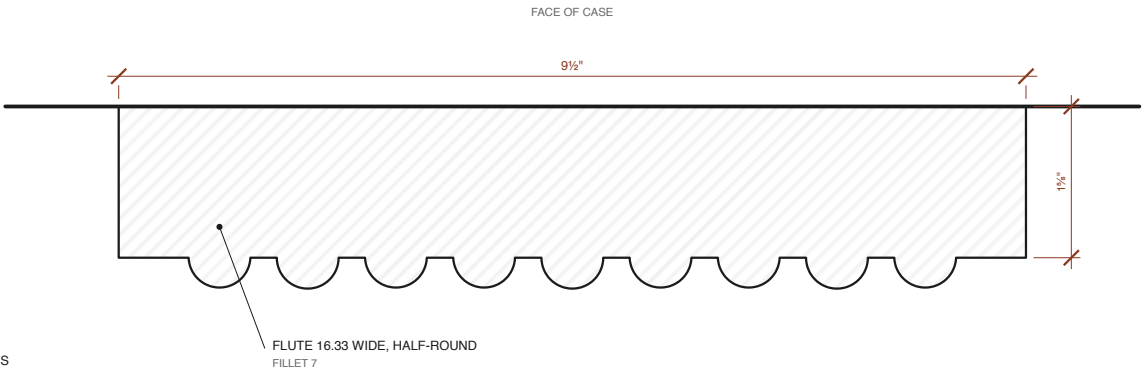


3 · CORNICE

SECTION · SCALE 1:6

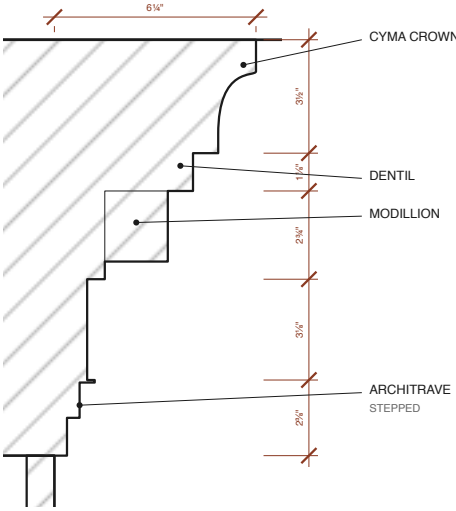


4 · MODILLION + DENTILS

FRONT · SCALE 1:2 · PLAIN

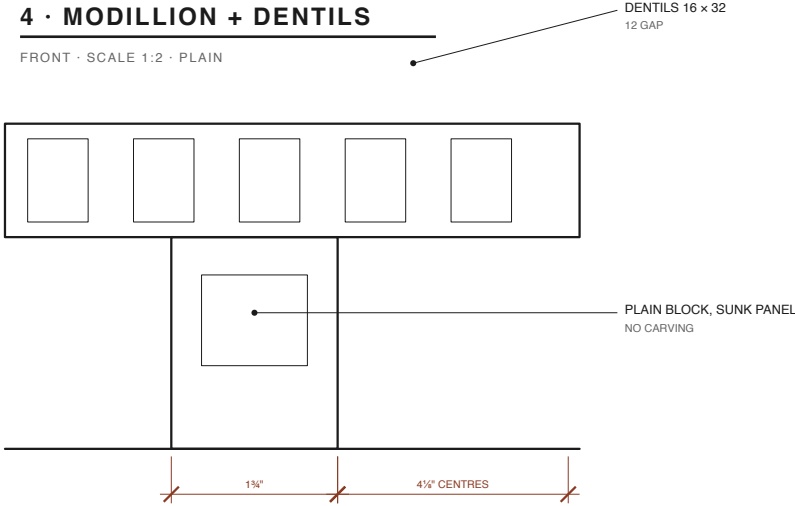


5 · PAINTING PANEL

BOLECTION MOULDING · SECTION · SCALE 1:2

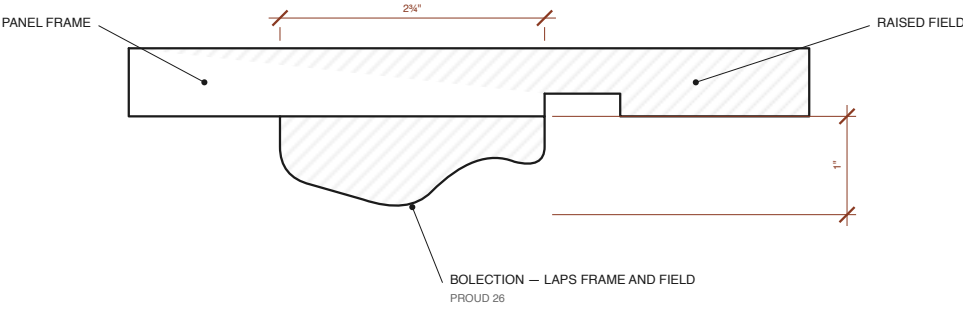


6 · BAND PANEL + SCENCE

ELEVATION · SCALE 1:25 · SAME PANEL OVER EVERY BAY

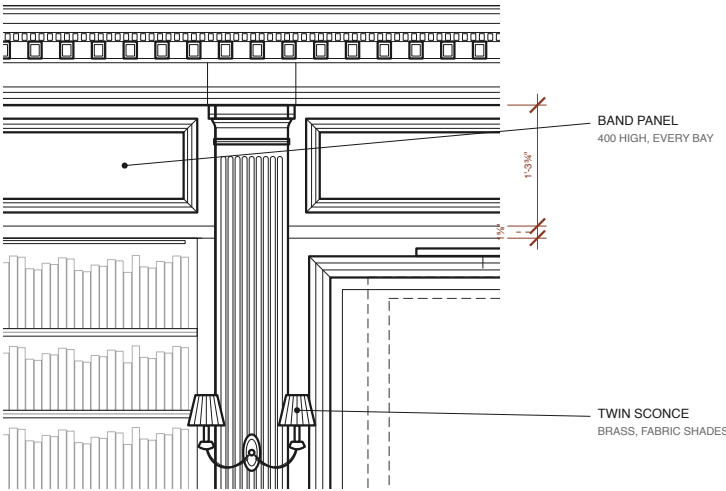

7 · COUNTER EDGE

SECTION · SCALE 1:2 · SAME REEDS AS THE DESK

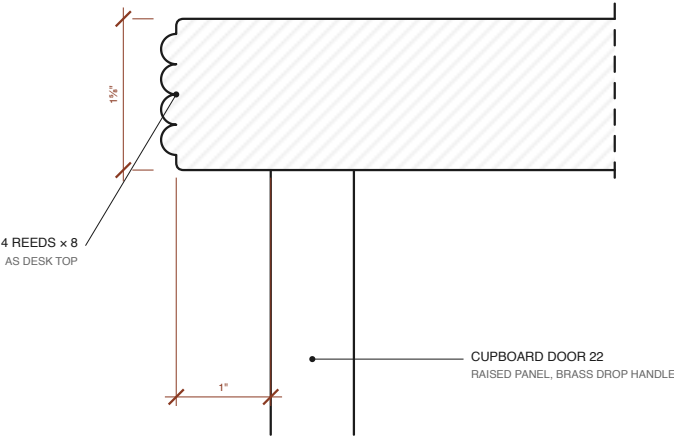

NOTES

DETAILS

No carving on pilasters or modillions — mouldings only.
Flute and modillion spacing to be set out on site
so they finish symmetrically on the wall.
Mock up profiles 3, 5 and 7 full size before cutting.

A STUDY IN TEAK

Particulars of the room

STUDY WALL — DETAILS

Pilaster · Cornice · Modillion · Panel · Band · Counter

SCALE

AS NOTED @ A3

REV

9 — sill datum confirmed at 686

DATE


19.09.2026

DWG

AST-DR-006


ELEVATION — LEFT WALL

SCALE 1:30 · SEEN FROM THE ROOM · STUDY CORNER LEFT, BED CORNER RIGHT

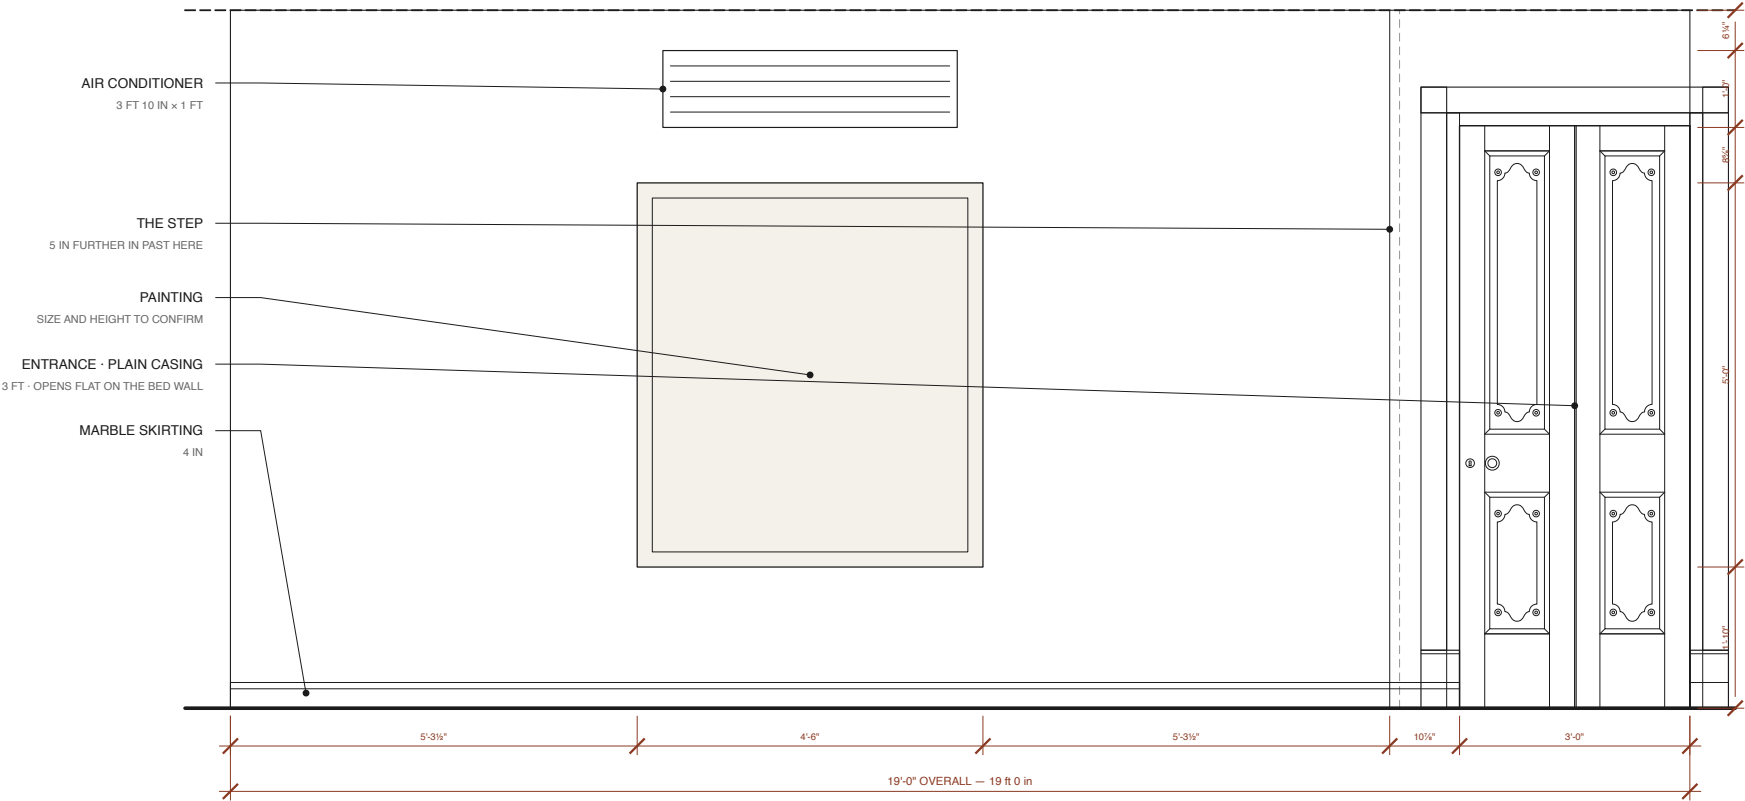

PLAN

CUT AT 1200 · SCALE 1:30 · ROOM BELOW THE WALL

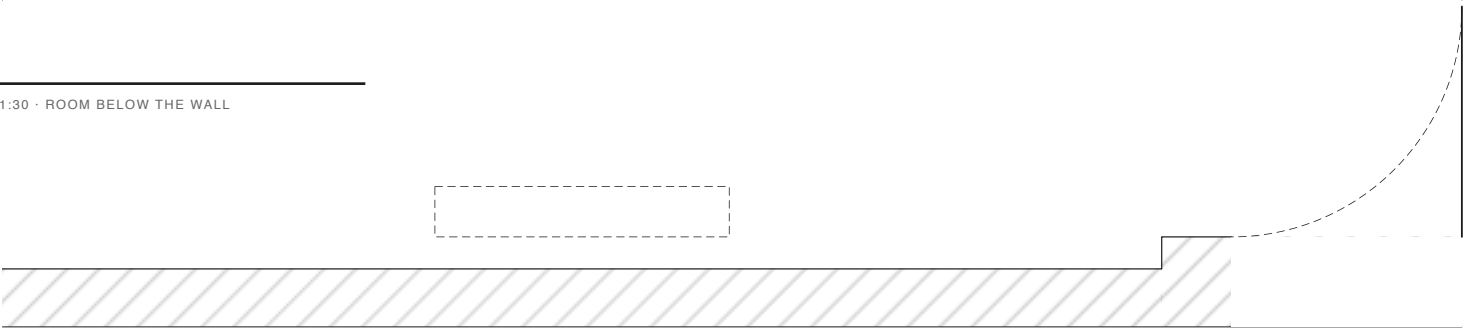

NOTES

REVISION 5

This wall stays plain. Paint, the marble skirting, one painting and the air conditioner over it — nothing is built into it and nothing is panelled. It is the quiet side of the room, opposite the panelled right wall, and it is the wall that carries the splay and the step, so anything fitted to it would have to be scribed twice. The painting is centred on the 15 ft 1 1/4 in of wall before the step, the only uninterrupted run. Centre line 7 ft 6 1/2 in from the study corner, 1 ft 10 in off the floor.

OPEN — the painting is drawn 4 ft 6 in x 5 ft 0 in, centred at 4 ft 4 in.

Still assumed. Send the real size and it is a one-line change.

Sized to the wall it has: 8 1/4 in clear under the air conditioner, and

8 in wider than the unit, so the AC sits within its width.

The air conditioner is 3 ft 10 in x 1 ft 0 in — MEASURED. Its depth (7 1/4 in)

and its height off the ceiling (6 1/4 in) are still assumed.

The AC needs a power point and a drain run before the wall is painted — decide the side the pipework leaves on.

The entrance takes the PLAIN casing: same 2 in lining and 4 in moulding as every opening, running straight across the head and stopping. The carved head on AST-DR-011 is the DRESSING door's alone.

OPEN — the profile of that 4 in plain band is not settled. Drawn flat.

A STUDY IN TEAK

Particulars of the room

LEFT WALL

Elevation · Plan · The plain wall

SCALE

1:30 @ A3

DATE

23.09.2026

REV


5 — the painting widened to 4 ft 6 in

DWG

AST-DR-014


ELEVATION — RIGHT WALL

SCALE 1:25 · SEEN FROM THE ROOM · STUDY WALL ON THE LEFT · OPTION C

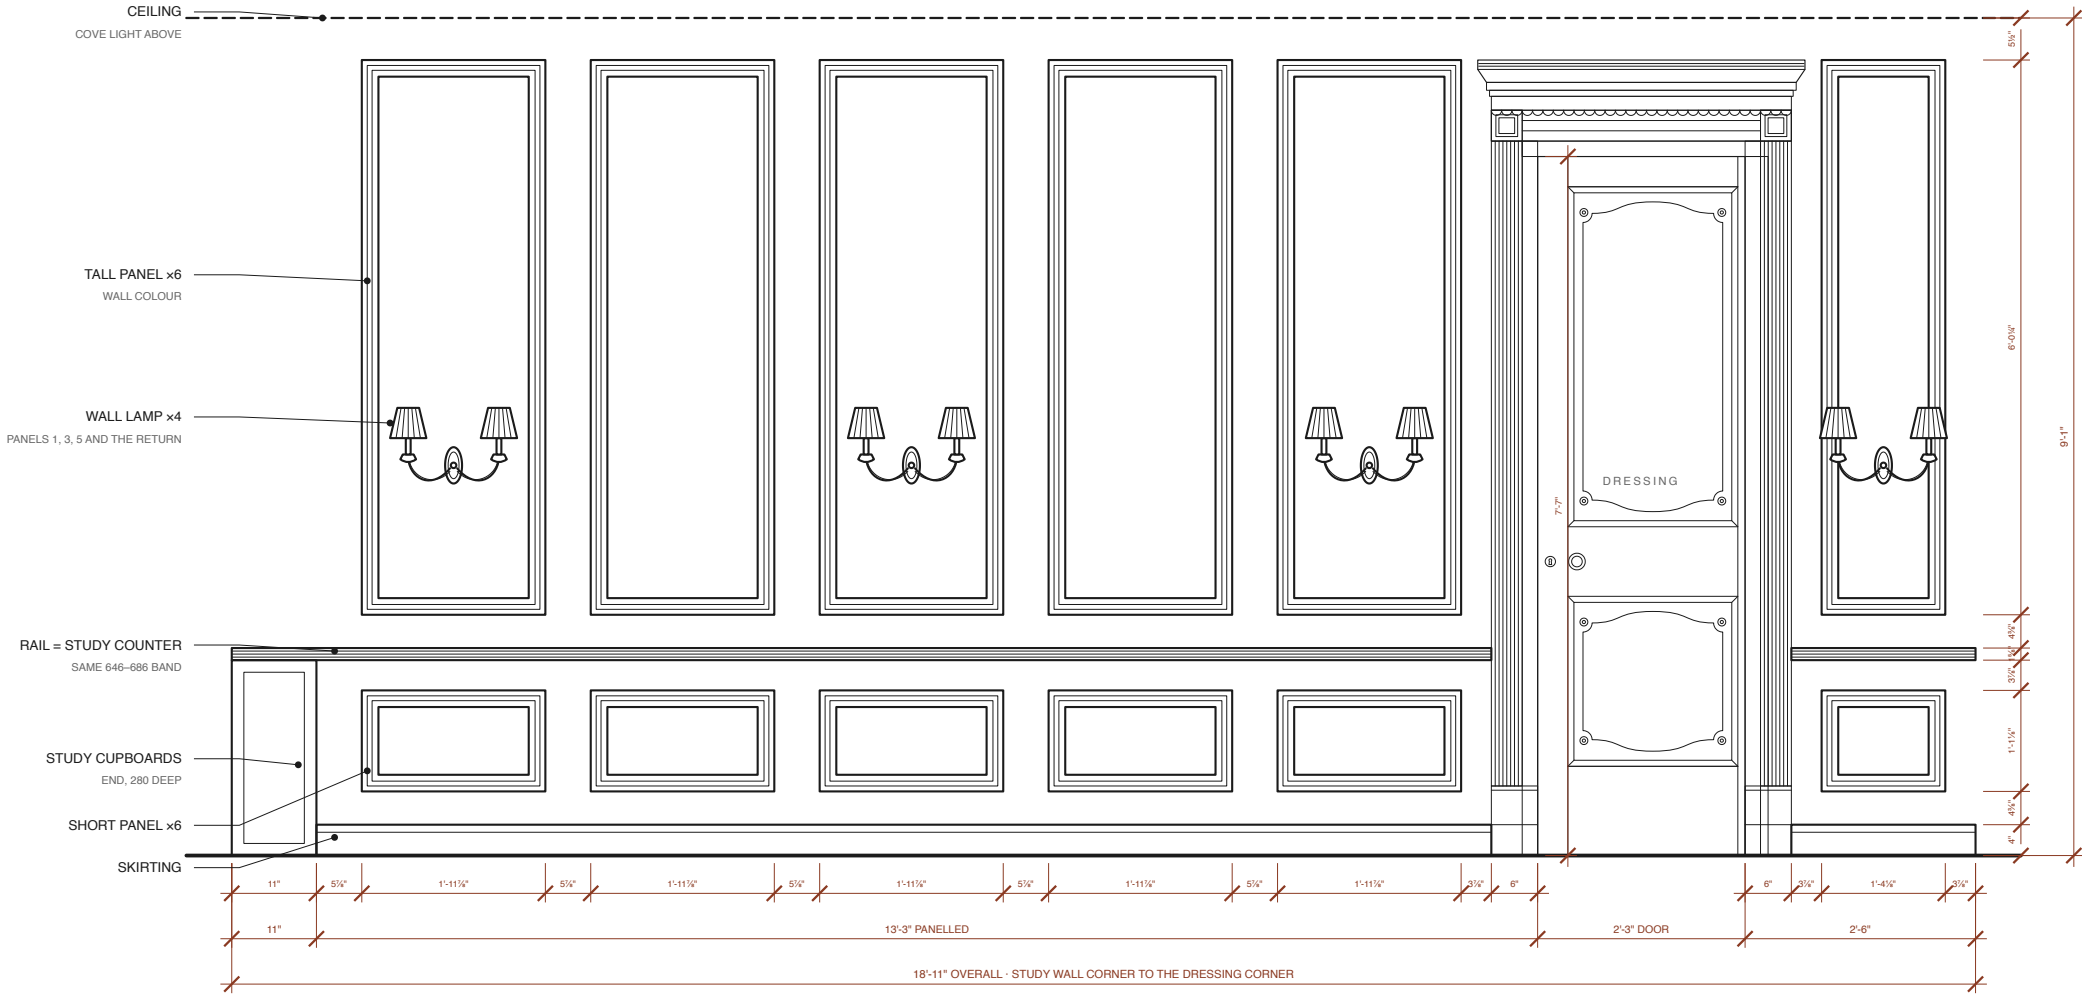


PLAN

CUT AT 1000 · SCALE 1:25 · ROOM BELOW, WALL ABOVE

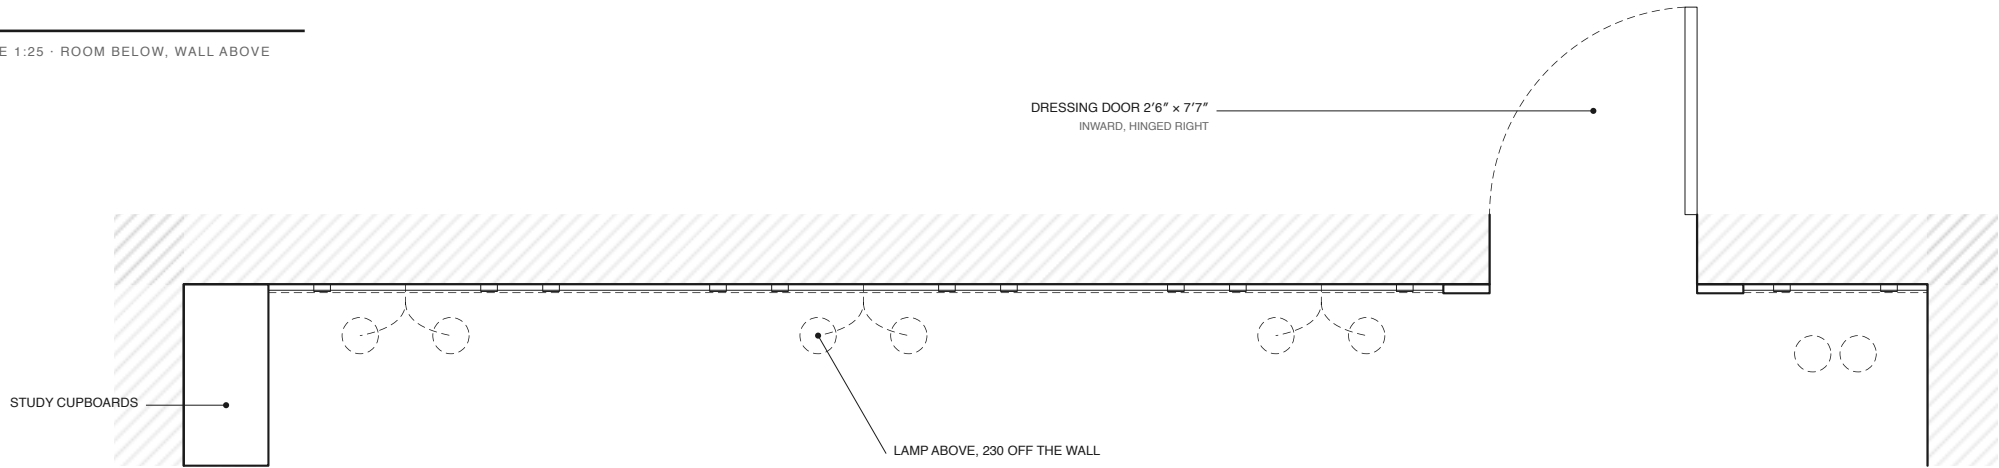


1 · PANEL MOULDING

SECTION · 1:1

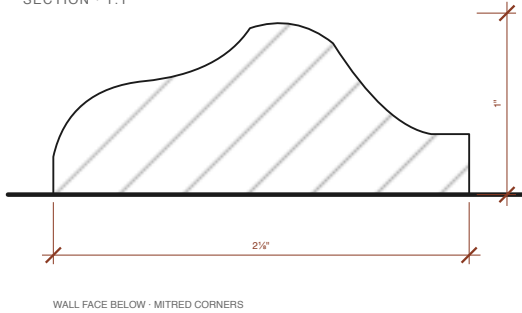


2 · RAIL

SECTION · 1:2

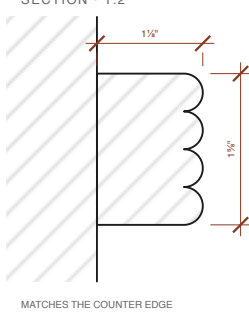


3 · SKIRTING

MARBLE · SECTION · 1:4

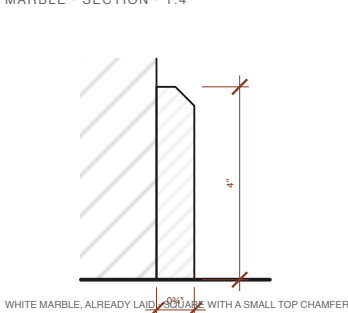


4 · WALL LAMP

ELEVATION · 1:10 · x4

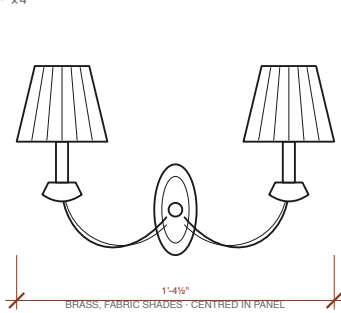

SECTION A-A

THROUGH PANEL 1 · 1:20

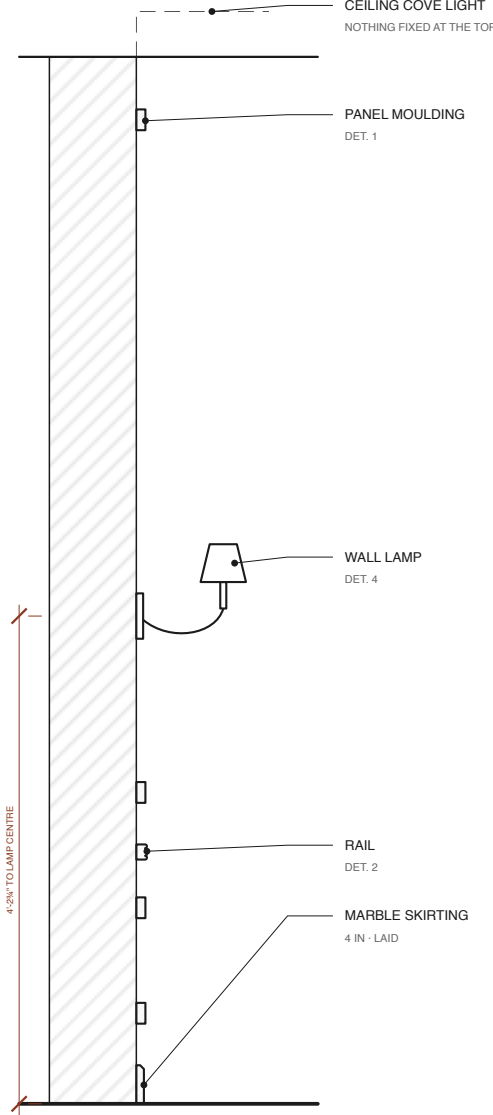

NOTES

REVISION 18

- Option C: 5 equal panels, lamps in 1, 3, 5 and the return.
- One narrow panel on the wall past the door.
- Moulding, rail and skirting painted the wall colour.
- SELECTED after four schemes: the rail is the study counter band carried round the corner, and it dies into the casing.
- Skirting is white marble, 4 in, already laid.
- Casing 2 in lining + 4 in moulding = 6 in, 1068 overall; crown at 8 ft 8 in, and the tall panels stop on that line, not the leaf head at 7 ft 7 in.
- 2 ft 4 in corner to frame, measured both sides; leaf 2 ft 3 in a 2 in frame. OPEN: that puts the frame 14 ft 0 from the study corner, 6 in off the taped 13 ft 6. Retape that end.

A STUDY IN TEAK

Particulars of the room

RIGHT WALL — PANEL MOULDING

Elevation · Plan · Section · Details

SCALE
AS NOTED @ A3


DATE
20.09.2026

REV
18 — SELECTED: the rail at 2 ft 3 in, carrying the study counter round

DWG
AST-DR-007


PLAN — BED AND PARTITION

SCALE 1:50 · BOTH 8 FT · SET OUT FROM THE RIGHT WALL

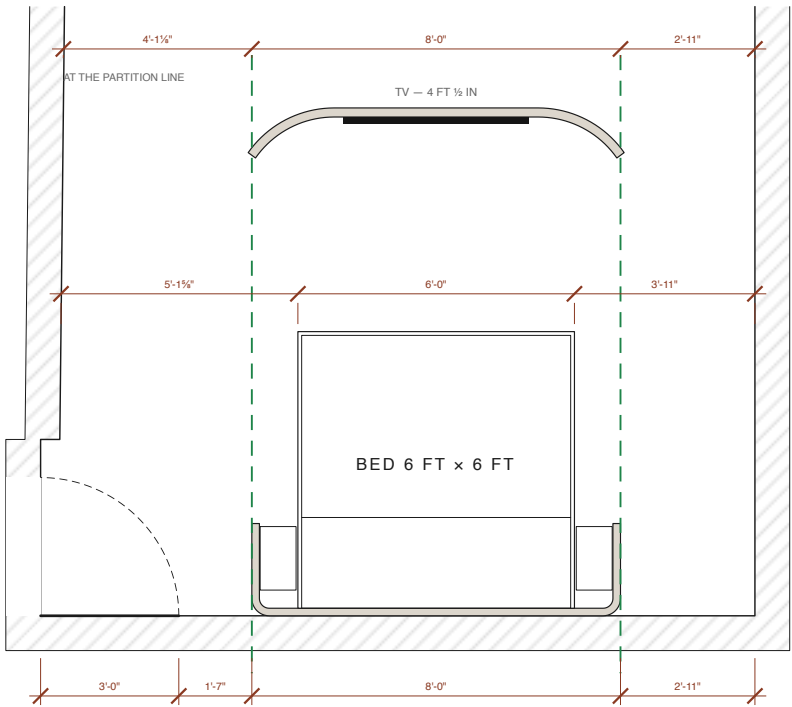


BED BACK — FROM THE FOOT OF THE BED

ELEVATION · 1:25 · THE CURLS SEEN END-ON

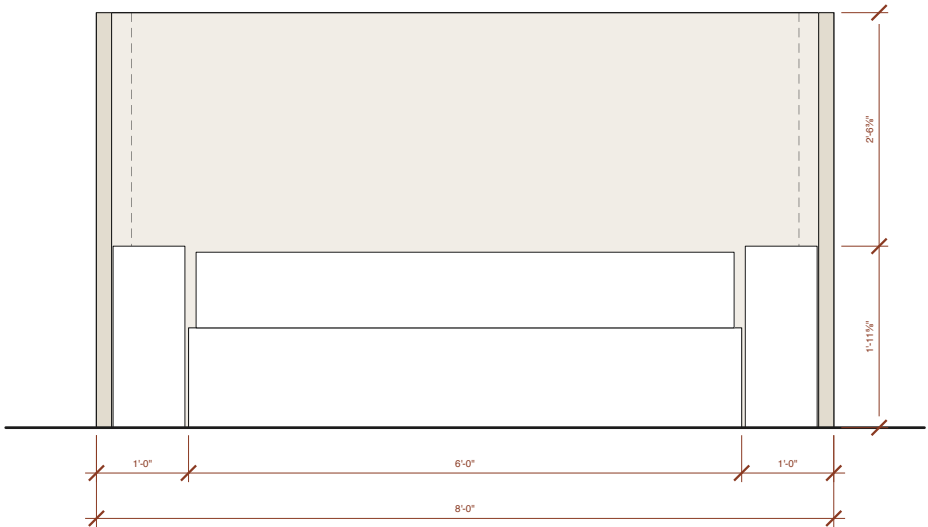


A · FROM THE DOOR

STANDING AT THE ENTRANCE, LOOKING IN

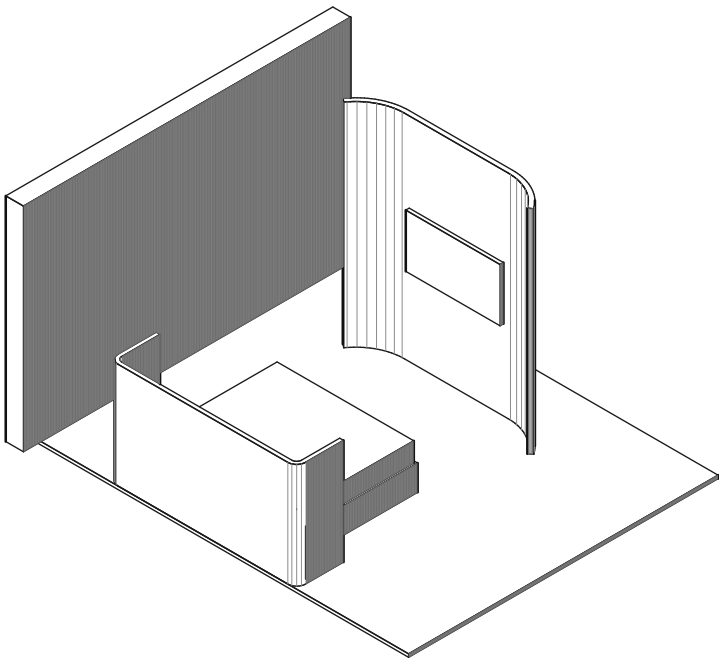


B · BED TO PARTITION

FROM THE BED, LOOKING AT THE TV

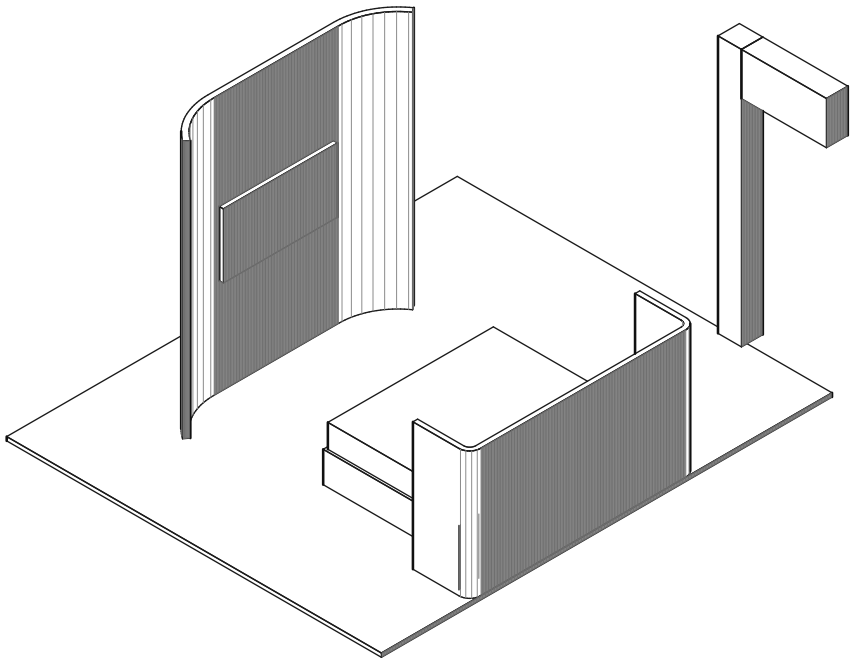


C · PARTITION TO BED

FROM THE PARTITION, LOOKING AT THE BED

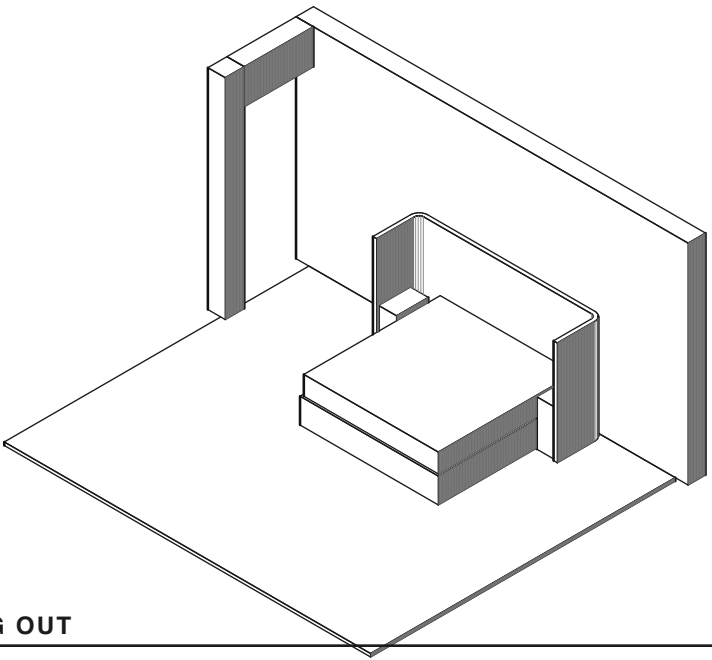

D · FROM THE STUDY

THE PARTITION'S BACK, THE BED BEYOND

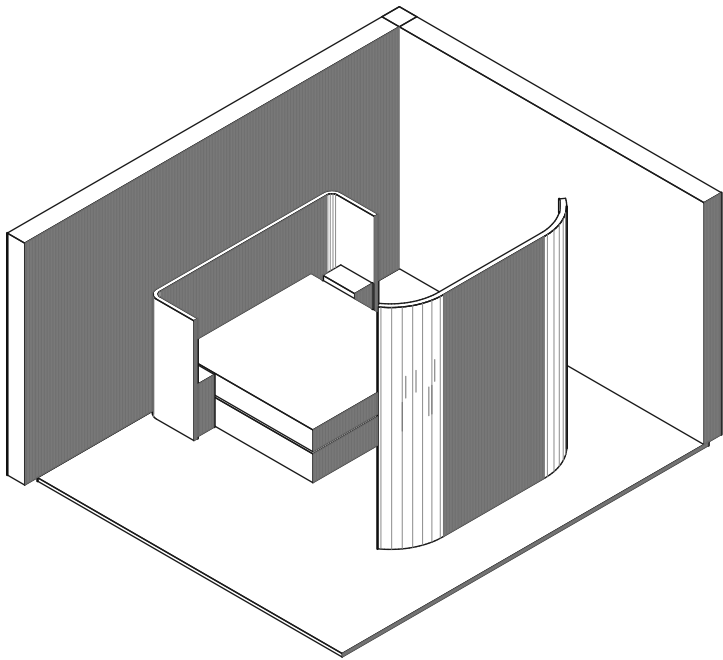

SETTING OUT

REVISION 5 · FEET AND INCHES

Both pieces moved 6 in to the right: 2 ft 11 in from the right wall to each.

Partition line: 4 ft 1½ in · partition 8 ft · 2 ft 11 in.

Bed wall: 3 ft 0 in open door · 1 ft 7 in clear · bed back 8 ft · 2 ft 11 in.

The bed is 6 ft 0 in × 6 ft 0 in, centred on the back, which shows 1 ft 0 in each side.

RIGHT wall to the bed: 3 ft 11 in the whole way — that wall is straight.

LEFT wall to the bed: 5 ft 1½ in at the foot, 5 ft 2 in at the step, 5 ft 7 in at the head —

that wall carries the splay AND the step, so the gap opens out along the bed.

The bed therefore sits off centre. Centring the 8 ft back in the 15 ft 6 in bed

wall would move everything 10 in left — but it is set off the RIGHT wall,

the only straight one, and moved 6 in right on purpose.

Walkway: curls reach 8 ft 11½ in, foot of the bed at 12 ft 9 in — 3 ft 9½ in between.

OPEN — the ledges inside the curls come to 9½ in × 1 ft 4½ in: a phone and a slim lamp, not a nightstand. 9 in a side is all 8 ft leaves.

ASSUMED — back 4 ft 6 tall, ledges 2 ft. Bed and partition line measured.

A STUDY IN TEAK

Particulars of the room

BED, BED BACK AND PARTITION

Plan · Bed back · Four views

SCALE

AS NOTED @ A3

DATE

20.09.2026

REV


5 — the bed's clearance to each wall, splay included

DWG

AST-DR-013

DRESSING ROOM — SHELL AND LAYOUT

PLAN · SCALE 1:35 · COPIED FROM THE OWNER'S SKETCH — NOT YET A SITE MEASUREMENT

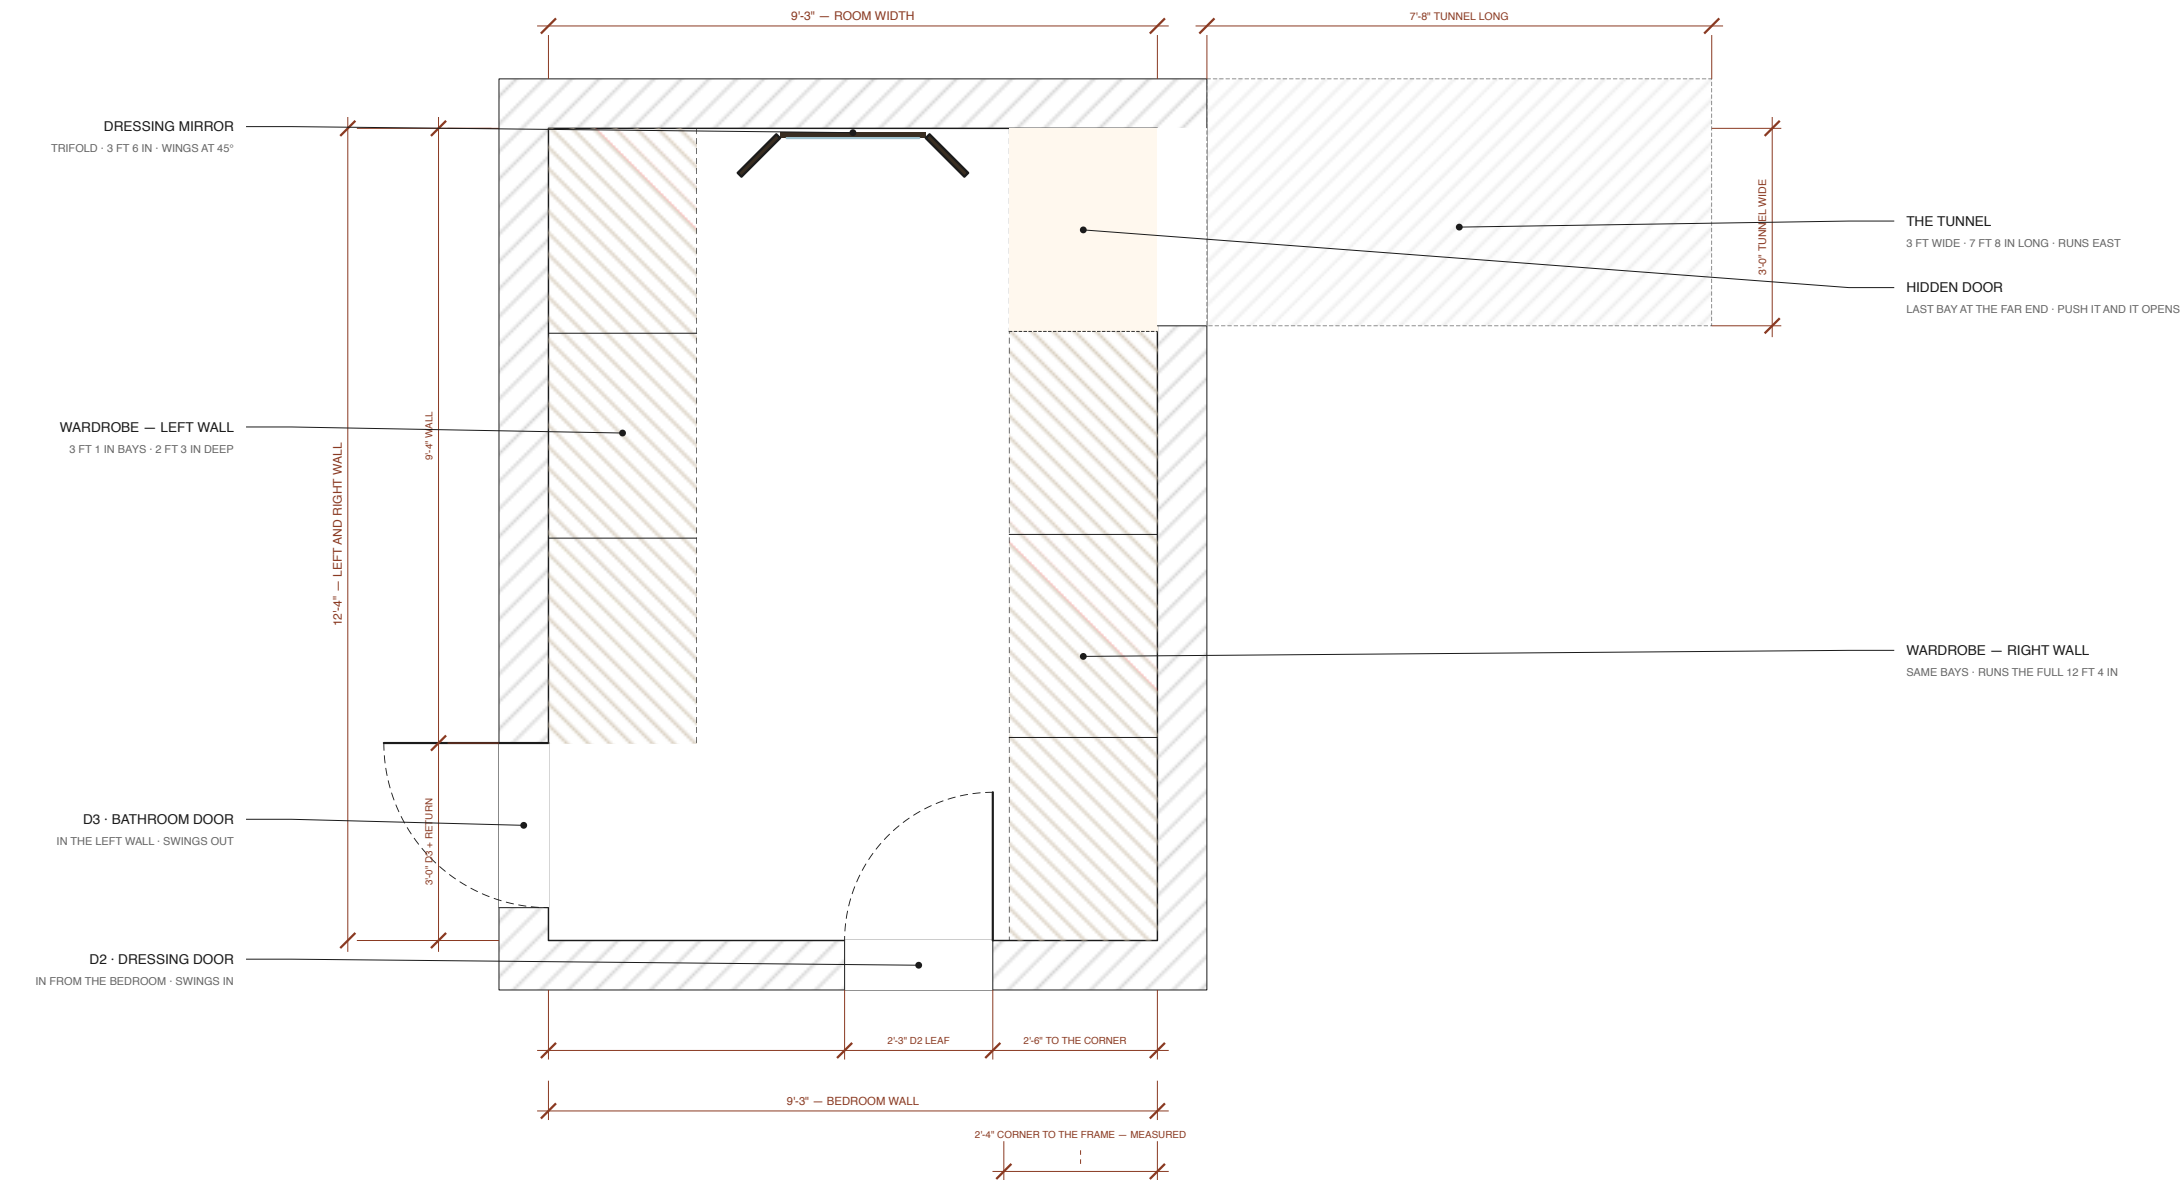

NOTES

REVISION 3

Third pass, and this one copies the sketch rather than interpreting it. The two earlier drawings both had the shape wrong; everything below is read straight off the owner's own clean drawing.

The BEDROOM wall is the bottom wall here, 9 ft 3 in, and it carries D2, the existing dressing door in from the bedroom, 2 ft 4 in from the right-hand corner to the door FRAME — measured on both sides of the wall, and the figure that now governs. The sketch's 2 ft 0 in is superseded.

The BATHROOM door, D3, is in the LEFT wall, at the bedroom end — not in the bedroom wall. The sketch runs 9 ft 4 in of wall down from the far corner and then opens the door.

The TUNNEL runs EAST, straight out of the far end of the right wall, 3 ft wide and 7 ft 8 in long, its far side flush with the far wall. The hidden door is the last wardrobe bay in front of it: built and shelved like every other bay, so from the room it reads as one more cupboard.

Ceiling 9 ft 1 in, plain, over the left and right sides — the same height as the main room. A domed centre rises to 10 ft 0 in, so the wardrobes are capped at 9 ft 0 in, clear under it.

SETTLED — D2 sits 2 ft 4 in from the corner to its frame, on both sides of the wall. That closes this sheet against AST-DR-000 and AST-DR-007: this room's right-hand corner and the bedroom's bed-wall corner are the same corner. Walls are taken at 9 in throughout. See AST-DR-024.

OPEN — D3's width. It is drawn 2 ft 6 in, as the owner said, but the sketch's own 9 ft 4 in against 12 ft 4 in leaves 3 ft 0 in — so a 6 in return is shown into the corner. To confirm.

SETTLED — the wardrobes are 2 ft 3 in deep, so the right-hand run reaches the bedroom wall and clears D2's frame, 2 ft 4 in off that corner, by 1 in.

OPEN — the left run is drawn stopping at D3. Whether it ends there or returns over the door is not decided.

OPEN — where the tunnel leads, and what is at its far end.

OPEN — the dome's own shape: how far along the room it runs, and its profile.

The mirror is the confirmed trifold, 3 ft 6 in across with its wings at 45° — see AST-DR-027.

A STUDY IN TEAK

Particulars of the room

DRESSING ROOM

Shell and layout · third pass

SCALE
1:35 @ A3



DATE
25.09.2026

REV
3 — drawn off the owner's clean sketch: bathroom door on the LEFT wall, dressing door on the bedroom wall, tunnel running east

DWG
AST-DR-023

DRESSING MIRROR — TRIFOLD

CONFIRMED · CENTRE GLASS 2 ft 0 in · WINGS AS WIDE AS THE 3 FT 6 IN ALLOWS · 45° · WHOLE FRAME INSIDE 3 FT 6 IN

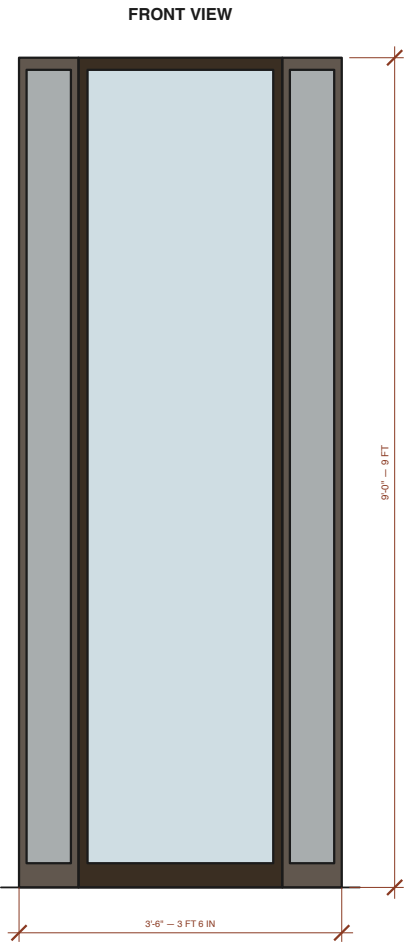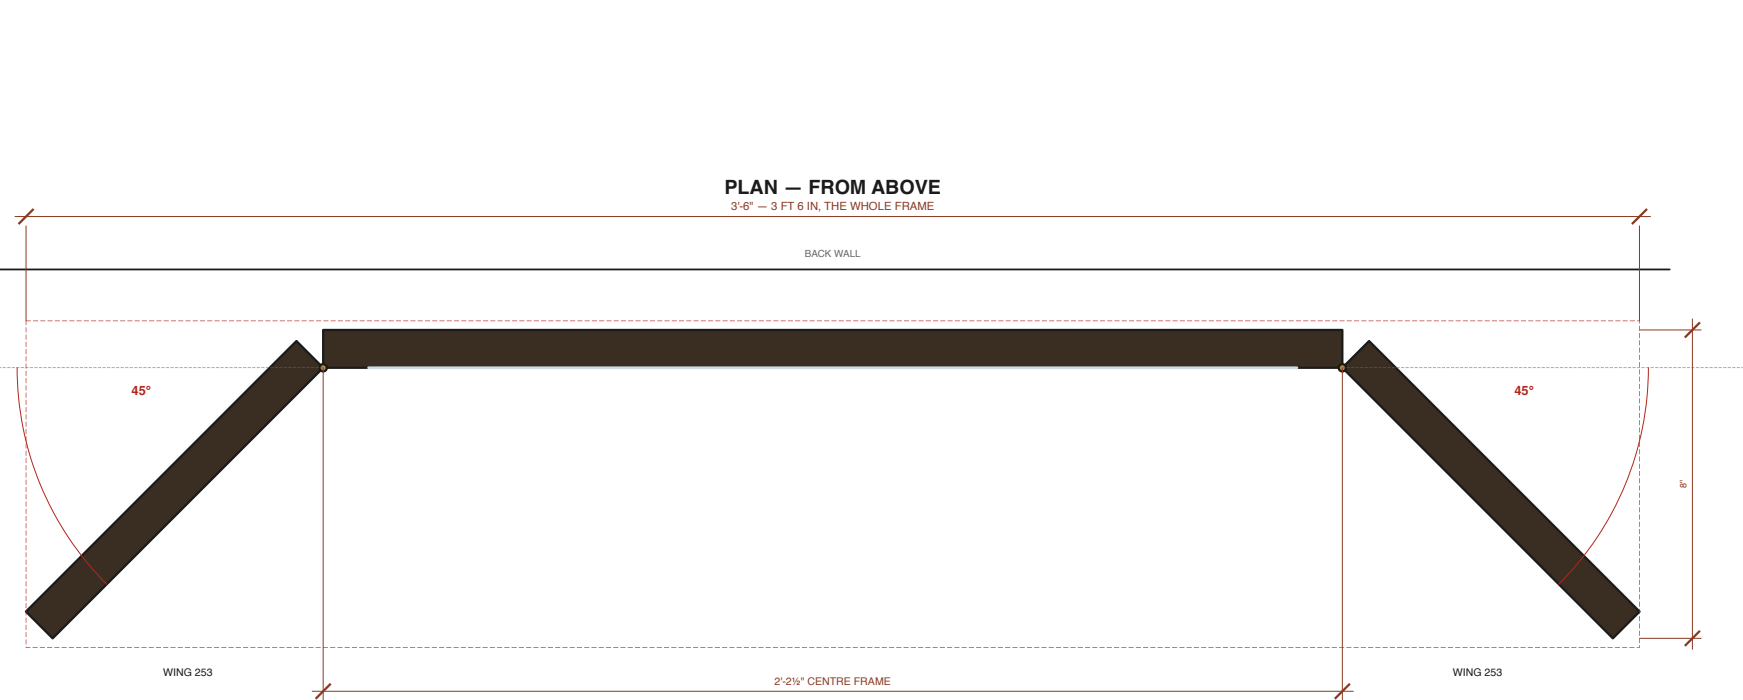

	FRAME	GLASS
Centre	2 ft 2½ in	2 ft 0 in
Each wing	10 in	7½ in
Height	9 ft 0 in	8 ft 9½ in
Wings	45° forward, fixed stop	
Whole frame across	3 ft 6 in	
Stands off the wall	8 in	
Floor either side	7½ in	

NOTES

CONFIRMED

CONFIRMED by the owner: wings at 45°, and the whole frame — wings angled — inside 3 ft 6 in across

(the red dashed box). All three panels 9 ft tall, level with the wardrobes.

FINAL: centre glass 2 ft 0 in; the wings take everything the 3 ft 6 in frame has left at 45° —

about 7½ in of glass each. Only two things would give bigger wings: a slimmer frame (¾ in

frame → about 9¼ in), or a steeper angle (60° → about 11¼ in).

The wings need a fixed stop at 45°. Opened any flatter, the frame gets wider than 3 ft 6 in.

Hinges: two continuous piano hinges on the back, one at each joint, in the frame finish.

Free-standing, centred on the far wall. 7½ in of floor either side, clear of the folding

end-bay doors, which come out only about 3 in at this depth. Frame finish still open.

A STUDY IN TEAK

Particulars of the room

DRESSING MIRROR

Trifold · confirmed

SCALE

1:5 AND 1:25 @ A3

REV

5 — FINAL: centre glass 2 ft 0 in, wings at 45°

DATE


26.09.2026

DWG

AST-DR-027


FRONT

1:10 · MARBLE THE FULL 5 FT · THE BOWL SITS UNDER THE FAUCET, 6 IN RIGHT OF CENTRE

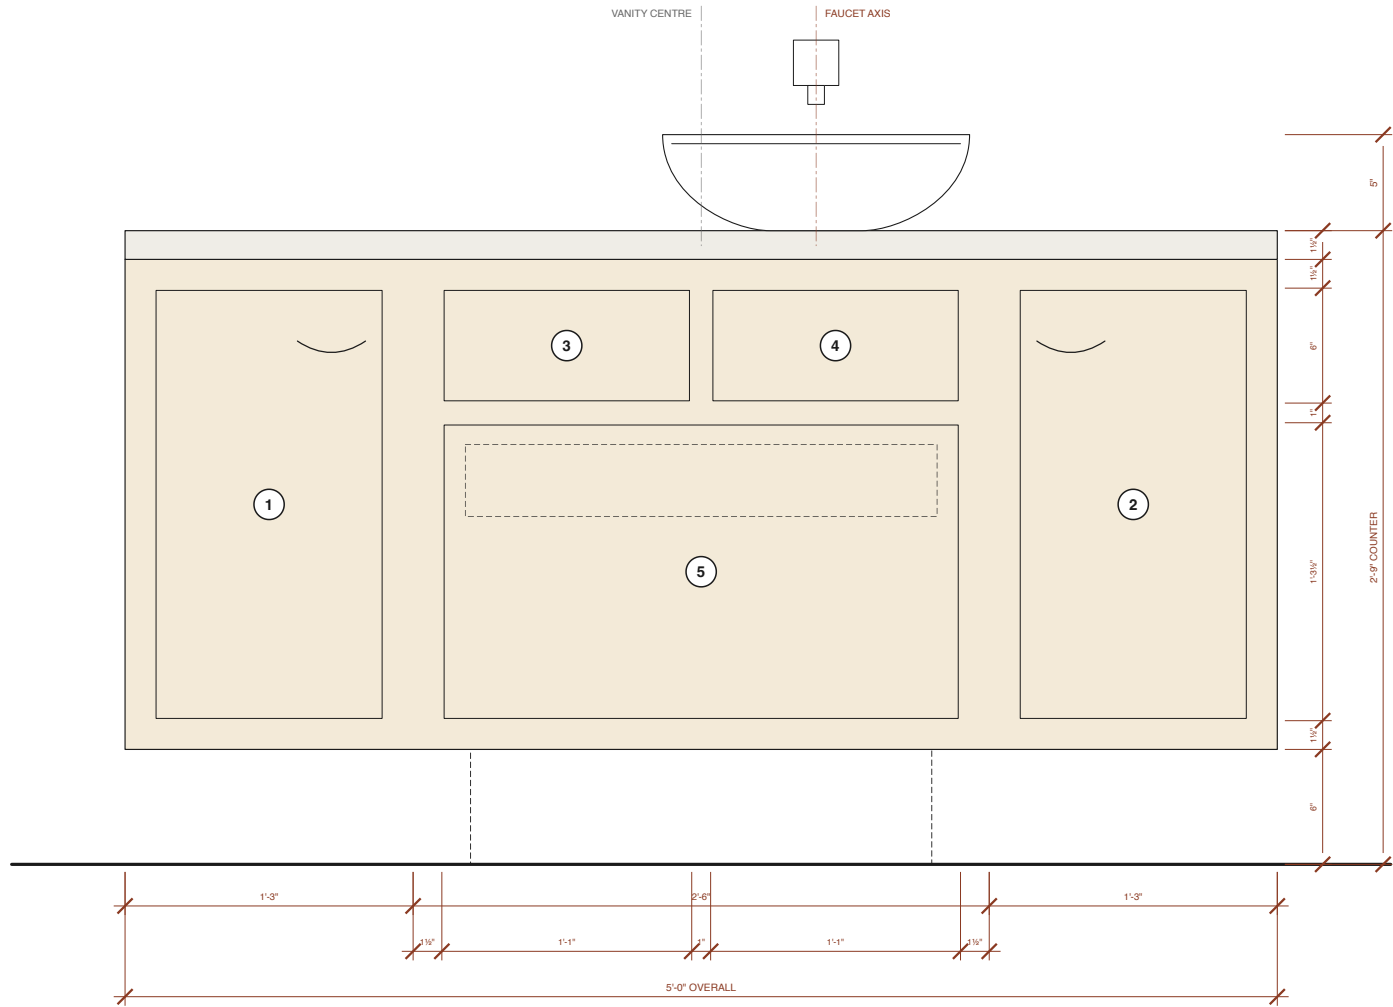

PLAN

1:10 · FROM ABOVE · WALL AT THE TOP

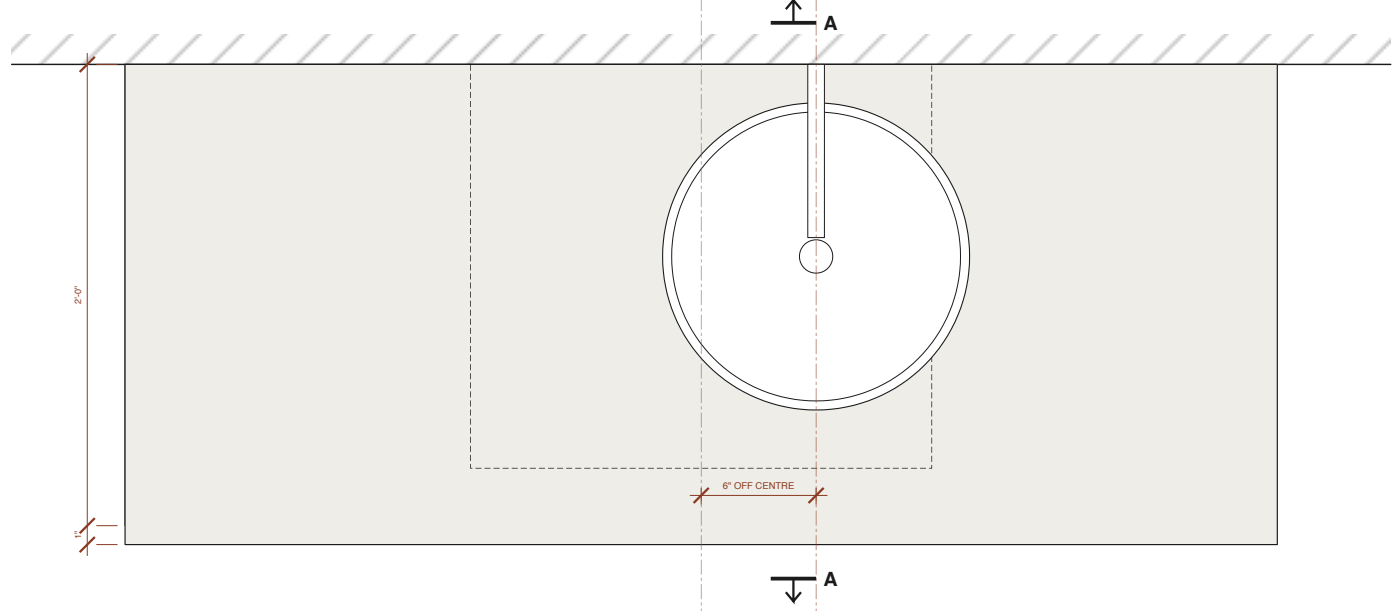

SECTION KEY

- A** Hanging cleat

D Support, set back 76

G Inner drawer
- B** Big drawer, U-box

E Wall spout
- C** Waste Ø40 and P-trap

F Ply sub-top

NOTES

REVISION 1
Symmetric about the vanity's centre — except the bowl, which has to sit under the faucet, 152 right of it.
The waste drops through the right-hand TOP drawer as well as the big one: both are U-boxes (see section).


OPEN — bowl Ø406 × 127 and the spout are assumed.

With the bowl on a 838 counter its rim is at 965 (38 in).

OPEN — the support's design: reference photos to come.


SECTION A–A

ON THE FAUCET AXIS · 1:10

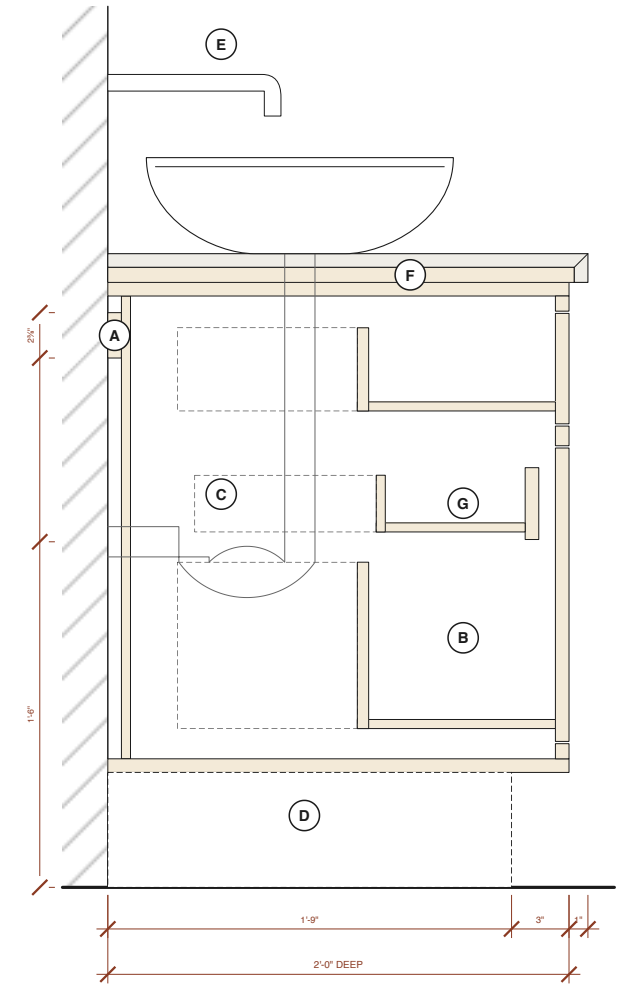


DETAIL 2 · THE BIG DRAWER

PLAN · 1:15 · INNER DRAWER DASHED

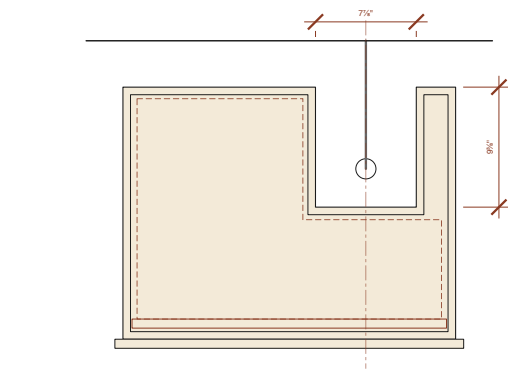

DETAIL 1 · THE MARBLE EDGE

SECTION · 1:2

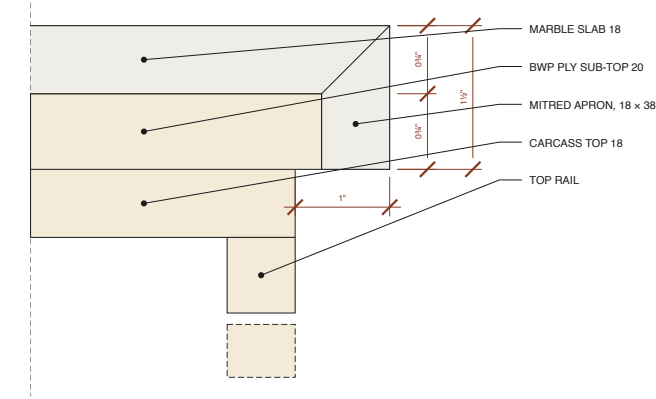

FRONTS

SIZES ARE THE FRONT ITSELF · 3 MM GAP ALL ROUND

No.	WHAT	W × H	FT-IN
1	Door, cup pull	299 × 566	11¾" × 1'10¼"
2	Door, cup pull	299 × 566	11¾" × 1'10¼"
3	Top drawer, push-open	325 × 146	1'0¾" × 5¾"
4	Top drawer, push-open	325 × 146	1'0¾" × 5¾"
5	Big drawer, U-box, push-open	680 × 388	2'2¾" × 1'3¼"
5a	Inner drawer, finger scoop	624 × 95	2'0½" × 3¾"

MATERIALS

THE ROOM'S PALETTE — NOTHING NEW

- Top**

Beige-gold marble, the bathroom stone. 18 slab

on a 20 BWP sub-top, mitred 38 apron, polished.
- Carcass**

18 BWP / marine ply, teak veneer both faces.

Every edge sealed — it stands in a wet room.
- Fronts**

18 BWP, teak veneer, 6 solid leak lipping.
- Runners**

Undermount, full extension. Drawers push-to-open —

no handles on them; the doors keep cup pulls.
- Fittings**

Chrome — already bought. Door cup pulls to match.
- Hanging**

18 ply cleat on the wall, 700–760 high.
- Inner**

A U-box on its own runners, above the big

drawer's low sides — see AST-DR-022.

A STUDY IN TEAK

Particulars of the room

VANITY — NORMAL

Marble full length · Door · Drawers · Door

SCALE AS NOTED @ A3	DATE 23.09.2026
REV 1 — as sketched	DWG AST-DR-019

1:10 · A 1 FT VENEER CUPBOARD LEFT · 4 FT OF MARBLE CENTRED ON THE FAUCET



- Taking 1 ft off the left moves the marble's centre 6 in right — onto the faucet. Bowl, drawer split and support all sit on that one line. The top drawers split on it, so the waste drops between them: only the big one is a

OPEN — bowl Ø406 x 127 and the spout are assumed.

With the bowl on a 838 counter its rim is at 965 (38 in).

OPEN — the support's design: reference photos to come.

ON THE FAUCET AXIS · 1:10



THE ROOM'S PALETTE — NOTHING NEW


Particulars of the room

1 ft cupboard left - 4 ft marble on the faucet

SCALE AS NOTED @ A3	DATE 23.09.2026
REV 1 — as sketched	DWG AST-DR-020


FRONT

1:10 · CHOSEN · 1 FT 6 LEFT, 6 IN RIGHT · 3 FT MARBLE BANK ON THE FAUCET, DOWN TO THE FLOOR

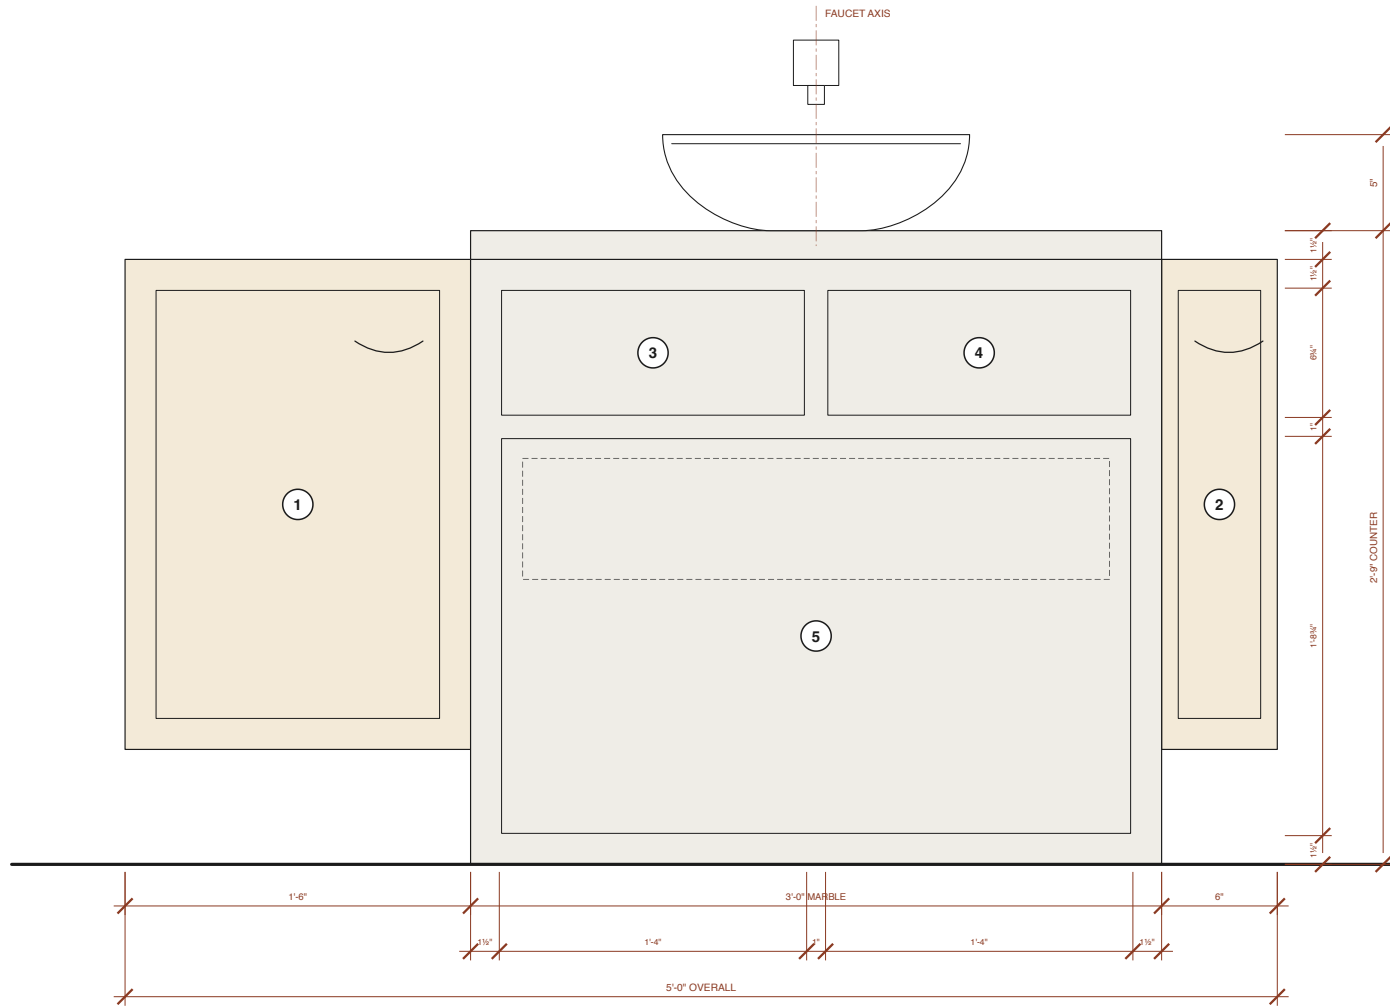

PLAN

1:10 · FROM ABOVE · WALL AT THE TOP

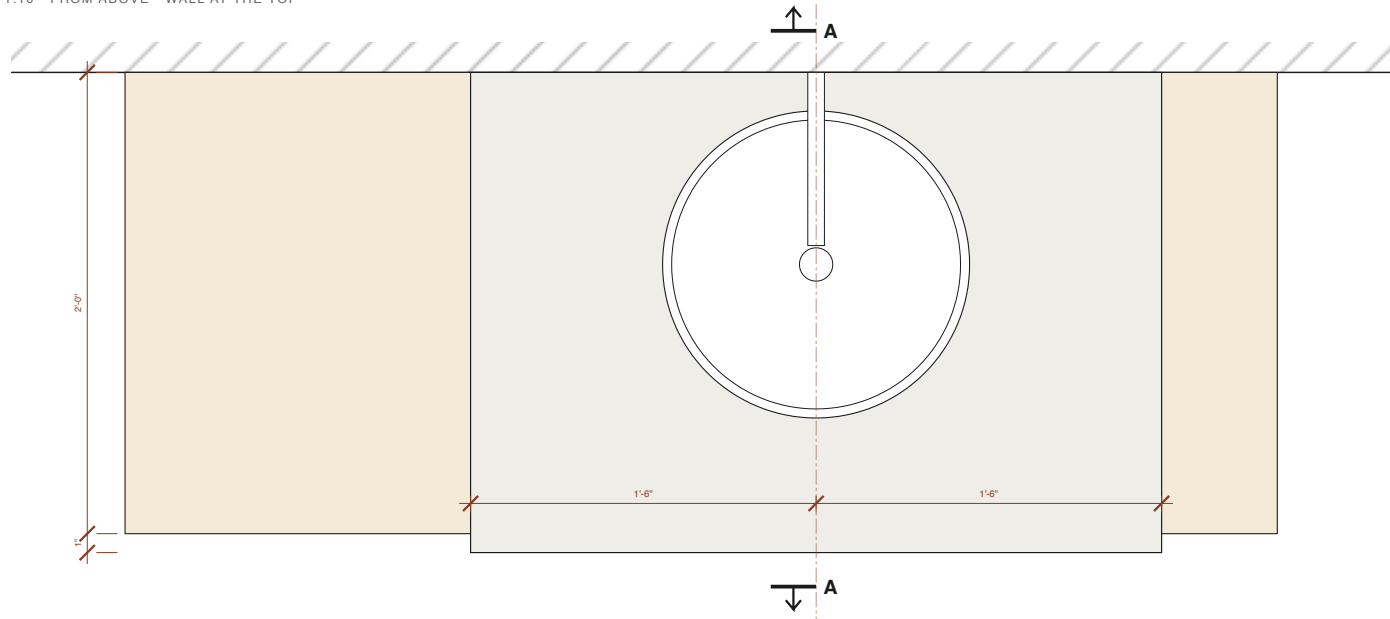

SECTION KEY

- (A) Hanging cleat (B) Big drawer, U-box (C) Waste Ø40 and P-trap
(E) Wall spout (F) Ply sub-top (G) Inner drawer


NOTES

REVISION 2
The marble bank now runs to the floor and is the support.
Top drawers: 6½ in fronts. Drawer within: a 5½ in box.
The big drawer takes the rest: 20½ in front, 12½ in clear
under the inner drawer for tall bottles.

OPEN — bowl Ø406 × 127 and the spout are assumed.
OPEN — marble front thickness and how it is bonded to the
drawer boxes: stone supplier to confirm.
The ends are pull-outs, the same height as before.


SECTION A–A

ON THE FAUCET AXIS · 1:10

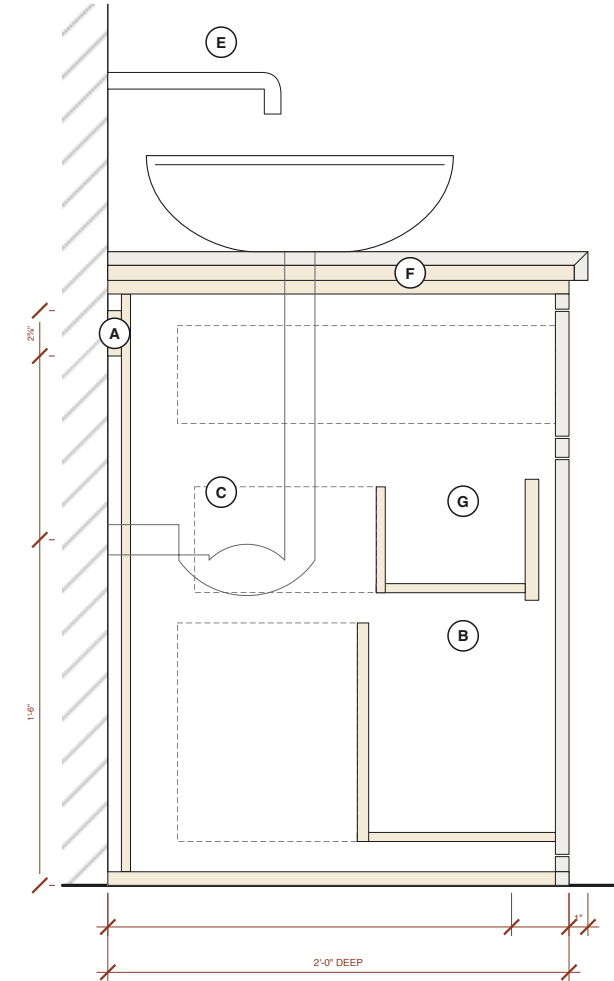


DETAIL 2 · THE BIG DRAWER

PLAN · 1:15 · INNER DRAWER DASHED

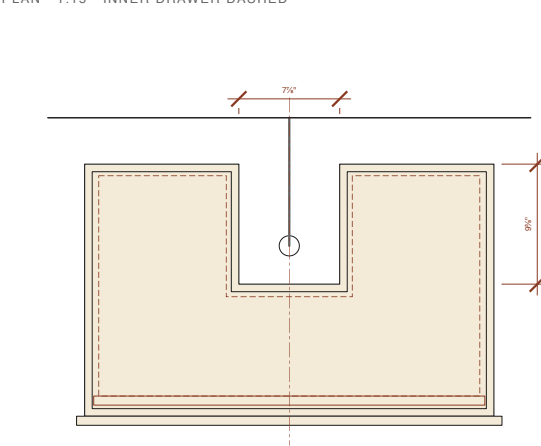

DETAIL 1 · THE MARBLE EDGE

SECTION · 1:2

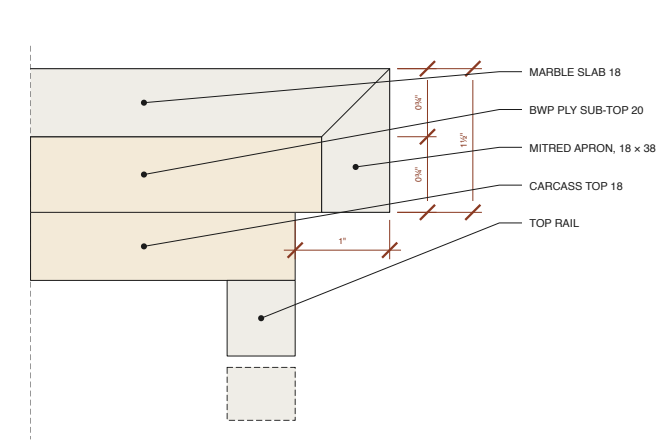

FRONTS

SIZES ARE THE FRONT ITSELF · 3 MM GAP ALL ROUND

No.	WHAT	W × H	FT-IN
1	Pull-out cabinet, cup pull	375 × 566	1'-2¾" × 1'-10½"
2	Pull-out cabinet, cup pull	109 × 566	4¼" × 1'-10½"
3	Top drawer, push-open · marble	401 × 165	1'-3¾" × 6½"
4	Top drawer, push-open · marble	401 × 165	1'-3¾" × 6½"
5	Big drawer, U-box, push-open · marble	832 × 522	2'-8¾" × 1'-8½"
5a	Inner drawer, finger scoop	776 × 160	2'-6½" × 6¼"

MATERIALS

THE ROOM'S PALETTE — NOTHING NEW

- Top** Beige-gold marble, the bathroom stone. 18 slab
on a 20 BWP sub-top, mitred 38 apron, polished.
- Bank** The same beige marble on the face frame and on
every drawer front, floor to counter. It stands
on the floor and carries the top — no support.
- Ends** Two pull-out cabinets, 9292 cream burl veneer,
high gloss, 18 BWP, edges sealed. 6 in off the floor.
- Ledges** The two veneer tops: solid nosing, sealed.
- Runners** Drawers: undermount, push-to-open. Pull-outs:
heavy full-extension runners, cup pull.
- Fittings** Chrome — already bought.
- Inner** U-box, 5½ in deep, on its own runners — AST-DR-022.

A STUDY IN TEAK

Particulars of the room


VANITY — SCHEME C

Chosen · marble bank to the floor · pull-outs each end

SCALE AS NOTED @ A3	DATE 30.09.2026
REV 2 — chosen: marble bank to the floor	DWG AST-DR-021


1 · CLOSED

SECTION THROUGH ONE ARM · 1:5 · SCHEME C, CHOSEN — BANK TO THE FLOOR

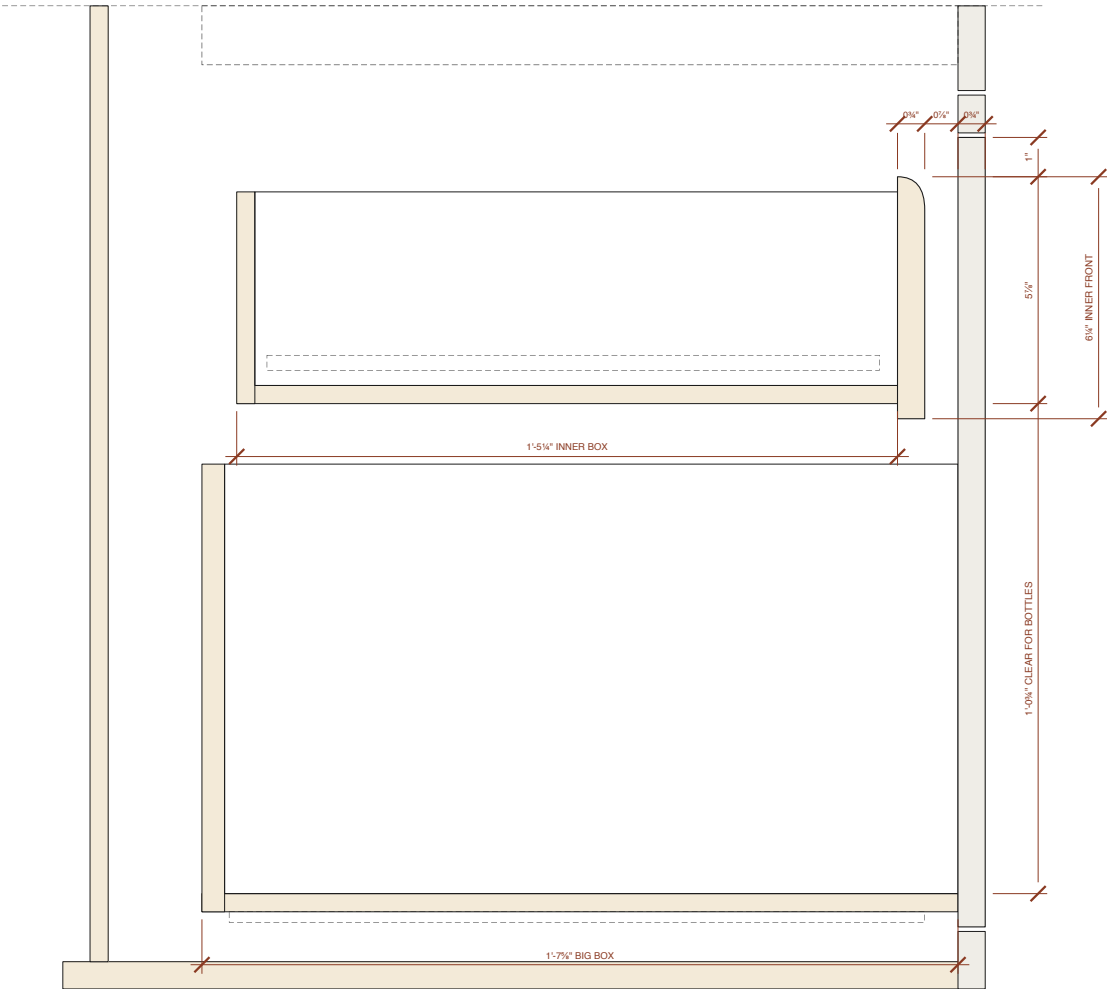


4 · FRONT

THE INNER DRAWER HIDES BEHIND THE BIG FRONT · 1:10 · MARBLE BANK, FLOOR TO COUNTER

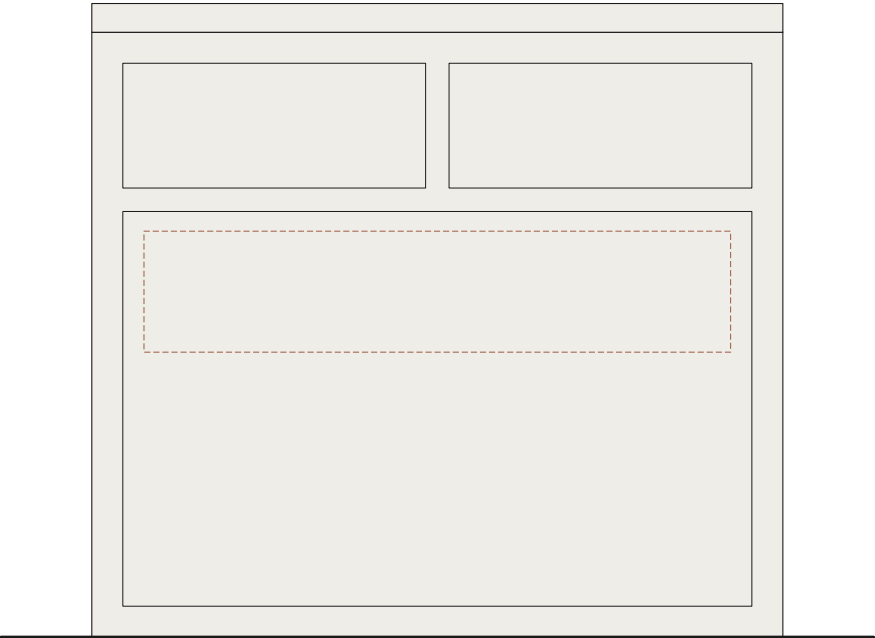


2 · OPEN

BIG DRAWER OUT · INNER ONE PULLED OUT BEHIND ITS FRONT · 1:10

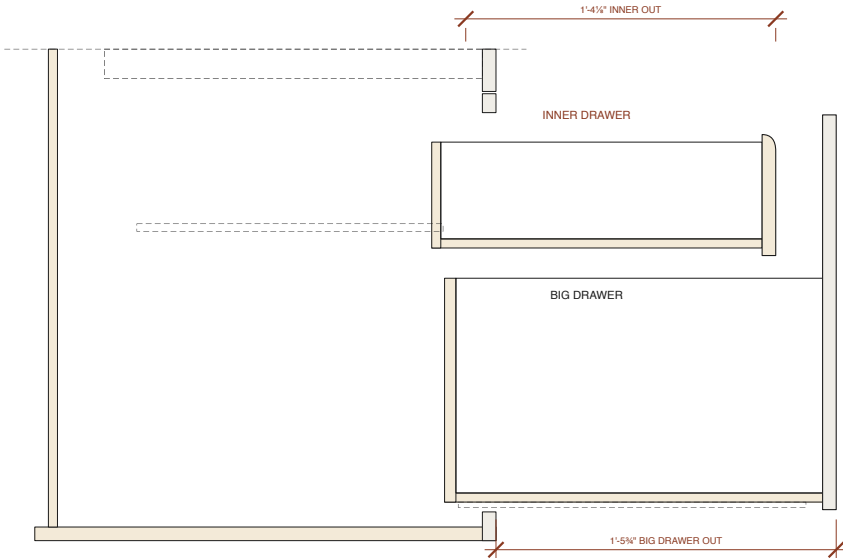

3 · PLAN

BOTH DRAWERS SHUT · 1:10 · THE PIPE DROPS THROUGH BOTH NOTCHES

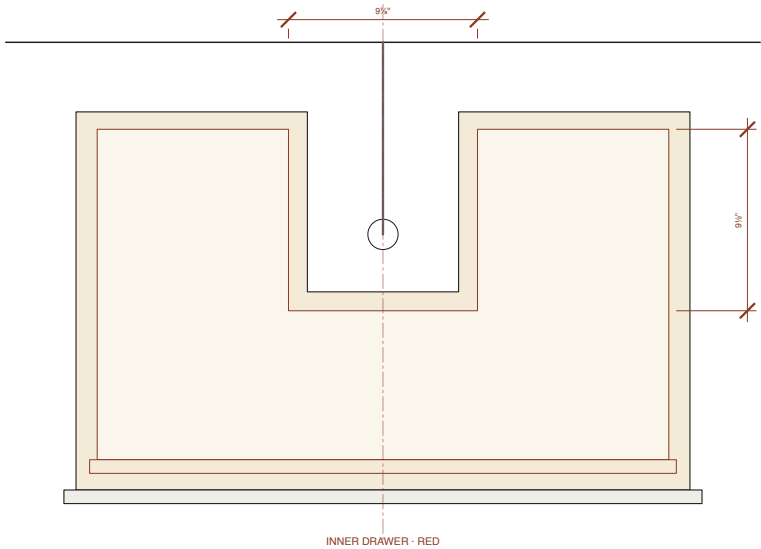

SIZES

THE SAME DRAWER IN ALL THREE SCHEMES

SCHEME	BIG FRONT	INNER FRONT	INNER BOX W
Normal	680 × 388	624 × 95	604 · L
B	1138 × 388	1082 × 95	1062 · U
C	832 × 522	776 × 160	756 · U

Scheme C (chosen): inner box 437 deep, 140 high (5 1/2 in), 12 ply; notch 250 wide.

HARDWARE

Big drawer	Undermount runners, full extension, push-to-open. Its sides stop at 347 to pass under the inner.
Inner drawer	Side-mounted runners 400, full extension, on the carcass partitions at 409–419. Independent.
Inner front	18 BWP, teak veneer both faces, top edge scooped for a finger. No handle.

NOTES

REVISION 2

Open the big drawer: the inner one stays put. Pull it and it comes out 410 behind the big front, over the bottles — the tray in the kitchen drawer photographed.

Both are U-boxes. The waste pipe drops through their notches whichever drawer is shut; neither may be solid across the back.

It can never pass the big front — that front is solid. Shut, it stands 22 behind it.

Below the inner drawer: 324 clear — tall bottles stand.

Normal version: the pipe is off centre, which leaves the inner drawer a 25 right arm. Too thin to keep — that arm is left off and the inner drawer is an L.

A STUDY IN TEAK

Particulars of the room

VANITY — DRAWER WITHIN


The big drawer, and a drawer inside it

SCALE AS NOTED @ A3	DATE 30.09.2026
REV 2 — scheme C: 5 1/2 in inner box, bank to the floor	DWG AST-DR-022

DRESSING ROOM — THE END-BAY DOORS


THREE WAYS TO OPEN THEM WITHOUT HITTING THE FREE-STANDING MIRROR · PLANS

THE ROOM — END BAYS OPEN AS A

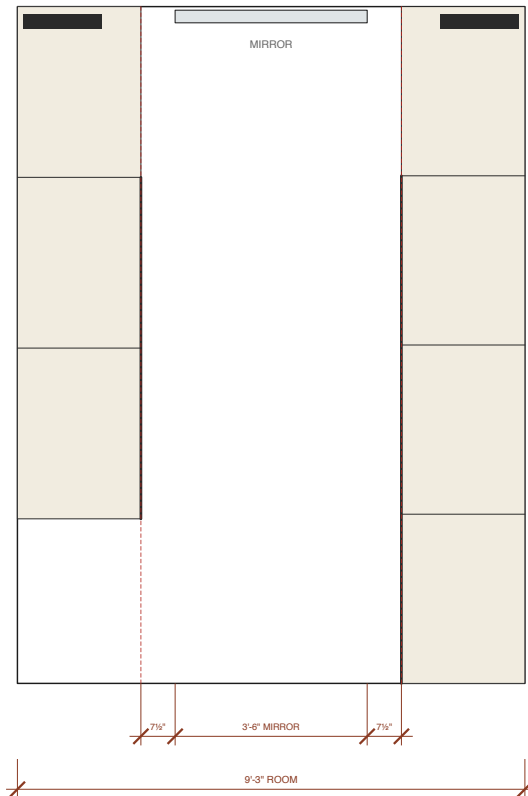


OPTION A

FOLDS IN · PARKS AT THE MIRROR END

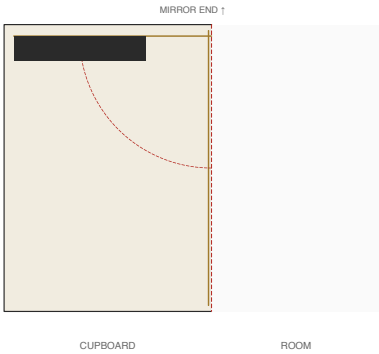


OPTION B

FOLDS IN · PARKS AT THE FRONT END

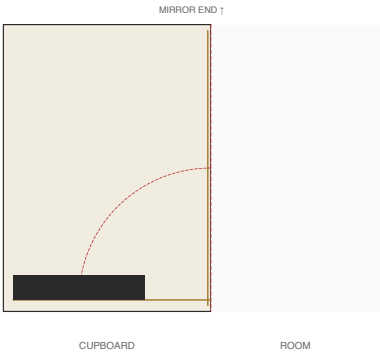

OPTION C

FOLDS OUT, THEN SLIDES IN · FRONT END

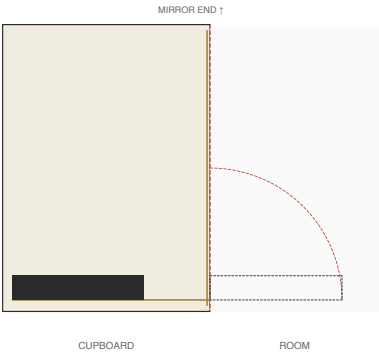

- the folded pair of doors, open
- dashed red — the wardrobe front / the path of the fold
- brass — head track along the front, runner along the side

HINGES AND HARDWARE

- CENTRE HINGE**
Continuous brass piano hinge, full height, between the two leaves. INSIDE face for A and B; room face for C.
- PARKING LEAF**
Top and bottom pivot pins on a carriage that runs in a runner along the side panel. The same for A, B and C.
- FREE LEAF**
Guide roller at the top, running in the head track along the front; small guide at the floor. All three options.
- PUSH-BACK**
All three. Folded pair is about 1 ft 6 in deep, 3 in thick; the 2 ft 3 in cupboard lets it go back about 8 in.
- HANGING RAIL**
Stop it about 4 in short of the side panel the pair parks against. Nothing else inside the bay changes.

NOTES

REVISION 2

Why not ordinary hinges: a leaf at the back of either run swings about 1 ft 6½ in into the room, and the mirror (3 ft 6 in across, centred) leaves only 7½ in beside it. It would hit the mirror.

Two leaves hinged together always fold into a triangle. A and B put the triangle INSIDE the cupboard and push the folded pair back, so nothing ever passes the wardrobe front.

C folds out into the room first, like the owner's photo, then slides back in the same way. It crosses the wardrobe front only while folding, at the front end of the bay, well away from the mirror.

Revision 1 of this sheet showed the pair folding flat against the front — that cannot be built and is withdrawn. The video on the Dressing page shows all three moving.

A — parks at the mirror end: you reach in from the front, never from behind the mirror.

B — parks at the front end: same mechanism, other side of the bay.

C — while it folds, it stands about 1 ft 6 in into the room; once slid in, the corridor is clear.

The tunnel bay works the same way; in A and B its folded pair can slide right back into the tunnel, out of sight.

CHOSEN — C, confirmed by the owner. A and B are kept here for reference.

A STUDY IN TEAK

Particulars of the room

END-BAY DOORS

Dressing room · three ways to open

SCALE
1:42 AND 1:25 @ A3


DATE
26.09.2026

REV
3 — option C chosen

DWG
AST-DR-026


PLAN

AN ALL-GLASS WALL · BOTH ENDS TURN 55° TOWARDS THE BED · 1:20

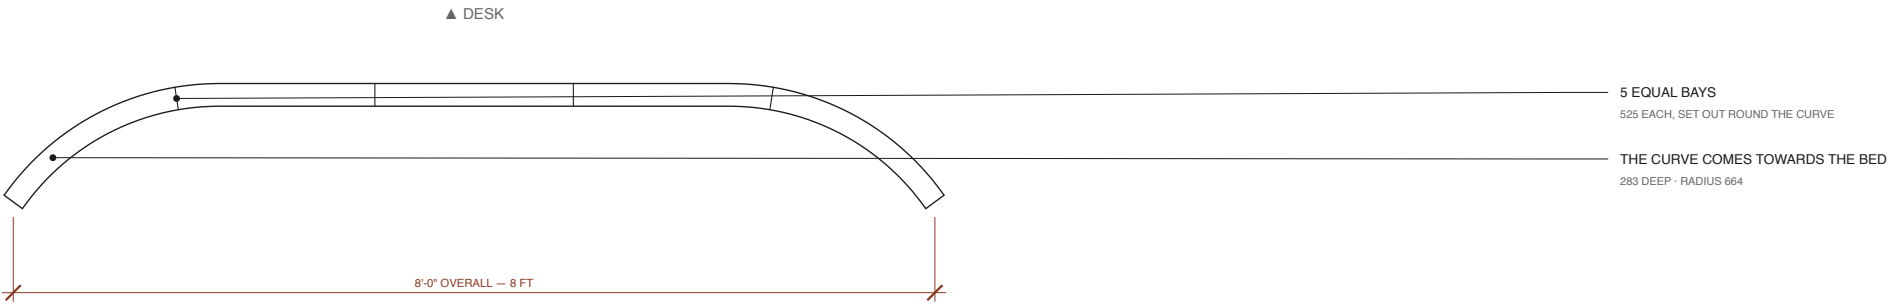

ELEVATION

THE CURVE UNROLLED FLAT · BOTH FACES THE SAME · 1:22

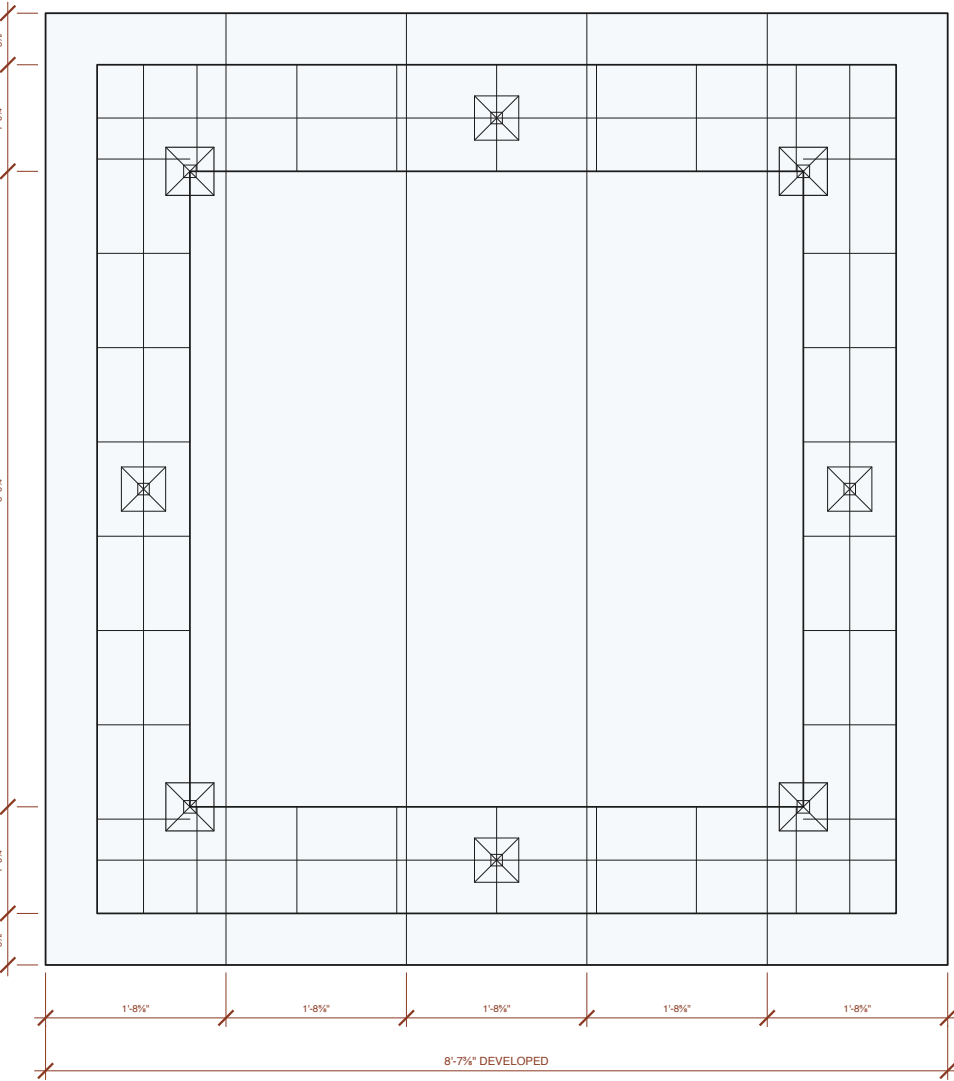

ALL GLASS. One composition across the whole wall — the border runs straight through the bay joints.

Border: an outer rectangle 150 in from every edge and an inner one 420 in at the sides, 460 at head and foot,


joined by a short bar at the middle of each side, with a cross at each corner of the inner rectangle.

All the leading is in the ring between them. The field inside the inner rectangle is one clear sheet.

White textured glass in lead came. No colour. The television is shown for position only — how it is carried is not drawn.


WITH THE TELEVISION

THE SAME WALL · THE SET CENTRED · 1:22

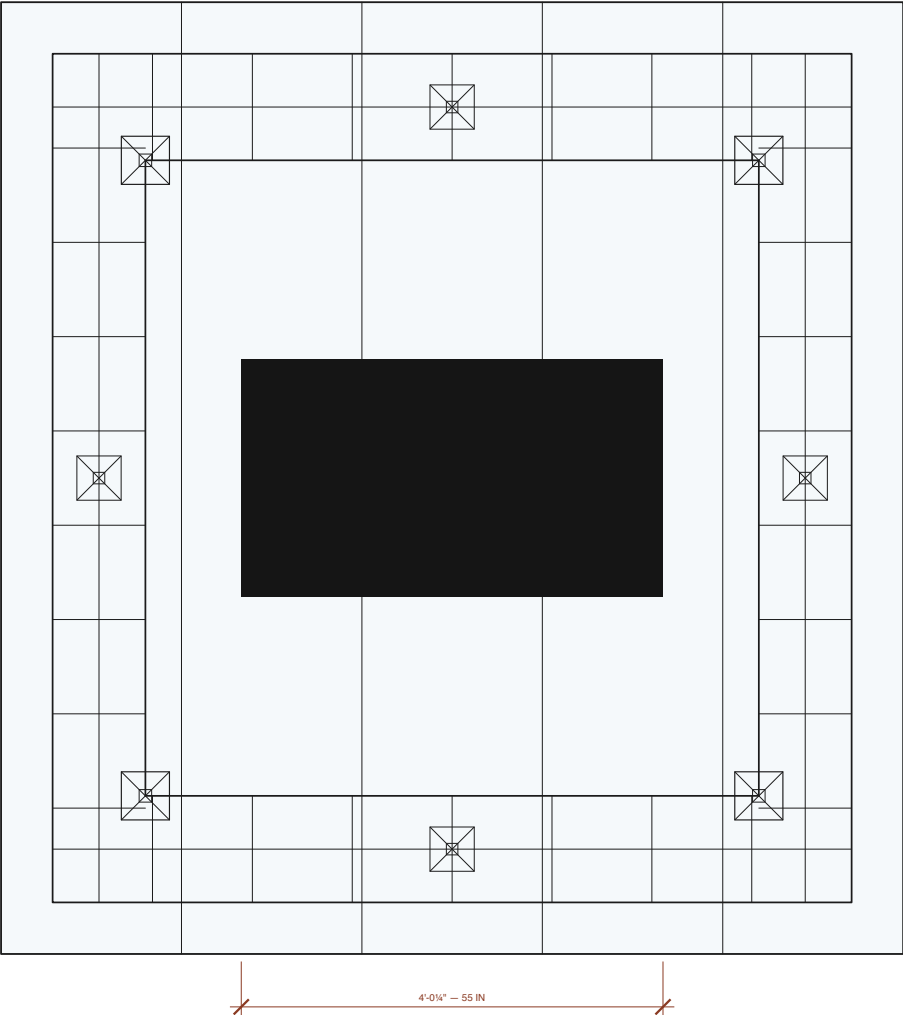

THE CURVE


PLAN · 1:10

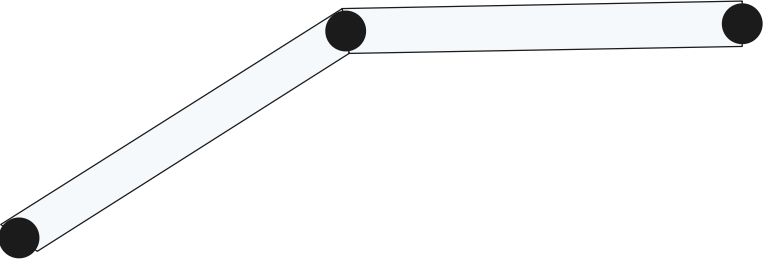

Every bay is flat. The came at each joint takes the angle — no glass is bent.

AXONOMETRIC

FROM THE BED SIDE

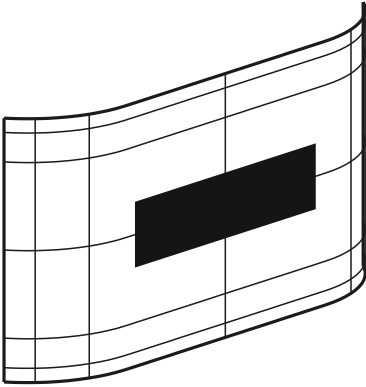

A STUDY IN TEAK

Particulars of the room

PARTITION — LEADED GLASS

Plan · Elevation · With the television · Curve · Axonometric

SCALE
AS NOTED @ A3


DATE
18.09.2026

REV
2 — the border only; the field inside stays clear

DWG
AST-DR-010

THE SHARED WALL — RECONCILED

AST-DR-000 AND AST-DR-023 SET OUT FROM ONE MEASUREMENT — 2 FT 4 IN, CORNER TO THE DOOR FRAME

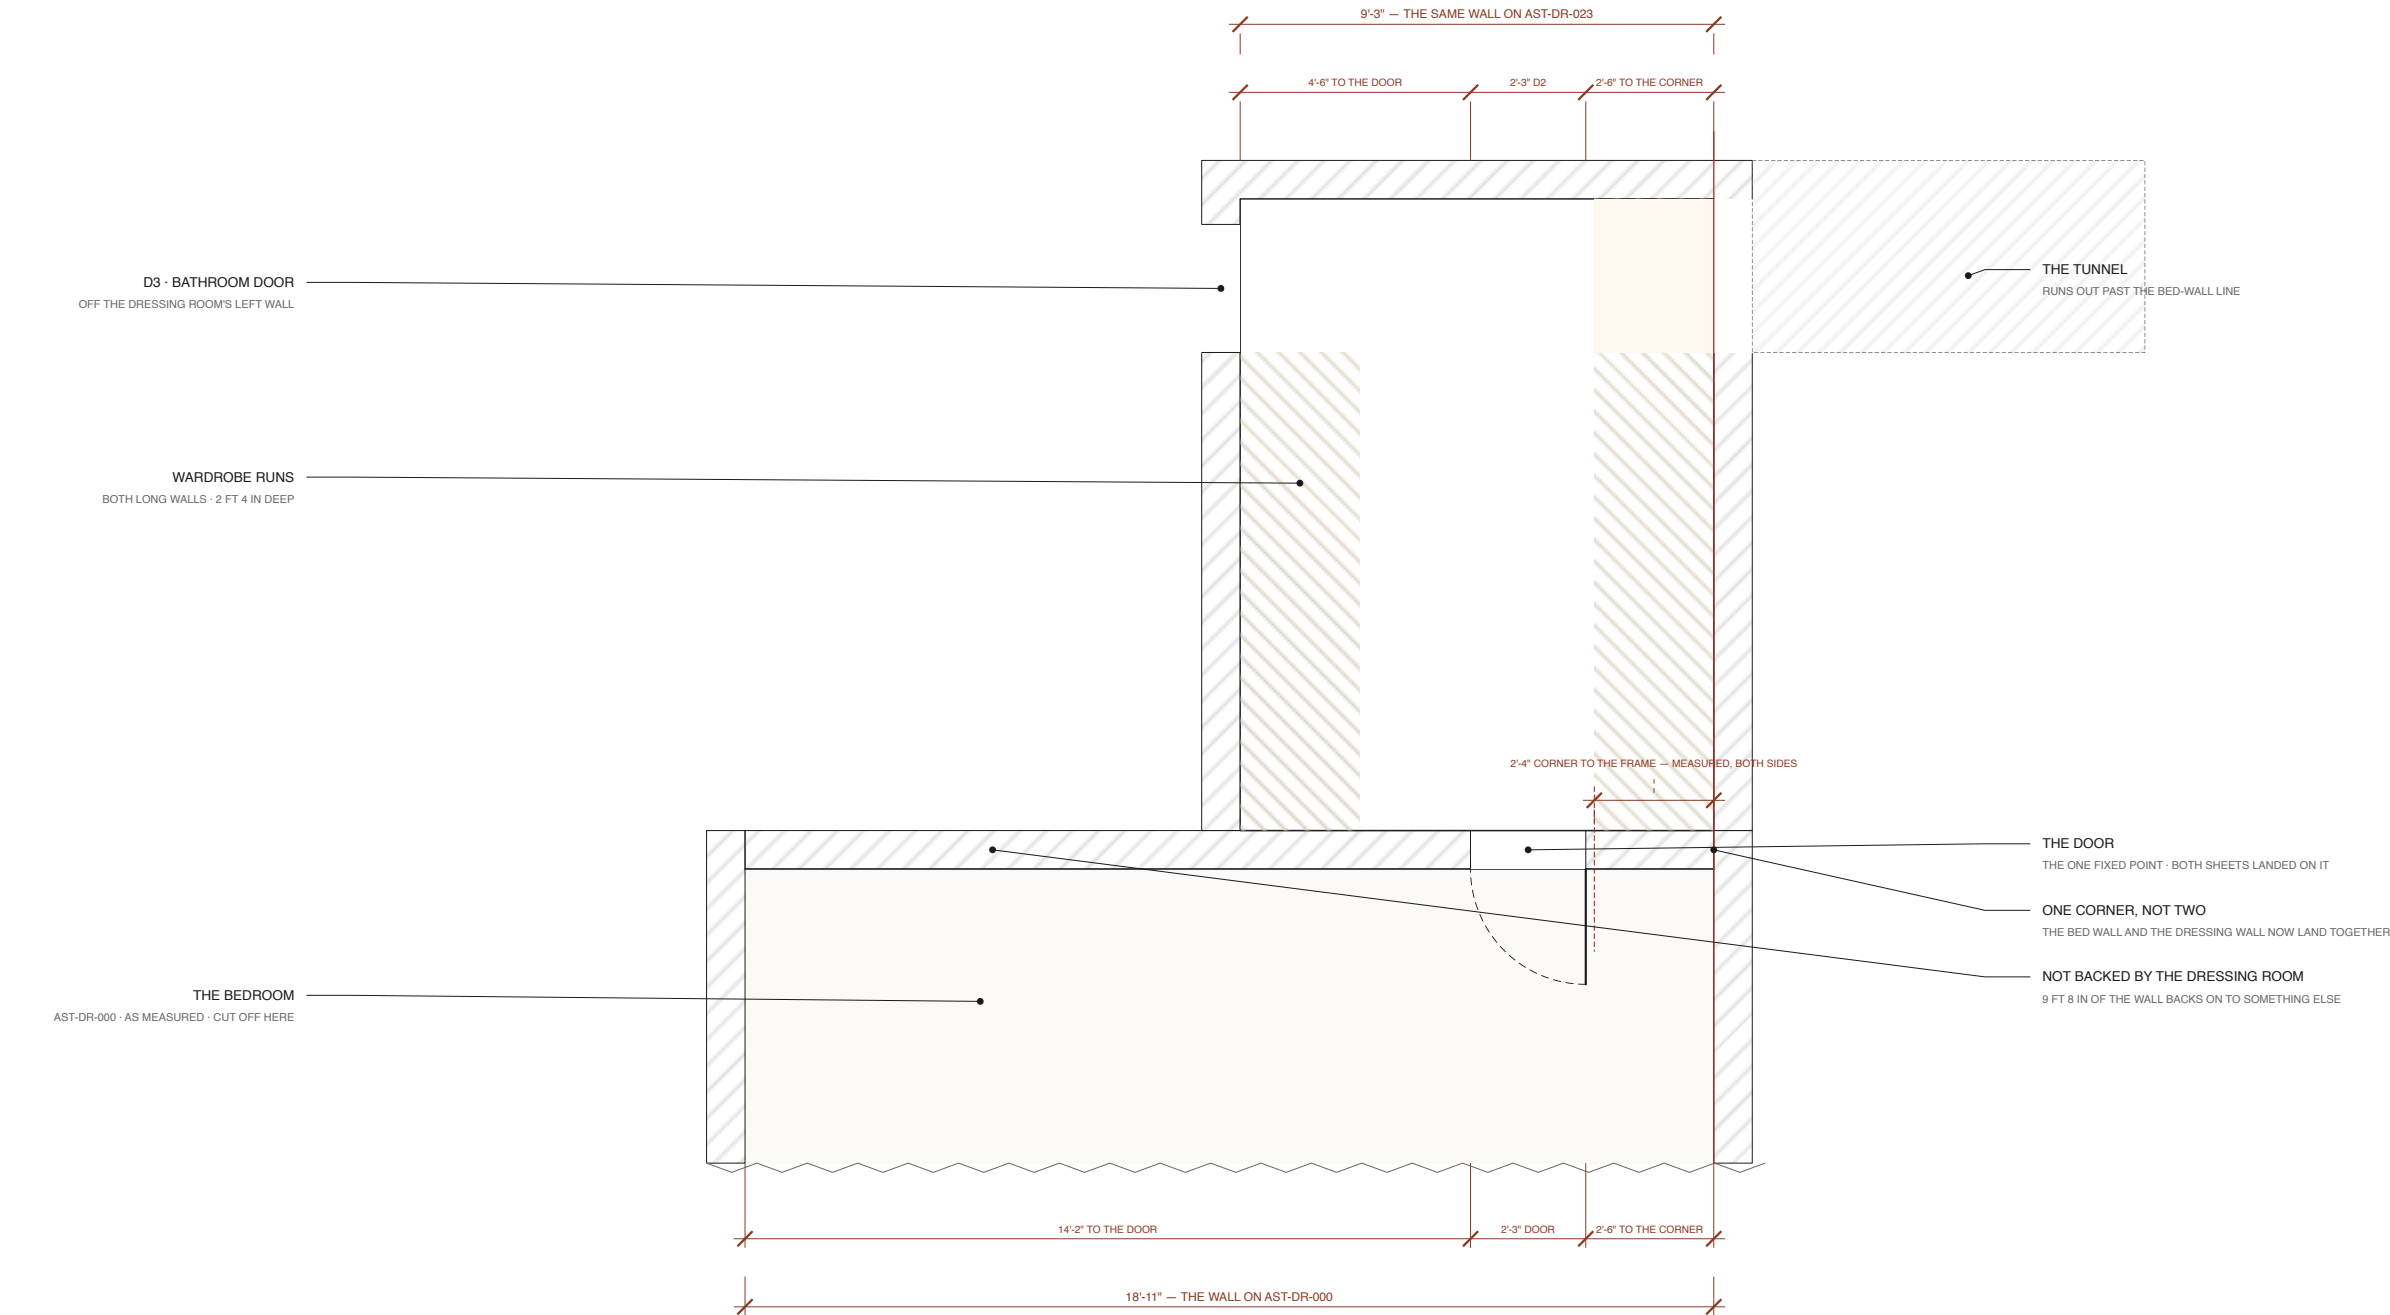

HOW IT WAS SETTLED

ONE MEASUREMENT, TAKEN ON BOTH SIDES, NOW GOVERNS BOTH SHEETS

THE CONTROL — 2 ft 4 in from the dressing corner to the door FRAME, taped on both sides of the

wall. Everything on this wall is now set out from that and nothing else. It replaced two figures

that disagreed: 2 ft 9 in on AST-DR-000, which had been back-calculated rather than measured,

and 2 ft 0 in on the dressing sketch, which was a reading off a hand drawing.

WHAT IT FIXED — with a 3 in lining the chain now closes: frame 13 ft 7 in from the study corner

(the tape said 13 ft 6 in), the 3 ft frame, then 2 ft 4 in to the corner, on the measured

18 ft 11 in overall. Both corners now fall on the same line, so the dressing room's right-hand

wall and the bedroom's bed wall are one wall, not two a hand's width apart.

WALLS — taken at 9 in throughout, as instructed. AST-DR-000 already carried 230 mm, which is the

same 9 in, so the two sheets no longer differ on thickness either.

STILL OPEN — the wall is 18 ft 11 in on the bedroom side and the dressing room only covers

9 ft 3 in of it. That leaves 9 ft 8 in at the study-wall end backing on to something that has

never been drawn. Worth knowing what is behind it before anything is fixed to that wall.

KNOCK-ON — moving the door 2 in along the wall shifts the right wall's panel setting out, so the

five bays and the narrow panel past the door are all slightly different from the last issue of

AST-DR-007. That sheet has been re-cut to suit and should be reread before anything is made.

A STUDY IN TEAK

Particulars of the room

THE SHARED WALL

Bedroom / dressing room · reconciled

SCALE

1:45 @ A3

DATE

25.09.2026

REV


2 — set out from the measured 2 ft 4 in, corner to the door frame, both sides

DWG

AST-DR-024

DRESSING ROOM — THE WARDROBES

DEVELOPED ELEVATION · 1:40 · THE THREE WALLS UNFOLDED, LEFT TO RIGHT AS YOU WALK IN

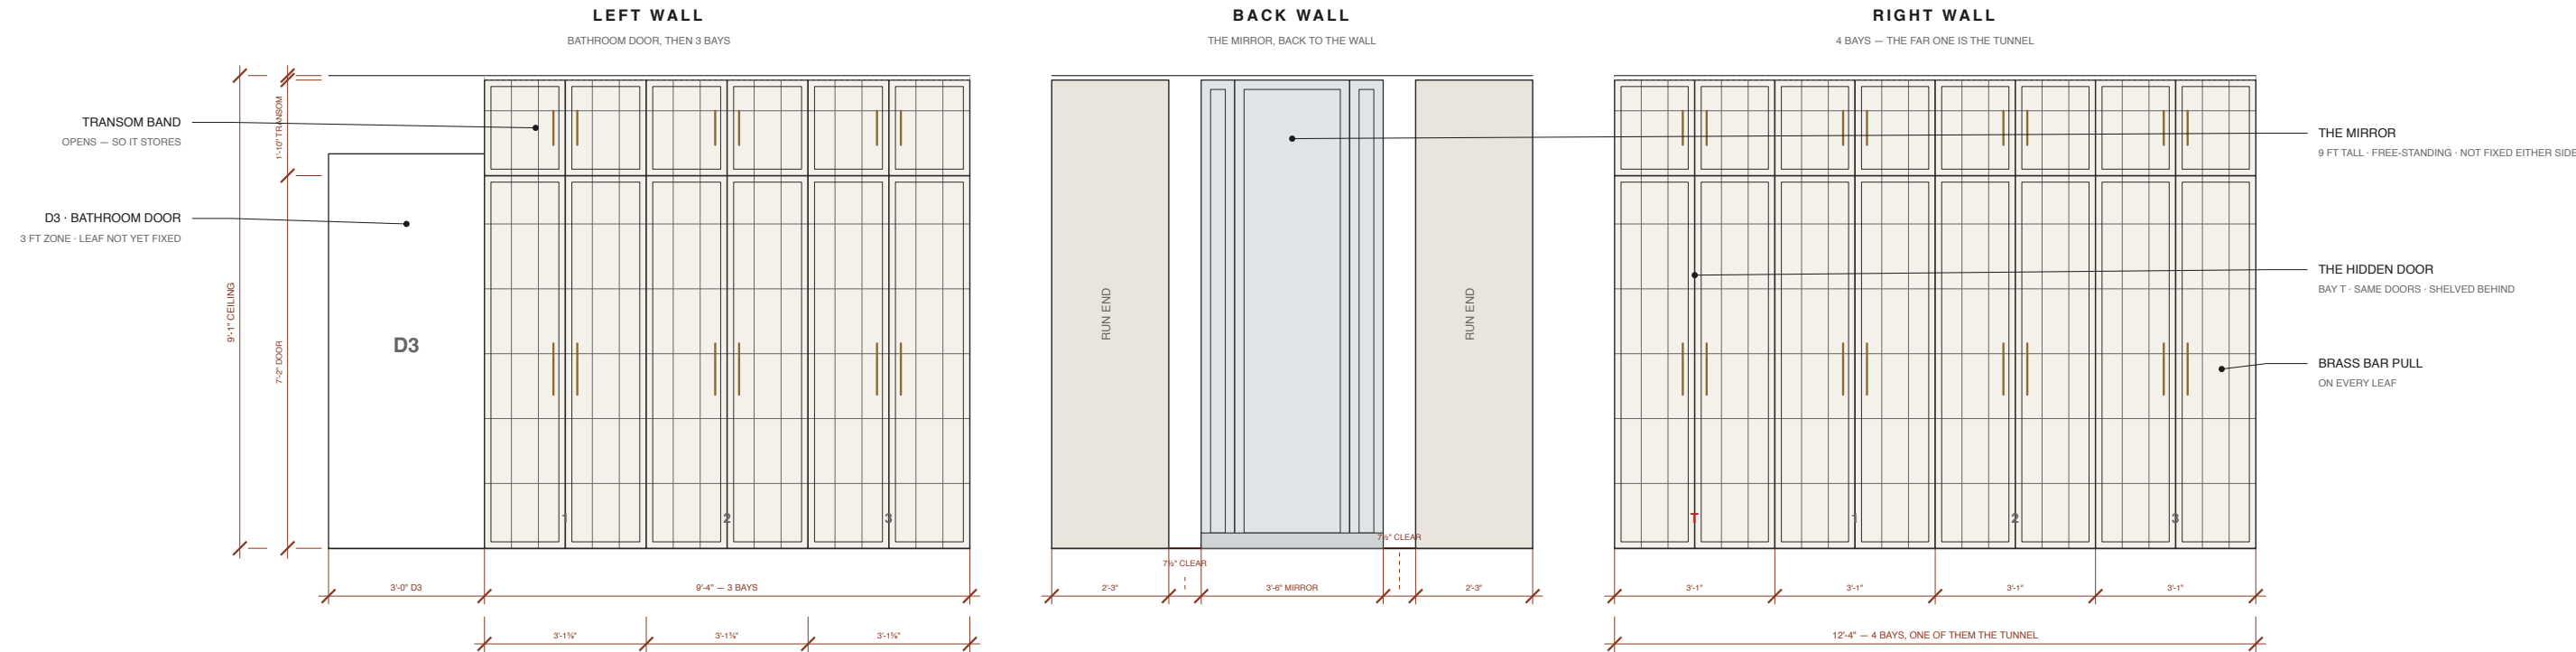

NOTES

REVISION 1

Depth 2 ft 3 in, as instructed. On the right that is what lets the run reach the bedroom wall: the door frame stands 2 ft 4 in off that corner, so the end of the run clears it by 1 in.

Bays are the wall divided equally, so nothing is left over and there are no filler strips: the right wall is 12 ft 4 in over 4 bays, the left is 9 ft 4 in over 3. Both come out at about 3 ft 1 in — an inch over the 3 ft you asked for, which is what makes them land exactly.

Each bay is a pair of doors with a pair of transom lights over, all glazed and all opening — so the transom is storage, not just a band of glass. 7 bays, 14 cupboards, 28 leaves.

Doors as the Wardrobes brief: blackened steel T-section, 38 face, white textured glass in linear lead came, lit from inside, brass bar pulls, transom bar 560 down from the top.

SETTLED — the mirror is a trifold, 3 ft 6 in across with its wings at 45°, free-standing and fixed to neither run. Centred in the 4 ft 9 in gap it leaves 7½ in of floor either side, and it is 9 ft tall — level with the top of the wardrobes. That narrow gap is why the two end bays cannot hinge open in the ordinary way — see AST-DR-026 for the fold-slide doors that solve it.

OPEN — D3, the bathroom door. 3 ft of wall is left for it, but the leaf is still not fixed. It is drawn as an opening only.

OPEN — the tunnel bay reads as one more cupboard, but it is a door onto a passage, so the transom over it cannot be storage in the ordinary way. Decide whether it is a dummy.

OPEN — 4 ft 9 in is what you are left standing in once both runs are built. Open one 1 ft 6 in leaf and there is still 3 ft 3 in. Workable, not generous — worth feeling on site first.

A STUDY IN TEAK

Particulars of the room

THE WARDROBES

Dressing room · developed elevation

SCALE

1:40 @ A3

DATE

25.09.2026

REV

1 — first setting out of the bays, off the owner's 2 ft 3 in depth and 3 ft bay

DWG

AST-DR-025