



FRONT ELEVATION — D1

7 ft 7 in x 3 ft · PAIR OF LEAVES · SCALE 1:12

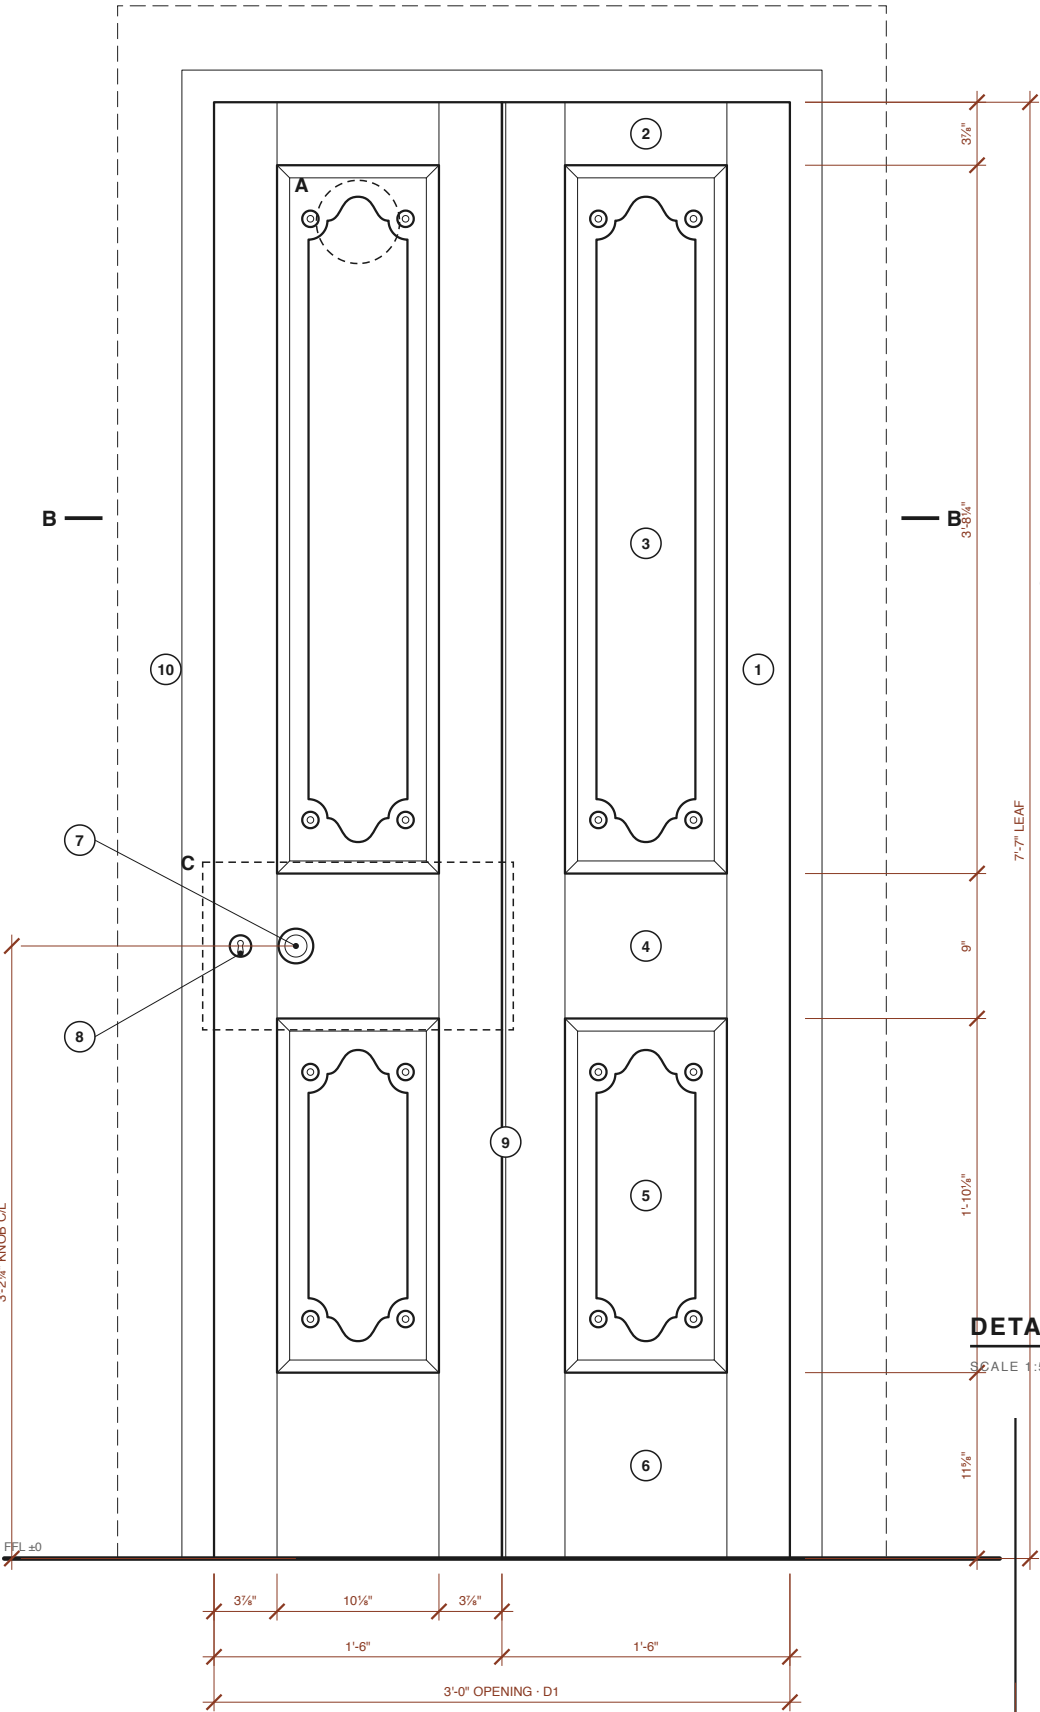


DETAIL A — PANEL HEAD

SCALE 1:2.5 · FOOT OF PANEL IS THE MIRROR

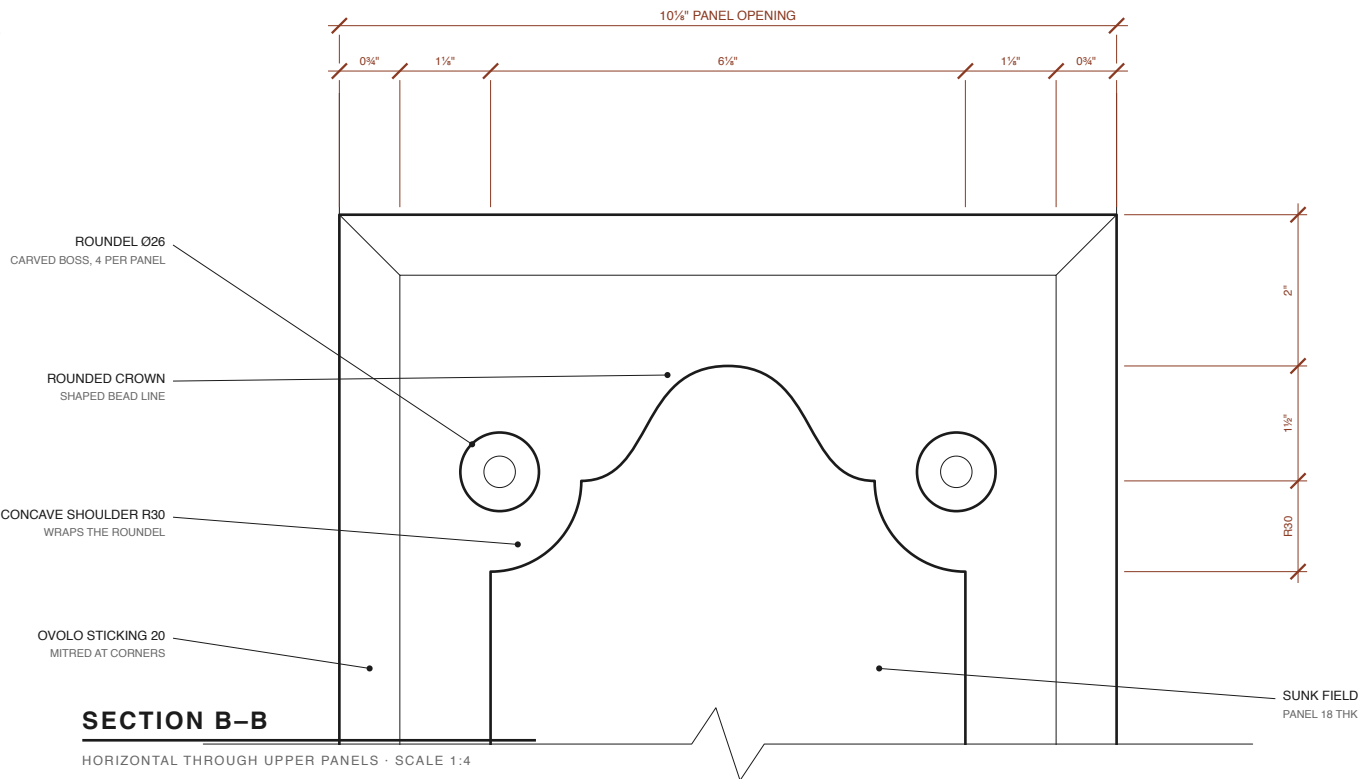


SECTION B-B

HORIZONTAL THROUGH UPPER PANELS · SCALE 1:4

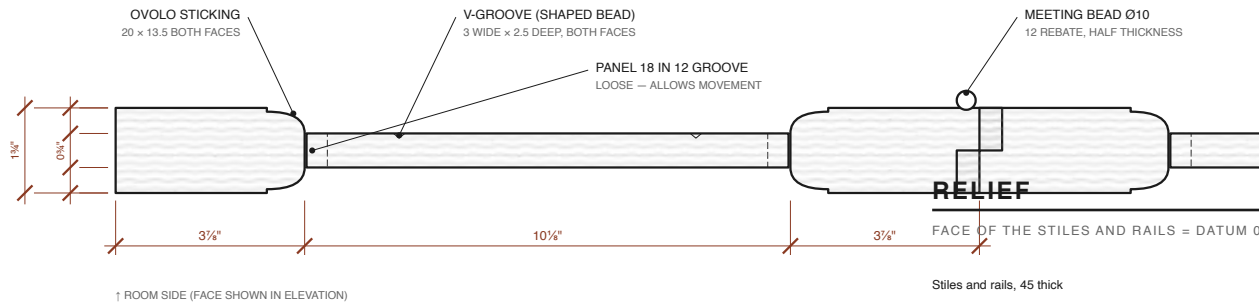

DETAIL C — LOCK RAIL

SCALE 1:5 · ACTIVE LEAF

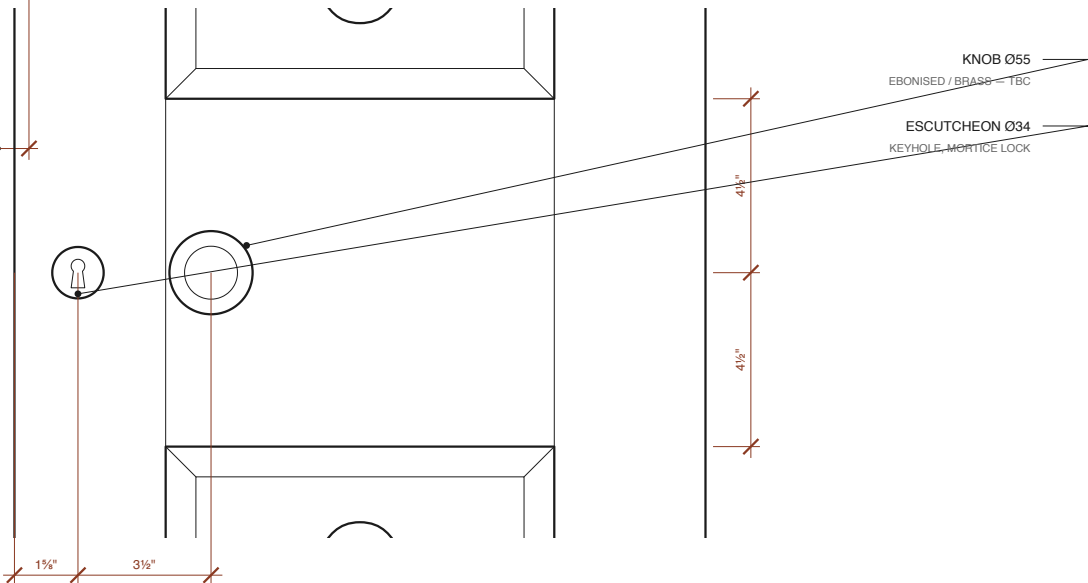

KEY

PARTS OF THE LEAF

- 1 Stile
- 2 Top rail
- 3 Upper panel — shaped bead, 4 roundels
- 4 Lock rail
- 5 Lower panel — same pattern
- 6 Bottom rail
- 7 Knob Ø55
- 8 Keyhole escutcheon
- 9 Meeting bead (pair only)
- 10 Architrave — to design

NOTES

READ BEFORE MAKING

Dimensions in feet and inches. Do not scale.

Proportions taken from a film-still reference;

leaf size, opening and thickness are ASSUMED.

Knob centre lands 958 above the floor — normal height.

D1 — MAIN DOOR, 7 ft 7 in x 3 ft.

Set out on the panel square. The 2 ft 6 leaf gives a

562 panel; the upper panel is two of those squares

(1124), the lower is one (562). Rails follow: top 100,

lock 230, bottom 295. Knob centre 972 above the floor.

Both widths take the identical rails and mouldings, so

only the panel width changes — here 257 per panel.

Solid teak frame. Veneer and polish per

Materials; polish to match the teak desk.

Casing: 2 in lining plus 4 in moulding over it, so the

moulding head sits 163 (6 in) above the leaf.

See AST-DR-011 (option A) and AST-DR-012 (option B).

Hinges and lock not yet designed.

A STUDY IN TEAK

Particulars of the room

DOOR D1 — 7 FT 7 IN x 3 FT

Elevation · Panel head · Section · Lock rail

SCALE

AS NOTED @ A3

REV

6 — set out on the panel square: upper two squares, lower one

DATE

17.09.2026

DWG

AST-DR-001