


D2 · D3


DRESSING AND BATHROOM · 2 FT 6 · AS AST-DR-009

D1

MAIN DOOR · 3 FT · AS AST-DR-001

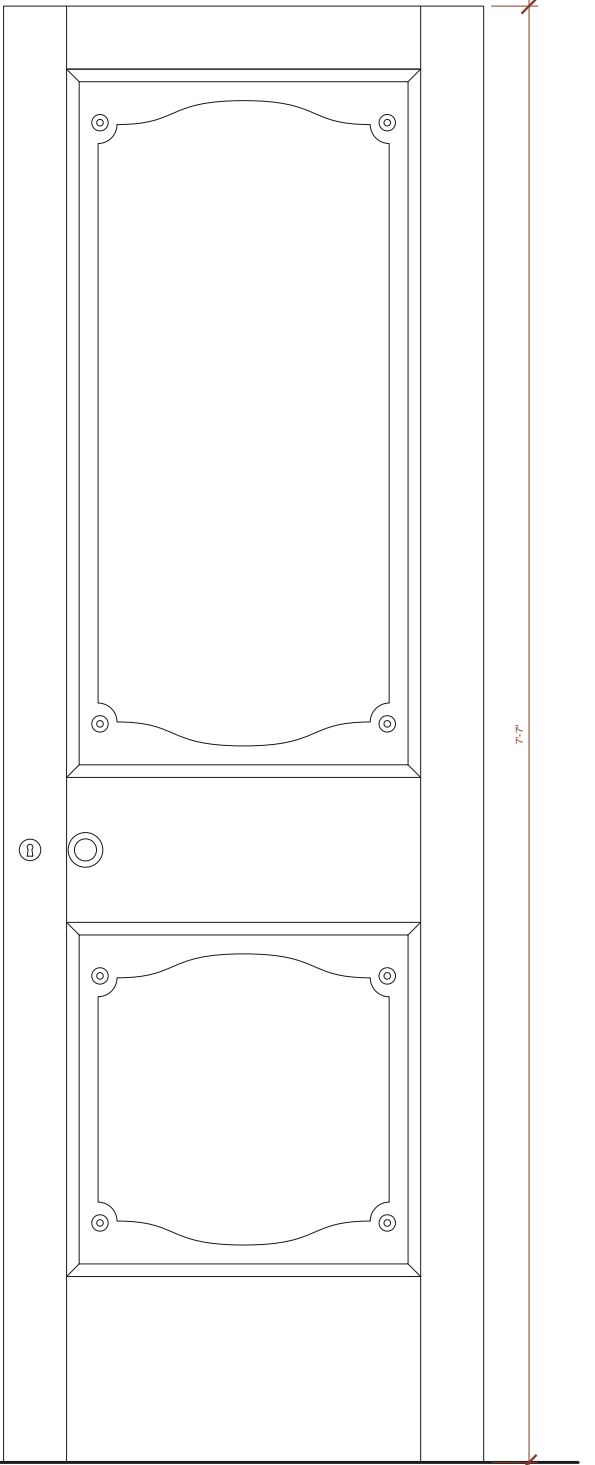


Both elevations are generated from the door sheets' own code, so the design cannot drift. Nothing on this sheet changes how the door LOOKS — only how it is made.

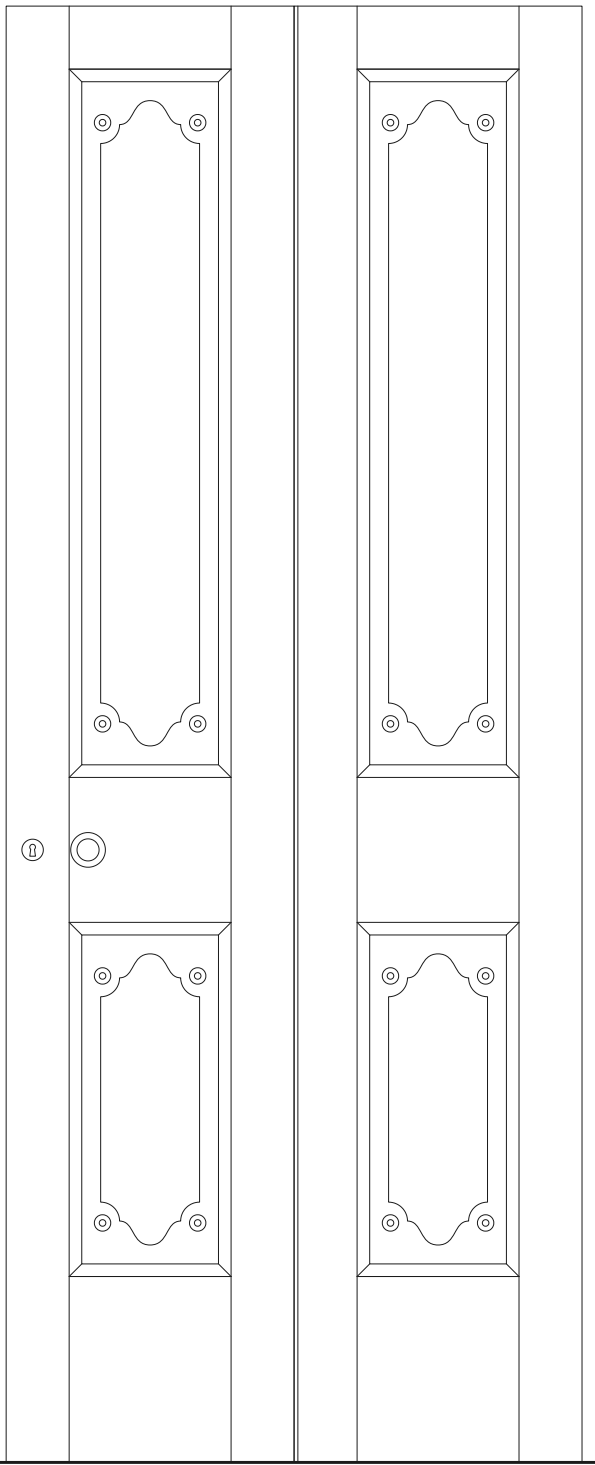

1 · THROUGH THE LEAF

SECTION ACROSS A PANEL · 1:2 · EVERY MEMBER PLANTED ON

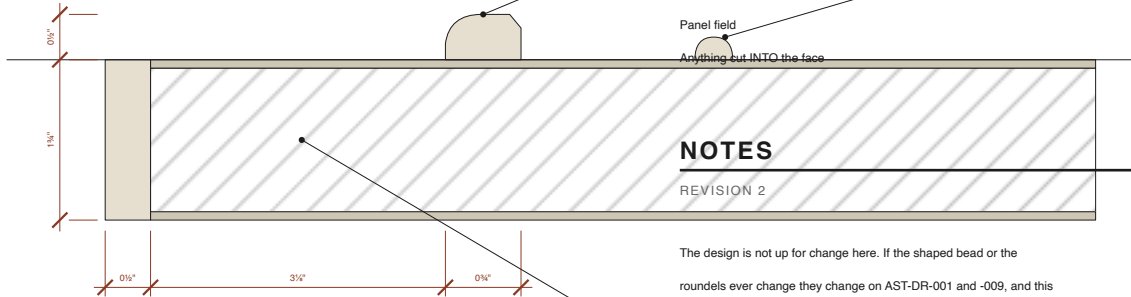

2 · WHAT CHANGES

THE SAME MEMBERS, MADE SEPARATELY AND GLUED ON

Panel field

was: sunk 13.5 into the solid
now: stays FLAT — the ovolo round it does the work
Ovolo sticking

was: worked on the stile edge
now: run as a separate 20 x 12 moulding, mitred on
Shaped bead

was: carved into the panel face
now: bandsawn to the curve in 10 x 6, planted on
Corner roundels

was: carved bosses
now: turned discs Ø26 x 5, glued on
The leaf

was: solid teak, 45
now: 38 blockboard, 12 lipping, veneer both sides

RELIEF

FACE OF THE VENEER = DATUM 0

Blockboard core	38
Veneer, each face	0.6
Solid lipping, four edges	12 WIDE
Leaf overall	45
Ovolo, planted	20 W · 12 OUT
Shaped bead, planted	10 W · 6 OUT
Roundel boss, glued on	Ø26 · 5 OUT
Panel field	FLAT · 0
Anything cut INTO the face	NONE

NOTES

REVISION 2

The design is not up for change here. If the shaped bead or the roundels ever change they change on AST-DR-001 and -009, and this sheet follows — it draws from the same code.

BLOCKBOARD CORE
Lipping is solid teak on all four edges so the leaf can be trimmed on site and the hinges and lock screw into wood, not into board.

Veneer both faces of the core and balance it: same thickness back and front, or the leaf will bow.

Ovolo, bead and bosses in solid teak, polished to match. They are small enough to take solid without moving, and they give a crisper arris than a cut face would.

Set the bead out from the panel opening, not from the leaf edge, so the four roundels land exactly on the corners of the curve.

OPEN — glue and pin, or glue only? Pins need filling and the filler shows through polish. Glue and cramp if the shop can.

A STUDY IN TEAK

Particulars of the room

DOORS — MADE IN VENEER

Same design · Planted mouldings · Construction only

SCALE

AS NOTED @ A3

DATE

23.09.2026

REV

2 — the design unchanged; only the construction differs

DWG

AST-DR-015