


DRESSING ROOM — SHELL AND LAYOUT

PLAN · SCALE 1:35 · COPIED FROM THE OWNER'S SKETCH — NOT YET A SITE MEASUREMENT

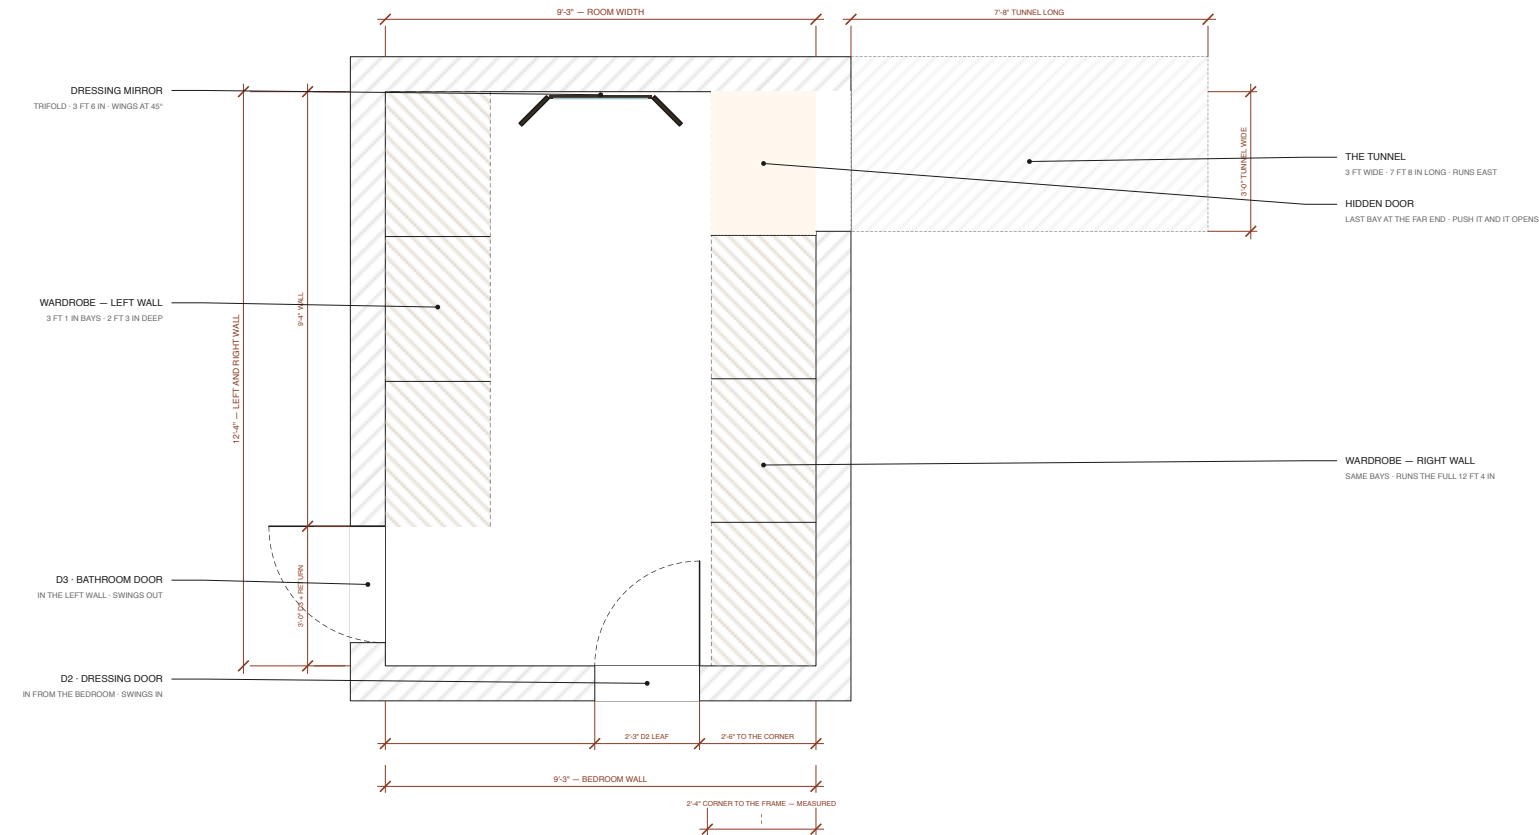

NOTES

REVISION 3

Third pass, and this one copies the sketch rather than interpreting it. The two earlier drawings both had the shape wrong; everything below is read straight off the owner's own clean drawing. The BEDROOM wall is the bottom wall here, 9 ft 3 in, and it carries D2, the existing dressing door in from the bedroom, 2 ft 4 in from the right-hand corner to the door FRAME — measured on both sides of the wall, and the figure that now governs. The sketch's 2 ft 0 in is superseded. The BATHROOM door, D3, is in the LEFT wall, at the bedroom end — not in the bedroom wall. The sketch runs 9 ft 4 in of wall down from the far corner and then opens the door. The TUNNEL runs EAST, straight out of the far end of the right wall, 3 ft wide and 7 ft 8 in long, its far side flush with the far wall. The hidden door is the last wardrobe bay in front of it: built and shelved like every other bay, so from the room it reads as one more cupboard. Ceiling 9 ft 1 in, plain, over the left and right sides — the same height as the main room. A domed centre rises to 10 ft 0 in, so the wardrobes are capped at 9 ft 0 in, clear under it.

SETTLED — D2 sits 2 ft 4 in from the corner to its frame, on both sides of the wall. That closes this sheet against AST-DR-000 and AST-DR-007: this room's right-hand corner and the bedroom's bed-wall corner are the same corner. Walls are taken at 9 in throughout. See AST-DR-024. OPEN — D3's width: It is drawn 2 ft 6 in, as the owner said, but the sketch's own 9 ft 4 in against 12 ft 4 in leaves 3 ft 0 in — so a 6 in return is shown into the corner. To confirm. SETTLED — the wardrobes are 2 ft 3 in deep, so the right-hand run reaches the bedroom wall and clears D2's frame, 2 ft 4 in off that corner, by 1 in. OPEN — the left run is drawn stopping at D3. Whether it ends there or returns over the door is not decided. OPEN — where the tunnel leads, and what is at its far end. OPEN — the dome's own shape: how far along the room it runs, and its profile. The mirror is the confirmed trifold, 3 ft 6 in across with its wings at 45° — see AST-DR-027.

A STUDY IN TEAK

Particulars of the room

DRESSING ROOM

Shell and layout · third pass

SCALE
1:35 @ A3

DATE
25.09.2026

REV

DWG

AST-DR-023