



PLAN

AN ALL-GLASS WALL · BOTH ENDS TURN 55° TOWARDS THE BED · 1:20

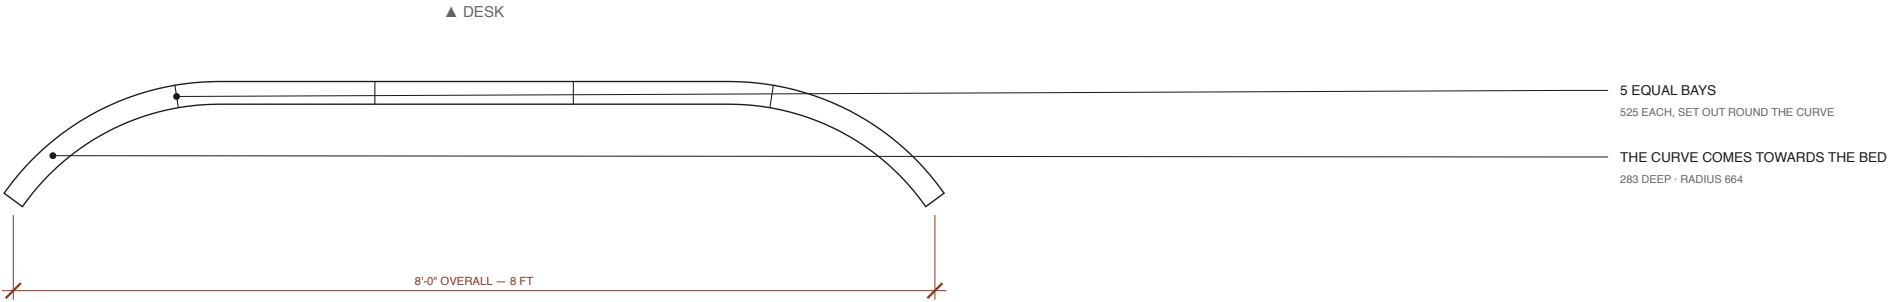

ELEVATION

THE CURVE UNROLLED FLAT · BOTH FACES THE SAME · 1:22

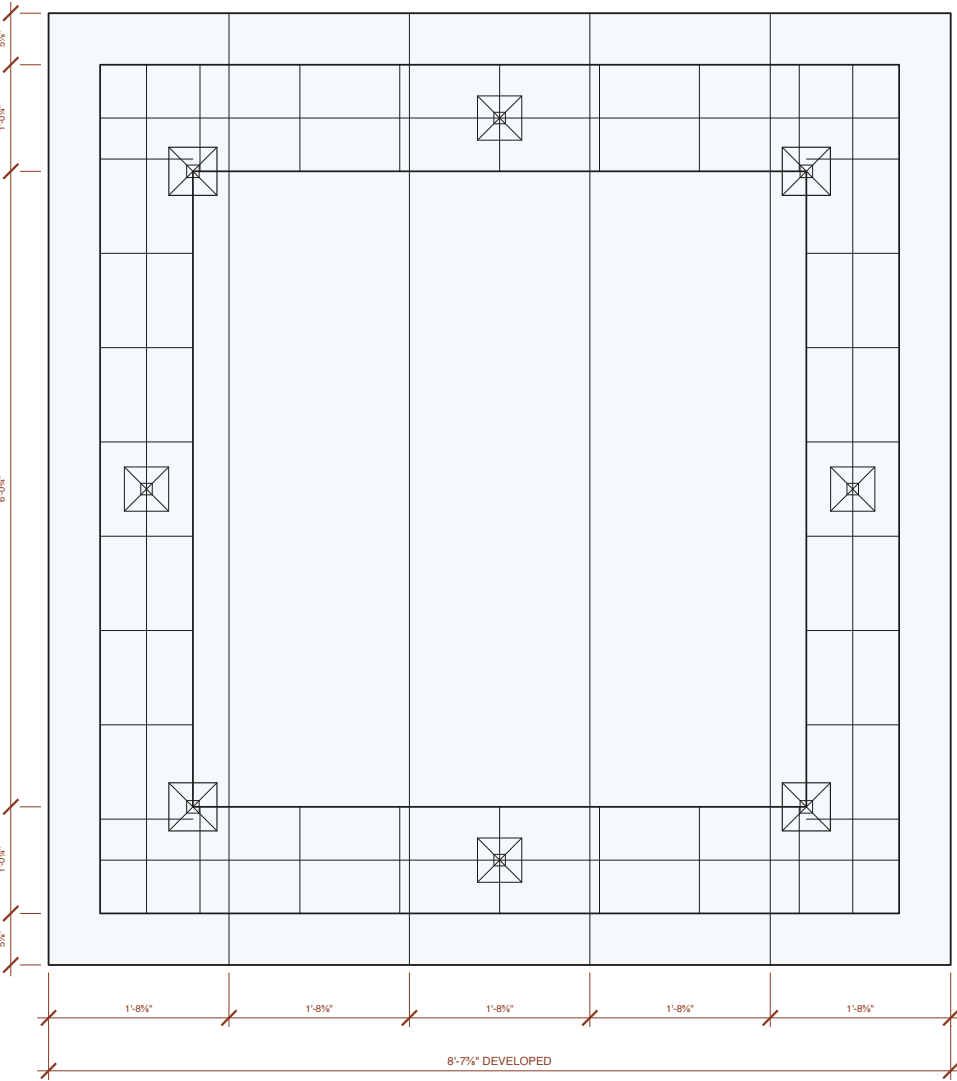

ALL GLASS. One composition across the whole wall — the border runs straight through the bay joints.

Border: an outer rectangle 150 in from every edge and an inner one 420 in at the sides, 460 at head and foot,


joined by a short bar at the middle of each side, with a cross at each corner of the inner rectangle.

All the leading is in the ring between them. The field inside the inner rectangle is one clear sheet.

White textured glass in lead came. No colour. The television is shown for position only — how it is carried is not drawn.


WITH THE TELEVISION

THE SAME WALL · THE SET CENTRED · 1:22

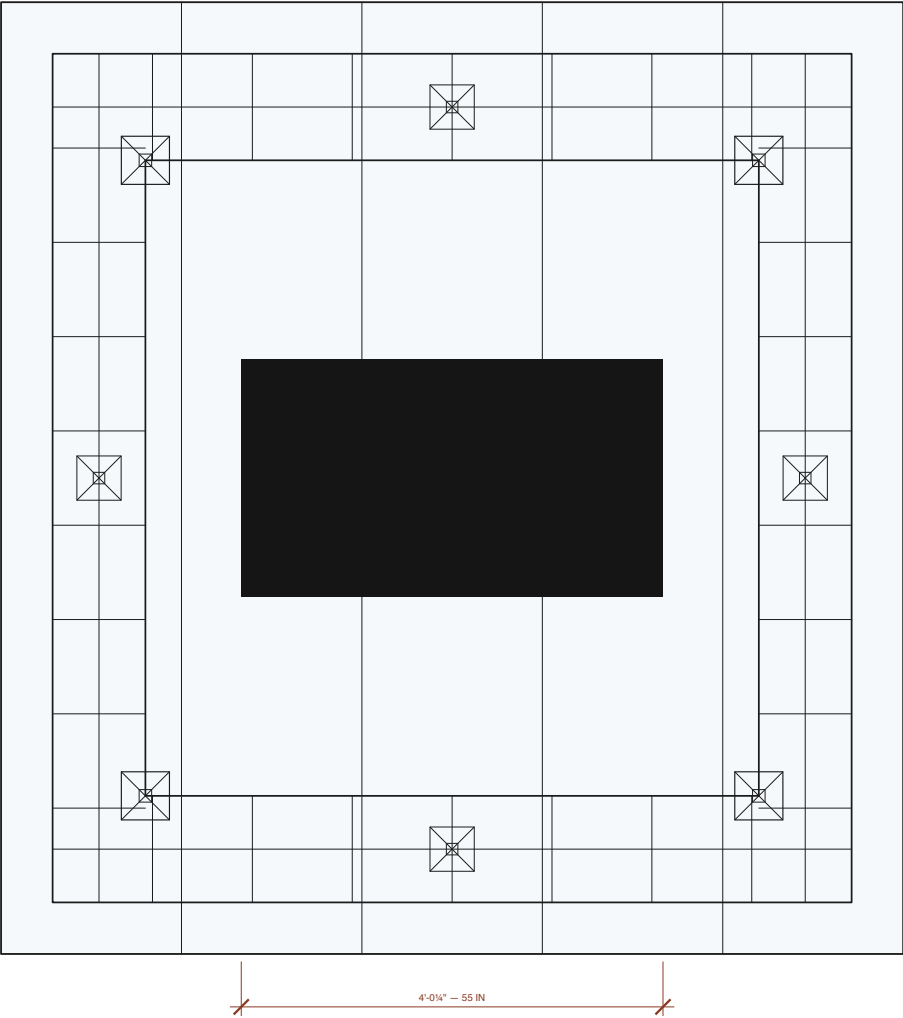

THE CURVE


PLAN · 1:10

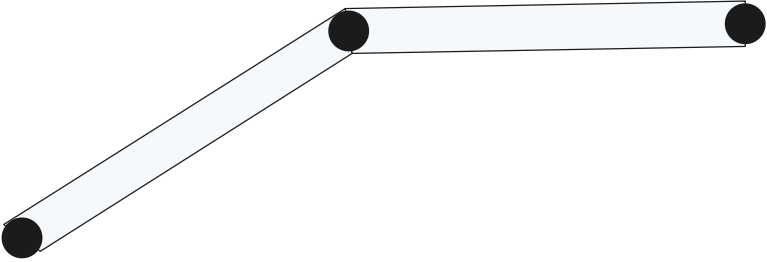

Every bay is flat. The came at each joint takes the angle — no glass is bent.

AXONOMETRIC

FROM THE BED SIDE

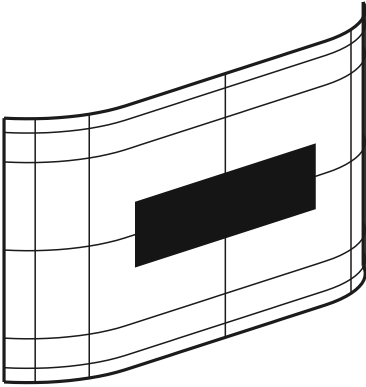

A STUDY IN TEAK

Particulars of the room

PARTITION — LEADED GLASS

Plan · Elevation · With the television · Curve · Axonometric

SCALE
AS NOTED @ A3

DATE
18.09.2026

REV
2 — the border only; the field inside stays clear

DWG
AST-DR-010