



ELEVATION — RIGHT WALL

SCALE 1:25 · SEEN FROM THE ROOM · STUDY WALL ON THE LEFT · OPTION C

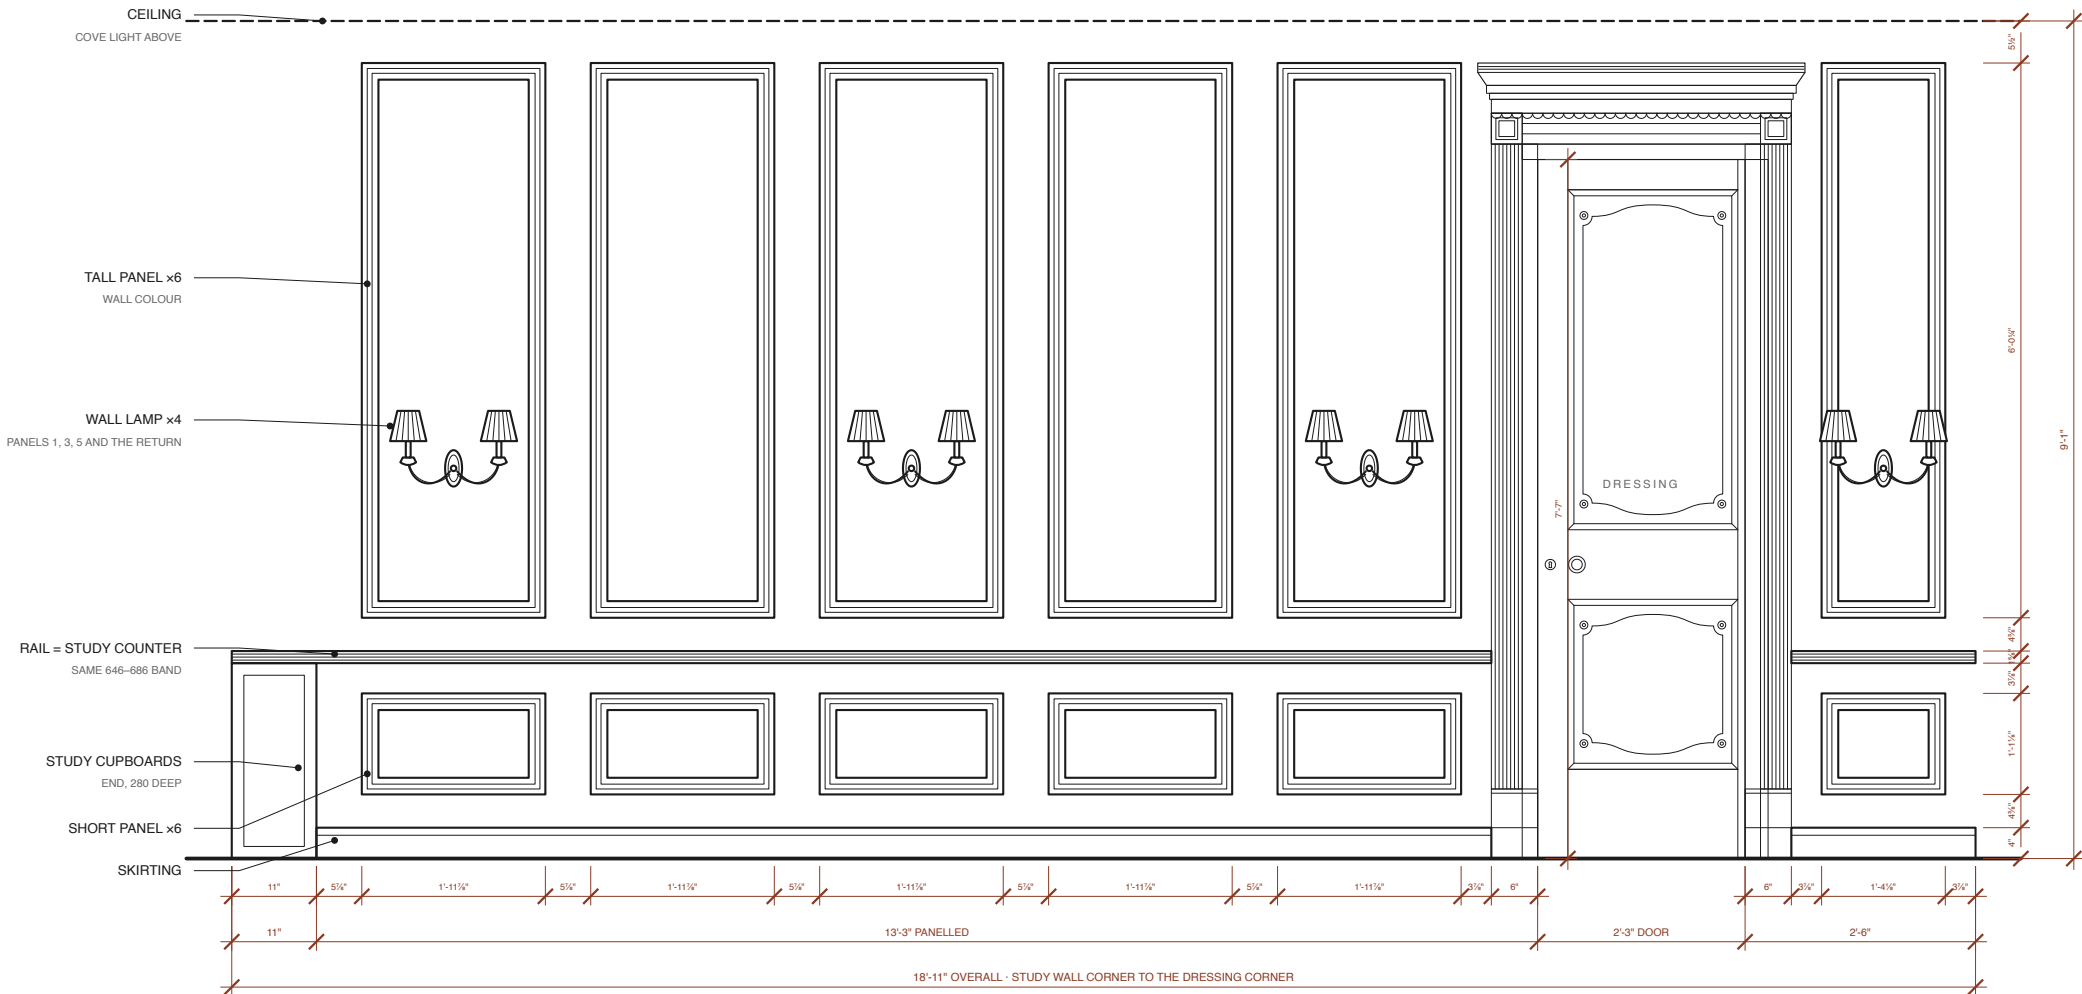


PLAN

CUT AT 1000 · SCALE 1:25 · ROOM BELOW, WALL ABOVE

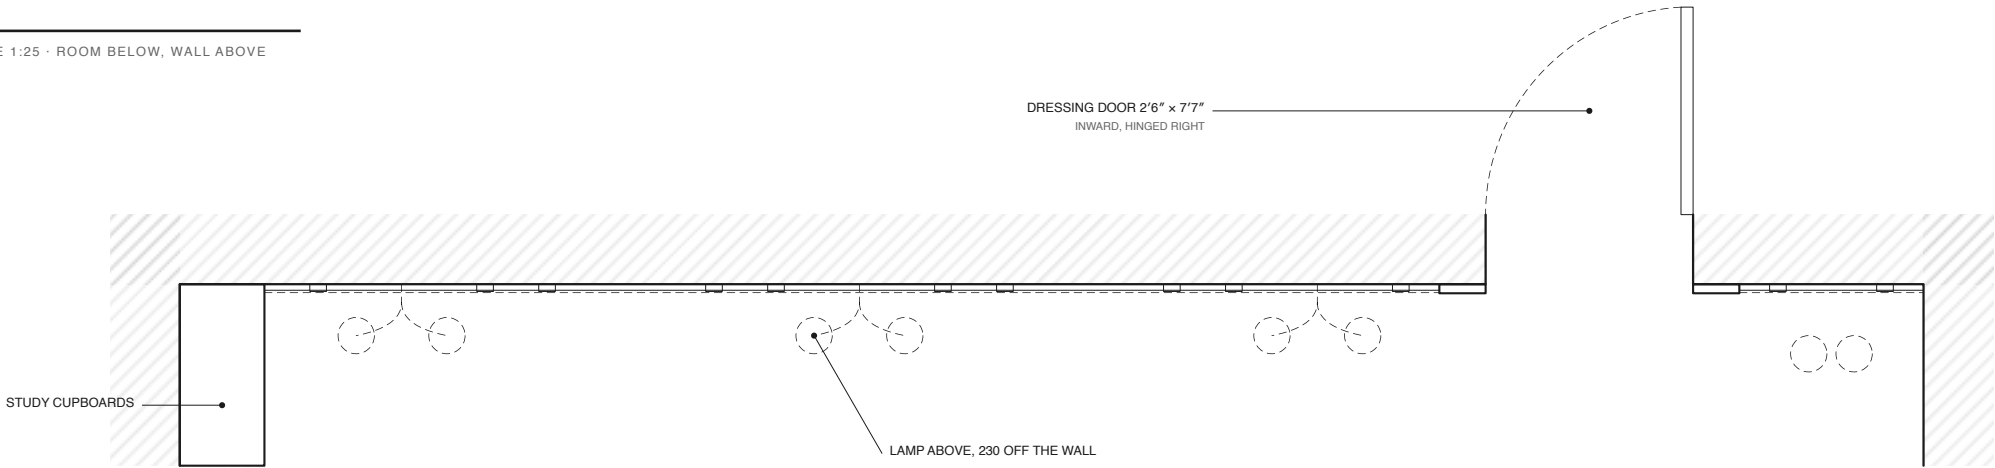


1 · PANEL MOULDING

SECTION · 1:1

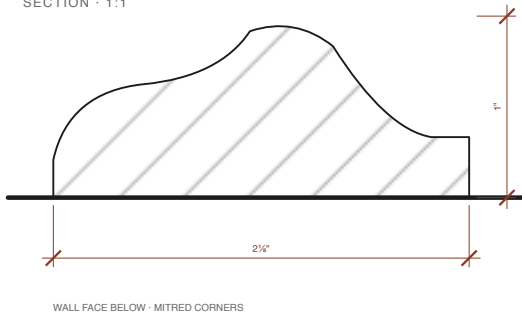


2 · RAIL

SECTION · 1:2

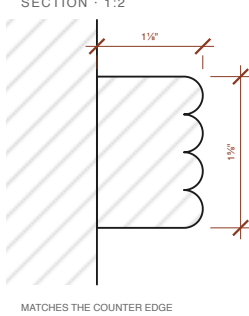


3 · SKIRTING

MARBLE · SECTION · 1:4

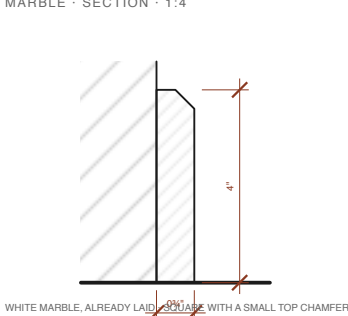


4 · WALL LAMP

ELEVATION · 1:10 · x4

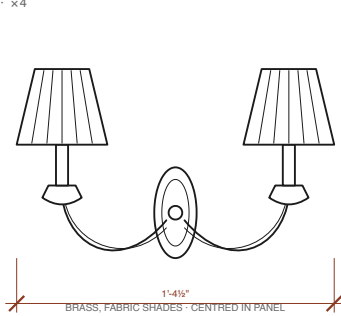

SECTION A-A

THROUGH PANEL 1 · 1:20

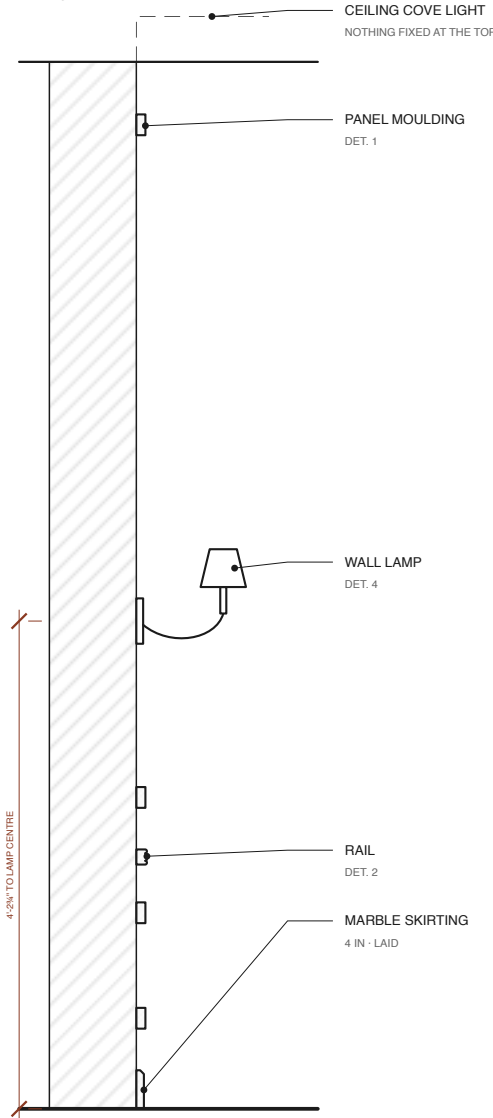

NOTES

REVISION 18

- Option C: 5 equal panels, lamps in 1, 3, 5 and the return.
- One narrow panel on the wall past the door.
- Moulding, rail and skirting painted the wall colour.
- SELECTED after four schemes: the rail is the study counter band carried round the corner, and it dies into the casing.
- Skirting is white marble, 4 in, already laid.
- Casing 2 in lining + 4 in moulding = 6 in, 1068 overall; crown at 8 ft 8 in, and the tall panels stop on that line, not the leaf head at 7 ft 7 in.
- 2 ft 4 in corner to frame, measured both sides; leaf 2 ft 3 in a 2 in frame. OPEN: that puts the frame 14 ft 0 from the study corner, 6 in off the taped 13 ft 6. Retape that end.

A STUDY IN TEAK

Particulars of the room

RIGHT WALL — PANEL MOULDING

Elevation · Plan · Section · Details

SCALE
AS NOTED @ A3

DATE
20.09.2026

REV
18 — SELECTED: the rail at 2 ft 3 in, carrying the study counter round

DWG
AST-DR-007