


THE SHARED WALL — RECONCILED

AST-DR-000 AND AST-DR-023 SET OUT FROM ONE MEASUREMENT — 2 FT 4 IN, CORNER TO THE DOOR FRAME

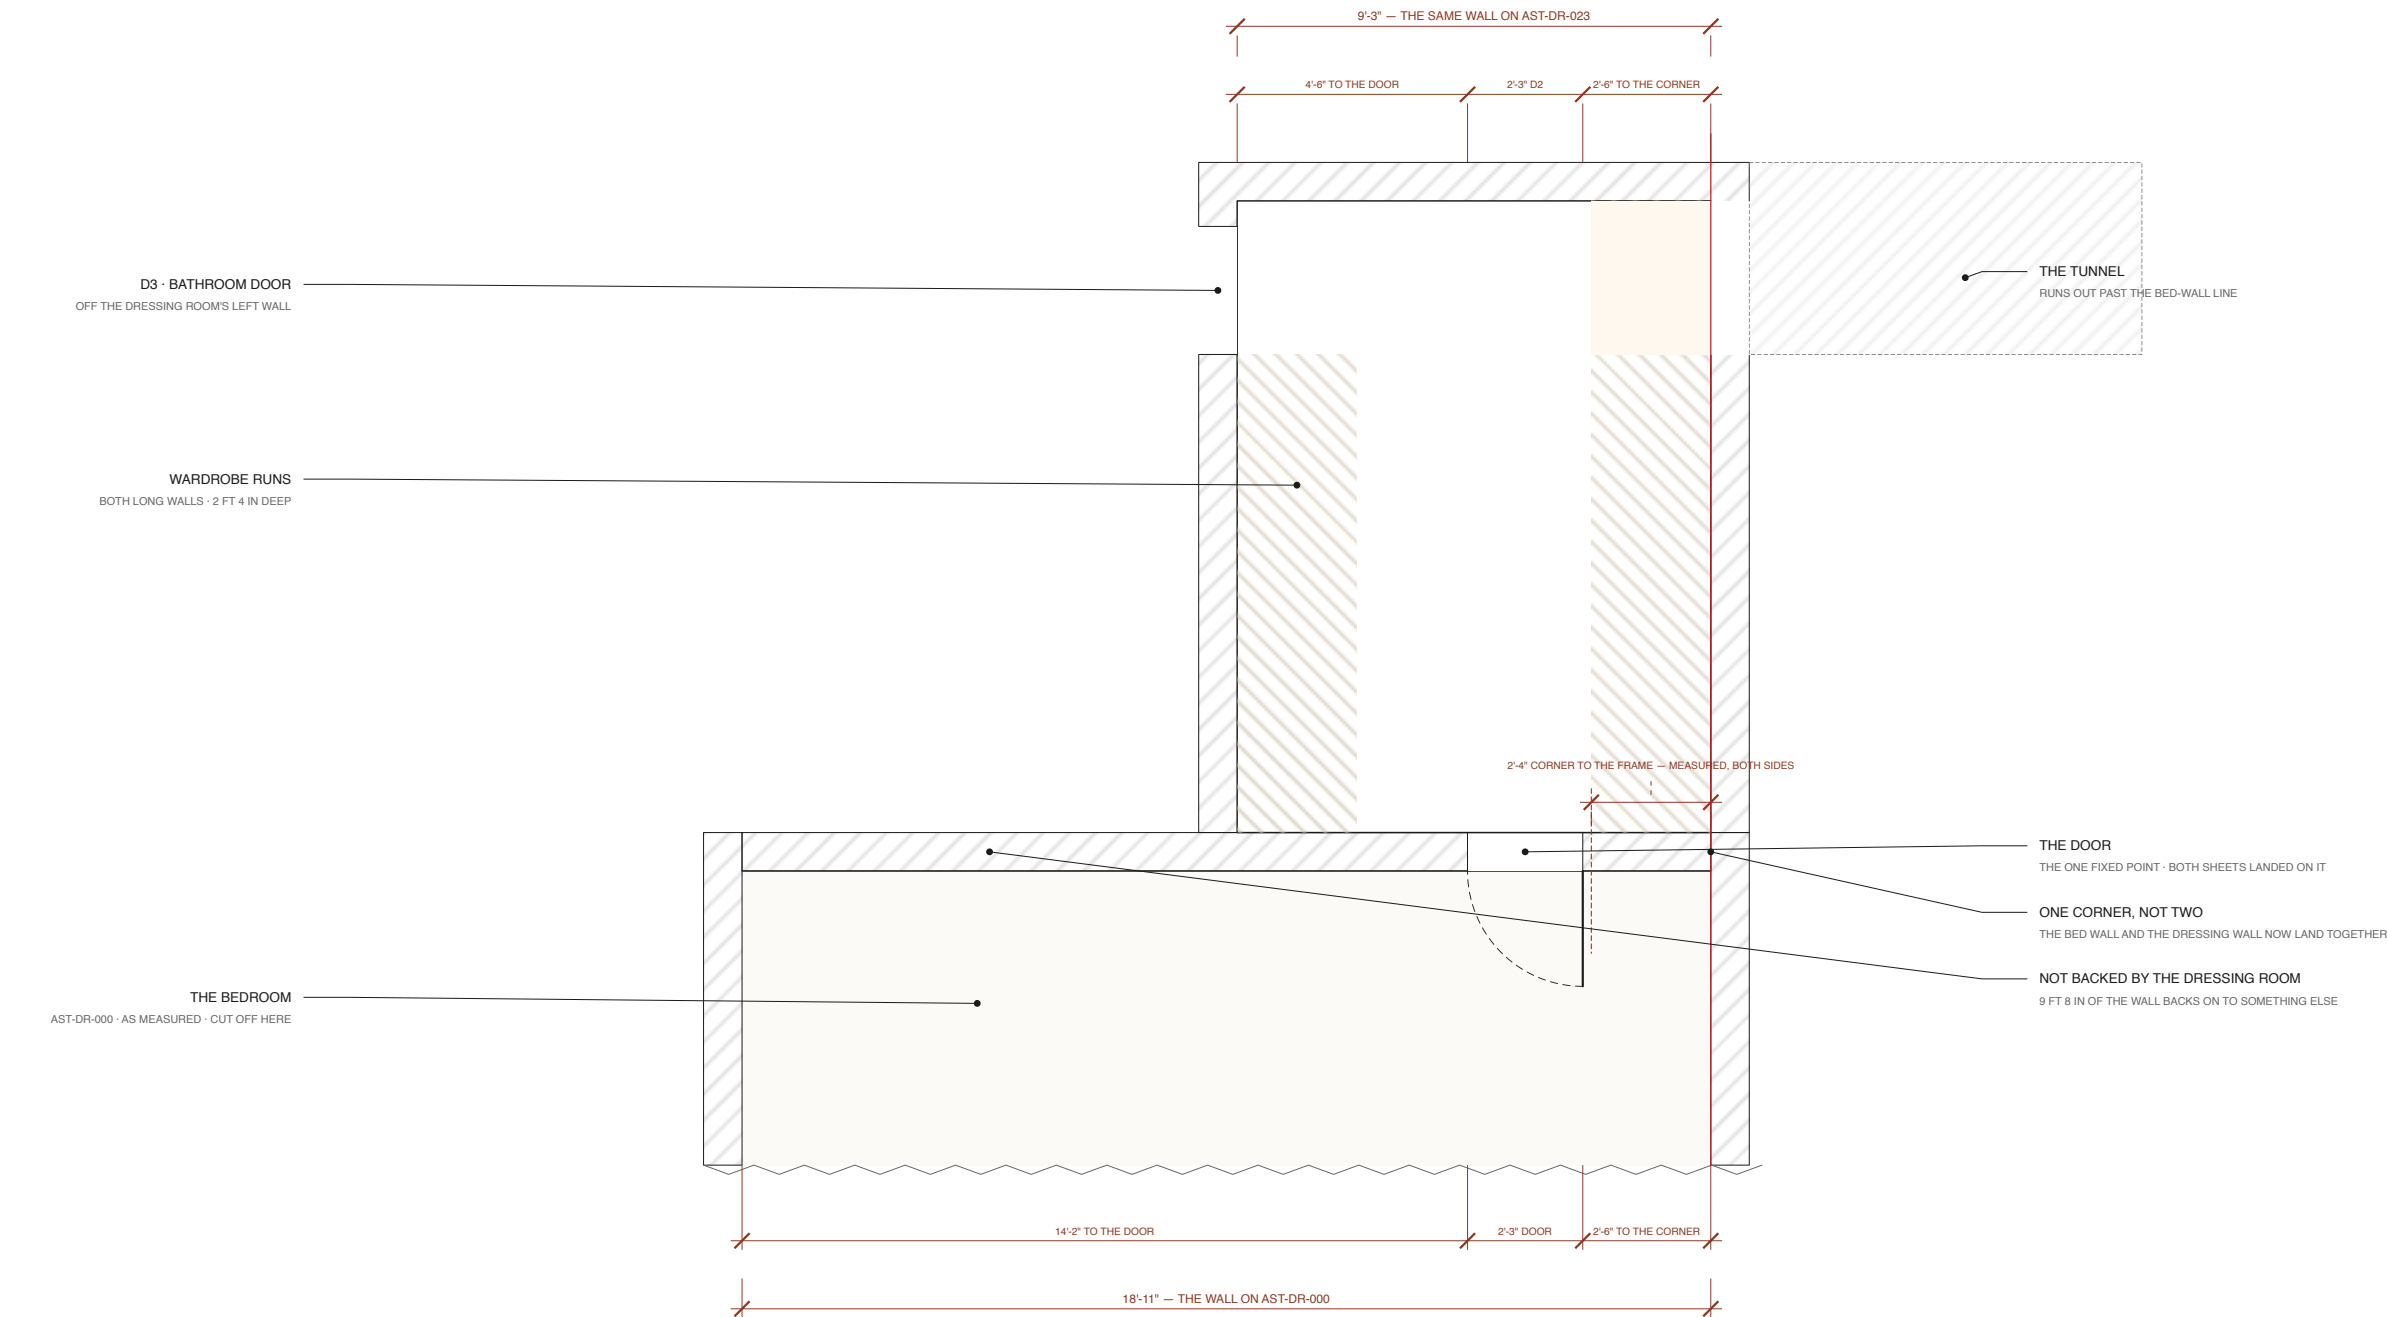

HOW IT WAS SETTLED

ONE MEASUREMENT, TAKEN ON BOTH SIDES, NOW GOVERNS BOTH SHEETS

THE CONTROL — 2 ft 4 in from the dressing corner to the door FRAME, taped on both sides of the wall. Everything on this wall is now set out from that and nothing else. It replaced two figures that disagreed: 2 ft 9 in on AST-DR-000, which had been back-calculated rather than measured, and 2 ft 0 in on the dressing sketch, which was a reading off a hand drawing.

WHAT IT FIXED — with a 3 in lining the chain now closes: frame 13 ft 7 in from the study corner (the tape said 13 ft 6 in), the 3 ft frame, then 2 ft 4 in to the corner, on the measured 18 ft 11 in overall. Both corners now fall on the same line, so the dressing room's right-hand wall and the bedroom's bed wall are one wall, not two a hand's width apart.

WALLS — taken at 9 in throughout, as instructed. AST-DR-000 already carried 230 mm, which is the same 9 in, so the two sheets no longer differ on thickness either.

STILL OPEN — the wall is 18 ft 11 in on the bedroom side and the dressing room only covers 9 ft 3 in of it. That leaves 9 ft 8 in at the study-wall end backing on to something that has never been drawn. Worth knowing what is behind it before anything is fixed to that wall.

KNOCK-ON — moving the door 2 in along the wall shifts the right wall's panel setting out, so the five bays and the narrow panel past the door are all slightly different from the last issue of AST-DR-007. That sheet has been re-cut to suit and should be reread before anything is made.

A STUDY IN TEAK Particulars of the room	
THE SHARED WALL Bedroom / dressing room · reconciled	
SCALE 1:45 @ A3	DATE 25.09.2026
REV 2 — set out from the measured 2 ft 4 in, corner to the door frame, both sides	DWG AST-DR-024