



ELEVATION — STUDY WALL

SCALE 1:25 · BOOKCASE · PANEL FOR PAINTING · WINDOW

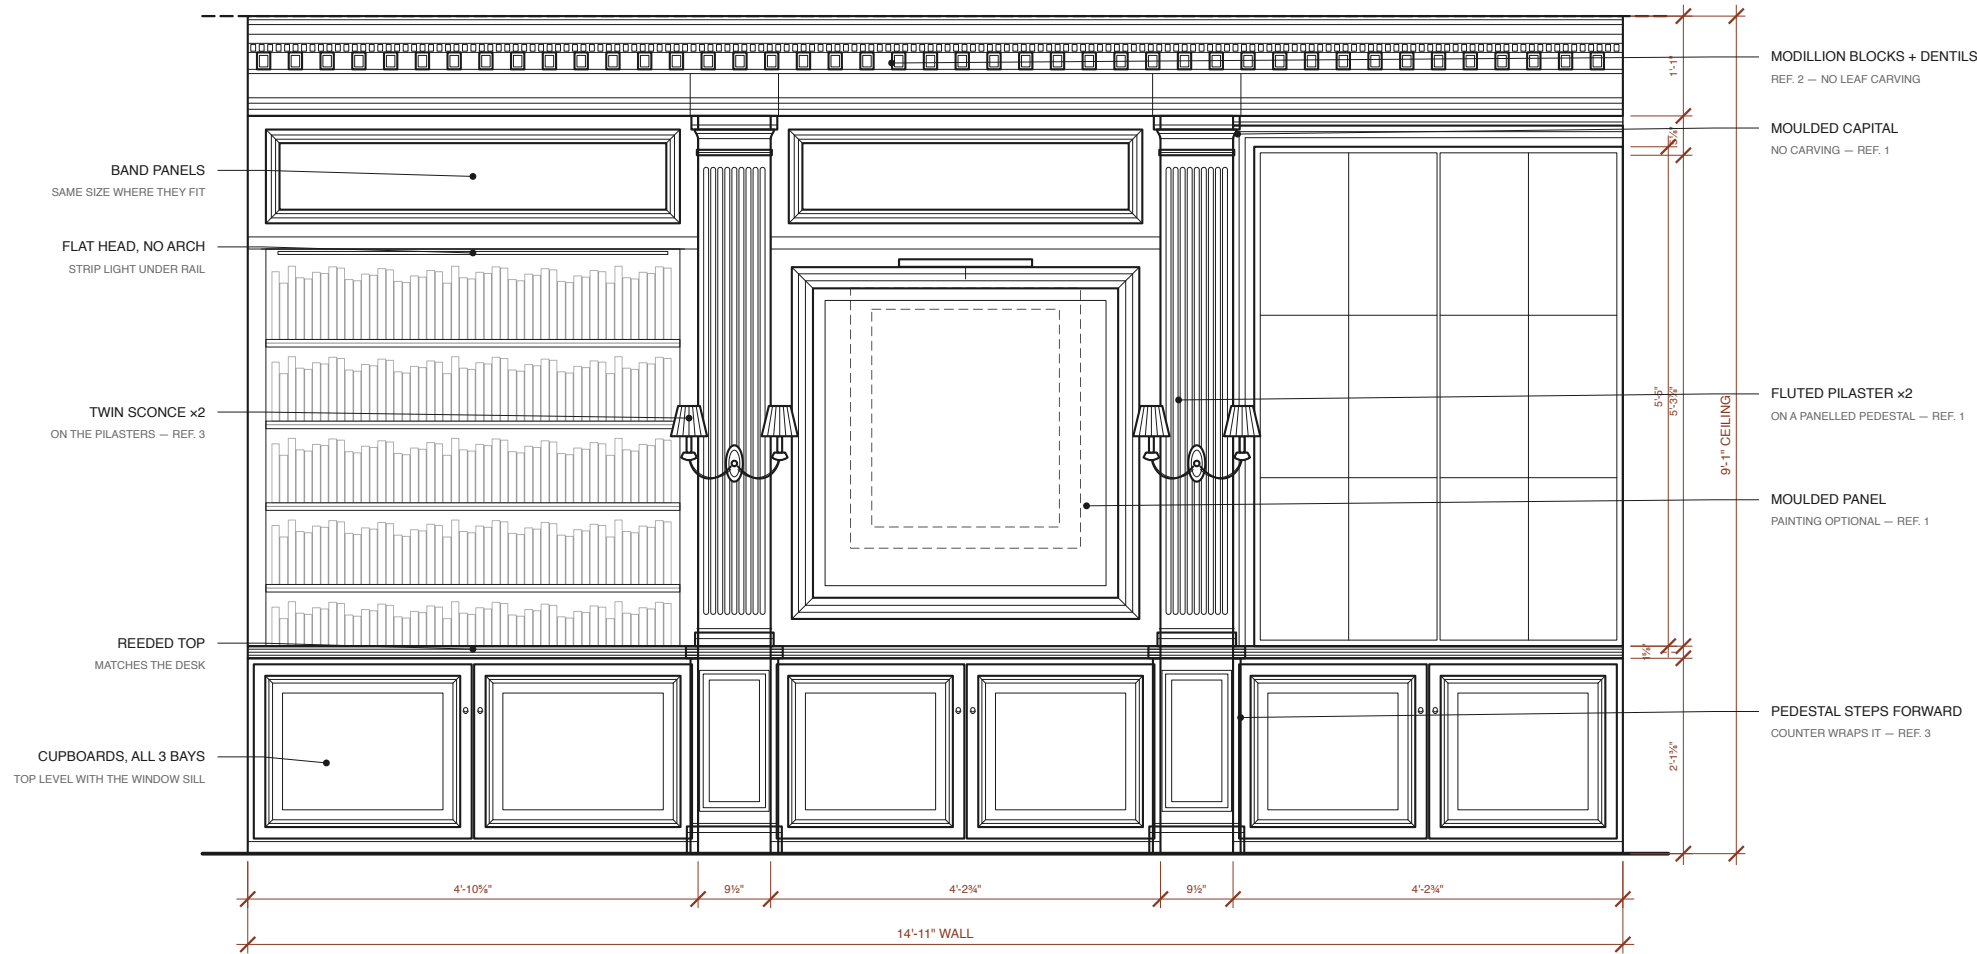


PLAN

CUT AT 1200 · SCALE 1:25 · ROOM BELOW, WALL ABOVE

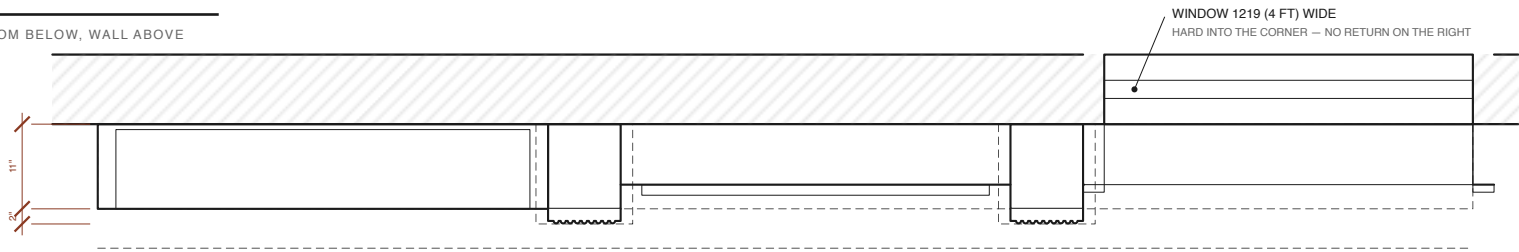

SECTION A-A

THROUGH BOOKCASE · 1:25

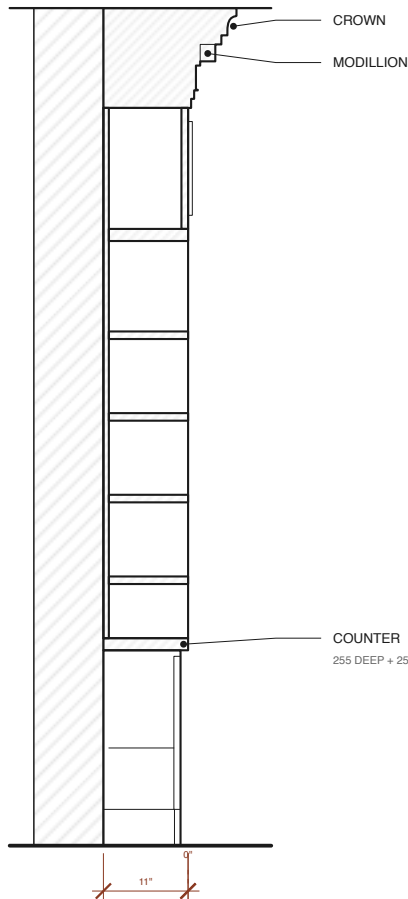

NOTES

REVISION 9

Wall 14 ft 11 in, ceiling 9 ft 1 in (measured).

Centre panel set equal to the window bay so the two pilasters frame a matched pair; the bookcase takes the remainder as the anchor at the end of the wall.

Window measured: 4 ft wide, 5 ft 5 in tall, hard into the right corner. Sill 2 ft 3 in (686) — CONFIRMED.

OPEN: sill 2 ft 3 + height 5 ft 5 + your 1 ft 3 to the ceiling makes 8 ft 11, two inches short of the 9 ft 1 ceiling. Sill and height are drawn as measured, so the head falls 1 ft 5 down, not 1 ft 3. Laser it.

Counter top is set to the sill at 686, so the two are one surface; this datum runs on round to the right wall rail.

Cupboards under all three bays. Gold on handles only.

A STUDY IN TEAK

Particulars of the room

STUDY WALL — GENERAL ARRANGEMENT

Elevation · Plan · Section

SCALE
AS NOTED @ A3

DATE
19.09.2026

REV
9 — sill datum confirmed at 686

DWG
AST-DR-005