


DRESSING ROOM — THE WARDROBES

DEVELOPED ELEVATION · 1:40 · THE THREE WALLS UNFOLDED, LEFT TO RIGHT AS YOU WALK IN

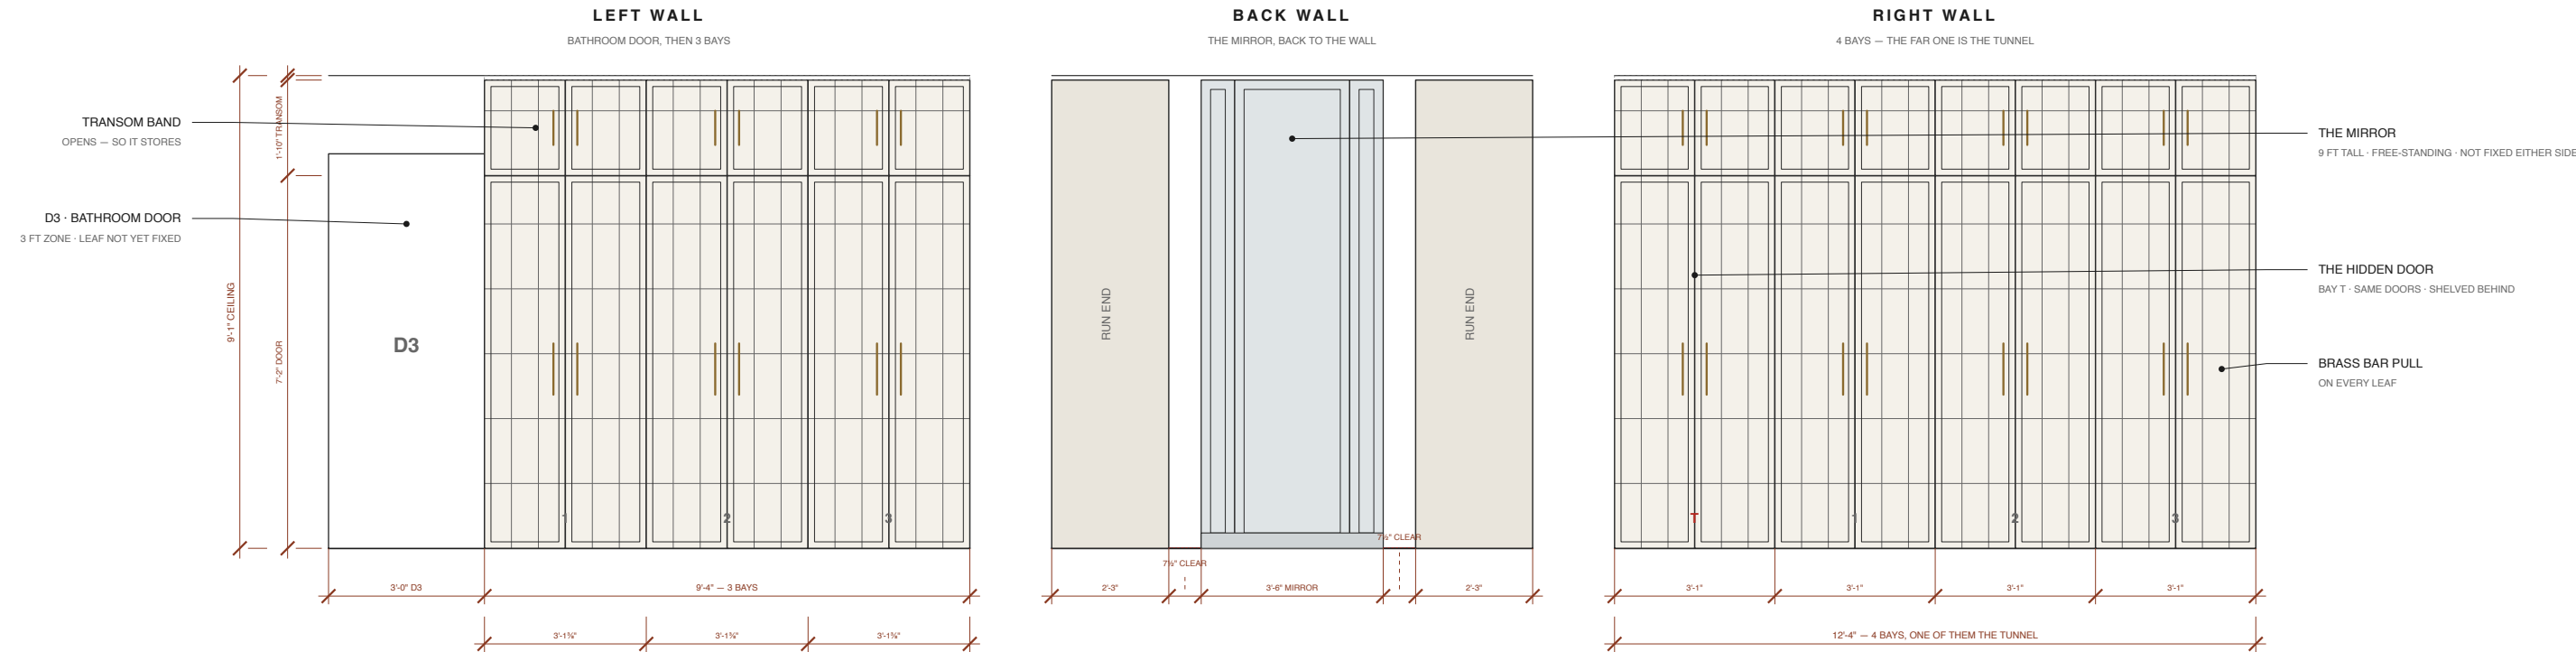

NOTES

REVISION 1

Depth 2 ft 3 in, as instructed. On the right that is what lets the run reach the bedroom wall: the door frame stands 2 ft 4 in off that corner, so the end of the run clears it by 1 in.

Bays are the wall divided equally, so nothing is left over and there are no filler strips: the right wall is 12 ft 4 in over 4 bays, the left is 9 ft 4 in over 3. Both come out at about 3 ft 1 in — an inch over the 3 ft you asked for, which is what makes them land exactly.

Each bay is a pair of doors with a pair of transom lights over, all glazed and all opening — so the transom is storage, not just a band of glass. 7 bays, 14 cupboards, 28 leaves.

Doors as the Wardrobes brief: blackened steel T-section, 38 face, white textured glass in linear lead came, lit from inside, brass bar pulls, transom bar 560 down from the top.

SETTLED — the mirror is a trifold, 3 ft 6 in across with its wings at 45°, free-standing and fixed to neither run. Centred in the 4 ft 9 in gap it leaves 7½ in of floor either side, and it is 9 ft tall — level with the top of the wardrobes. That narrow gap is why the two end bays cannot hinge open in the ordinary way — see AST-DR-026 for the fold-slide doors that solve it.

OPEN — D3, the bathroom door. 3 ft of wall is left for it, but the leaf is still not fixed. It is drawn as an opening only.

OPEN — the tunnel bay reads as one more cupboard, but it is a door onto a passage, so the transom over it cannot be storage in the ordinary way. Decide whether it is a dummy.

OPEN — 4 ft 9 in is what you are left standing in once both runs are built. Open one 1 ft 6 in leaf and there is still 3 ft 3 in. Workable, not generous — worth feeling on site first.

A STUDY IN TEAK

Particulars of the room

THE WARDROBES

Dressing room · developed elevation

SCALE

1:40 @ A3

DATE

25.09.2026

REV

1 — first setting out of the bays, off the owner's 2 ft 3 in depth and 3 ft bay

DWG

AST-DR-025