


PLAN

THE WINDOW WALL AT THE TOP - THE DOOR FROM THE DRESSING ROOM BOTTOM LEFT

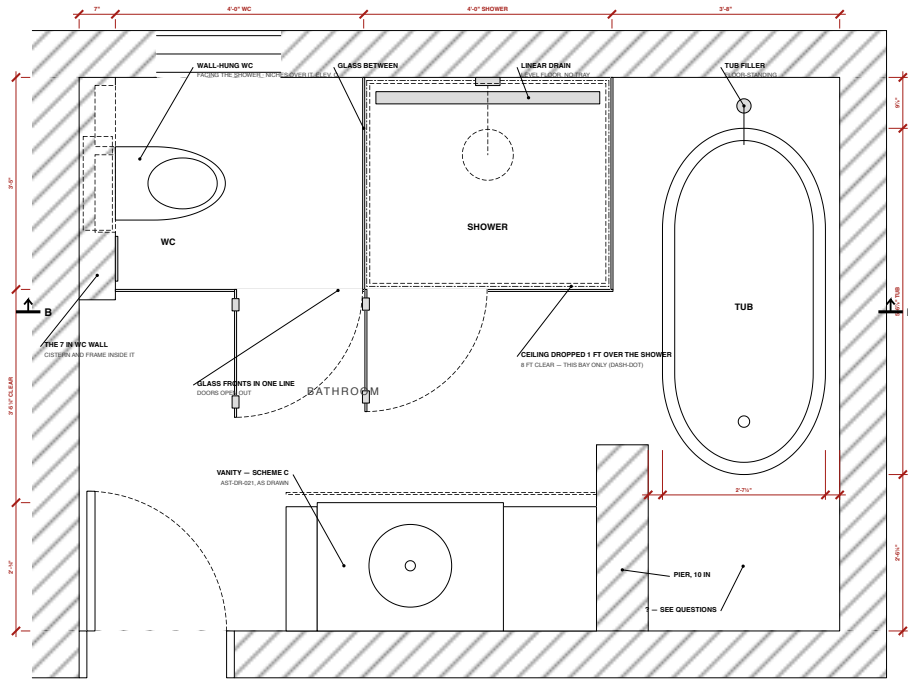


NOTES

REVISION 2

From the owner's sketch and words: along the window wall, after the 7' in wall -- the owner's "WC wall" -- the WC and the shower side by side, each 4 ft wide, both behind glass and coming the same distance off the wall (3 ft 5 in). The tub on the right, in the bay between the pier and the east wall. The vanity stays on the door wall against the pier, as AST-DR-037. That leaves 2 ft 5 in in clear between the glass and the vanity, and the door swings clear of everything. The shell is the measured one; the fittings are all to choose. Rev 2 (pence: 7 Oct): the ceiling drops 1 ft over the shower bay only, to 8 ft clear -- a plastered loss from the window wall to the glass line. Two niches in the WC wall, set side by side above the flush plate, each framed in a marble moulding, as the owner's photo. The window starts at the WC wall's corner, as the photo; its size is left to measure.

ELEVATION C -- THE WC WALL


LOOKING WEST - THE WINDOW WALL ON THE RIGHT

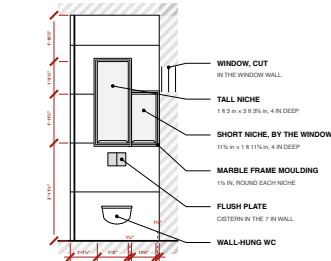

Niches read off the owner's photo -- sizes ASSUMED, to measure on site.

SECTION B-B

JUST IN FRONT OF THE GLASS, LOOKING AT THE WINDOW WALL

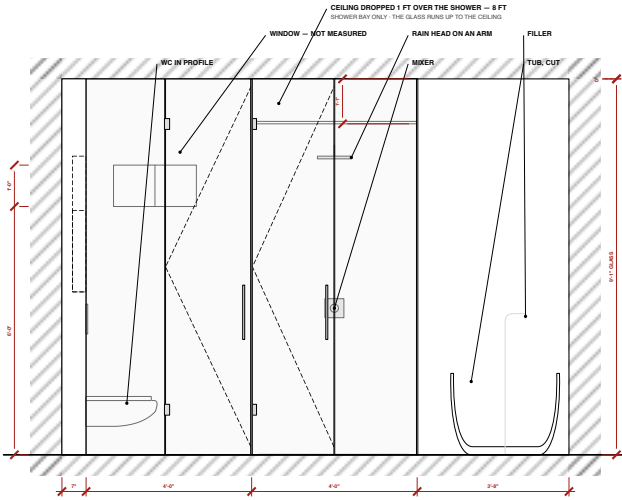

ASSUMED

FROM THE SKETCH -- TELL ME IF ANY OF THESE IS WRONG

WC and shower each 4 ft wide and 3 ft 5 in from the window wall, glass fronts in one line. The WC wall-hung on the 7' in wall, its cistern hidden in it, facing the shower. Glass clear, 1", frameless, 6 ft 6 in in high, open above; chrome hinges, doors opening out. Shower: level floor falling to a linear drain at the back; rain head on an arm, mixer on the wall. Tub: freestanding oval, 5 ft 7 in x 2 ft 7 in, in the 2 ft 5 in bay, a floor-standing filler at its head. Vanity: scheme C, unchanged. The window's size and height are still not measured.

TO ASK

The sketch writes 3'0" by the tub: the tub's width, or the pier's length (it is 3 ft 5 in)

What is the shape along the door wall between the pier and the east wall?

Glass: clear, needed (very 100%) or frosted -- the WC's especially? To the ceiling?

Wall-hung WC, or one standing on the floor? And the walls: marble or plaster?

A STUDY IN TEAK

Particulars of the room

BATHROOM

Plan - Section B-B - The WC wall

SCALE

AS NOTED @ A3

DATE

07.10.2026

REV

2 -- the shower's 1 ft dropped ceiling; the two WC-wall niches

DWG

AST-DR-037

PROJECT
A Study in Teak -- Bathroom

SHEET
General arrangement -- the whole sheet
each view follows at its own scale, pages 2 to 7

SCALE
NTS


DATE
07.10.2026

REV
2

DRAWING
AST-DR-037 · 1 of 7

PLAN

SCALE 1:24 (1/2" = 1'-0") @ A4 · THE WINDOW WALL AT THE TOP · THE DOOR FROM THE DRESSING ROOM BOTTOM LEFT

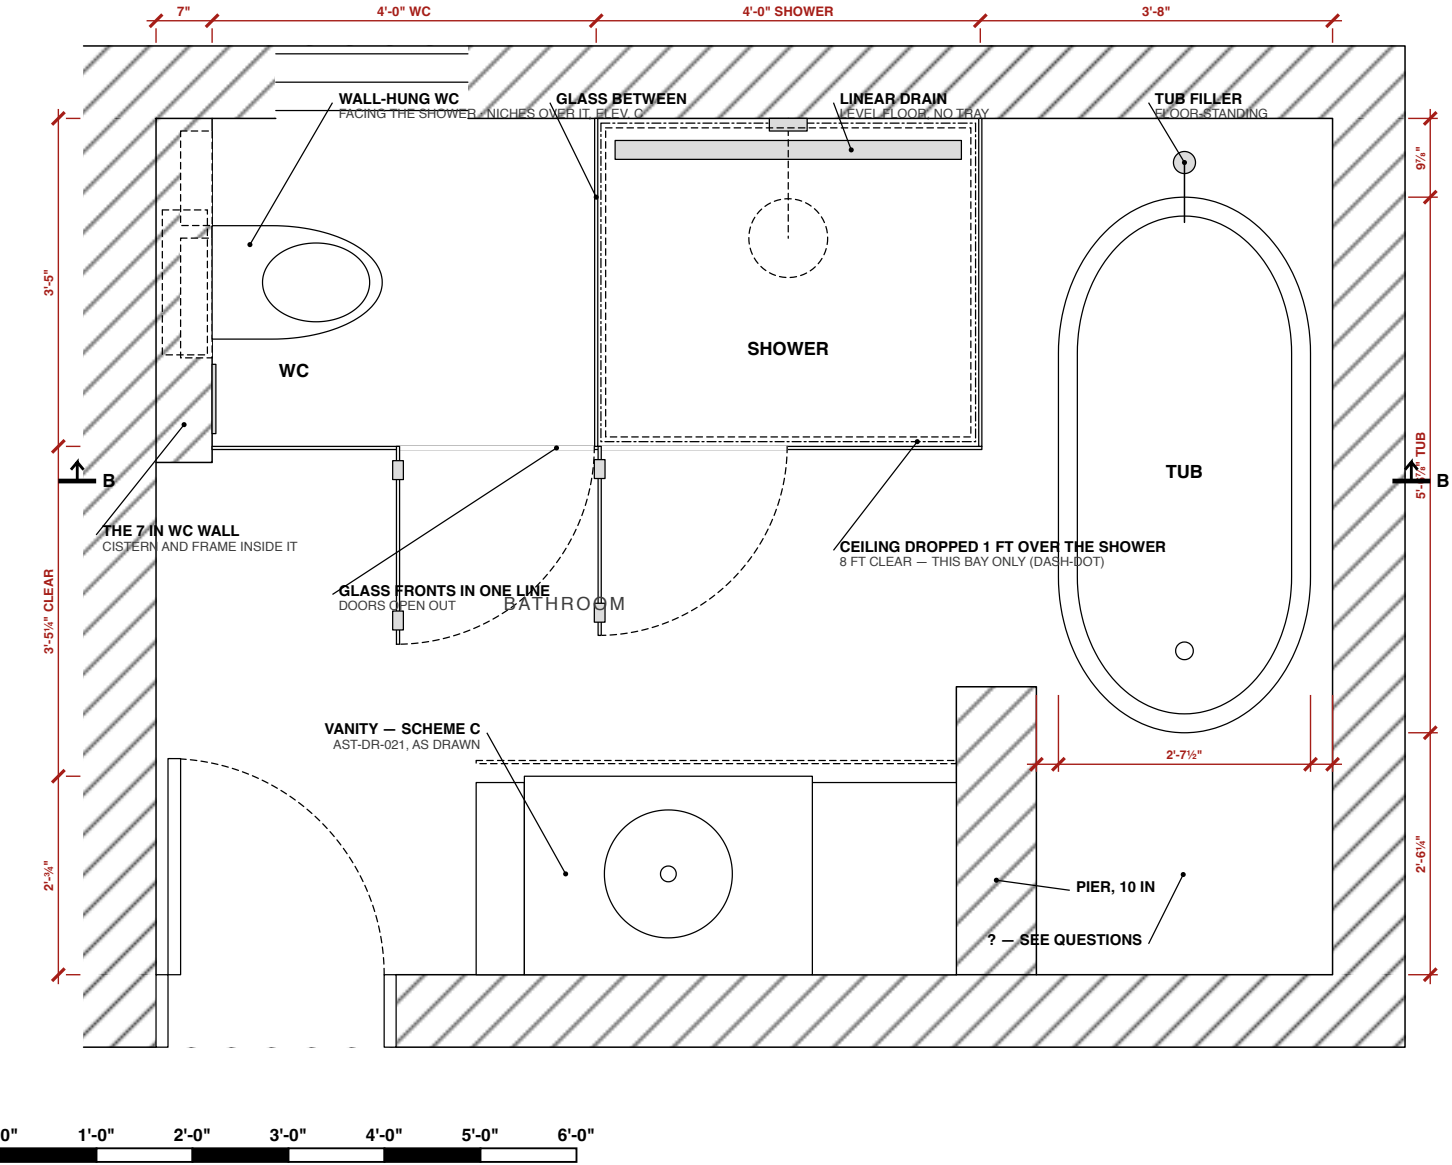

PROJECT
A Study in Teak — Bathroom

SHEET
Plan
Plan · Section B-B · The WC wall

SCALE
1:24 @ A4



DATE
07.10.2026

REV
2

DRAWING
AST-DR-037 · 2 of 7

SECTION B-B

SCALE 1:30 @ A4 · JUST IN FRONT OF THE GLASS, LOOKING AT THE WINDOW WALL

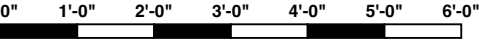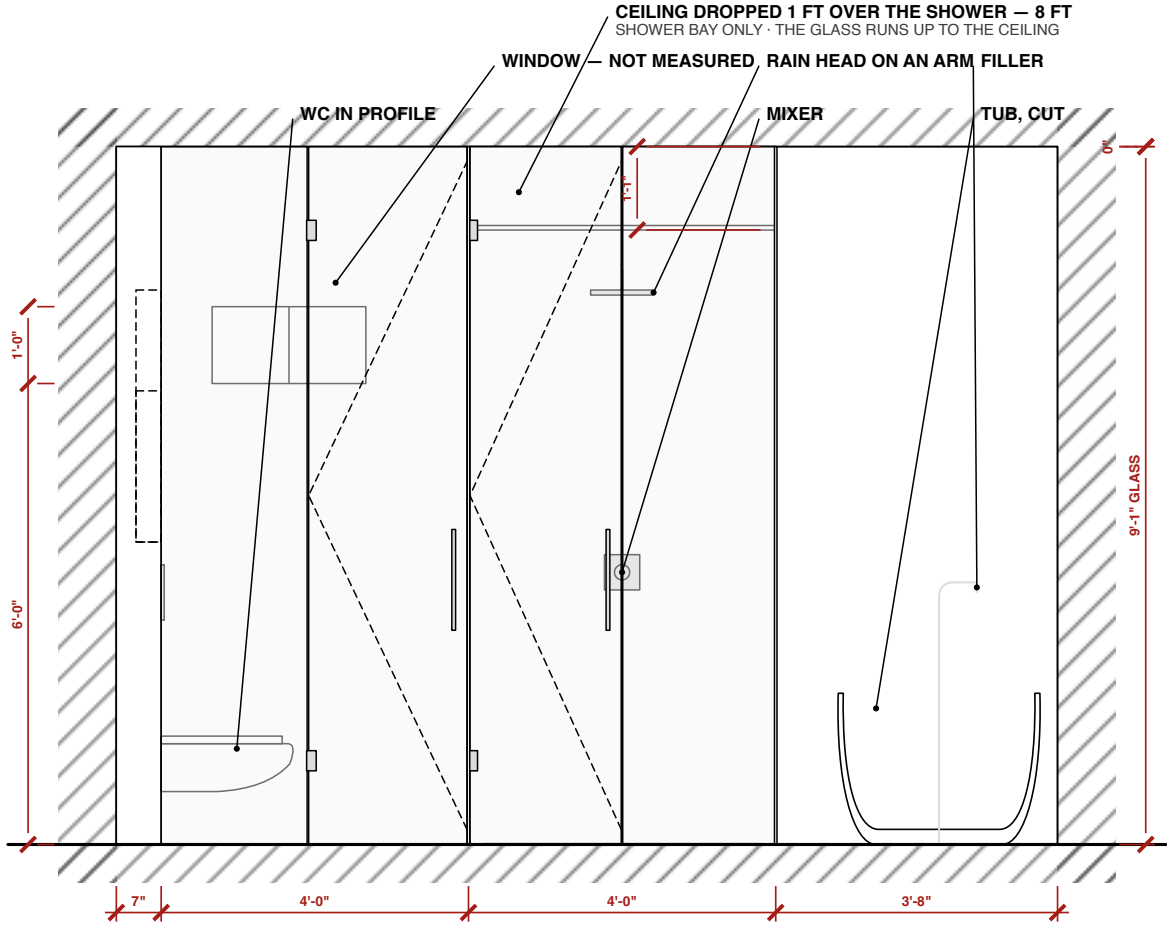

PROJECT A Study in Teak — Bathroom	SHEET Section B-B Plan · Section B-B · The WC wall	SCALE 1:30 @ A4	DATE 07.10.2026	REV 2	DRAWING AST-DR-037 · 3 of 7
---------------------------------------	--	--------------------	--------------------	----------	--------------------------------

ASSUMED

FROM THE SKETCH — TELL ME IF ANY OF THESE IS WRONG

WC and shower each 4 ft wide and 3 ft 5 in from the window wall, glass fronts in one line.

The WC wall-hung on the 7 in wall, its cistern hidden in it, facing the shower.

Glass clear, ¾", frameless, 6 ft 6¾ in high, open above; chrome hinges, doors opening out.

Shower: level floor falling to a linear drain at the back; rain head on an arm, mixer on the wall.

Tub: freestanding oval, 5 ft 7 × 2 ft 7½, in the 3 ft 1 in bay, a floor-standing filler at its head.

Vanity: scheme C, unchanged. The window's size and height are still not measured.

PROJECT
A Study in Teak — Bathroom

SHEET
Assumed
Plan · Section B–B · The WC wall

SCALE
NTS

DATE
07.10.2026

REV
2

DRAWING
AST-DR-037 · 4 of 7

NOTES

REVISION 2

From the owner's sketch and words: along the window wall, after the 7 in wall — the owner's

"WC wall" — the WC and the shower side by side, each 4 ft wide, both behind glass and coming

the same distance off the wall (3 ft 5 in). The tub on the right, in the bay between the pier and

the east wall. The vanity stays on the door wall against the pier, as AST-DR-021.

That leaves 3 ft 5¼ in clear between the glass and the vanity, and the door swings

clear of everything. The shell is the measured one; the fittings are all to choose.

Rev 2 (owner, 7 Oct): the ceiling drops 1 ft over the shower bay only, to 8 ft clear —

a plastered box from the window wall to the glass line. Two niches in the WC wall, tall,

side by side above the flush plate, each framed in a marble moulding, as the owner's photo.

The window starts at the WC wall's corner, as the photo; its size is still to measure.

PROJECT
A Study in Teak — Bathroom

SHEET
Notes
Plan · Section B–B · The WC wall

SCALE
NTS


DATE
07.10.2026

REV
2


DRAWING
AST-DR-037 · 5 of 7

ELEVATION C — THE WC WALL

SCALE 1:30 @ A4 · LOOKING WEST · THE WINDOW WALL ON THE RIGHT

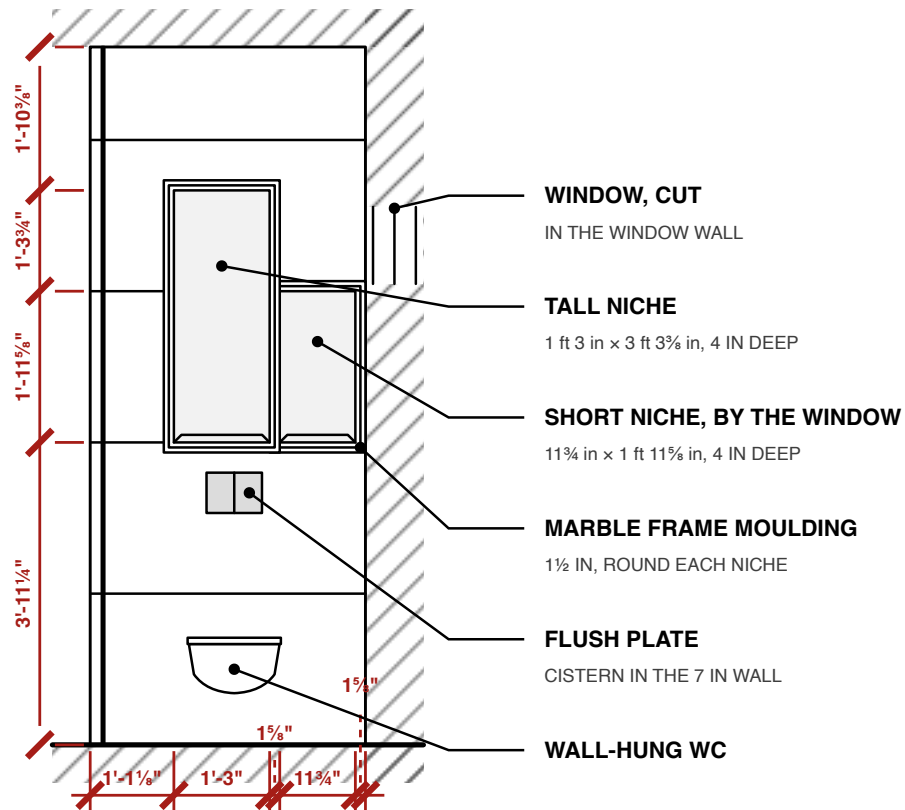

Niches read off the owner's photo — sizes ASSUMED, to measure on site.

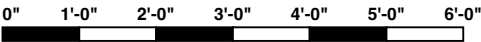

PROJECT
A Study in Teak — Bathroom

SHEET
Elevation c — the wc wall
Plan · Section B–B · The WC wall

SCALE
1:30 @ A4

DATE
07.10.2026

REV
2

DRAWING
AST-DR-037 · 6 of 7

TO ASK

The sketch writes 3'0" by the tub: the tub's width, or the pier's length (it is 3 ft)?

What is the shape along the door wall between the pier and the east wall?

Glass: clear, reeded (very 1930s) or frosted — the WC's especially? To the ceiling?

Wall-hung WC, or one standing on the floor? And the walls: marble or plaster?

PROJECT	SHEET	SCALE	DATE	REV	DRAWING
A Study in Teak — Bathroom	To ask Plan · Section B–B · The WC wall	NTS	07.10.2026	2	AST-DR-037 · 7 of 7