

THE WINDOW WALL AT THE TOP · THE DOOR FROM THE DRESSING ROOM BOTTOM LEFT



REVISION 2

From the owner's sketch and words: along the window wall, after the 7 in wall — the owner's

"WC wall" — the WC and the shower side by side, each 4 ft wide, both behind glass and coming the same distance off the wall (3 ft 5 in). The tub on the right, in the bay between the pier and the east wall. The vanity stays on the door wall against the pier, as AST-DR-021.

That leaves 3 ft 5½ in clear between the glass and the vanity, and the door swing

clear of everything. The shell is the measured one; the fittings are all to choose.

Rev 2 (owner, 7 Oct): the ceiling drops 1 ft over the shower bay only, to 8 ft clear —

a plastered box from the window wall to the glass line. Two niches in the WC wall, tall, side by side above the flush plate, each framed in a marble moulding, as the owner's photo.

The window starts at the WC wall's corner, as the photo; its size is still to measure.

LOOKING WEST · THE WINDOW WALL ON THE RIGHT



JUST IN FRONT OF THE GLASS, LOOKING AT THE WINDOW WALL



WC and shower each 4 ft wide and 3 ft 5 in from the window wall, glass fronts in one line.

The WC wall-hung on the 7 in wall, its cistern hidden in it, facing the shower

Glass clear, 3/4", frameless, 6 ft 6 1/2 in high, open above; chrome hinges, doors opening out.

Shower: level floor falling to a linear drain at the back; rain head on an arm, mixer on the wall.

Tub: freestanding oval, 5 ft 7 x 2 ft 7½, in the 3 ft 1 in bay, a floor-standing filler at its head.

Vanity: scheme C, unchanged. The window's size and height are still not measured.

The sketch writes 3'0" by the tub: the tub's width, or the pier's length (it is 3 ft)?

What is the shape along the door wall between the pier and the east wall?

Glass: clear, reeded (very 1930s) or frosted — the WC's especially? To the

Wall-hung WC, or one standing on the floor? And the walls: marble or plaster?

Particulars of the room

Plan - Section B-B - The WC wall

SCALE AS NOTED @ A3	DATE 07.10.2026
REV 2 – the shower's 1 ft dropped ceiling; the two WC-wall niches	DWG AST-DR-037

PROJECT

A Study in Teak — Bathroom

SHEET

General arrangement — the whole sheet

each view follows at its own scale, pages 2 to 7

SCALE

NTS

DATE _____

07.10.2026

REV

2


DRAWING

AST-DR-037 · 1 of 7

ALL DIMENSIONS IN FEET & INCHES. PRINT ON A3 AT 100% / "ACTUAL SIZE" — NOT "FIT TO PAGE" — AND CHECK THE SCALE BAR. DO NOT SCALE; WORK TO FIGURED DIMENSIONS. VERIFY ON SITE.

PLAN

SCALE 1:16 (3/4" = 1'-0") @ A3 · THE WINDOW WALL AT THE TOP · THE DOOR FROM THE DRESSING ROOM BOTTOM LEFT

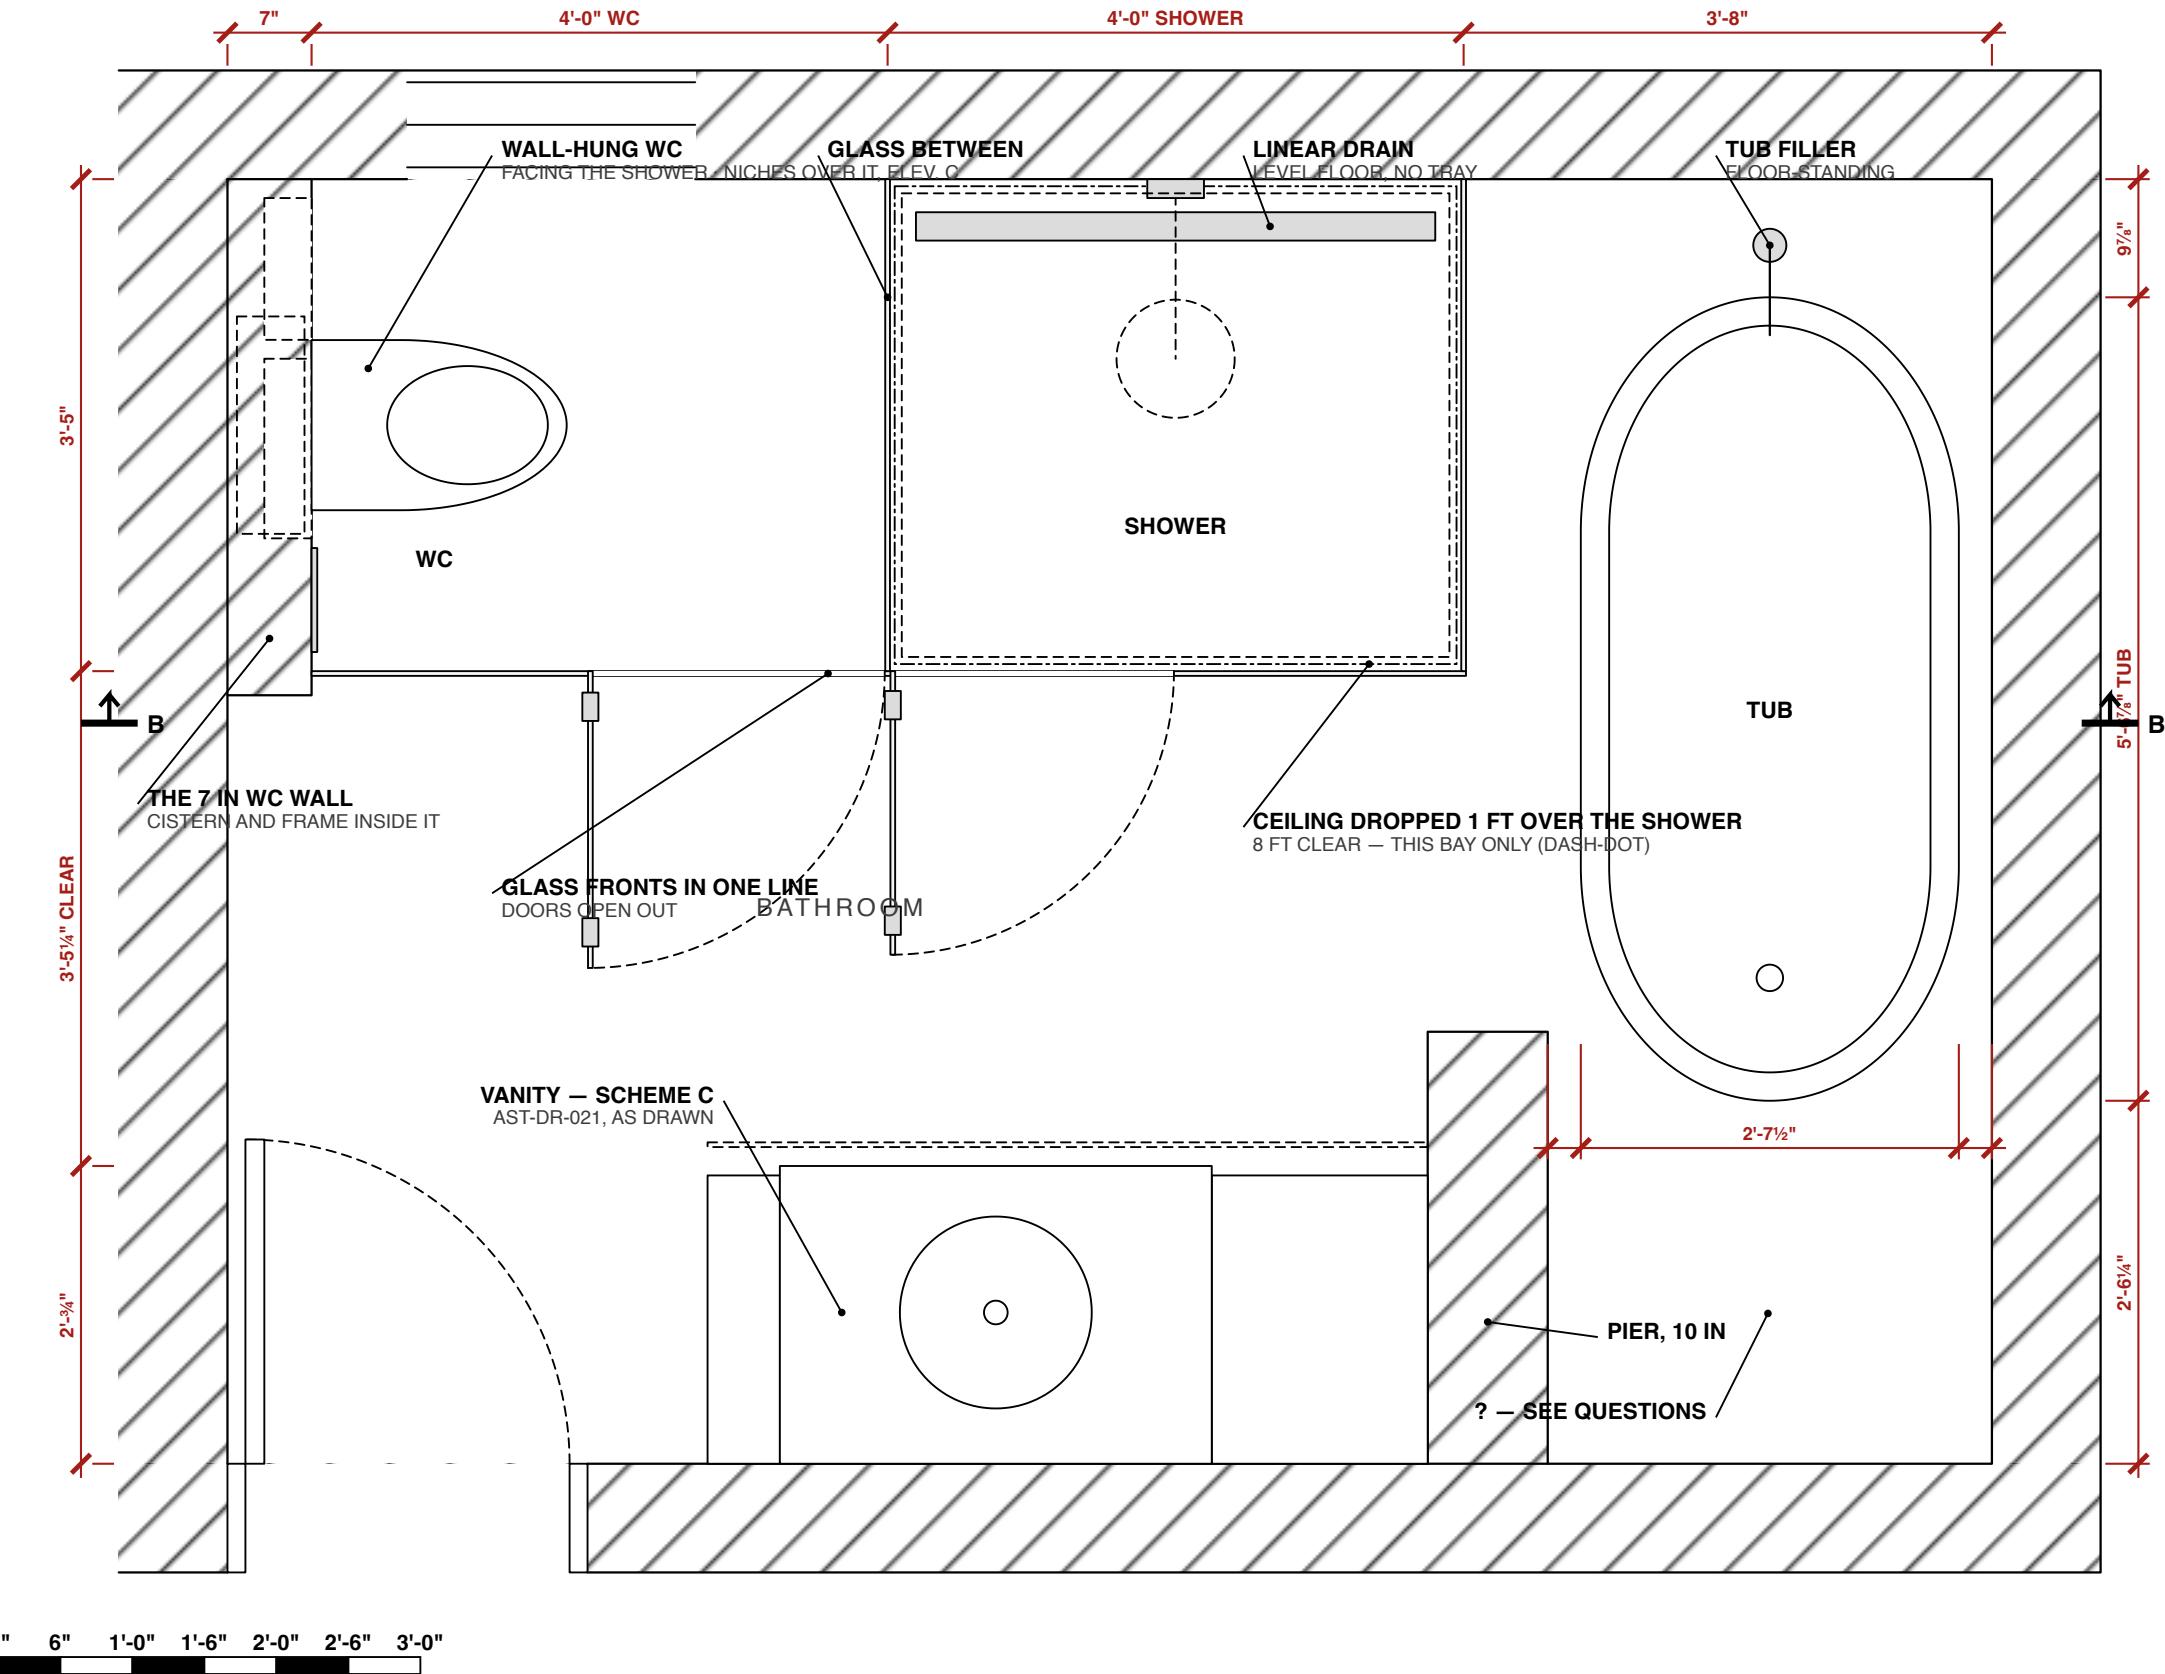

PROJECT
A Study in Teak — Bathroom

SHEET
Plan
Plan · Section B-B · The WC wall

SCALE
1:16 @ A3


DATE
07.10.2026

REV
2

DRAWING
AST-DR-037 · 2 of 7

SECTION B-B

SCALE 1:20 @ A3 · JUST IN FRONT OF THE GLASS, LOOKING AT THE WINDOW WALL

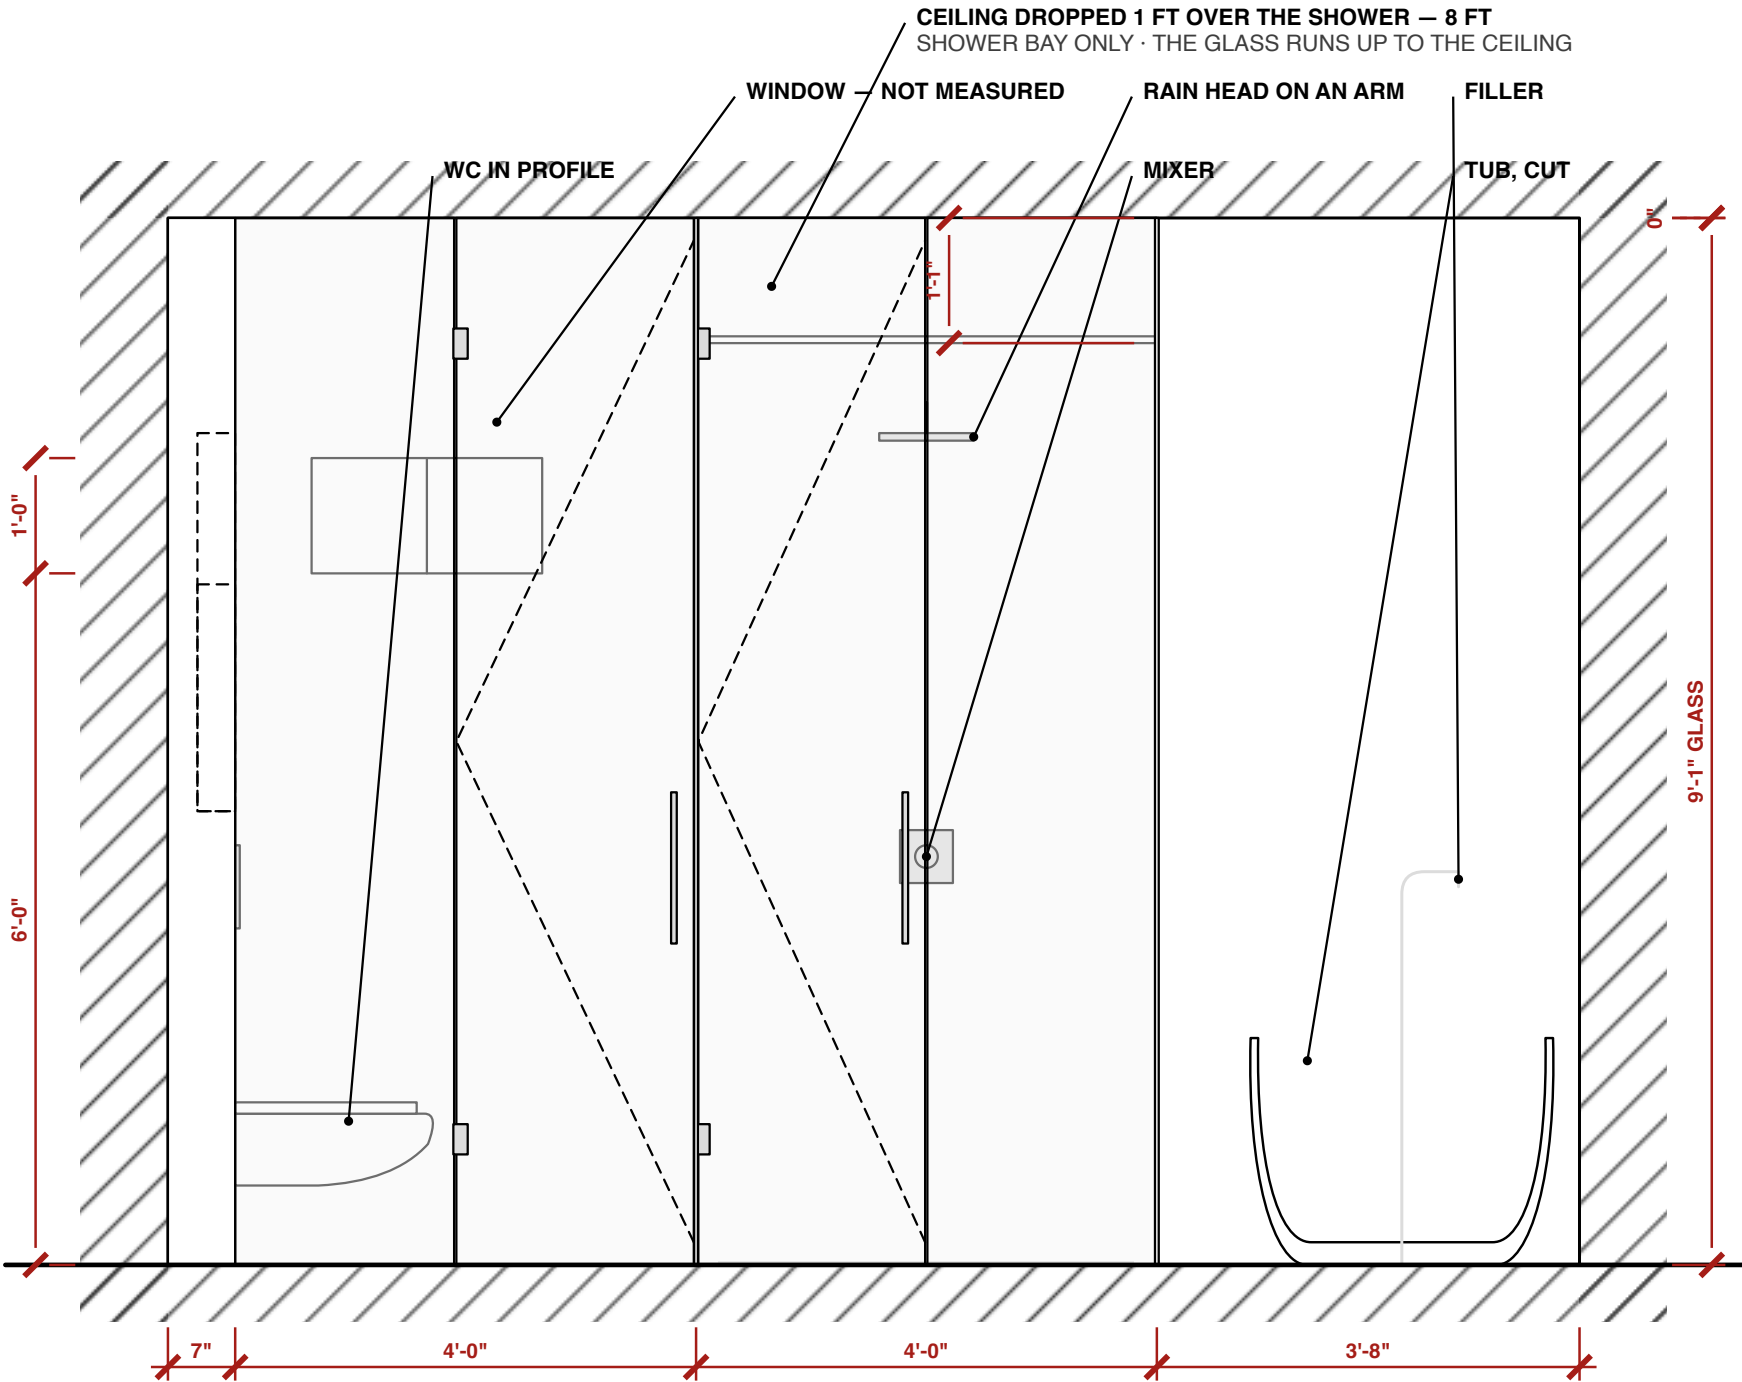

PROJECT
A Study in Teak — Bathroom

SHEET
Section B-B
Plan · Section B-B · The WC wall

SCALE
1:20 @ A3

DATE
07.10.2026

REV
2

DRAWING
AST-DR-037 · 3 of 7

ASSUMED

FROM THE SKETCH — TELL ME IF ANY OF THESE IS WRONG

WC and shower each 4 ft wide and 3 ft 5 in from the window wall, glass fronts in one line.

The WC wall-hung on the 7 in wall, its cistern hidden in it, facing the shower.

Glass clear, 3⁄8", frameless, 6 ft 6¾ in high, open above; chrome hinges, doors opening out.

Shower: level floor falling to a linear drain at the back; rain head on an arm, mixer on the wall.

Tub: freestanding oval, 5 ft 7 × 2 ft 7½, in the 3 ft 1 in bay, a floor-standing filler at its head.

Vanity: scheme C, unchanged. The window's size and height are still not measured.

PROJECT
A Study in Teak — Bathroom

SHEET
Assumed
Plan · Section B–B · The WC wall

SCALE
NTS

DATE
07.10.2026

REV
2

DRAWING
AST-DR-037 · 4 of 7

NOTES

REVISION 2

From the owner's sketch and words: along the window wall, after the 7 in wall — the owner's

"WC wall" — the WC and the shower side by side, each 4 ft wide, both behind glass and coming

the same distance off the wall (3 ft 5 in). The tub on the right, in the bay between the pier and

the east wall. The vanity stays on the door wall against the pier, as AST-DR-021.

That leaves 3 ft 5¼ in clear between the glass and the vanity, and the door swings

clear of everything. The shell is the measured one; the fittings are all to choose.

Rev 2 (owner, 7 Oct): the ceiling drops 1 ft over the shower bay only, to 8 ft clear —

a plastered box from the window wall to the glass line. Two niches in the WC wall, tall,


side by side above the flush plate, each framed in a marble moulding, as the owner's photo.

The window starts at the WC wall's corner, as the photo; its size is still to measure.


PROJECT A Study in Teak — Bathroom	SHEET Notes Plan · Section B–B · The WC wall	SCALE NTS	DATE 07.10.2026	REV 2	DRAWING AST-DR-037 · 5 of 7
---------------------------------------	--	--------------	--------------------	----------	--------------------------------

ELEVATION C — THE WC WALL

SCALE 1:20 @ A3 · LOOKING WEST · THE WINDOW WALL ON THE RIGHT

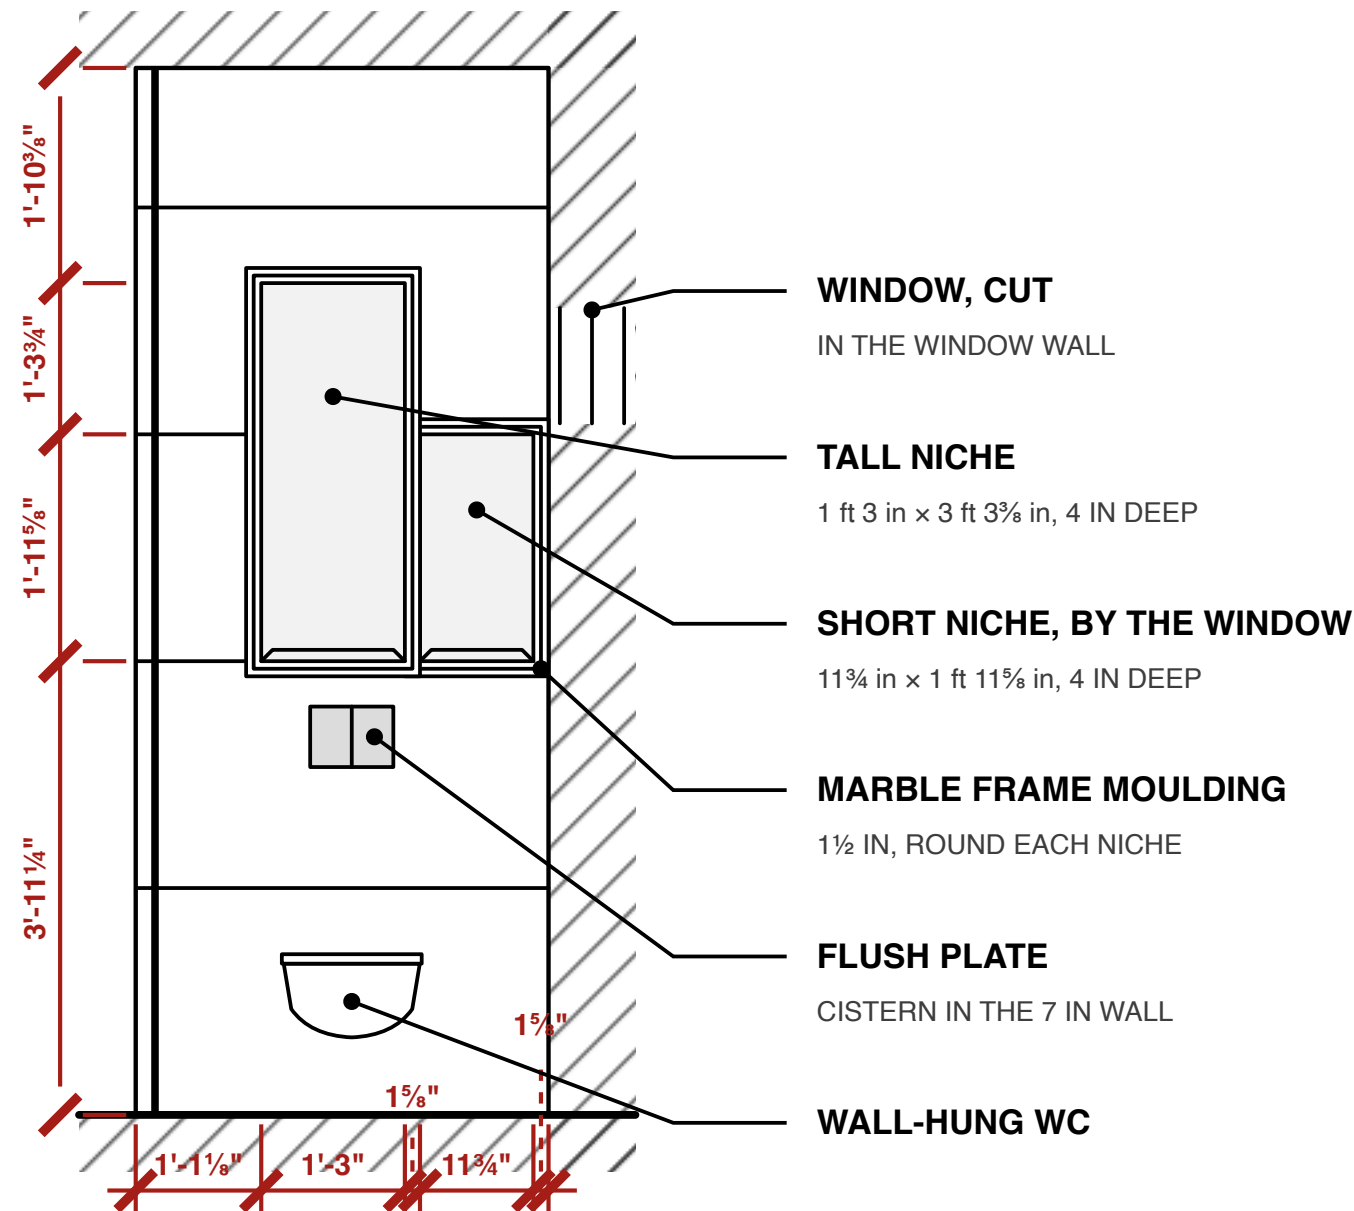

Niches read off the owner's photo — sizes ASSUMED, to measure on site.

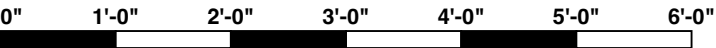

PROJECT
A Study in Teak — Bathroom

SHEET
Elevation c — the wc wall
Plan · Section B–B · The WC wall

SCALE
1:20 @ A3

DATE
07.10.2026

REV
2

DRAWING
AST-DR-037 · 6 of 7

TO ASK

The sketch writes 3'0" by the tub: the tub's width, or the pier's length (it is 3 ft)?

What is the shape along the door wall between the pier and the east wall?

Glass: clear, reeded (very 1930s) or frosted — the WC's especially? To the ceiling?

Wall-hung WC, or one standing on the floor? And the walls: marble or plaster?

PROJECT
A Study in Teak — Bathroom

SHEET
To ask
Plan · Section B–B · The WC wall

SCALE
NTS

DATE
07.10.2026

REV
2

DRAWING
AST-DR-037 · 7 of 7