



FRONT

FINAL - 1 FT 6 LEFT, 6 IN RIGHT - 3 FT MARBLE BANK ON THE FAUCET - THE ROW WALL-HUNG 6 IN OFF THE FLOOR, A DRAIN BELOW

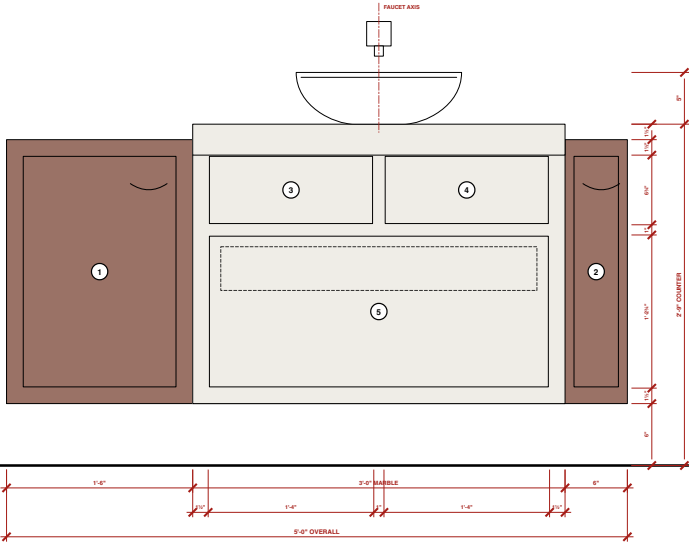

PLAN

FROM ABOVE - WALL AT THE TOP

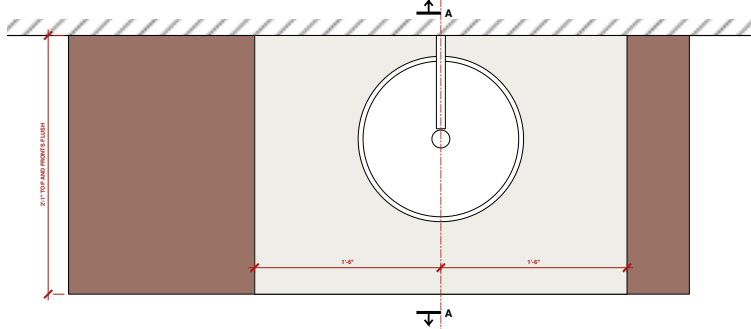

SECTION KEY

- A Hanging cabinet  
B Big drawer, U-box  
C Waste D11V and P-trap  
E Wall support  
F Ply sub-top  
G Inner drawer

NOTES

REVISION 5

Rev 5: the marble bank is back — face frame and fronts — but stops 6 in off the floor, level with the under a drain is on the floor below. The row hangs on the wall, no support. Top drawers 6 1/2 in; the big drawer 14 1/2 in, a 4 in inner one.


OPEN — bowl D11V 4" x 3" and the spout are assumed.

OPEN — marble front thickness and its bond to the drawer boxes, and the brackets' slat: stone supplier to confirm.

Rev 2: top and front meet in one mitred corner, flush.


SECTION A-A

ON THE FAUCET AXIS

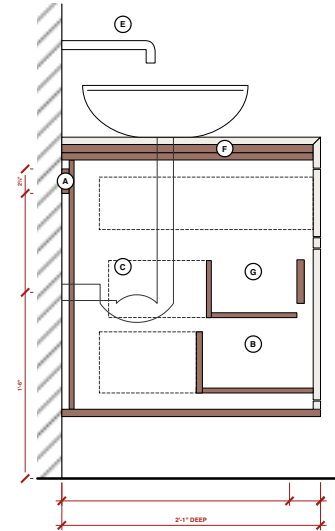


DETAIL 2 - THE BIG DRAWER

PLAN - INNER DRAWER DASHED

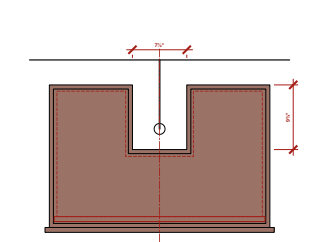

DETAIL 1 - THE MARBLE EDGE

SECTION - ONE MITRED CORNER, FRONTS FLUSH

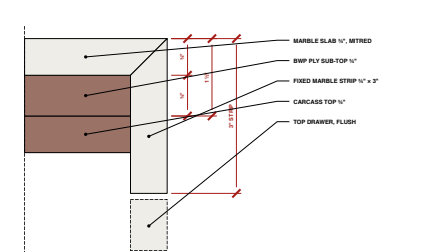

FRONTS

SIZES ARE THE FRONT ITSELF - 1/4" GAP ALL ROUND

| No. | NOTAT                                 | W x H                  | FT-IN                  |
|-----|---------------------------------------|------------------------|------------------------|
| 1   | Pull-out cabinet, cup pull            | 1'-2 1/2" x 1'-10 1/4" | 1'-2 1/2" x 1'-10 1/4" |
| 2   | Pull-out cabinet, cup pull            | 4 1/2" x 1'-10 1/4"    | 4 1/2" x 1'-10 1/4"    |
| 3   | Top drawer, push-open - marble        | 1'-3 1/2" x 6 1/2"     | 1'-3 1/2" x 6 1/2"     |
| 4   | Top drawer, push-open - marble        | 1'-3 1/2" x 6 1/2"     | 1'-3 1/2" x 6 1/2"     |
| 5   | Big drawer, U-box, push-open - marble | 2'-8 1/2" x 1'-2 1/2"  | 2'-8 1/2" x 1'-2 1/2"  |
| 5a  | Inner drawer, finger scoop            | 2'-8 1/2" x 4 1/2"     | 2'-8 1/2" x 4 1/2"     |

MATERIALS

THE ROOM'S PALETTE — NOTHING NEW

- Top: Beige-gold marble, the bathroom stone, 1 1/2" slab on a 1/2" BWP sub-top, mitred at the front edge into a fixed 1/2" marble strip: one corner, fronts flush.
- Bank: The same beige marble on the face frame and on every drawer front, bonded to BWP boxes. It stops 6 in off the face, level with the under a drain below.
- Ends: Two pull-out cabinets, 3032 hot-veneer, polished dark and red (the owner's photo), glass, edges sealed.
- Hanging: 10" ply crest 2'-3 1/2" x 2'-6 1/2" and concealed steel brackets into the wall: the stone is heavy. Nothing on the floor.
- Ledges: The two veneer tops, solid nooting, sealed.
- Runners: Drawers: undermount, push-to-open. Pull-outs: heavy full-extension runners, cup pull.
- Fittings: Chrome — already bought.

A STUDY IN TEAK

Particulars of the room

VANITY — SCHEME C

Final - marble bank and top - dark red but pull-outs - wall-hung, 6 in clear

|                                                                                           |                    |
|-------------------------------------------------------------------------------------------|--------------------|
| SCALE<br>AS NOTED @ A3                                                                    | DATE<br>08.10.2026 |
| REV<br>5 — marble bank 6 in off the floor (a slab below), wall-hung: ends in dark red but | DWG<br>AST-DR-021  |

PROJECT

A Study in Teak — Vanity — Scheme C

SHEET

General arrangement — the whole sheet

each view follows at its own scale, pages 2 to 10

SCALE

NTS

DATE

08.10.2026

REV



5

DRAWING

AST-DR-021 · 1 of 10

FRONT



SCALE 1:10 @ A4 · FINAL · 1 FT 6 LEFT, 6 IN RIGHT · 3 FT MARBLE BANK ON THE FAUCET · THE ROW WALL-HUNG 6 IN OFF THE FLOOR, A DR.

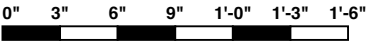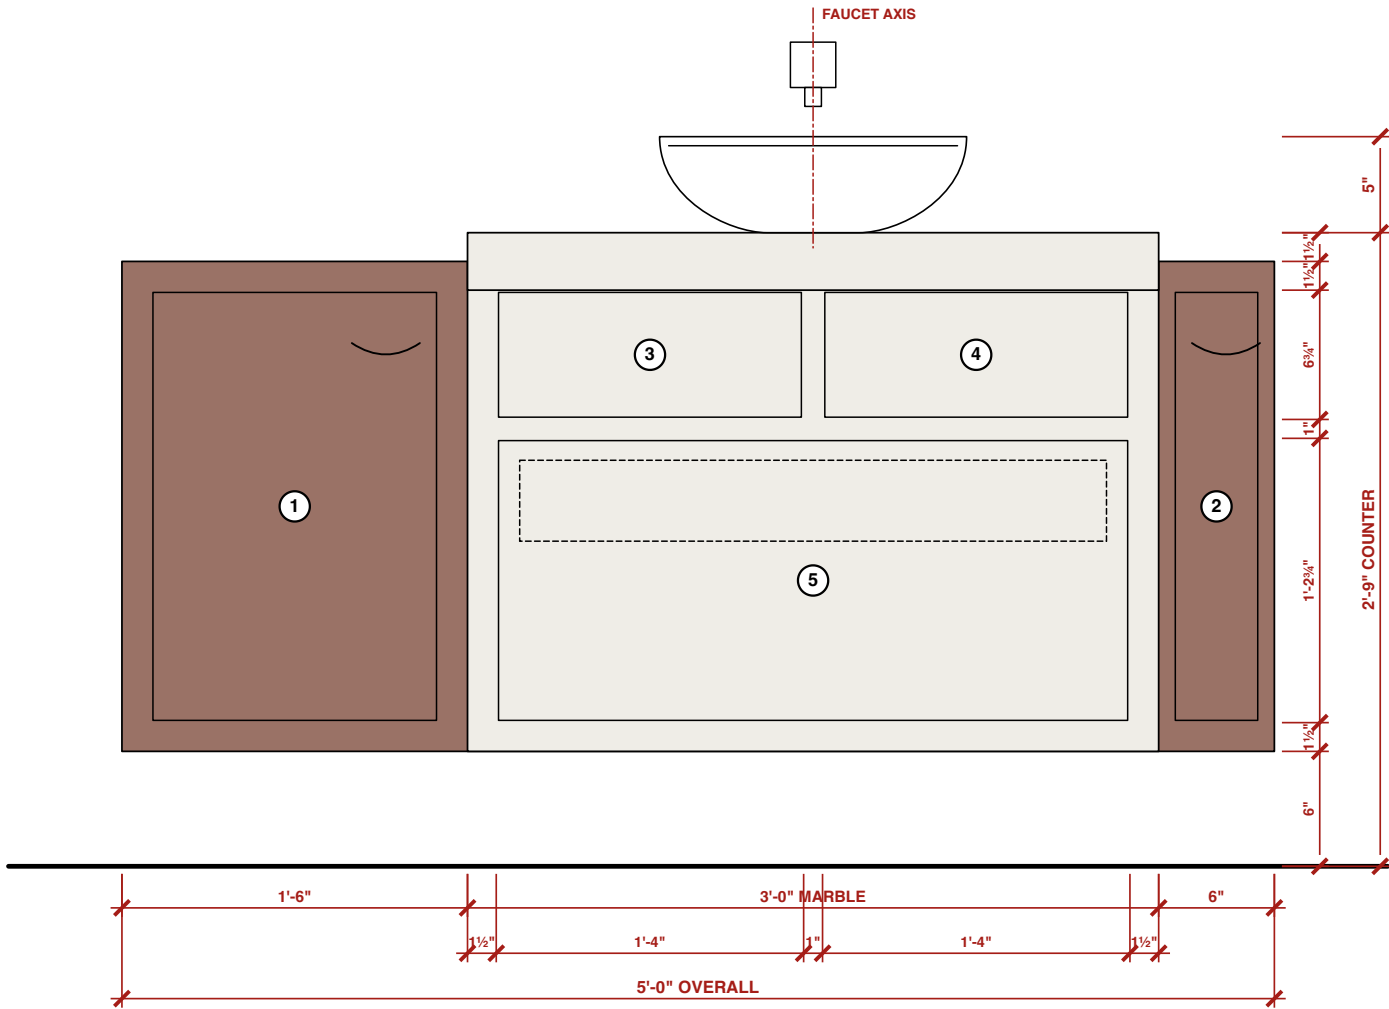

|                                                |                                                                                                 |                    |                    |          |                                 |
|------------------------------------------------|-------------------------------------------------------------------------------------------------|--------------------|--------------------|----------|---------------------------------|
| PROJECT<br>A Study in Teak — Vanity — Scheme C | SHEET<br>Front<br>Final · marble bank and top · dark red burl pull-outs · wall-hung, 6 in clear | SCALE<br>1:10 @ A4 | DATE<br>08.10.2026 | REV<br>5 | DRAWING<br>AST-DR-021 · 2 of 10 |
|------------------------------------------------|-------------------------------------------------------------------------------------------------|--------------------|--------------------|----------|---------------------------------|

SECTION A-A

SCALE 1:10 @ A4 · ON THE FAUCET AXIS

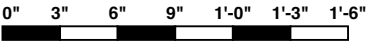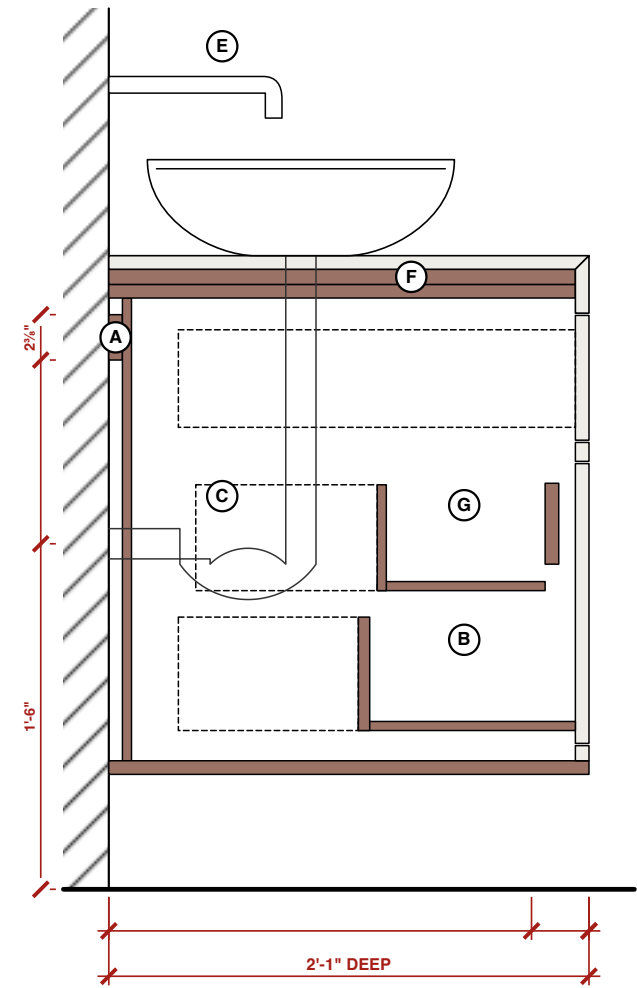

PROJECT  
A Study in Teak — Vanity — Scheme C

SHEET  
**Section A-A**  
Final · marble bank and top · dark red burl pull-outs · wall-hung, 6 in clear

SCALE  
1:10 @ A4


DATE  
08.10.2026

REV  
5

DRAWING  
**AST-DR-021 · 3 of 10**

# DETAIL 1 · THE MARBLE EDGE

SCALE 1:1 (FULL SIZE) @ A4 · SECTION · ONE MITRED CORNER, FRONTS FLUSH

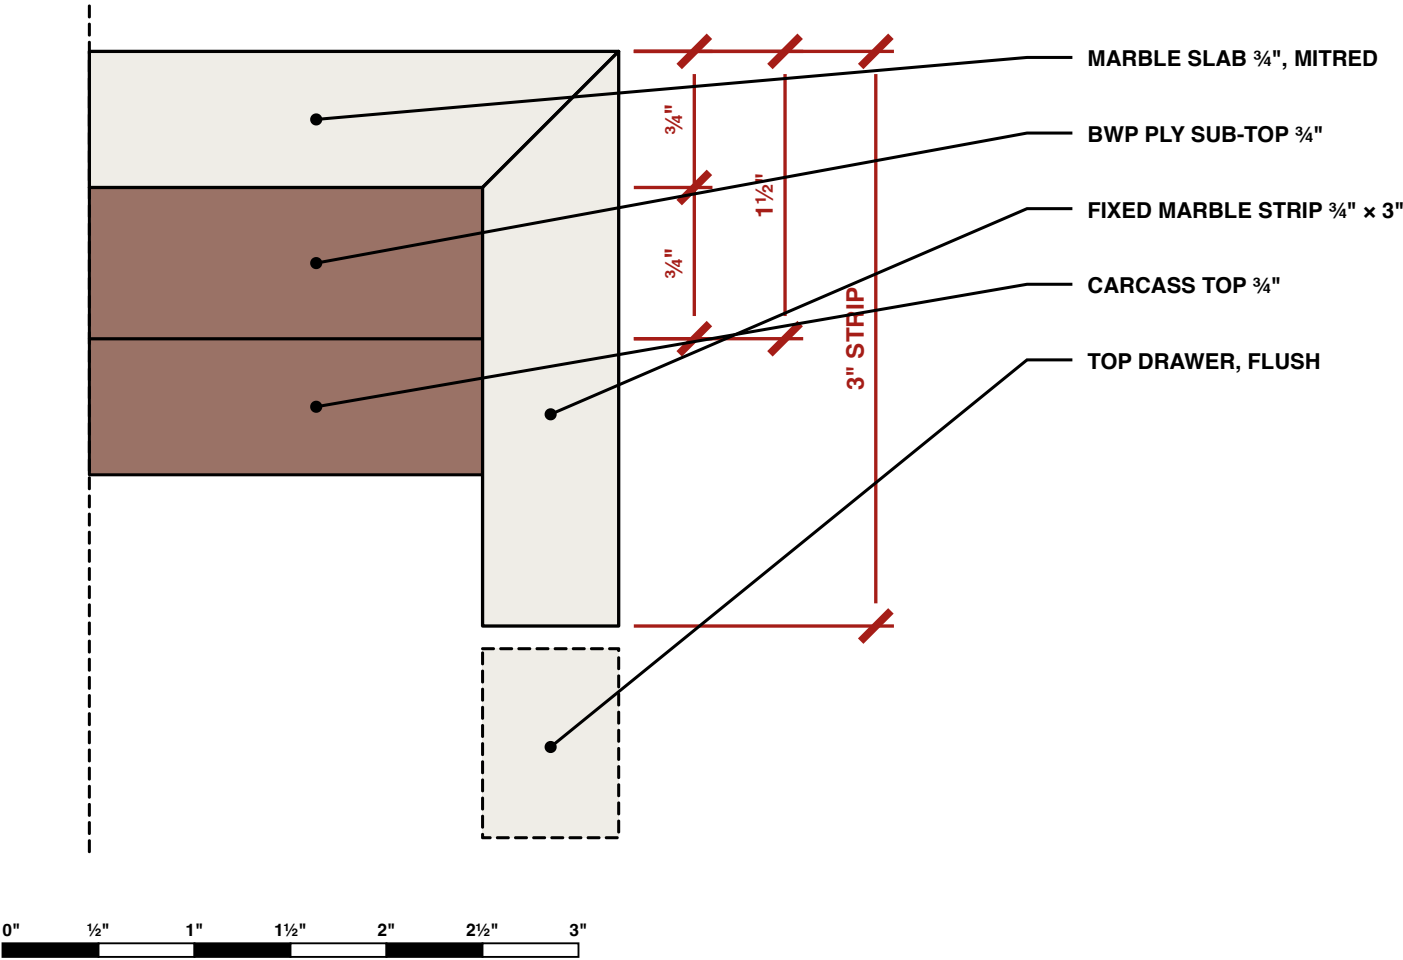

|                                     |   |          |            |     |                             |
|-------------------------------------|---|----------|------------|-----|-----------------------------|
| PROJECT                             | SHEET   | SCALE    | DATE       | REV | DRAWING                     |
| A Study in Teak — Vanity — Scheme C | <b>Detail 1 · the marble edge</b><br>Final · marble bank and top · dark red burl pull-outs · wall-hung, 6 in clear | 1:1 @ A4 | 08.10.2026 | 5   | <b>AST-DR-021 · 4 of 10</b> |

# FRONTS

SIZES ARE THE FRONT ITSELF · 1/8" GAP ALL ROUND

| No. | WHAT                                  | W × H            | FT-IN            |
|-----|---------------------------------------|------------------|------------------|
| 1   | Pull-out cabinet, cup pull            | 1'-2¾" × 1'-10¼" | 1'-2¾" × 1'-10¼" |
| 2   | Pull-out cabinet, cup pull            | 4¼" × 1'-10¼"    | 4¼" × 1'-10¼"    |
| 3   | Top drawer, push-open · marble        | 1'-3¾" × 6½"     | 1'-3¾" × 6½"     |
| 4   | Top drawer, push-open · marble        | 1'-3¾" × 6½"     | 1'-3¾" × 6½"     |
| 5   | Big drawer, U-box, push-open · marble | 2'-8¾" × 1'-2⅝"  | 2'-8¾" × 1'-2⅝"  |
| 5a  | Inner drawer, finger scoop            | 2'-6½" × 4¼"     | 2'-6½" × 4¼"     |

|                                     |                                                                                         |       |            |     |                      |
|-------------------------------------|-----------------------------------------------------------------------------------------|-------|------------|-----|----------------------|
| PROJECT                             | SHEET                                                                                   | SCALE | DATE       | REV | DRAWING              |
| A Study in Teak — Vanity — Scheme C | Fronts<br>Final · marble bank and top · dark red burl pull-outs · wall-hung, 6 in clear | NTS   | 08.10.2026 | 5   | AST-DR-021 · 5 of 10 |

# MATERIALS



## THE ROOM'S PALETTE — NOTHING NEW

|          |   |
|----------|---|
| Top      | Beige-gold marble, the bathroom stone. ¾" slab<br><br>on a ¾" BWP sub-top, mitred at the front edge into<br><br>a fixed ¾" marble strip: one corner, fronts flush.     |
| Bank     | The same beige marble on the face frame and on<br><br>every drawer front, bonded to BWP boxes. It stops<br><br>6 in off the floor, level with the ends: a drain below. |
| Ends     | Two pull-out cabinets, 9292 burl veneer, polished<br><br>dark and red (the owner's photo), gloss, edges sealed.                                                        |
| Hanging  | ¾" ply cleat 2'-3½"—2'-5⅞" and concealed steel brackets<br><br>into the wall: the stone is heavy. Nothing on the floor.                                                |
| Ledges   | The two veneer tops: solid nosing, sealed.   |
| Runners  | Drawers: undermount, push-to-open. Pull-outs:<br><br>heavy full-extension runners, cup pull.                                                                           |
| Fittings | Chrome — already bought.   |

|                                                |   |              |                    |          |                                 |
|------------------------------------------------|---|--------------|--------------------|----------|---------------------------------|
| PROJECT<br>A Study in Teak — Vanity — Scheme C | SHEET<br>Materials<br>Final · marble bank and top · dark red burl pull-outs · wall-hung, 6 in clear | SCALE<br>NTS | DATE<br>08.10.2026 | REV<br>5 | DRAWING<br>AST-DR-021 · 6 of 10 |
|------------------------------------------------|---|--------------|--------------------|----------|---------------------------------|

PLAN



SCALE 1:8 (1½" = 1'-0") @ A4 · FROM ABOVE · WALL AT THE TOP

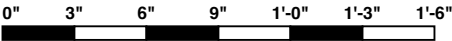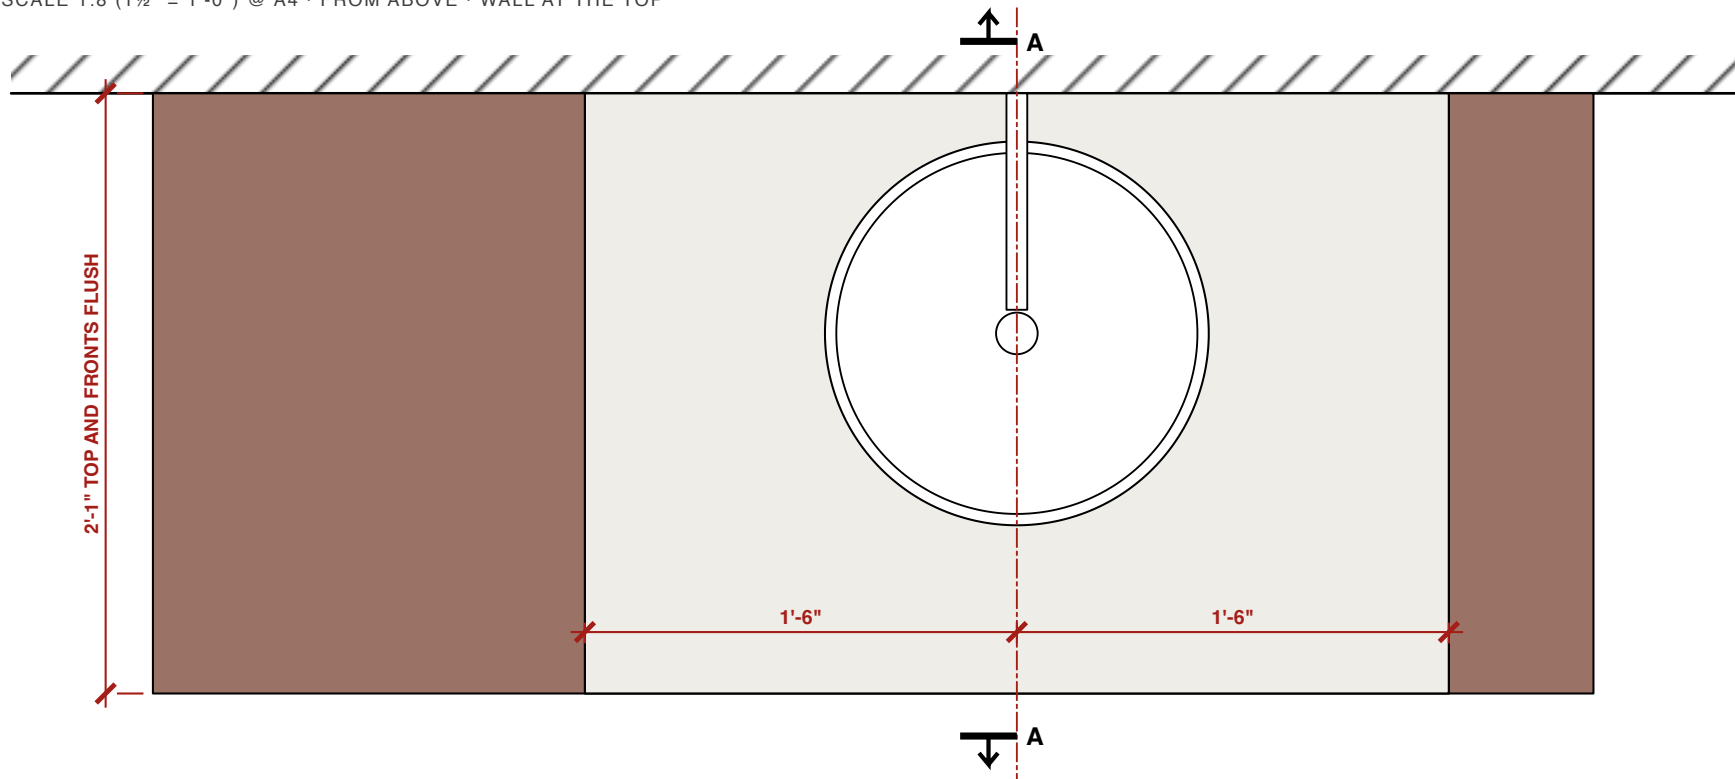

|                                     |                                                                                              |          |            |     |                             |
|-------------------------------------|----------------------------------------------------------------------------------------------|----------|------------|-----|-----------------------------|
| PROJECT                             | SHEET                                                                                        | SCALE    | DATE       | REV | DRAWING                     |
| A Study in Teak — Vanity — Scheme C | <b>Plan</b><br>Final · marble bank and top · dark red burl pull-outs · wall-hung, 6 in clear | 1:8 @ A4 | 08.10.2026 | 5   | <b>AST-DR-021 · 7 of 10</b> |

# DETAIL 2 · THE BIG DRAWER

SCALE 1:8 (1½" = 1'-0") @ A4 · PLAN · INNER DRAWER DASHED

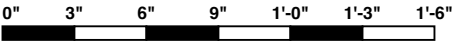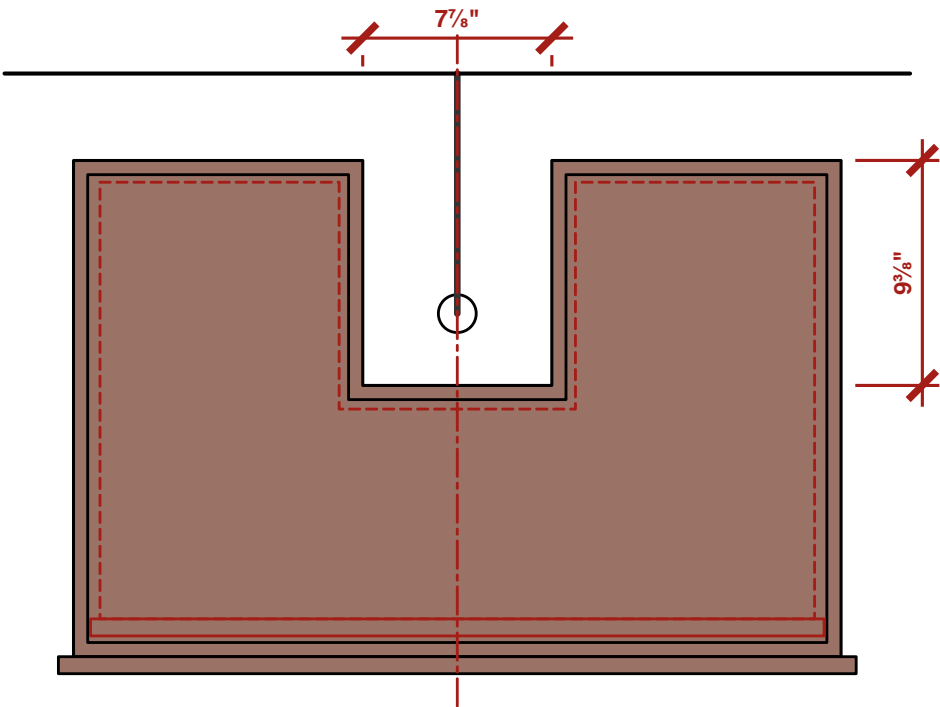

PROJECT  
A Study in Teak — Vanity — Scheme C

SHEET  
**Detail 2 · the big drawer**  
Final · marble bank and top · dark red burl pull-outs · wall-hung, 6 in clear

SCALE  
1:8 @ A4

DATE  
08.10.2026

REV  
5

DRAWING  
**AST-DR-021 · 8 of 10**

SECTION KEY

- A

Hanging cleat
- B

Big drawer, U-box
- C

Waste Ø1<sup>5</sup>/<sub>8</sub>" and P-trap
- E

Wall spout
- F

Ply sub-top
- G

Inner drawer

|                                                |   |              |                    |          |                                 |
|------------------------------------------------|---|--------------|--------------------|----------|---------------------------------|
| PROJECT<br>A Study in Teak — Vanity — Scheme C | SHEET<br>Section key<br>Final · marble bank and top · dark red burl pull-outs · wall-hung, 6 in clear | SCALE<br>NTS | DATE<br>08.10.2026 | REV<br>5 | DRAWING<br>AST-DR-021 · 9 of 10 |
|------------------------------------------------|---|--------------|--------------------|----------|---------------------------------|

NOTES

REVISION 5

Rev 5: the marble bank is back — face frame and fronts —  
but stops 6 in off the floor, level with the ends: a drain  
is on the floor below. The row hangs on the wall; no support.  
Top drawers 6½ in; the big drawer 14½ in, a 4 in inner one.

OPEN — bowl Ø1'-4" x 5" and the spout are assumed.  
OPEN — marble front thickness and its bond to the drawer  
boxes, and the brackets' size: stone supplier to confirm.  
Rev 3: top and front meet in one mitred corner, flush.

|                                                |                                                                                                 |              |                    |          |                                  |
|------------------------------------------------|-------------------------------------------------------------------------------------------------|--------------|--------------------|----------|----------------------------------|
| PROJECT<br>A Study in Teak — Vanity — Scheme C | SHEET<br>Notes<br>Final · marble bank and top · dark red burl pull-outs · wall-hung, 6 in clear | SCALE<br>NTS | DATE<br>08.10.2026 | REV<br>5 | DRAWING<br>AST-DR-021 · 10 of 10 |
|------------------------------------------------|-------------------------------------------------------------------------------------------------|--------------|--------------------|----------|----------------------------------|