



FRONT

FINAL · 1 FT 6 LEFT, 6 IN RIGHT · 3 FT MARBLE BANK ON THE FAUCET · THE ROW WALL-HUNG 6 IN OFF THE FLOOR, A DRAIN BELOW

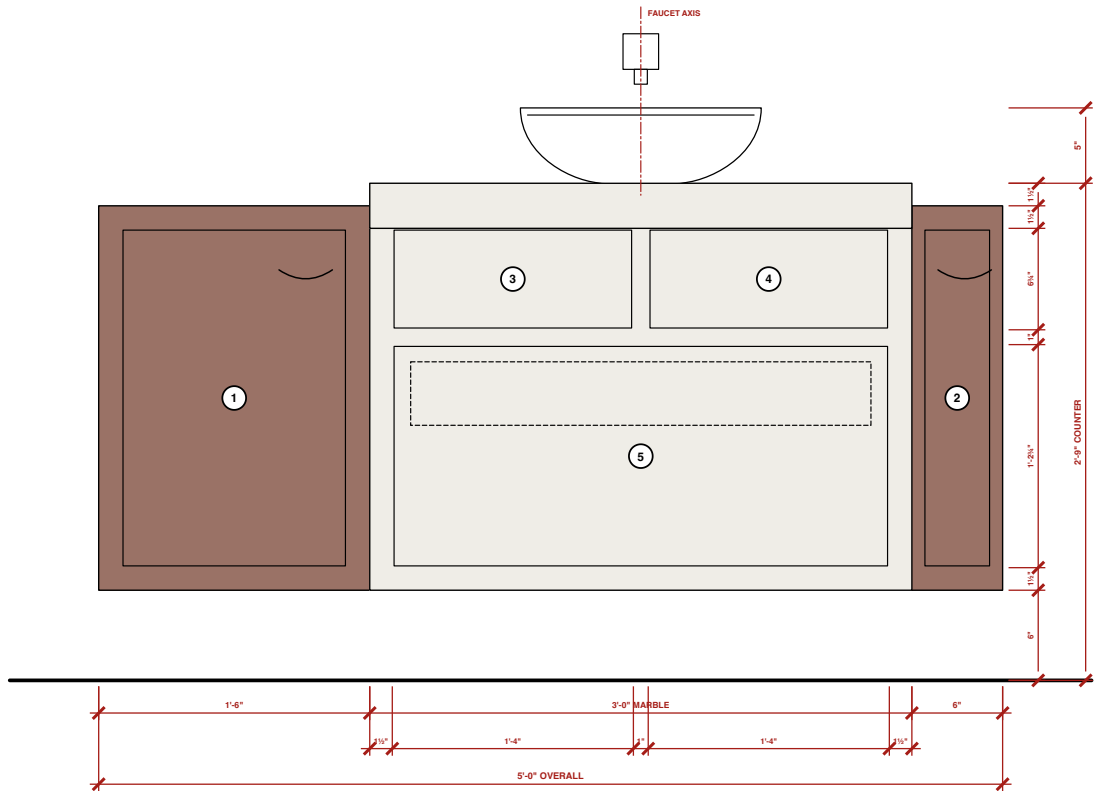

PLAN

FROM ABOVE · WALL AT THE TOP

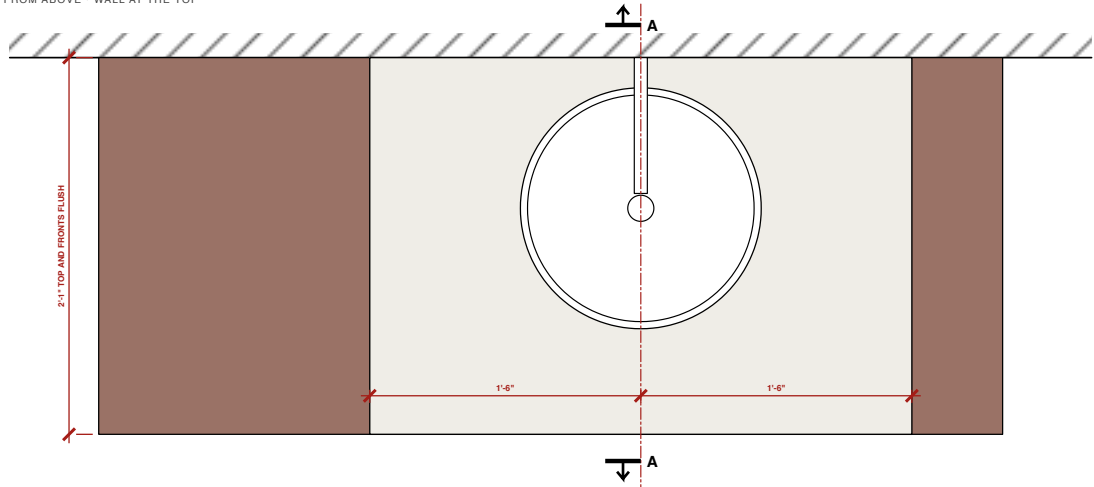

SECTION KEY

- (A) Hanging cleat (B) Big drawer, U-box (C) Waste Ø1½" and P-trap (E) Wall spout (F) Ply sub-top (G) Inner drawer

NOTES

REVISION 5

Rev 5: the marble bank is back — face frame and fronts — but stops 6 in off the floor, level with the ends: a drain is on the floor below. The row hangs on the wall; no support. Top drawers 6½ in; the big drawer 14½ in, a 4 in inner one.


OPEN — bowl Ø1'-4" x 5" and the spout are assumed.

OPEN — marble front thickness and its bond to the drawer boxes, and the brackets' size: stone supplier to confirm.

Rev 3: top and front meet in one mitred corner, flush.


SECTION A-A

ON THE FAUCET AXIS

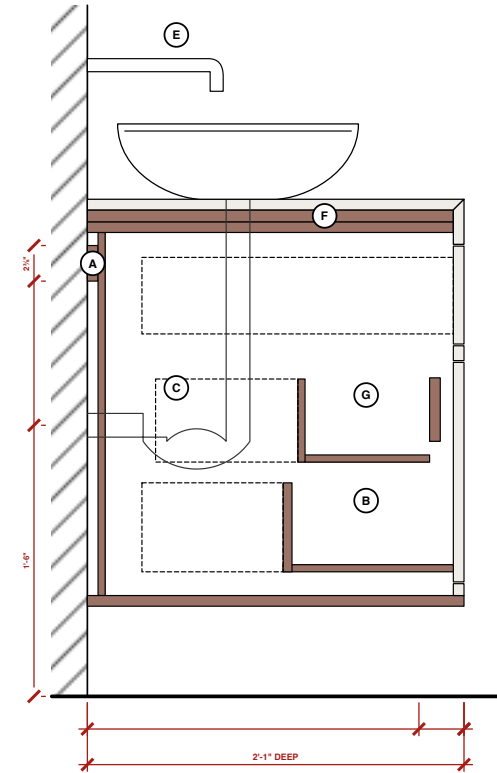


DETAIL 2 · THE BIG DRAWER

PLAN · INNER DRAWER DASHED

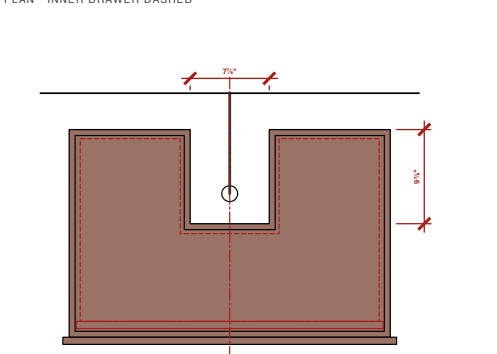

DETAIL 1 · THE MARBLE EDGE

SECTION · ONE MITRED CORNER, FRONTS FLUSH

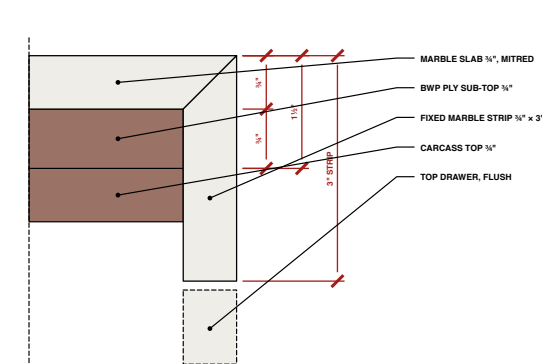

FRONTS

SIZES ARE THE FRONT ITSELF · ¼" GAP ALL ROUND

No.	WHAT	W x H	FT-IN
1	Pull-out cabinet, cup pull	1'-2¼" x 1'-10¼"	1'-2¾" x 1'-10¼"
2	Pull-out cabinet, cup pull	4¼" x 1'-10¼"	4¼" x 1'-10¼"
3	Top drawer, push-open · marble	1'-3¼" x 6¼"	1'-3¾" x 6¼"
4	Top drawer, push-open · marble	1'-3¼" x 6¼"	1'-3¾" x 6¼"
5	Big drawer, U-box, push-open · marble	2'-8¼" x 1'-2¼"	2'-8¾" x 1'-2¾"
5a	Inner drawer, finger scoop	2'-6¼" x 4¼"	2'-6½" x 4¼"

MATERIALS

THE ROOM'S PALETTE — NOTHING NEW

- Top: Beige-gold marble, the bathroom stone. ¾" slab on a ¾" BWP sub-top, mitred at the front edge into a fixed ¾" marble strip: one corner, fronts flush.
- Bank: The same beige marble on the face frame and on every drawer front, bonded to BWP boxes. It stops 6 in off the floor, level with the ends: a drain below.
- Ends: Two pull-out cabinets, 9292 burl veneer, polished dark and red (the owner's photo), gloss, edges sealed.
- Hanging: ¾" ply cleat 2'-3½"-2'-5¼" and concealed steel brackets into the wall: the stone is heavy. Nothing on the floor.
- Ledges: The two veneer tops: solid nosing, sealed.
- Runners: Drawers: undermount, push-to-open. Pull-outs: heavy full-extension runners, cup pull.
- Fittings: Chrome — already bought.

A STUDY IN TEAK

Particulars of the room

VANITY — SCHEME C

Final · marble bank and top · dark red burl pull-outs · wall-hung, 6 in clear

SCALE AS NOTED @ A3	DATE 08.10.2026
REV 5 — marble bank 6 in off the floor (a drain below), wall-hung: ends in dark red burl	DWG AST-DR-021

PROJECT

A Study in Teak — Vanity — Scheme C

SHEET

General arrangement — the whole sheet

each view follows at its own scale, pages 2 to 10

SCALE

NTS

DATE

08.10.2026

REV



5

DRAWING

AST-DR-021 · 1 of 10

FRONT

SCALE 1:8 (1½" = 1'-0") @ A3 · FINAL · 1 FT 6 LEFT, 6 IN RIGHT · 3 FT MARBLE BANK ON THE FAUCET · THE ROW WALL-HUNG 6 IN OFF THE FL

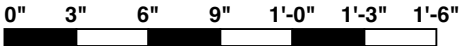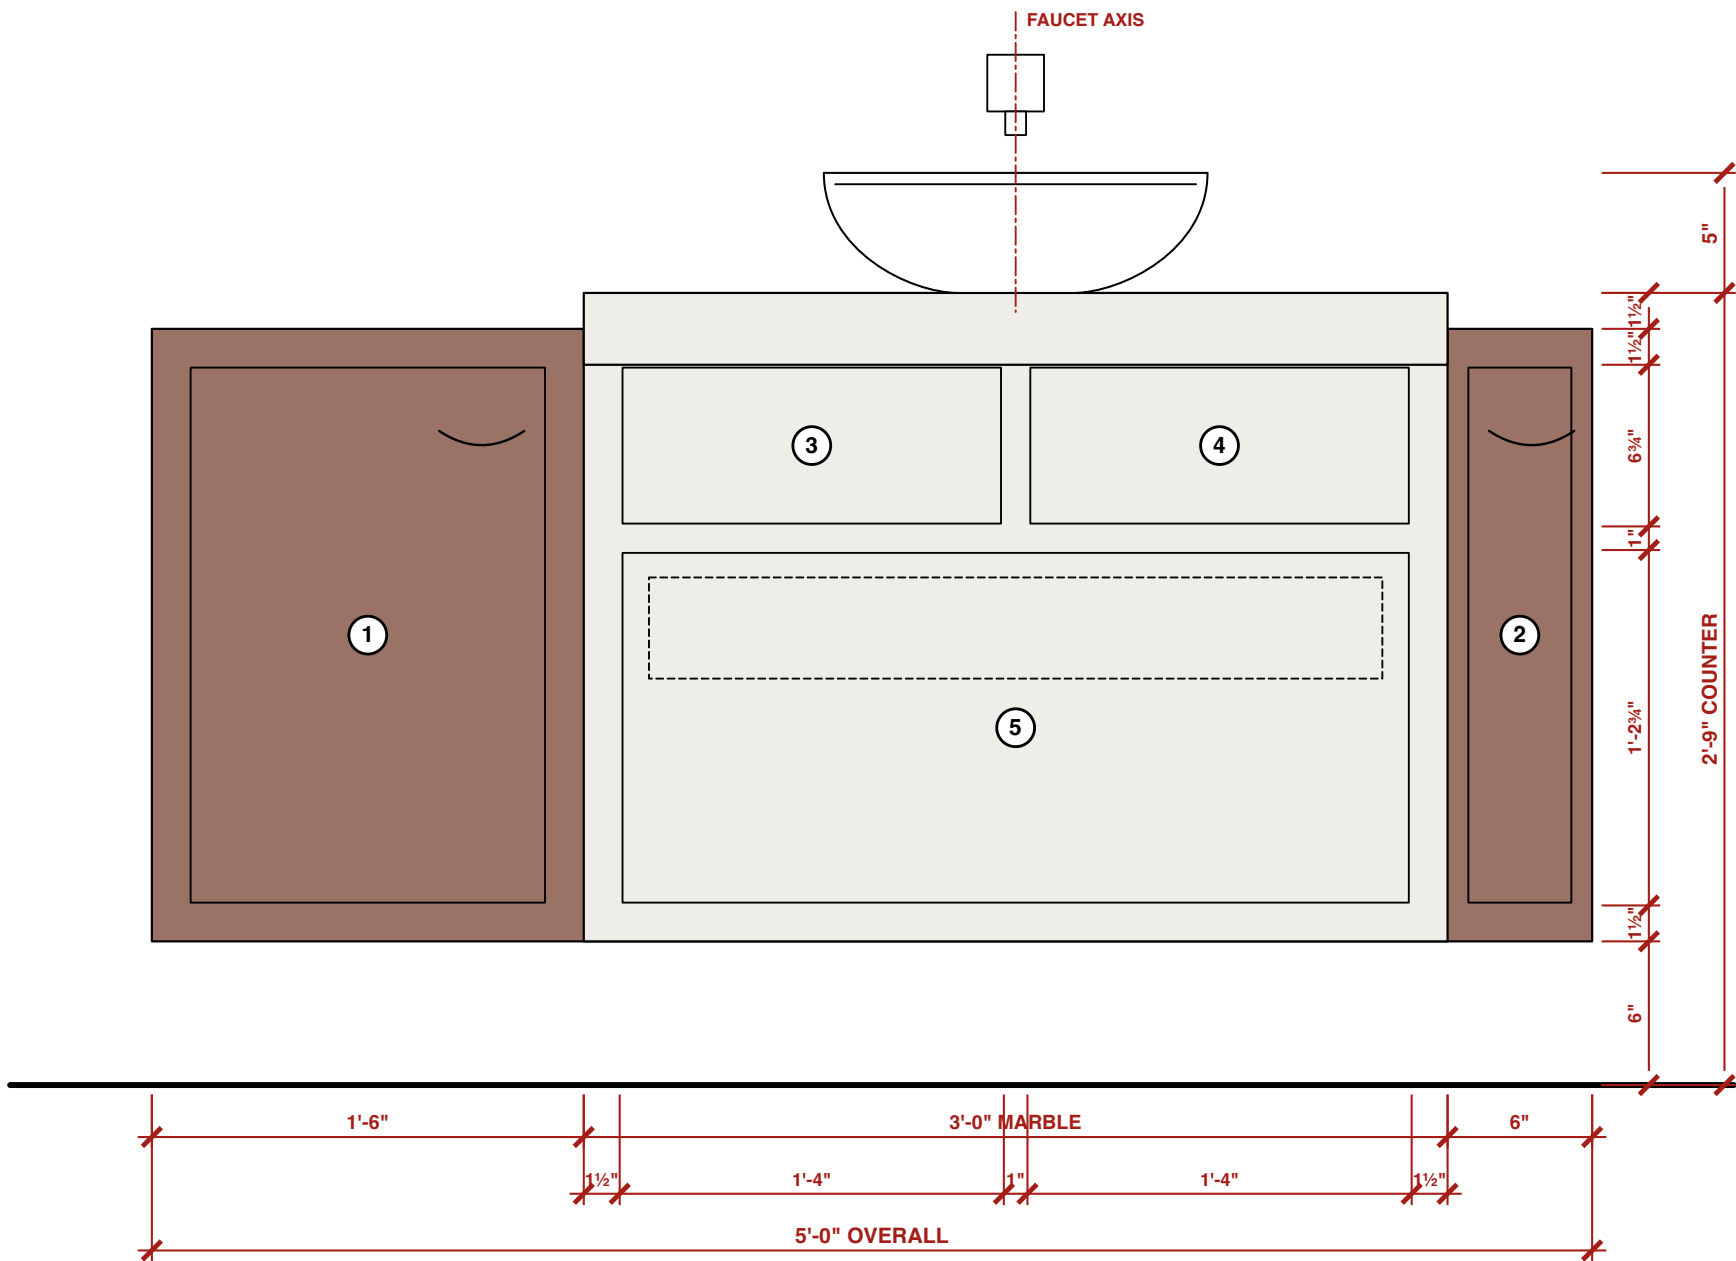

PROJECT
A Study in Teak — Vanity — Scheme C

SHEET
Front
Final · marble bank and top · dark red burl pull-outs · wall-hung, 6 in clear

SCALE
1:8 @ A3



DATE
08.10.2026

REV
5

DRAWING
AST-DR-021 · 2 of 10

SECTION A-A

SCALE 1:8 (1½" = 1'-0") @ A3 · ON THE FAUCET AXIS

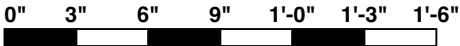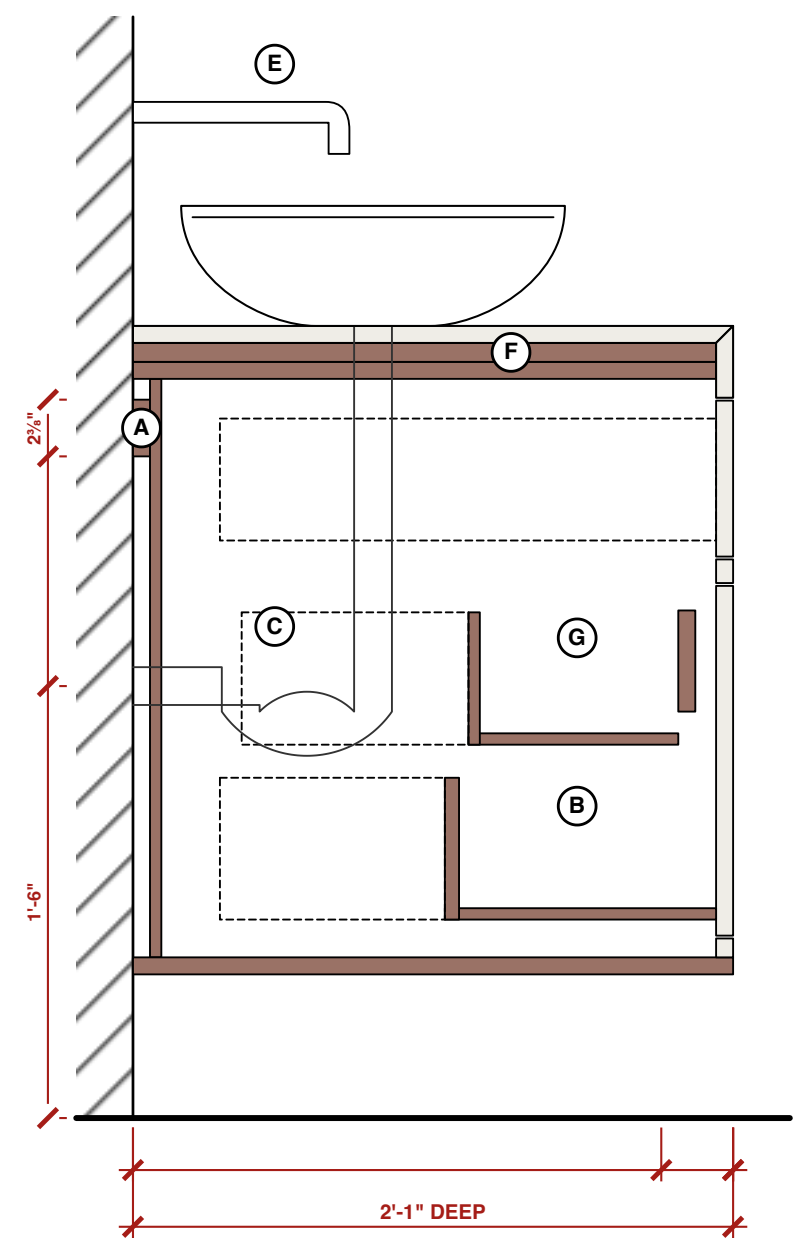

PROJECT
A Study in Teak — Vanity — Scheme C

SHEET
Section A-A
Final · marble bank and top · dark red burl pull-outs · wall-hung, 6 in clear

SCALE
1:8 @ A3



DATE
08.10.2026

REV
5

DRAWING
AST-DR-021 · 3 of 10

DETAIL 1 · THE MARBLE EDGE

SCALE 1:1 (FULL SIZE) @ A3 · SECTION · ONE MITRED CORNER, FRONTS FLUSH

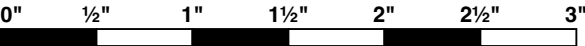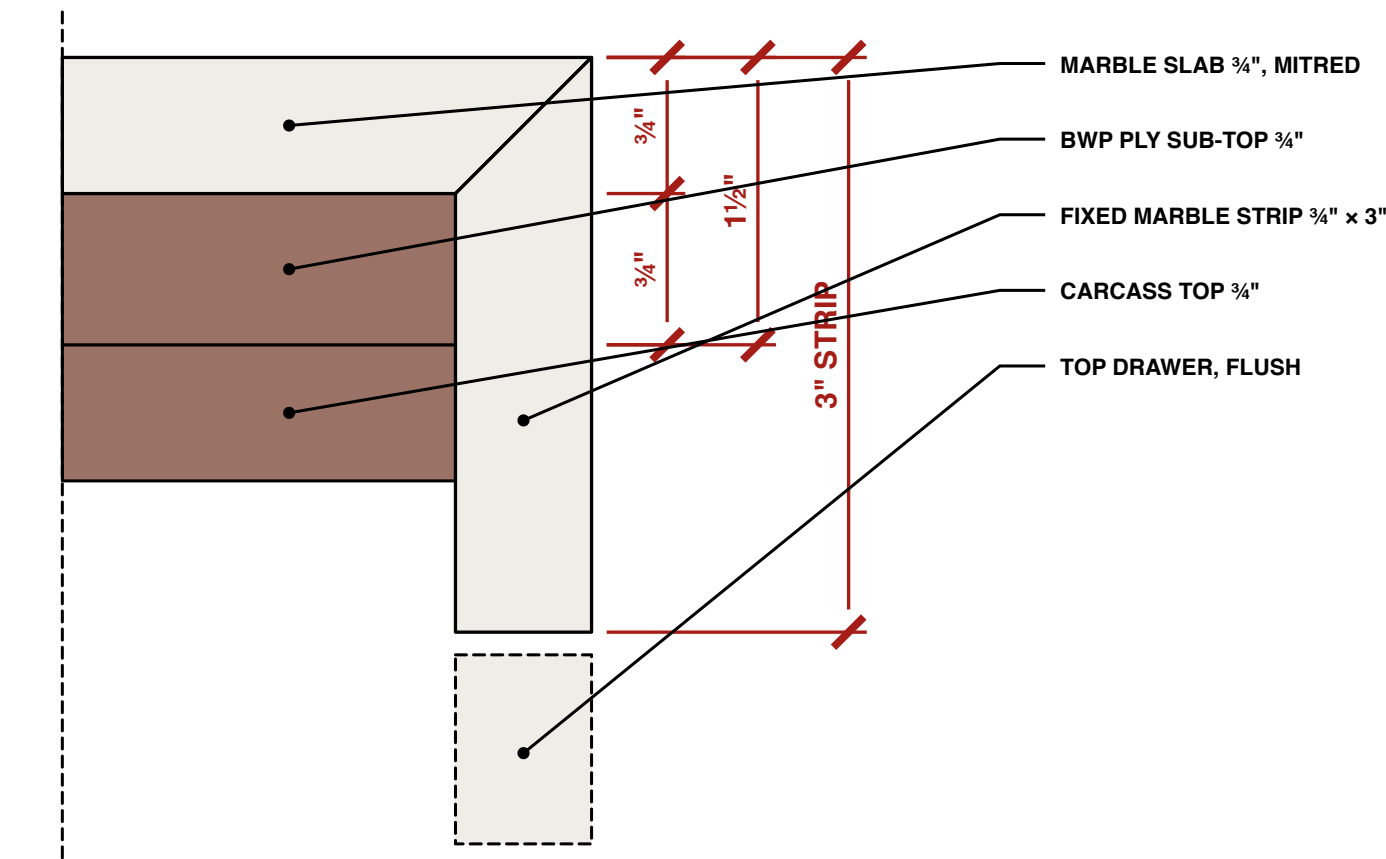

PROJECT
A Study in Teak — Vanity — Scheme C

SHEET
Detail 1 · the marble edge
Final · marble bank and top · dark red burl pull-outs · wall-hung, 6 in clear

SCALE
1:1 @ A3

DATE
08.10.2026

REV
5

DRAWING
AST-DR-021 · 4 of 10

FRONTS

SIZES ARE THE FRONT ITSELF · 1⁄8" GAP ALL ROUND

No.	WHAT	W × H	FT-IN
1	Pull-out cabinet, cup pull	1'-2¾" × 1'-10¼"	1'-2¾" × 1'-10¼"
2	Pull-out cabinet, cup pull	4¼" × 1'-10¼"	4¼" × 1'-10¼"
3	Top drawer, push-open · marble	1'-3¾" × 6½"	1'-3¾" × 6½"
4	Top drawer, push-open · marble	1'-3¾" × 6½"	1'-3¾" × 6½"
5	Big drawer, U-box, push-open · marble	2'-8¾" × 1'-2⅝"	2'-8¾" × 1'-2⅝"
5a	Inner drawer, finger scoop	2'-6½" × 4¼"	2'-6½" × 4¼"

PROJECT A Study in Teak — Vanity — Scheme C	SHEET Fronts Final · marble bank and top · dark red burl pull-outs · wall-hung, 6 in clear	SCALE NTS	DATE 08.10.2026	REV 5	DRAWING AST-DR-021 · 5 of 10
--	--	--------------	--------------------	----------	---------------------------------

MATERIALS



THE ROOM'S PALETTE — NOTHING NEW

Top	Beige-gold marble, the bathroom stone. ¾" slab on a ¾" BWP sub-top, mitred at the front edge into a fixed ¾" marble strip: one corner, fronts flush.
Bank	The same beige marble on the face frame and on every drawer front, bonded to BWP boxes. It stops 6 in off the floor, level with the ends: a drain below.
Ends	Two pull-out cabinets, 9292 burl veneer, polished dark and red (the owner's photo), gloss, edges sealed.
Hanging	¾" ply cleat 2'-3½"—2'-5⅞" and concealed steel brackets into the wall: the stone is heavy. Nothing on the floor.
Ledges	The two veneer tops: solid nosing, sealed.
Runners	Drawers: undermount, push-to-open. Pull-outs: heavy full-extension runners, cup pull.
Fittings	Chrome — already bought.

PROJECT A Study in Teak — Vanity — Scheme C	SHEET Materials Final · marble bank and top · dark red burl pull-outs · wall-hung, 6 in clear	SCALE NTS	DATE 08.10.2026	REV 5	DRAWING AST-DR-021 · 6 of 10
--	---	--------------	--------------------	----------	---------------------------------

PLAN



SCALE 1:5 @ A3 · FROM ABOVE · WALL AT THE TOP

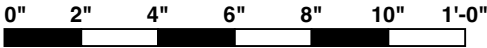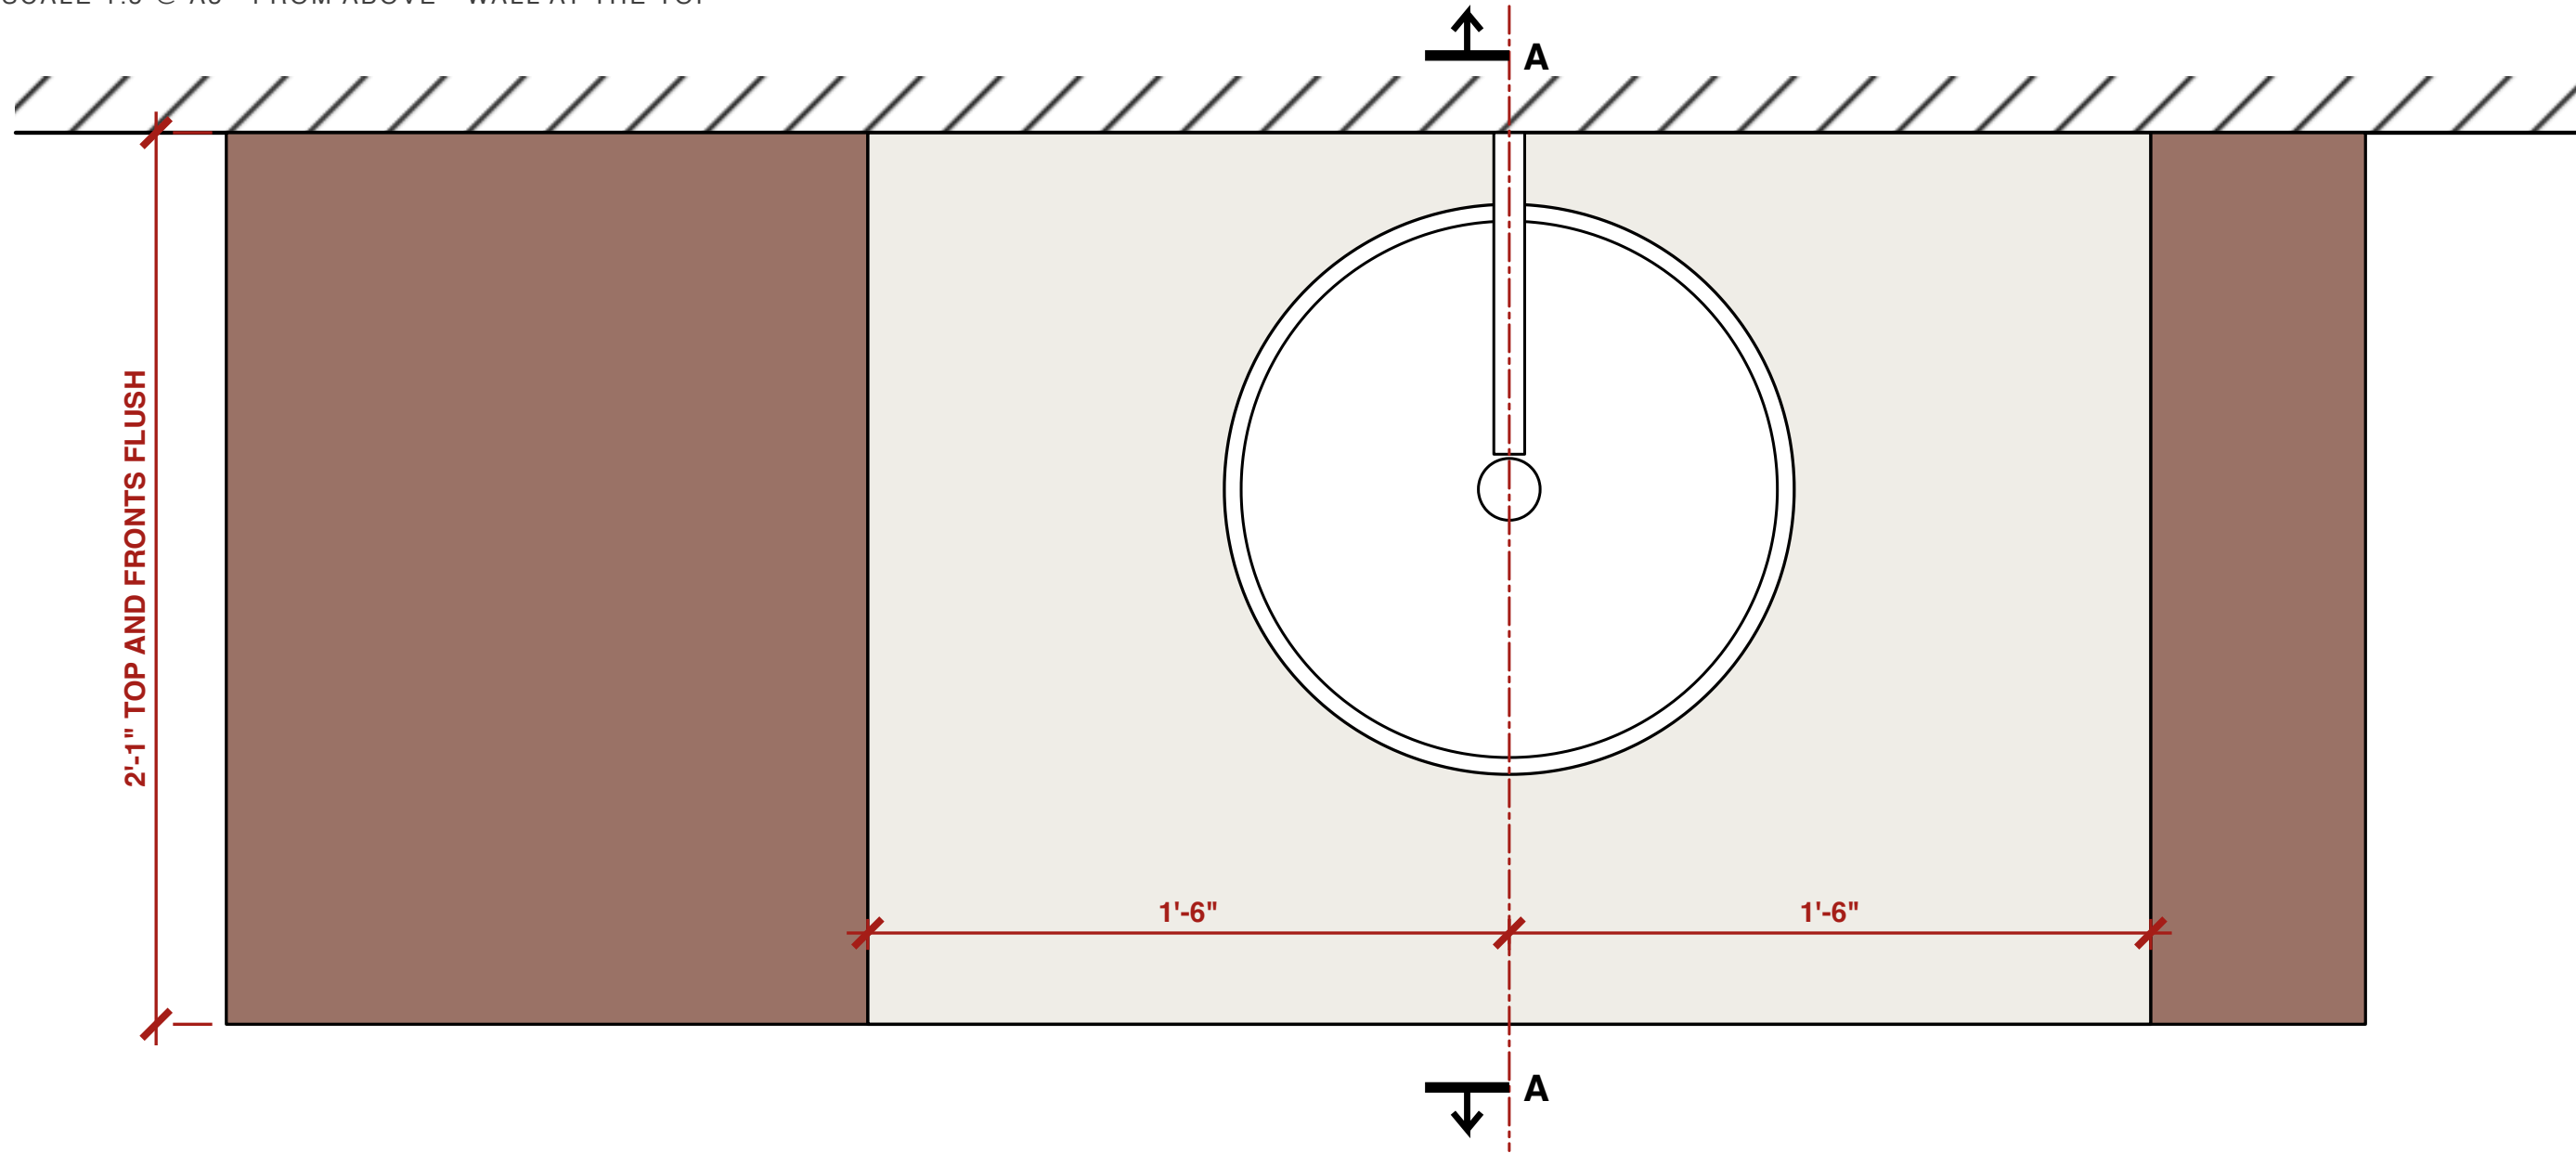

PROJECT A Study in Teak — Vanity — Scheme C	SHEET Plan Final · marble bank and top · dark red burl pull-outs · wall-hung, 6 in clear	SCALE 1:5 @ A3	DATE 08.10.2026	REV 5	DRAWING AST-DR-021 · 7 of 10
--	--	-------------------	--------------------	----------	---------------------------------

DETAIL 2 · THE BIG DRAWER

SCALE 1:5 @ A3 · PLAN · INNER DRAWER DASHED

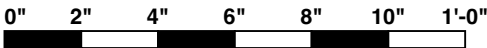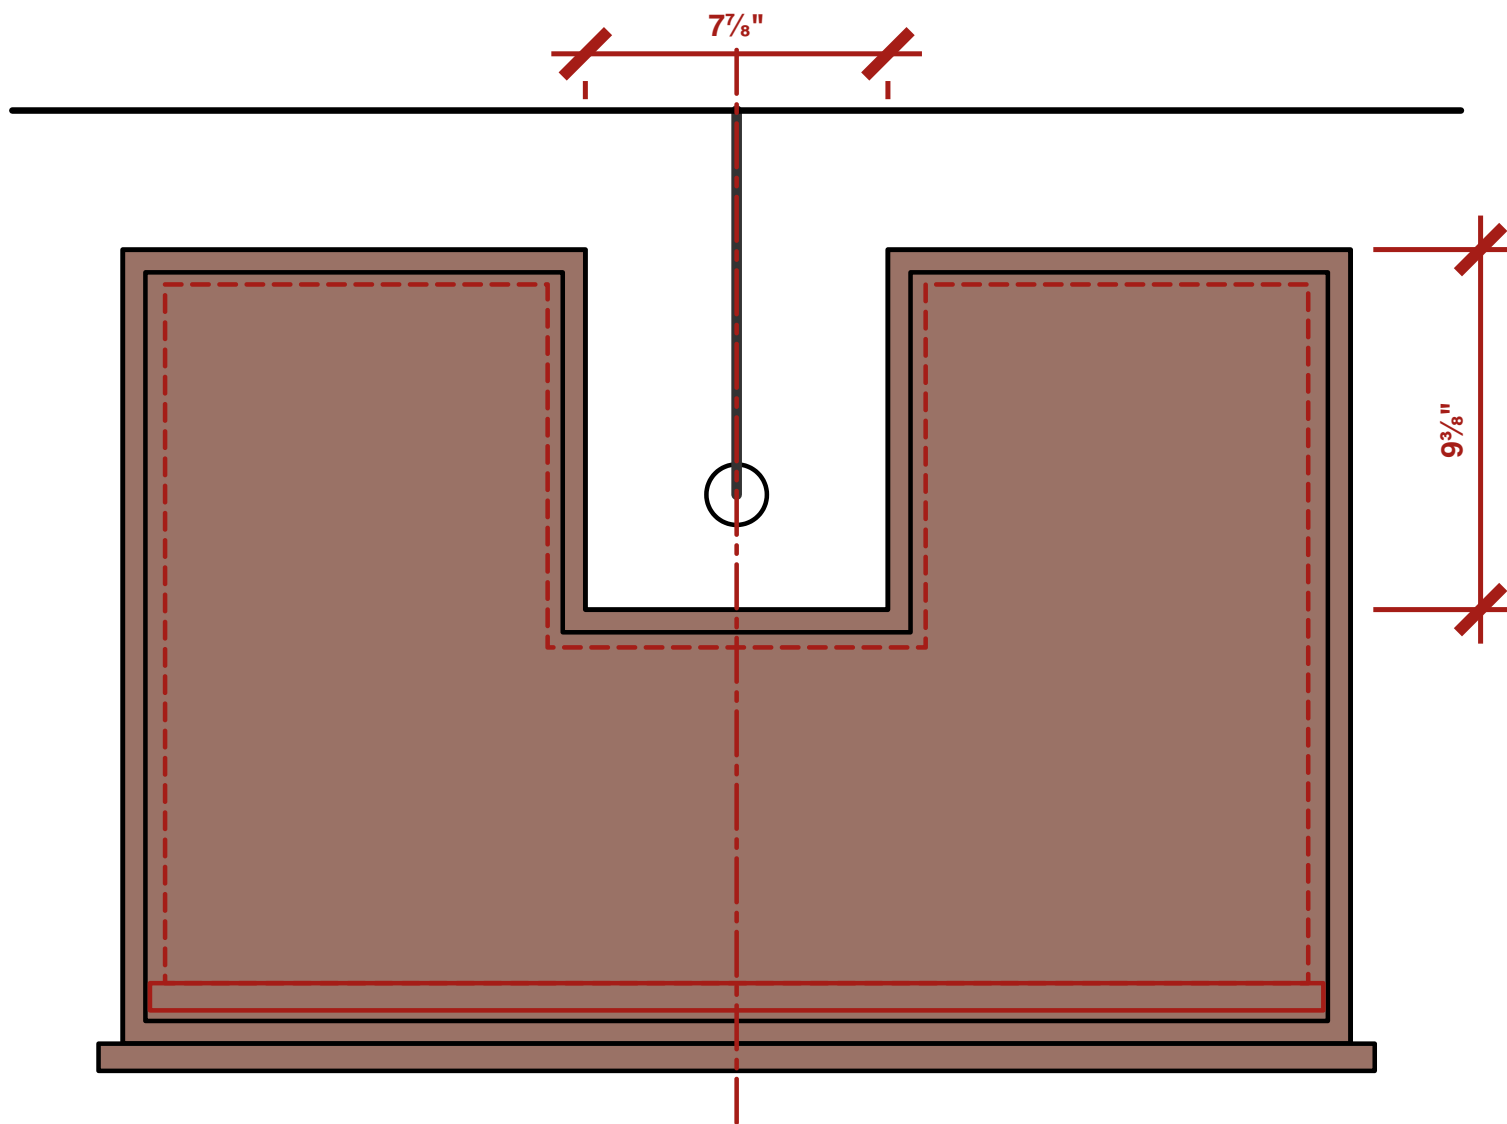

PROJECT A Study in Teak — Vanity — Scheme C	SHEET Detail 2 · the big drawer Final · marble bank and top · dark red burl pull-outs · wall-hung, 6 in clear	SCALE 1:5 @ A3	DATE 08.10.2026	REV 5	DRAWING AST-DR-021 · 8 of 10
--	---	-------------------	--------------------	----------	---------------------------------

SECTION KEY

- A

Hanging cleat
- B

Big drawer, U-box
- C

Waste Ø1⁵/₈" and P-trap
- E

Wall spout
- F

Ply sub-top
- G

Inner drawer

PROJECT A Study in Teak — Vanity — Scheme C	SHEET Section key Final · marble bank and top · dark red burl pull-outs · wall-hung, 6 in clear	SCALE NTS	DATE 08.10.2026	REV 5	DRAWING AST-DR-021 · 9 of 10
--	---	--------------	--------------------	----------	---------------------------------

NOTES

REVISION 5

Rev 5: the marble bank is back — face frame and fronts —

but stops 6 in off the floor, level with the ends: a drain

is on the floor below. The row hangs on the wall; no support.

Top drawers 6½ in; the big drawer 14½ in, a 4 in inner one.

OPEN — bowl Ø1'-4" × 5" and the spout are assumed.

OPEN — marble front thickness and its bond to the drawer

boxes, and the brackets' size: stone supplier to confirm.

Rev 3: top and front meet in one mitred corner, flush.

PROJECT	SHEET	SCALE	DATE	REV	DRAWING
A Study in Teak — Vanity — Scheme C	Notes Final · marble bank and top · dark red burl pull-outs · wall-hung, 6 in clear	NTS	08.10.2026	5	AST-DR-021 · 10 of 10