


WARDROBE INTERIORS — DOORS OFF

SEEN FROM THE ROOM - EVERY BAY 3'-0" WIDE, 9 FT HIGH, 2 FT 3 IN DEEP

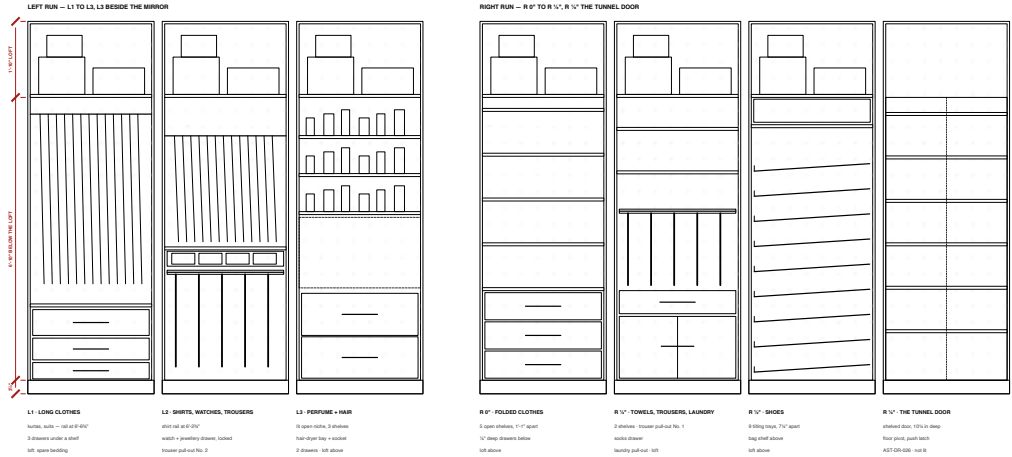

NOTES

REVISION 1


The layout the owner approved in chat (7 Oct), set out as built. Every bay has a left at 7 ft 0 in — one open 1 ft 10 in space, no middle shelf, a step stool reaches it. Ralls at 6'-0 1/2" (L1) and 6'-2 1/4" (L2). Two trouser pull-outs: No. 1 in R 1 1/2", No. 2 in L2. Shelves 1/2" thick, soft-close runners everywhere, no glass inside. Shoe trays in R 1 1/2" sit out as the owner's photo: 3 open trays for later. L2's open niche is fit for the perfume (about 1/2" to 1 1/4"). Doors, end bays and the tunnel door: AST-DR-025, -026 and the hidden-door drawings.

TO MEASURE ON SITE

The bay widths: 2'-1/4" each as drawn, set out to the real runs on site. The sockets: L2's hair-dryer bay and one LED driver per run, in the photo.

1 - THE LIT BACK

PLAN AT A BAY'S BACK CORNER - NOT THE TUNNEL DOOR

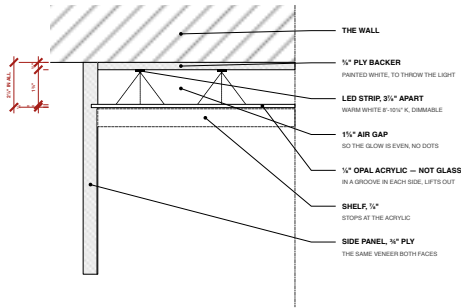

INSIDE (OWNER, 7 OCT)

The trade in a laminate the corner has chosen; its sample is still to come. Until then it is drawn and modified as the SAME VENEER as the doors, on every face inside — sides, shelves, drawer fronts, the left. The back of every bay glows: an opal acrylic panel fit from behind (detail 1) — the tunnel door 9 1/2" excepted. One drawer for both runs. LED strips also down the door edges, as before (not drawn).

A STUDY IN TEAK Particulars of the room	
WARDROBE INTERIORS Both runs, doors off - The lit back	
SCALE AS NOTED @ A3	DATE 07.10.2026
REV 1 — the approved layout; the same veneer inside, backlit backs	DWG AST-DR-048

PROJECT
A Study in Teak — Wardrobe Interiors

SHEET
General arrangement — the whole sheet
each view follows at its own scale, pages 2 to 6

SCALE
NTS



DATE
07.10.2026

REV
1

DRAWING
AST-DR-048 · 1 of 6

WARDROBE INTERIORS — DOORS OFF



SCALE 1:30 @ A4 · SEEN FROM THE ROOM · EVERY BAY 3'- $\frac{5}{8}$ " WIDE, 9 FT HIGH, 2 FT 3 IN DEEP

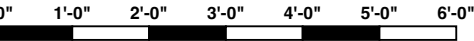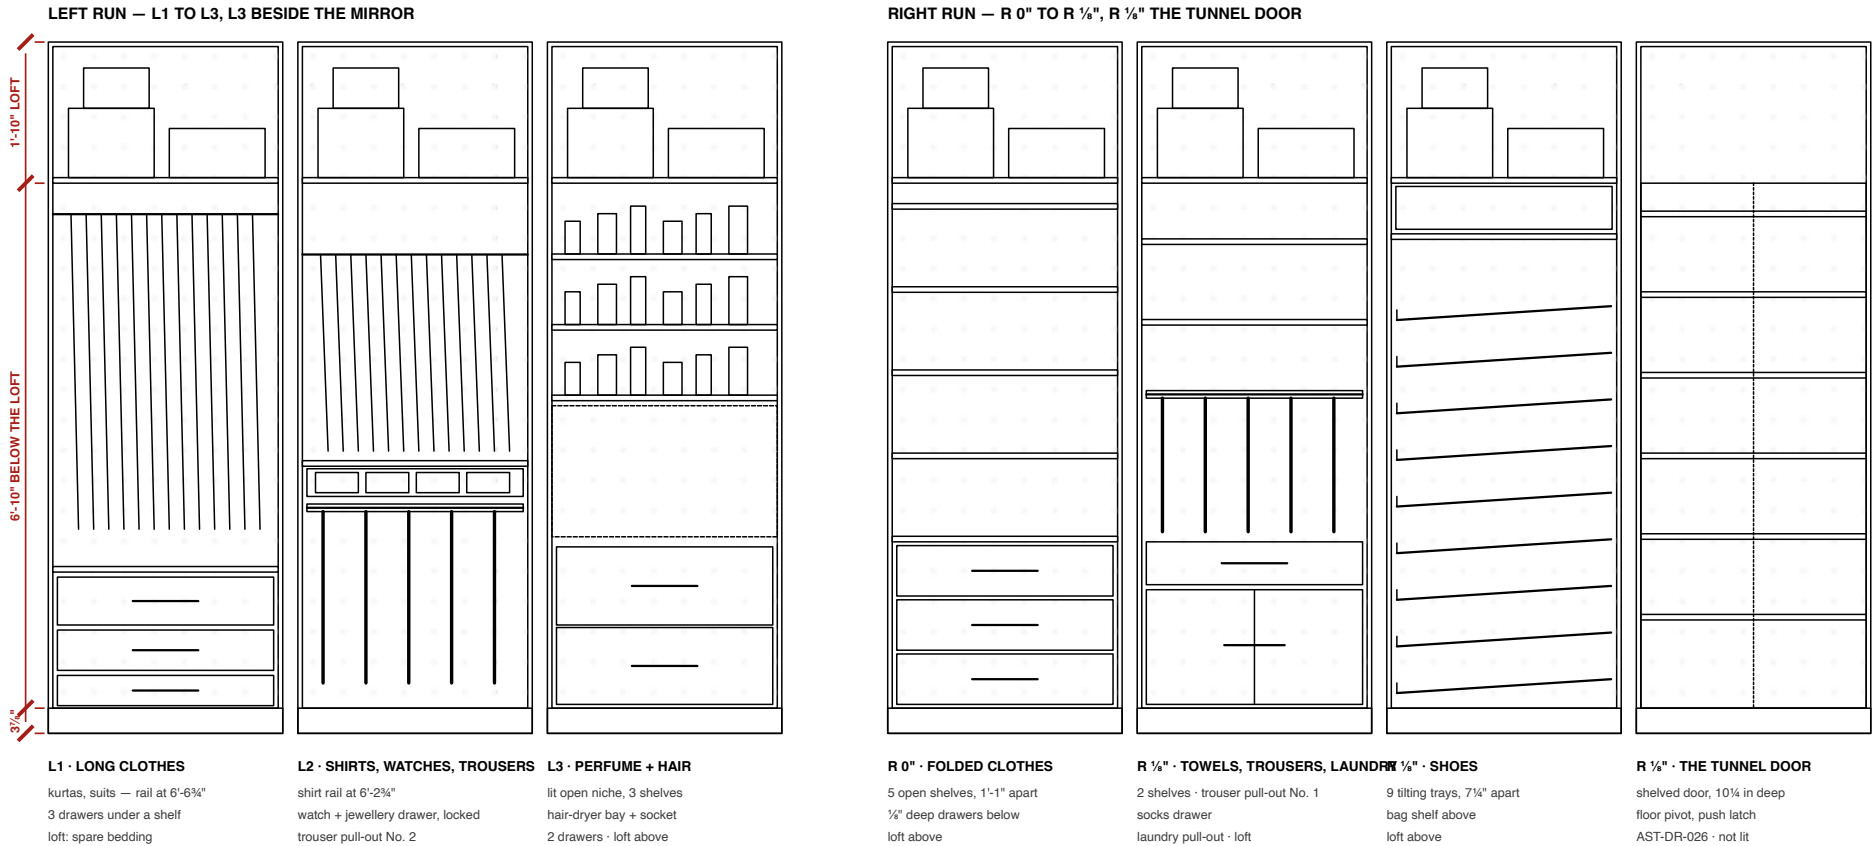

PROJECT	SHEET	SCALE	DATE	REV	DRAWING
A Study in Teak — Wardrobe Interiors	Wardrobe interiors — doors off Both runs, doors off · The lit back	1:30 @ A4	07.10.2026	1	AST-DR-048 · 2 of 6

1 · THE LIT BACK

SCALE 1:4 (3" = 1'-0") @ A4 · PLAN AT A BAY'S BACK CORNER · NOT THE TUNNEL DOOR

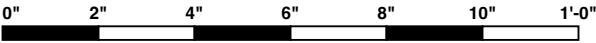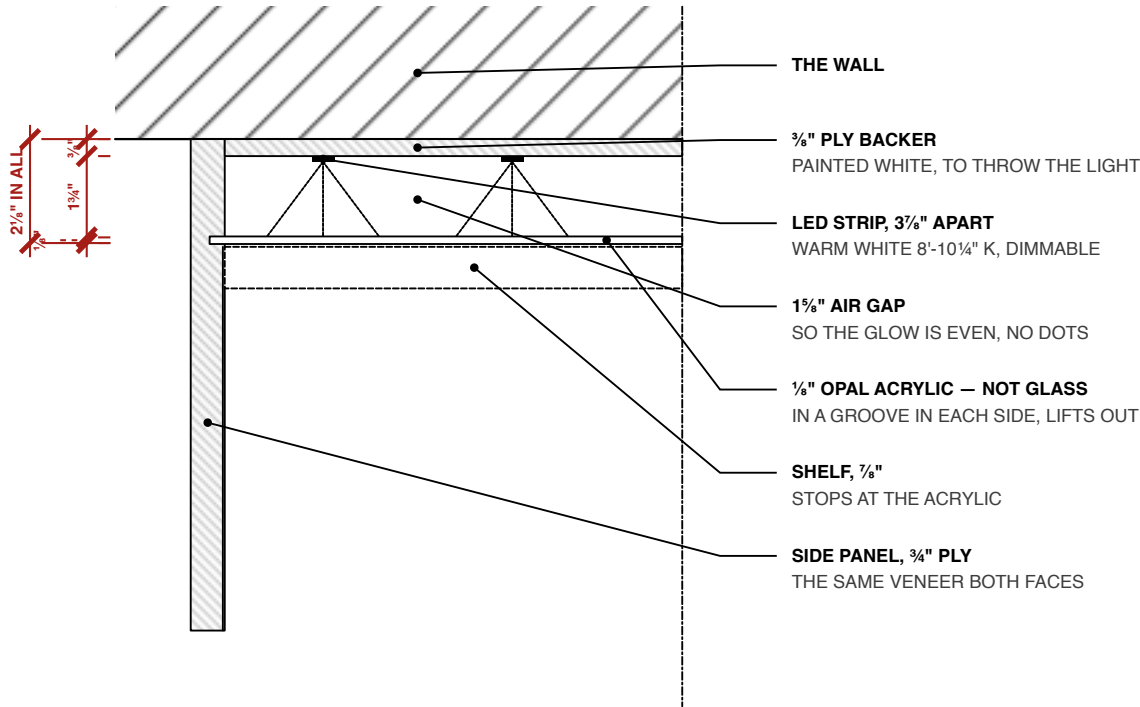

PROJECT
A Study in Teak — Wardrobe Interiors

SHEET
1 · the lit back
Both runs, doors off · The lit back

SCALE
1:4 @ A4

DATE
07.10.2026

REV
1

DRAWING
AST-DR-048 · 3 of 6

NOTES

REVISION 1

The layout the owner approved in chat (7 Oct), set out as built. Every bay has a loft at 7 ft 2 in — one open 1 ft 10 in space, no middle shelf; a step stool reaches it. Rails at 6'-6¾" (L1) and 6'-2¾" (L2). Two trouser pull-outs: No. 1 in R ⅛", No. 2 in L2. Shelves ⅞" thick, soft-close runners everywhere, no glass inside. Shoe trays in R ⅛" tilt out as the owner's photo; 5 spare trays for later. L3's open niche is lit for the perfumes (about ⅜" to ½").

Doors, end bays and the tunnel door: AST-DR-025, -026 and the hidden-door drawings.

PROJECT	SHEET	SCALE	DATE	REV	DRAWING
A Study in Teak — Wardrobe Interiors	Notes Both runs, doors off · The lit back	NTS	07.10.2026	1	AST-DR-048 · 4 of 6

TO MEASURE ON SITE

The bay widths: 3'-5/8" each as drawn, set out to the
real runs on site. The sockets: L3's hair-dryer bay
and one LED driver per run, in the plinth.

PROJECT A Study in Teak — Wardrobe Interiors	SHEET To measure on site Both runs, doors off · The lit back	SCALE NTS	DATE 07.10.2026	REV 1	DRAWING AST-DR-048 · 5 of 6
---	--	--------------	--------------------	----------	--------------------------------

INSIDE (OWNER, 7 OCT)

The inside is a laminate the owner has chosen; its sample is still to come. Until then it is drawn and modelled as the SAME VENEER as the doors, on every face inside — sides, shelves, drawer fronts, the loft.

The back of every bay glows: an opal acrylic panel lit from behind (detail 1) — the tunnel door R ⅛" excepted. One dimmer for both runs.

LED strips also down the door edges, as before (not drawn).

PROJECT A Study in Teak — Wardrobe Interiors	SHEET Inside (owner, 7 oct) Both runs, doors off · The lit back	SCALE NTS	DATE 07.10.2026	REV 1	DRAWING AST-DR-048 · 6 of 6
---	---	--------------	--------------------	----------	--------------------------------