


WARDROBE INTERIORS — DOORS OFF

SEEN FROM THE ROOM · EVERY BAY 3'-½" WIDE, 9 FT HIGH, 2 FT 3 IN DEEP

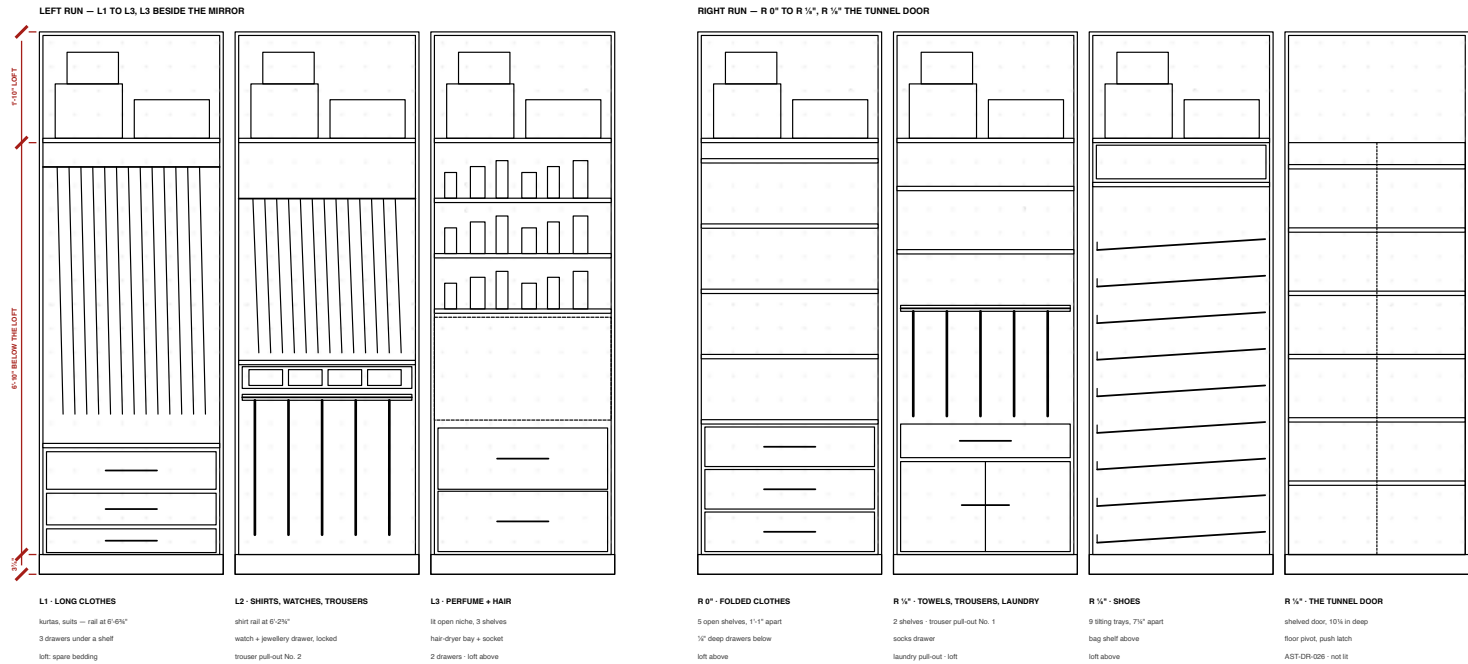

NOTES

REVISION 1


The layout the owner approved in chat (7 Oct), set out as built. Every bay has a loft at 7 ft 2 in — one open 1 ft 10 in space, no middle shelf; a step stool reaches it. Rails at 6'-6½" (L1) and 6'-2½" (L2). Two trouser pull-outs: No. 1 in R ½", No. 2 in L2. Shelves ½" thick, soft-close runners everywhere, no glass inside. Shoe trays in R ½" tilt out as the owner's photo; 5 spare trays for later. L3's open niche is lit for the perfumes (about ¼" to ½"). Doors, end bays and the tunnel door: AST-DR-025, -026 and the hidden-door drawings.

TO MEASURE ON SITE

The bay widths: 3'-½" each as drawn, set out to the real runs on site. The sockets: L3's hair-dryer bay and one LED driver per run, in the plinth.

1 · THE LIT BACK

PLAN AT A BAY'S BACK CORNER · NOT THE TUNNEL DOOR

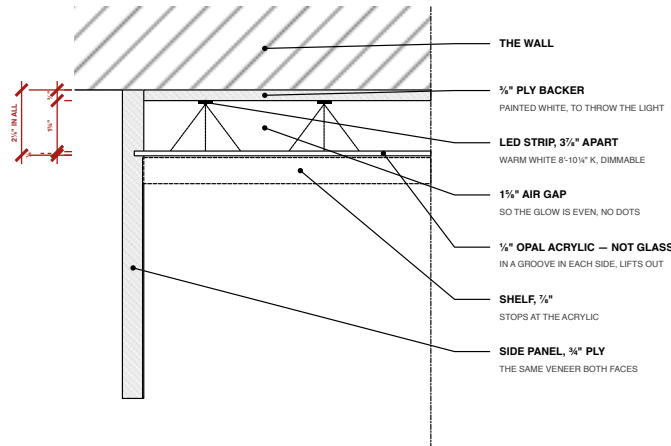

INSIDE (OWNER, 7 OCT)

The inside is a laminate the owner has chosen; its sample is still to come. Until then it is drawn and modelled as the SAME VENEER as the doors, on every face inside — sides, shelves, drawer fronts, the loft.

The back of every bay glows: an opal acrylic panel lit from behind (detail 1) — the tunnel door R ½" excepted. One dimmer for both runs.

LED strips also down the door edges, as before (not drawn).

A STUDY IN TEAK	
Particulars of the room	
WARDROBE INTERIORS	
Both runs, doors off · The lit back	
SCALE AS NOTED @ A3	DATE 07.10.2026
REV 1 — the approved layout; the same veneer inside, backlit backs	DWG AST-DR-048

PROJECT
A Study in Teak — Wardrobe Interiors

SHEET
General arrangement — the whole sheet
each view follows at its own scale, pages 2 to 6

SCALE
NTS


DATE
07.10.2026

REV
1

DRAWING
AST-DR-048 · 1 of 6

WARDROBE INTERIORS — DOORS OFF

SCALE 1:20 @ A3 · SEEN FROM THE ROOM · EVERY BAY 3'-5/8" WIDE, 9 FT HIGH, 2 FT 3 IN DEEP

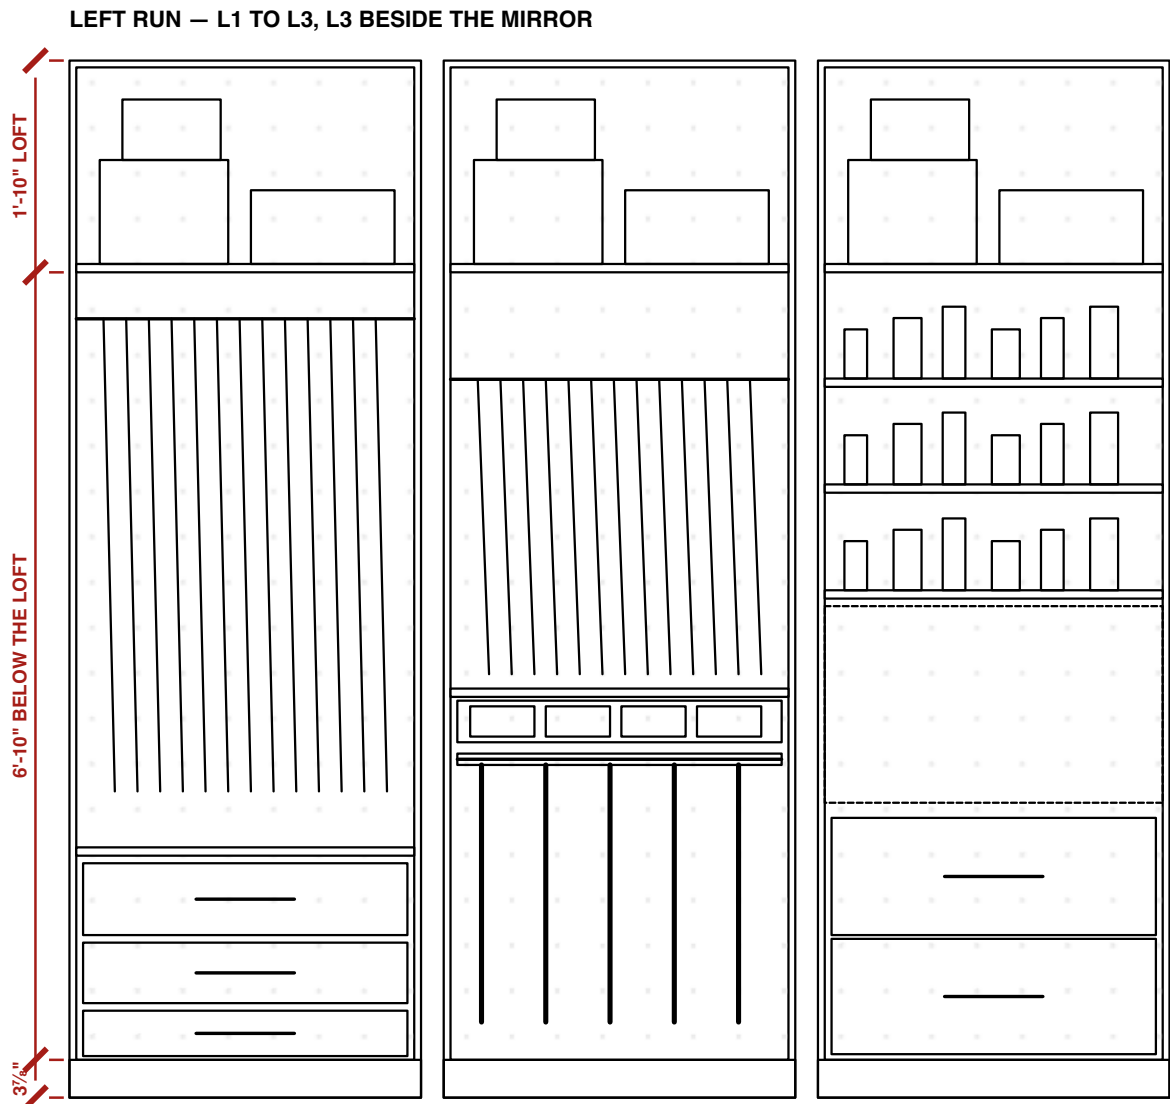

L1 · LONG CLOTHES


kurtas, suits — rail at 6'-6 3/4"
3 drawers under a shelf
loft: spare bedding

L2 · SHIRTS, WATCHES, TROUSERS

shirt rail at 6'-2 3/4"
watch + jewellery drawer, locked
trouser pull-out No. 2

L3 · PERFUME + HAIR

lit open niche, 3 shelves
hair-dryer bay + socket
2 drawers · loft above

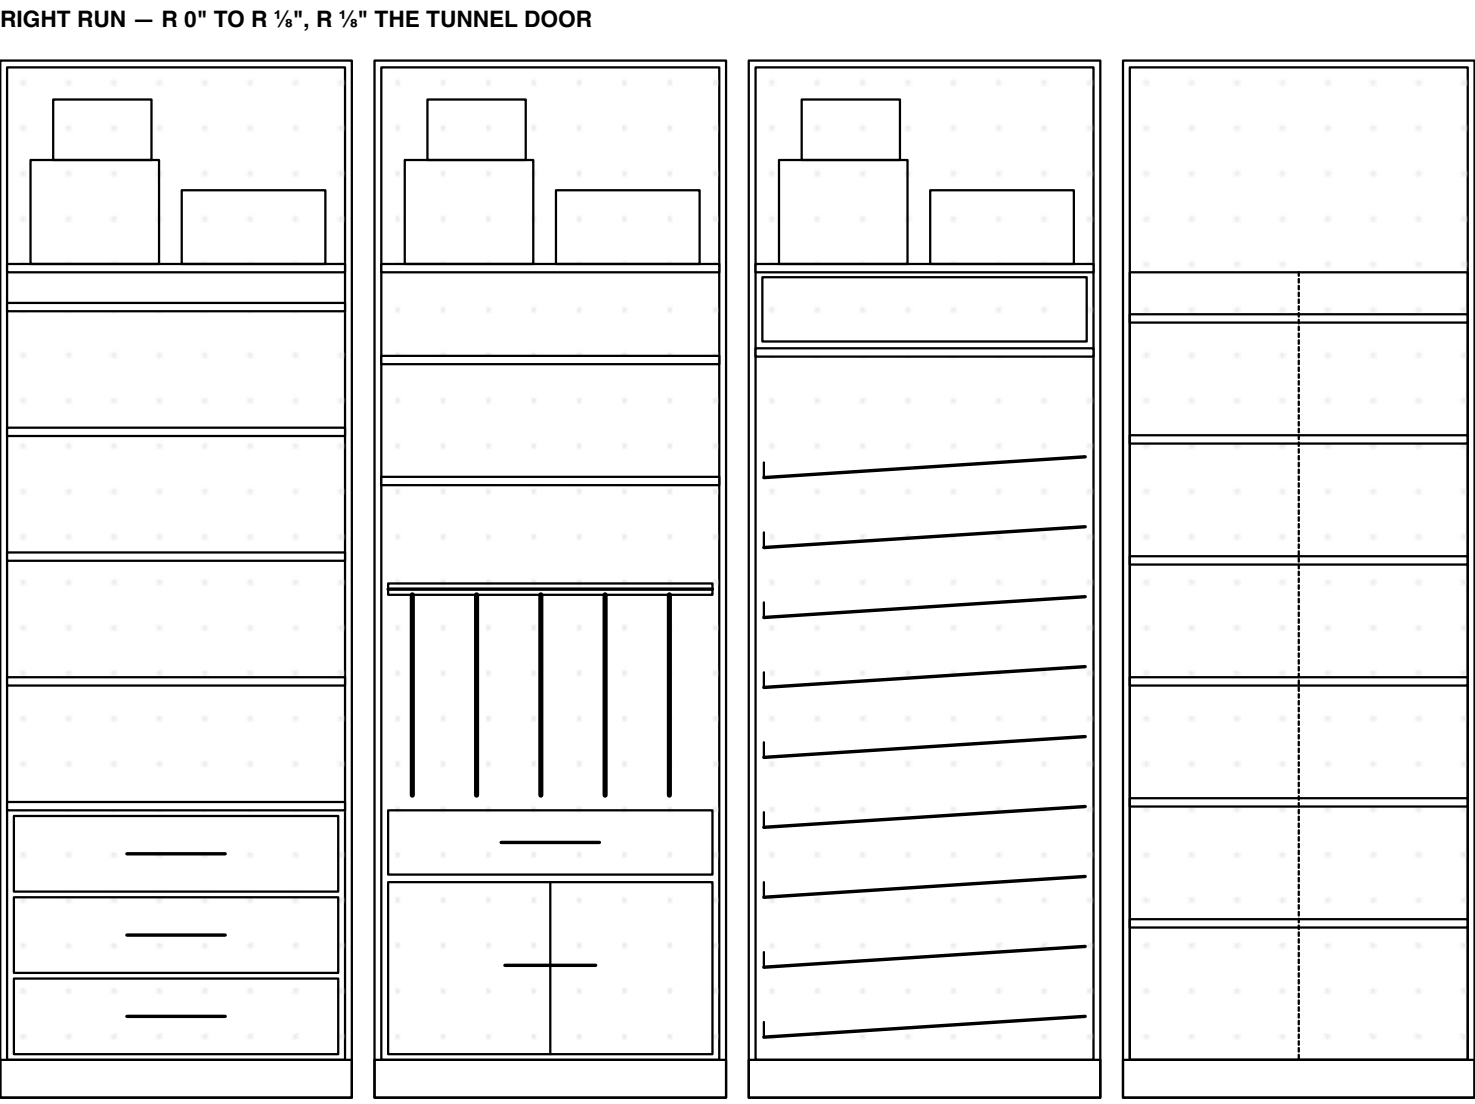

R 0" · FOLDED CLOTHES

5 open shelves, 1'-1" apart
1/8" deep drawers below
loft above

R 1/8" · TOWELS, TROUSERS, LAUNDRY


2 shelves · trouser pull-out No. 1
socks drawer
laundry pull-out · loft

R 1/8" · SHOES

9 tilting trays, 7 1/4" apart
bag shelf above
loft above

R 1/8" · THE TUNNEL DOOR

shelved door, 10 1/4 in deep
floor pivot, push latch
AST-DR-026 · not lit

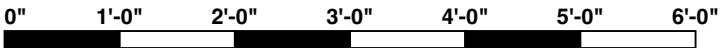

PROJECT
A Study in Teak — Wardrobe Interiors

SHEET
Wardrobe interiors — doors off
Both runs, doors off · The lit back

SCALE
1:20 @ A3



DATE
07.10.2026

REV
1

DRAWING
AST-DR-048 · 2 of 6

1 · THE LIT BACK

SCALE 1:3 (4" = 1'-0") @ A3 · PLAN AT A BAY'S BACK CORNER · NOT THE TUNNEL DOOR

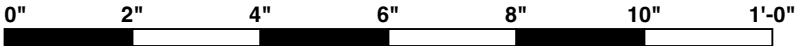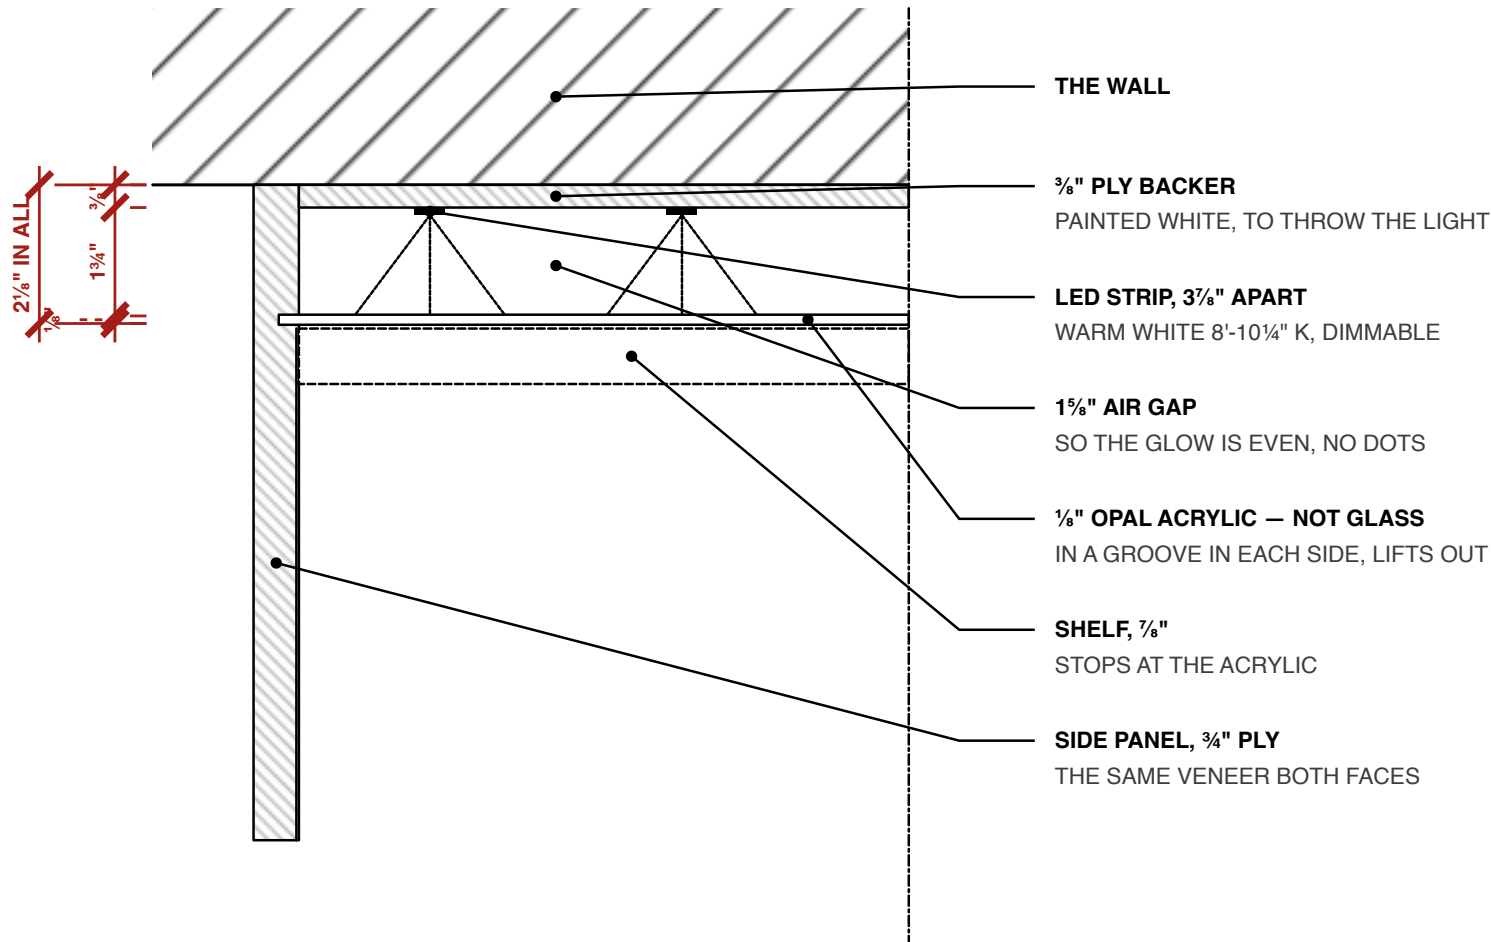

PROJECT
A Study in Teak — Wardrobe Interiors

SHEET
1 · the lit back
Both runs, doors off · The lit back

SCALE
1:3 @ A3

DATE
07.10.2026

REV
1

DRAWING
AST-DR-048 · 3 of 6

NOTES

REVISION 1

The layout the owner approved in chat (7 Oct), set out as built. Every bay has a loft at 7 ft 2 in — one open 1 ft 10 in space, no middle shelf; a step stool reaches it. Rails at 6'-6¾" (L1) and 6'-2¾" (L2). Two trouser pull-outs: No. 1 in R ⅛", No. 2 in L2. Shelves ⅞" thick, soft-close runners everywhere, no glass inside. Shoe trays in R ⅛" tilt out as the owner's photo; 5 spare trays for later. L3's open niche is lit for the perfumes (about ⅜" to ½").

Doors, end bays and the tunnel door: AST-DR-025, -026 and the hidden-door drawings.

PROJECT A Study in Teak — Wardrobe Interiors	SHEET Notes Both runs, doors off · The lit back	SCALE NTS	DATE 07.10.2026	REV 1	DRAWING AST-DR-048 · 4 of 6
---	---	--------------	--------------------	----------	--------------------------------

TO MEASURE ON SITE

The bay widths: 3'-⁵/₈" each as drawn, set out to the real runs on site. The sockets: L3's hair-dryer bay and one LED driver per run, in the plinth.

PROJECT A Study in Teak — Wardrobe Interiors	SHEET To measure on site Both runs, doors off · The lit back	SCALE NTS	DATE 07.10.2026	REV 1	DRAWING AST-DR-048 · 5 of 6
---	--	--------------	--------------------	----------	--------------------------------

INSIDE (OWNER, 7 OCT)

The inside is a laminate the owner has chosen; its sample is still to come. Until then it is drawn and modelled as the SAME VENEER as the doors, on every face inside — sides, shelves, drawer fronts, the loft.

The back of every bay glows: an opal acrylic panel lit from behind (detail 1) — the tunnel door R 1⁄8" excepted. One dimmer for both runs.

LED strips also down the door edges, as before (not drawn).

PROJECT A Study in Teak — Wardrobe Interiors	SHEET Inside (owner, 7 oct) Both runs, doors off · The lit back	SCALE NTS	DATE 07.10.2026	REV 1	DRAWING AST-DR-048 · 6 of 6
---	---	--------------	--------------------	----------	--------------------------------