


DRESSING ROOM — THE WARDROBES

DEVELOPED ELEVATION · THE THREE WALLS UNFOLDED, LEFT TO RIGHT AS YOU WALK IN

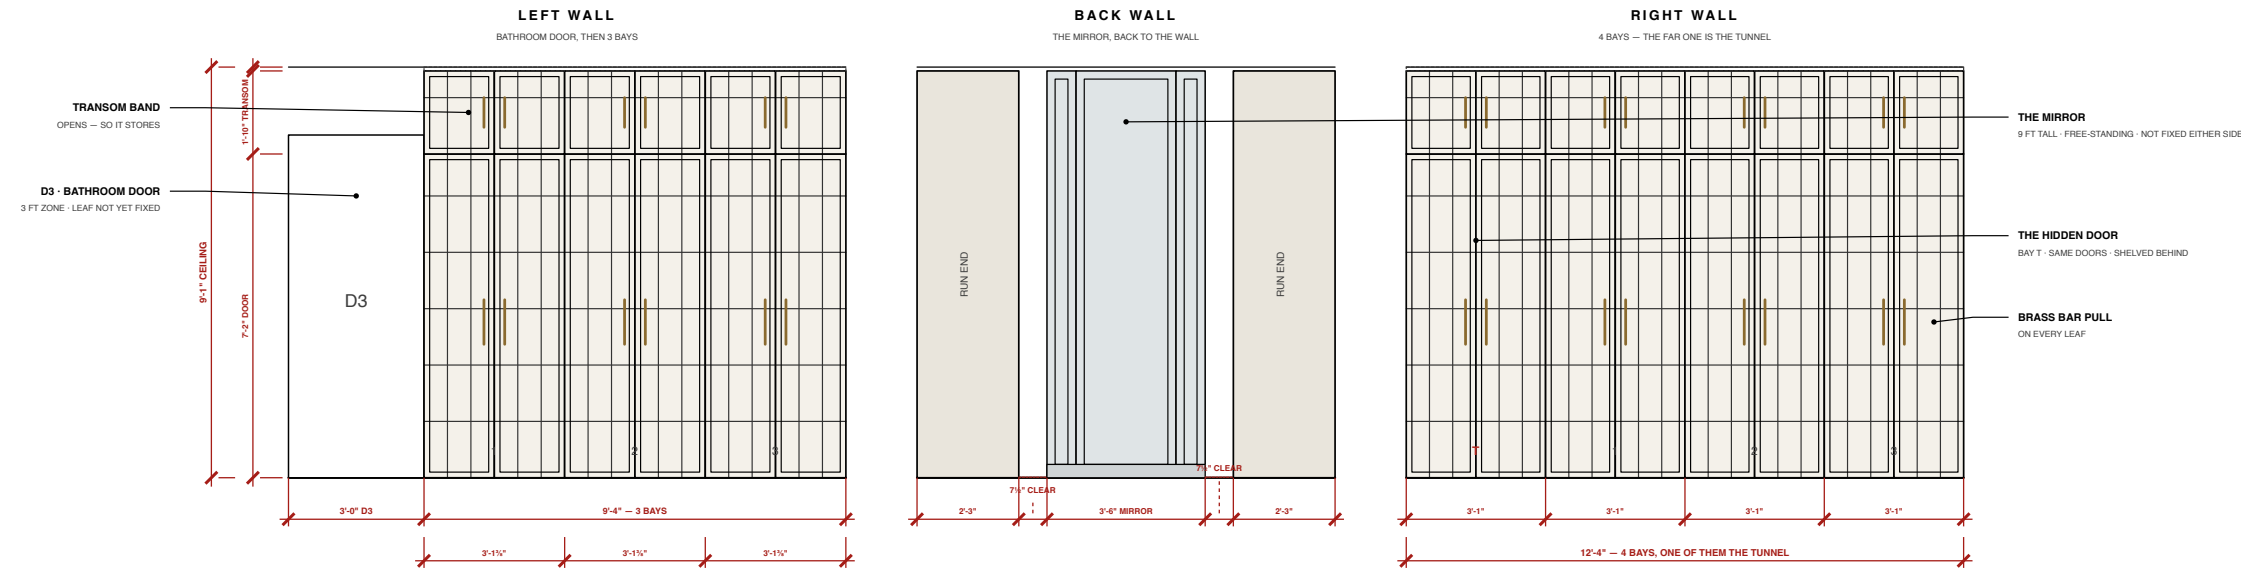

WHAT THAT COMES TO

	BAYS	DOORS BELOW	DOORS ABOVE	BAY WIDTH
LEFT WALL	3	6	6	3'-1 1/4"
RIGHT WALL	4	8	8	3'-1"
— of which tunnel	1	2	—	the far bay, right
TOTAL	7	14	14	14" leaves in all

NOTES

REVISION 1

Depth 2 ft 3 in, as instructed. On the right that is what lets the run reach the bedroom wall: the door frame stands 2 ft 4 in off that corner, so the end of the run clears it by 1 in.

Bays are the wall divided equally, so nothing is left over and there are no filler strips: the right wall is 12 ft 4 in over 4 bays, the left is 9 ft 4 in over 3. Both come out at about 3 ft 1 in — an inch over the 3 ft you asked for, which is what makes them land exactly.

Each bay is a pair of doors with a pair of transom lights over, all glazed and all opening — so the transom is storage, not just a band of glass. 7 bays, 1/2" cupboards, 1 1/4" leaves.

Doors as the Wardrobes brief: blackened steel T-section, 1 1/2" face, white textured glass in linear lead came, lit from inside, brass bar pulls, transom bar 1'-10" down from the top.

SETTLED — the mirror is a trifold, 3 ft 6 in across with its wings at 45°, free-standing and fixed to neither run. Centred in the 4 ft 9 in gap it leaves 7 1/2 in of floor either side, and it is 9 ft tall — level with the top of the wardrobes. That narrow gap is why the two end bays cannot hinge open in the ordinary way — see AST-DR-026 for the fold-slide doors that solve it.

OPEN — D3, the bathroom door. 3 ft of wall is left for it, but the leaf is still not fixed. It is drawn as an opening only.

OPEN — the tunnel bay reads as one more cupboard, but it is a door onto a passage, so the transom over it cannot be storage in the ordinary way. Decide whether it is a dummy.

OPEN — 4 ft 9 in is what you are left standing in once both runs are built. Open one 1 ft 6 in leaf and there is still 3 ft 3 in. Workable, not generous — worth feeling on site first.

A STUDY IN TEAK Particulars of the room	
THE WARDROBES Dressing room · developed elevation	
SCALE 1:40 @ A3	DATE 25.09.2026
REV 1 — first setting out of the bays, off the owner's 2 ft 3 in depth and 3 ft bay	DWG AST-DR-025

PROJECT
A Study in Teak — The Wardrobes

SHEET
General arrangement — the whole sheet
each view follows at its own scale, pages 2 to 2

SCALE
NTS

DATE
25.09.2026

REV
1

DRAWING
AST-DR-025 · 1 of 2

NOTES

REVISION 1

Depth 2 ft 3 in, as instructed. On the right that is what lets the run reach the bedroom wall: the door frame stands 2 ft 4 in off that corner, so the end of the run clears it by 1 in.

Bays are the wall divided equally, so nothing is left over and there are no filler strips: the right wall is 12 ft 4 in over 4 bays, the left is 9 ft 4 in over 3. Both come out at about 3 ft 1 in — an inch over the 3 ft you asked for, which is what makes them land exactly.

Each bay is a pair of doors with a pair of transom lights over, all glazed and all opening — so the transom is storage, not just a band of glass. 7 bays, ½" cupboards, 1⅙" leaves.

Doors as the Wardrobes brief: blackened steel T-section, 1½" face, white textured glass in linear lead came, lit from inside, brass bar pulls, transom bar 1'-10" down from the top.

SETTLED — the mirror is a trifold, 3 ft 6 in across with its wings at 45°, free-standing to neither run. Centred in the 4 ft 9 in gap it leaves 7½ in of floor either side, at level with the top of the wardrobes. That narrow gap is why the two end bays cannot be in the ordinary way — see AST-DR-026 for the fold-slide doors that solve it.

OPEN — D3, the bathroom door. 3 ft of wall is left for it, but the leaf is still not drawn as an opening only.

OPEN — the tunnel bay reads as one more cupboard, but it is a door onto a passage. A transom over it cannot be storage in the ordinary way. Decide whether it is a door or not.

OPEN — 4 ft 9 in is what you are left standing in once both runs are built. Open the leaf and there is still 3 ft 3 in. Workable, not generous — worth feeling on site if possible.

PROJECT
A Study in Teak — The Wardrobes

SHEET
Notes
Dressing room · developed elevation

SCALE
NTS

DATE
25.09.2026

REV
1

DRAWING
AST-DR-025 · 2 of 2