


ELEVATION — LEFT WALL

SEEN FROM THE ROOM · STUDY CORNER LEFT, BED CORNER RIGHT

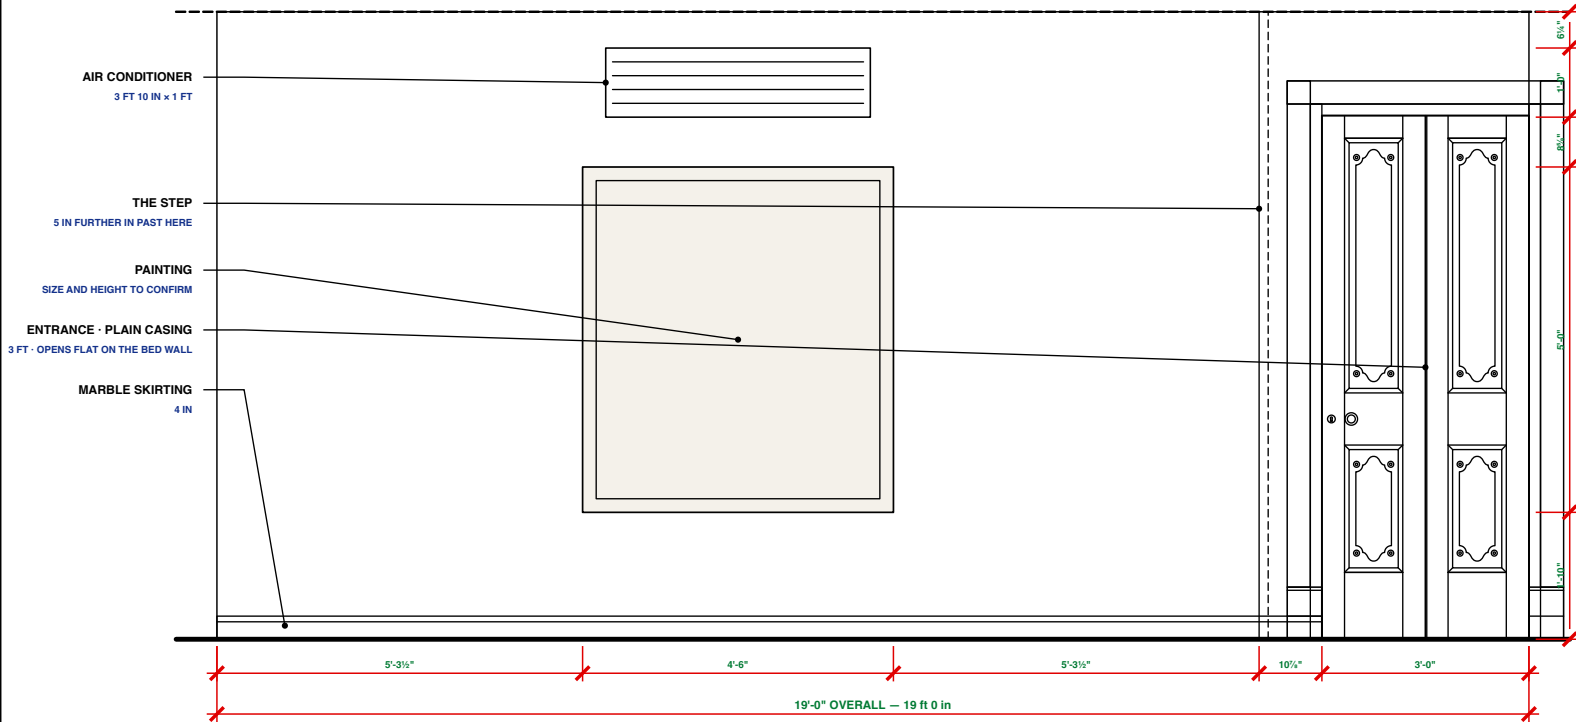

PLAN

CUT AT 3'-11 1/4" · ROOM BELOW THE WALL



NOTES

REVISION 5

This wall stays plain. Paint, the marble skirting, one painting and the air conditioner over it — nothing is built into it and nothing is panelled. It is the quiet side of the room, opposite the panelled right wall, and it is the wall that carries the splay and the step, so anything fitted to it would have to be scribed twice. The painting is centred on the 15 ft 1 1/4 in of wall before the step, the only uninterrupted run. Centre line 7 ft 6 1/4 in from the study corner, 1 ft 10 in off the floor.

OPEN — the painting is drawn 4 ft 6 in x 5 ft 0 in, centred at 4 ft 4 in. Still assumed. Send the real size and it is a one-line change. Sized to the wall it has: 8 1/4 in clear under the air conditioner, and 8 in wider than the unit, so the AC sits within its width. The air conditioner is 3 ft 10 in x 1 ft 0 in — MEASURED. Its depth (7 1/4 in) and its height off the ceiling (6 1/4 in) are still assumed. The AC needs a power point and a drain run before the wall is painted — decide the side the pipework leaves on. The entrance takes the PLAIN casing: same 2 in lining and 4 in moulding as every opening, running straight across the head and stopping. The carved head on AST-DR-011 is the DRESSING door's alone. OPEN — the profile of that 4 in plain band is not settled. Drawn flat.

A STUDY IN TEAK

Particulars of the room

LEFT WALL

Elevation · Plan · The plain wall

SCALE

1:30 @ A3

DATE

23.09.2026

REV


5 — the painting widened to 4 ft 6 in

DWG

AST-DR-014


ELEVATION — LEFT WALL

SEEN FROM THE ROOM · STUDY CORNER LEFT, BED CORNER RIGHT

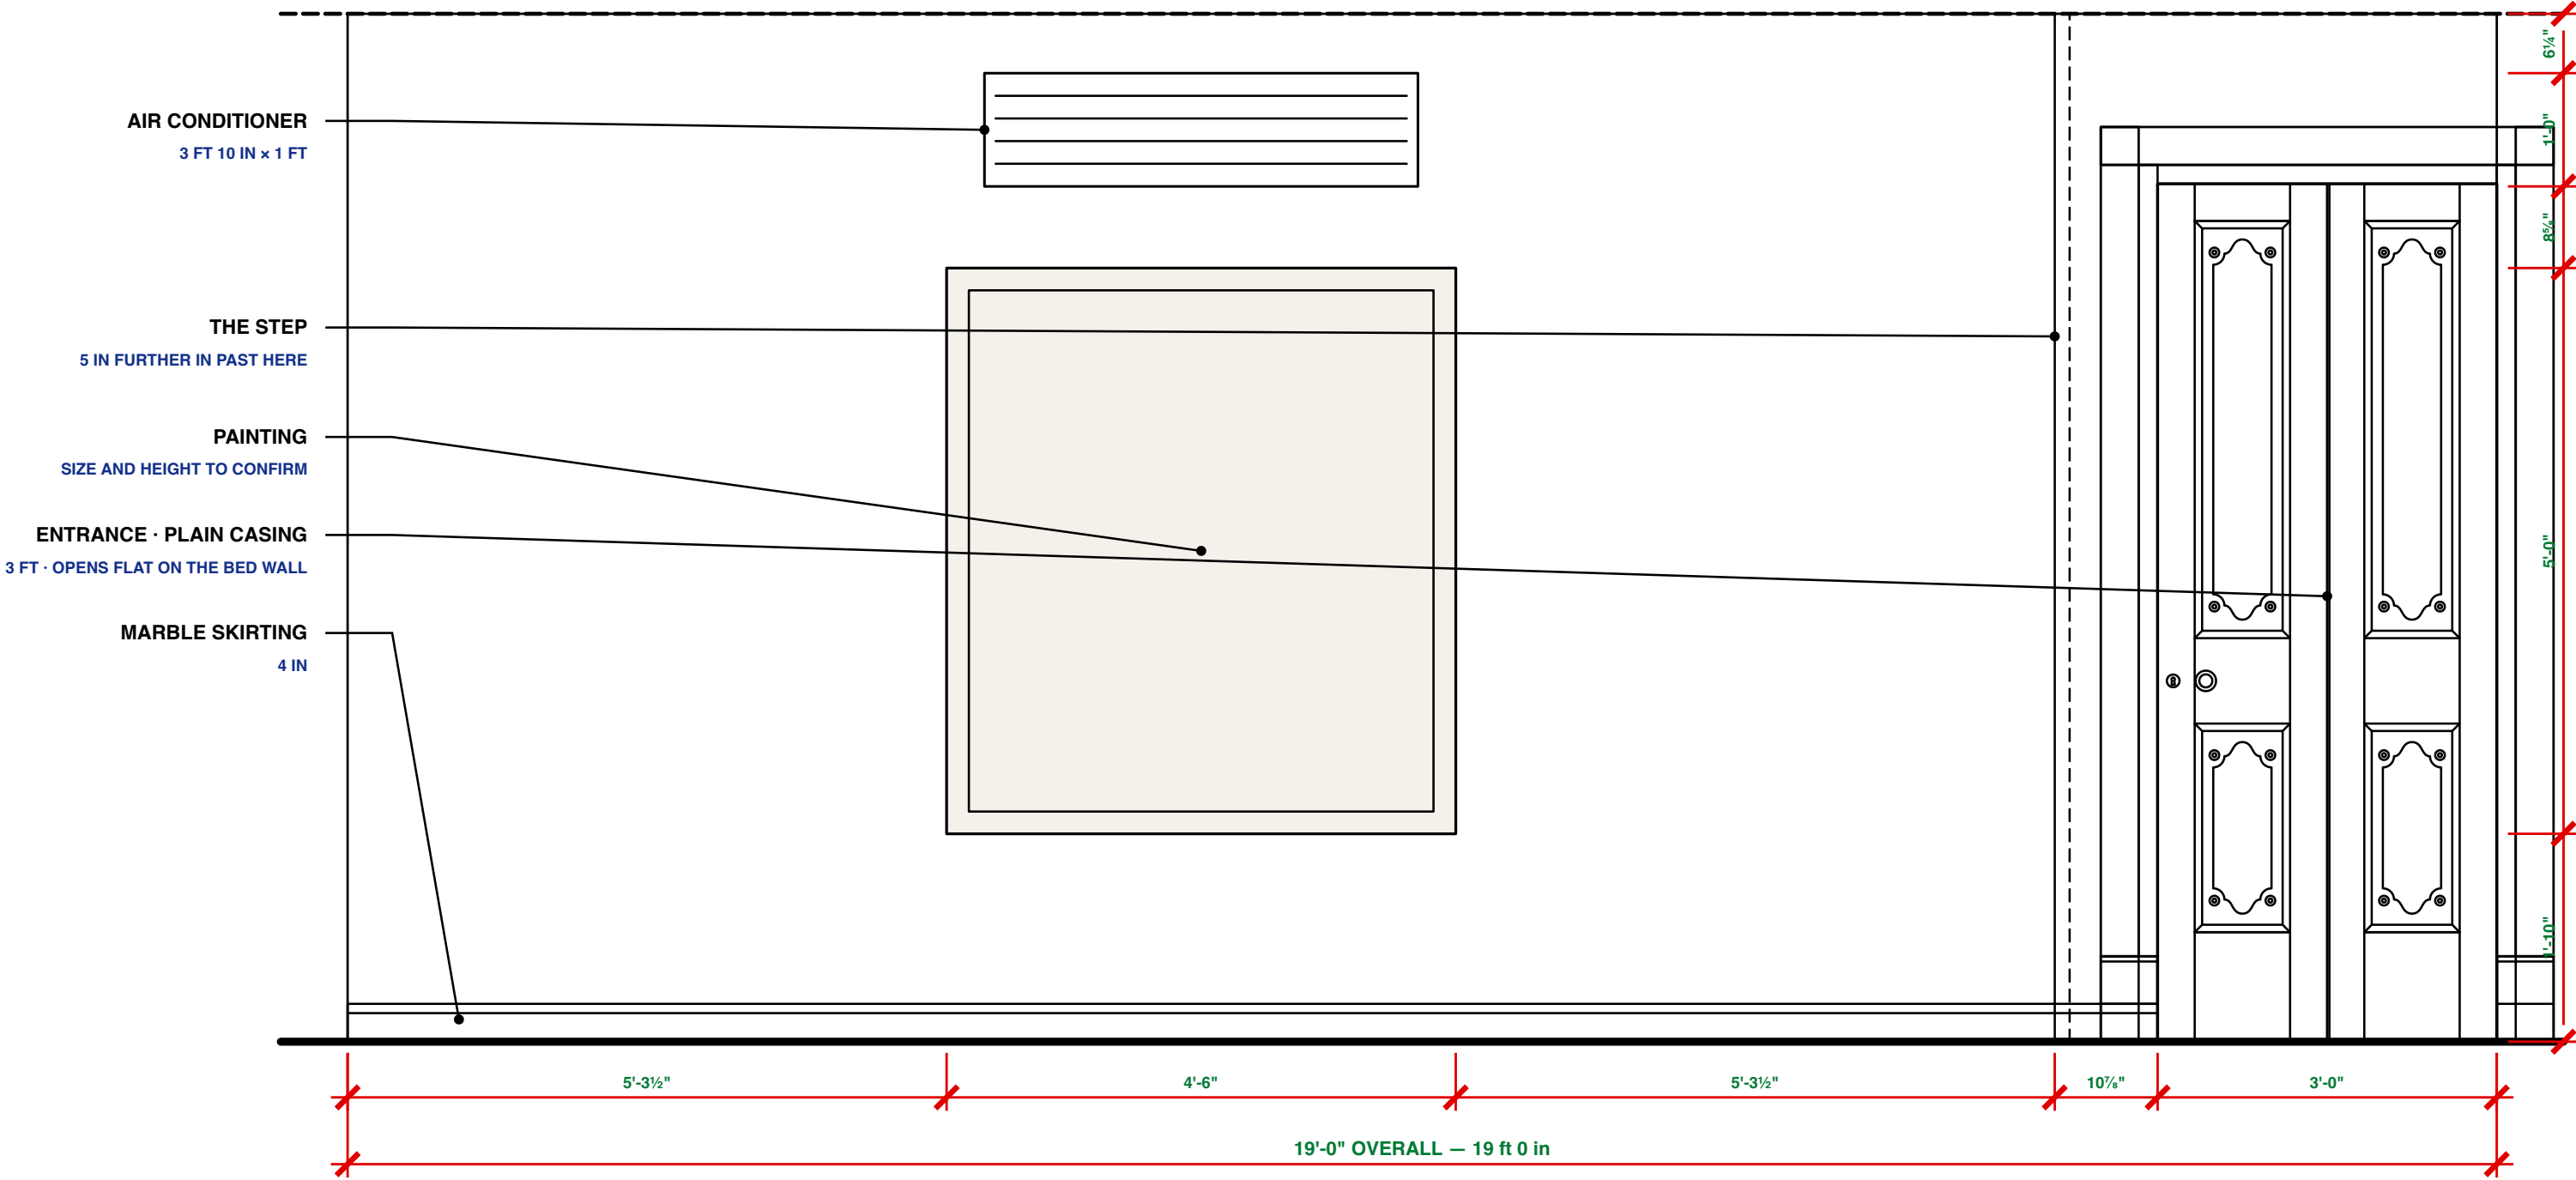

PLAN

CUT AT 3'-11¼" · ROOM BELOW THE WALL

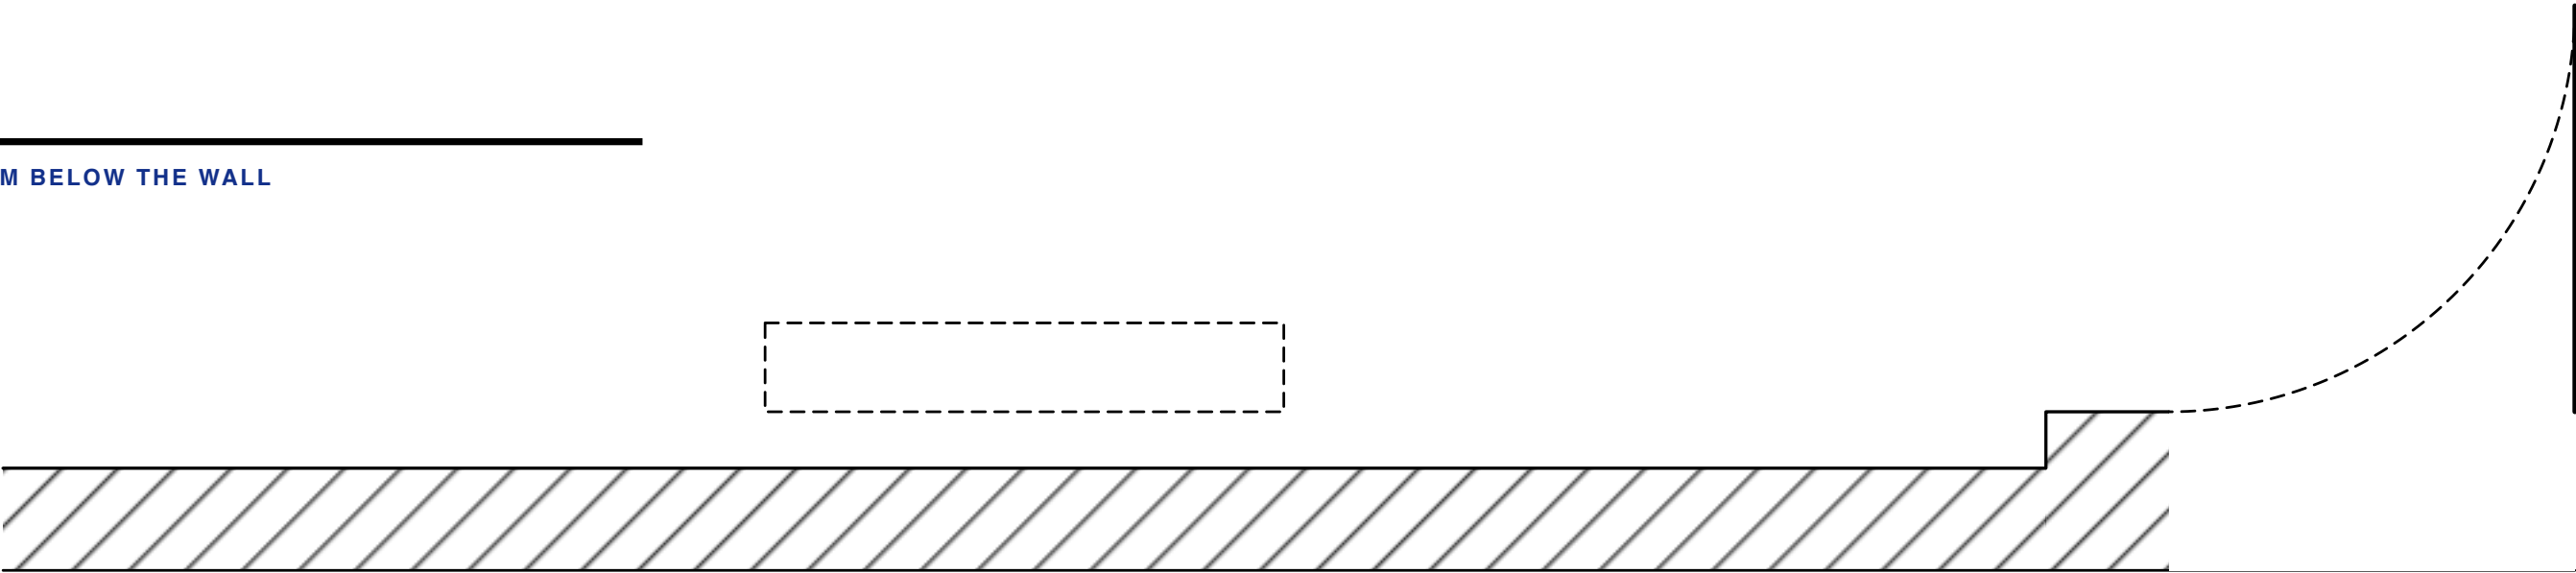

NOTES

REVISION 5

This wall stays plain. Paint, the marble skirting, one painting and the air conditioner over it — nothing is built into it and nothing is panelled.

It is the quiet side of the room, opposite the panelled right wall, and it is the wall that carries the splay and the step, so anything fitted to it would have to be scribed twice.

The painting is centred on the 15 ft 1⅞ in of wall before the step, the only uninterrupted run. Centre line 7 ft 6½ in from the study corner, 1 ft 10 in off the floor.

OPEN — the painting is drawn 4 ft 6 in × 5 ft 0 in, centred at 4 ft 4 in.

Still assumed. Send the real size and it is a one-line change.

Sized to the wall it has: 8⅝ in clear under the air conditioner, and 8 in wider than the unit, so the AC sits within its width.

The air conditioner is 3 ft 10 in × 1 ft 0 in — MEASURED. Its depth (7⅞ in) and its height off the ceiling (6¼ in) are still assumed.

The AC needs a power point and a drain run before the wall is painted — decide the side the pipework leaves on.

The entrance takes the PLAIN casing: same 2 in lining and 4 in moulding at every opening, running straight across the head and stopping. The carved head on AST-DR-011 is the DRESSING door's alone.

OPEN — the profile of that 4 in plain band is not settled. Drawn flat.