



ELEVATION – RIGHT WALL

SEEN FROM THE ROOM · STUDY WALL ON THE LEFT · OPTION C

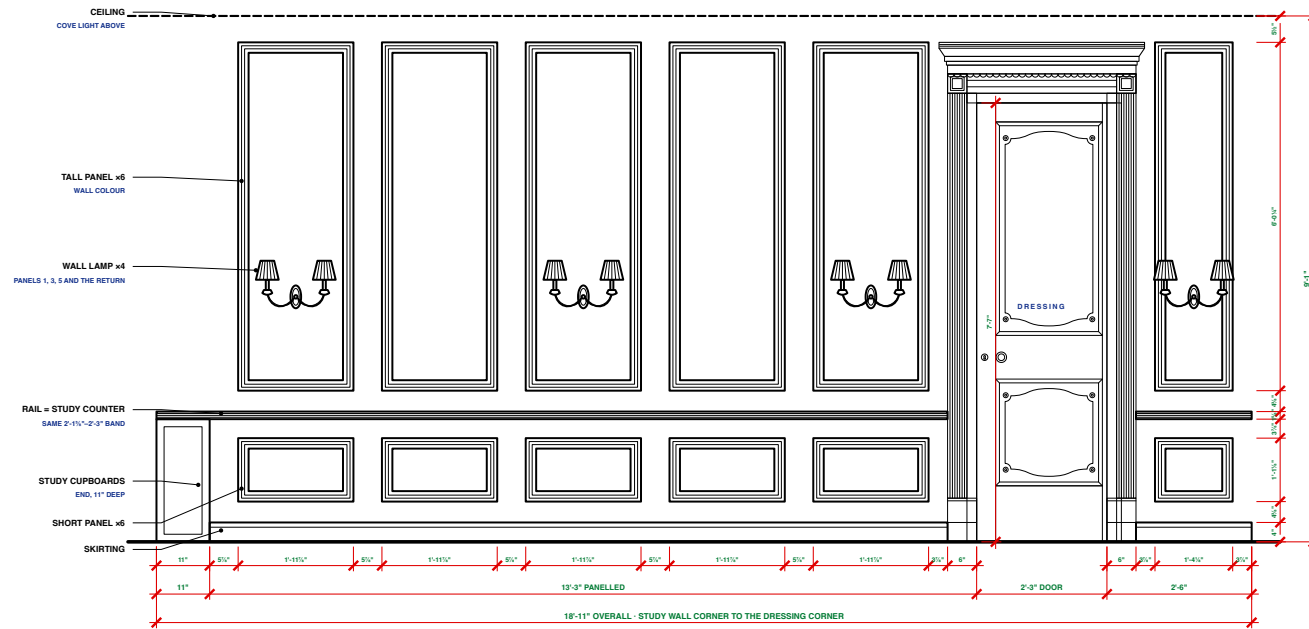


PLAN

CUT AT 3'-3 1/2" - ROOM BELOW, WALL ABOVE

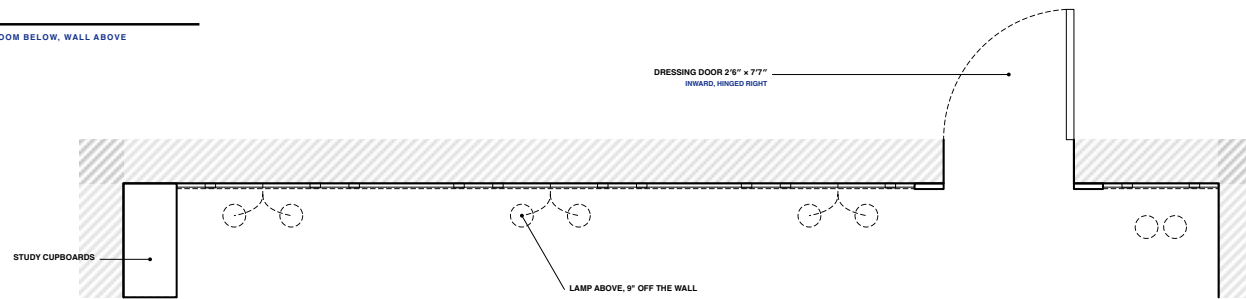


1 · PANEL MOULDING

SECTION

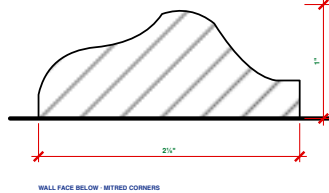


2 · RAIL

SECTION

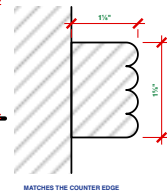


3 · SKIRTING

MARBLE · SECTION

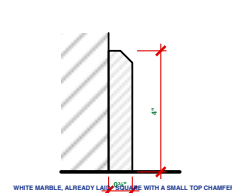


4 · WALL LAMP

ELEVATION · x4

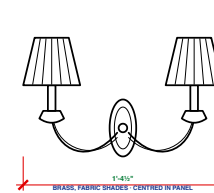

SECTION A-A

THROUGH PANEL 1

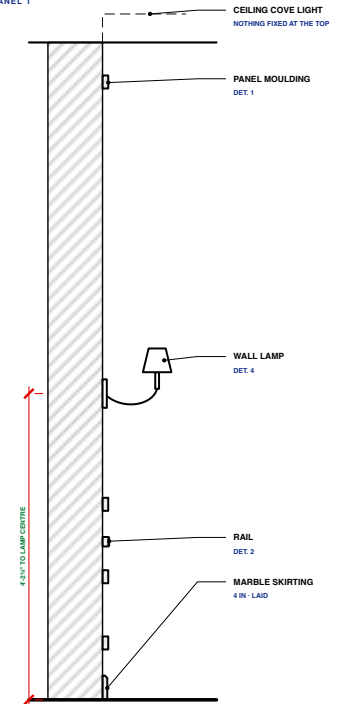

NOTES

REVISION 18

Option C: 5 equal panels, lamps in 1, 3, 5 and the return.

One narrow panel on the wall past the door.

Moulding, rail and skirting painted the wall colour.

SELECTED after four schemes: the rail is the study counter

band carried round the corner, and it dies into the casing.

Skirting is white marble, 4 in, already laid.

Casing 2 in lining + 4 in moulding = 6 in, 3'-6" overall;

crown at 8 ft 8 in, and the tall panels stop on that

line, not the leaf head at 7 ft 7 in.

2 ft 4 in corner to frame, measured both sides; leaf 2 ft 3

in a 2 in frame. OPEN: that puts the frame 14 ft 0 from the

study corner, 6 in off the taped 13 ft 6. Retape that end.

A STUDY IN TEAK

Particulars of the room


RIGHT WALL – PANEL MOULDING

Elevation · Plan · Section · Details

SCALE AS NOTED @ A3	DATE 20.09.2026
REV 18 -- SELECTED: the rail at 2 ft 3 in, carrying the study counter round	DWG AST-DR-007


ELEVATION — RIGHT WALL

SEEN FROM THE ROOM · STUDY WALL ON THE LEFT · OPTION C

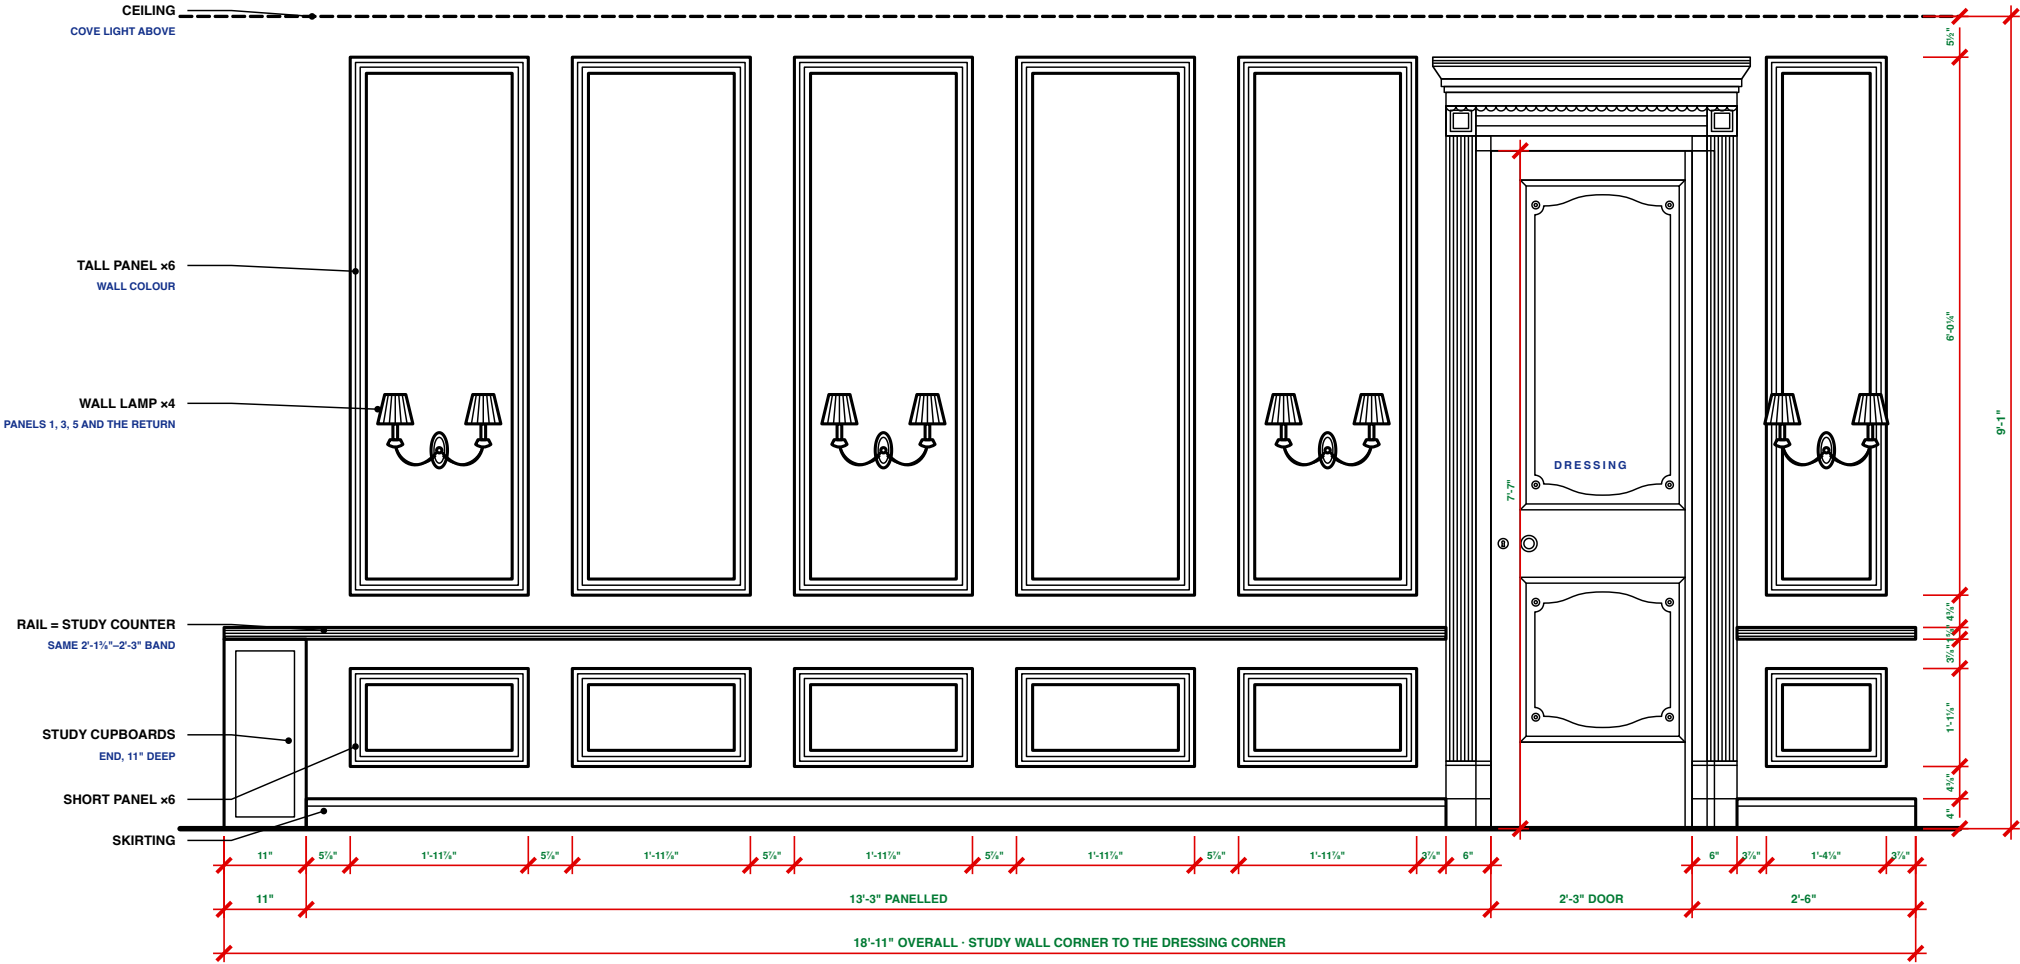


SECTION A-A

THROUGH PANEL 1

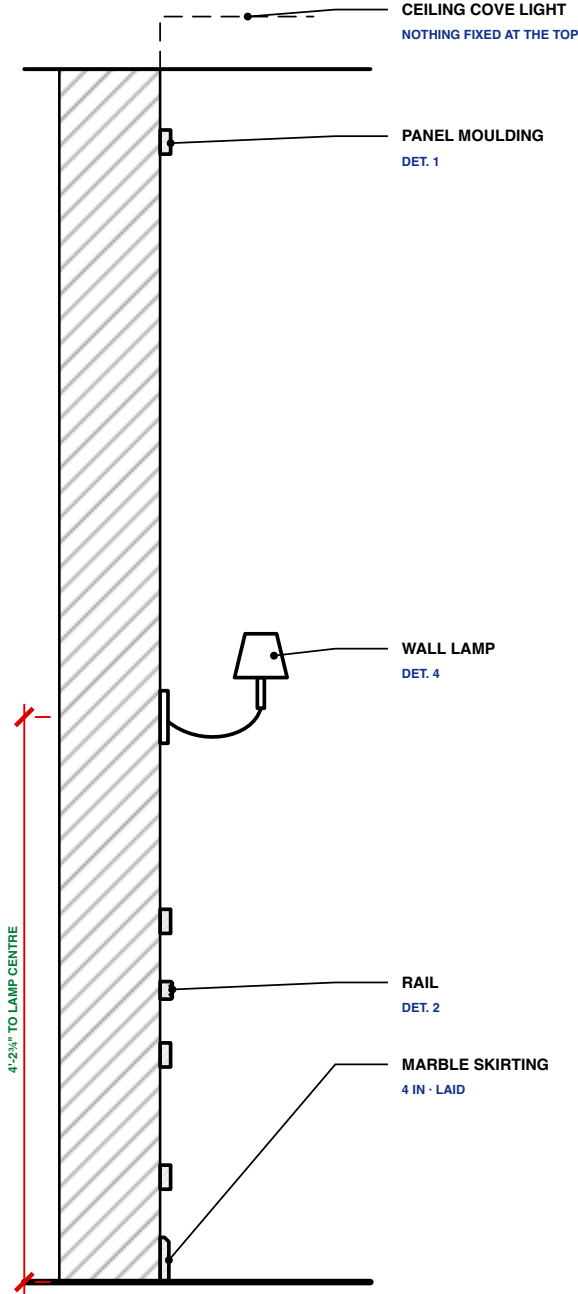

PLAN

CUT AT 3'-3 3/4" · ROOM BELOW, WALL ABOVE

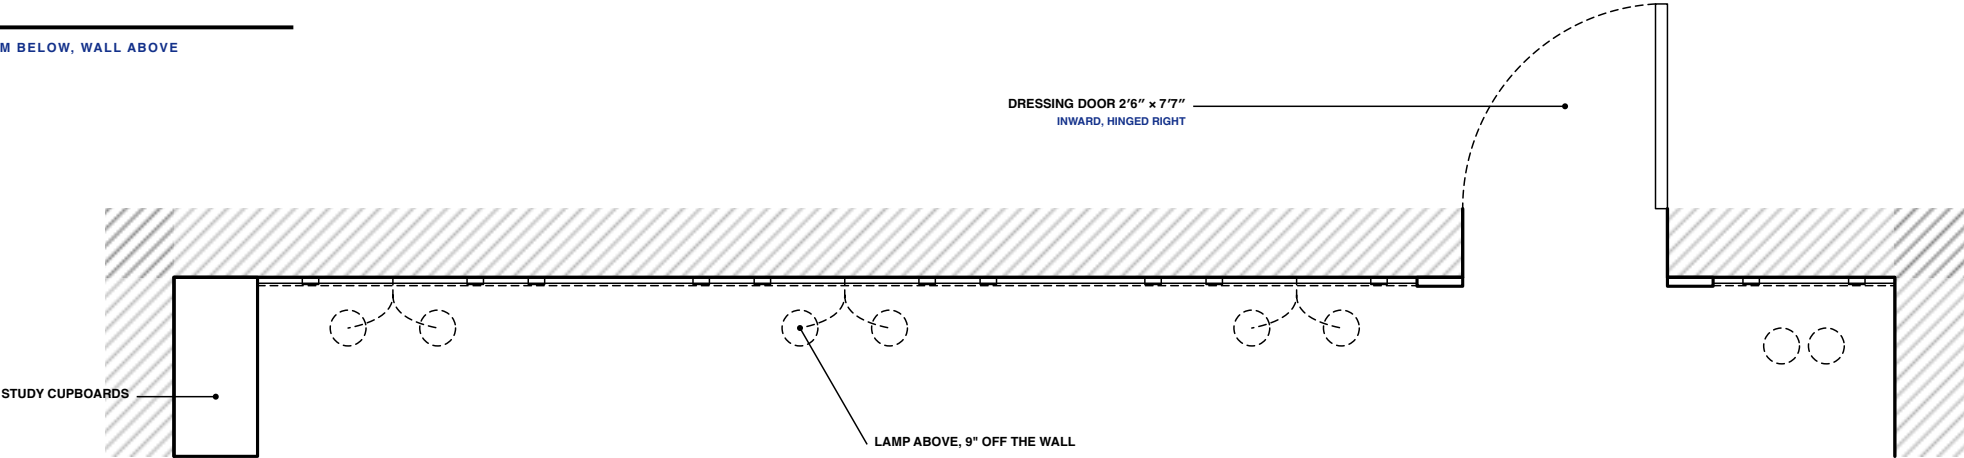

NOTES

REVISION 18

Option C: 5 equal panels, lamps in 1, 3, 5 and the return.

One narrow panel on the wall past the door.

Moulding, rail and skirting painted the wall colour.

SELECTED after four schemes: the rail is the study counter

band carried round the corner, and it dies into the casing.

Skirting is white marble, 4 in, already laid.

Casing 2 in lining + 4 in moulding = 6 in, 3'-6" overall;

crown at 8 ft 8 in, and the tall panels stop on that

line, not the leaf head at 7 ft 7 in.


2 ft 4 in corner to frame, measured both sides; leaf 2 ft 3

in a 2 in frame. OPEN: that puts the frame 14 ft 0 from the

study corner, 6 in off the taped 13 ft 6. Retape that end.

1 · PANEL MOULDING


SECTION

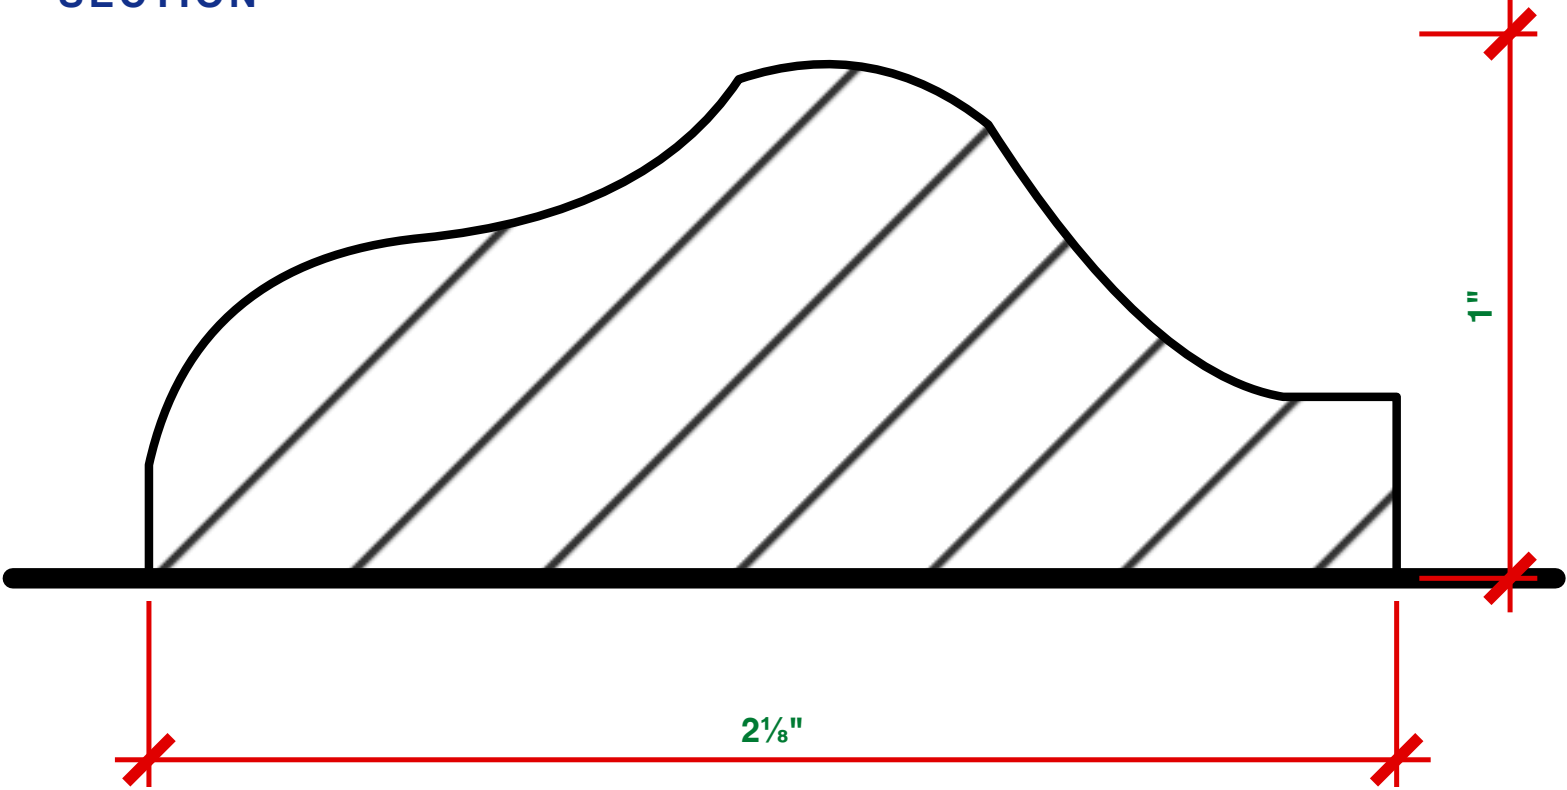

WALL FACE BELOW · MITRED CORNERS

2 · RAIL


SECTION

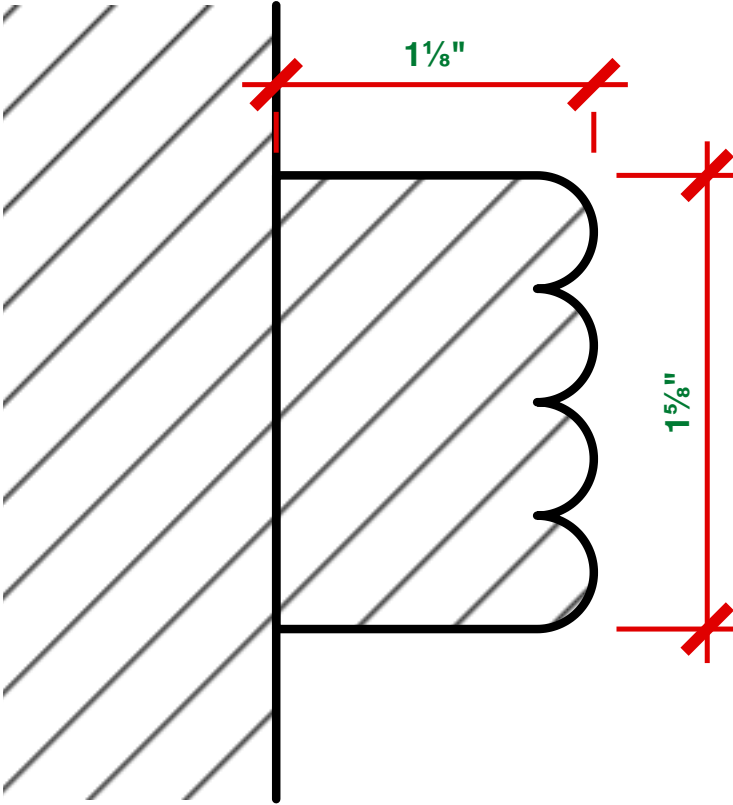

MATCHES THE COUNTER EDGE

3 · SKIRTING

MARBLE · SECTION

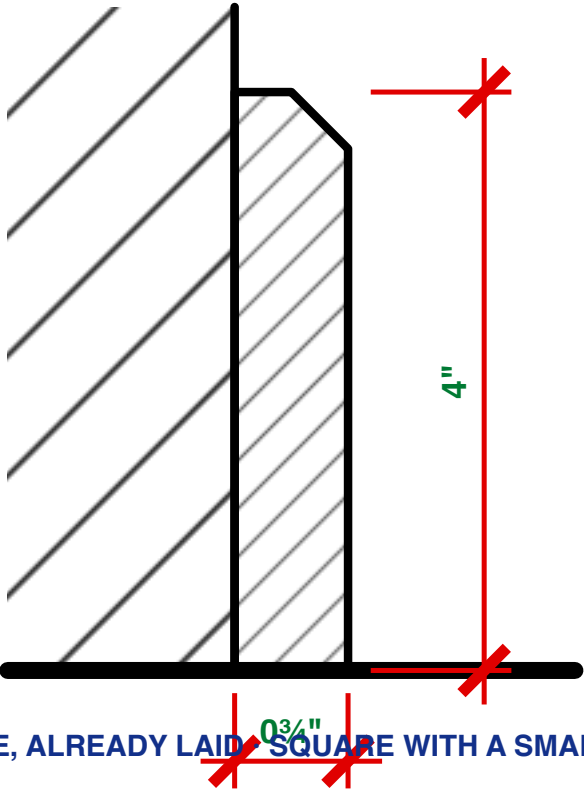

4 · WALL LAMP

ELEVATION · x4

