



FRONT

CHOSEN · 1 FT 6 IN LEFT, 6 IN RIGHT · 3 FT MARBLE BANK ON THE FAUCET, DOWN TO THE FLOOR

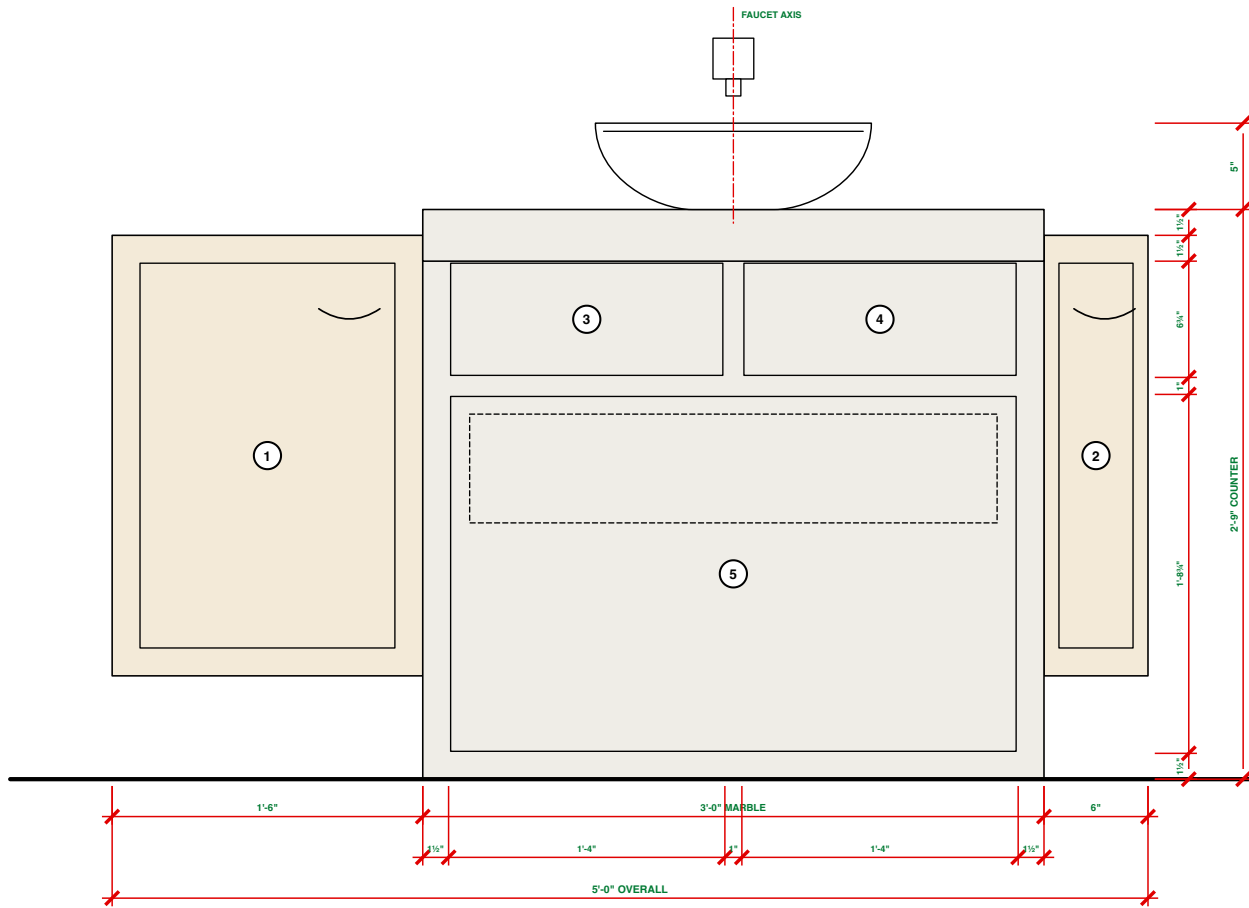

PLAN

FROM ABOVE · WALL AT THE TOP

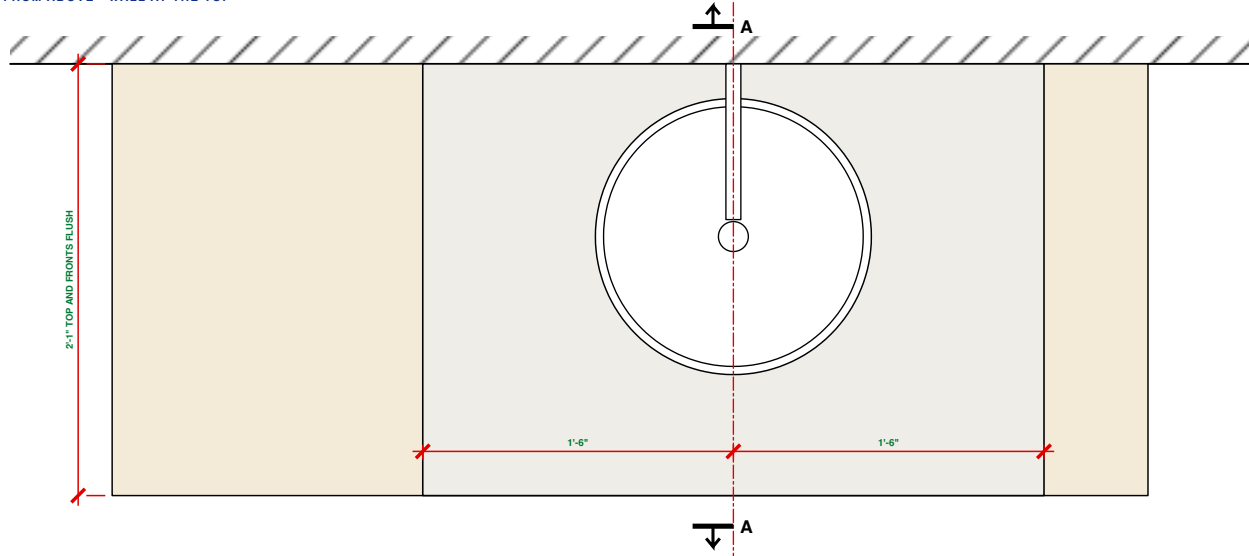

SECTION KEY

- (A) Hanging cleat
- (B) Big drawer, U-box
- (C) Waste Ø1½" and P-trap
- (E) Wall spout
- (F) Ply sub-top
- (G) Inner drawer


NOTES

REVISION 3
The marble bank now runs to the floor and is the support.
Top drawers: 6½ in fronts. Drawer within: a 5½ in box.
The big drawer takes the rest: 20½ in front, 12½ in clear under the inner drawer for tall bottles.

OPEN — bowl Ø1'-4" x 5" and the spout are assumed.
OPEN — marble front thickness and how it is bonded to the drawer boxes: stone supplier to confirm.
Rev 3: top and front meet in one mitred corner, flush.


SECTION A-A

ON THE FAUCET AXIS

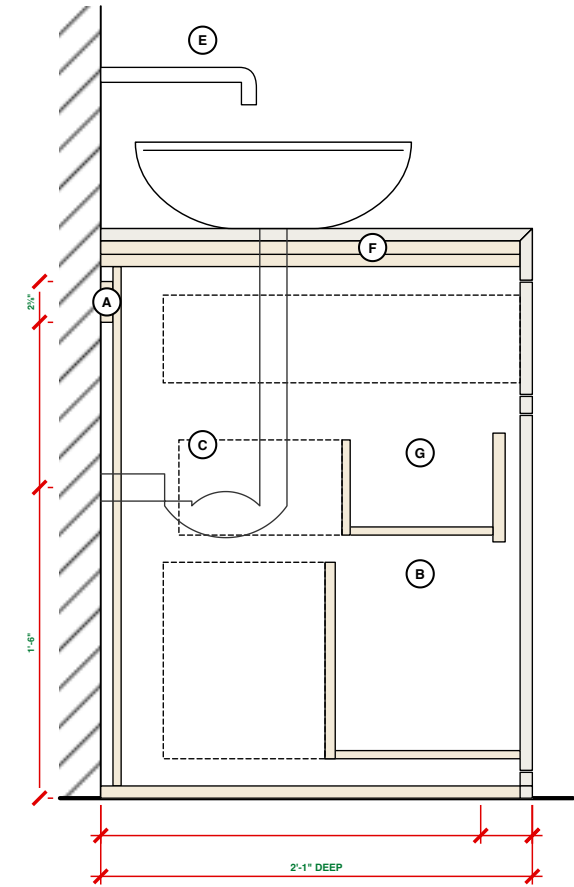

DETAIL 1 · THE MARBLE EDGE

SECTION · ONE MITRED CORNER, FRONTS FLUSH

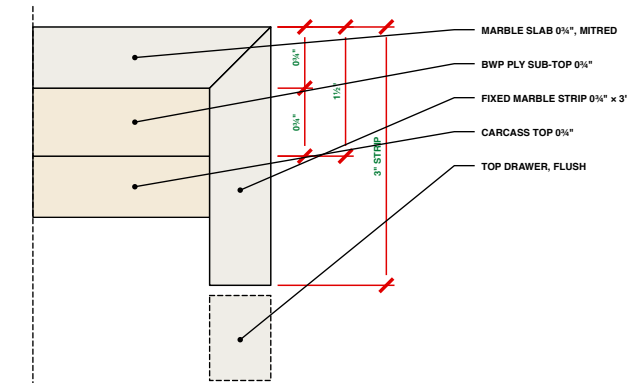

FRONTS

SIZES ARE THE FRONT ITSELF · 0¼" GAP ALL ROUND

No.	WHAT	W x H	FT-IN
1	Pull-out cabinet, cup pull	1'-2¼" x 1'-10¼"	1'-2¼" x 1'-10¼"
2	Pull-out cabinet, cup pull	4¼" x 1'-10¼"	4¼" x 1'-10¼"
3	Top drawer, push-open · marble	1'-3¾" x 6½"	1'-3¾" x 6½"
4	Top drawer, push-open · marble	1'-3¾" x 6½"	1'-3¾" x 6½"
5	Big drawer, U-box, push-open · marble	2'-8¼" x 1'-8½"	2'-8¼" x 1'-8½"
5a	Inner drawer, finger scoop	2'-6½" x 6¼"	2'-6½" x 6¼"

MATERIALS

THE ROOM'S PALETTE — NOTHING NEW

- Top** Beige-gold marble, the bathroom stone. 0¼" slab on a 0¼" BWP sub-top, mitred at the front edge into a fixed 0¼" marble strip: one corner, fronts flush.
- Bank** The same beige marble on the face frame and on every drawer front, floor to counter. It stands on the floor and carries the top — no support.
- Ends** Two pull-out cabinets, 9292 cream burl veneer, high gloss, 0¼" BWP, edges sealed. 6 in off the floor.
- Ledges** The two veneer tops: solid nosing, sealed.
- Runners** Drawers: undermount, push-to-open. Pull-outs: heavy full-extension runners, cup pull.
- Fittings** Chrome — already bought.
- Inner** U-box, 5½ in deep, on its own runners — AST-DR-022.

A STUDY IN TEAK

Particulars of the room


VANITY — SCHEME C

Chosen · marble bank to the floor · pull-outs each end

SCALE AS NOTED @ A3	DATE 02.10.2026
REV 3 — one mitred corner, fronts flush with the top	DWG AST-DR-021


FRONT

CHOSEN · 1 FT 6 LEFT, 6 IN RIGHT · 3 FT MARBLE BANK ON THE FAUCET, DOWN TO THE FLOOR

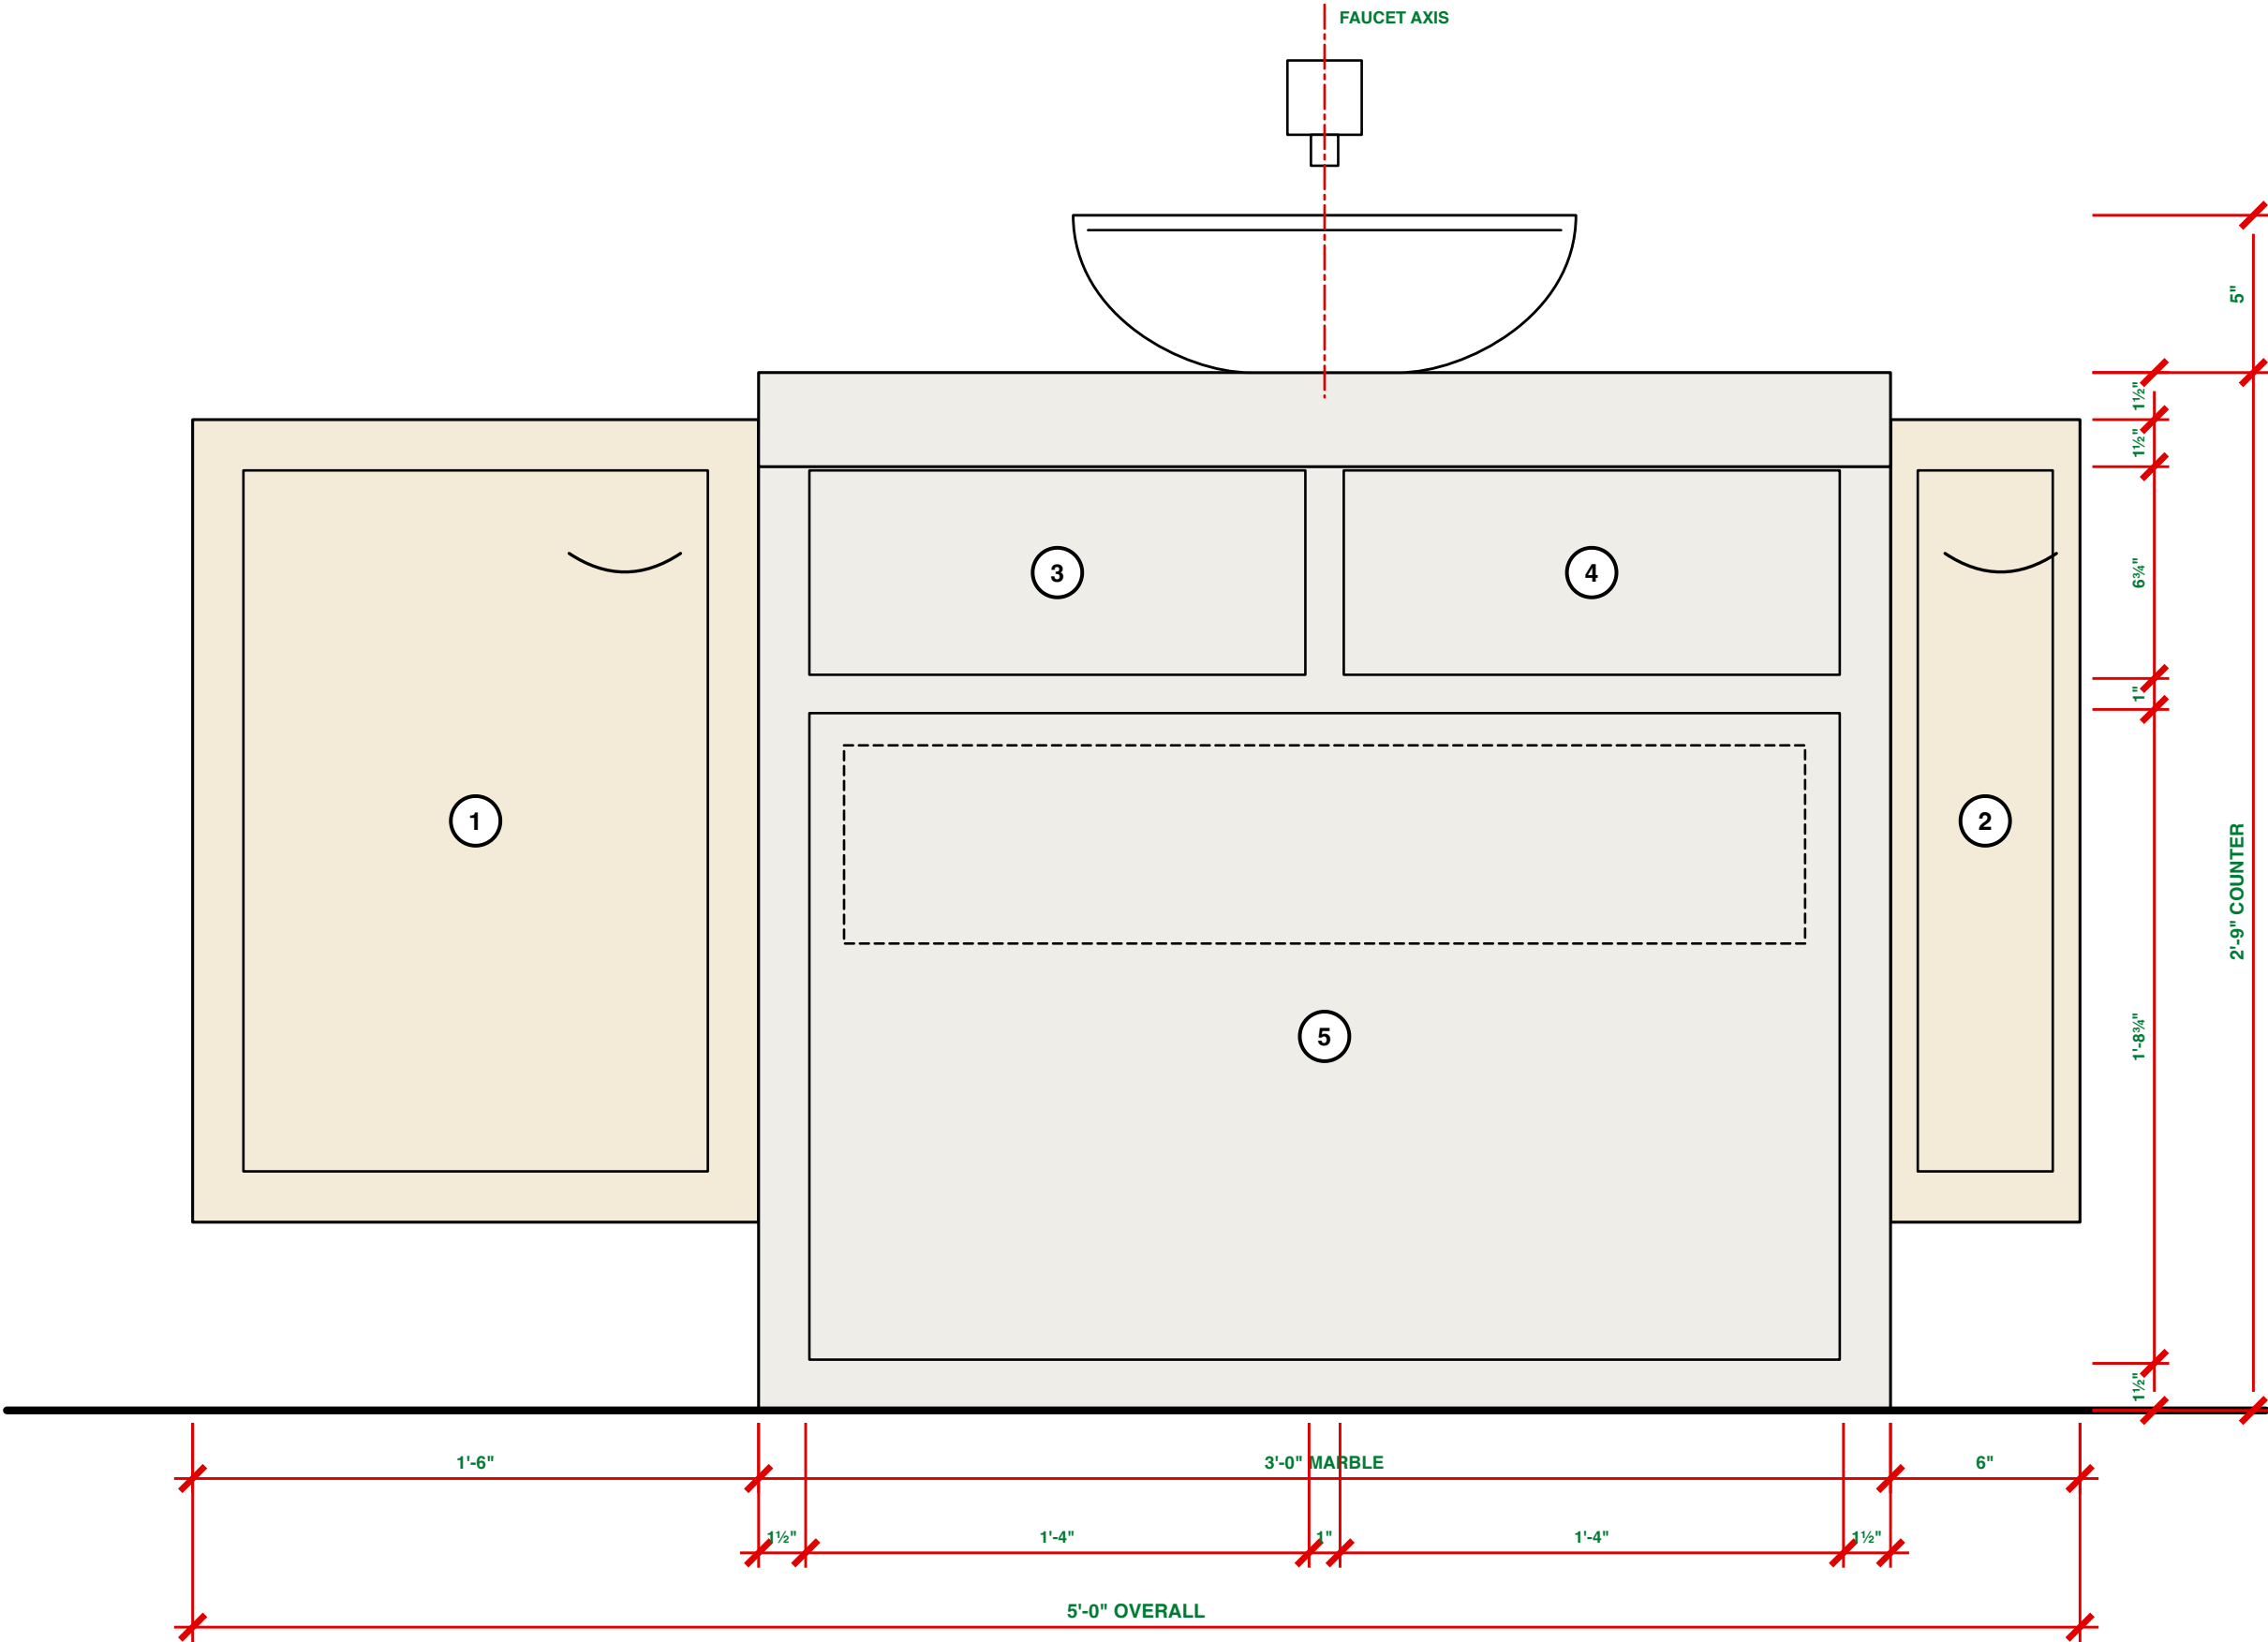


SECTION A-A

ON THE FAUCET AXIS

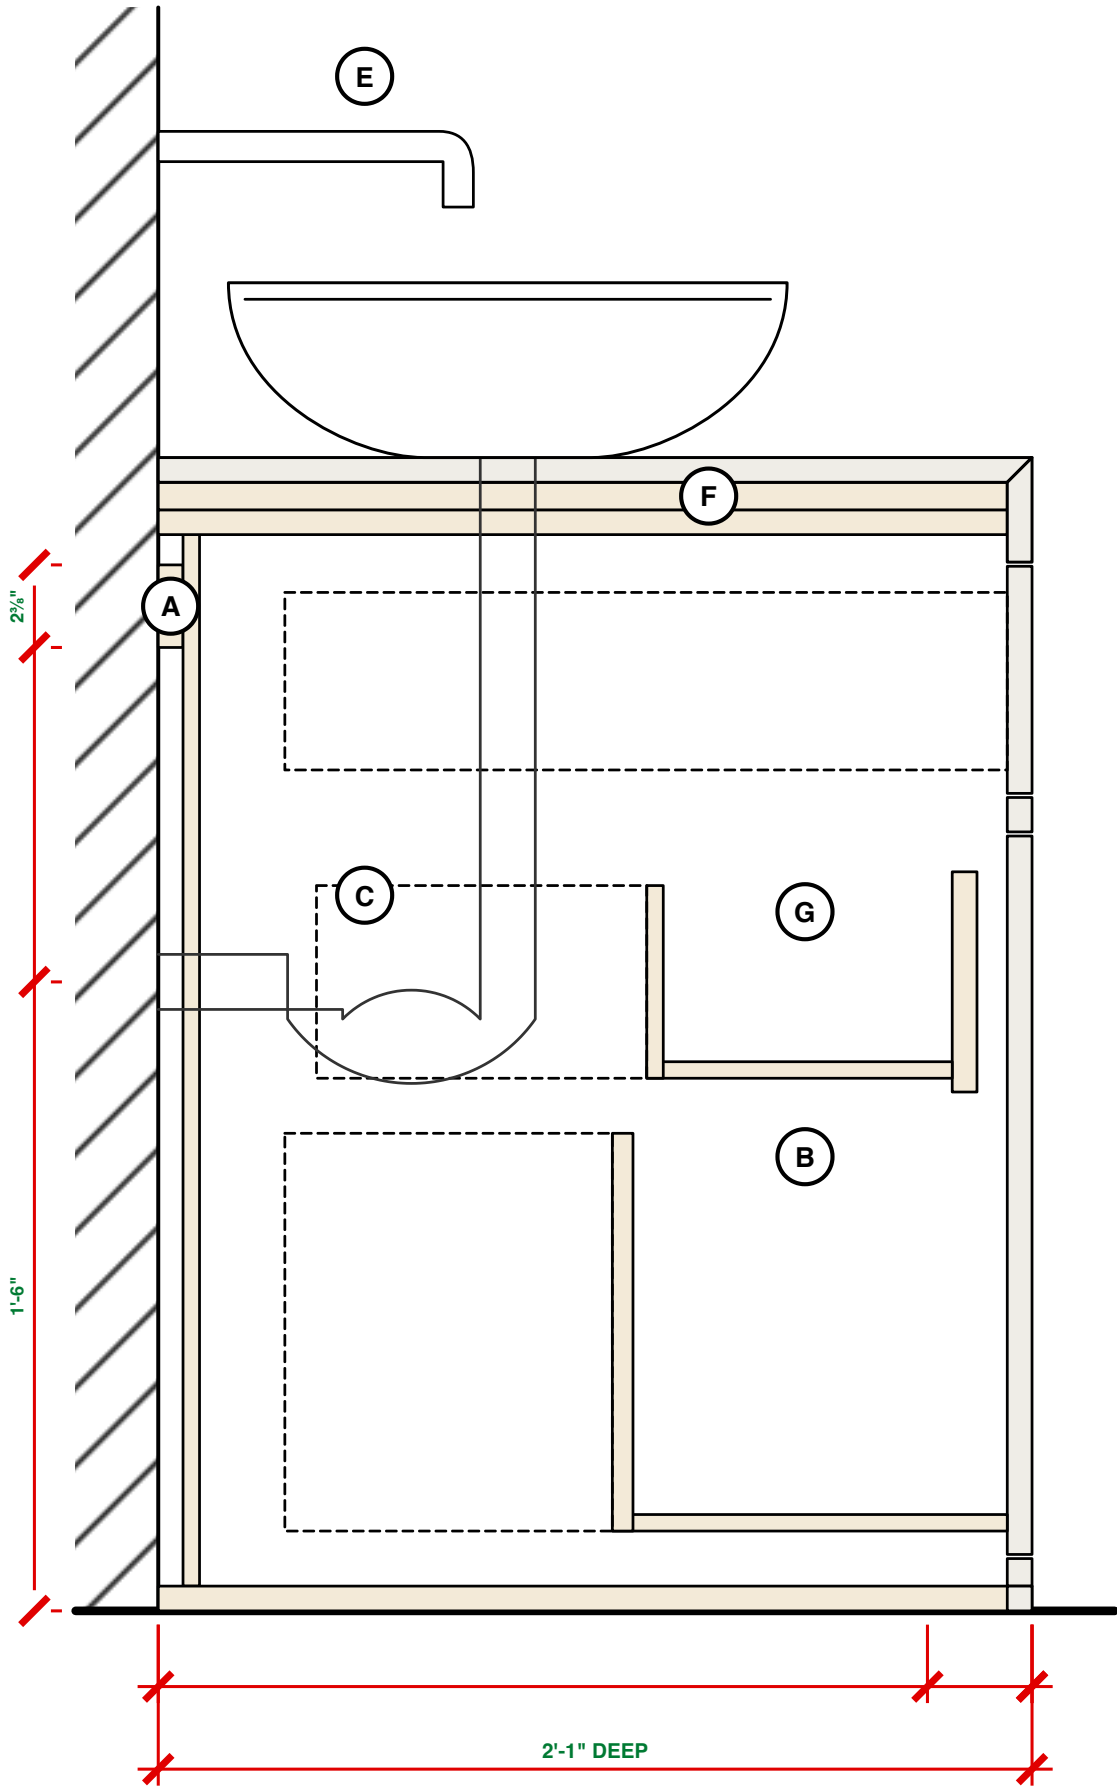

DETAIL 1 · THE MARBLE EDGE

SECTION · ONE MITRED CORNER, FRONTS FLUSH

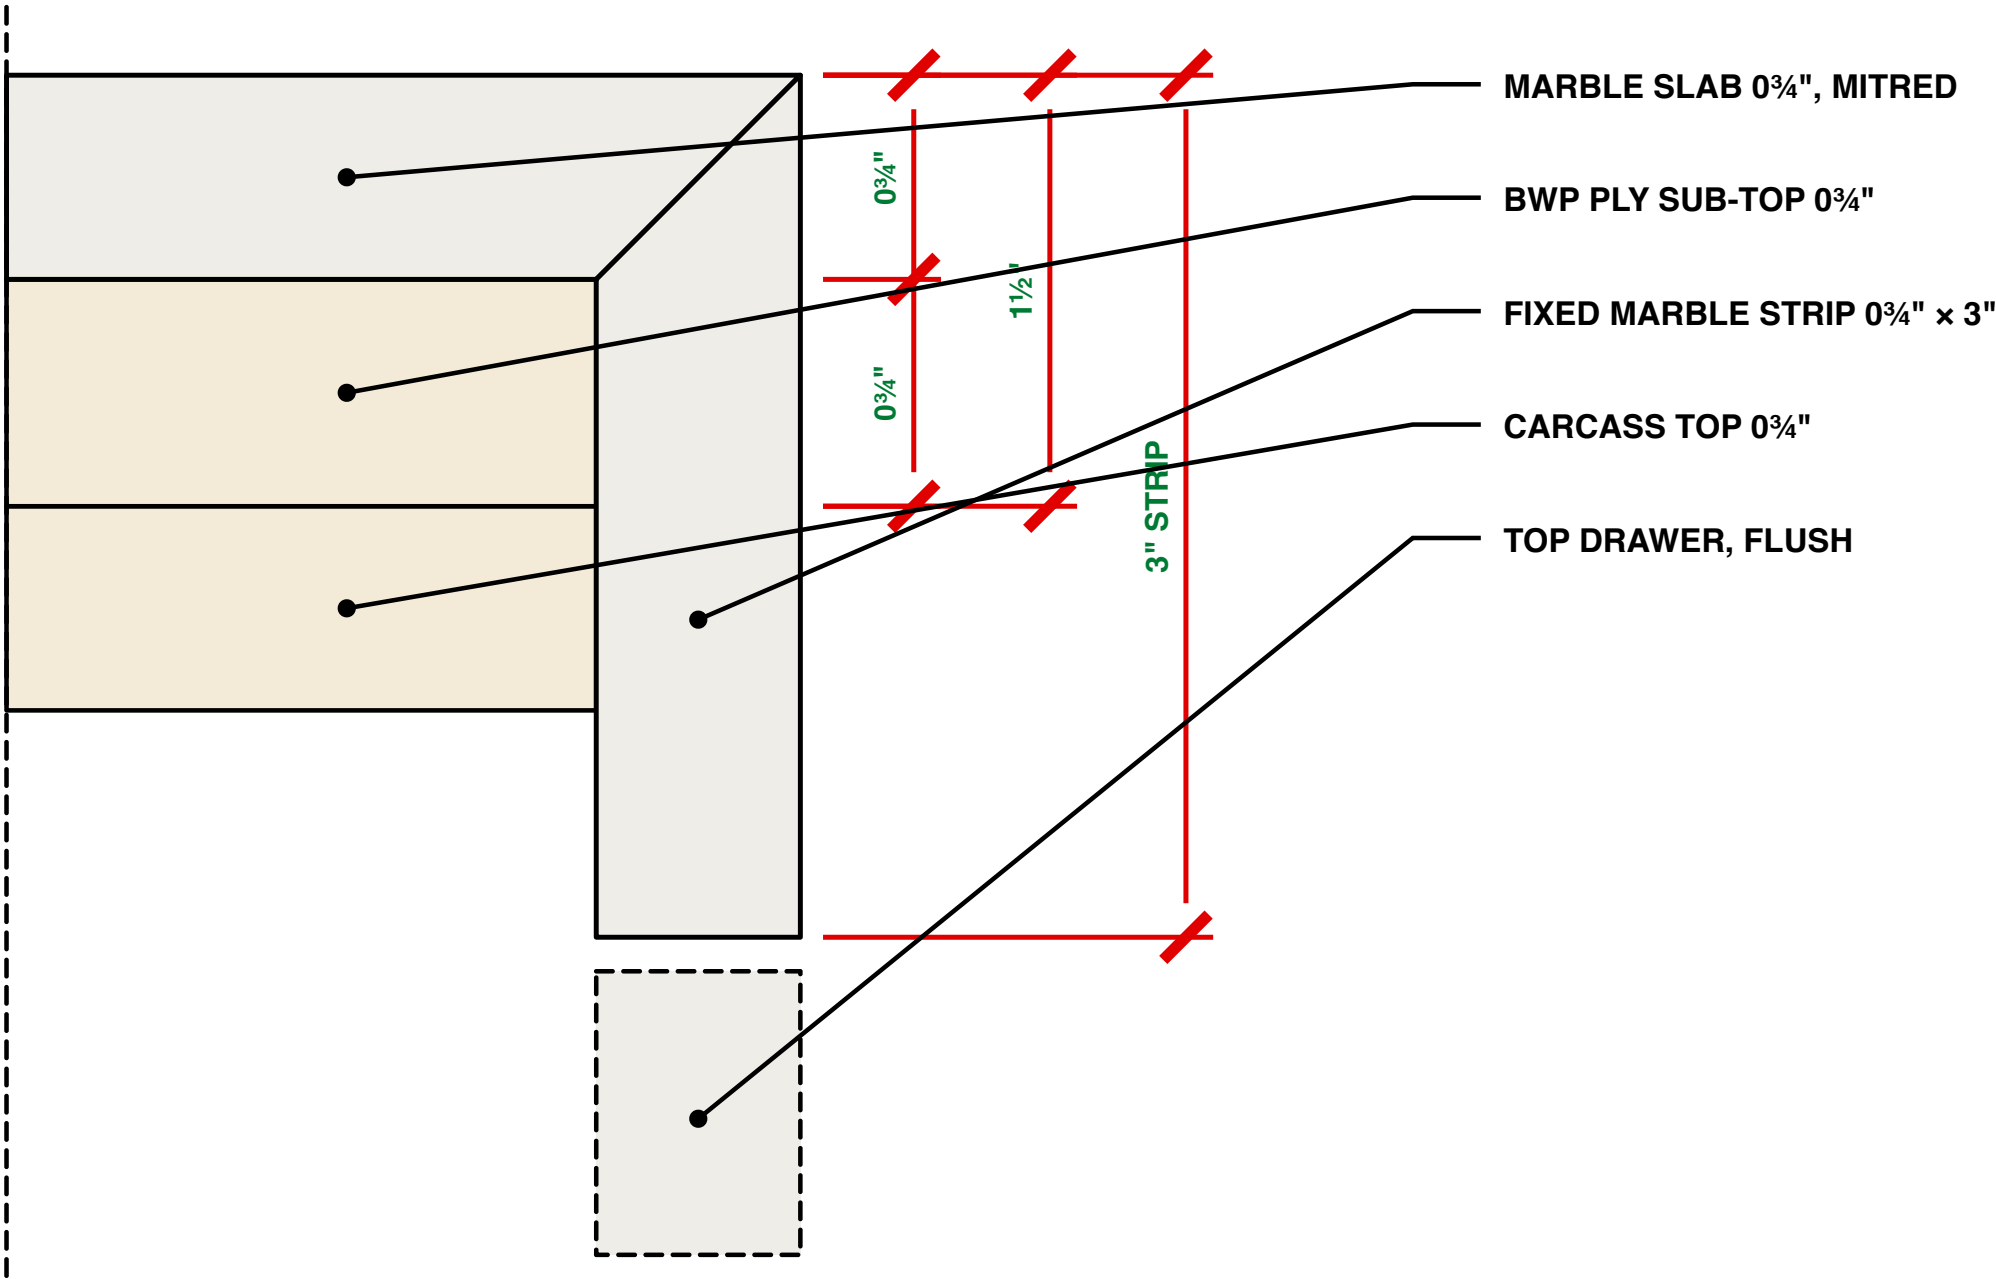

FRONTS

SIZES ARE THE FRONT ITSELF · 0⅛" GAP ALL ROUND

No.	WHAT	W × H	FT-IN
1	Pull-out cabinet, cup pull	1'-2¾" × 1'-10¼"	1'-2¾" × 1'-10¼"
2	Pull-out cabinet, cup pull	4¼" × 1'-10¼"	4¼" × 1'-10¼"
3	Top drawer, push-open · marble	1'-3¾" × 6½"	1'-3¾" × 6½"
4	Top drawer, push-open · marble	1'-3¾" × 6½"	1'-3¾" × 6½"
5	Big drawer, U-box, push-open · marble	2'-8¾" × 1'-8½"	2'-8¾" × 1'-8½"
5a	Inner drawer, finger scoop	2'-6½" × 6¼"	2'-6½" × 6¼"


MATERIALS

THE ROOM'S PALETTE — NOTHING NEW

Top	Beige-gold marble, the bathroom stone. 0¾" slab on a 0¾" BWP sub-top, mitred at the front edge into a fixed 0¾" marble strip: one corner, fronts flush.
Bank	The same beige marble on the face frame and on every drawer front, floor to counter. It stands on the floor and carries the top — no support.
Ends	Two pull-out cabinets, 9292 cream burl veneer, high gloss, 0¾" BWP, edges sealed. 6 in off the floor.
Ledges	The two veneer tops: solid nosing, sealed.
Runners	Drawers: undermount, push-to-open. Pull-outs: heavy full-extension runners, cup pull.
Fittings	Chrome — already bought.
Inner	U-box, 5½ in deep, on its own runners — AST-DR-022.


PLAN

FROM ABOVE · WALL AT THE TOP

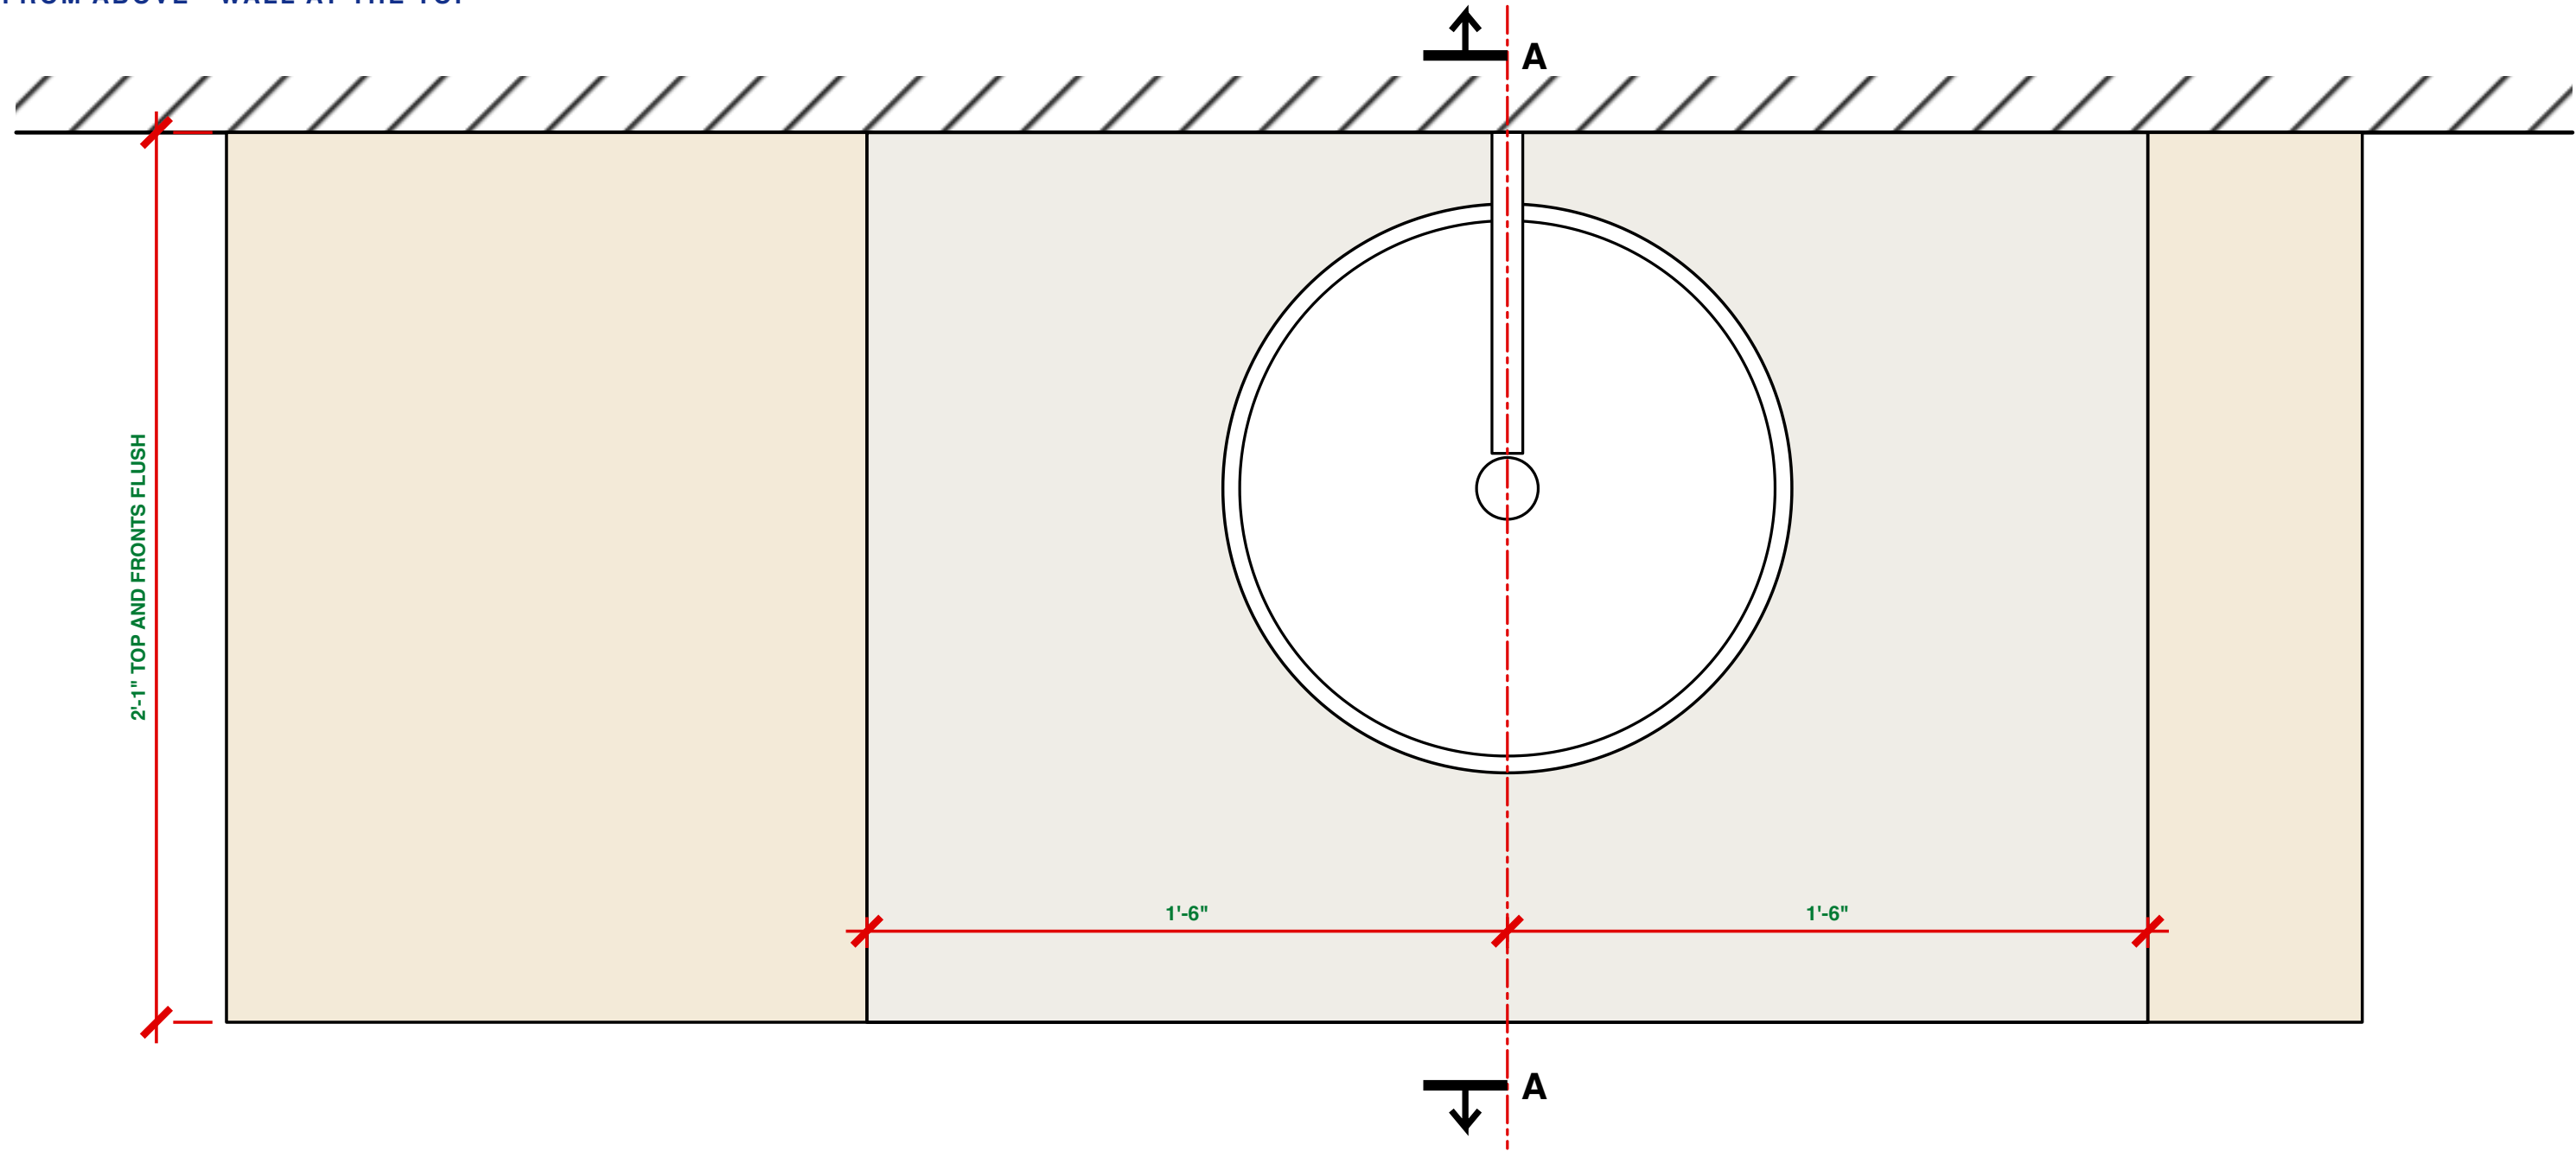

DETAIL 2 · THE BIG DRAWER

PLAN · INNER DRAWER DASHED

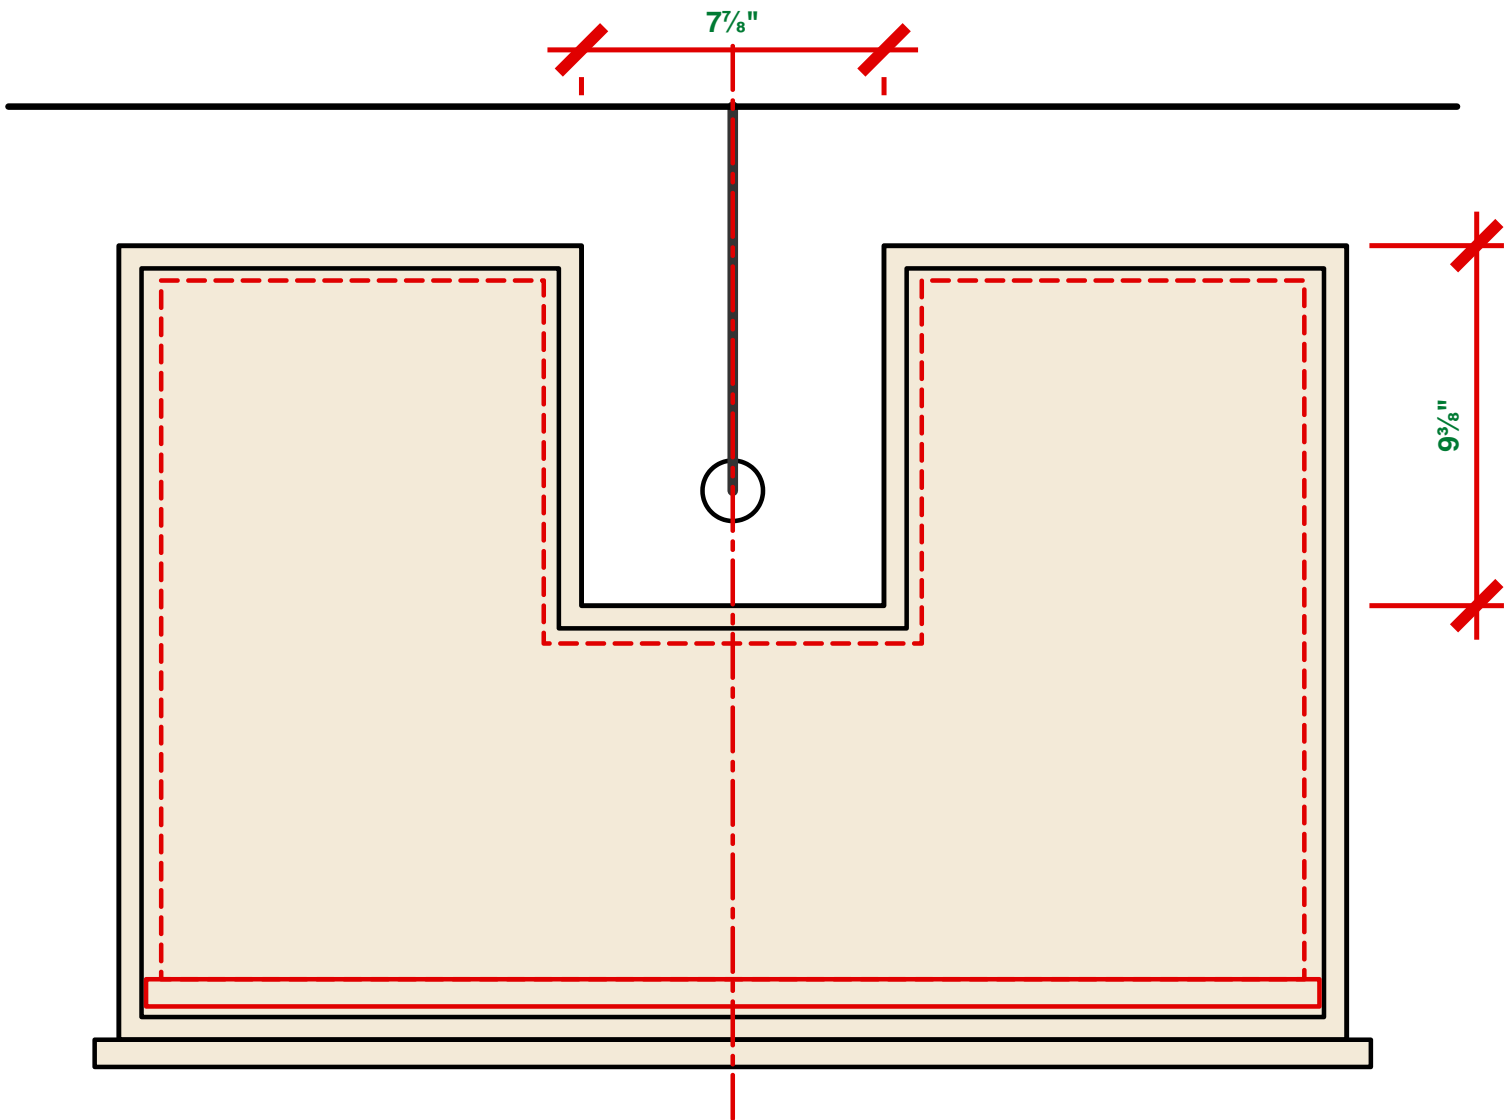

SECTION KEY



Hanging cleat



Big drawer, U-box



Waste Ø1⁵/₈" and P-trap



Wall spout



Ply sub-top



Inner drawer

NOTES

REVISION 3

The marble bank now runs to the floor and is the support.

Top drawers: 6½ in fronts. Drawer within: a 5½ in box.

The big drawer takes the rest: 20½ in front, 12¾ in clear

under the inner drawer for tall bottles.

OPEN — bowl Ø1'-4" × 5" and the spout are assumed.


OPEN — marble front thickness and how it is bonded to the

drawer boxes: stone supplier to confirm.

Rev 3: top and front meet in one mitred corner, flush.


1 · CLOSED

SECTION THROUGH ONE ARM · SCHEME C, CHOSEN — BANK TO THE FLOOR

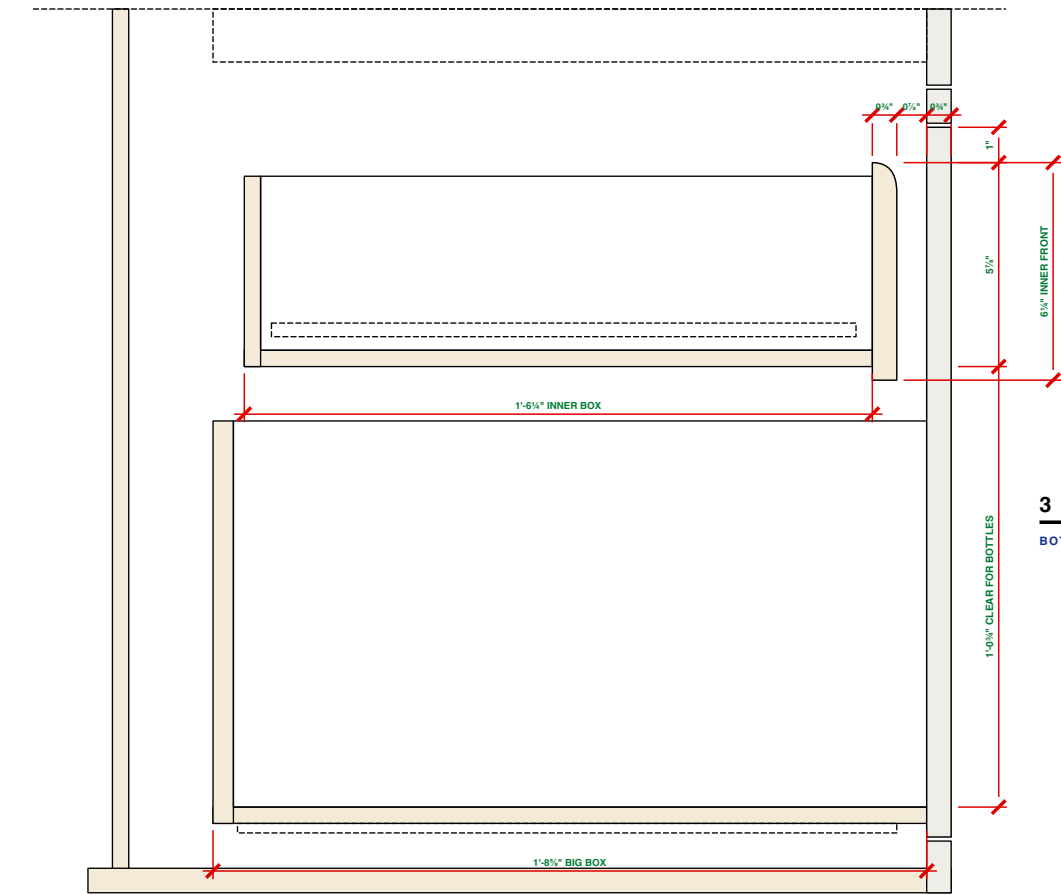


4 · FRONT

THE INNER DRAWER HIDES BEHIND THE BIG FRONT · MARBLE BANK, FLOOR TO COUNTER

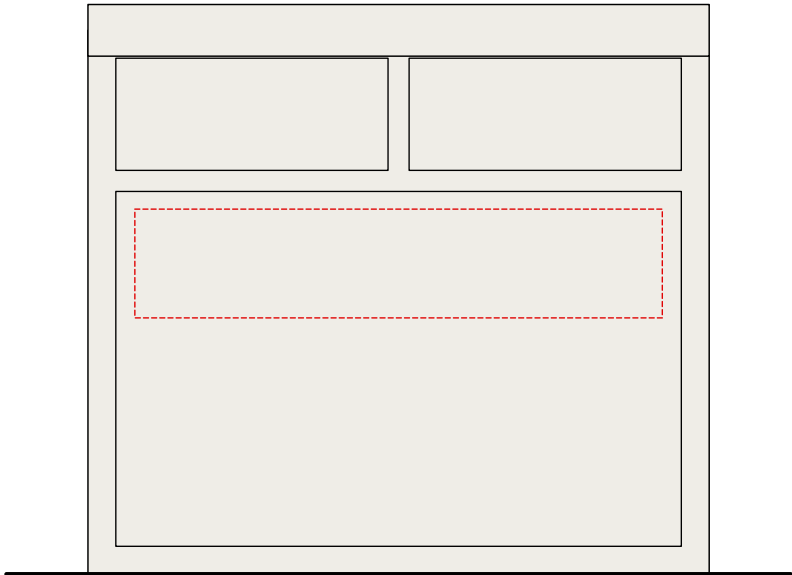


2 · OPEN

BIG DRAWER OUT · INNER ONE PULLED OUT BEHIND ITS FRONT

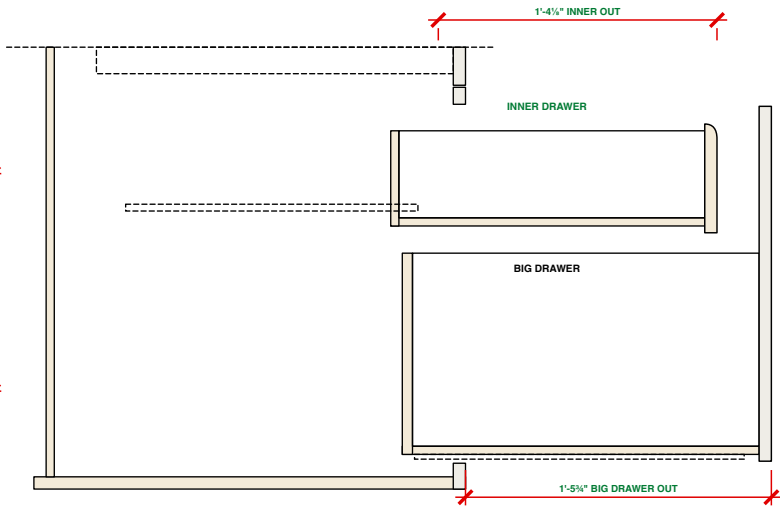

3 · PLAN

BOTH DRAWERS SHUT · THE PIPE DROPS THROUGH BOTH NOTCHES

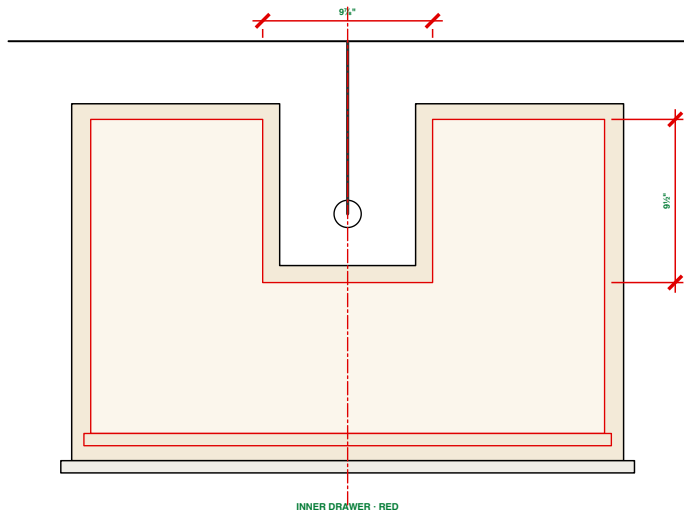

SIZES

THE SAME DRAWER IN ALL THREE SCHEMES

SCHEME	BIG FRONT	INNER FRONT	INNER BOX W
Normal	2'-2 1/4" x 1'-3 1/4"	2'-0 1/2" x 3 1/4"	1'-11 1/4" · L
B	3'-8 1/4" x 1'-3 1/4"	3'-6 1/2" x 3 1/4"	3'-5 1/4" · U
C	2'-8 1/4" x 1'-8 1/2"	2'-6 1/2" x 6 1/4"	2'-5 1/4" · U

Scheme C (chosen): inner box 1'-6 1/4" deep, 5 1/2" high, 0 1/2" ply; notch 9 1/4" wide.

HARDWARE

Big drawer	Undermount runners, full extension, push-to-open. Its sides stop at 1'-1 1/2" to pass under the inner.
Inner drawer	Side-mounted runners 1'-3 1/4", full extension, on the carcass partitions at 1'-4 1/4"-1'-4 1/2". Independent.
Inner front	0 1/4" BWP, teak veneer both faces, top edge scooped for a finger. No handle.

NOTES

REVISION 2

Open the big drawer: the inner one stays put. Pull it and it comes out 1'-4 1/4" behind the big front, over the bottles — the tray in the kitchen drawer photographed.

Both are U-boxes. The waste pipe drops through their notches whichever drawer is shut; neither may be solid across the back.

It can never pass the big front — that front is solid. Shut, it stands 0 1/4" behind it.

Below the inner drawer: 1'-0 1/4" clear — tall bottles stand.

Normal version: the pipe is off centre, which leaves the inner drawer a 1" right arm. Too thin to keep — that arm is left off and the inner drawer is an L.

A STUDY IN TEAK

Particulars of the room


VANITY — DRAWER WITHIN

The big drawer, and a drawer inside it

SCALE AS NOTED @ A3	DATE 30.09.2026
REV 2 — scheme C: 5 1/2" in inner box, bank to the floor	DWG AST-DR-022


1 · CLOSED

SECTION THROUGH ONE ARM · SCHEME C, CHOSEN — BANK TO THE FLOOR

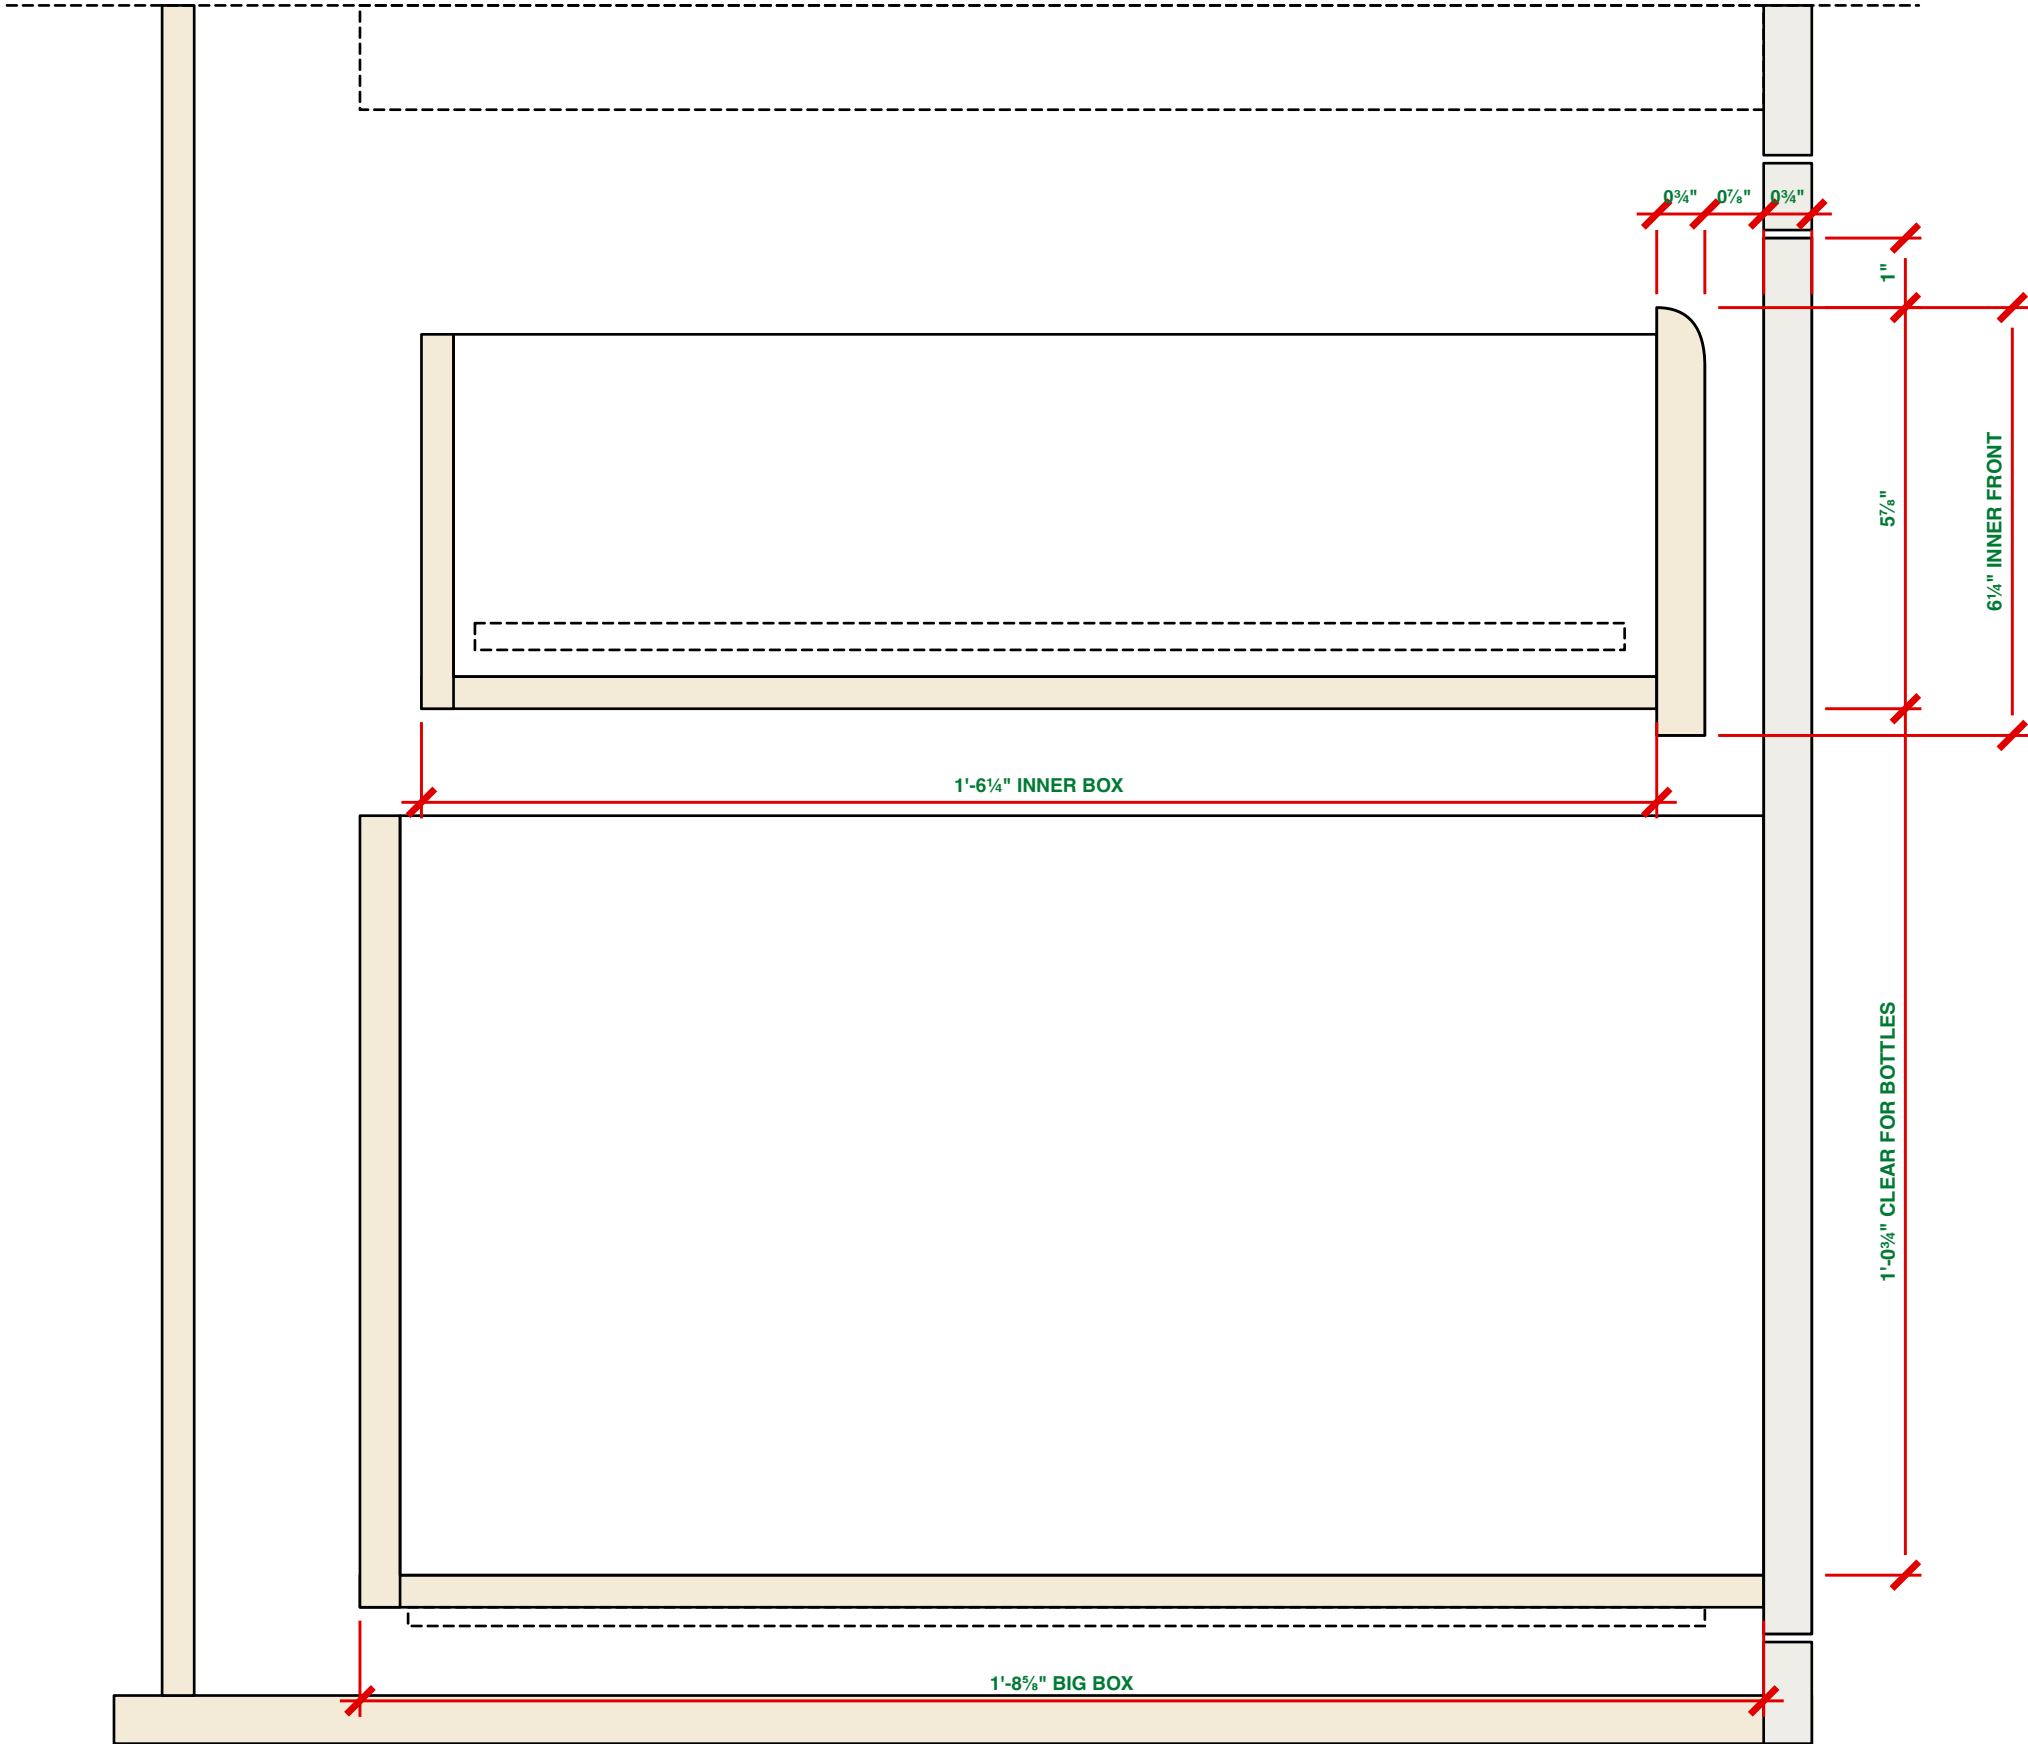

2 · OPEN

BIG DRAWER OUT · INNER ONE PULLED OUT BEHIND ITS FRONT

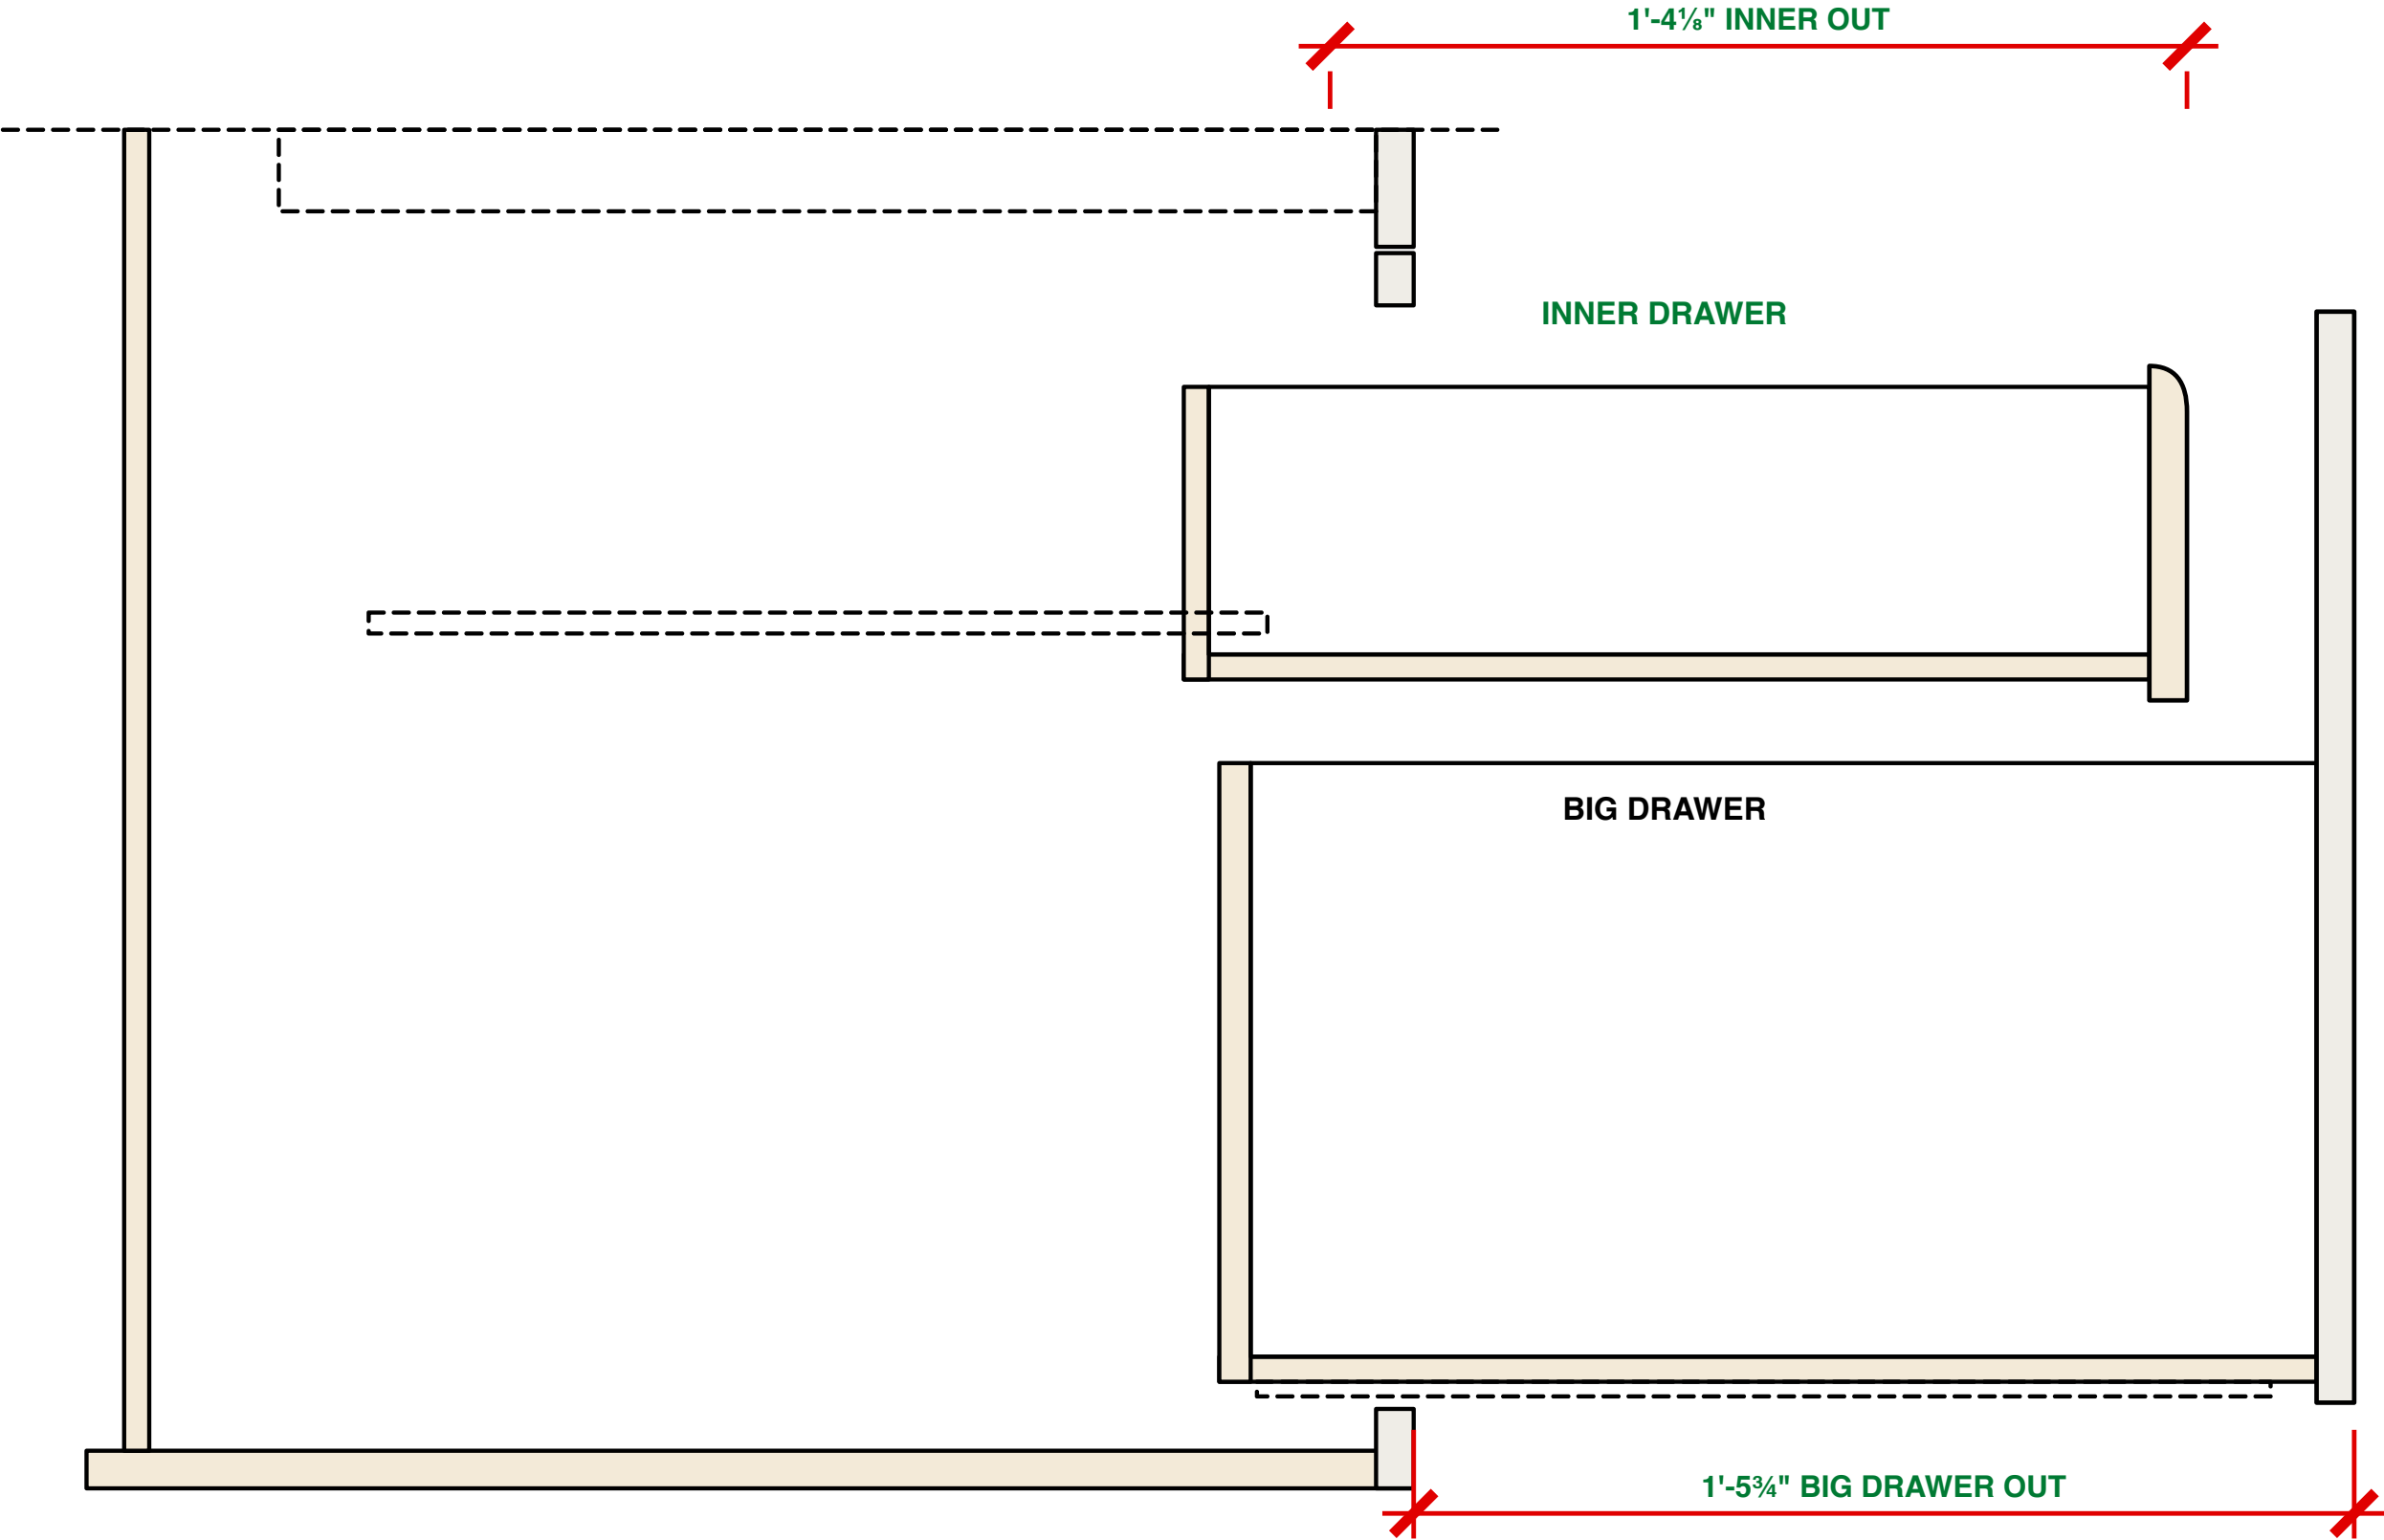

SIZES

THE SAME DRAWER IN ALL THREE SCHEMES

SCHEME	BIG FRONT	INNER FRONT	INNER BOX W
Normal	2'-2¾" × 1'-3¼"	2'-0⅝" × 3¾"	1'-11¾" · L
B	3'-8¾" × 1'-3¼"	3'-6⅝" × 3¾"	3'-5¾" · U
C	2'-8¾" × 1'-8½"	2'-6½" × 6¼"	2'-5¾" · U


Scheme C (chosen): inner box 1'-6¼" deep, 5½" high, 0½" ply; notch 9⅞" wide.

HARDWARE

Big drawer	Undermount runners, full extension, push-to-open. Its sides stop at 1'-1 ⁵ / ₈ " to pass under the inner.
Inner drawer	Side-mounted runners 1'-3 ³ / ₄ ", full extension, on the carcass partitions at 1'-4 ¹ / ₈ "–1'-4 ¹ / ₂ ". Independent.
Inner front	0 ³ / ₄ " BWP, teak veneer both faces, top edge scooped for a finger. No handle.

3 · PLAN

BOTH DRAWERS SHUT · THE PIPE DROPS THROUGH BOTH NOTCHES

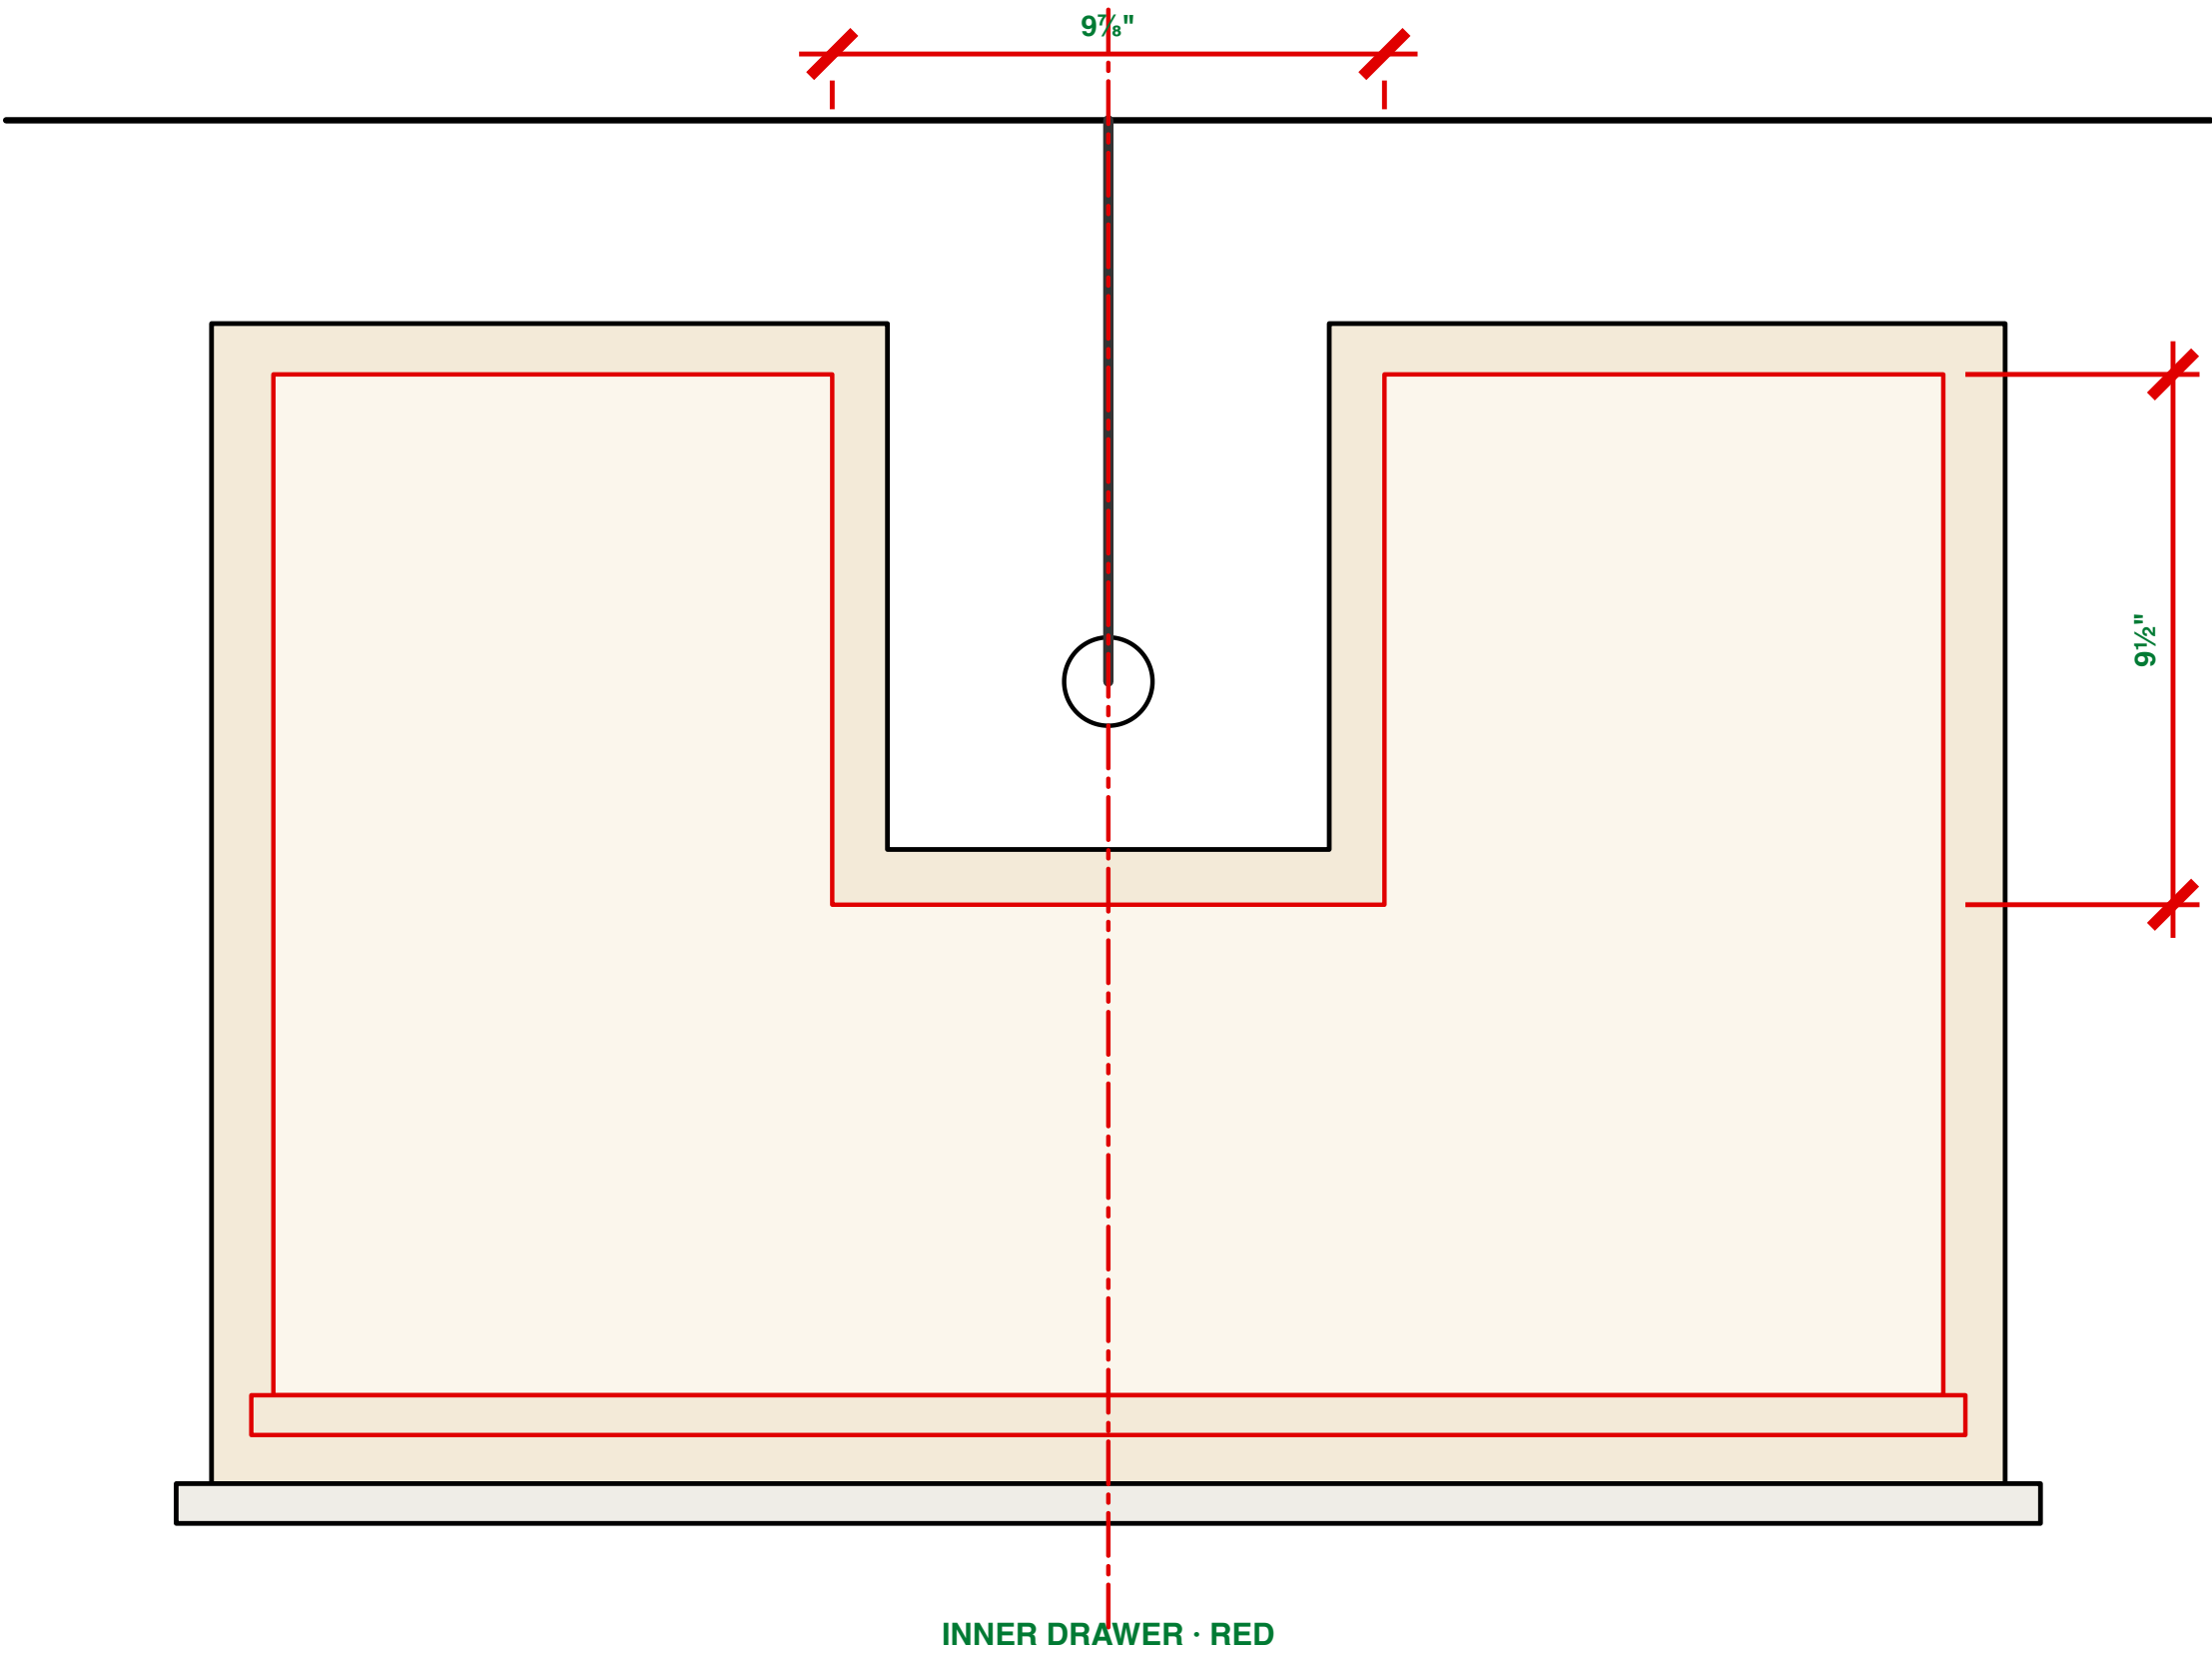

NOTES

REVISION 2

Open the big drawer: the inner one stays put. Pull it
and it comes out 1'-4¹/₈" behind the big front, over the
bottles — the tray in the kitchen drawer photographed.

Both are U-boxes. The waste pipe drops through their
notches whichever drawer is shut; neither may be solid
across the back.

It can never pass the big front — that front is solid.
Shut, it stands 0⁷/₈" behind it.

Below the inner drawer: 1'-0³/₄" clear — tall bottles stand.

Normal version: the pipe is off centre, which leaves
the inner drawer a 1" right arm. Too thin to keep — that
arm is left off and the inner drawer is an L.

4 · FRONT

THE INNER DRAWER HIDES BEHIND THE BIG FRONT · MARBLE BANK, FLOOR TO COUNTER

