



FRONT

MARBLE THE FULL 5 FT · THE BOWL SITS UNDER THE FAUCET, 6 IN RIGHT OF CENTRE

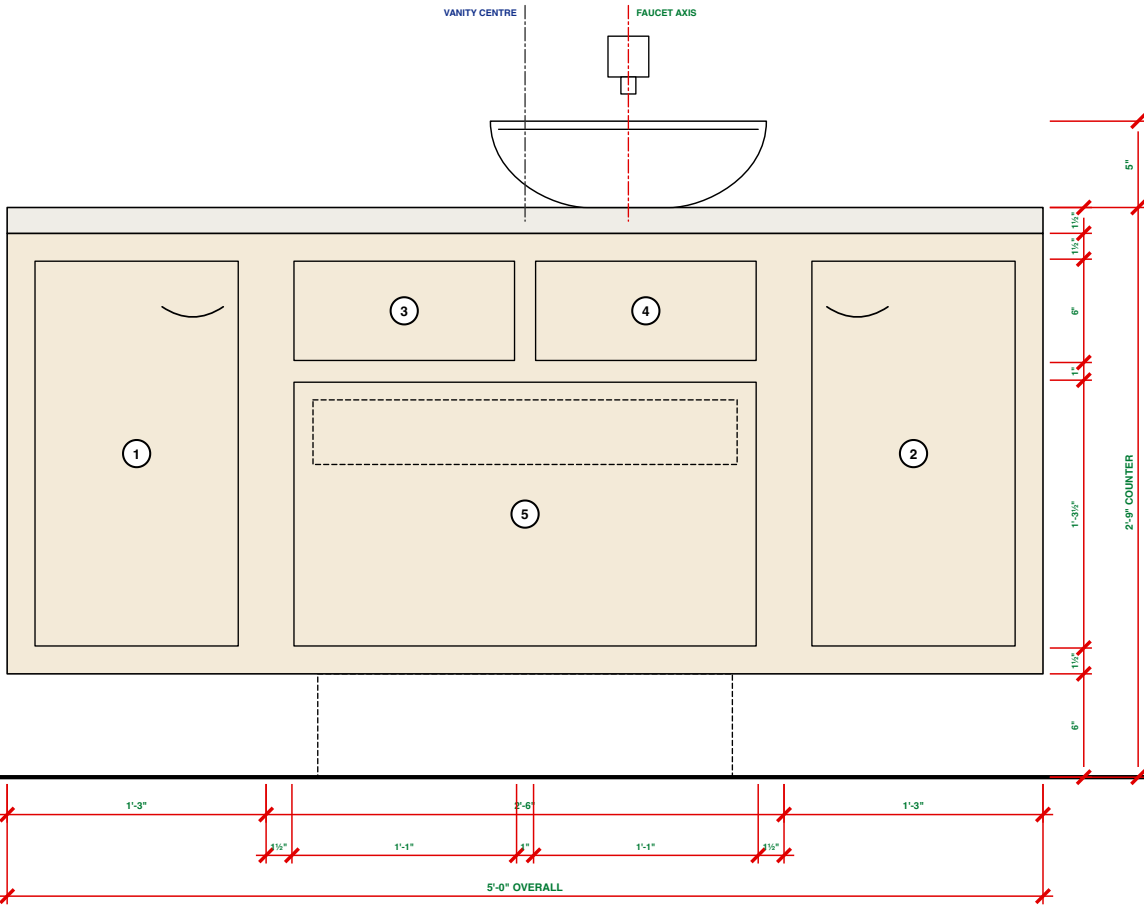

PLAN

FROM ABOVE · WALL AT THE TOP

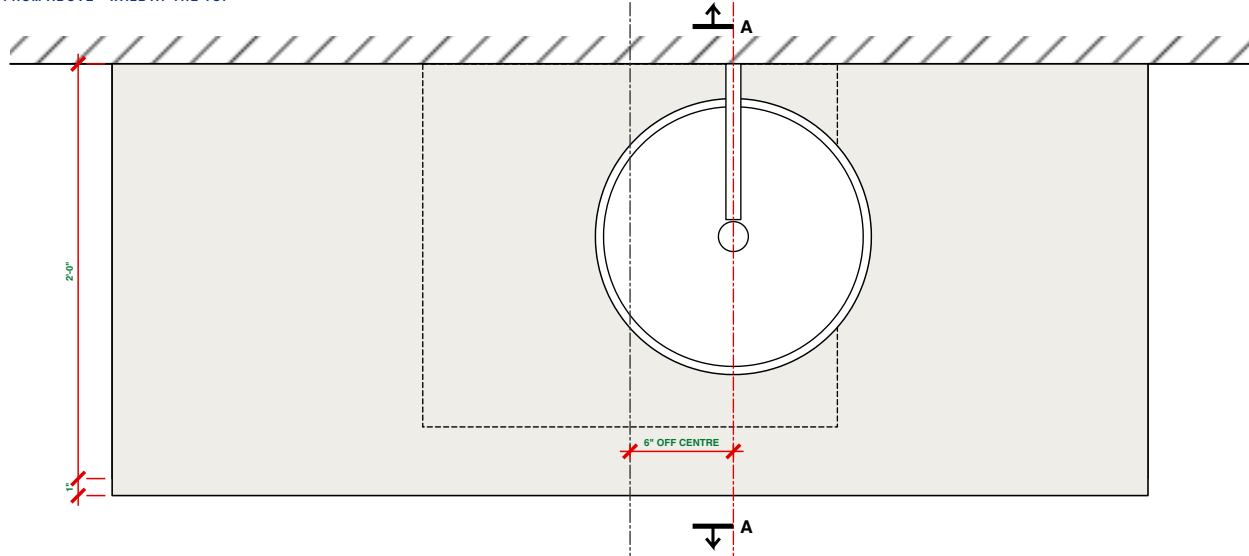

SECTION KEY

- (A) Hanging cleat
- (B) Big drawer, U-box
- (C) Waste Ø1½" and P-trap
- (D) Support, set back 3"
- (E) Wall spout
- (F) Ply sub-top
- (G) Inner drawer


NOTES

REVISION 1
Symmetric about the vanity's centre — except the bowl, which has to sit under the faucet, 6" right of it.
The waste drops through the right-hand TOP drawer as well as the big one: both are U-boxes (see section).

OPEN — bowl Ø1'-4" x 5" and the spout are assumed.
With the bowl on a 2'-9" counter its rim is at 3'-2".
OPEN — the support's design: reference photos to come.


SECTION A-A

ON THE FAUCET AXIS

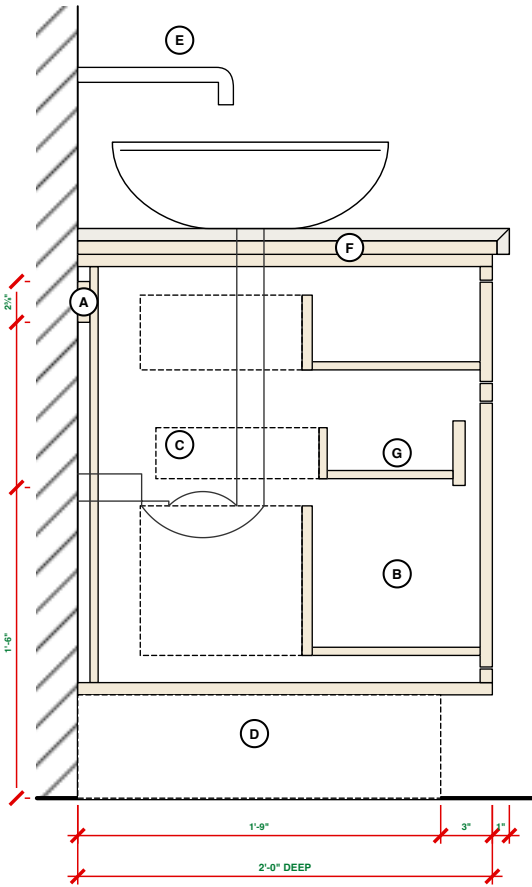


DETAIL 2 · THE BIG DRAWER

PLAN · INNER DRAWER DASHED

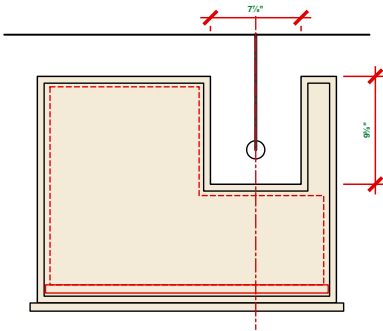

DETAIL 1 · THE MARBLE EDGE

SECTION

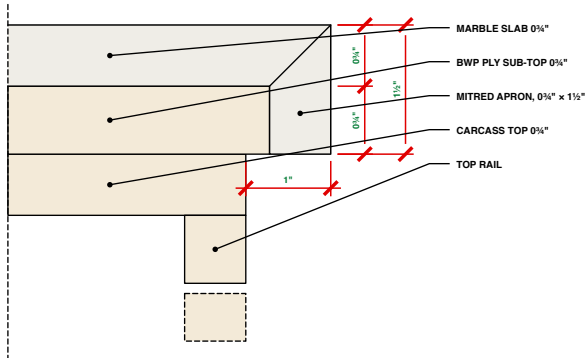

FRONTS

SIZES ARE THE FRONT ITSELF · 0½" GAP ALL ROUND

No.	WHAT	W x H	FT-IN
1	Door, cup pull	11½" x 1'-10¼"	11½" x 1'-10¼"
2	Door, cup pull	11½" x 1'-10¼"	11½" x 1'-10¼"
3	Top drawer, push-open	1'-0¾" x 5¾"	1'-0¾" x 5¾"
4	Top drawer, push-open	1'-0¾" x 5¾"	1'-0¾" x 5¾"
5	Big drawer, U-box, push-open	2'-2½" x 1'-3¼"	2'-2½" x 1'-3¼"
5a	Inner drawer, finger scoop	2'-0½" x 3¼"	2'-0½" x 3¼"

MATERIALS

THE ROOM'S PALETTE — NOTHING NEW

- Top: Beige-gold marble, the bathroom stone. 0¾" slab on a 0¾" BWP sub-top, mitred 1½" apron, polished.
- Carcass: 0¾" BWP / marine ply, teak veneer both faces. Every edge sealed — it stands in a wet room.
- Fronts: 0¾" BWP, teak veneer, 0¼" solid teak lippling.
- Runners: Undermount, full extension. Drawers push-to-open — no handles on them; the doors keep cup pulls.
- Fittings: Chrome — already bought. Door cup pulls to match.
- Hanging: 0¾" ply cleat on the wall, 2'-3½"-2'-5½" high.
- Inner: A U-box on its own runners, above the big drawer's low sides — see AST-DR-022.

A STUDY IN TEAK

Particulars of the room


VANITY — NORMAL

Marble full length · Door · Drawers · Door

SCALE AS NOTED @ A3	DATE 23.09.2026
REV 1 — as sketched	DWG AST-DR-019


FRONT

MARBLE THE FULL 5 FT · THE BOWL SITS UNDER THE FAUCET, 6 IN RIGHT OF CENTRE

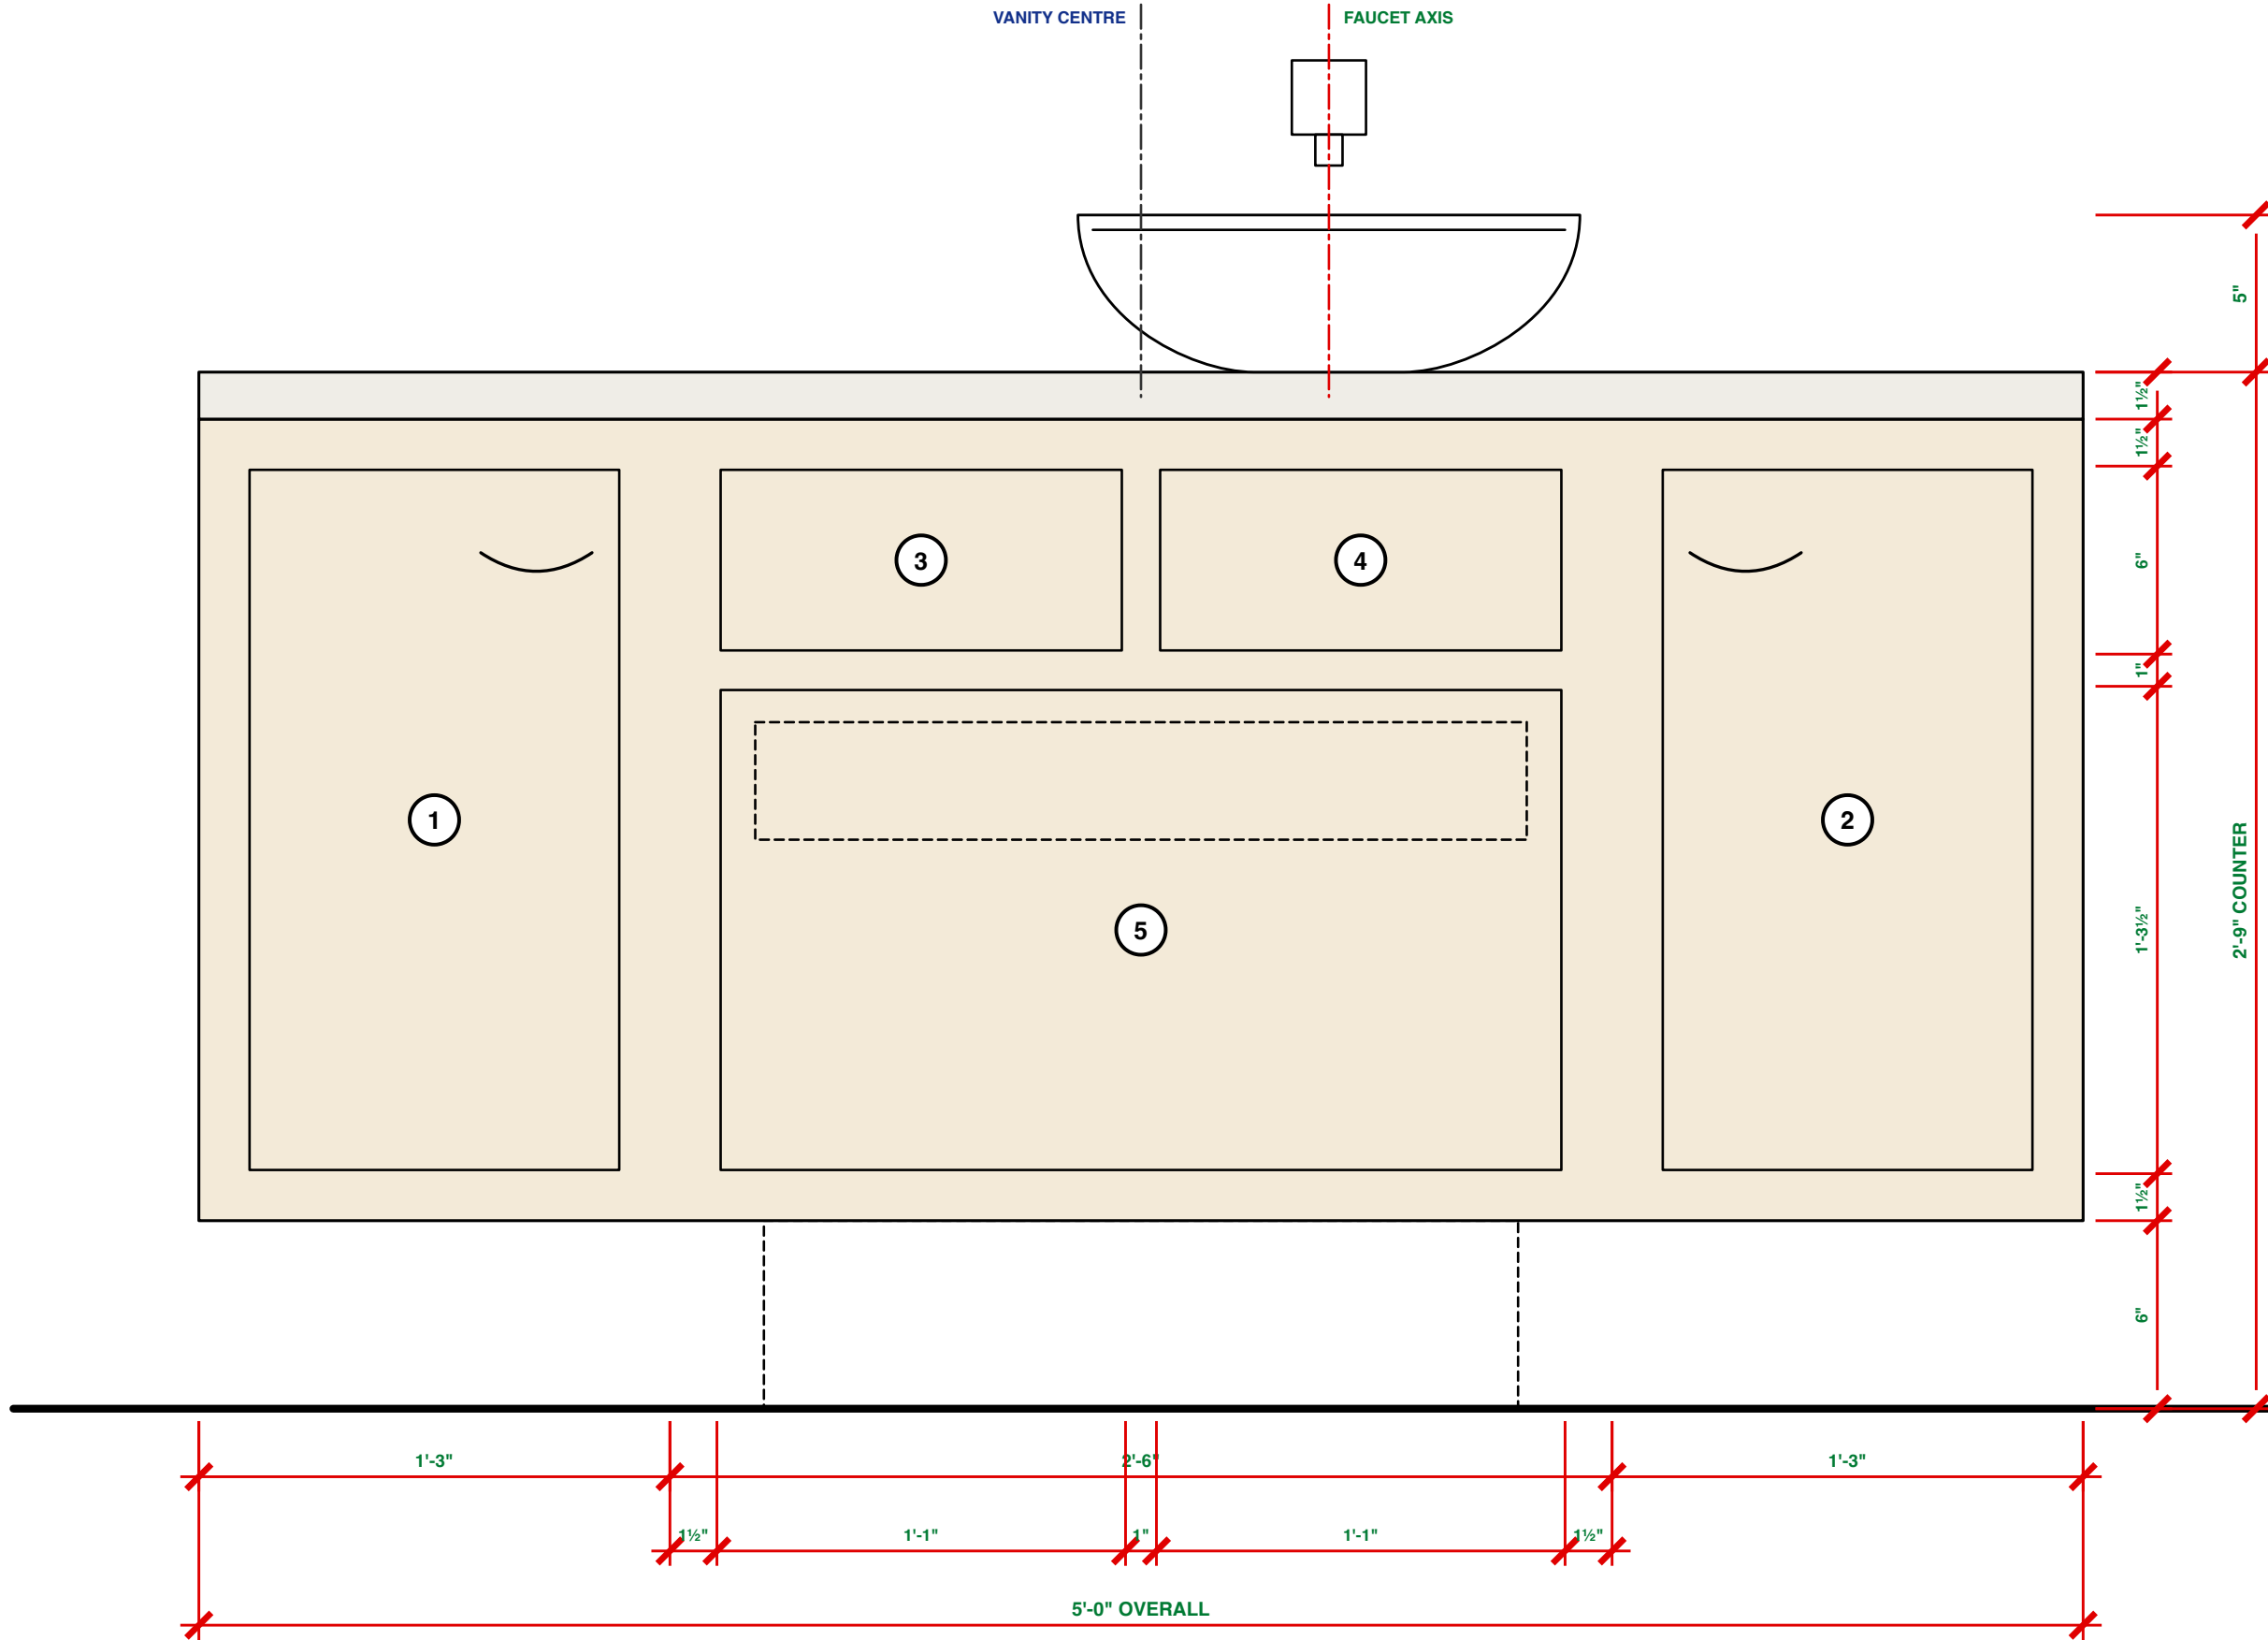


SECTION A-A

ON THE FAUCET AXIS

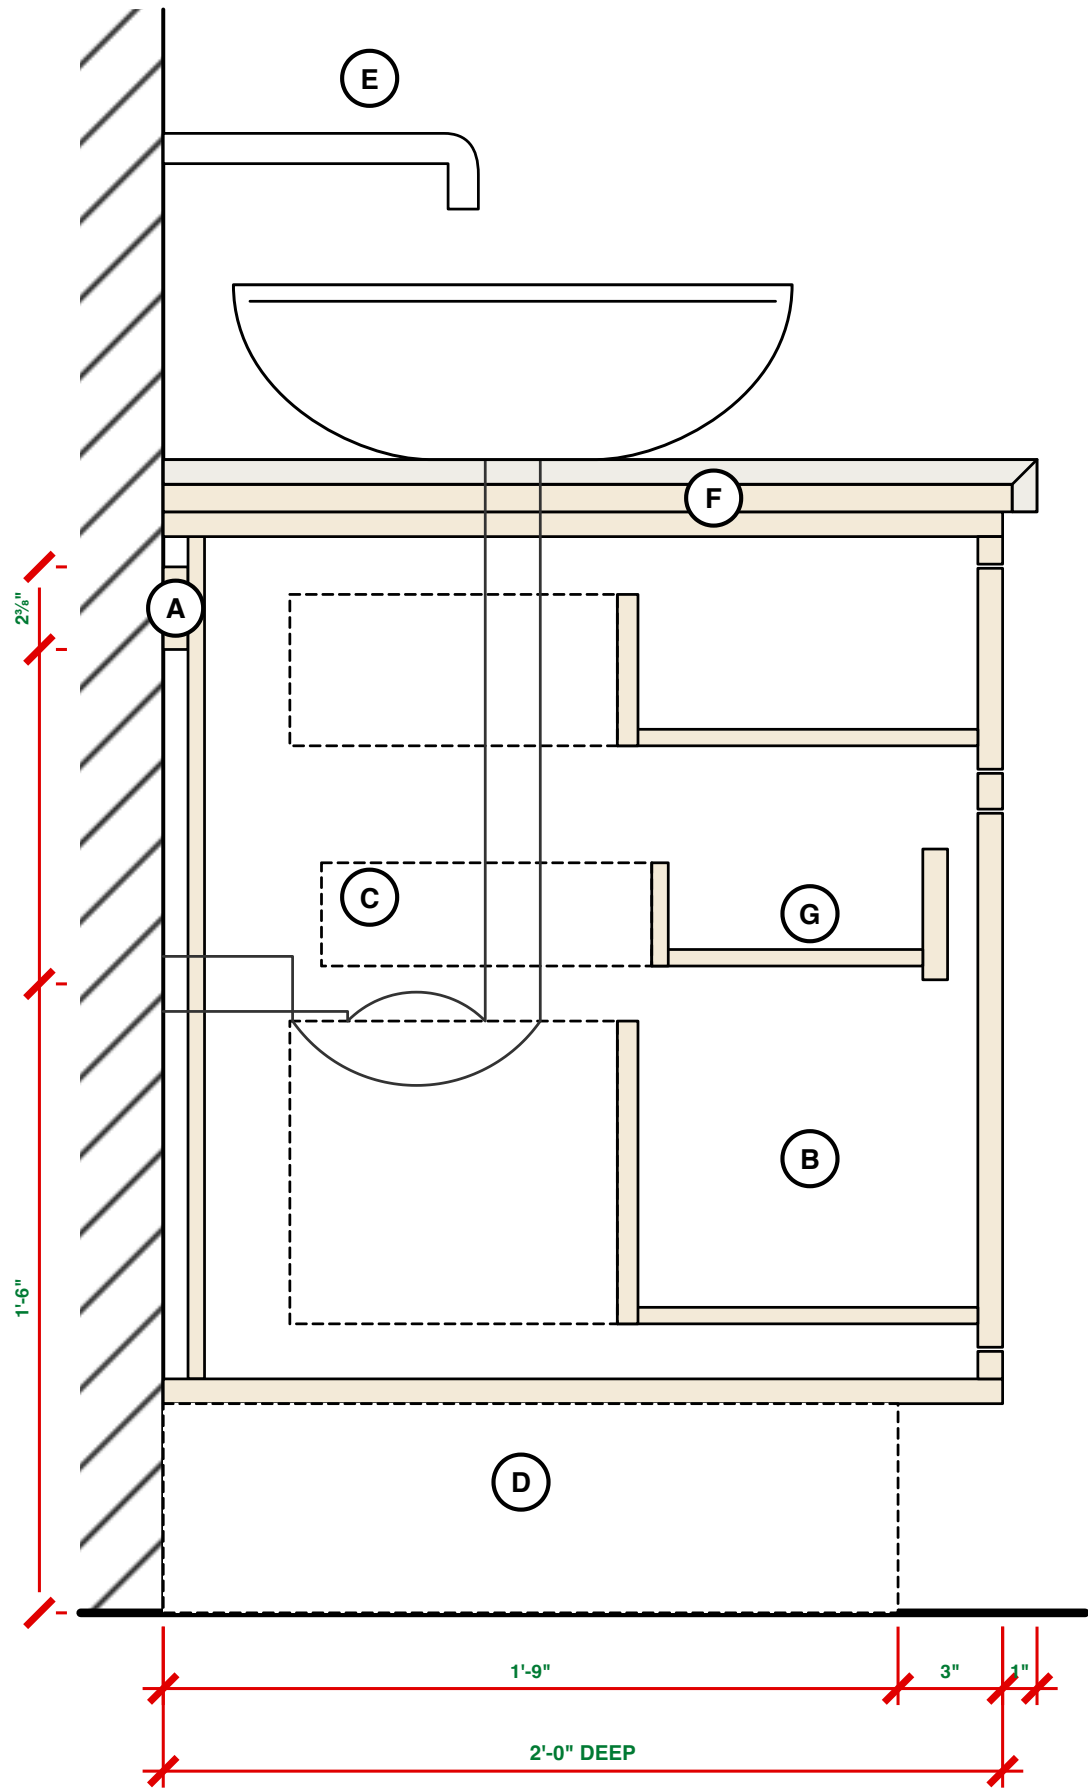

DETAIL 1 · THE MARBLE EDGE

SECTION

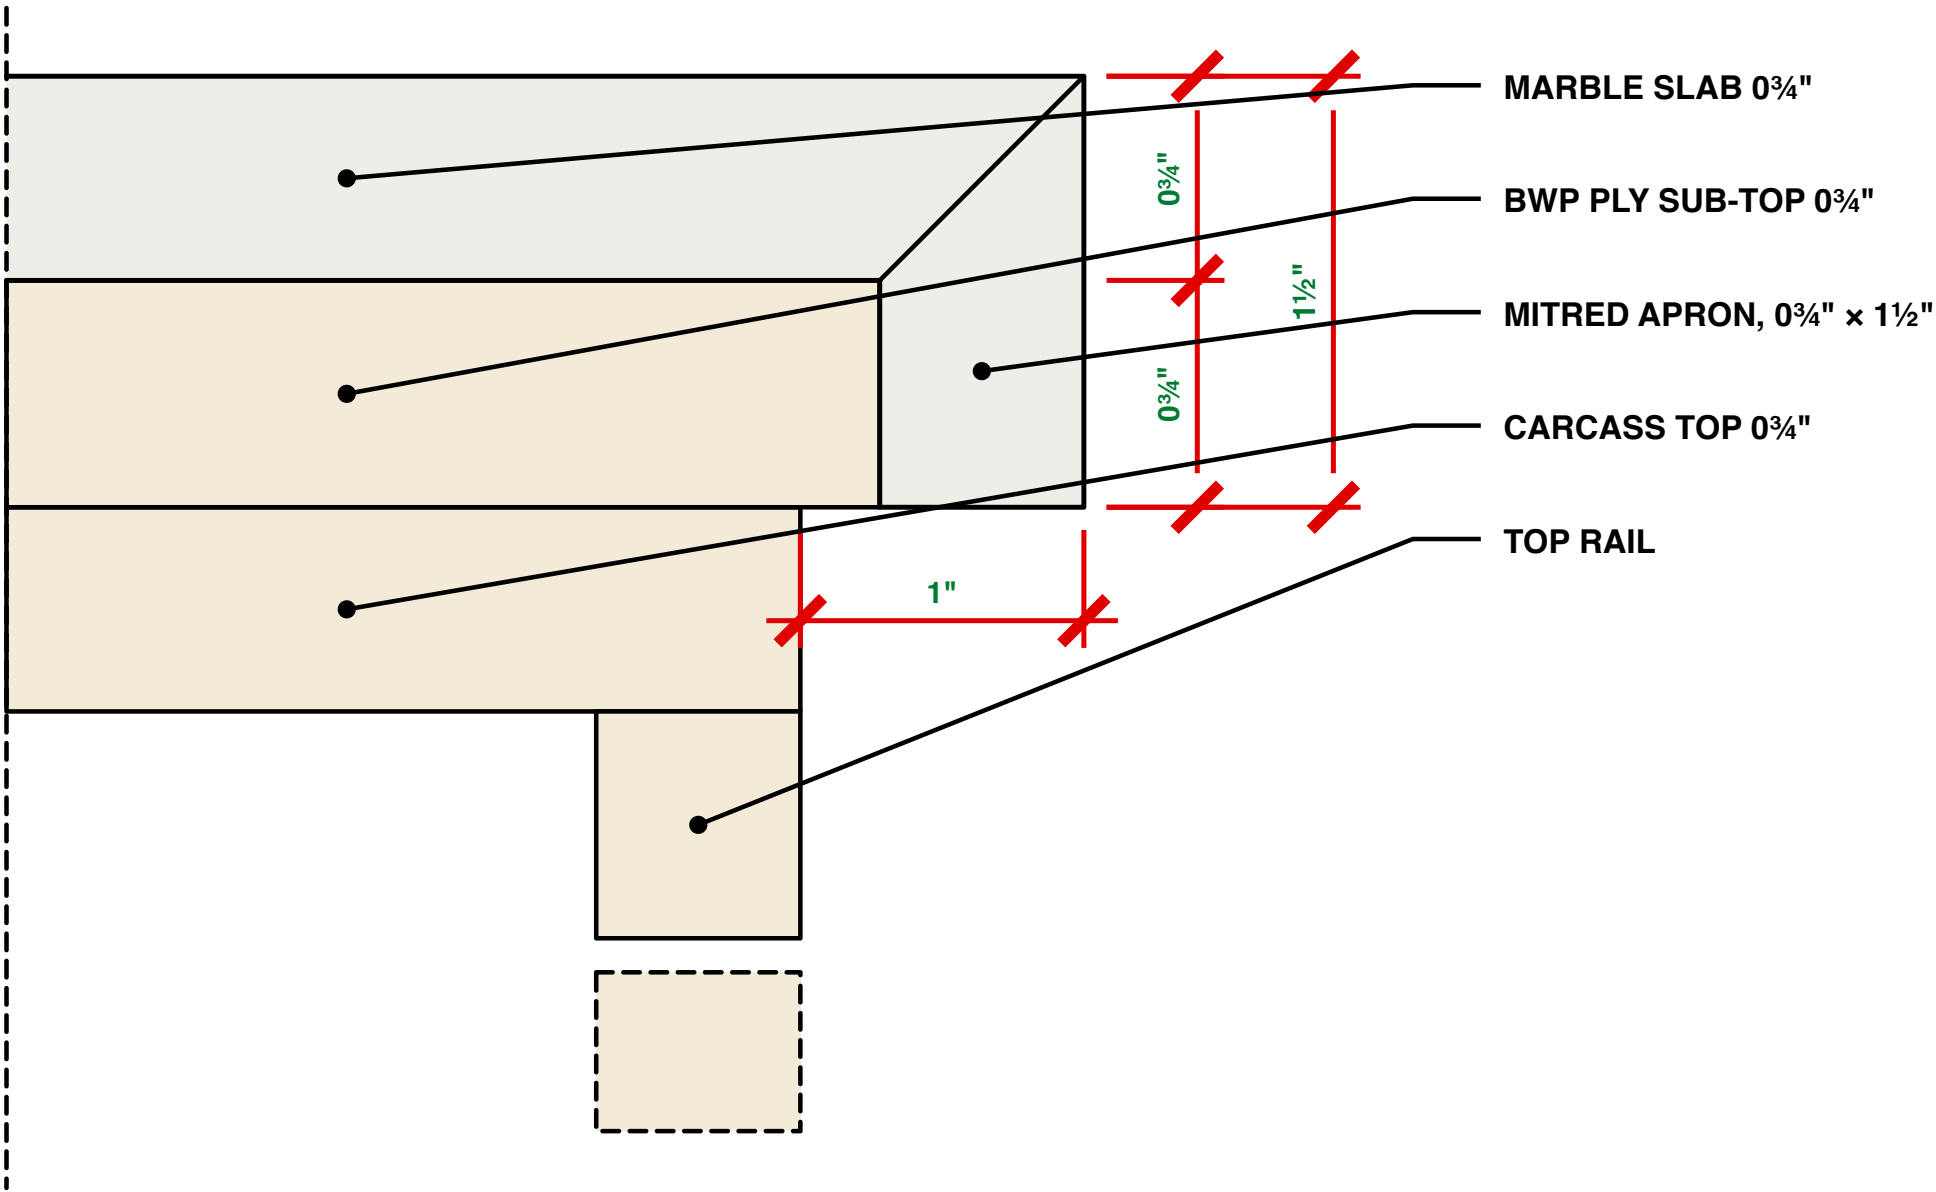

FRONTS

SIZES ARE THE FRONT ITSELF · 0 1⁄8" GAP ALL ROUND

No.	WHAT	W × H	FT-IN
1	Door, cup pull	11 3⁄4" × 1'-10 1⁄4"	11 3⁄4" × 1'-10 1⁄4"
2	Door, cup pull	11 3⁄4" × 1'-10 1⁄4"	11 3⁄4" × 1'-10 1⁄4"
3	Top drawer, push-open	1'-0 3⁄4" × 5 3⁄4"	1'-0 3⁄4" × 5 3⁄4"
4	Top drawer, push-open	1'-0 3⁄4" × 5 3⁄4"	1'-0 3⁄4" × 5 3⁄4"
5	Big drawer, U-box, push-open	2'-2 3⁄4" × 1'-3 1⁄4"	2'-2 3⁄4" × 1'-3 1⁄4"
5a	Inner drawer, finger scoop	2'-0 5⁄8" × 3 3⁄4"	2'-0 5⁄8" × 3 3⁄4"


MATERIALS

THE ROOM'S PALETTE — NOTHING NEW

Top	Beige-gold marble, the bathroom stone. 0¾" slab on a 0¾" BWP sub-top, mitred 1½" apron, polished.
Carcass	0¾" BWP / marine ply, teak veneer both faces. Every edge sealed — it stands in a wet room.
Fronts	0¾" BWP, teak veneer, 0¼" solid teak lipping.
Runners	Undermount, full extension. Drawers push-to-open — no handles on them; the doors keep cup pulls.
Fittings	Chrome — already bought. Door cup pulls to match.
Hanging	0¾" ply cleat on the wall, 2'-3½"—2'-5⅞" high.
Inner	A U-box on its own runners, above the big drawer's low sides — see AST-DR-022.


PLAN

FROM ABOVE · WALL AT THE TOP

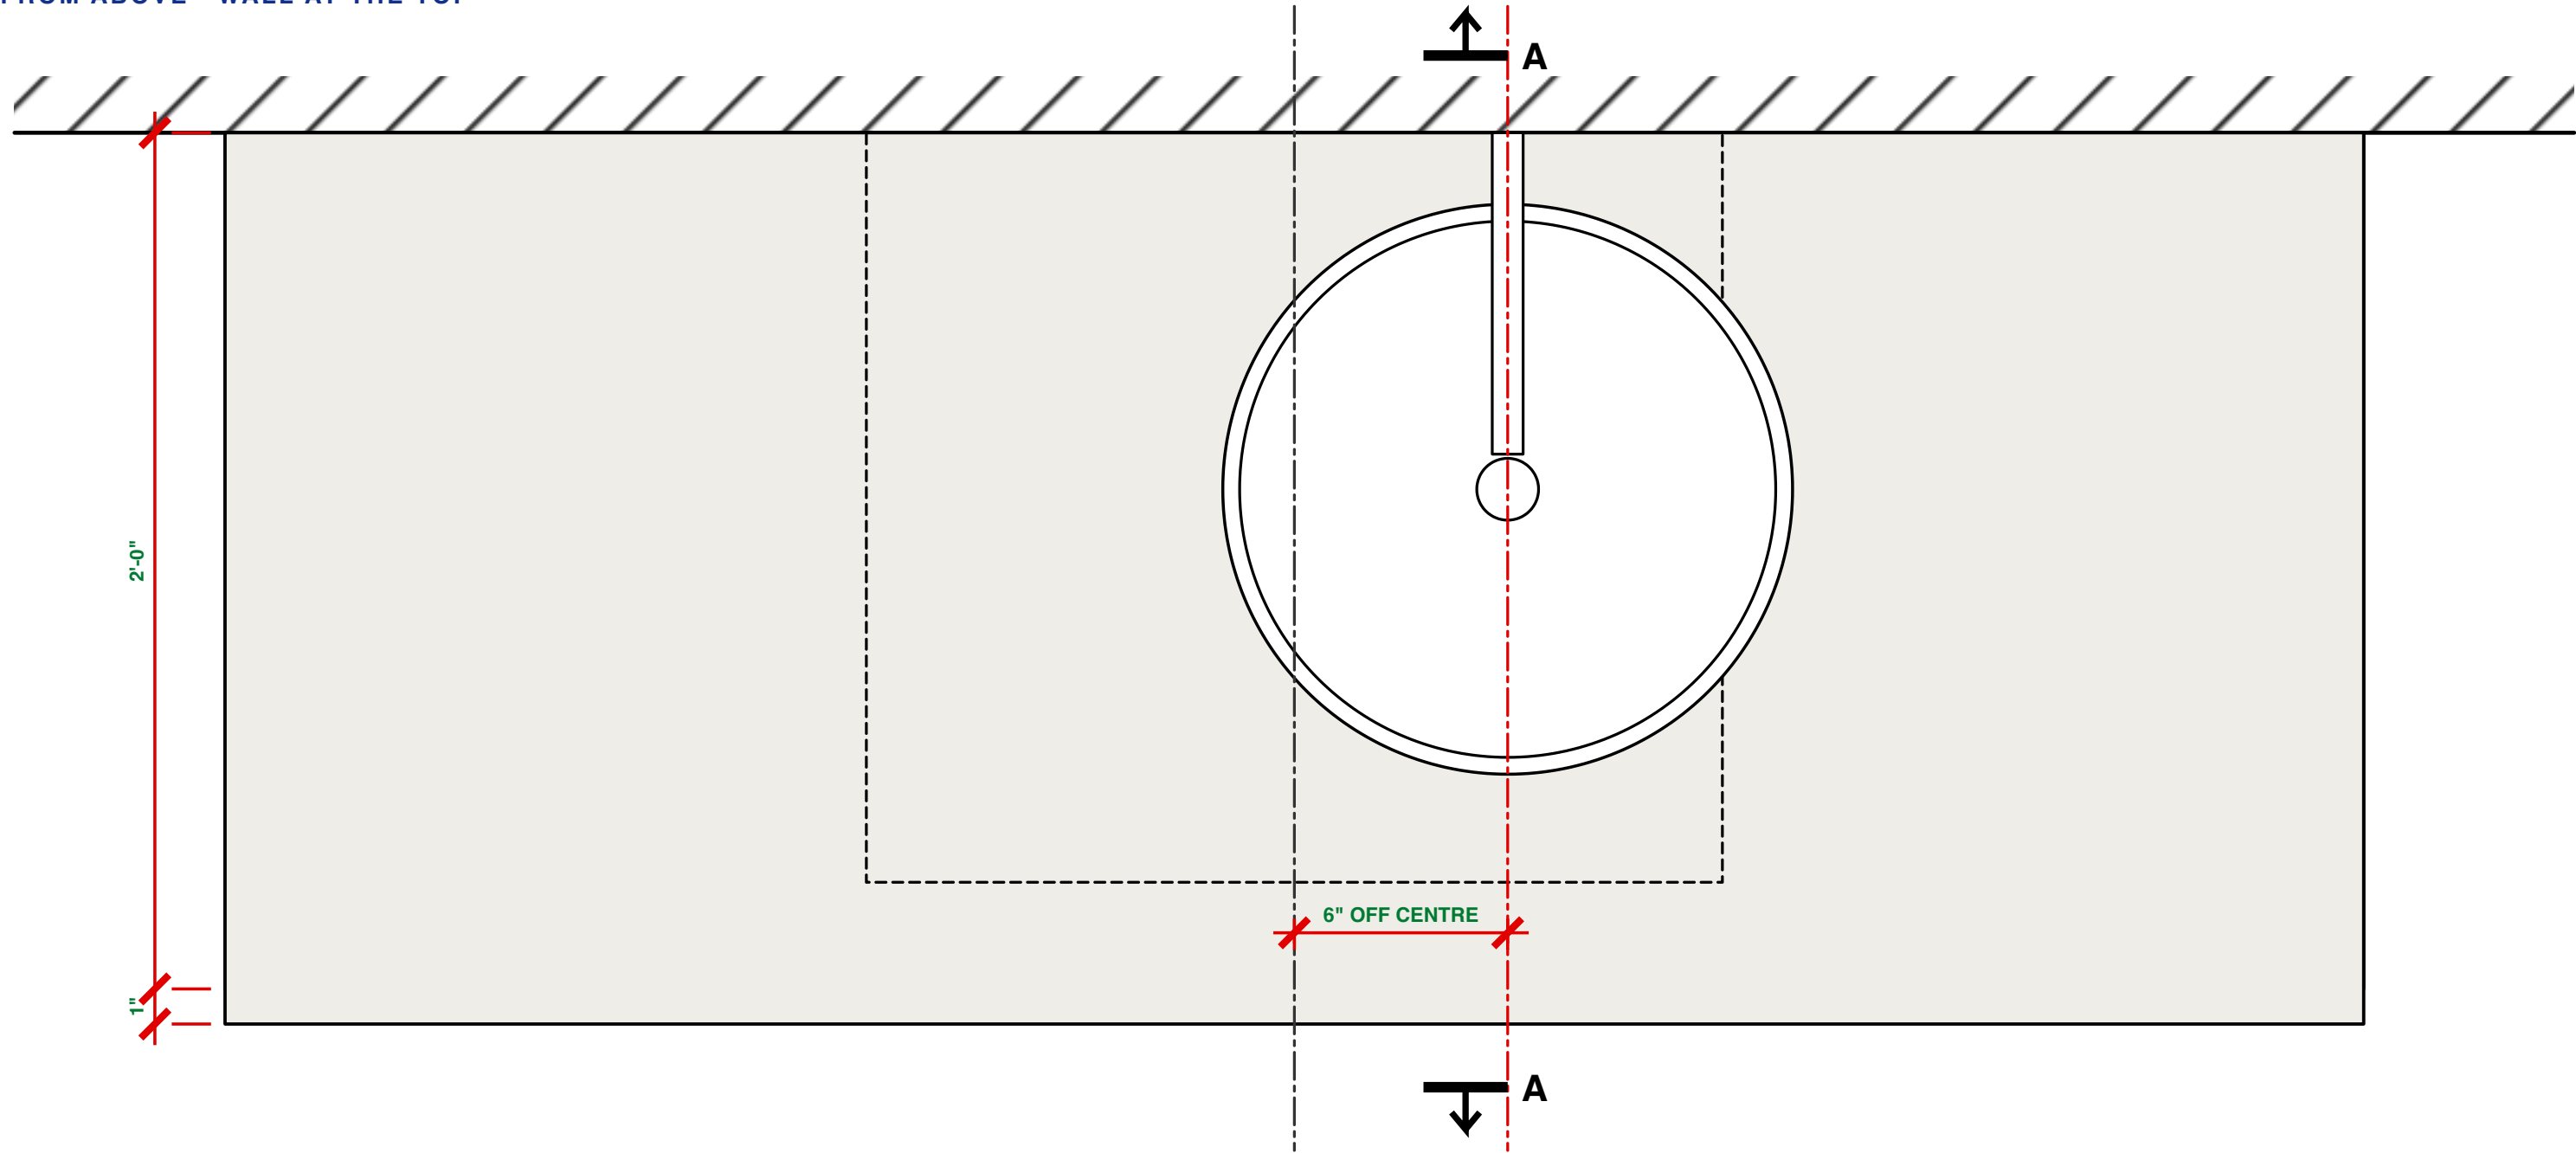

DETAIL 2 · THE BIG DRAWER

PLAN · INNER DRAWER DASHED

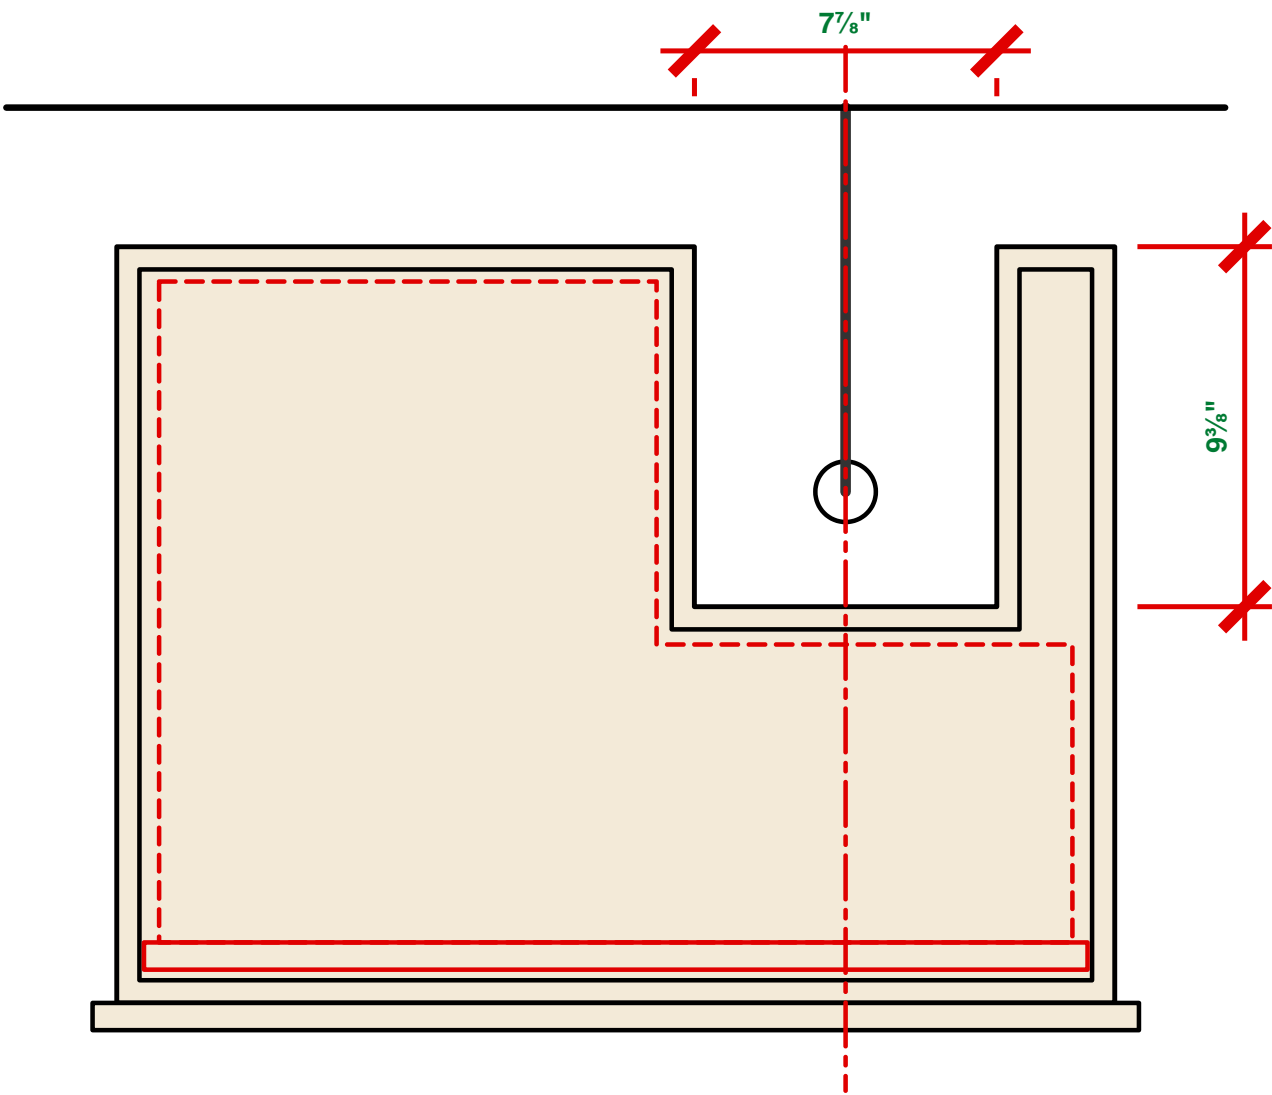

SECTION KEY

- A

Hanging cleat
- B

Big drawer, U-box
- C

Waste Ø1⁵/₈" and P-trap
- D

Support, set back 3"
- E

Wall spout
- F

Ply sub-top
- G

Inner drawer

NOTES

REVISION 1

Symmetric about the vanity's centre — except the bowl,

which has to sit under the faucet, 6" right of it.

The waste drops through the right-hand TOP drawer as

well as the big one: both are U-boxes (see section).

OPEN — bowl Ø1'-4" × 5" and the spout are assumed.

With the bowl on a 2'-9" counter its rim is at 3'-2".

OPEN — the support's design: reference photos to come.