



ELEVATION — THE BED WALL

SEEN FROM THE ROOM - DRESSING CORNER LEFT, ENTRANCE CORNER RIGHT

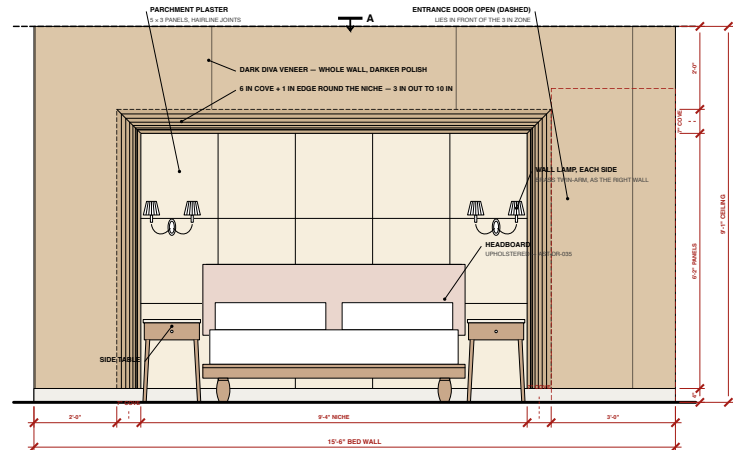

PLAN

CUT AT 4 FT - THE BED WALL AT THE TOP, THE ROOM BELOW

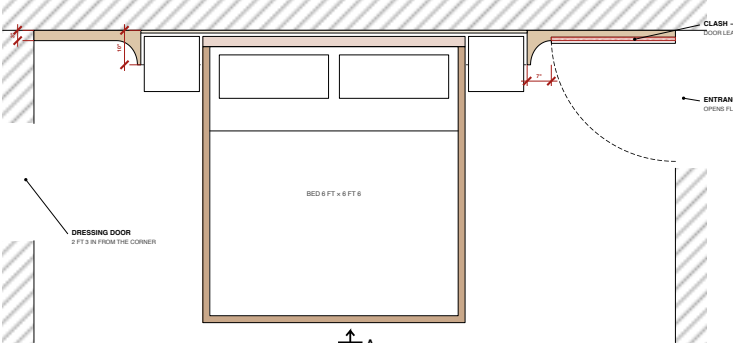


NOTES

REVISION 3

From the owner's sketches and photo. The whole wall is built out 3 in in Dark Diva veneer, polished darker, on a ply carcass. Round the niche it sweeps forward in a 6 in concave cove to 10 in at the niche's edge — up both sides and across the top. The niche — bed end both tables — is 10 in deep, in parchment plaster, 5 x 3 panels. The build-out is set square to the bed's centre line and scribed at both corners, so it also hides the room's 2 in splay. The niche is the old bed-back span, centred on the TV; the cove stops where the open door's lead ends. Cove light in the ceiling. Headboard: dusty-rose suede (owner). A brass twin-arm wall lamp over each table. The bed is drawn on AST-DR-035.

SECTION A-A

THROUGH THE BED

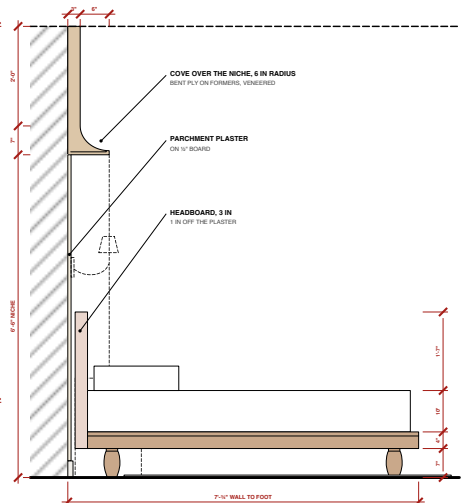

ASSUMED

TELL ME IF ANY OF THESE IS WRONG

Niche 9 ft 4 in wide — the old bed-back span (you said 2 ft 6 in). Five panels across and three up, as sketched: each about 1 ft 10 1/2 in x 2 ft 1/2 in — nearly square. The 4 in white marble skirting runs along the build-out and into the niche. The build-out runs to the ceiling. Side tables 1/2 in x 1/2 in, 1 in high (from the photo). Bed and headboard heights: AST-DR-035.


PROBLEMS FOUND

TO DECIDE

1. DOOR — not its 3 ft, which is kept clear, but the DEPTH: DT's hinge pin is 2 in off this wall, so a 3 in face there stops it opening flat (detail 2). Projecting hinges (A), or 1 1/2 in deep at that corner (B).
 2. The bed comes 4 in further out (headboard + frame) 2 ft 0 1/2 in left to the TV drawers instead of 2 ft 0 1/2 in.
 3. Lamp sockets and switches go through the plaster panels — to their places (flat item B2) before the panels are made.
- DECIDED: the cove light stays in the ceiling; no other light on this wall but the two wall lamps over the side tables (over).

DETAIL 2 · THE ENTRANCE CORNER

NEAR THE DOOR VS THE 3 IN FACE

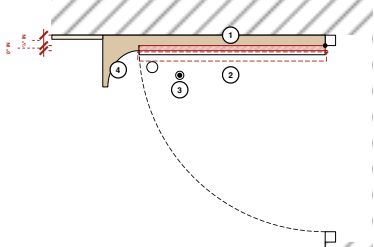

1. AS SKETCHED — the open leaf into the 3 in face: its hinge pin stands only 2 in off the wall (red).
2. FIX A — projecting (parchment) hinges throw the pin out 1 1/2 in; the leaf clears and still opens flat (dashed).
3. Floor stop — keeps the knob off the veneer.
4. FIX B — 1 1/2 in at this corner instead of 3 in: ordinary hinges clear.

A STUDY IN TEAK

Particulars of the room

BED WALL — THE NICHE

Elevation · Plan · Section · The entrance corner

SCALE

AS NOTED @ A3

DATE

03.10.2026

REV

3

DWG

AST-DR-034

PROJECT
A Study in Teak — Bed Wall — the Niche

SHEET
General arrangement — the whole sheet
each view follows at its own scale, pages 2 to 8

SCALE
NTS



DATE
03.10.2026

REV
3

DRAWING
AST-DR-034 · 1 of 8

ELEVATION — THE BED WALL

SCALE 1:30 @ A4 · SEEN FROM THE ROOM · DRESSING CORNER LEFT, ENTRANCE CORNER RIGHT

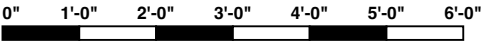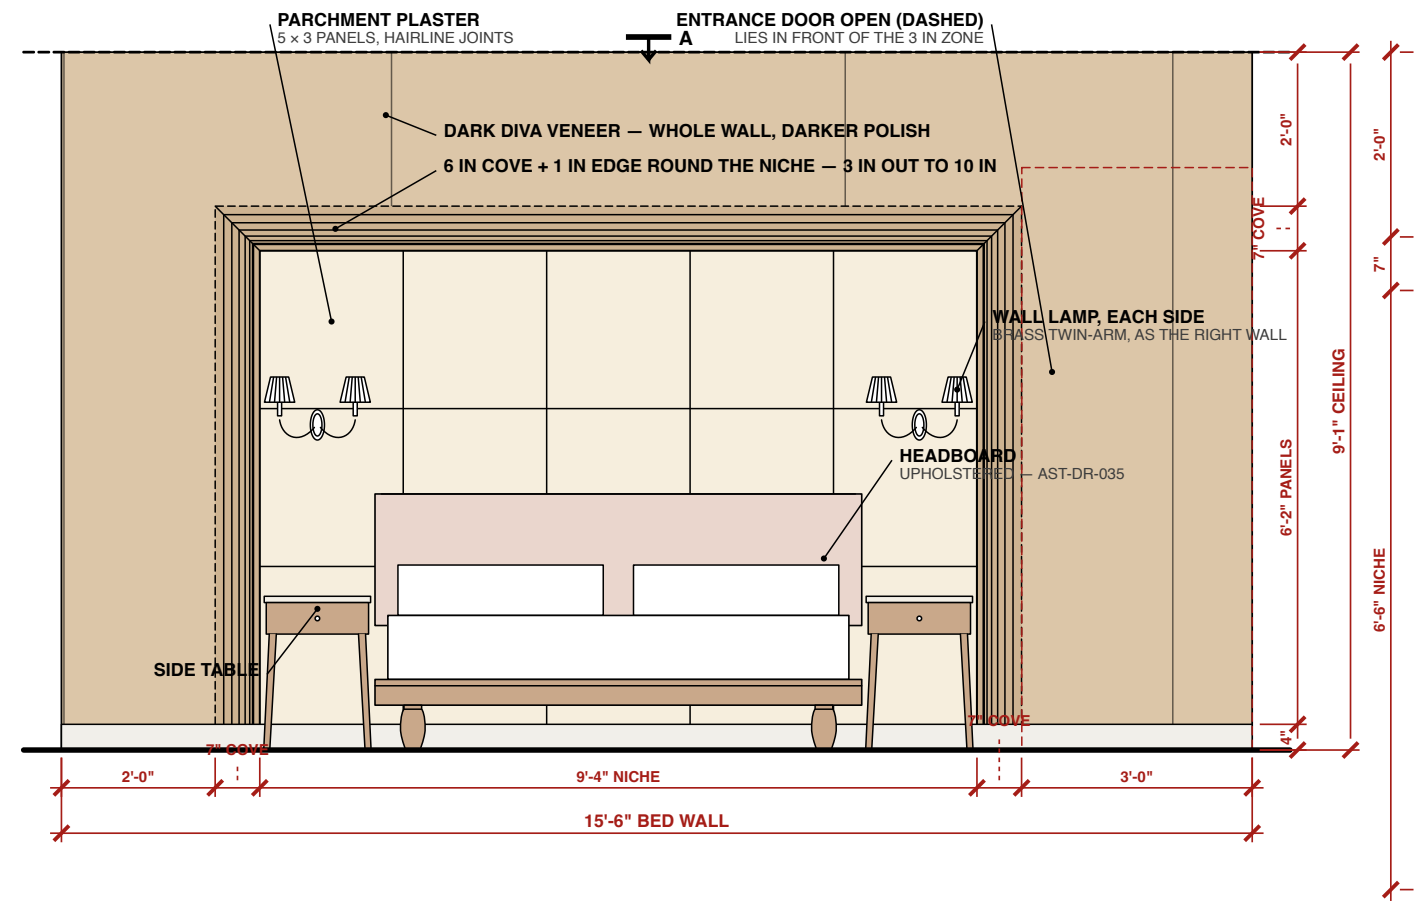

PROJECT
A Study in Teak — Bed Wall — the Niche

SHEET
Elevation — the bed wall
Elevation · Plan · Section · The entrance corner

SCALE
1:30 @ A4


DATE
03.10.2026

REV
3

DRAWING
AST-DR-034 · 2 of 8

SECTION A-A

SCALE 1:24 (1/2" = 1'-0") @ A4 · THROUGH THE BED

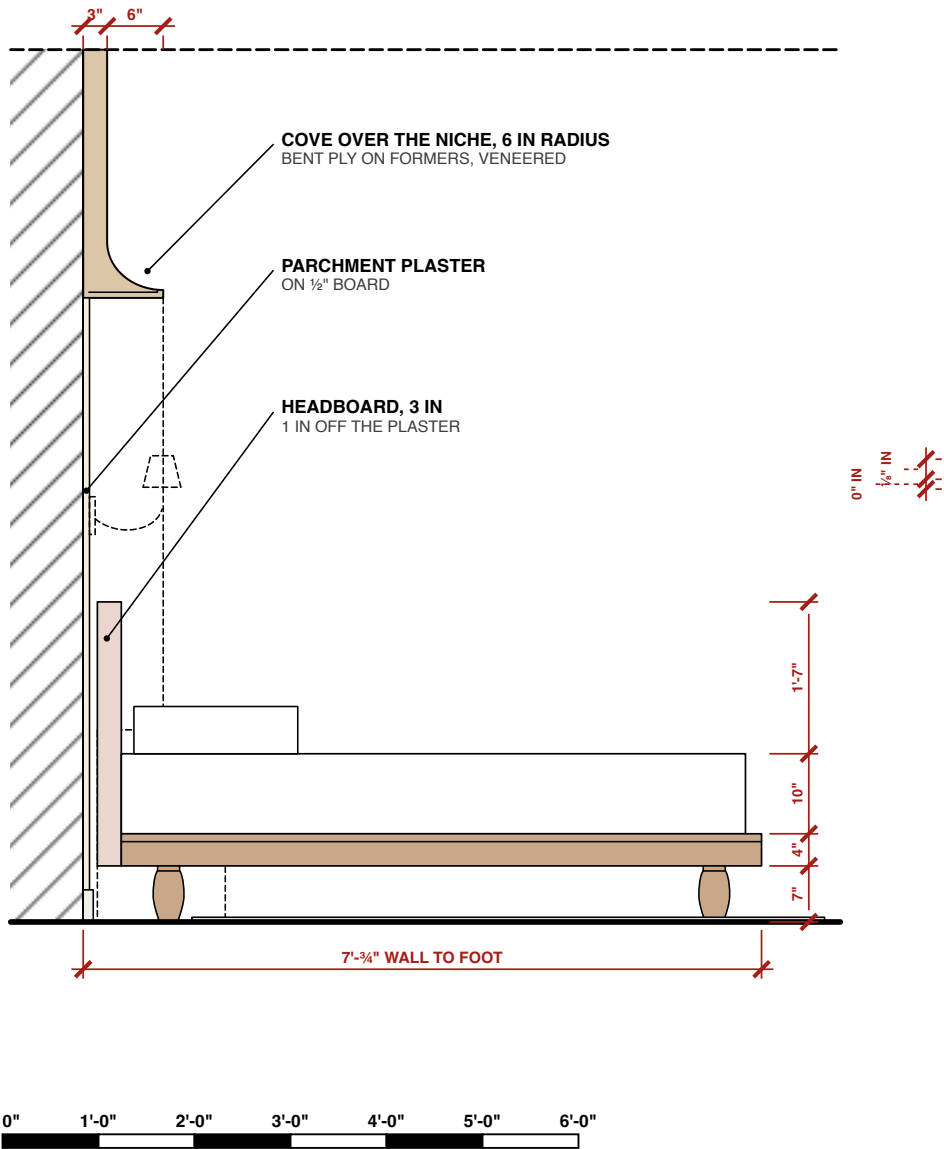

PROJECT
A Study in Teak — Bed Wall — the Niche

SHEET
Section A-A
Elevation · Plan · Section · The entrance corner

SCALE
1:24 @ A4

DATE
03.10.2026

REV
3

DRAWING
AST-DR-034 · 3 of 8

PROBLEMS FOUND

TO DECIDE

1 · DOOR — not its 3 ft, which is kept clear, but the DEPTH: D1's hinge pin

is 2 in off this wall, so a 3 in face there stops it opening flat (detail 2).

Projecting hinges (A), or 1½ in deep at that corner (B).

2 · The bed comes 4½ in further out (headboard + frame): 2 ft 5½ in left

to the TV drawers instead of 2 ft 9¾ in.

3 · Lamp sockets and switches go through the plaster panels — fix their

places (list item B2) before the panels are made.


DECIDED: the cove light stays in the ceiling; no other light on this wall

but the two wall lamps over the side tables (owner).


PROJECT	SHEET	SCALE	DATE	REV	DRAWING
A Study in Teak — Bed Wall — the Niche	Problems found Elevation · Plan · Section · The entrance corner	NTS	03.10.2026	3	AST-DR-034 · 4 of 8

DETAIL 2 · THE ENTRANCE CORNER

SCALE 1:15 @ A4 · PLAN · THE DOOR vs THE 3 IN FACE

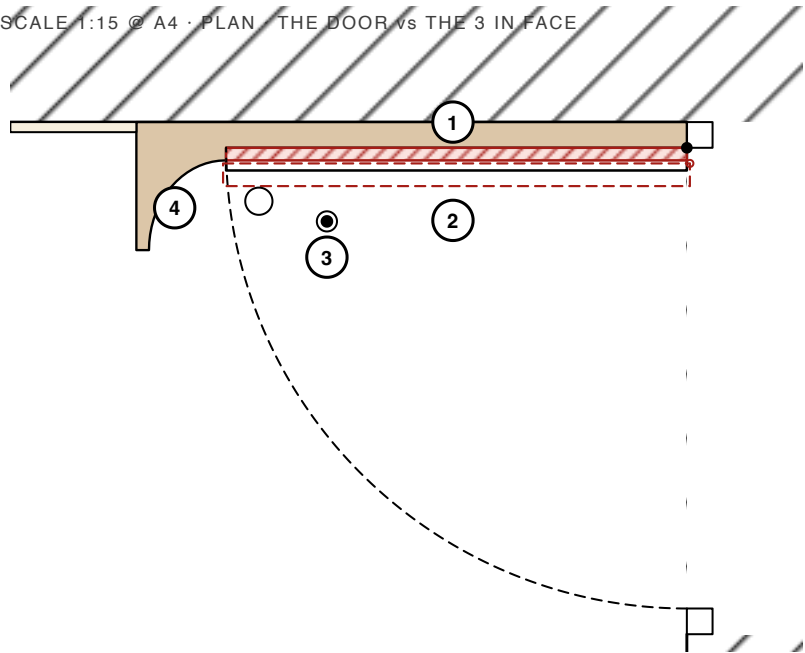



- 1 AS SKETCHED — the open leaf hits the 3 in face: its hinge pin stands only 2 in off the wall (red).
- 2 FIX A — projecting (parliament) hinges throw the pin out 1½ in; the leaf clears and still opens flat (dashed).
- 3 Floor stop — keeps the knob off the veneer.
- 4 FIX B — 1½ in at this corner instead of 3 in: ordinary hinges clear.

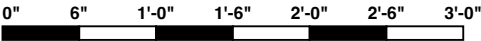

PROJECT	SHEET	SCALE	DATE	REV	DRAWING
A Study in Teak — Bed Wall — the Niche	Detail 2 · the entrance corner Elevation · Plan · Section · The entrance corner	1:15 @ A4	03.10.2026	3	AST-DR-034 · 5 of 8

PLAN

SCALE 1:24 (1/2" = 1'-0") @ A4 · CUT AT 4 FT · THE BED WALL AT THE TOP, THE ROOM BELOW

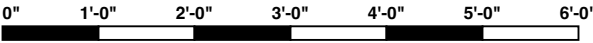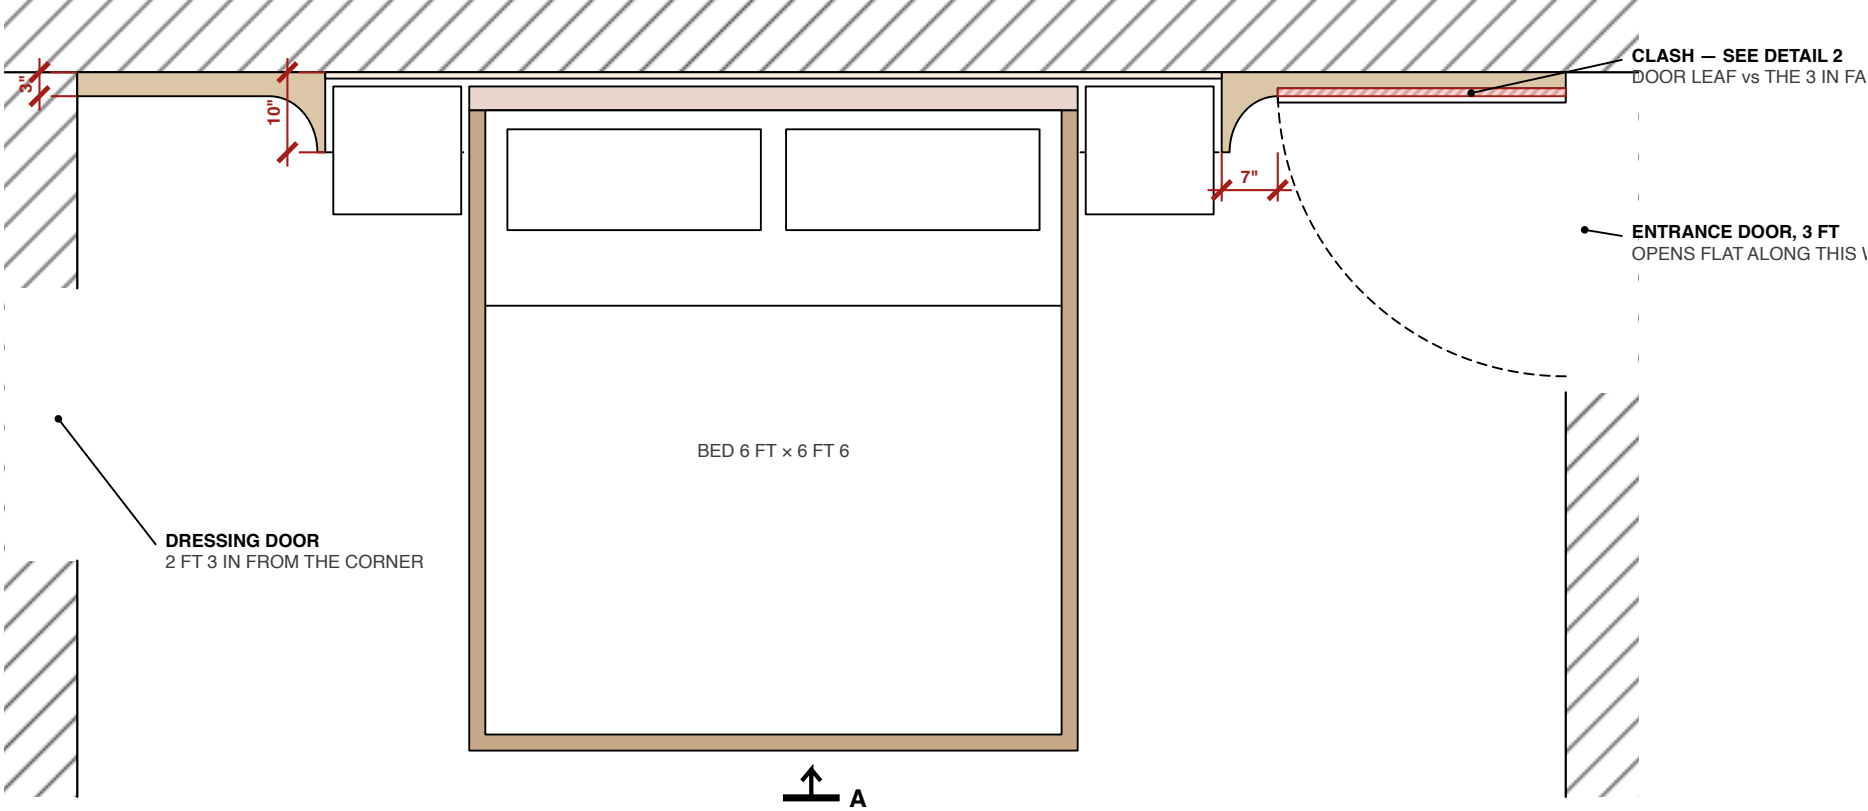

PROJECT	SHEET	SCALE	DATE	REV	DRAWING
A Study in Teak — Bed Wall — the Niche	Plan Elevation · Plan · Section · The entrance corner	1:24 @ A4	03.10.2026	3	AST-DR-034 · 6 of 8

ASSUMED

TELL ME IF ANY OF THESE IS WRONG

Niche 9 ft 4 in wide — the old bed-back span (you said 9 ft 6 in).

Five panels across and three up, as sketched:

each about 1 ft 10³/₈ × 2 ft ⁵/₈ in — nearly square.

The 4 in white marble skirting runs along the build-out
and into the niche.

The build-out runs to the ceiling.

Side tables ⁵/₈" × ⁵/₈" in, 1" in high (from the photo).

Bed and headboard heights: AST-DR-035.

PROJECT A Study in Teak — Bed Wall — the Niche	SHEET Assumed Elevation · Plan · Section · The entrance corner	SCALE NTS	DATE 03.10.2026	REV 3	DRAWING AST-DR-034 · 7 of 8
---	--	--------------	--------------------	----------	--------------------------------

NOTES

REVISION 3

From the owner's sketches and photo. The whole wall is built out 3 in in Dark Diva veneer, polished darker, on a ply carcase. Round the niche it sweeps forward in a 6 in concave cove to 10 in at the niche's edge — up both sides and across the top.

The niche — bed and both tables — is 10 in deep, in parchment plaster, 5 × 3 panels.

The build-out is set square to the bed's centre line and scribed at both corners, so it also hides the room's 2 in splay. The niche is the old bed-back span, centred on the TV; the cove stops where the open door's leaf ends. Cove light: in the ceiling.

Headboard: dusty-rose suede (owner). A brass twin-arm wall lamp over each table.

The bed is drawn on AST-DR-035.

PROJECT	SHEET	SCALE	DATE	REV	DRAWING
A Study in Teak — Bed Wall — the Niche	Notes Elevation · Plan · Section · The entrance corner	NTS	03.10.2026	3	AST-DR-034 · 8 of 8