

SEEN FROM THE ROOM - DRESSING CORNER LEFT, ENTRANCE CORNER RIGHT



CUT AT 4 FT - THE BED WALL AT THE TOP, THE ROOM BELOW



REVISION 4

REVISION 4

From the owner's sketches and photo. The whole wall is built out 3 in in Dark Dove veneer, polished dark, on a ply carcass. Round the niche it sweeps forward in a concave curve 50° to 15° at the niche's edge — up both sides and across the top. The niche — bed and both tables — is 1/2" in deep, all parchment plaster: its back in 5 x 3 panels, its two sides and soffit plain (owner). The build-out is set square to the bed's centre line and scribed at both corners, so it also hides the owner's 2 in spay. The niche is the old bed-back span, centred on the TV; the cove stops where the open door's leaf ends. Cove light: in the ceiling. No headboard — a long white cushion along the back (owner). A brass wall lamp each side. The bed is drawn on ASH ORB-035.

THROUGH THE BED



TELL ME IF ANY OF THESE IS WRONG

Niche 9 ft 4 in wide — the old bed-back span — and $\frac{1}{2}$ " in deep.

Five panels across and three up, as sketched:

each about 1 ft 10" x 2 ft in — nearly square.

The 4 in white marble skirting runs along the build-out and into the niche.

The build-out runs to the ceiling.

Side tables $\frac{1}{2}$ " in wide, $\frac{1}{2}$ " in deep, 1" in high, all wood.

Bed and cushion heights: AST-OR-035.

TO DECIDE


1 - DOOR – not to 3 ft, which is kept clear, but the DEPTH: D/Ys hinge pin is 2 in off this wall, so a 2 in face there stops it opening flat (detail 2).
Projecting hinges (A), or 1½ in deep at that corner (B).

2 - The bed comes 3½ in further out (its frame runs 2 in past the mattress all round): 2 ft 6 in to left to the TV drawers instead of 2 ft 9½ in.

3 - Lamp sockets and switches go through the plaster panels – fix their places (just item B2) before the panels are made.

DECIDED: the cove light stays in the ceiling; no other light on this wall but the two wall lamps over the side tables (owner).

PLAN • THE DOOR vs THE 3 IN FACE

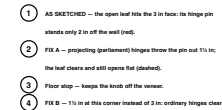



A STUDY IN TEAK Particulars of the room	
BED WALL — THE NICHE Elevation · Plan · Section · The entrance corner	
SCALE AS NOTED @ A3	DATE 03.10.2026
REV 4 — niche 16 is deep, the side tables inside it; no headboard	DWG AST-DR-034

DRAWING

AST-DR-034 · 1 of 8

ELEVATION — THE BED WALL

SCALE 1:30 @ A4 · SEEN FROM THE ROOM · DRESSING CORNER LEFT, ENTRANCE CORNER RIGHT

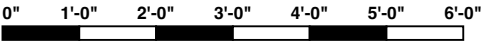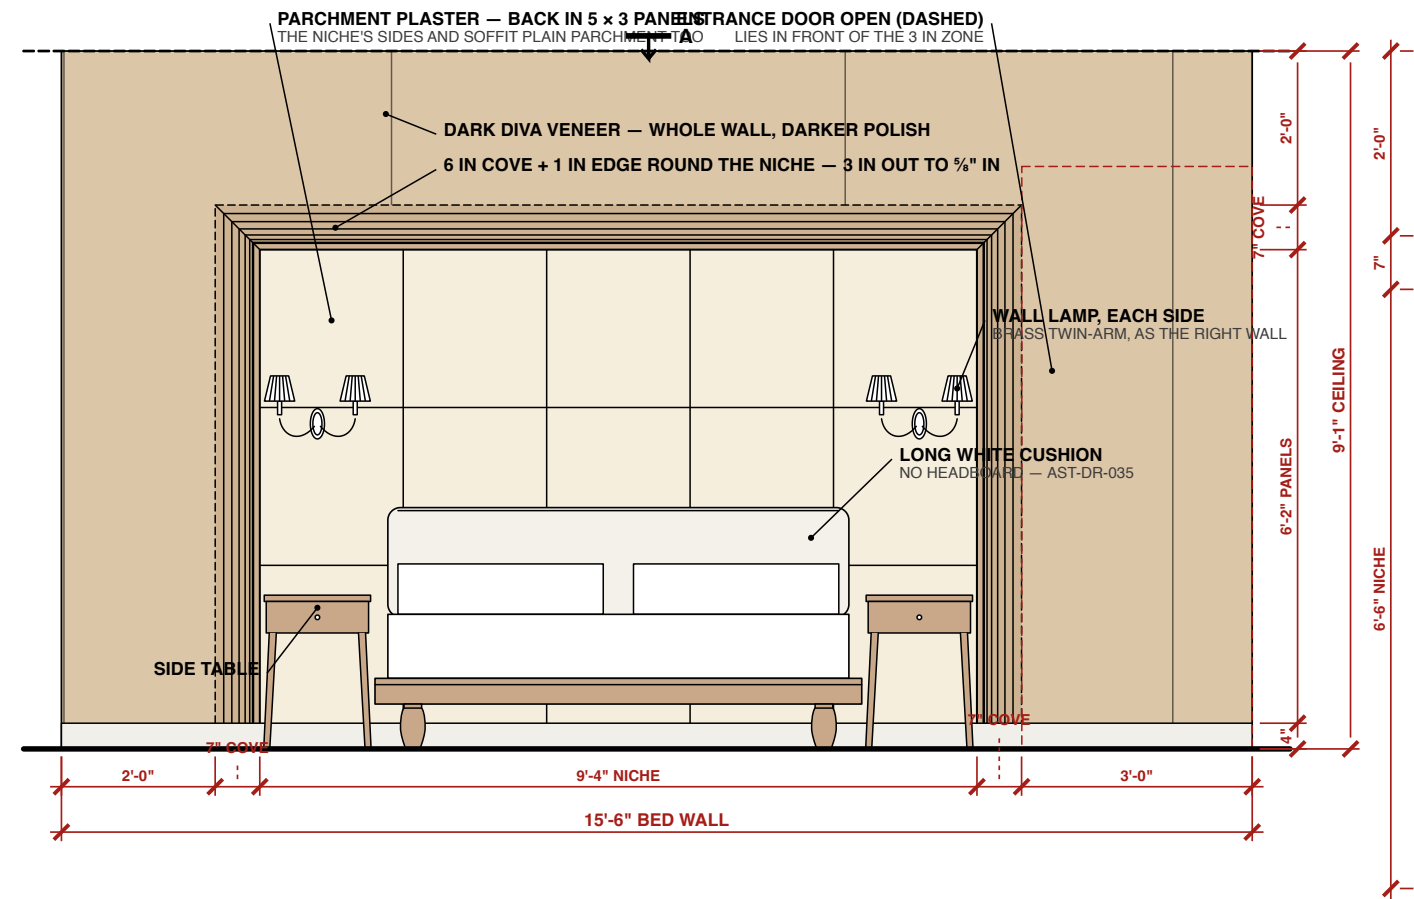

PROJECT
A Study in Teak — Bed Wall — the Niche

SHEET
Elevation — the bed wall
Elevation · Plan · Section · The entrance corner

SCALE
1:30 @ A4


DATE
03.10.2026

REV
4

DRAWING
AST-DR-034 · 2 of 8

SECTION A-A

SCALE 1:24 (1/2" = 1'-0") @ A4 · THROUGH THE BED

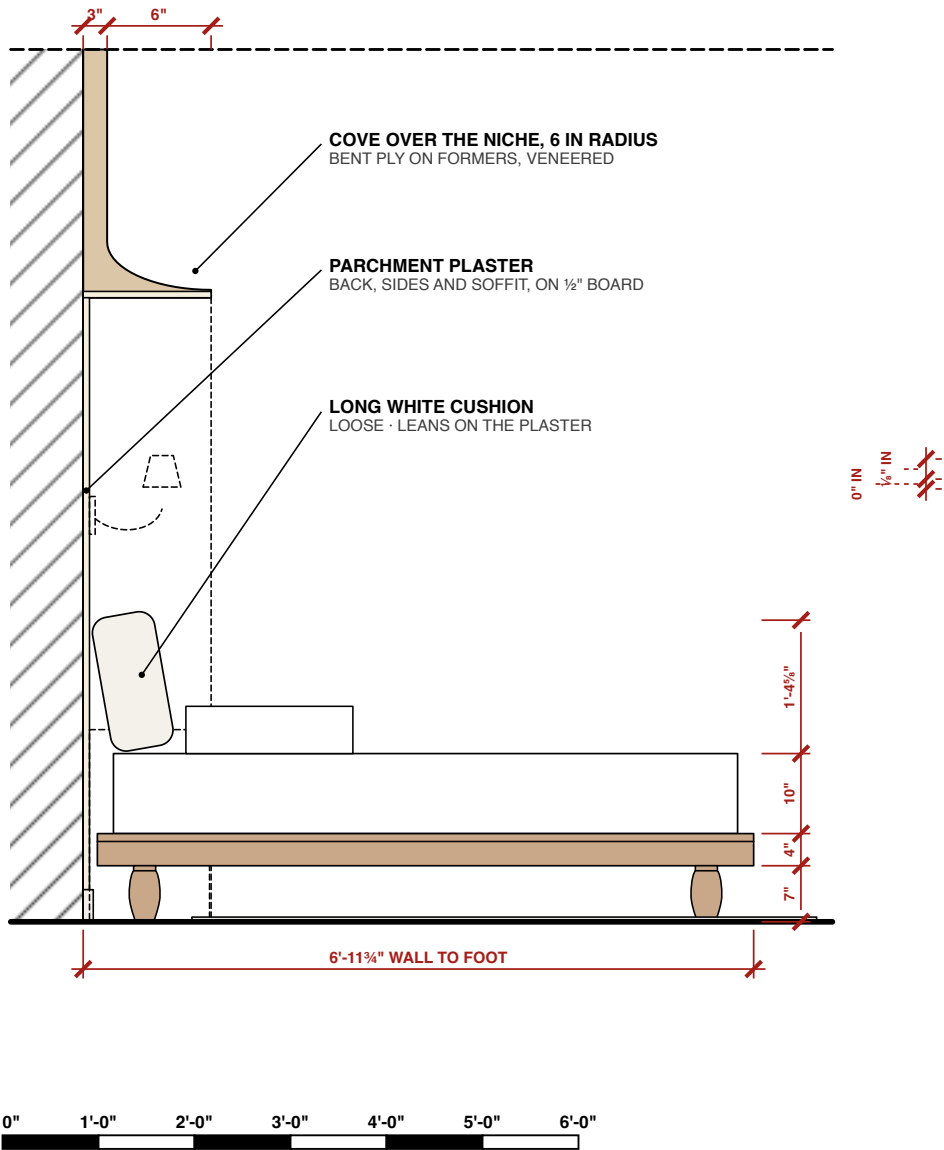

PROJECT
A Study in Teak — Bed Wall — the Niche

SHEET
Section A-A
Elevation · Plan · Section · The entrance corner

SCALE
1:24 @ A4

DATE
03.10.2026

REV
4

DRAWING
AST-DR-034 · 3 of 8

PROBLEMS FOUND

TO DECIDE

1 · DOOR — not its 3 ft, which is kept clear, but the DEPTH: D1's hinge pin

is 2 in off this wall, so a 3 in face there stops it opening flat (detail 2).

Projecting hinges (A), or 1½ in deep at that corner (B).

2 · The bed comes 3½ in further out (its frame runs 2 in past the mattress

all round): 2 ft 6¾ in left to the TV drawers instead of 2 ft 9¾ in.

3 · Lamp sockets and switches go through the plaster panels — fix their

places (list item B2) before the panels are made.


DECIDED: the cove light stays in the ceiling; no other light on this wall

but the two wall lamps over the side tables (owner).


PROJECT	SHEET	SCALE	DATE	REV	DRAWING
A Study in Teak — Bed Wall — the Niche	Problems found Elevation · Plan · Section · The entrance corner	NTS	03.10.2026	4	AST-DR-034 · 4 of 8

DETAIL 2 · THE ENTRANCE CORNER

SCALE 1:15 @ A4 · PLAN · THE DOOR vs THE 3 IN FACE

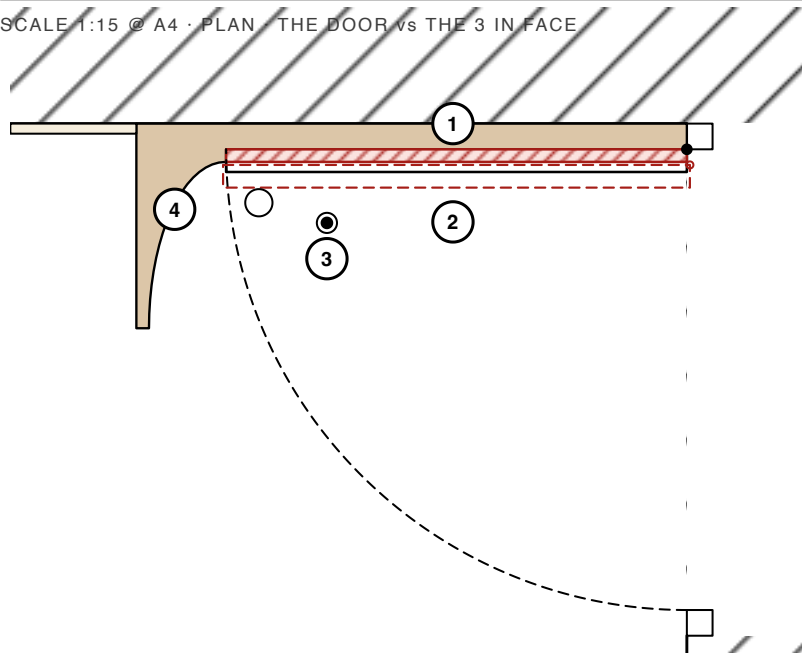



- 1 AS SKETCHED — the open leaf hits the 3 in face: its hinge pin stands only 2 in off the wall (red).
- 2 FIX A — projecting (parliament) hinges throw the pin out 1¼ in; the leaf clears and still opens flat (dashed).
- 3 Floor stop — keeps the knob off the veneer.
- 4 FIX B — 1½ in at this corner instead of 3 in: ordinary hinges clear.

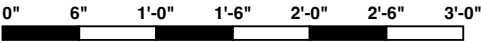

PROJECT	SHEET	SCALE	DATE	REV	DRAWING
A Study in Teak — Bed Wall — the Niche	Detail 2 · the entrance corner Elevation · Plan · Section · The entrance corner	1:15 @ A4	03.10.2026	4	AST-DR-034 · 5 of 8

PLAN

SCALE 1:24 (1/2" = 1'-0") @ A4 · CUT AT 4 FT · THE BED WALL AT THE TOP, THE ROOM BELOW

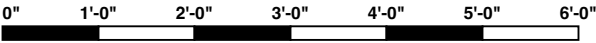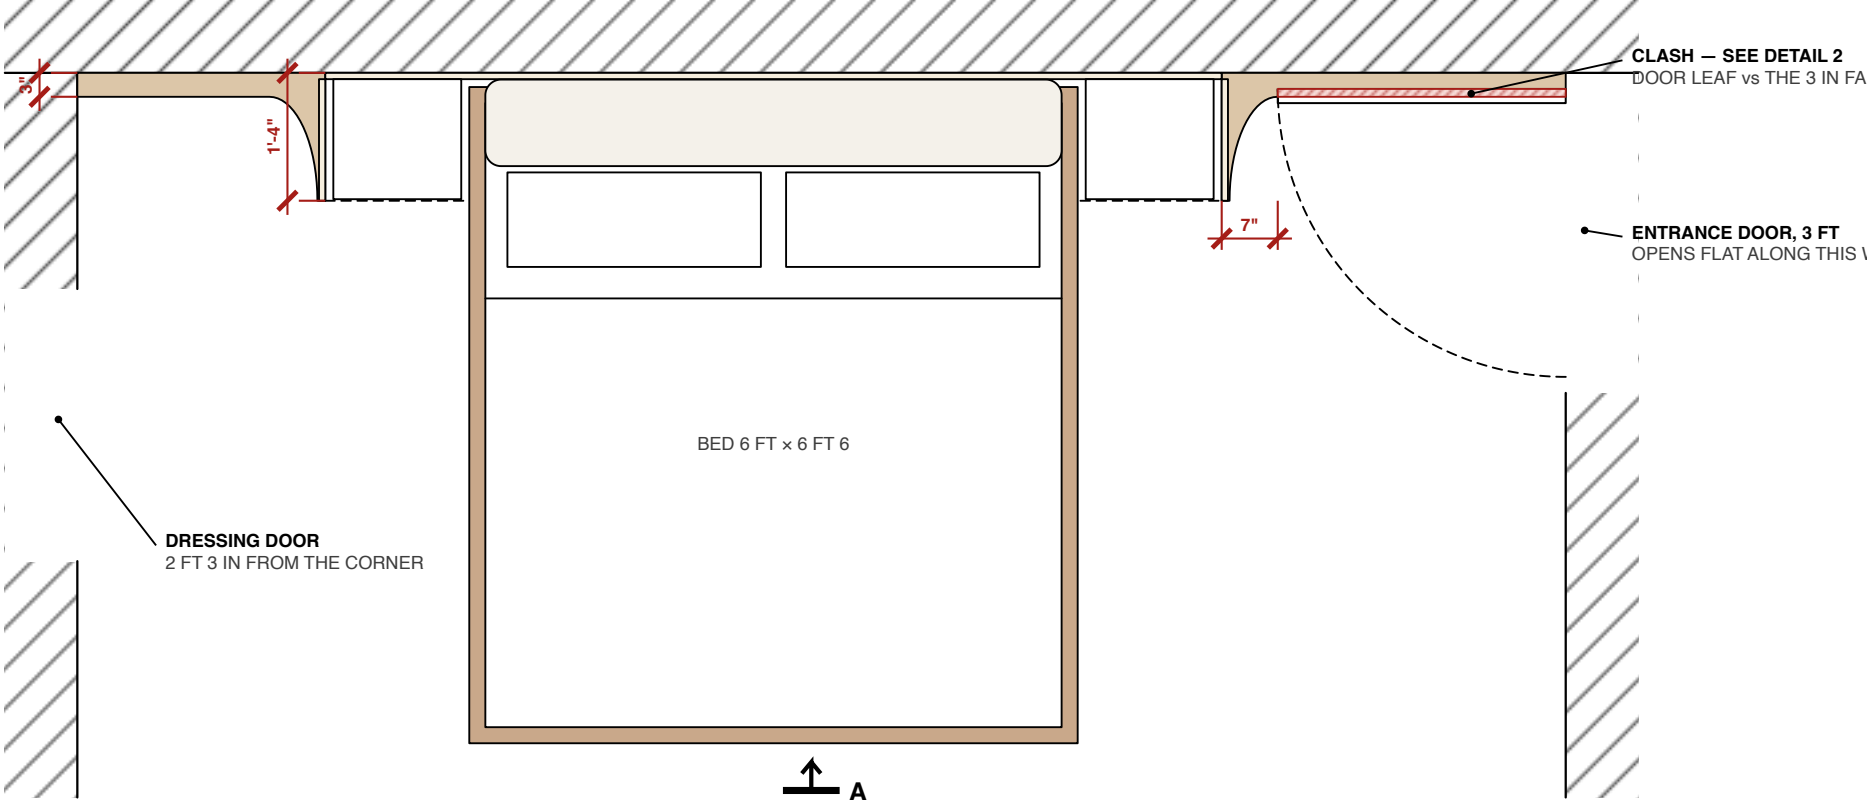

PROJECT	SHEET	SCALE	DATE	REV	DRAWING
A Study in Teak — Bed Wall — the Niche	Plan Elevation · Plan · Section · The entrance corner	1:24 @ A4	03.10.2026	4	AST-DR-034 · 6 of 8

ASSUMED

TELL ME IF ANY OF THESE IS WRONG

Niche 9 ft 4 in wide — the old bed-back span — and 5⁄8" in deep.

Five panels across and three up, as sketched:

each about 1 ft 10³⁄₈ × 2 ft ⁵⁄₈ in — nearly square.

The 4 in white marble skirting runs along the build-out
and into the niche.

The build-out runs to the ceiling.

Side tables 5⁄8" in wide, 5⁄8" in deep, 1" in high, all wood.

Bed and cushion heights: AST-DR-035.

PROJECT	SHEET	SCALE	DATE	REV	DRAWING
A Study in Teak — Bed Wall — the Niche	Assumed Elevation · Plan · Section · The entrance corner	NTS	03.10.2026	4	AST-DR-034 · 7 of 8

NOTES

REVISION 4

From the owner's sketches and photo. The whole wall is built out 3 in in Dark Diva veneer, polished darker, on a ply carcase. Round the niche it sweeps forward in a 6 in concave cove to 5/8" in at the niche's edge — up both sides and across the top.

The niche — bed and both tables — is 5/8" in deep, all parchment plaster: its back in 5 x 3 panels, its two sides and soffit plain (owner).

The build-out is set square to the bed's centre line and scribed at both corners, so it also hides the room's 2 in splay. The niche is the old bed-back span, centred on the TV; the cove stops where the open door's leaf ends. Cove light: in the ceiling.

No headboard: a long white cushion along the back (owner). A brass wall lamp each side.

The bed is drawn on AST-DR-035.

PROJECT	SHEET	SCALE	DATE	REV	DRAWING
A Study in Teak — Bed Wall — the Niche	Notes Elevation · Plan · Section · The entrance corner	NTS	03.10.2026	4	AST-DR-034 · 8 of 8