



ELEVATION — THE BED WALL

SEEN FROM THE ROOM · DRESSING CORNER LEFT, ENTRANCE CORNER RIGHT

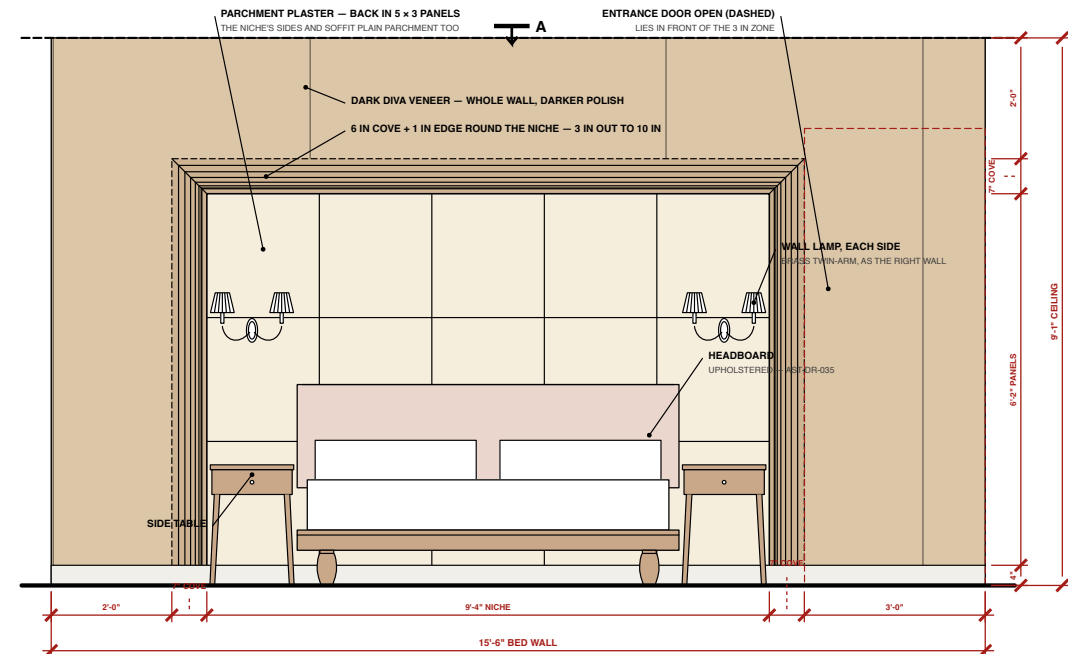

PLAN

CUT AT 4 FT · THE BED WALL AT THE TOP, THE ROOM BELOW

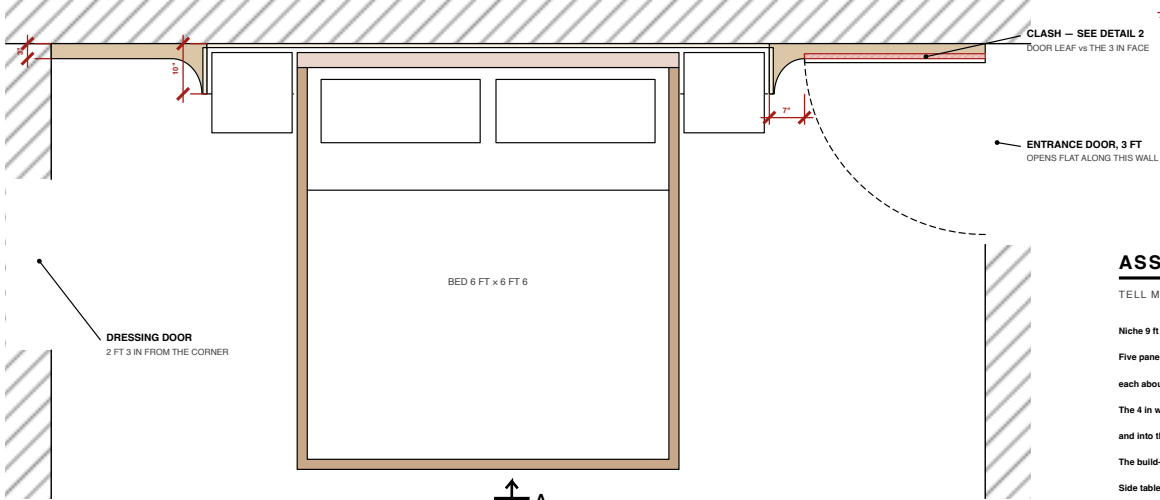


NOTES

REVISION 3

From the owner's sketches and photo. The whole wall is built out 3 in in Dark Diva veneer, polished darker, on a ply carcass. Round the niche it sweeps forward in a veneer, polished darker, on a ply carcass. Round the niche it sweeps forward in a 6 in concave cove to 10 in at the niche's edge — up both sides and across the top. The niche — bed and both tables — is 10 in deep, all parchment plaster: its back in 5 x 3 panels, its two sides and soffit plain (owner). The build-out is set square to the bed's centre line and scribed at both corners, so it also hides the room's 2 in splay. The niche is the old bed-back span, centred on the TV; the cove stops where the open door's leaf ends. Cove light: in the ceiling. Headboard: dusty-rose suede (owner). A brass twin-arm wall lamp over each table. The bed is drawn on AST-DR-035.

SECTION A-A

THROUGH THE BED

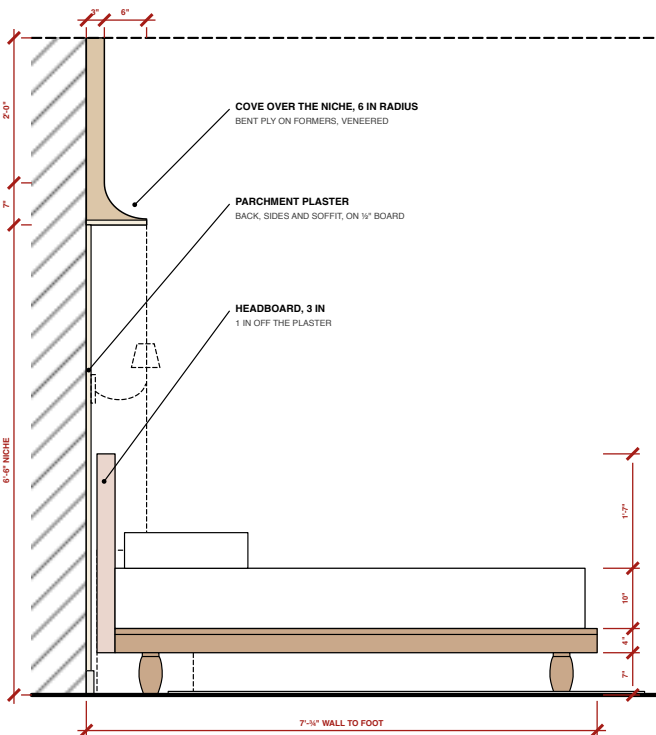

ASSUMED

TELL ME IF ANY OF THESE IS WRONG

Niche 9 ft 4 in wide — the old bed-back span (you said 9 ft 6 in).
Five panels across and three up, as sketched:
each about 1 ft 10" x 2 ft 1/2 in — nearly square.
The 4 in white marble skirting runs along the build-out and into the niche.
The build-out runs to the ceiling.
Side tables 1/2" x 1/2" in, 1" in high, all wood (from the photo).
Bed and headboard heights: AST-DR-035.


PROBLEMS FOUND

TO DECIDE

- 1 - DOOR — not its 3 ft, which is kept clear, but the DEPTH: D's hinge pin is 2 in off this wall, so a 3 in face there stops it opening flat (detail 2).
Projecting hinges (A), or 1 1/2 in deep at that corner (B).
- 2 - The bed comes 4 1/2 in further out (headboard + frame): 2 ft 5 1/2 in left to the TV drawers instead of 2 ft 9 1/2 in.
- 3 - Lamp sockets and switches go through the plaster panels — fix their places (list item B2) before the panels are made.
DECIDED: the cove light stays in the ceiling; no other light on this wall but the two wall lamps over the side tables (owner).

DETAIL 2 · THE ENTRANCE CORNER

PLAN · THE DOOR VS THE 3 IN FACE

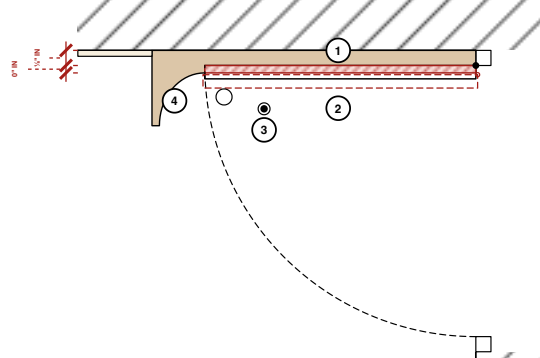

- 1 AS SKETCHED — the open leaf hits the 3 in face: its hinge pin stands only 2 in off the wall (red).
- 2 FIX A — projecting (parliament) hinges throw the pin out 1 1/2 in; the leaf clears and still opens flat (dashed).
- 3 Floor stop — keeps the knob off the veneer.
- 4 FIX B — 1 1/2 in at this corner instead of 3 in: ordinary hinges clear.

A STUDY IN TEAK

Particulars of the room

BED WALL — THE NICHE

Elevation · Plan · Section · The entrance corner

SCALE

AS NOTED @ A3

DATE

03.10.2026

REV

3 — niche on the old bed-back span, cove clear of the door, cove light kept

DWG

AST-DR-034

PROJECT

A Study in Teak — Bed Wall — the Niche

SHEET

General arrangement — the whole sheet

each view follows at its own scale, pages 2 to 8

SCALE

NTS

DATE

03.10.2026

REV



3

DRAWING

AST-DR-034 · 1 of 8

ELEVATION — THE BED WALL

SCALE 1:20 @ A3 · SEEN FROM THE ROOM · DRESSING CORNER LEFT, ENTRANCE CORNER RIGHT

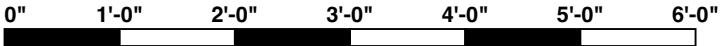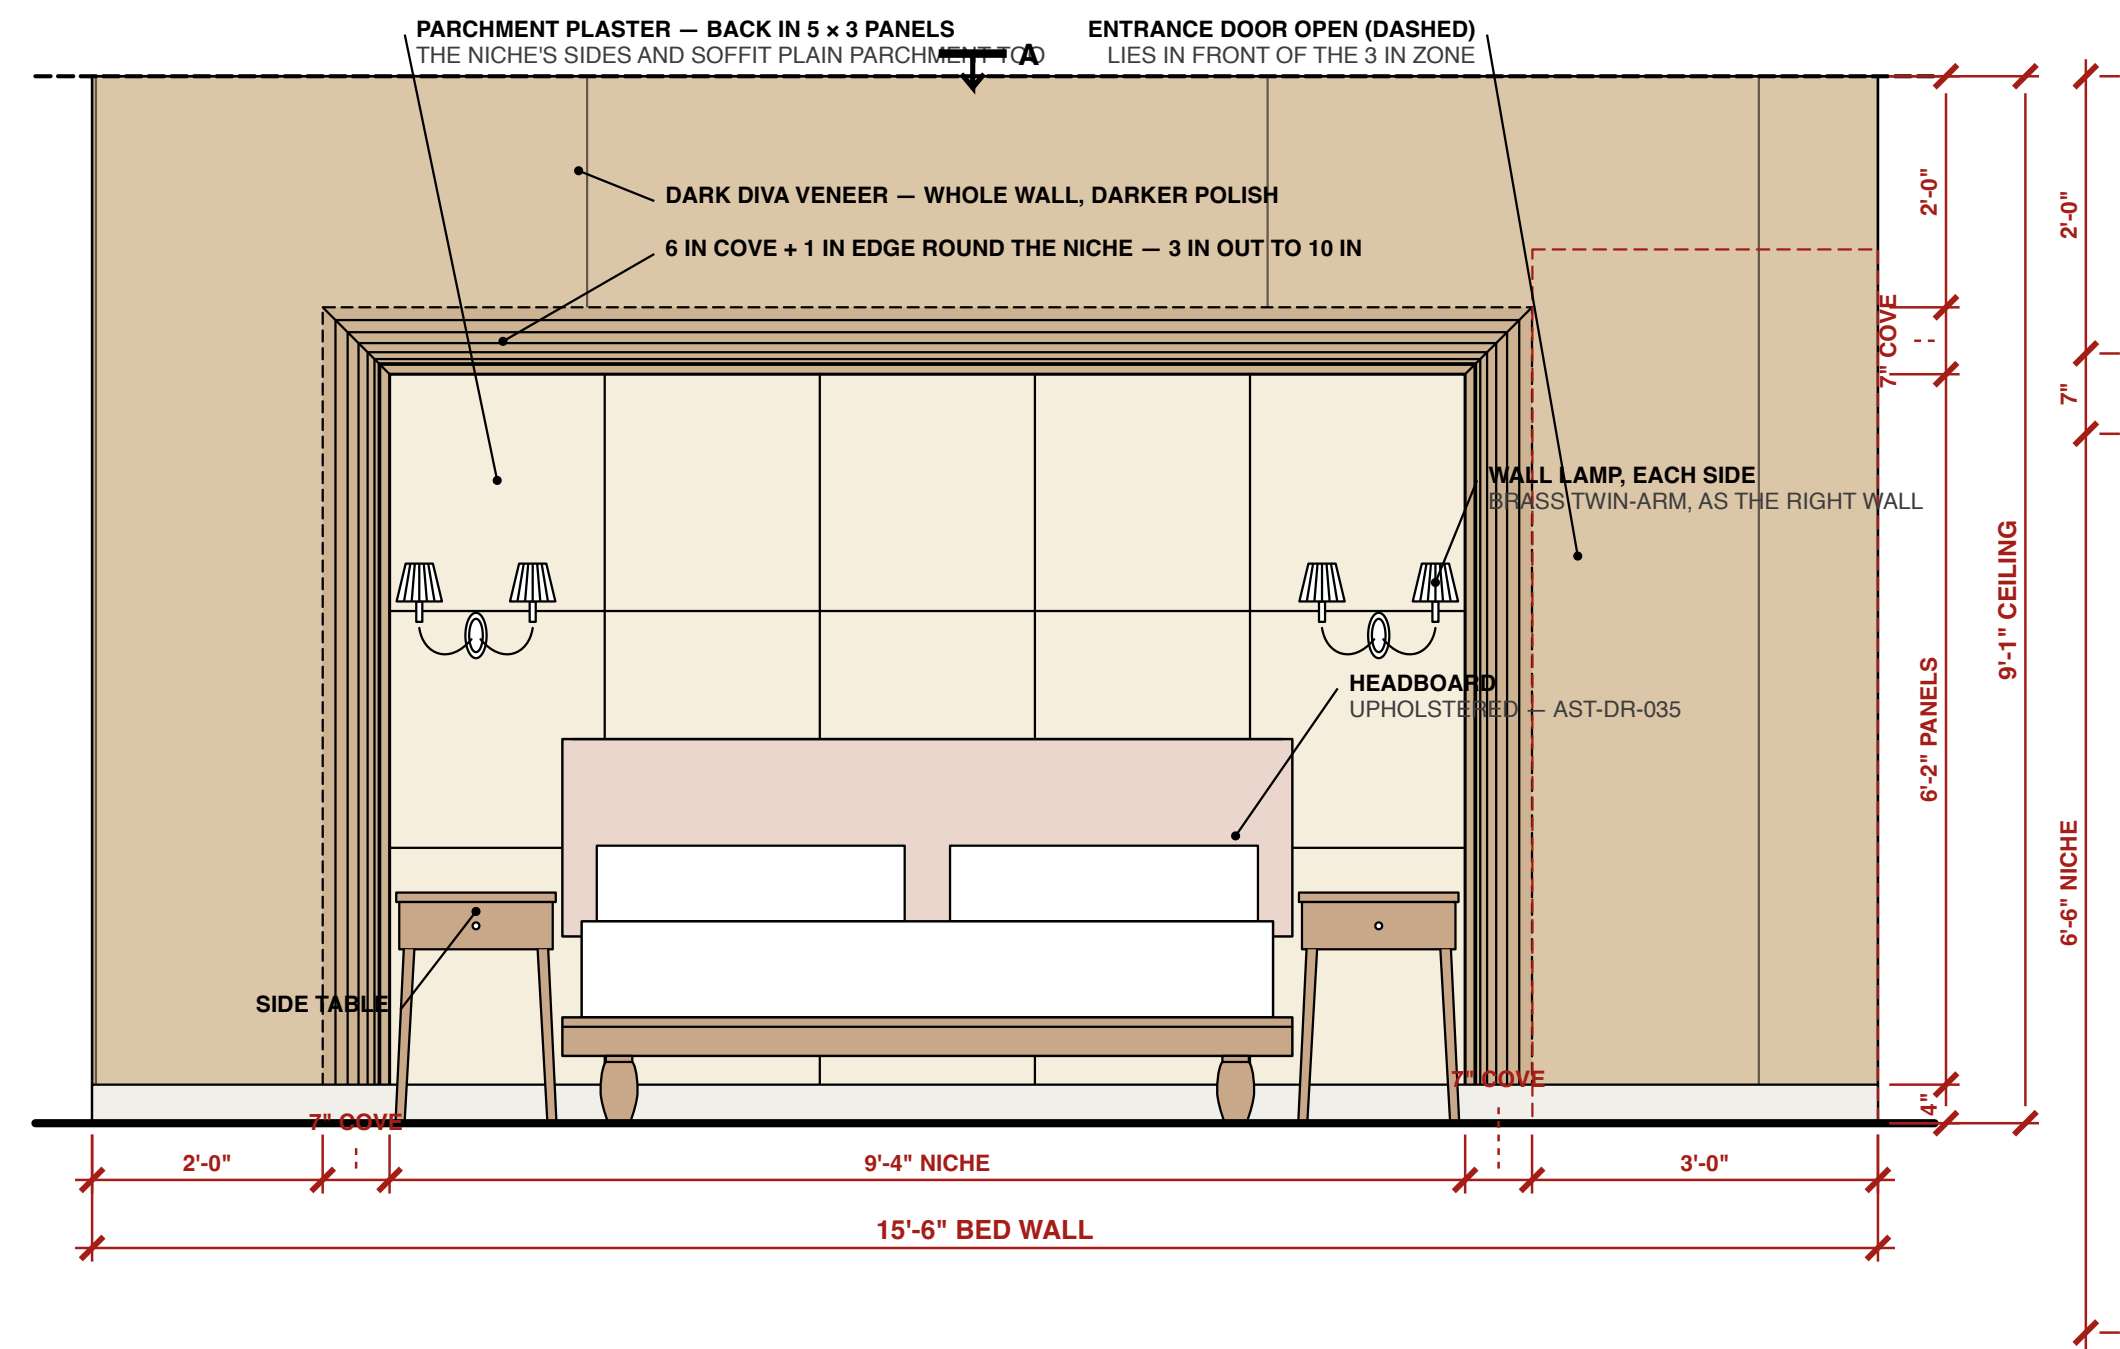

PROJECT
A Study in Teak — Bed Wall — the Niche

SHEET
Elevation — the bed wall
Elevation · Plan · Section · The entrance corner

SCALE
1:20 @ A3


DATE
03.10.2026

REV
3

DRAWING
AST-DR-034 · 2 of 8

SECTION A-A

SCALE 1:16 (3/4" = 1'-0") @ A3 · THROUGH THE BED

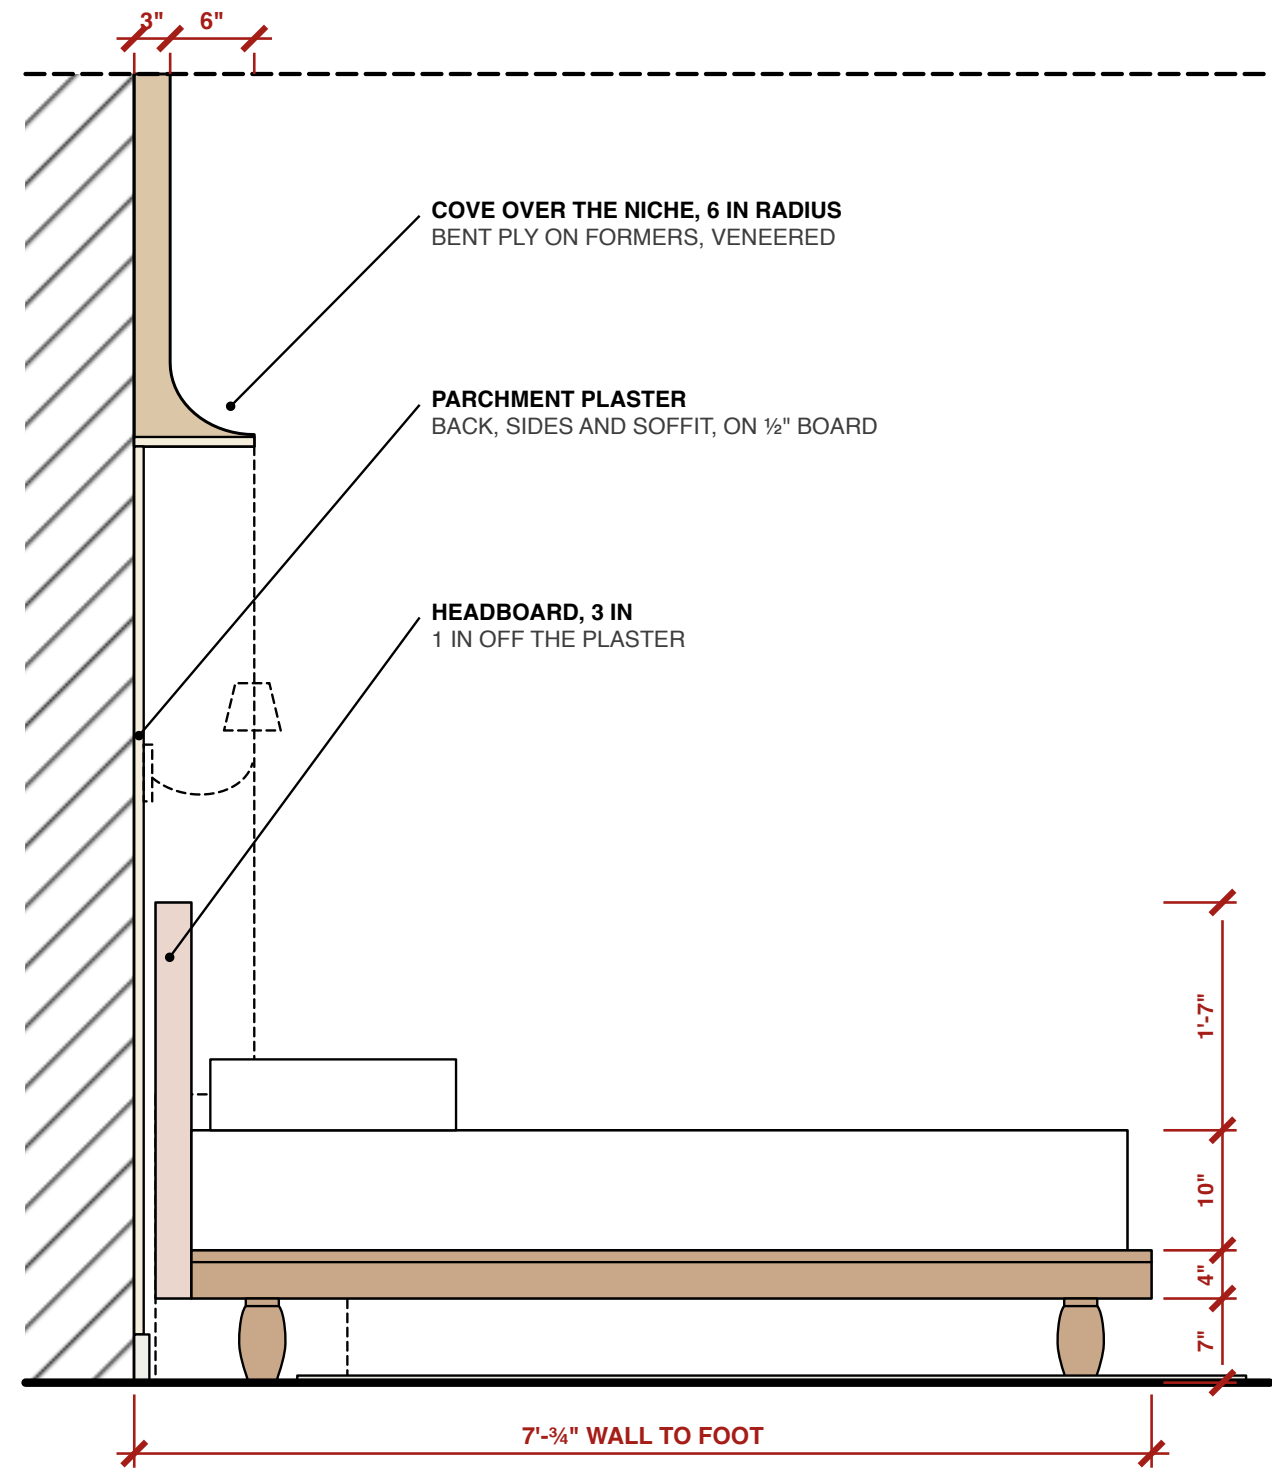

PROJECT
A Study in Teak — Bed Wall — the Niche

SHEET
Section A-A
Elevation · Plan · Section · The entrance corner

SCALE
1:16 @ A3

DATE
03.10.2026

REV
3

DRAWING
AST-DR-034 · 3 of 8

PROBLEMS FOUND

TO DECIDE

1 · DOOR — not its 3 ft, which is kept clear, but the DEPTH: D1's hinge pin

is 2 in off this wall, so a 3 in face there stops it opening flat (detail 2).

Projecting hinges (A), or 1½ in deep at that corner (B).

2 · The bed comes 4½ in further out (headboard + frame): 2 ft 5½ in left

to the TV drawers instead of 2 ft 9¾ in.

3 · Lamp sockets and switches go through the plaster panels — fix their

places (list item B2) before the panels are made.

DECIDED: the cove light stays in the ceiling; no other light on this wall

but the two wall lamps over the side tables (owner).

PROJECT
A Study in Teak — Bed Wall — the Niche

SHEET
Problems found
Elevation · Plan · Section · The entrance corner

SCALE
NTS


DATE
03.10.2026

REV
3


DRAWING
AST-DR-034 · 4 of 8

DETAIL 2 · THE ENTRANCE CORNER

SCALE 1:10 @ A3 · PLAN · THE DOOR vs THE 3 IN FACE

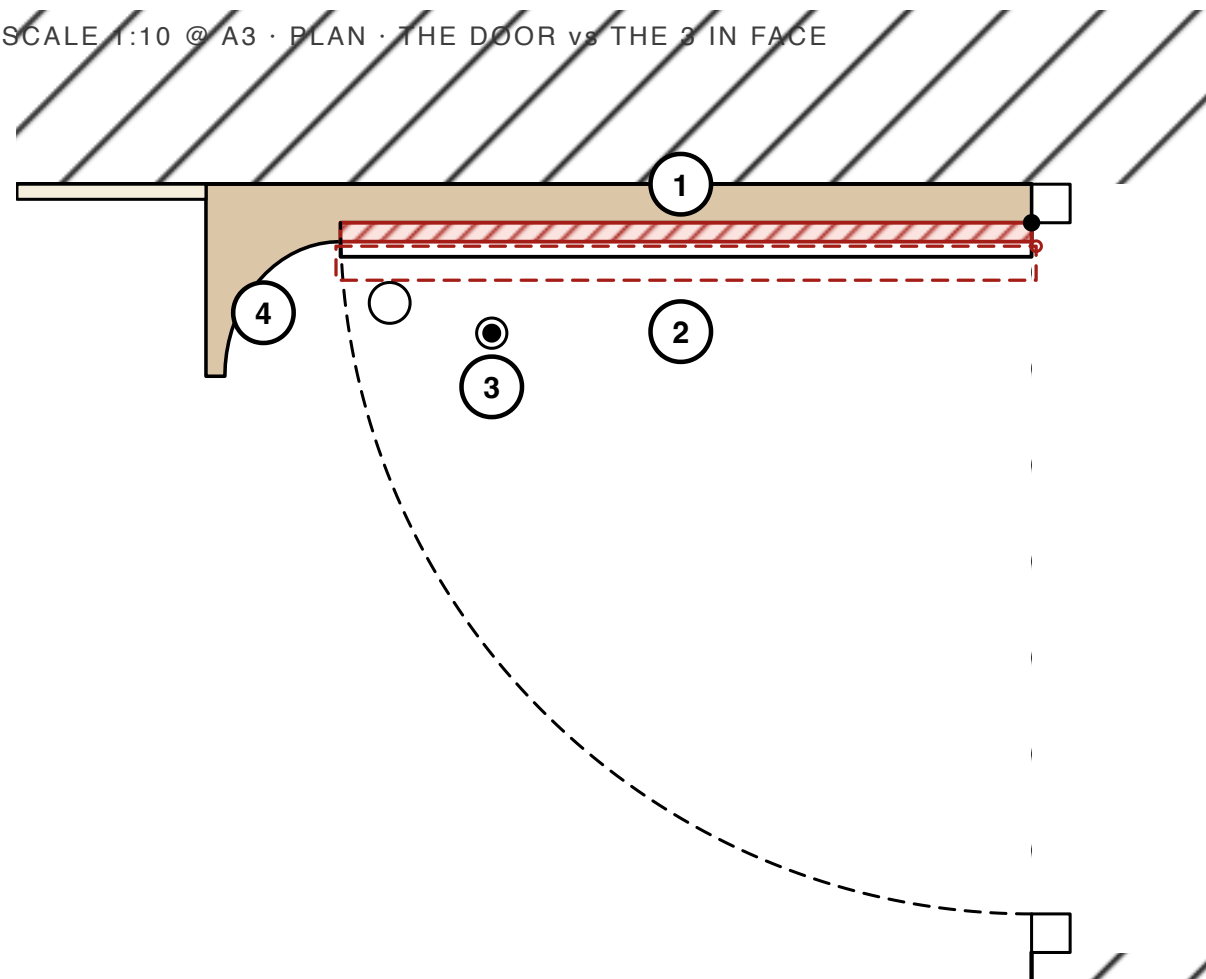

- 1 AS SKETCHED — the open leaf hits the 3 in face: its hinge pin stands only 2 in off the wall (red).
- 2 FIX A — projecting (parliament) hinges throw the pin out 1 1/4 in; the leaf clears and still opens flat (dashed).
- 3 Floor stop — keeps the knob off the veneer.
- 4 FIX B — 1 1/2 in at this corner instead of 3 in: ordinary hinges clear.

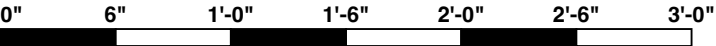

PROJECT
A Study in Teak — Bed Wall — the Niche

SHEET
Detail 2 · the entrance corner
Elevation · Plan · Section · The entrance corner

SCALE
1:10 @ A3



DATE
03.10.2026

REV
3

DRAWING
AST-DR-034 · 5 of 8

PLAN

SCALE 1:16 (3/4" = 1'-0") @ A3 · CUT AT 4 FT · THE BED WALL AT THE TOP, THE ROOM BELOW

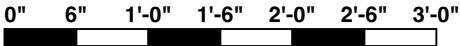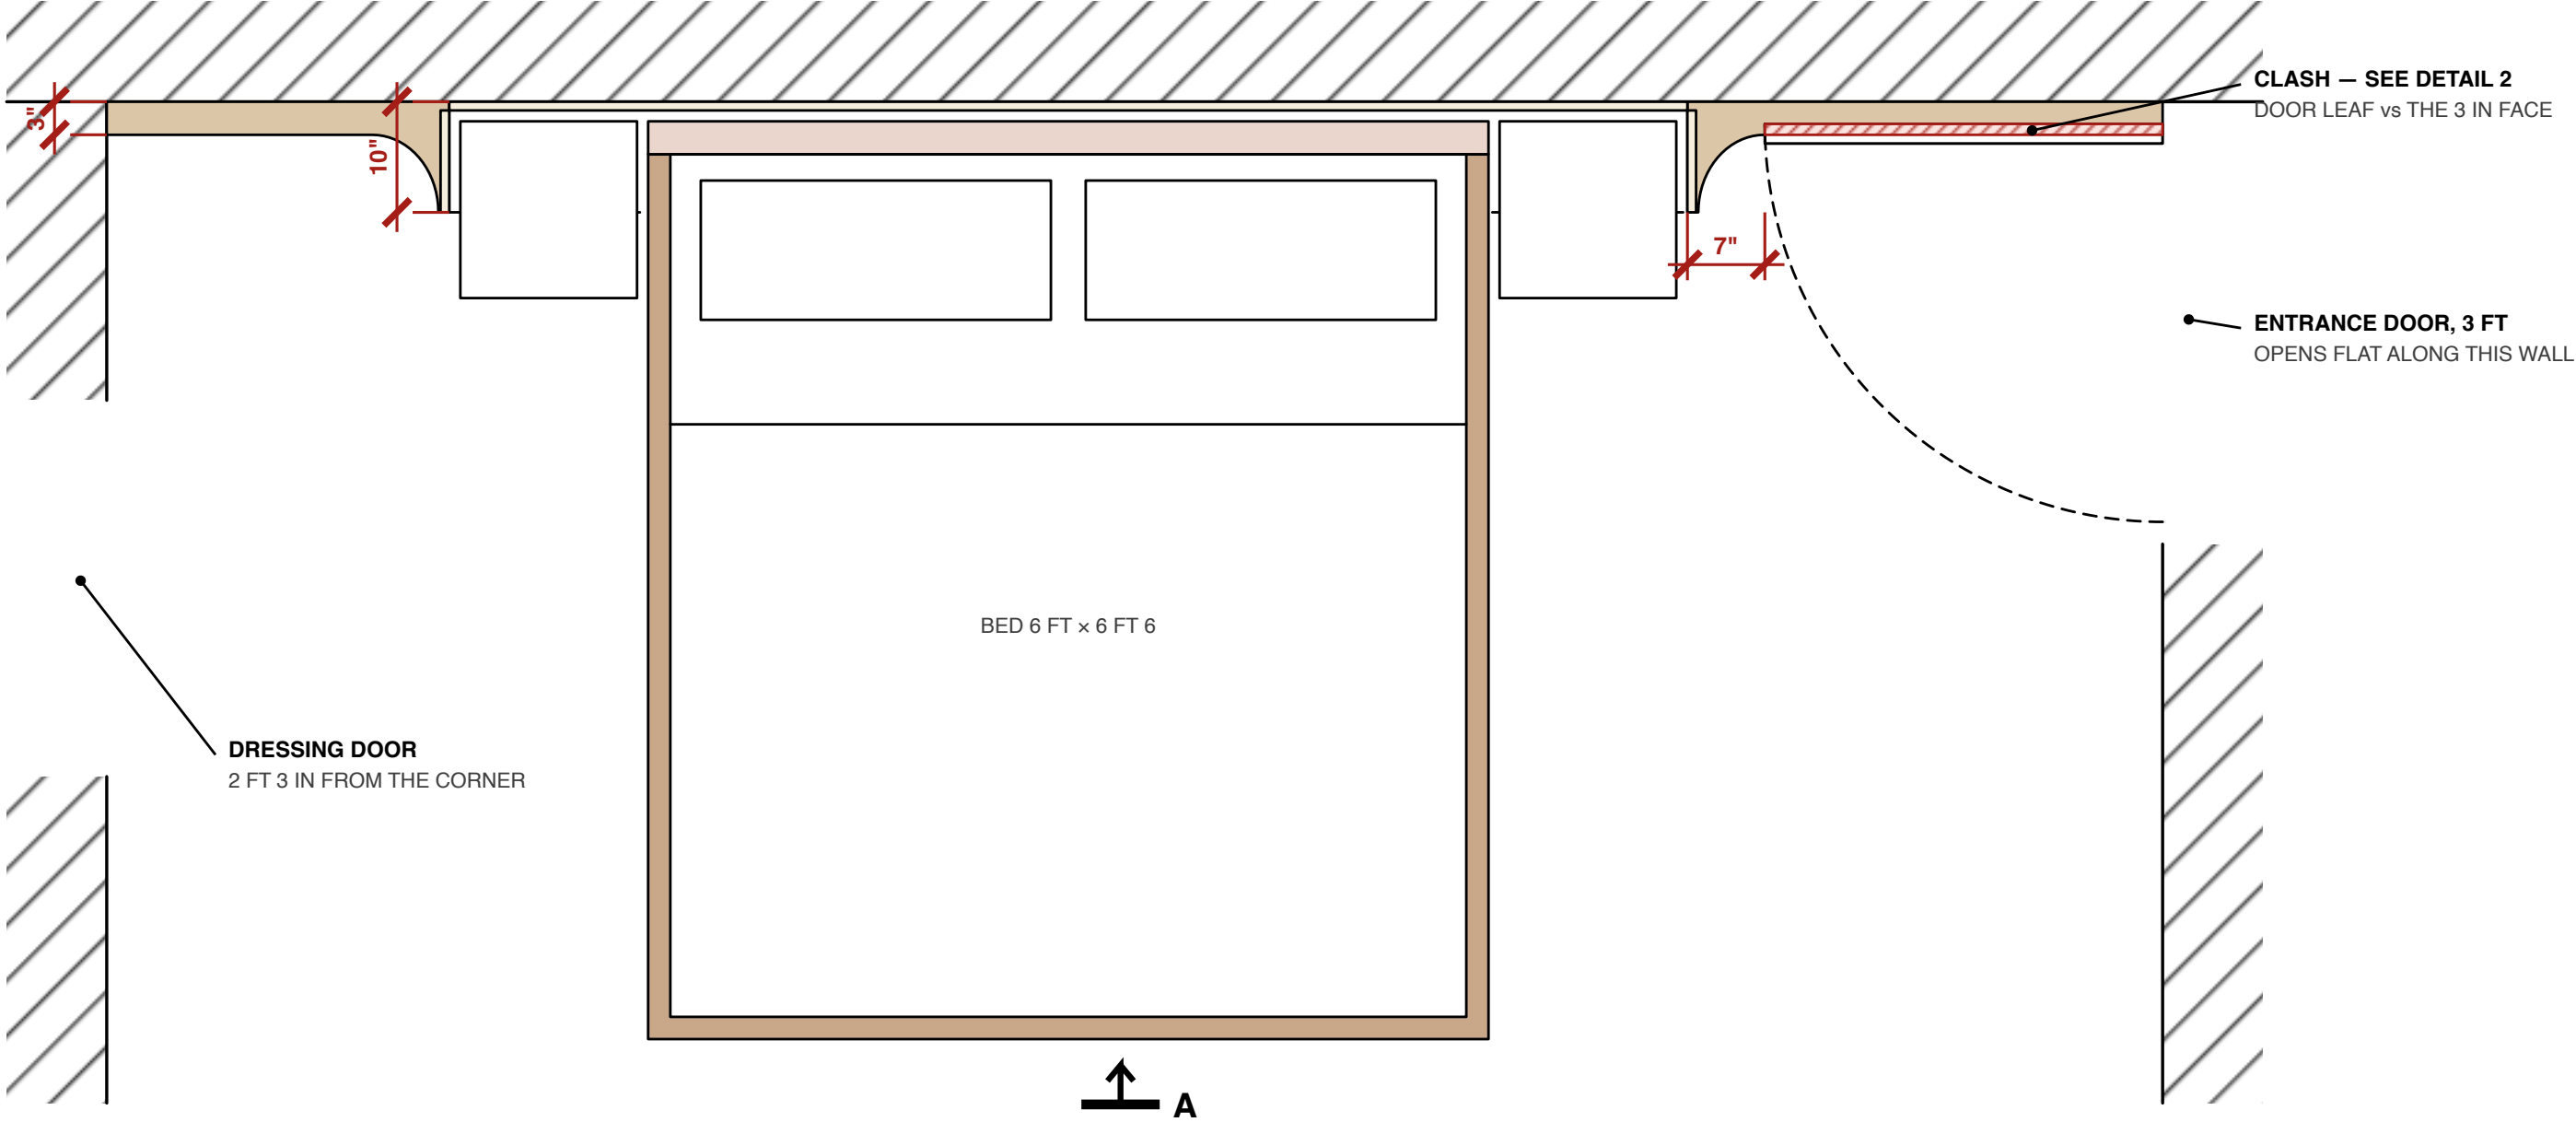

PROJECT
A Study in Teak — Bed Wall — the Niche

SHEET
Plan
Elevation · Plan · Section · The entrance corner

SCALE
1:16 @ A3

DATE
03.10.2026

REV
3

DRAWING
AST-DR-034 · 6 of 8

ASSUMED

TELL ME IF ANY OF THESE IS WRONG

Niche 9 ft 4 in wide — the old bed-back span (you said 9 ft 6 in).

Five panels across and three up, as sketched:

each about 1 ft 10³/₈ × 2 ft ⁵/₈ in — nearly square.

The 4 in white marble skirting runs along the build-out
and into the niche.

The build-out runs to the ceiling.

Side tables ⁵/₈" × ⁵/₈" in, 1" in high, all wood (from the photo).

Bed and headboard heights: AST-DR-035.

PROJECT A Study in Teak — Bed Wall — the Niche	SHEET Assumed Elevation · Plan · Section · The entrance corner	SCALE NTS	DATE 03.10.2026	REV 3	DRAWING AST-DR-034 · 7 of 8
---	--	--------------	--------------------	----------	--------------------------------

NOTES

REVISION 3

From the owner's sketches and photo. The whole wall is built out 3 in in Dark Diva veneer, polished darker, on a ply carcase. Round the niche it sweeps forward in a 6 in concave cove to 10 in at the niche's edge — up both sides and across the top. The niche — bed and both tables — is 10 in deep, all parchment plaster: its back in 5 x 3 panels, its two sides and soffit plain (owner).

The build-out is set square to the bed's centre line and scribed at both corners, so it also hides the room's 2 in splay. The niche is the old bed-back span, centred on the TV; the cove stops where the open door's leaf ends. Cove light: in the ceiling.

Headboard: dusty-rose suede (owner). A brass twin-arm wall lamp over each table.

The bed is drawn on AST-DR-035.

PROJECT A Study in Teak — Bed Wall — the Niche	SHEET Notes Elevation · Plan · Section · The entrance corner	SCALE NTS	DATE 03.10.2026	REV 3	DRAWING AST-DR-034 · 8 of 8
---	--	--------------	--------------------	----------	--------------------------------