

ELEVATION — THE BED WALL

SEEN FROM THE ROOM · DRESSING CORNER LEFT, ENTRANCE CORNER RIGHT

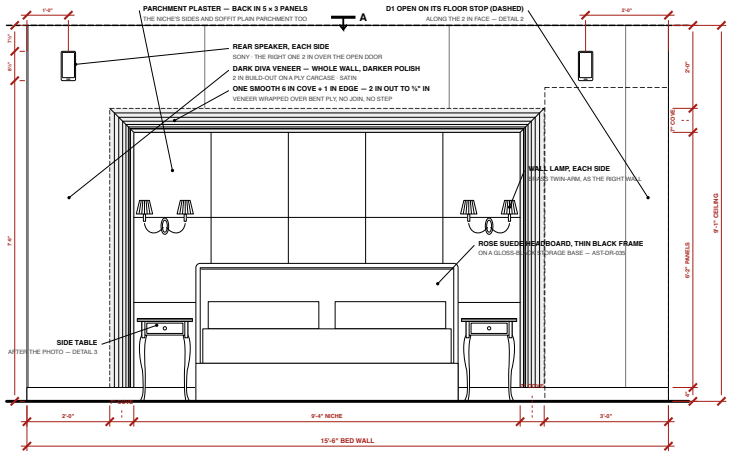


SECTION A–A

THROUGH THE BED

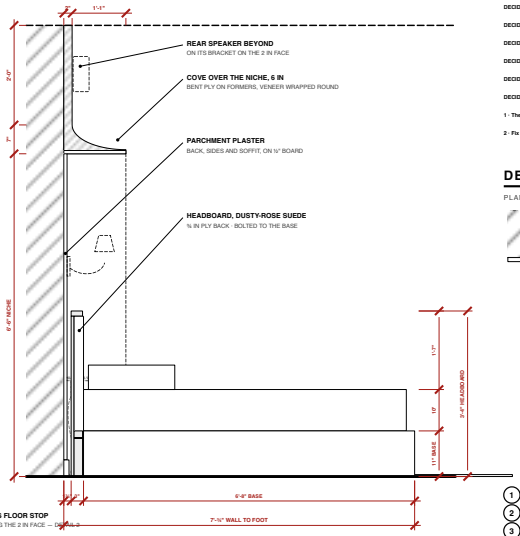


PLAN

CUT AT 4 FT · THE BED WALL AT THE TOP, THE ROOM BELOW

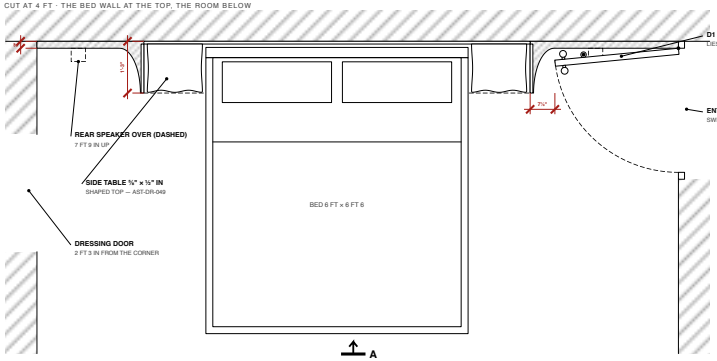

DETAIL 3 · THE SIDE TABLES

FRONT AND PLAN AFTER THE OWNER'S PHOTO · IN FULL ON AST-DR-049

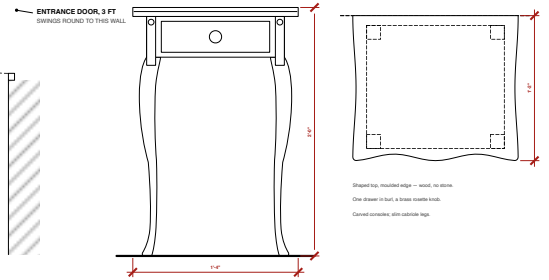

Shaped top, moulded edge — wood, no stone.

One drawer in burl, a brass rosette knob.

Carved consoles; slim cabriole legs.

DECIDED · STILL OPEN

OWNER, 7 OCT

DECIDED: 2 in face all along — D1 lies along it on a floor stop (detail 2).

DECIDED: one smooth cove (option A); niche ¾" in; tables ¾" × ½" in.

DECIDED: the headboard back in rose suede, in a thin gloss-black frame.

DECIDED: side tables after the owner's photo, no stone (detail 3, AST-DR-049).

DECIDED: two rear speakers high on the plain faces, either side, clear of D1.


DECIDED: the bed on a storage base to the floor, no legs, in gloss black.

1 · The bed stands 2 ft 5¼ in clear of the TV drawers (was 2 ft 9¼ in).

2 · Fix the lamp and speaker sockets (list B2) before the panels are made.

DETAIL 2 · THE ENTRANCE CORNER

PLAN · D1 OPEN ON ITS FLOOR STOP

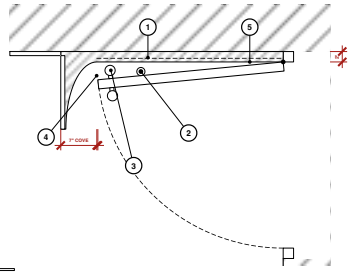

1. THE 2 IN FACE — as deep as D1's lining, so the open leaf lies along it.
2. Brass floor stop, 6 in in from the knob: the leaf rests on it 5½" off the face.
3. The knob stays ¾ in off the veneer.
4. The cove starts where the leaf ends: the whole 3 ft opening stays clear.
5. Marble skirting set flush with the veneer here — the leaf's heel clears it.

NOTES

REVISION 5

From the owner's sketches and photos. The whole wall is built out 2 in in Dark Diva veneer, polished darker (satin), on a ply carcase. Round the niche it sweeps forward in one smooth 6 in concave cove to ¾" in, then a 1 in flat — up both sides and across the top, no step; the veneer wrapped over bent ply, grain running round the curve. The niche — bed and both tables — is ¾" in deep, all parchment plaster: back in 5 × 3 panels, sides and soffit plain. Set square to the bed's centre line and scribed at both corners, it hides the room's 2 in splay. Bed and headboard: AST-DR-035. A brass lamp over each table; cove light in the ceiling, nothing else.

ASSUMED

TELL ME IF ANY OF THESE IS WRONG

Five panels across and three up, as sketched: each about 1 ft 10⅝ × 2 ft ⅝ in.

The 4 in white marble skirting runs along the build-out (flush with the veneer) and into the niche. The build-out runs to the ceiling.

Side tables 1" in high — the photo's table is taller; its look is kept.

Speakers: Sony's rear speakers, 4¼" × 8½" × 3¼" from Sony's spec page — the Bar 6 has none in the box; confirm the model before the brackets go up. Mattress 10 in (AST-DR-035).

A STUDY IN TEAK

Particulars of the room

BED WALL — THE NICHE

Elevation · Plan · Section · Entrance corner · Side table


SCALE	DATE
AS NOTED @ A3	07.10.2026
REV	DWG
5 — 2 in face, 15 in niche; headboard; new side tables; speakers	AST-DR-034

PROJECT	SHEET	SCALE	DATE	REV	DRAWING
A Study in Teak — Bed Wall — the Niche	**General arrangement — the whole sheet** each view follows at its own scale, pages 2 to 9	NTS	07.10.2026	5	**AST-DR-034 · 1 of 9**

ALL DIMENSIONS IN FEET & INCHES. PRINT ON A4 AT 100% / "ACTUAL SIZE" — NOT "FIT TO PAGE" — AND CHECK THE SCALE BAR. DO NOT SCALE; WORK TO FIGURED DIMENSIONS. VERIFY ON SITE.

ELEVATION — THE BED WALL

SCALE 1:30 @ A4 · SEEN FROM THE ROOM · DRESSING CORNER LEFT, ENTRANCE CORNER RIGHT

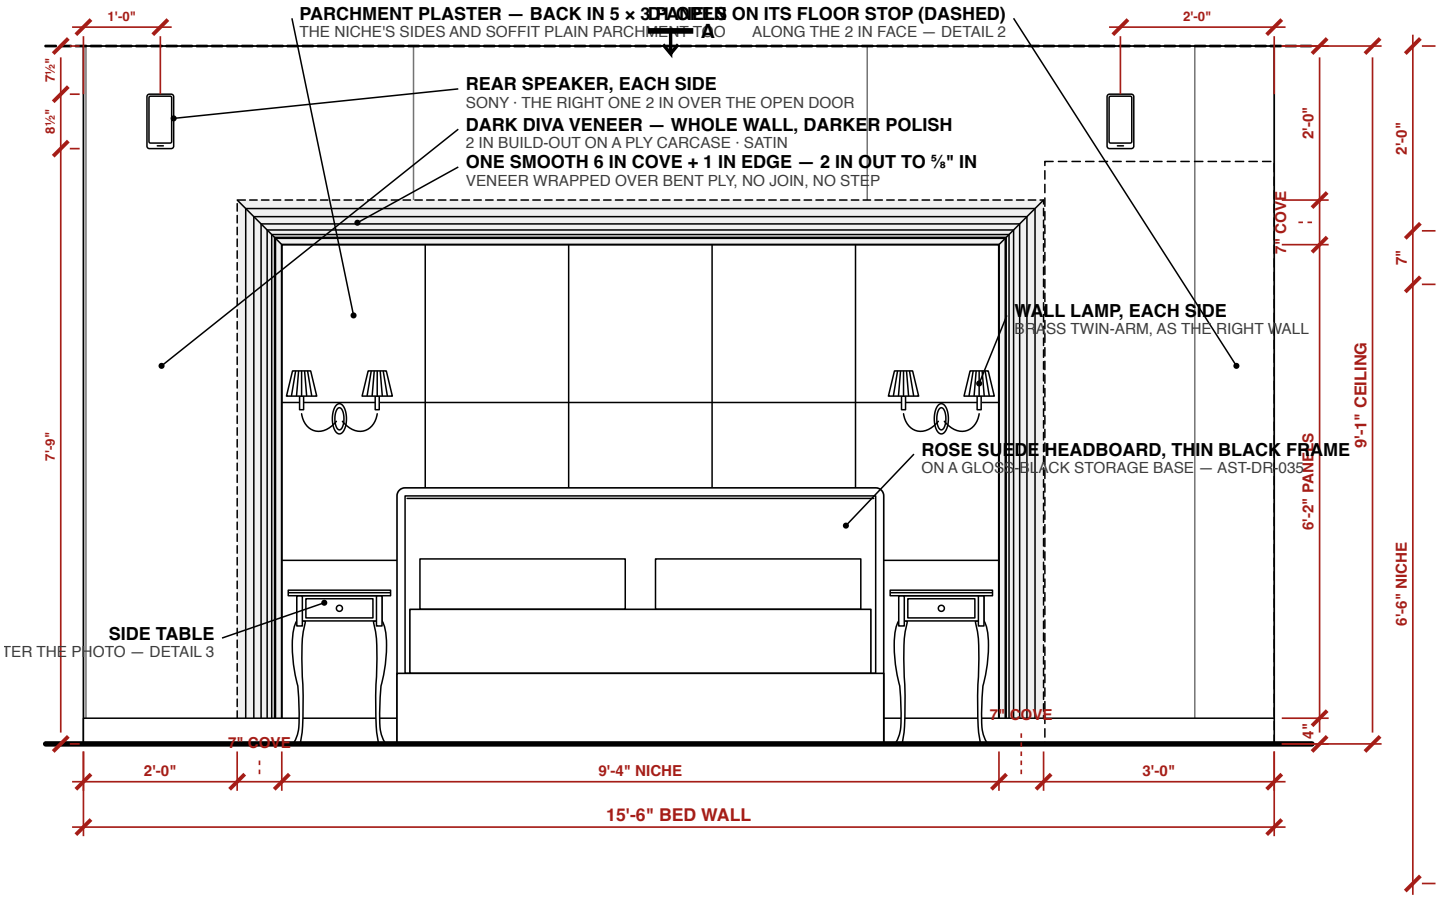


0" 1'-0" 2'-0" 3'-0" 4'-0" 5'-0" 6'-0"


PROJECT	SHEET	SCALE	DATE	REV	DRAWING
A Study in Teak — Bed Wall — the Niche	**Elevation — the bed wall** Elevation · Plan · Section · Entrance corner · Side table	1:30 @ A4	07.10.2026	5	**AST-DR-034 · 2 of 9**

ALL DIMENSIONS IN FEET & INCHES. PRINT ON A4 AT 100% / "ACTUAL SIZE" — NOT "FIT TO PAGE" — AND CHECK THE SCALE BAR. DO NOT SCALE; WORK TO FIGURED DIMENSIONS. VERIFY ON SITE.

SECTION A–A

SCALE 1:24 (½" = 1'-0") @ A4 · THROUGH THE BED

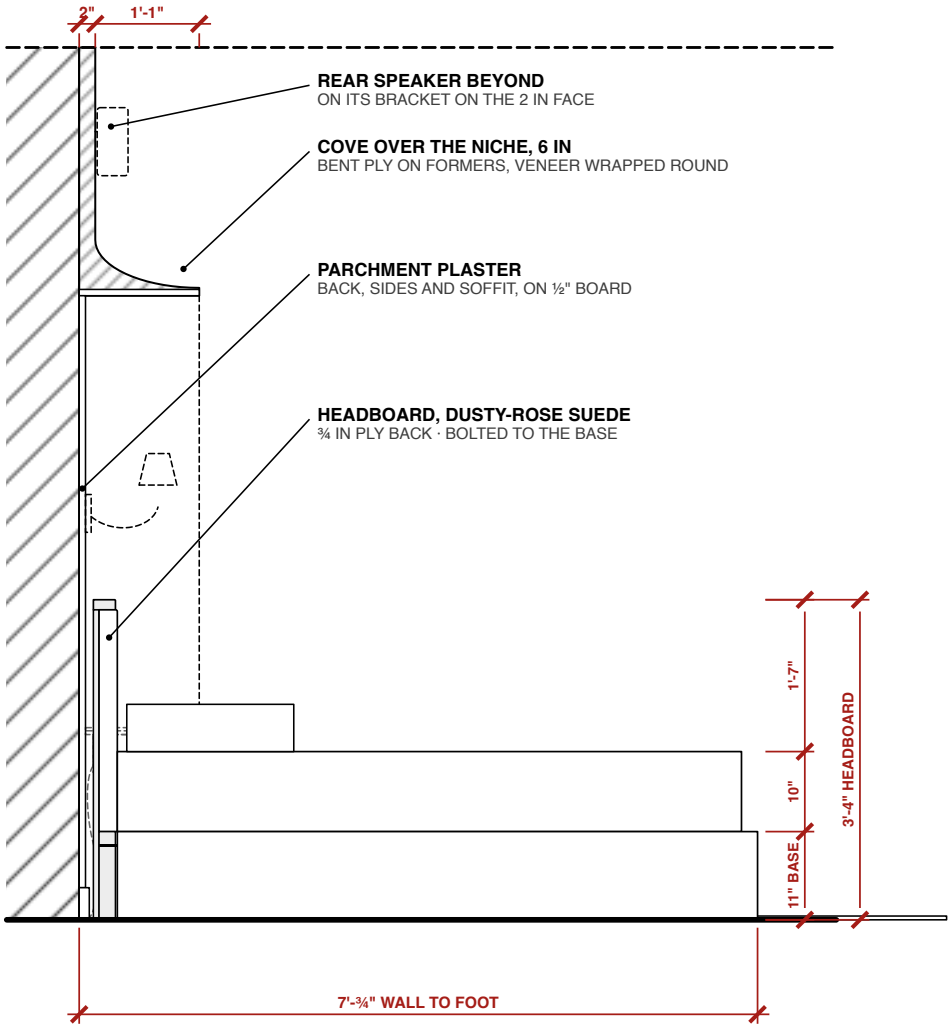

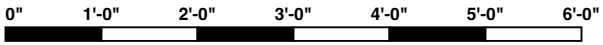

PROJECT	SHEET	SCALE	DATE	REV	DRAWING
A Study in Teak — Bed Wall — the Niche	**Section A–A** Elevation · Plan · Section · Entrance corner · Side table	1:24 @ A4	07.10.2026	5	**AST-DR-034 · 3 of 9**

ALL DIMENSIONS IN FEET & INCHES. PRINT ON A4 AT 100% / "ACTUAL SIZE" — NOT "FIT TO PAGE" — AND CHECK THE SCALE BAR. DO NOT SCALE; WORK TO FIGURED DIMENSIONS. VERIFY ON SITE.

DECIDED · STILL OPEN

OWNER, 7 OCT

DECIDED: 2 in face all along — D1 lies along it on a floor stop (detail 2).

DECIDED: one smooth cove (option A); niche ⅝" in; tables ⅝" × ½" in.

DECIDED: the headboard back in rose suede, in a thin gloss-black frame.

DECIDED: side tables after the owner's photo, no stone (detail 3, AST-DR-049).

DECIDED: two rear speakers high on the plain faces, either side, clear of D1.

DECIDED: the bed on a storage base to the floor, no legs, in gloss black.

1 · The bed stands 2 ft 5⅜ in clear of the TV drawers (was 2 ft 9¾ in).


2 · Fix the lamp and speaker sockets (list B2) before the panels are made.

PROJECT	SHEET	SCALE	DATE	REV	DRAWING
A Study in Teak — Bed Wall — the Niche	**Decided · still open** Elevation · Plan · Section · Entrance corner · Side table	NTS	07.10.2026	5	**AST-DR-034 · 4 of 9**


ALL DIMENSIONS IN FEET & INCHES. PRINT ON A4 AT 100% / "ACTUAL SIZE" — NOT "FIT TO PAGE" — AND CHECK THE SCALE BAR. DO NOT SCALE; WORK TO FIGURED DIMENSIONS. VERIFY ON SITE.

DETAIL 2 · THE ENTRANCE CORNER

SCALE 1:15 @ A4 · PLAN · D1 OPEN ON ITS FLOOR STOP

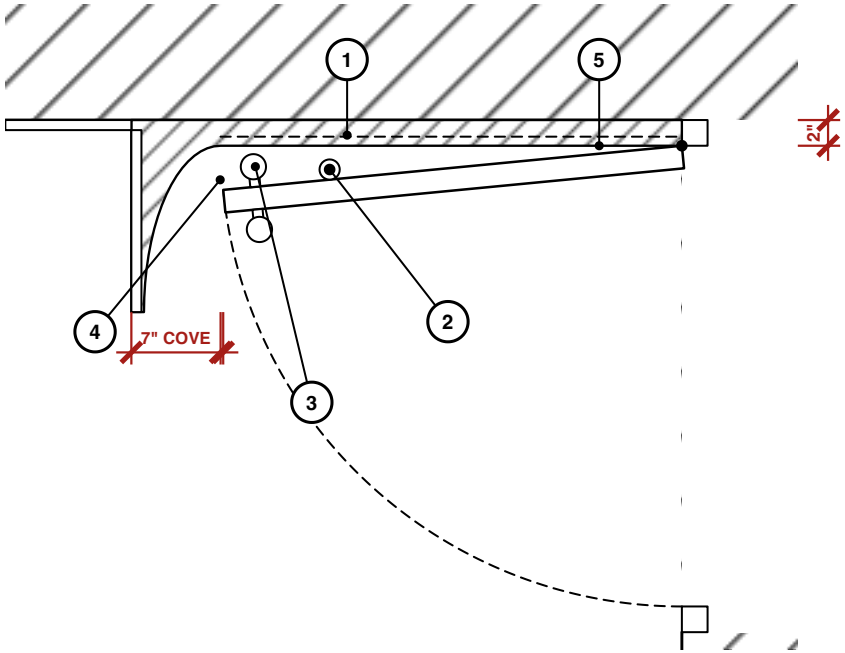

1. **THE 2 IN FACE — as deep as D1's lining, so the open leaf lies along it.**
2. **Brass floor stop, 6 in in from the knob: the leaf rests on it 5½° off the face.**
3. **The knob stays ⅝ in off the veneer.**
4. **The cove starts where the leaf ends: the whole 3 ft opening stays clear.**
5. **Marble skirting set flush with the veneer here — the leaf's heel clears it.**

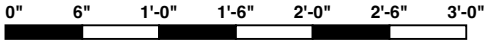


PROJECT	SHEET	SCALE	DATE	REV	DRAWING
A Study in Teak — Bed Wall — the Niche	**Detail 2 · the entrance corner** Elevation · Plan · Section · Entrance corner · Side table	1:15 @ A4	07.10.2026	5	**AST-DR-034 · 5 of 9**

ALL DIMENSIONS IN FEET & INCHES. PRINT ON A4 AT 100% / "ACTUAL SIZE" — NOT "FIT TO PAGE" — AND CHECK THE SCALE BAR. DO NOT SCALE; WORK TO FIGURED DIMENSIONS. VERIFY ON SITE.

PLAN

SCALE 1:32 (⅜" = 1'-0") @ A4 · CUT AT 4 FT · THE BED WALL AT THE TOP, THE ROOM BELOW

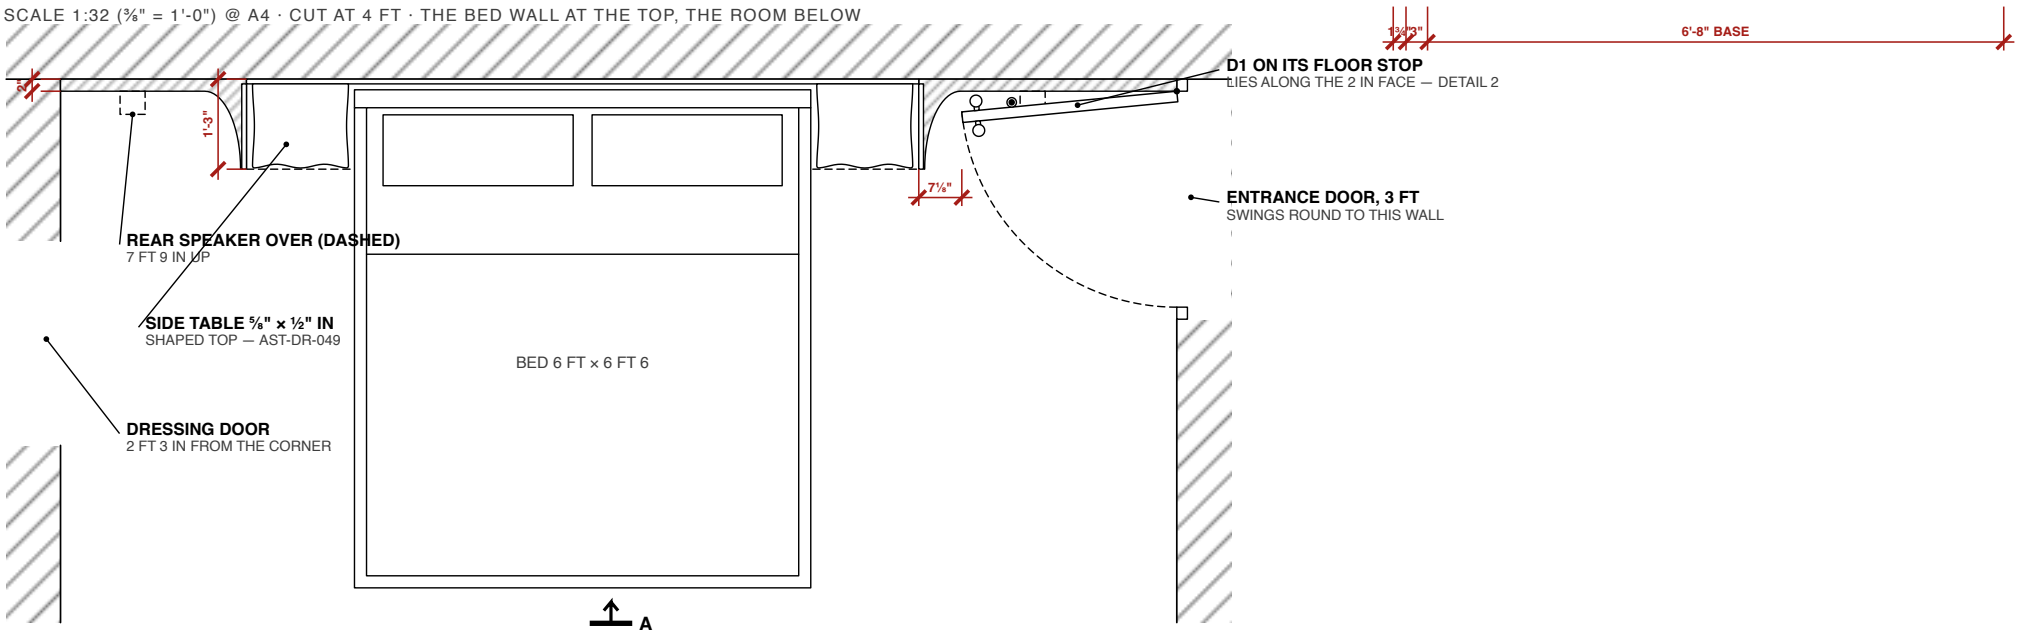


0" 1'-0" 2'-0" 3'-0" 4'-0" 5'-0" 6'-0"


PROJECT	SHEET	SCALE	DATE	REV	DRAWING
A Study in Teak — Bed Wall — the Niche	**Plan** Elevation · Plan · Section · Entrance corner · Side table	1:32 @ A4	07.10.2026	5	**AST-DR-034 · 6 of 9**

ALL DIMENSIONS IN FEET & INCHES. PRINT ON A4 AT 100% / "ACTUAL SIZE" — NOT "FIT TO PAGE" — AND CHECK THE SCALE BAR. DO NOT SCALE; WORK TO FIGURED DIMENSIONS. VERIFY ON SITE.

DETAIL 3 · THE SIDE TABLES

SCALE 1:6 (2" = 1'-0") @ A4 · FRONT AND PLAN AFTER THE OWNER'S PHOTO · IN FULL ON AST-DR-049

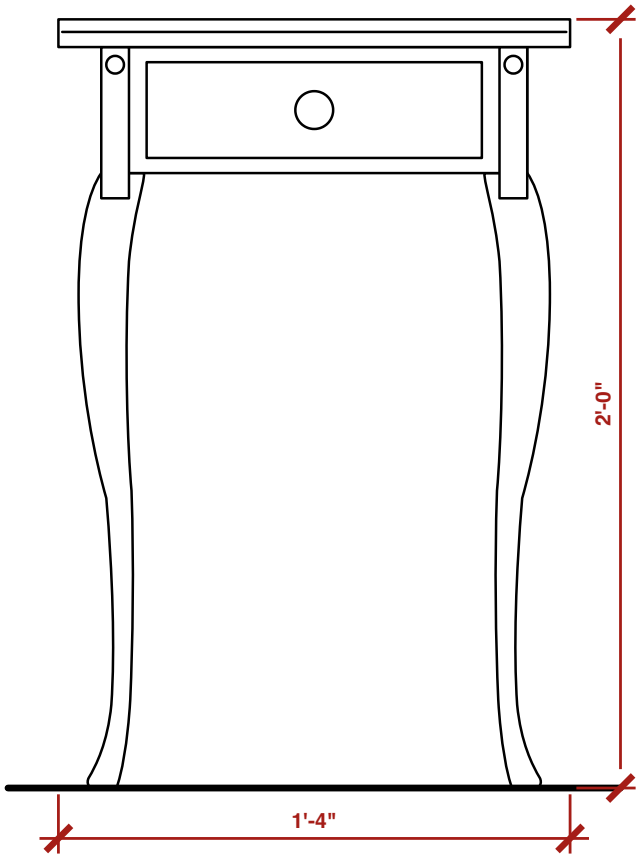


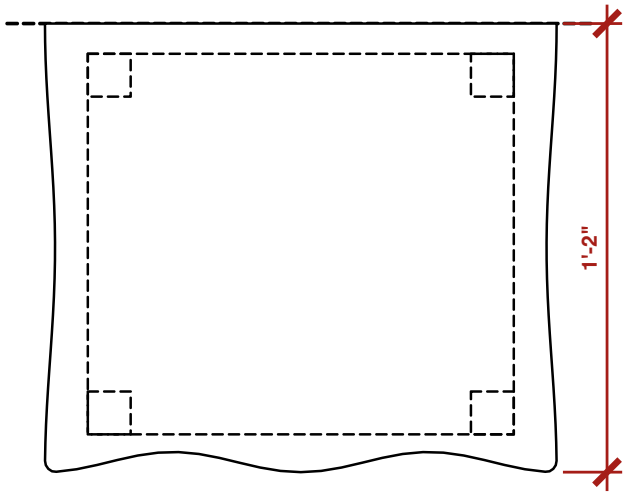

Shaped top, moulded edge — wood, no stone.

One drawer in burl, a brass rosette knob.

Carved consoles; slim cabriole legs.

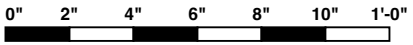

PROJECT	SHEET	SCALE	DATE	REV	DRAWING
A Study in Teak — Bed Wall — the Niche	**Detail 3 · the side tables** Elevation · Plan · Section · Entrance corner · Side table	1:6 @ A4	07.10.2026	5	**AST-DR-034 · 7 of 9**

ALL DIMENSIONS IN FEET & INCHES. PRINT ON A4 AT 100% / "ACTUAL SIZE" — NOT "FIT TO PAGE" — AND CHECK THE SCALE BAR. DO NOT SCALE; WORK TO FIGURED DIMENSIONS. VERIFY ON SITE.

NOTES

REVISION 5

From the owner's sketches and photos. The whole wall is built out 2 in

in Dark Diva veneer, polished darker (satin), on a ply carcase. Round the

niche it sweeps forward in one smooth 6 in concave cove to ⅝" in, then a

1 in flat — up both sides and across the top, no step; the veneer wrapped

over bent ply, grain running round the curve. The niche — bed and both

tables — is ⅝" in deep, all parchment plaster: back in 5 × 3 panels, sides

and soffit plain. Set square to the bed's centre line and scribed at both

corners, it hides the room's 2 in splay. Bed and headboard: AST-DR-035.

A brass lamp over each table; cove light in the ceiling, nothing else.

PROJECT	SHEET	SCALE	DATE	REV	DRAWING
A Study in Teak — Bed Wall — the Niche	**Notes** Elevation · Plan · Section · Entrance corner · Side table	NTS	07.10.2026	5	**AST-DR-034 · 8 of 9**

ALL DIMENSIONS IN FEET & INCHES. PRINT ON A4 AT 100% / "ACTUAL SIZE" — NOT "FIT TO PAGE" — AND CHECK THE SCALE BAR. DO NOT SCALE; WORK TO FIGURED DIMENSIONS. VERIFY ON SITE.

ASSUMED

TELL ME IF ANY OF THESE IS WRONG

Five panels across and three up, as sketched: each about 1 ft 10⅜ × 2 ft ⅝ in.

The 4 in white marble skirting runs along the build-out (flush with the veneer) and into the niche. The build-out runs to the ceiling.

Side tables 1" in high — the photo's table is taller; its look is kept.

Speakers: Sony's rear speakers, 4⅛" × 8½" × 3⅞" from Sony's spec page — the Bar 6 has none in the box; confirm the model before the brackets go up. Mattress 10 in (AST-DR-035).

PROJECT	SHEET	SCALE	DATE	REV	DRAWING
A Study in Teak — Bed Wall — the Niche	**Assumed** Elevation · Plan · Section · Entrance corner · Side table	NTS	07.10.2026	5	**AST-DR-034 · 9 of 9**

ALL DIMENSIONS IN FEET & INCHES. PRINT ON A4 AT 100% / "ACTUAL SIZE" — NOT "FIT TO PAGE" — AND CHECK THE SCALE BAR. DO NOT SCALE; WORK TO FIGURED DIMENSIONS. VERIFY ON SITE.