

## ELEVATION — THE BED WALL

SEEN FROM THE ROOM · DRESSING CORNER LEFT, ENTRANCE CORNER RIGHT

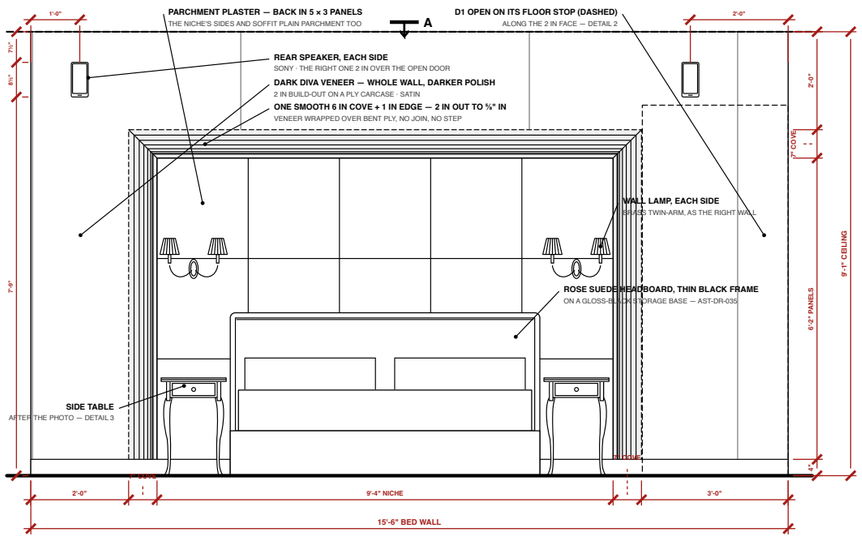


## SECTION A–A

THROUGH THE BED

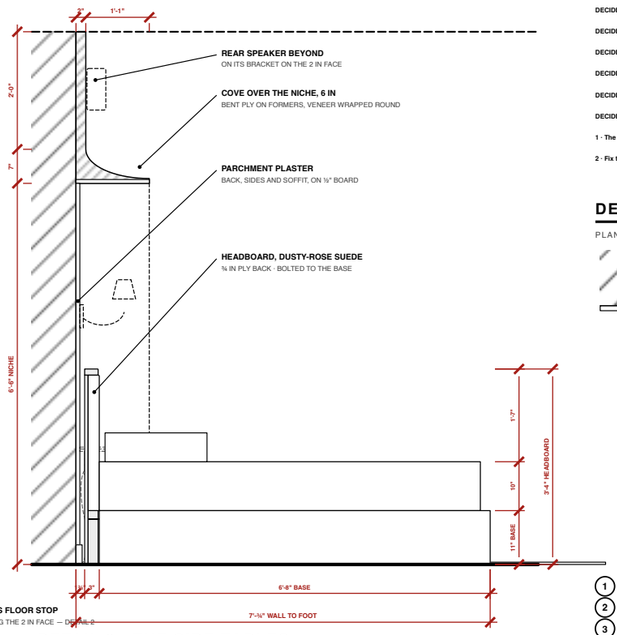


## DECIDED · STILL OPEN

OWNER, 7 OCT

**DECIDED: 2 in face all along — D1 lies along it on a floor stop (detail 2).**

**DECIDED: one smooth cove (option A); niche ¾" in; tables ¾" × ½" in.**

**DECIDED: the headboard back in rose suede, in a thin gloss-black frame.**

**DECIDED: side tables after the owner's photo, no stone (detail 3, AST-DR-049).**

**DECIDED: two rear speakers high on the plain faces, either side, clear of D1.**


**DECIDED: the bed on a storage base to the floor, no legs, in gloss black.**

**1 · The bed stands 2 ft 5¾ in clear of the TV drawers (was 2 ft 9½ in).**

**2 · Fix the lamp and speaker sockets (list B2) before the panels are made.**

## DETAIL 2 · THE ENTRANCE CORNER


PLAN · D1 OPEN ON ITS FLOOR STOP

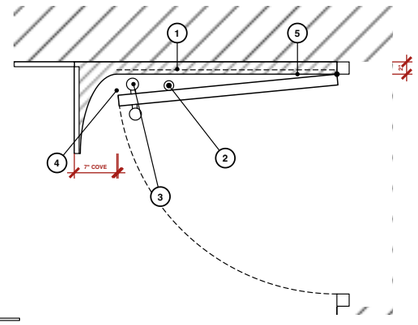


1. **THE 2 IN FACE — as deep as D1's lining, so the open leaf lies along it.**
2. **Brass floor stop, 6 in in from the knob: the leaf rests on it 5½" off the face.**
3. **The knob stays ¾ in off the veneer.**
4. **The cove starts where the leaf ends: the whole 3 ft opening stays clear.**
5. **Marble skirting set flush with the veneer here — the leaf's heel clears it.**


## PLAN

CUT AT 4 FT · THE BED WALL AT THE TOP, THE ROOM BELOW

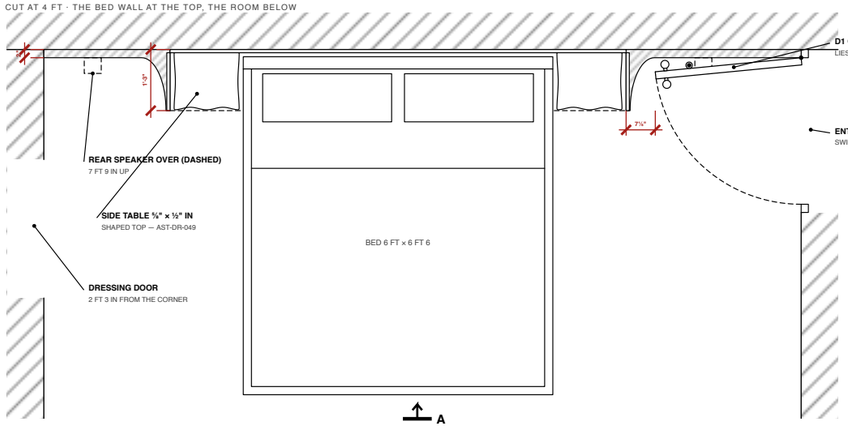


## DETAIL 3 · THE SIDE TABLES

FRONT AND PLAN AFTER THE OWNER'S PHOTO · IN FULL ON AST-DR-049

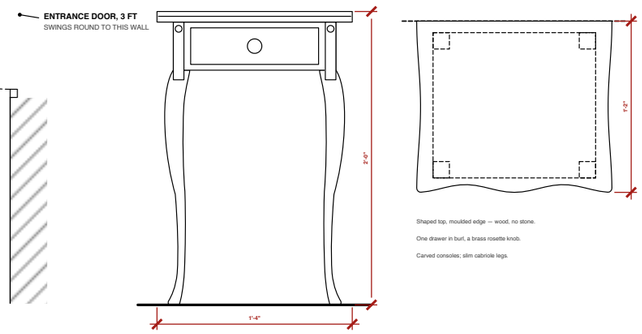


Shaped top, moulded edge — wood, no stone.

One drawer in burl, a brass rosette knob.

Carved consoles; slim cabriole legs.

## NOTES

REVISION 5

**From the owner's sketches and photos. The whole wall is built out 2 in in Dark Diva veneer, polished darker (satin), on a ply carcase. Round the niche it sweeps forward in one smooth 6 in concave cove to ¾" in, then a 1 in flat — up both sides and across the top, no step; the veneer wrapped over bent ply, grain running round the curve. The niche — bed and both tables — is ¾" in deep, all parchment plaster: back in 5 × 3 panels, sides and soffit plain. Set square to the bed's centre line and scribed at both corners, it hides the room's 2 in splay. Bed and headboard: AST-DR-035. A brass lamp over each table; cove light in the ceiling, nothing else.**

## ASSUMED

TELL ME IF ANY OF THESE IS WRONG

**Five panels across and three up, as sketched: each about 1 ft 10⅝ × 2 ft ¾ in. The 4 in white marble skirting runs along the build-out (flush with the veneer) and into the niche. The build-out runs to the ceiling. Side tables 1" in high — the photo's table is taller; its look is kept. Speakers: Sony's rear speakers, 4¼" × 8½" × 3¾" from Sony's spec page — the Bar 6 has none in the box; confirm the model before the brackets go up. Mattress 10 in (AST-DR-035).**

## A STUDY IN TEAK

Particulars of the room

## BED WALL — THE NICHE

Elevation · Plan · Section · Entrance corner · Side table


| SCALE | DATE |
|---|---|
| **AS NOTED @ A3** | **07.10.2026** |
| REV | DWG |
| **5 — 2 in face, 15 in niche; headboard; new side tables; speakers** | **AST-DR-034** |

| PROJECT | SHEET | SCALE | DATE | REV | DRAWING |
|---|---|---|---|---|---|
| A Study in Teak — Bed Wall — the Niche | **General arrangement — the whole sheet** each view follows at its own scale, pages 2 to 9 | NTS | 07.10.2026 | 5 | **AST-DR-034 · 1 of 9** |

ALL DIMENSIONS IN FEET & INCHES. PRINT ON A3 AT 100% / "ACTUAL SIZE" — NOT "FIT TO PAGE" — AND CHECK THE SCALE BAR. DO NOT SCALE; WORK TO FIGURED DIMENSIONS. VERIFY ON SITE.

# ELEVATION — THE BED WALL

SCALE 1:20 @ A3 · SEEN FROM THE ROOM · DRESSING CORNER LEFT, ENTRANCE CORNER RIGHT

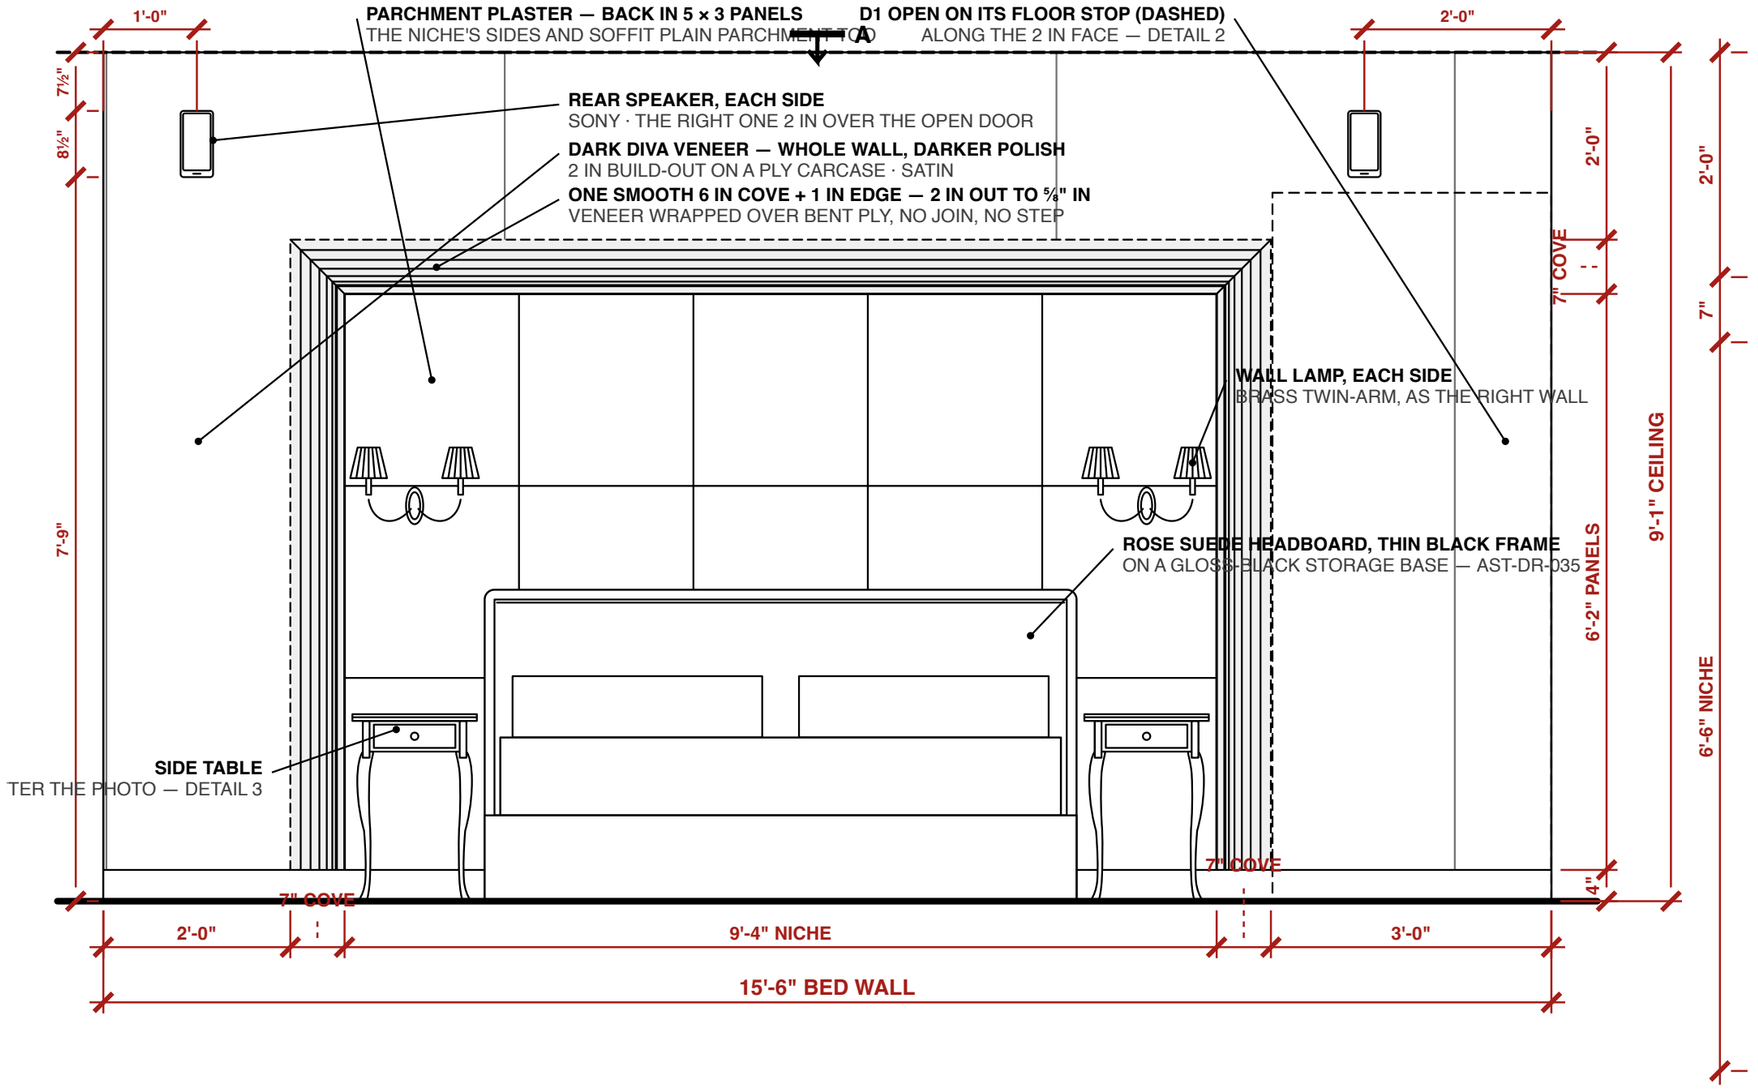



0" 1'-0" 2'-0" 3'-0" 4'-0" 5'-0" 6'-0"

| PROJECT | SHEET | SCALE | DATE | REV | DRAWING |
|---|---|---|---|---|---|
| A Study in Teak — Bed Wall — the Niche | **Elevation — the bed wall**<br>Elevation · Plan · Section · Entrance corner · Side table | 1:20 @ A3 | 07.10.2026 | 5 | **AST-DR-034 · 2 of 9** |

ALL DIMENSIONS IN FEET & INCHES. PRINT ON A3 AT 100% / "ACTUAL SIZE" — NOT "FIT TO PAGE" — AND CHECK THE SCALE BAR. DO NOT SCALE; WORK TO FIGURED DIMENSIONS. VERIFY ON SITE.

## SECTION A–A

SCALE 1:16 (¾" = 1'-0") @ A3 · THROUGH THE BED

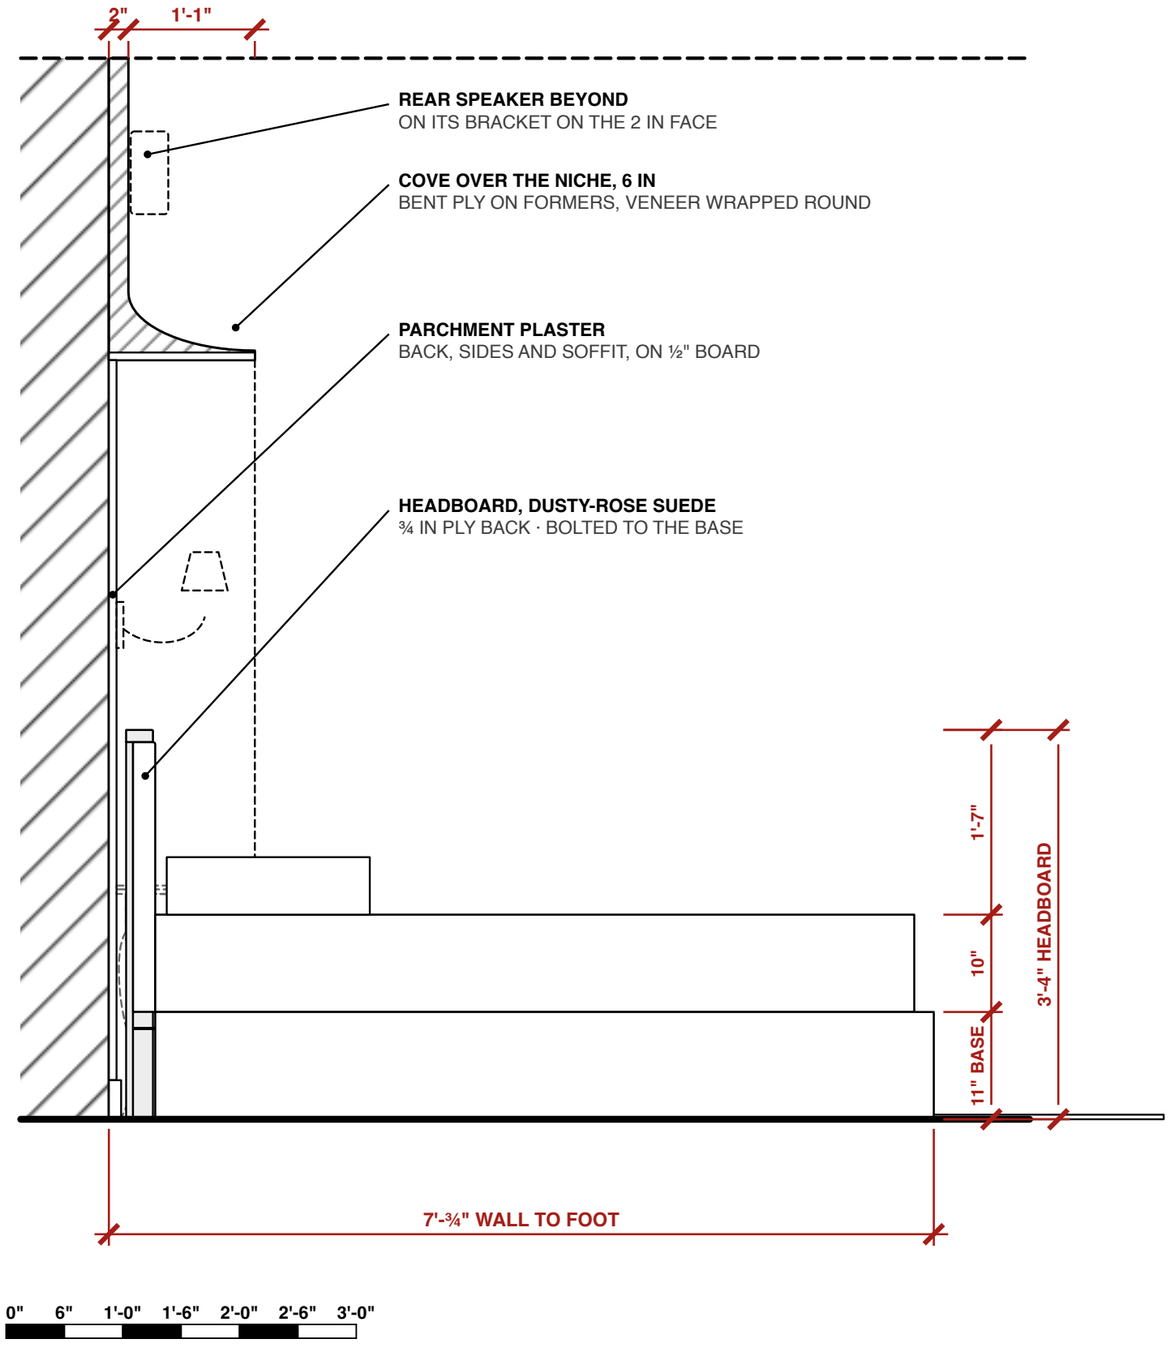





| PROJECT | SHEET | SCALE | DATE | REV | DRAWING |
|---|---|---|---|---|---|
| A Study in Teak — Bed Wall — the Niche | **Section A–A**<br>Elevation · Plan · Section · Entrance corner · Side table | 1:16 @ A3 | 07.10.2026 | 5 | **AST-DR-034 · 3 of 9** |

ALL DIMENSIONS IN FEET & INCHES. PRINT ON A3 AT 100% / "ACTUAL SIZE" — NOT "FIT TO PAGE" — AND CHECK THE SCALE BAR. DO NOT SCALE; WORK TO FIGURED DIMENSIONS. VERIFY ON SITE.

# DECIDED · STILL OPEN

OWNER, 7 OCT

**DECIDED: 2 in face all along — D1 lies along it on a floor stop (detail 2).**

**DECIDED: one smooth cove (option A); niche ⅝" in; tables ⅝" × ½" in.**

**DECIDED: the headboard back in rose suede, in a thin gloss-black frame.**

**DECIDED: side tables after the owner's photo, no stone (detail 3, AST-DR-049).**

**DECIDED: two rear speakers high on the plain faces, either side, clear of D1.**

**DECIDED: the bed on a storage base to the floor, no legs, in gloss black.**

**1 · The bed stands 2 ft 5⅜ in clear of the TV drawers (was 2 ft 9¾ in).**


**2 · Fix the lamp and speaker sockets (list B2) before the panels are made.**

| PROJECT | SHEET | SCALE | DATE | REV | DRAWING |
|---|---|---|---|---|---|
| A Study in Teak — Bed Wall — the Niche | **Decided · still open**<br>Elevation · Plan · Section · Entrance corner · Side table | NTS | 07.10.2026 | 5 | **AST-DR-034 · 4 of 9** |

ALL DIMENSIONS IN FEET & INCHES. PRINT ON A3 AT 100% / "ACTUAL SIZE" — NOT "FIT TO PAGE" — AND CHECK THE SCALE BAR. DO NOT SCALE; WORK TO FIGURED DIMENSIONS. VERIFY ON SITE.

# DETAIL 2 · THE ENTRANCE CORNER

SCALE 1:10 @ A3 · PLAN · D1 OPEN ON ITS FLOOR STOP

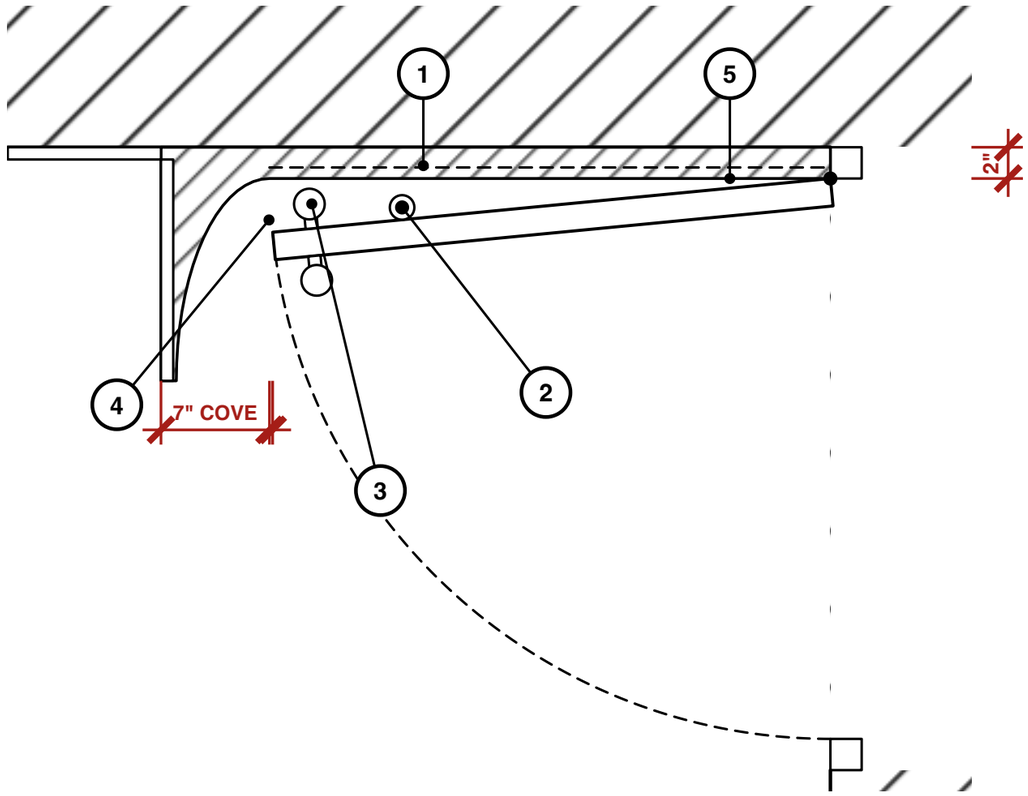


1. **THE 2 IN FACE — as deep as D1's lining, so the open leaf lies along it.**
2. **Brass floor stop, 6 in in from the knob: the leaf rests on it 5½° off the face.**
3. **The knob stays ⅝ in off the veneer.**
4. **The cove starts where the leaf ends: the whole 3 ft opening stays clear.**
5. **Marble skirting set flush with the veneer here — the leaf's heel clears it.**


0" 6" 1'-0" 1'-6" 2'-0" 2'-6" 3'-0"

| PROJECT | SHEET | SCALE | DATE | REV | DRAWING |
|---|---|---|---|---|---|
| A Study in Teak — Bed Wall — the Niche | **Detail 2 · the entrance corner**<br>Elevation · Plan · Section · Entrance corner · Side table | 1:10 @ A3 | 07.10.2026 | 5 | **AST-DR-034 · 5 of 9** |

ALL DIMENSIONS IN FEET & INCHES. PRINT ON A3 AT 100% / "ACTUAL SIZE" — NOT "FIT TO PAGE" — AND CHECK THE SCALE BAR. DO NOT SCALE; WORK TO FIGURED DIMENSIONS. VERIFY ON SITE.

## PLAN

SCALE 1:24 (½" = 1'-0") @ A3 · CUT AT 4 FT · THE BED WALL AT THE TOP, THE ROOM BELOW

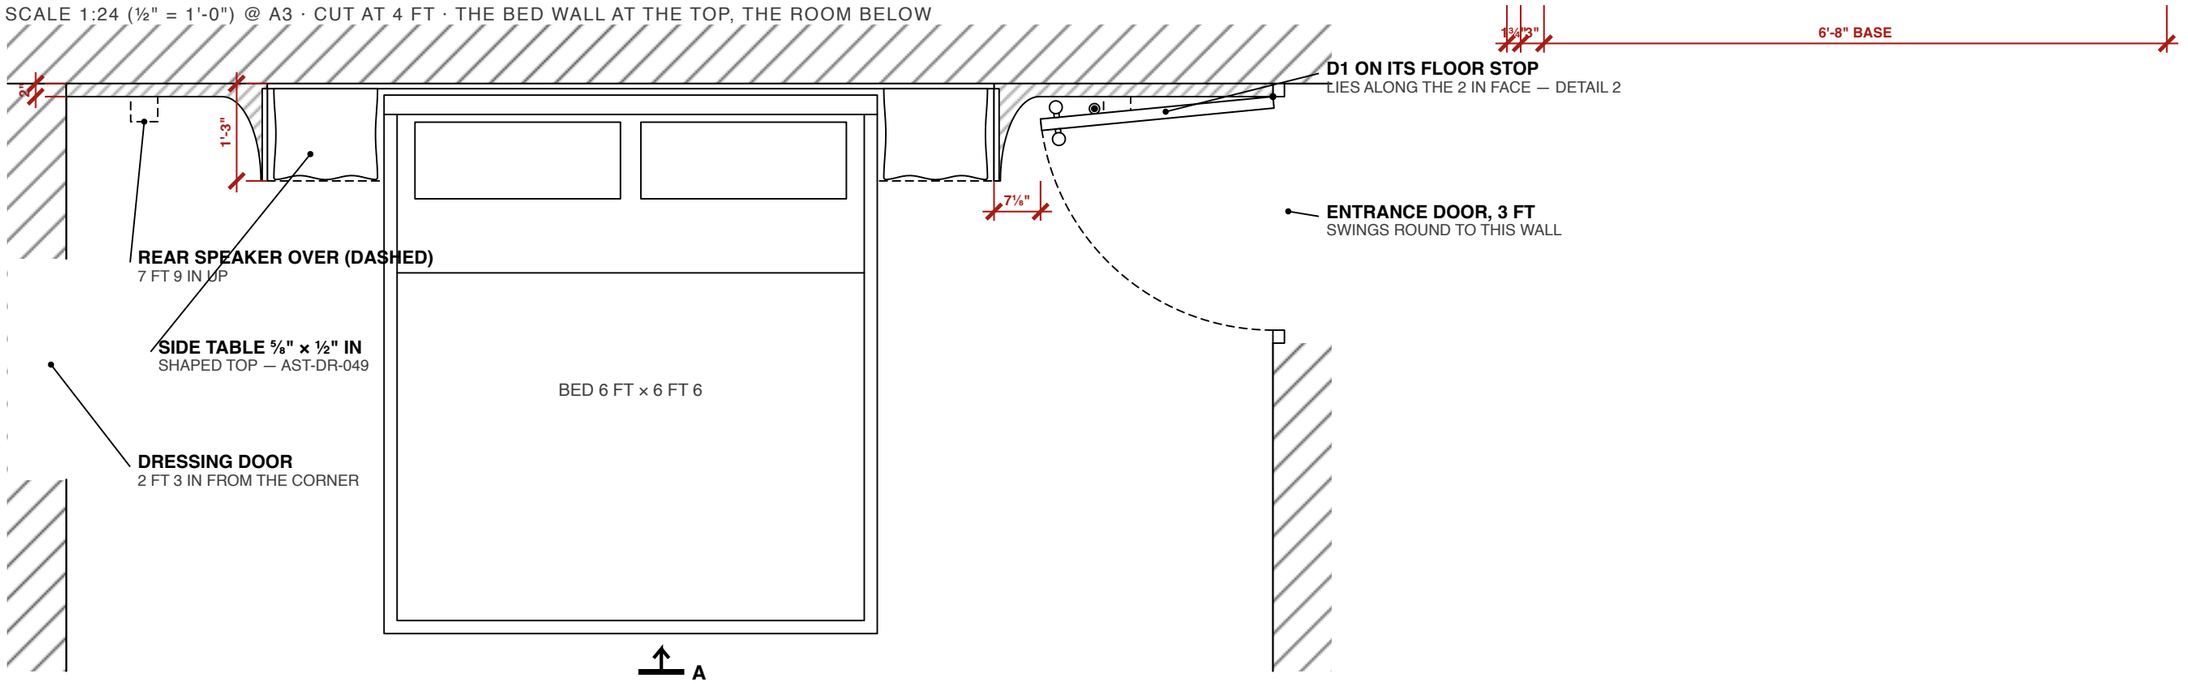



0" 1'-0" 2'-0" 3'-0" 4'-0" 5'-0" 6'-0"


| PROJECT | SHEET | SCALE | DATE | REV | DRAWING |
|---|---|---|---|---|---|
| A Study in Teak — Bed Wall — the Niche | **Plan**<br>Elevation · Plan · Section · Entrance corner · Side table | 1:24 @ A3 | 07.10.2026 | 5 | **AST-DR-034 · 6 of 9** |

ALL DIMENSIONS IN FEET & INCHES. PRINT ON A3 AT 100% / "ACTUAL SIZE" — NOT "FIT TO PAGE" — AND CHECK THE SCALE BAR. DO NOT SCALE; WORK TO FIGURED DIMENSIONS. VERIFY ON SITE.

# DETAIL 3 · THE SIDE TABLES

SCALE 1:4 (3" = 1'-0") @ A3 · FRONT AND PLAN AFTER THE OWNER'S PHOTO · IN FULL ON AST-DR-049

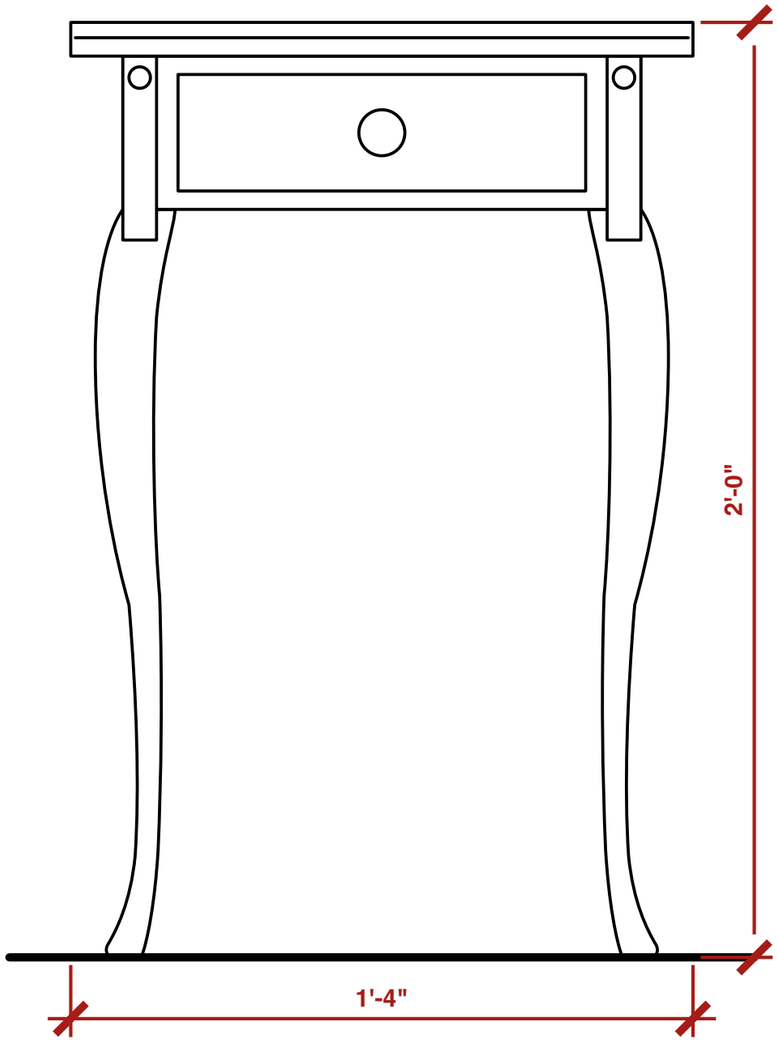


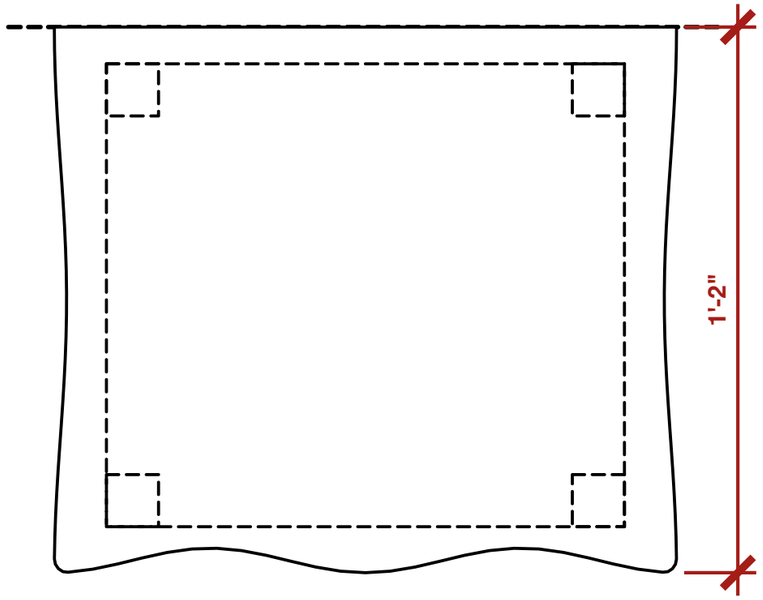
Shaped top, moulded edge — wood, no stone.

One drawer in burl, a brass rosette knob.

Carved consoles; slim cabriole legs.

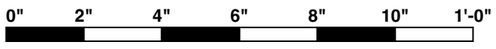


| PROJECT | SHEET | SCALE | DATE | REV | DRAWING |
|---|---|---|---|---|---|
| A Study in Teak — Bed Wall — the Niche | **Detail 3 · the side tables**<br>Elevation · Plan · Section · Entrance corner · Side table | 1:4 @ A3 | 07.10.2026 | 5 | **AST-DR-034 · 7 of 9** |

ALL DIMENSIONS IN FEET & INCHES. PRINT ON A3 AT 100% / "ACTUAL SIZE" — NOT "FIT TO PAGE" — AND CHECK THE SCALE BAR. DO NOT SCALE; WORK TO FIGURED DIMENSIONS. VERIFY ON SITE.

# NOTES

REVISION 5

**From the owner's sketches and photos. The whole wall is built out 2 in in Dark Diva veneer, polished darker (satin), on a ply carcase. Round the niche it sweeps forward in one smooth 6 in concave cove to ⅝" in, then a 1 in flat — up both sides and across the top, no step; the veneer wrapped over bent ply, grain running round the curve. The niche — bed and both tables — is ⅝" in deep, all parchment plaster: back in 5 × 3 panels, sides and soffit plain. Set square to the bed's centre line and scribed at both corners, it hides the room's 2 in splay. Bed and headboard: AST-DR-035.**

**A brass lamp over each table; cove light in the ceiling, nothing else.**

| PROJECT | SHEET | SCALE | DATE | REV | DRAWING |
|---|---|---|---|---|---|
| A Study in Teak — Bed Wall — the Niche | **Notes**<br>Elevation · Plan · Section · Entrance corner · Side table | NTS | 07.10.2026 | 5 | **AST-DR-034 · 8 of 9** |

ALL DIMENSIONS IN FEET & INCHES. PRINT ON A3 AT 100% / “ACTUAL SIZE” — NOT “FIT TO PAGE” — AND CHECK THE SCALE BAR. DO NOT SCALE; WORK TO FIGURED DIMENSIONS. VERIFY ON SITE.

# ASSUMED

## TELL ME IF ANY OF THESE IS WRONG

**Five panels across and three up, as sketched: each about 1 ft 10⅜ × 2 ft ⅝ in.**

**The 4 in white marble skirting runs along the build-out (flush with the**

**veneer) and into the niche. The build-out runs to the ceiling.**

**Side tables 1" in high — the photo's table is taller; its look is kept.**

**Speakers: Sony's rear speakers, 4⅛" × 8½" × 3⅞" from Sony's spec**

**page — the Bar 6 has none in the box; confirm the model before the**

**brackets go up. Mattress 10 in (AST-DR-035).**

| PROJECT | SHEET | SCALE | DATE | REV | DRAWING |
|---|---|---|---|---|---|
| A Study in Teak — Bed Wall — the Niche | **Assumed**<br>Elevation · Plan · Section · Entrance corner · Side table | NTS | 07.10.2026 | 5 | **AST-DR-034 · 9 of 9** |

ALL DIMENSIONS IN FEET & INCHES. PRINT ON A3 AT 100% / “ACTUAL SIZE” — NOT “FIT TO PAGE” — AND CHECK THE SCALE BAR. DO NOT SCALE; WORK TO FIGURED DIMENSIONS. VERIFY ON SITE.