



ELEVATION — STUDY WALL, WITH THE ARCHES

SEEN FROM THE ROOM - CURTAINS NOT DRAWN

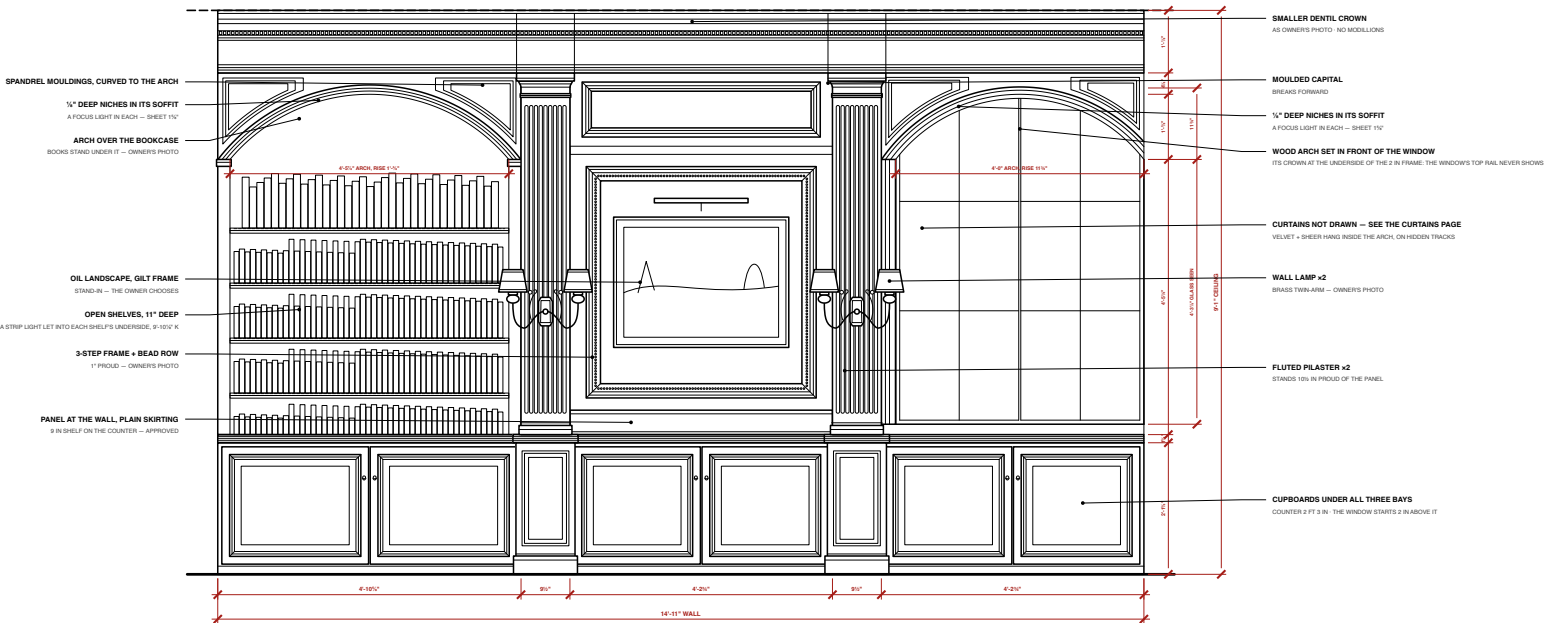

PLAN

CUT AT 3'-11 1/2" - WALL AT THE TOP - OVERHEAD AND BELOW DASHED

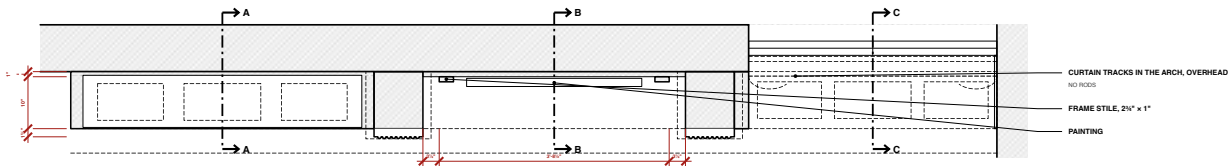

NOTES

REVISION 4

Owner's second scheme (7 Oct). Arches over the bookcase and the window, three deep rectangular niches cut into each

arch's underside - a focus light in each (8 Oct) - and spandrel mouldings curved to follow the arch. The window's glass is unchanged: the wood arch

is a veneered panel set in front of the window's top: its crown sits at the underside of the window's 2" top rail, so the window's top rail is hidden and only glass shows; both arches spring at one line. Curtains not drawn.

Centre: the panel goes back to the wall plane, so the counter is a 5" in shelf and the pilasters stand 10" in proud (approved).

Mouldings, crown and lamp from the owner's photos. Sections: AST-DR-042. Details: AST-DR-043.

A STUDY IN TEAK

Particulars of the room

STUDY WALL — WITH ARCHES

Elevation - Plan

SCALE

1:20 @ A3

REV

DATE

09.10.2026

DWG

AST-DR-040

PROJECT

A Study in Teak — Study Wall — With Arches

SHEET

General arrangement — the whole sheet

each view follows at its own scale, pages 2 to 3

SCALE

NTS

DATE

09.10.2026

REV



4

DRAWING

AST-DR-040 · 1 of 16

PLAN

SCALE 1:25 @ A4 · CUT AT 3'-11 1/4" · WALL AT THE TOP · OVERHEAD AND BELOW DASHED

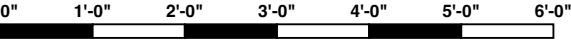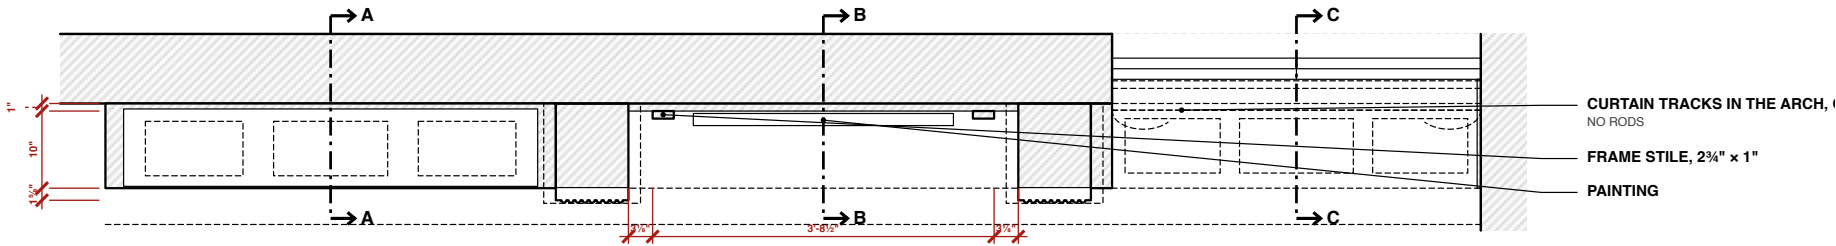

PROJECT
A Study in Teak — Study Wall — With Arches

SHEET
Plan
Elevation · Plan

SCALE
1:25 @ A4

DATE
09.10.2026

REV
4

DRAWING
AST-DR-040 · 2 of 16

NOTES

REVISION 4


Owner's second scheme (7 Oct). Arches over the bookcase and the window, three deep rectangular niches cut into each arch's underside — a focus light in each (8 Oct) — and spandrel mouldings curved to follow the arch. The window's glass is unchanged: the wood arch is a veneered panel set in front of the window's top: its crown sits at the underside of the window's 2 in top rail, so the window's top rail is hidden and only glass shows; both arches spring at one line. Curtains: the panel goes back to the wall plane, so the counter is a 9 in shelf and the pilasters stand 10½ in proud (approved).

Mouldings, crown and lamp from the owner's photos. Sections: AST-DR-042. Details: AST-DR-043.

PROJECT	SHEET	SCALE	DATE	REV	DRAWING
A Study in Teak — Study Wall — With Arches	Notes Elevation · Plan	NTS	09.10.2026	4	AST-DR-040 · 3 of 16


SECTION A-A

THROUGH THE BOOKCASE AT THE ARCH'S CROWN

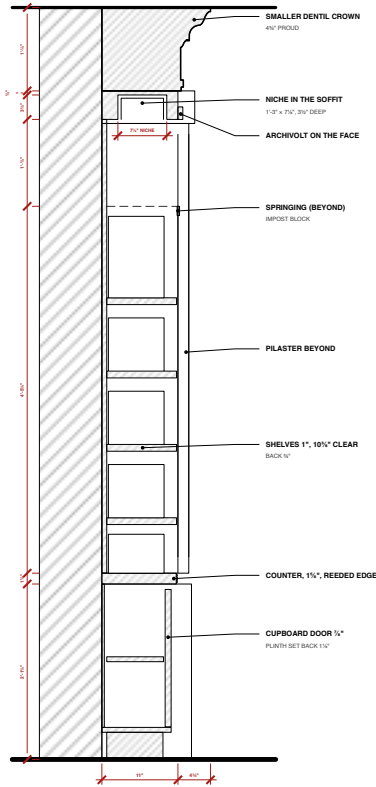


SECTION B-B

THROUGH THE CENTRE BAY AND PAINTING

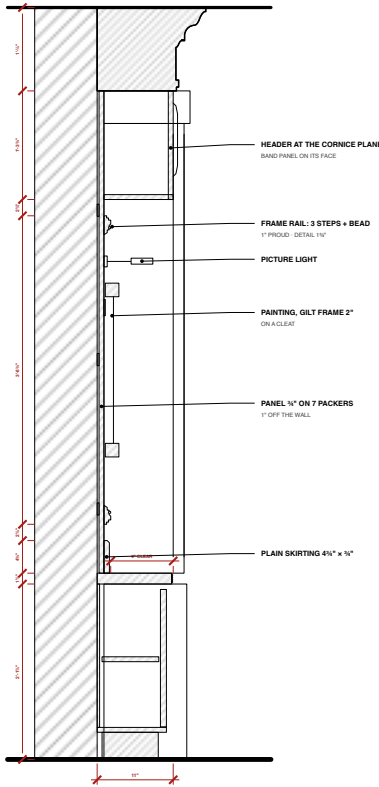

SECTION C-C

THROUGH THE WINDOW AT THE ARCH'S CROWN

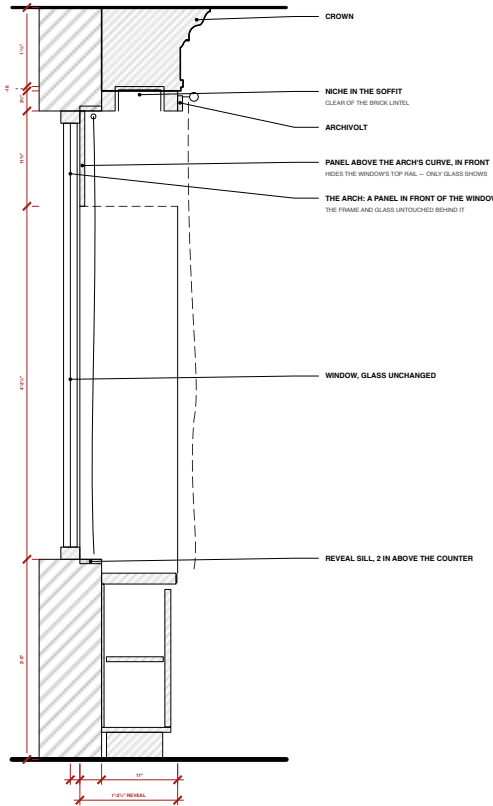

NOTES

REVISION 4

All three cut looking along the wall to the right (not lines on AST-DR-042's plan). Each arch's head is a ply former, veneered;
its three niches are boxes set into it, 3 1/2\"/>

A STUDY IN TEAK

Particulars of the room

STUDY WALL - SECTIONS

A-A bookcase - B-B centre - C-C window

SCALE

1:15 @ A3

DATE

09.10.2026

REV

DWG

AST-DR-042

PROJECT
A Study in Teak — Study Wall — Sections

SHEET
General arrangement — the whole sheet
each view follows at its own scale, pages 5 to 7

SCALE
NTS



DATE
09.10.2026

REV
4

DRAWING
AST-DR-042 · 4 of 16

SECTION A-A

SCALE 1:24 (1/2" = 1'-0") @ A4 · THROUGH THE BOOKCASE AT THE ARCH'S CRO1

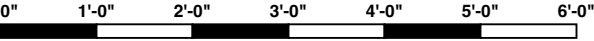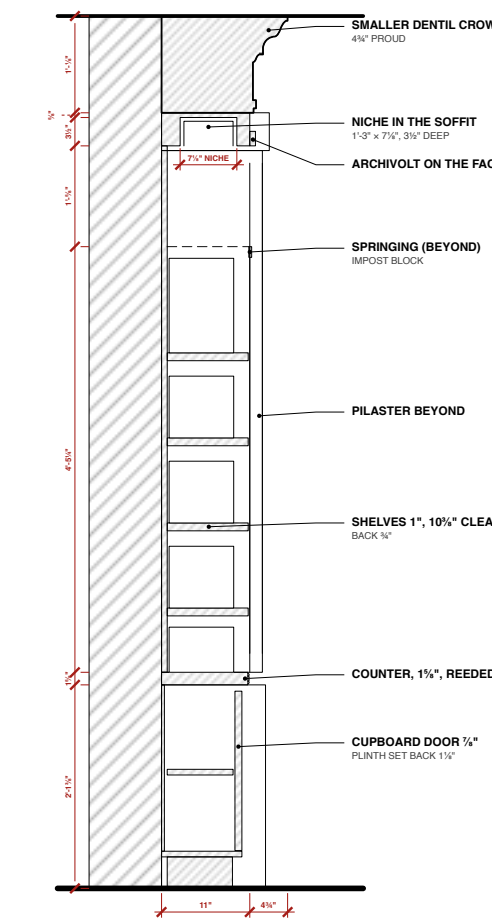

PROJECT
A Study in Teak — Study Wall — Sections

SHEET
Section A-A
A-A bookcase · B-B centre · C-C window

SCALE
1:24 @ A4



DATE
09.10.2026

REV
4

DRAWING
AST-DR-042 · 5 of 16

SECTION B-B

SCALE 1:24 (1/2" = 1'-0") @ A4 · THROUGH THE CENTRE BAY AND PAINTING

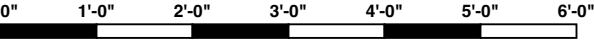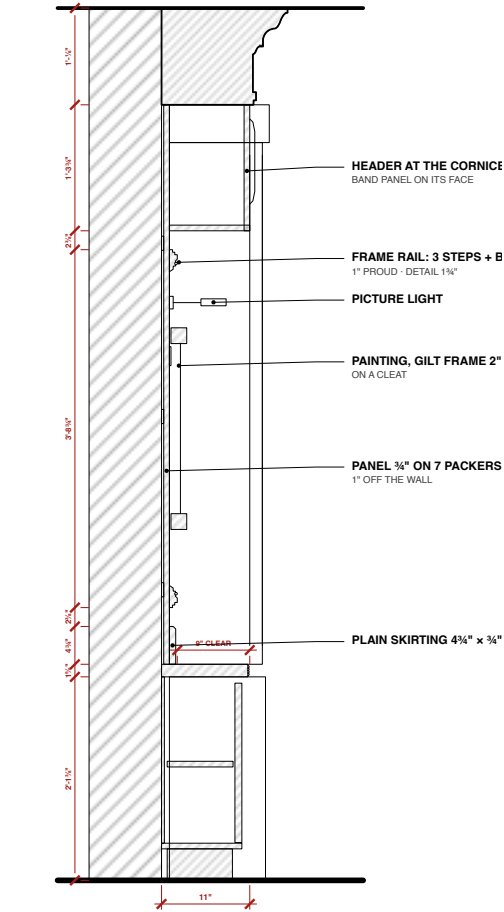

PROJECT
A Study in Teak — Study Wall — Sections

SHEET
Section B-B
A-A bookcase · B-B centre · C-C window

SCALE
1:24 @ A4

DATE
09.10.2026

REV
4

DRAWING
AST-DR-042 · 6 of 16

NOTES

REVISION 4


All three cut looking along the wall to the right (cut lines on AST-DR-040's plan). Each arch's head is a ply former, veneered; its three niches are boxes let into it, 3½" deep, lined in the same veneer, a small focus light (9'-10⅛" K) in the middle of each. The window's niches stay in the timber, in front of the brick lintel. The window bay's panelling now runs at 11" like the rest, so the crown is one plane and the reveal ½" in.

Centre: panel at the wall plane, header at the cornice plane — the counter becomes a 9 in shelf under it. Details: AST-DR-043.

PROJECT	SHEET	SCALE	DATE	REV	DRAWING
A Study in Teak — Study Wall — Sections	Notes A–A bookcase · B–B centre · C–C window	NTS	09.10.2026	4	AST-DR-042 · 7 of 16


1 · BOOKCASE ARCH — ITS UNDERSIDE

LOOKING UP, UNROLLED FLAT - WALL AT THE TOP, ROOM BELOW

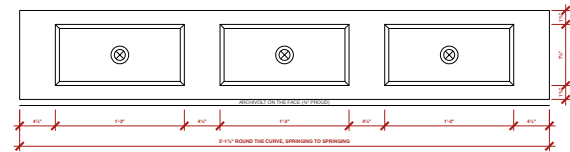


2 · WINDOW ARCH — ITS UNDERSIDE

LOOKING UP, UNROLLED FLAT

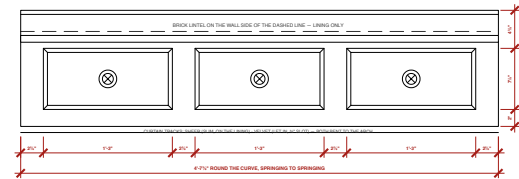


3 · A NICHE IN SECTION

ACROSS THE SOFFIT AT THE CROWN

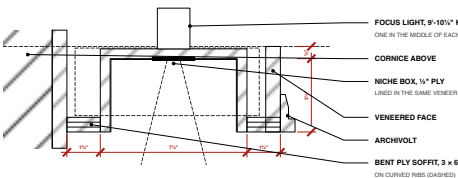


4 · THE CROWN

SECTION - OWNER'S PHOTO

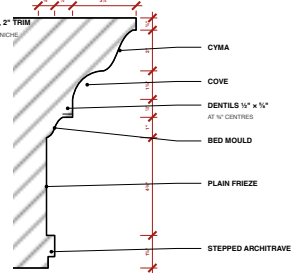


5 · THE PAINTING FRAME

SECTION + FACE - BEAD ROW, OWNER'S PHOTO

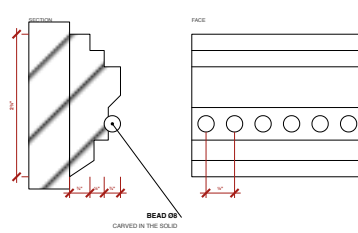


7 · SPANDREL MOULDING

SECTION

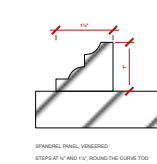

6 · SKIRTING + COUNTER

SECTION

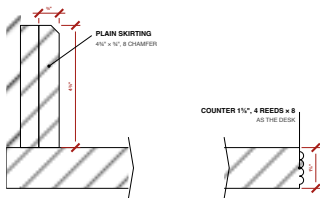

NOTES

REVISION 4

Details for AST-DR-043/042 (and 041/044 except the arches). Mouldings from the owner's photos; profiles to be mocked up full size before cutting. Each niche has one small focus light, 9'-10 1/2" K, in the middle of its top (owner, 8 Oct). All timber in the room's teak veneer; no colour in this set.

A STUDY IN TEAK

Particulars of the room

STUDY WALL — DETAILS

Niches · crown · frame · skirting

SCALE

AS NOTED @ A3

DATE

09.10.2026

REV

2 — niche lights (owner, 8 Oct); niches for the arches only

DWG

AST-DR-043

PROJECT
A Study in Teak — Study Wall — Details

SHEET
General arrangement — the whole sheet
each view follows at its own scale, pages 9 to 16

SCALE
NTS



DATE
09.10.2026

REV
2

DRAWING
AST-DR-043 · 8 of 16

1 · BOOKCASE ARCH — ITS UNDERSIDE

SCALE 1:8 (1½" = 1'-0") @ A4 · LOOKING UP, UNROLLED FLAT · WALL AT THE TOP, ROOM BELOW

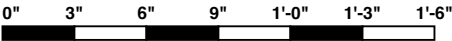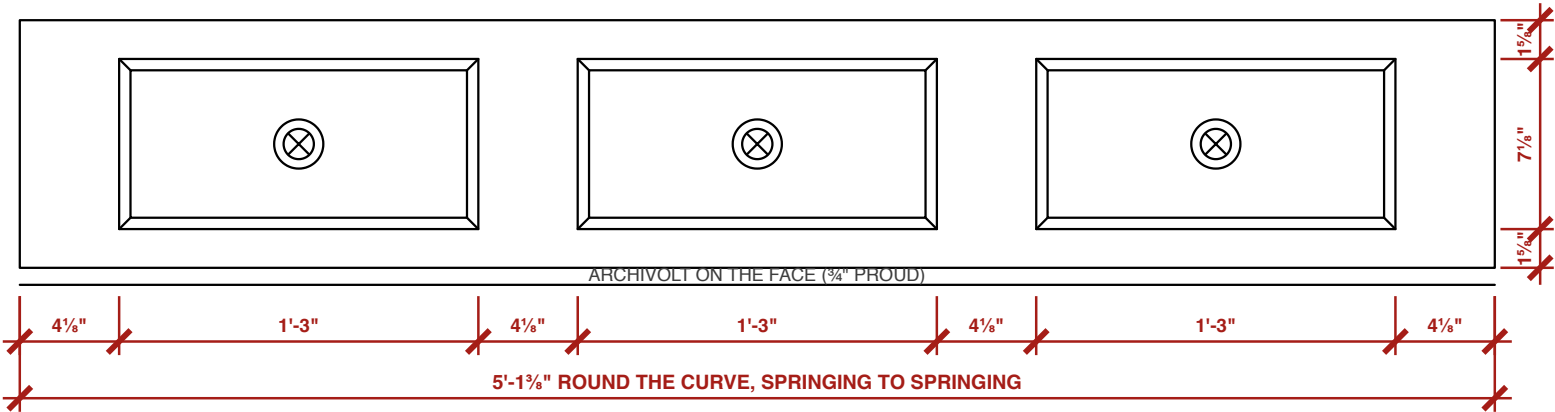

PROJECT
A Study in Teak — Study Wall — Details

SHEET
1 · bookcase arch — its underside
Niches · crown · frame · skirting

SCALE
1:8 @ A4



DATE
09.10.2026

REV
2

DRAWING
AST-DR-043 · 9 of 16

2 · WINDOW ARCH — ITS UNDERSIDE



SCALE 1:6 (2" = 1'-0") @ A4 · LOOKING UP, UNROLLED FLAT

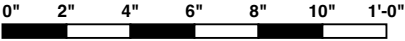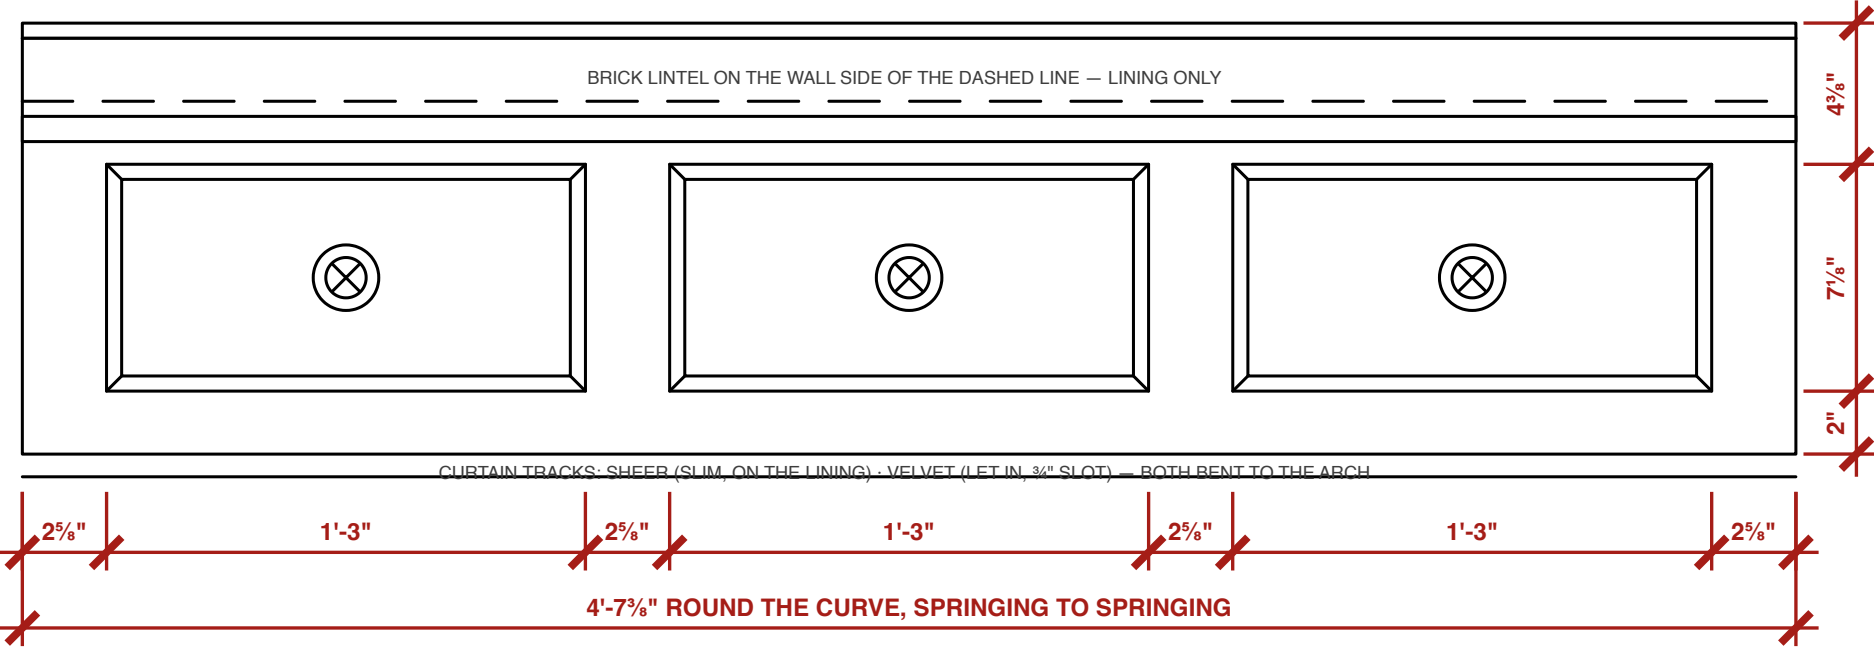

PROJECT	SHEET	SCALE	DATE	REV	DRAWING
A Study in Teak — Study Wall — Details	2 · window arch — its underside Niches · crown · frame · skirting	1:6 @ A4	09.10.2026	2	AST-DR-043 · 10 of 16

3 · A NICHE IN SECTION

SCALE 1:3 (4" = 1'-0") @ A4 · ACROSS THE SOFFIT AT THE CROWN

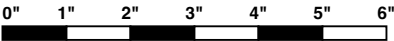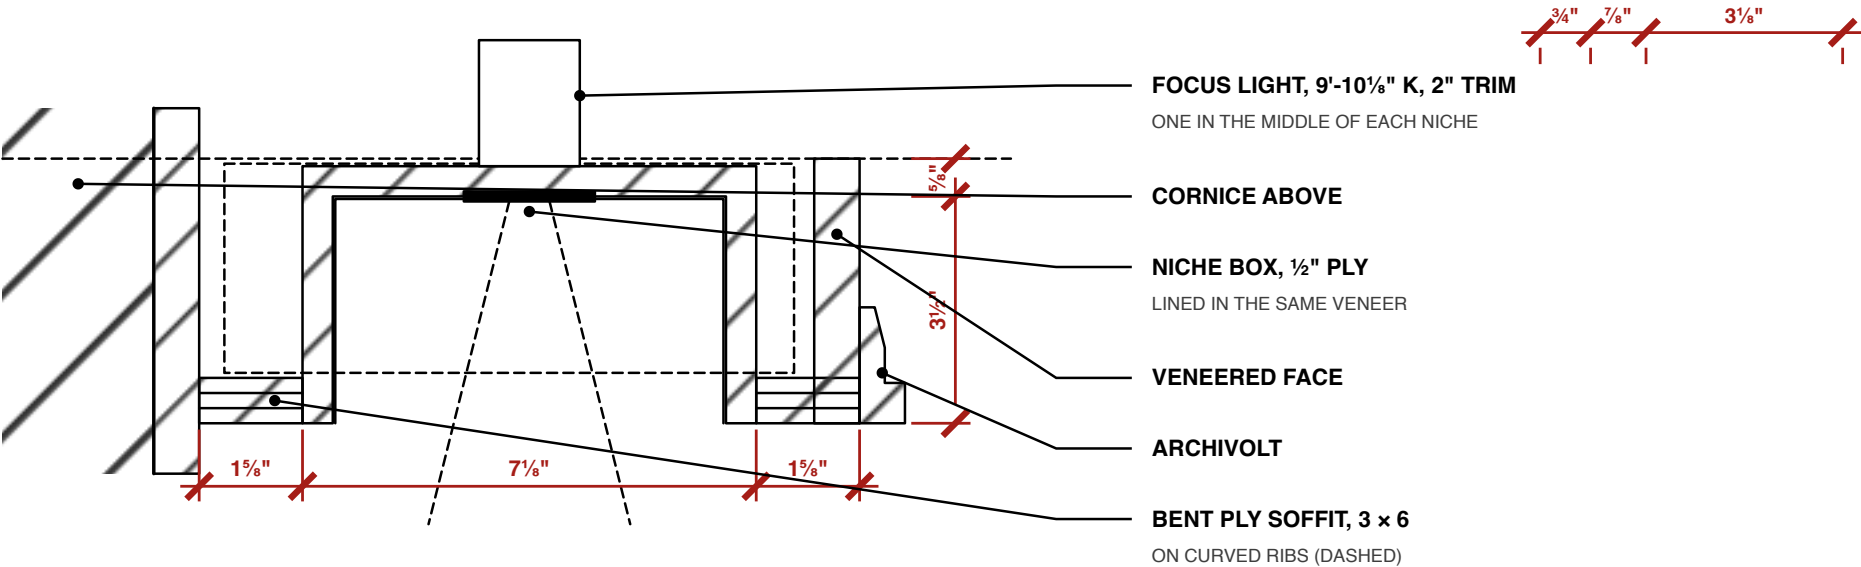

PROJECT
A Study in Teak — Study Wall — Details

SHEET
3 · a niche in section
Niches · crown · frame · skirting

SCALE
1:3 @ A4


DATE
09.10.2026

REV
2

DRAWING
AST-DR-043 · 11 of 16

4 · THE CROWN



SCALE 1:3 (4" = 1'-0") @ A4 · SECTION · OWNER'S PHOTO

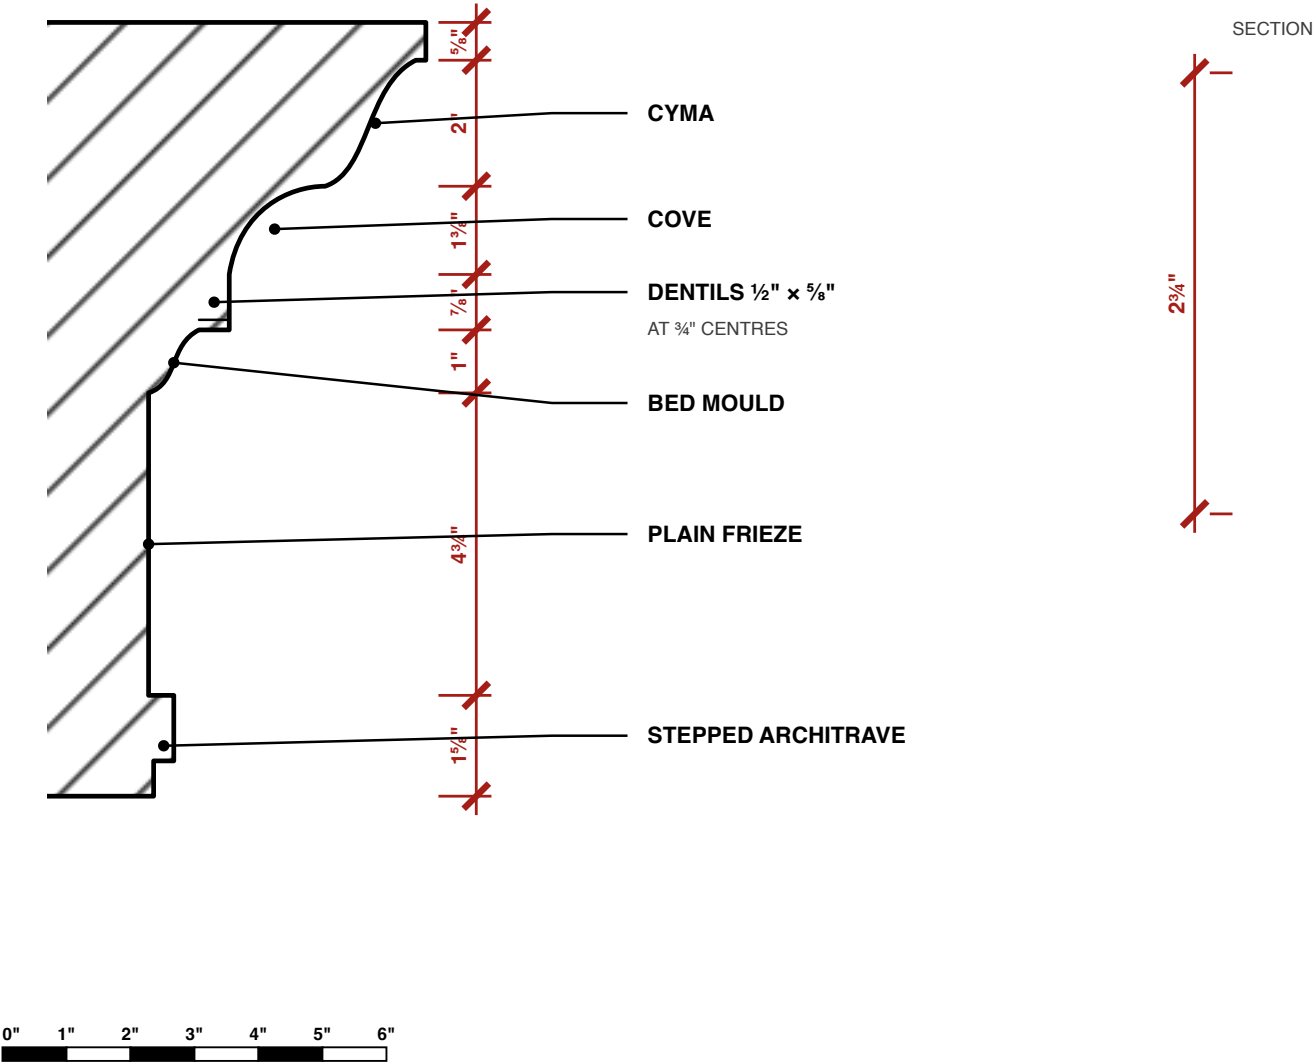

PROJECT A Study in Teak — Study Wall — Details	SHEET 4 · the crown Niches · crown · frame · skirting	SCALE 1:3 @ A4	DATE 09.10.2026	REV 2	DRAWING AST-DR-043 · 12 of 16
---	---	-------------------	--------------------	----------	----------------------------------

5 · THE PAINTING FRAME

SCALE 1:1 (FULL SIZE) @ A4 · SECTION + FACE · BEAD ROW, OWNER'S PHOTO

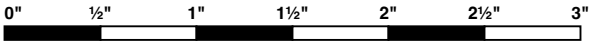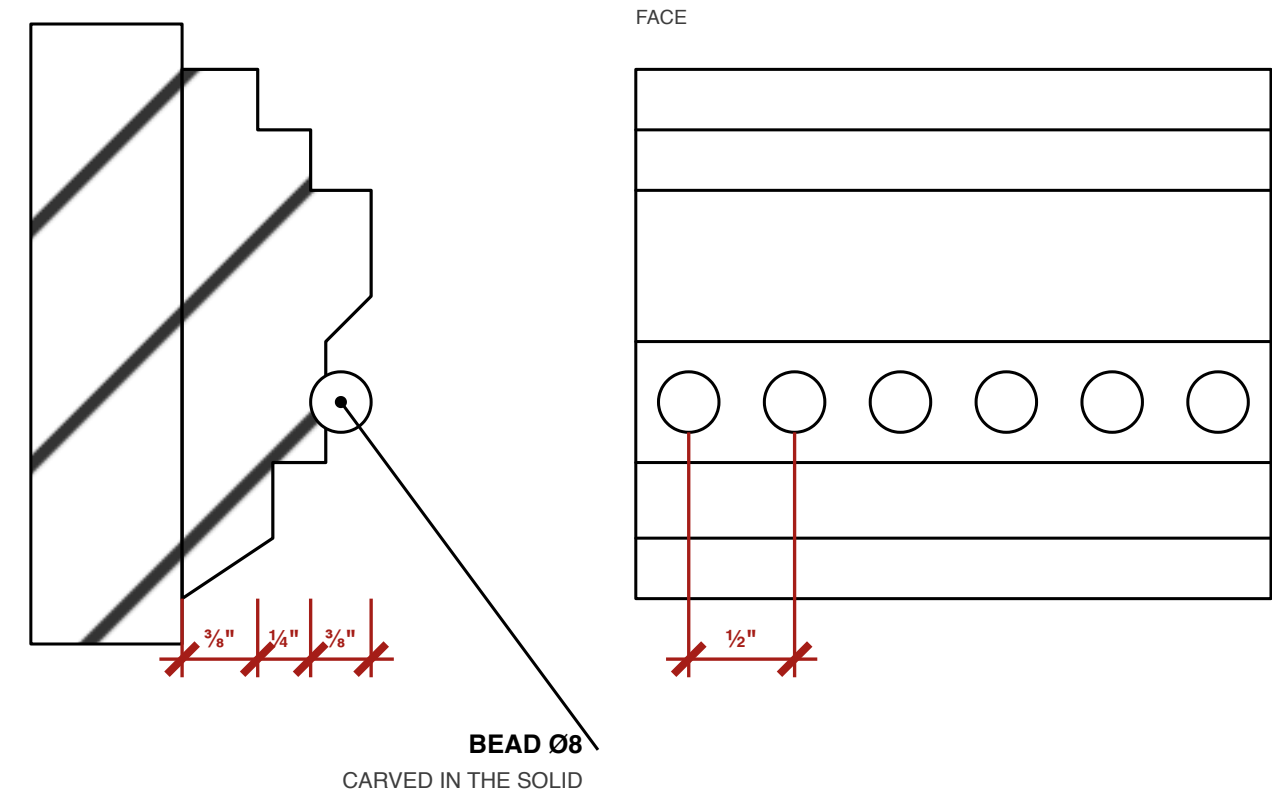

PROJECT
A Study in Teak — Study Wall — Details

SHEET
5 · the painting frame
Niches · crown · frame · skirting

SCALE
1:1 @ A4


DATE
09.10.2026

REV
2

DRAWING
AST-DR-043 · 13 of 16


7 · SPANDREL MOULDING

SCALE 1:1 (FULL SIZE) @ A4 · SECTION

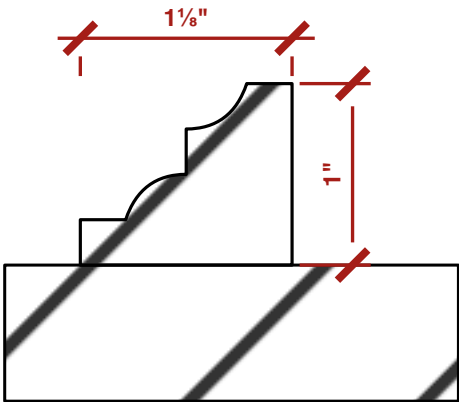

SPANDREL PANEL, VENEERED

STEPS AT 1/2" AND 1 1/8", ROUND THE CURVE TOO

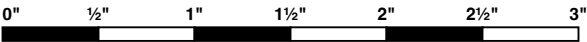

PROJECT
A Study in Teak — Study Wall — Details

SHEET
7 · spandrel moulding
Niches · crown · frame · skirting

SCALE
1:1 @ A4


DATE
09.10.2026

REV
2



DRAWING
AST-DR-043 · 14 of 16

6 · SKIRTING + COUNTER

SCALE 1:2 (6" = 1'-0") @ A4 · SECTION

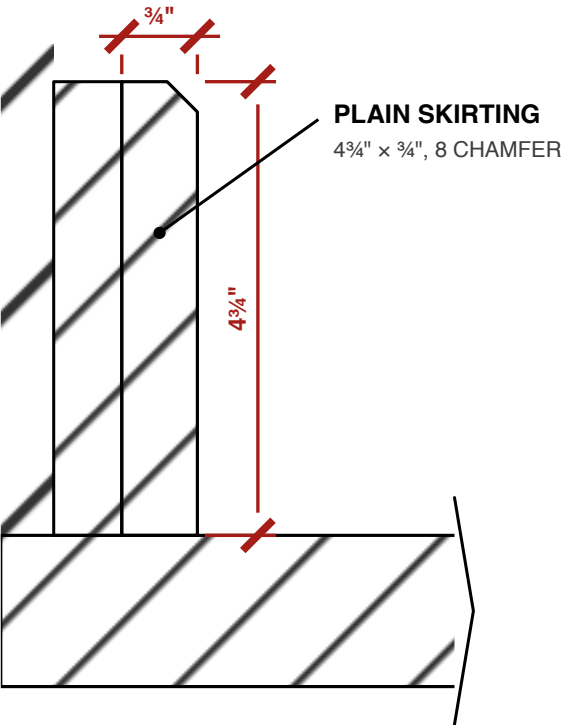

COUNTER 1⅝", 4 REEDS x 8
AS THE DESK

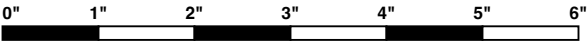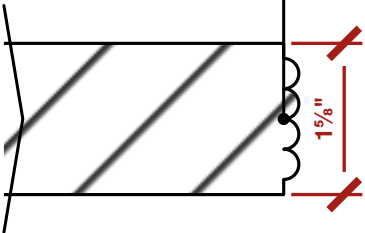

PROJECT A Study in Teak — Study Wall — Details	SHEET 6 · skirting + counter Niches · crown · frame · skirting	SCALE 1:2 @ A4	DATE 09.10.2026	REV 2	DRAWING AST-DR-043 · 15 of 16
---	--	-------------------	--------------------	----------	----------------------------------

NOTES

REVISION 4

Details for AST-DR-040/042 (and 041/044 except the arches). Mouldings from the owner's photos; profiles to be mocked up full size before cutting. Each niche has one small focus light, 9'-10¹/₈" K, in the middle of its top (owner, 8 Oct). All timber in the room's teak veneer; no colour in this set.

PROJECT A Study in Teak — Study Wall — Details	SHEET Notes Niches · crown · frame · skirting	SCALE NTS	DATE 09.10.2026	REV 2	DRAWING AST-DR-043 · 16 of 16
---	---	--------------	--------------------	----------	----------------------------------