





PLAN · COPIED FROM THE OWNER'S SKETCH — NOT YET A SITE MEASUREMENT

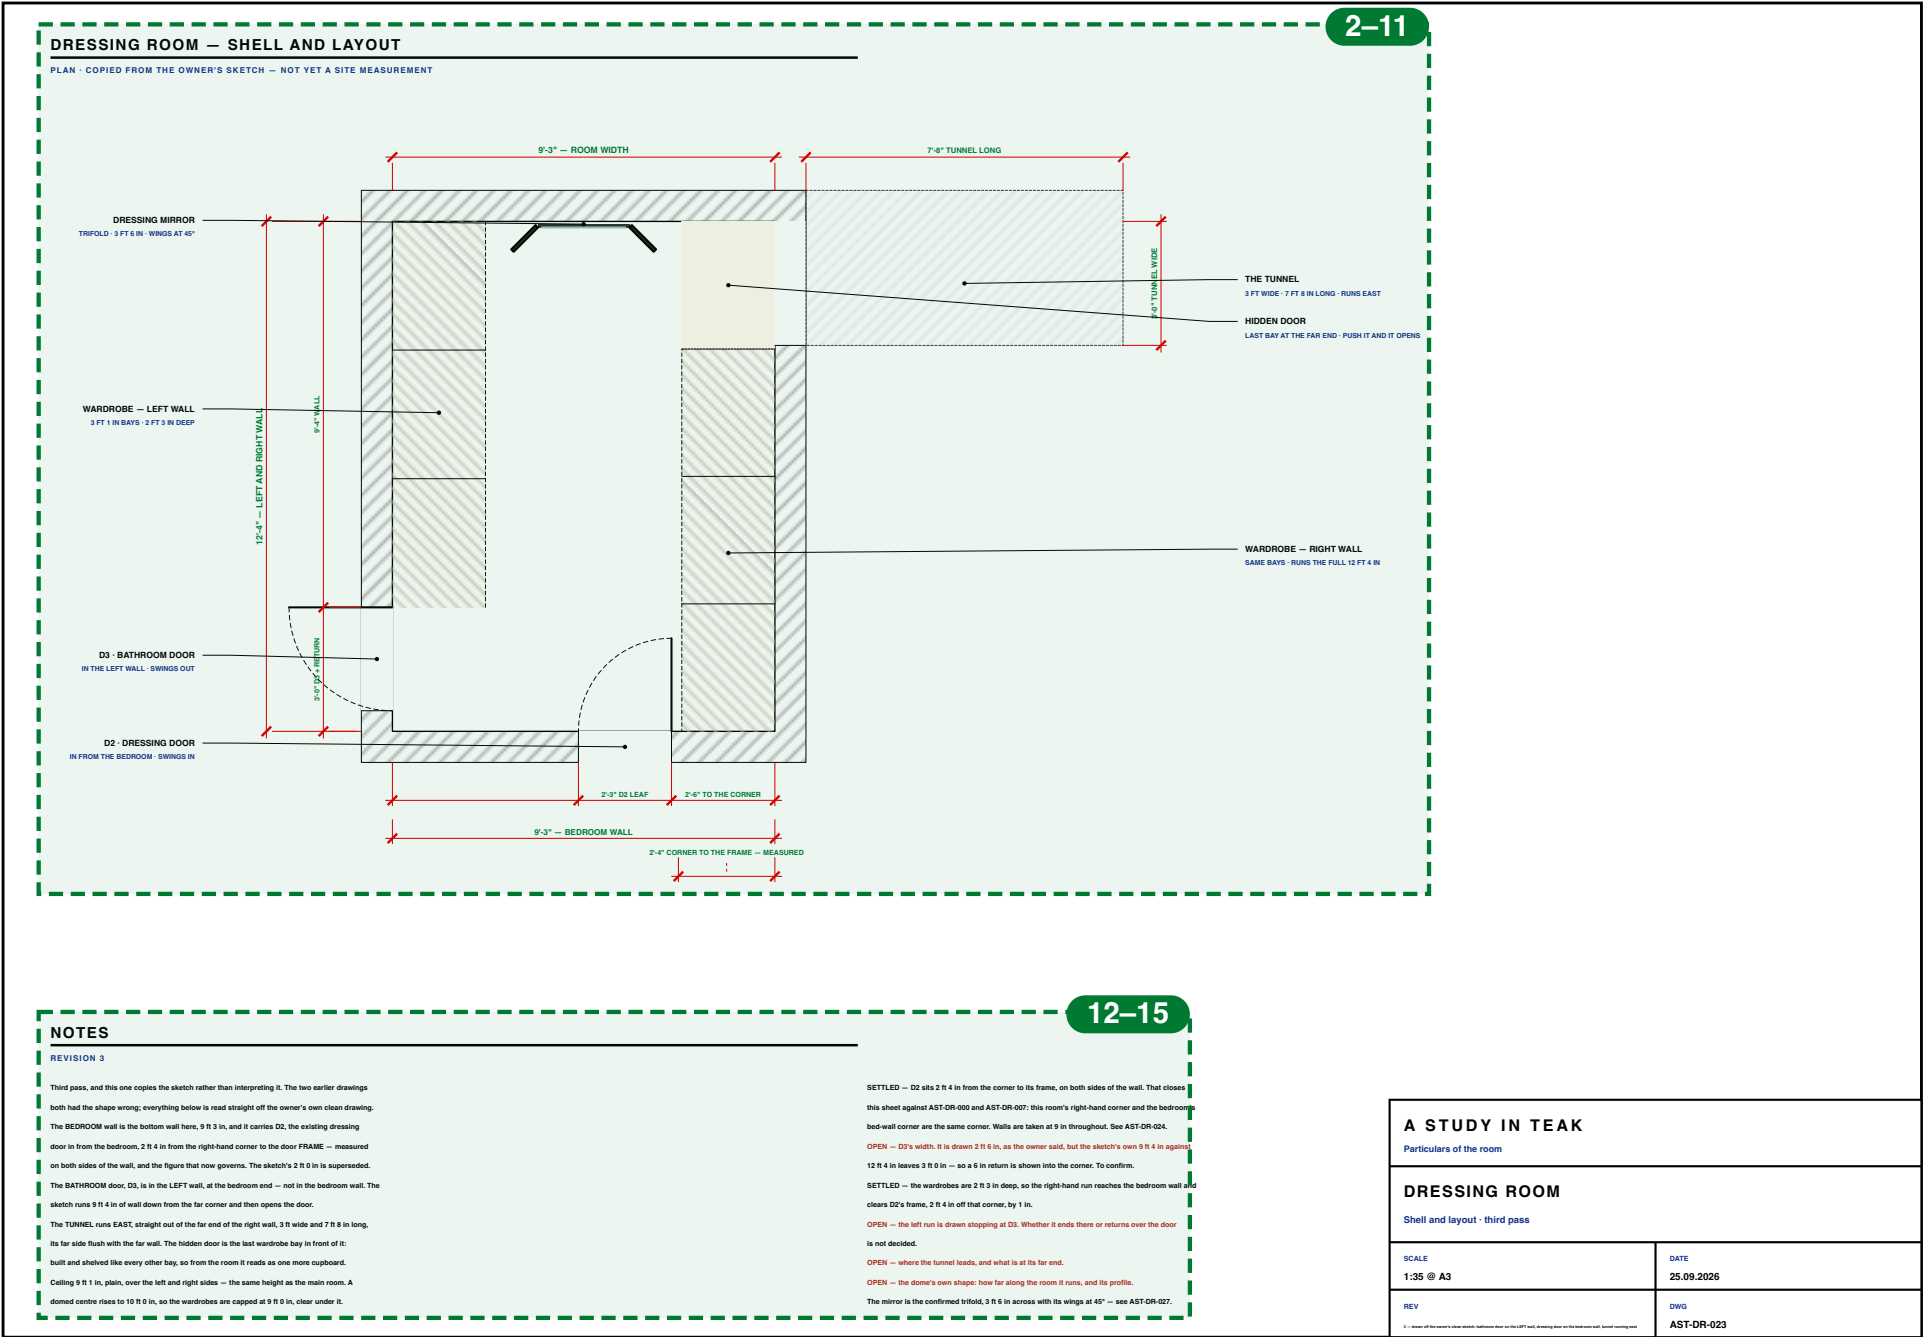



DRESSING ROOM — SHELL AND LAYOUT

PLAN · COPIED FROM THE OWNER'S SKETCH — NOT YET A SITE MEASUREMENT

DRESSING MIRROR
TRIFOLD · 3 FT 6 IN · WINGS AT 45°

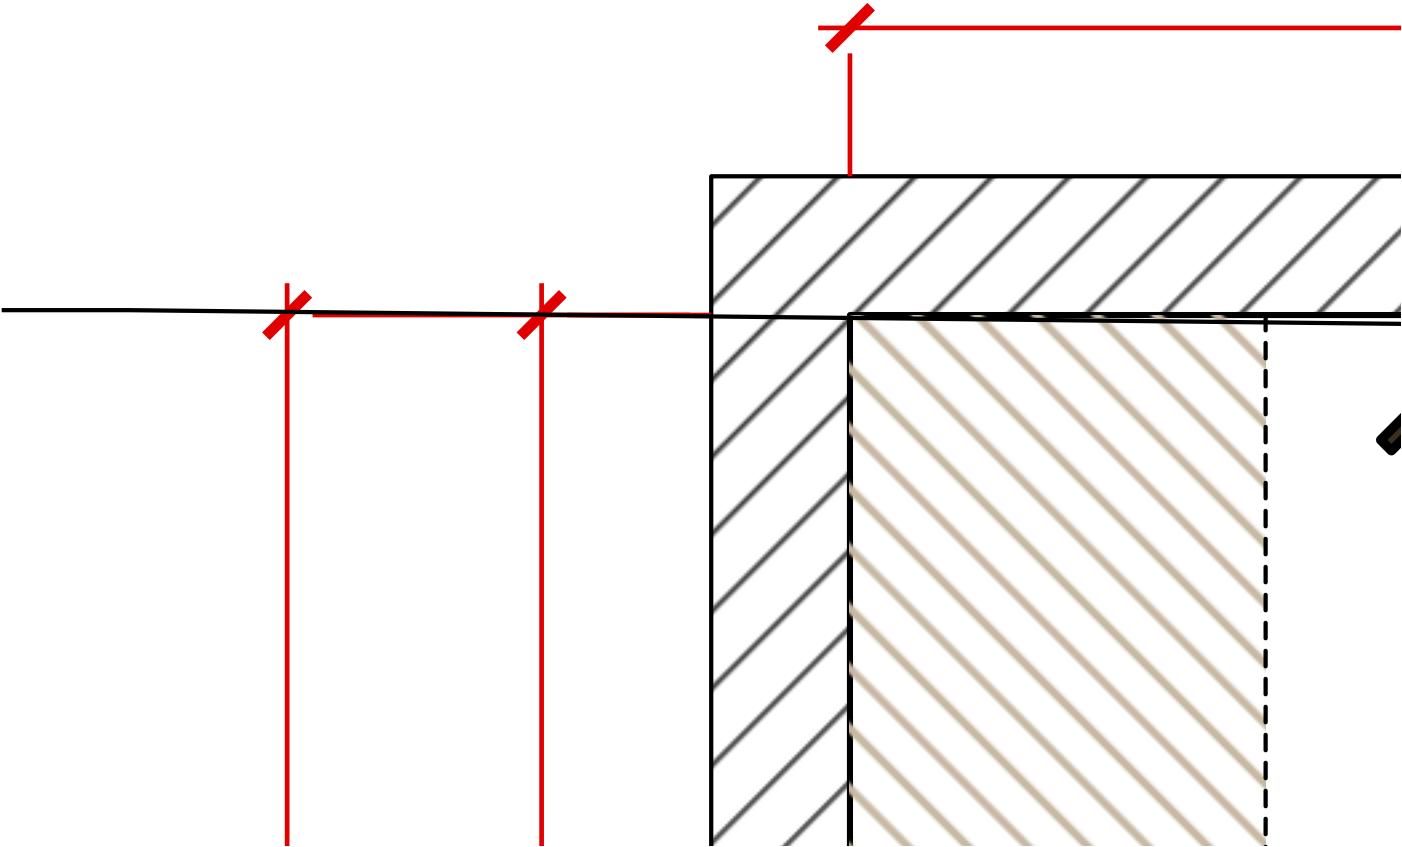

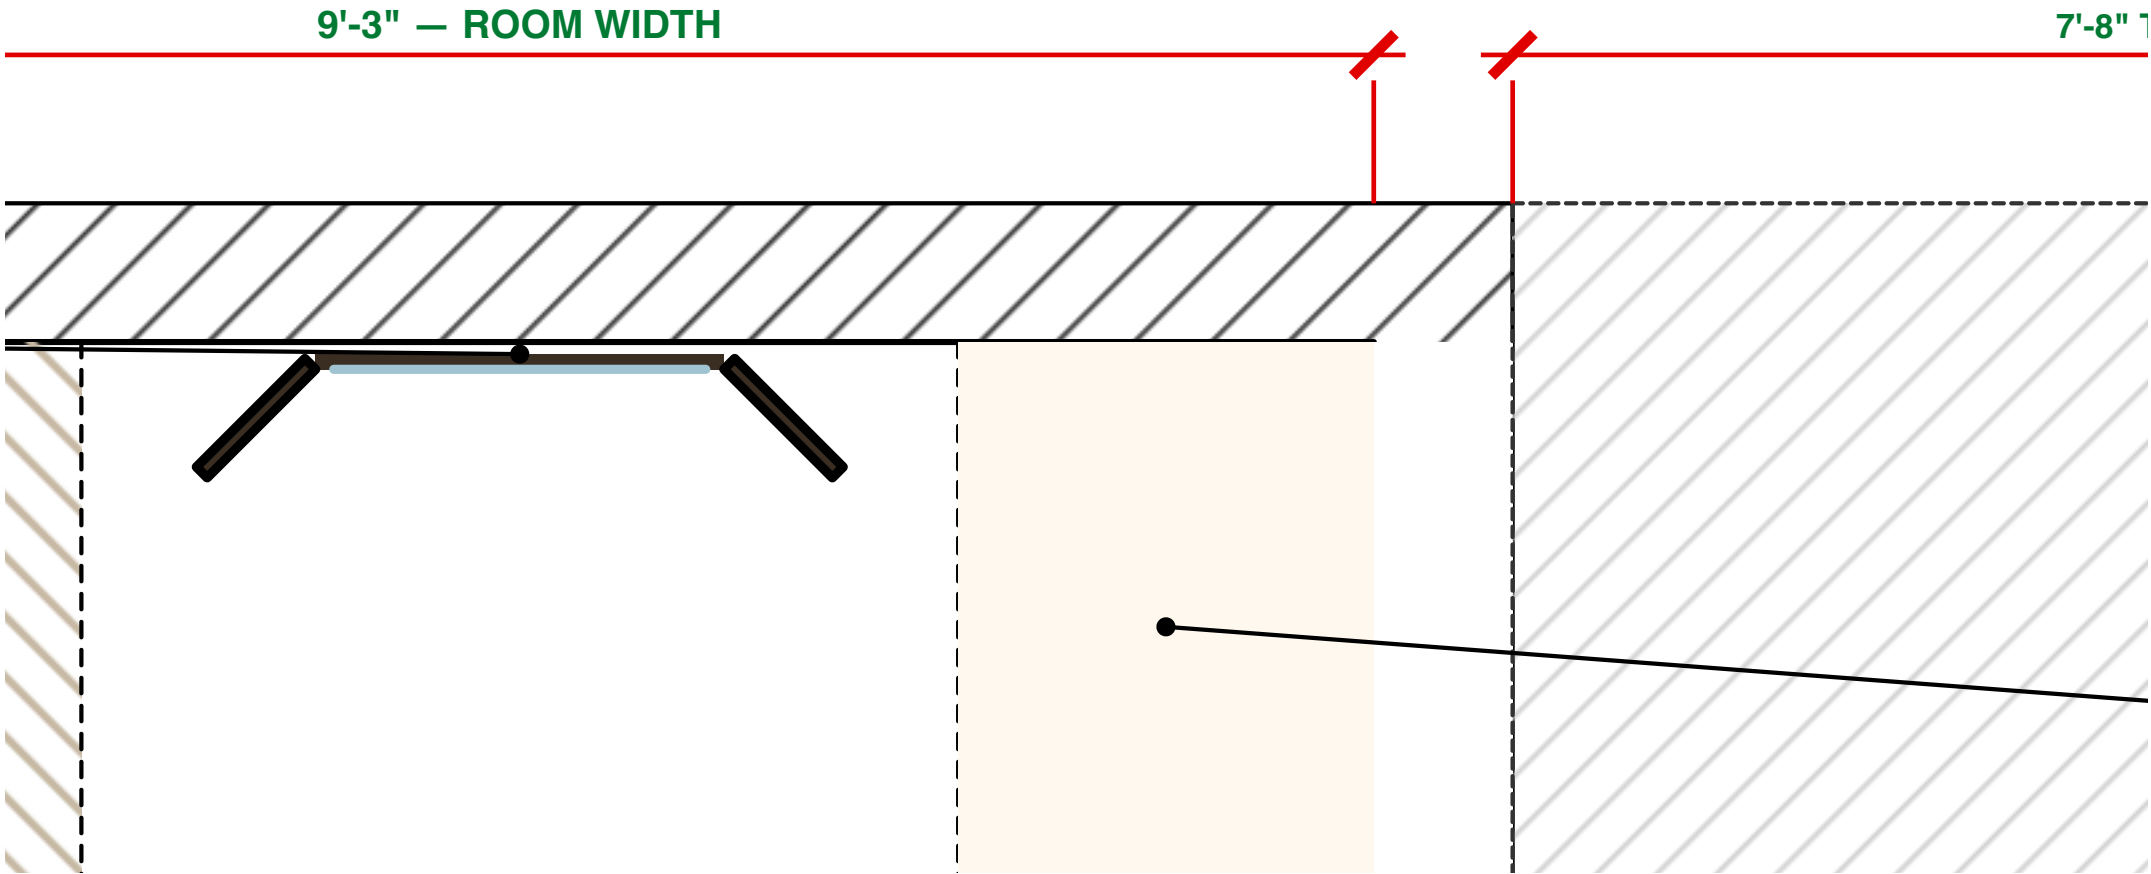

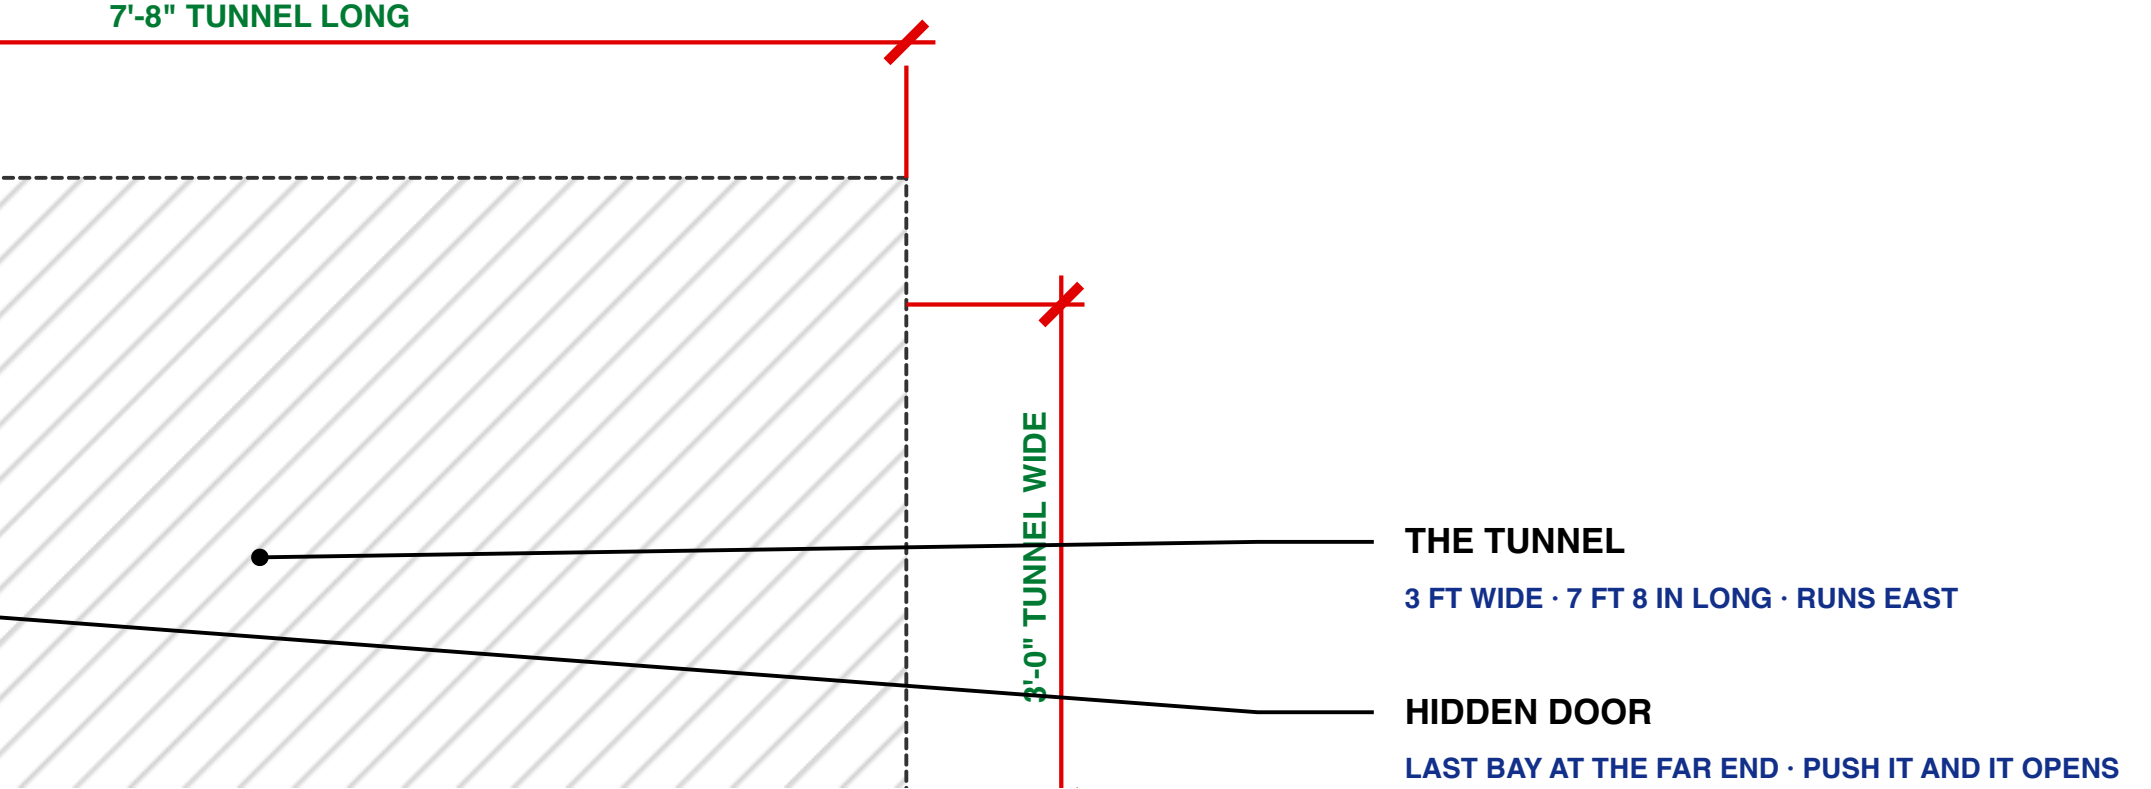



All sizes in feet and inches. Enlarged — go by the written sizes, never measure the paper.


WARDROBE — LEFT WALL
3 FT 1 IN BAYS · 2 FT 3 IN DEEP

12'-4" — LEFT AND RIGHT WALL

9'-4" WALL

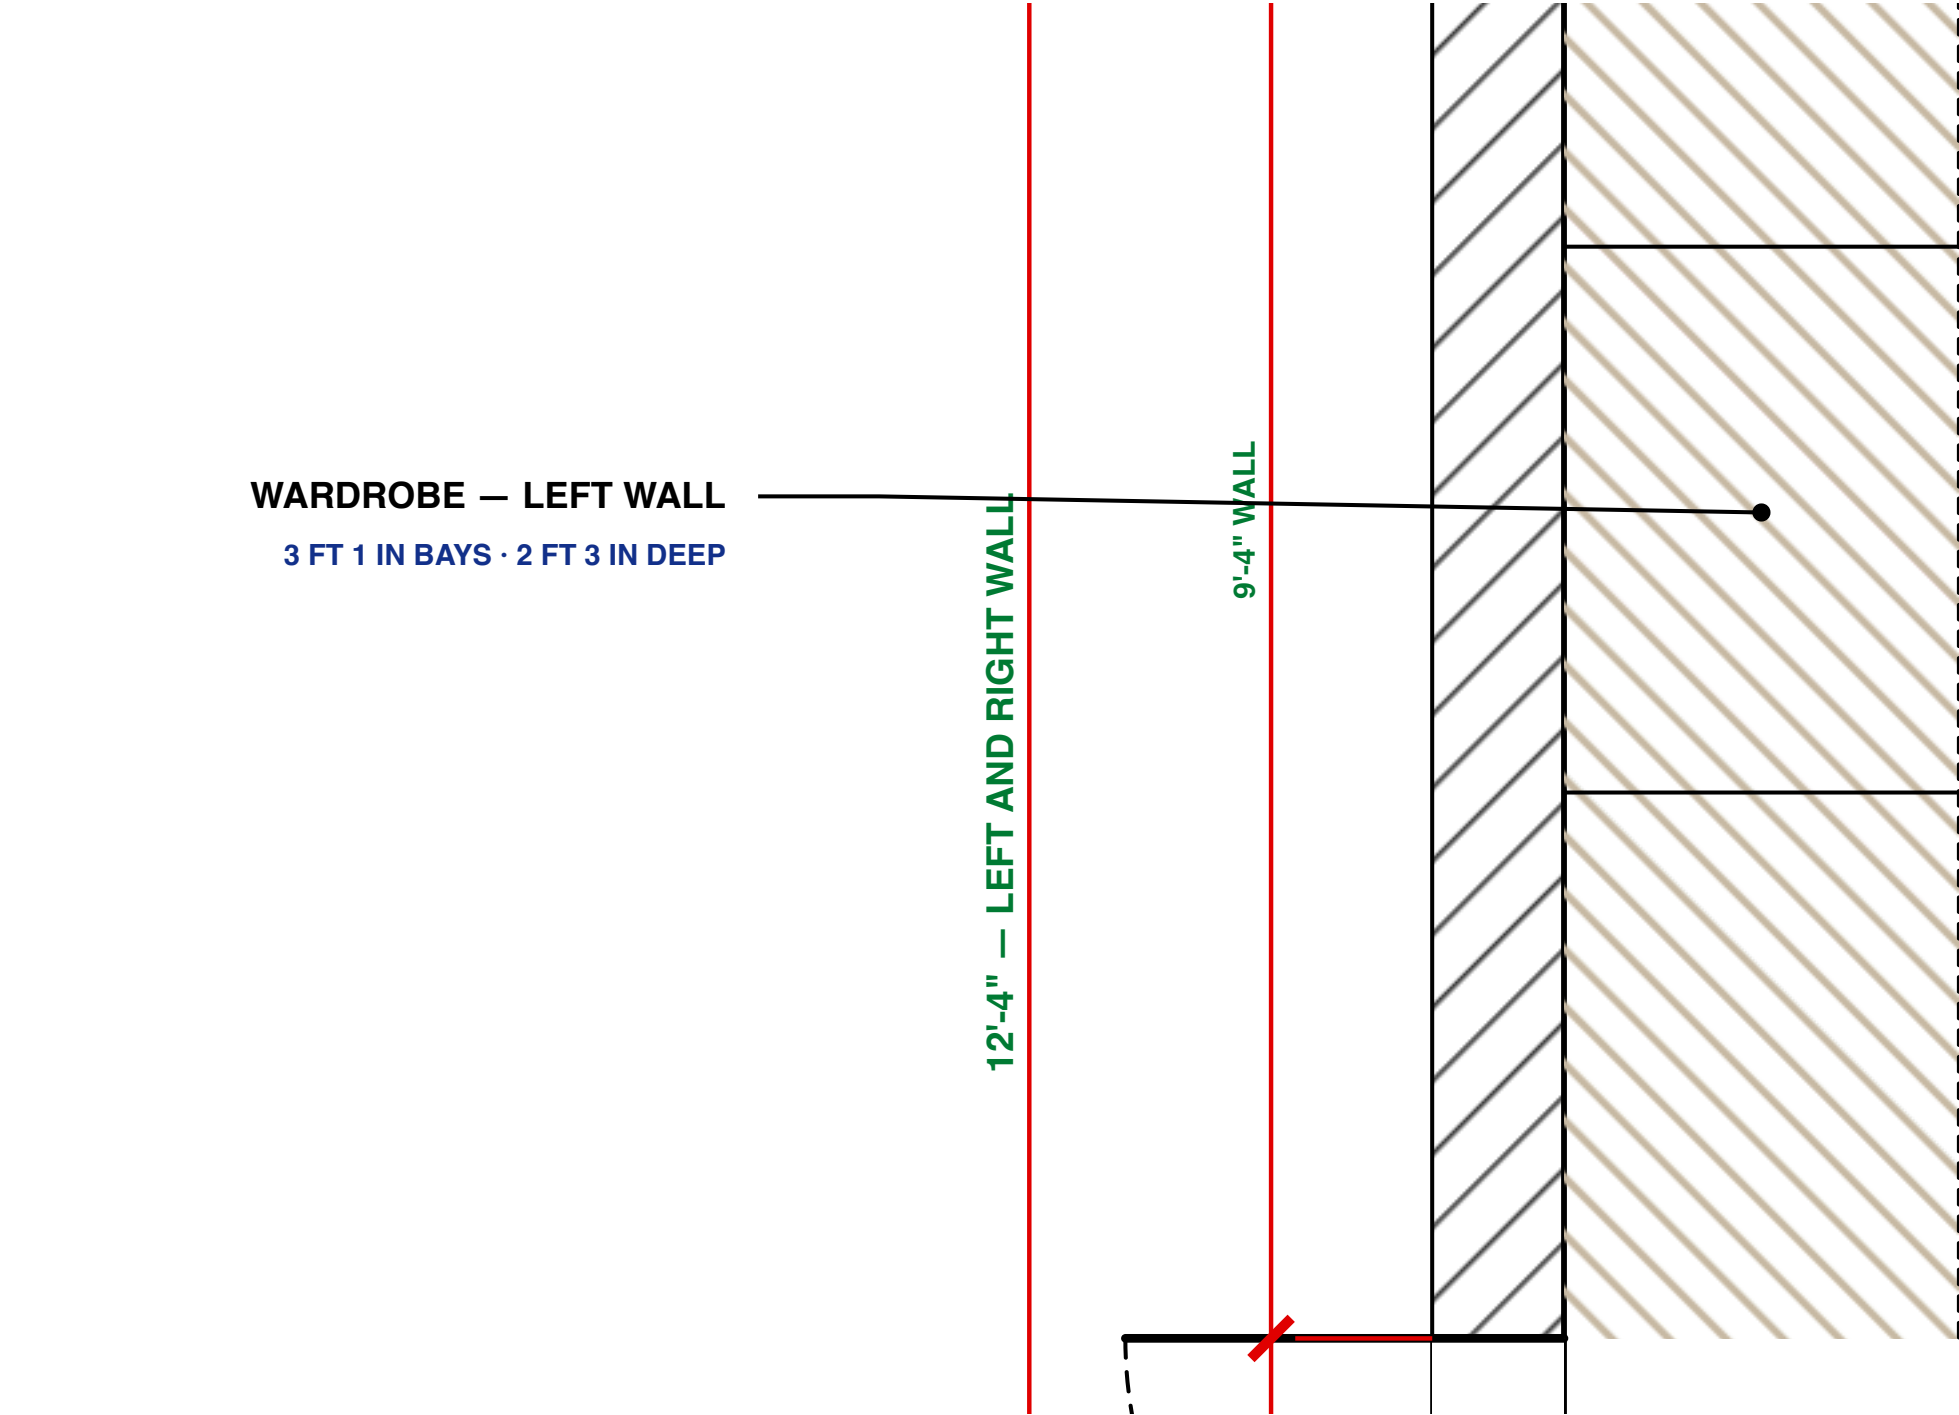


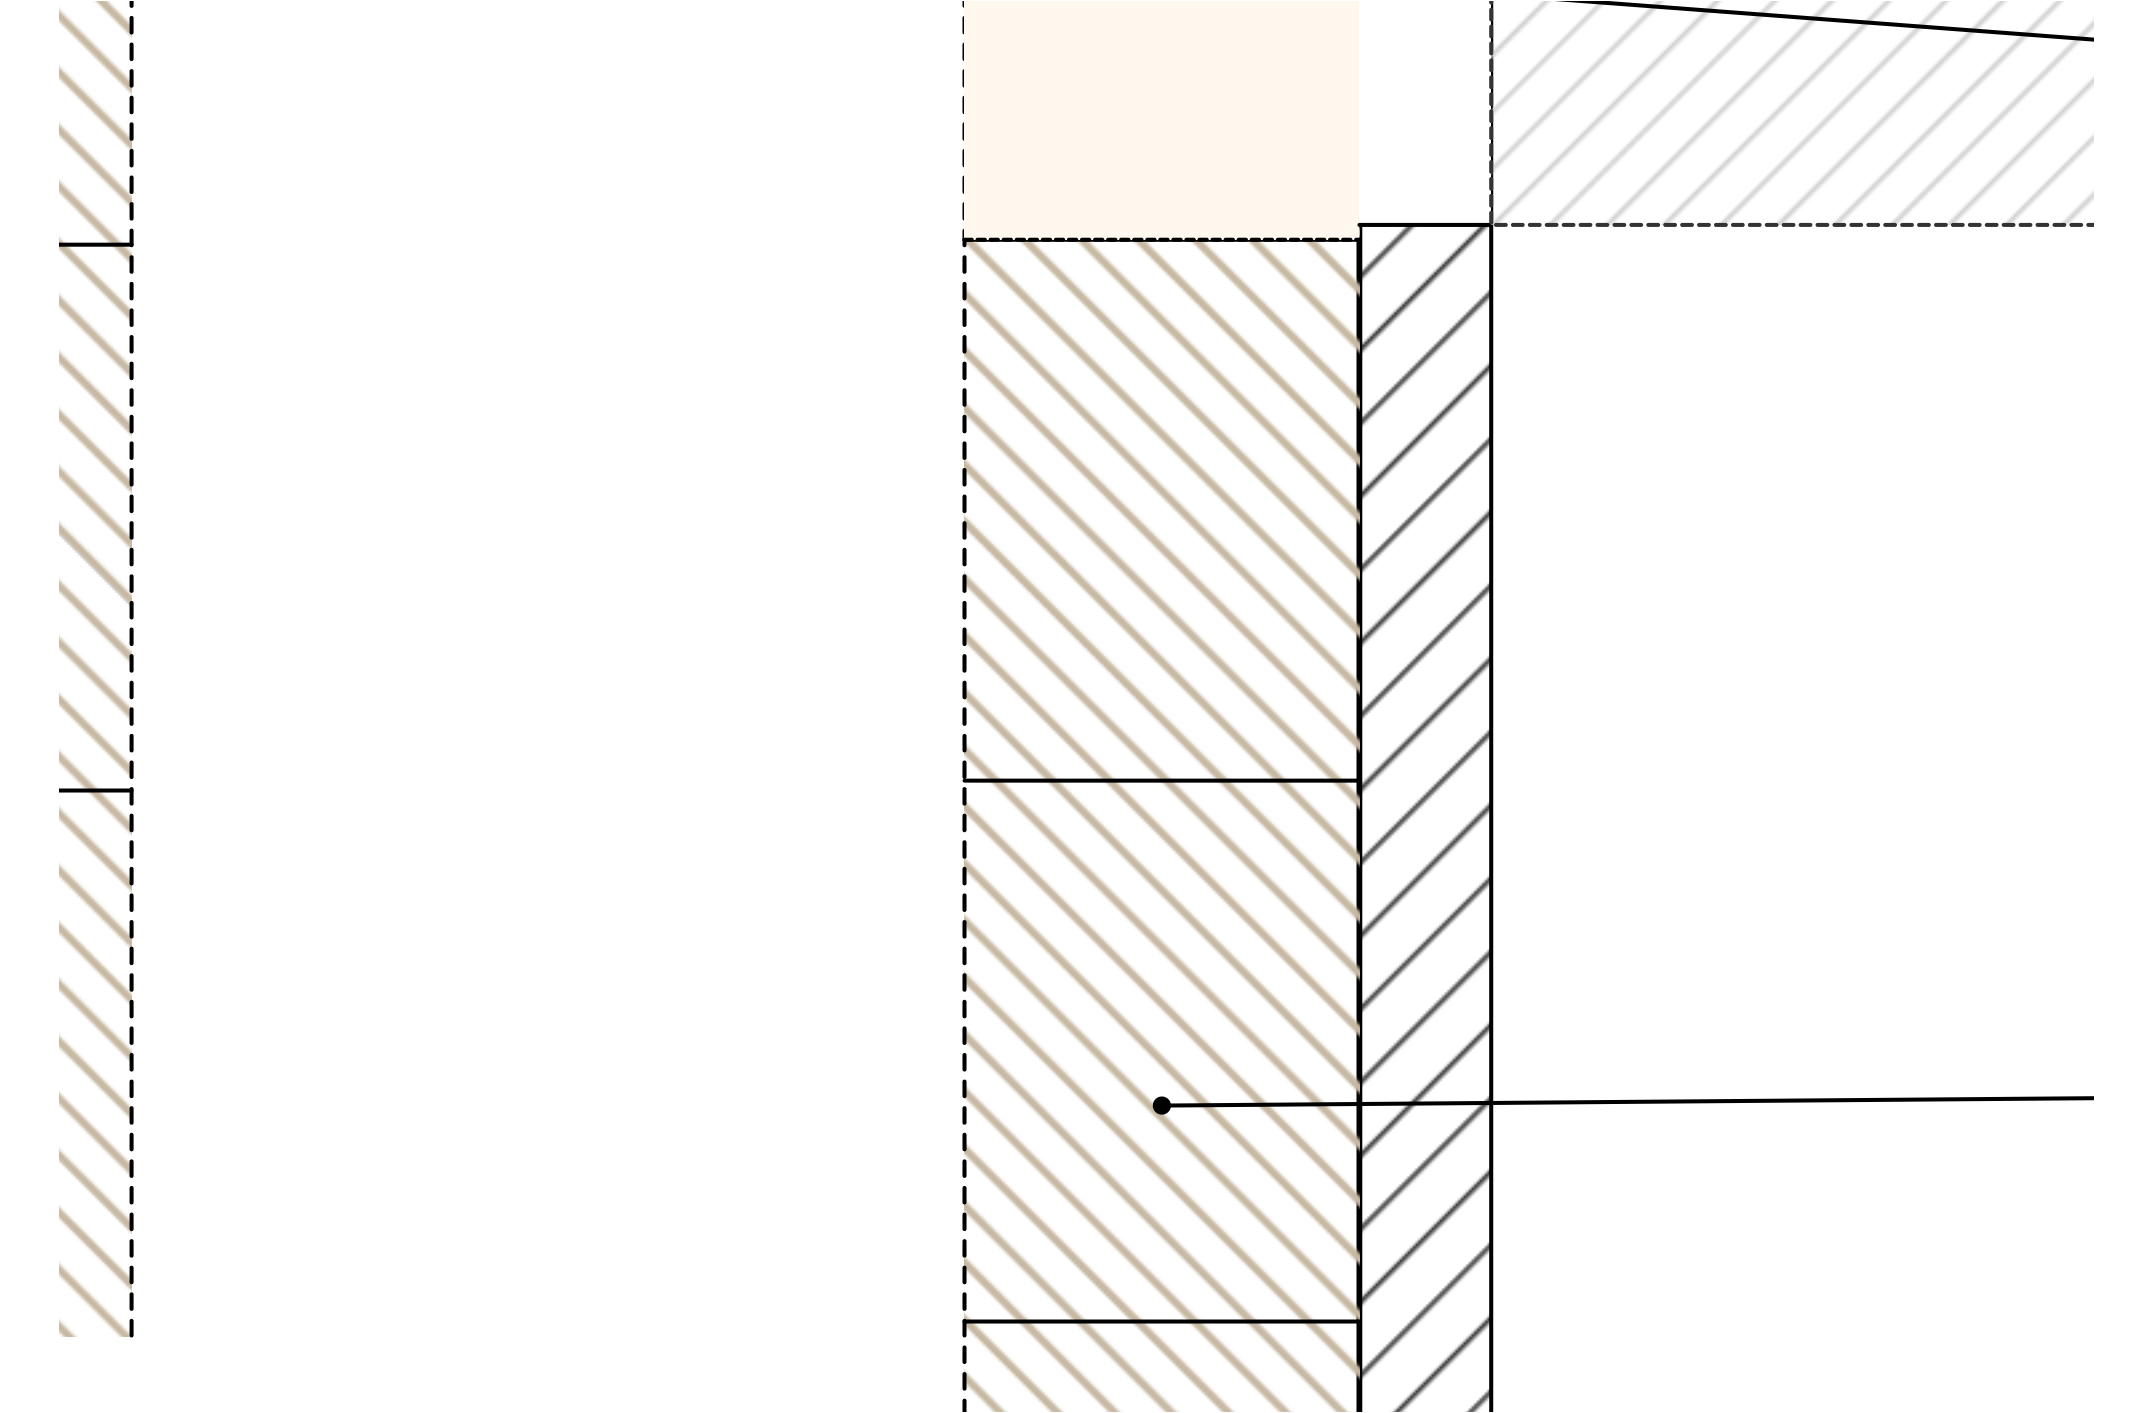


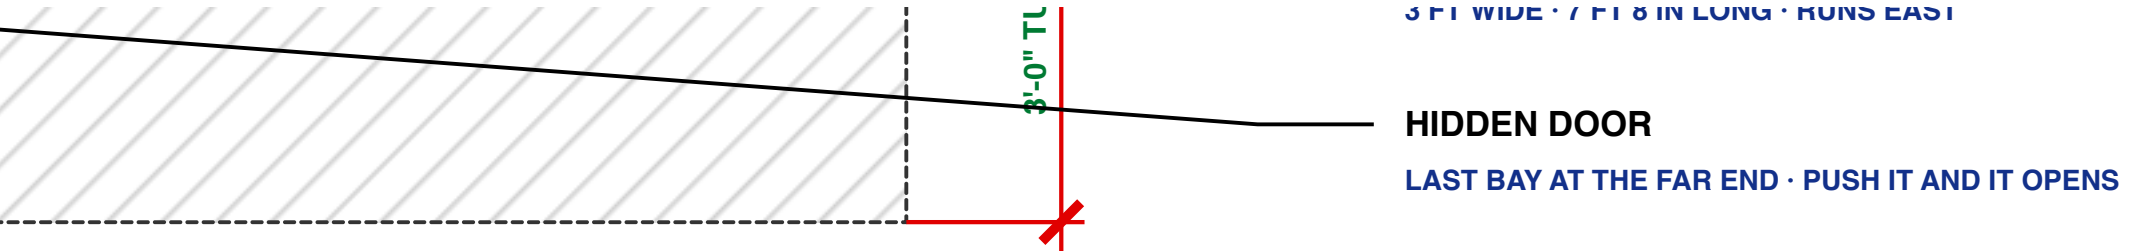

D3 · BATHROOM DOOR
IN THE LEFT WALL · SWINGS OUT

D2 · DRESSING DOOR
IN FROM THE BEDROOM · SWINGS IN

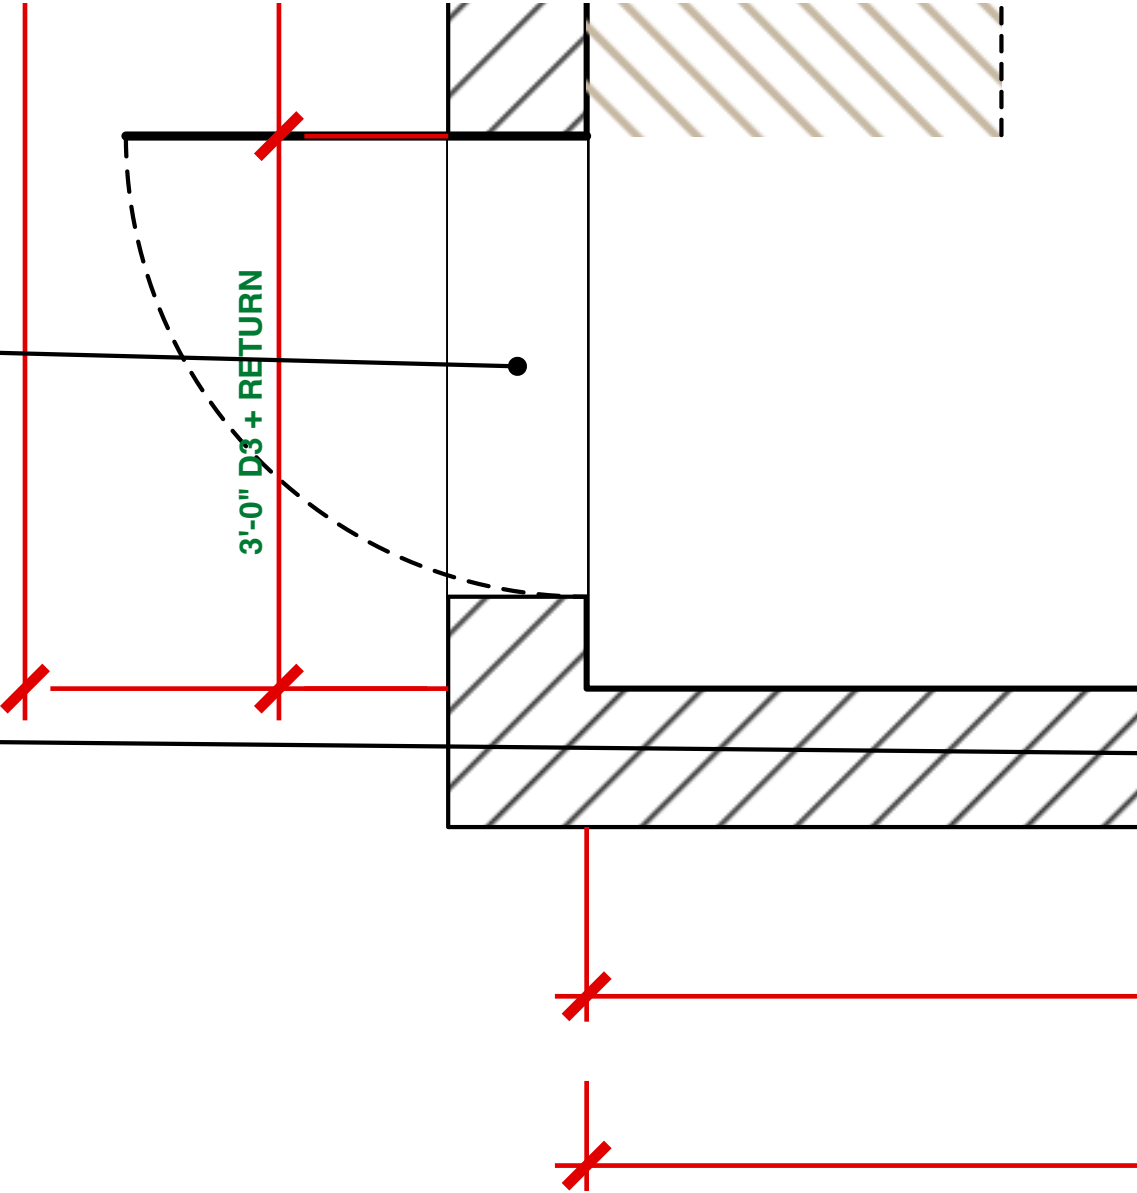

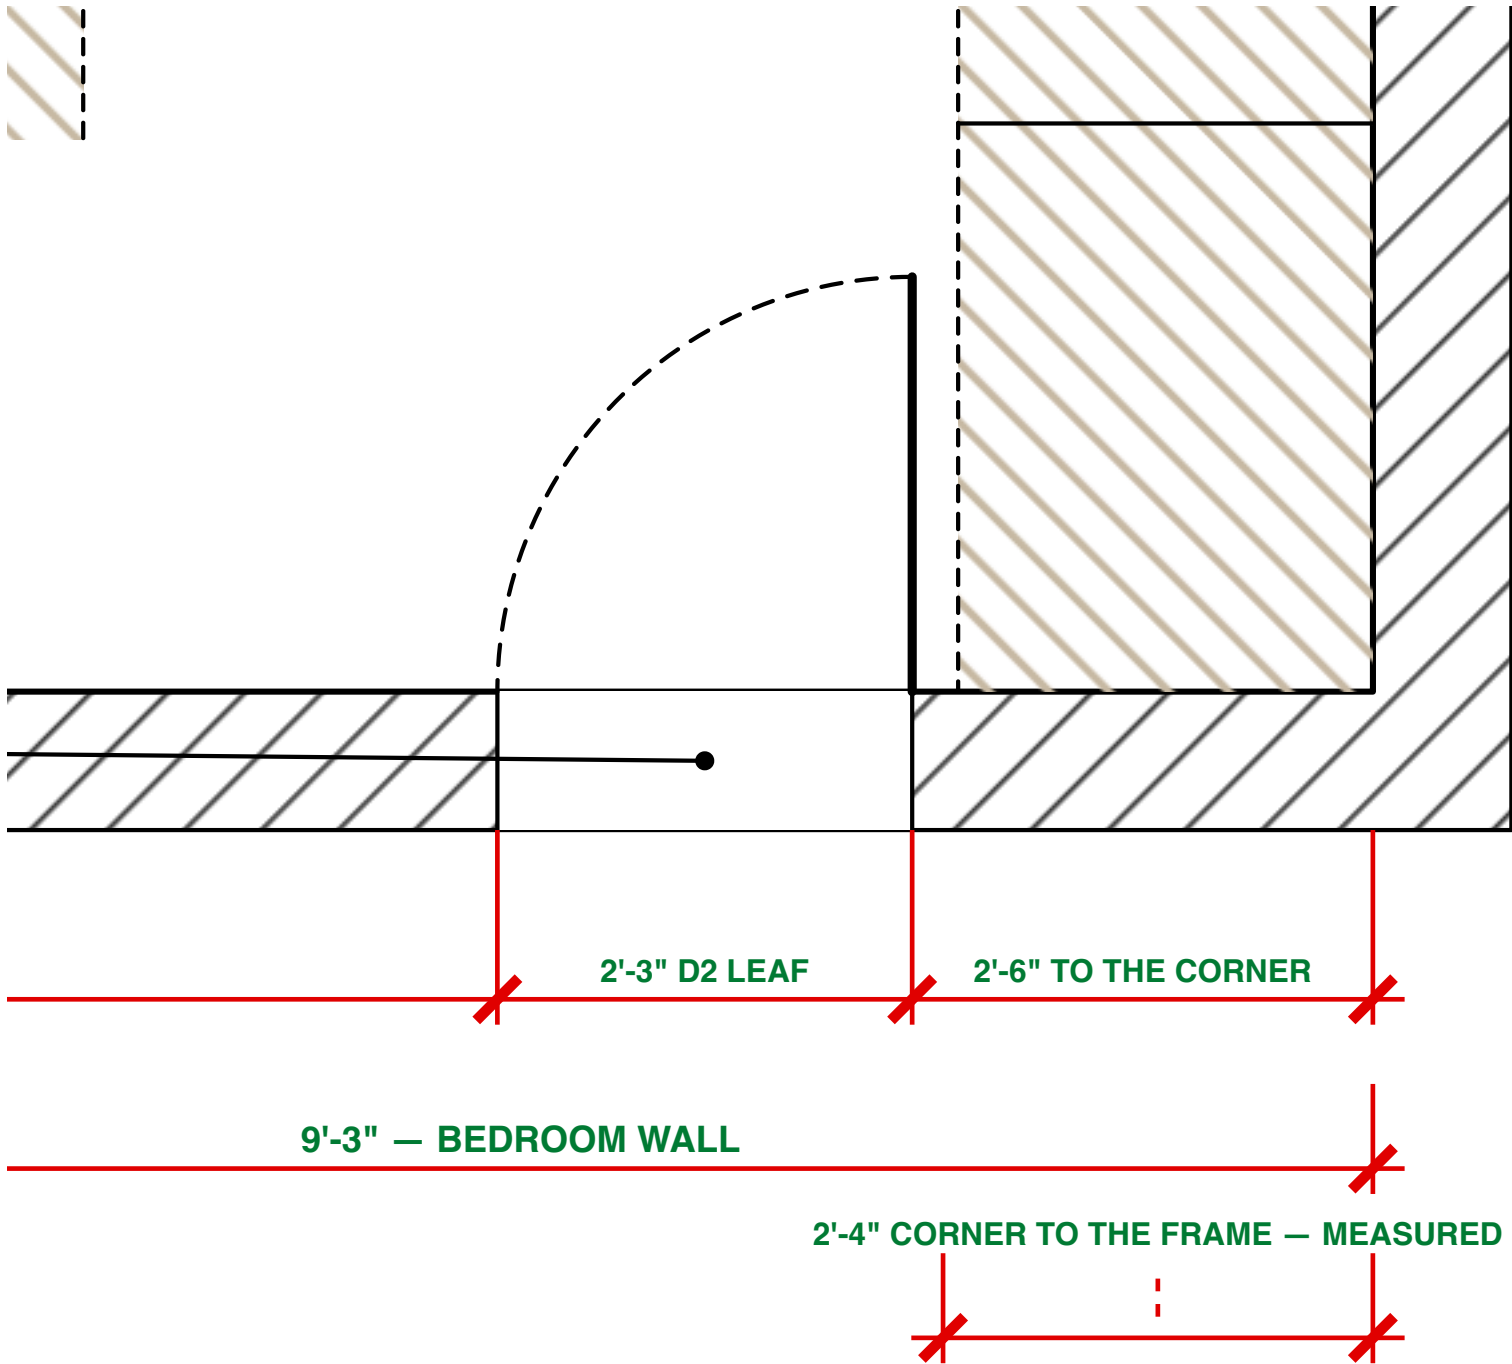



NOTES

REVISION 3

Third pass, and this one copies the sketch rather than interpreting it. The two earlier drawings both had the shape wrong; everything below is read straight off the owner's own clean drawing.	
The BEDROOM wall is the bottom wall here, 9 ft 3 in, and it carries D2, the existing dressing door in from the bedroom, 2 ft 4 in from the right-hand corner to the door FRAME — measured on both sides of the wall, and the figure that now governs. The sketch's 2 ft 0 in is superseded.	
The BATHROOM door, D3, is in the LEFT wall, at the bedroom end — not in the bedroom wall. The sketch runs 9 ft 4 in of wall down from the far corner and then opens the door.	SETTLED — D2 sits 2 ft 4 in from the corner to its frame, on both sides of the wall. That closes this sheet against AST-DR-000 and AST-DR-007: this room's right-hand corner and the bedroom bed-wall corner are the same corner. Walls are taken at 9 in throughout. See AST-DR-024.
The TUNNEL runs EAST, straight out of the far end of the right wall, 3 ft wide and 7 ft 8 in long, its far side flush with the far wall. The hidden door is the last wardrobe bay in front of it: built and shelved like every other bay, so from the room it reads as one more cupboard.	OPEN — D3's width. It is drawn 2 ft 6 in, as the owner said, but the sketch's own 9 ft 4 in against 12 ft 4 in leaves 3 ft 0 in — so a 6 in return is shown into the corner. To confirm.
Ceiling 9 ft 1 in, plain, over the left and right sides — the same height as the main room. A domed centre rises to 10 ft 0 in, so the wardrobes are capped at 9 ft 0 in, clear under it.	SETTLED — the wardrobes are 2 ft 3 in deep, so the right-hand run reaches the bedroom wall and clears D2's frame, 2 ft 4 in off that corner, by 1 in.
	OPEN — the left run is drawn stopping at D3. Whether it ends there or returns over the door is not decided.
	OPEN — where the tunnel leads, and what is at its far end.
	OPEN — the dome's own shape: how far along the room it runs, and its profile.
	The mirror is the confirmed trifold, 3 ft 6 in across with its wings at 45° — see AST-DR-027.

NOTES

REVISION 3

Third pass, and this one copies the sketch rather than interpreting it. The two earlier drawings both had the shape wrong; everything below is read straight off the owner's own clean drawing.

The BEDROOM wall is the bottom wall here, 9 ft 3 in, and it carries D2, the existing dressing door in from the bedroom, 2 ft 4 in from the right-hand corner to the door FRAME — measured on both sides of the wall, and the figure that now governs. The sketch's 2 ft 0 in is superseded.

The BATHROOM door, D3, is in the LEFT wall, at the bedroom end — not in the bedroom wall. The sketch runs 9 ft 4 in of wall down from the far corner and then opens the door.

The TUNNEL runs EAST, straight out of the far end of the right wall, 3 ft wide and 7 ft 8 in long, its far side flush with the far wall. The hidden door is the last wardrobe bay in front of it: built and shelved like every other bay, so from the room it reads as one more cupboard.

Ceiling 9 ft 1 in, plain, over the left and right sides — the same height as the main room. A domed centre rises to 10 ft 0 in, so the wardrobes are capped at 9 ft 0 in, clear under it.



SET

this

bed-

OPE

12 ft

SET

clea

OPE

is n

OPE

OPE

The



SETTLED — D2 sits 2 ft 4 in from the corner to its frame, on both sides of the wall. That closes this sheet against AST-DR-000 and AST-DR-007: this room's right-hand corner and the bedroom bed-wall corner are the same corner. Walls are taken at 9 in throughout. See AST-DR-024.

OPEN — D3's width. It is drawn 2 ft 6 in, as the owner said, but the sketch's own 9 ft 4 in against 12 ft 4 in leaves 3 ft 0 in — so a 6 in return is shown into the corner. To confirm.

SETTLED — the wardrobes are 2 ft 3 in deep, so the right-hand run reaches the bedroom wall and clears D2's frame, 2 ft 4 in off that corner, by 1 in.

OPEN — the left run is drawn stopping at D3. Whether it ends there or returns over the door is not decided.

OPEN — where the tunnel leads, and what is at its far end.

OPEN — the dome's own shape: how far along the room it runs, and its profile.

The mirror is the confirmed trifold, 3 ft 6 in across with its wings at 45° — see AST-DR-027.