



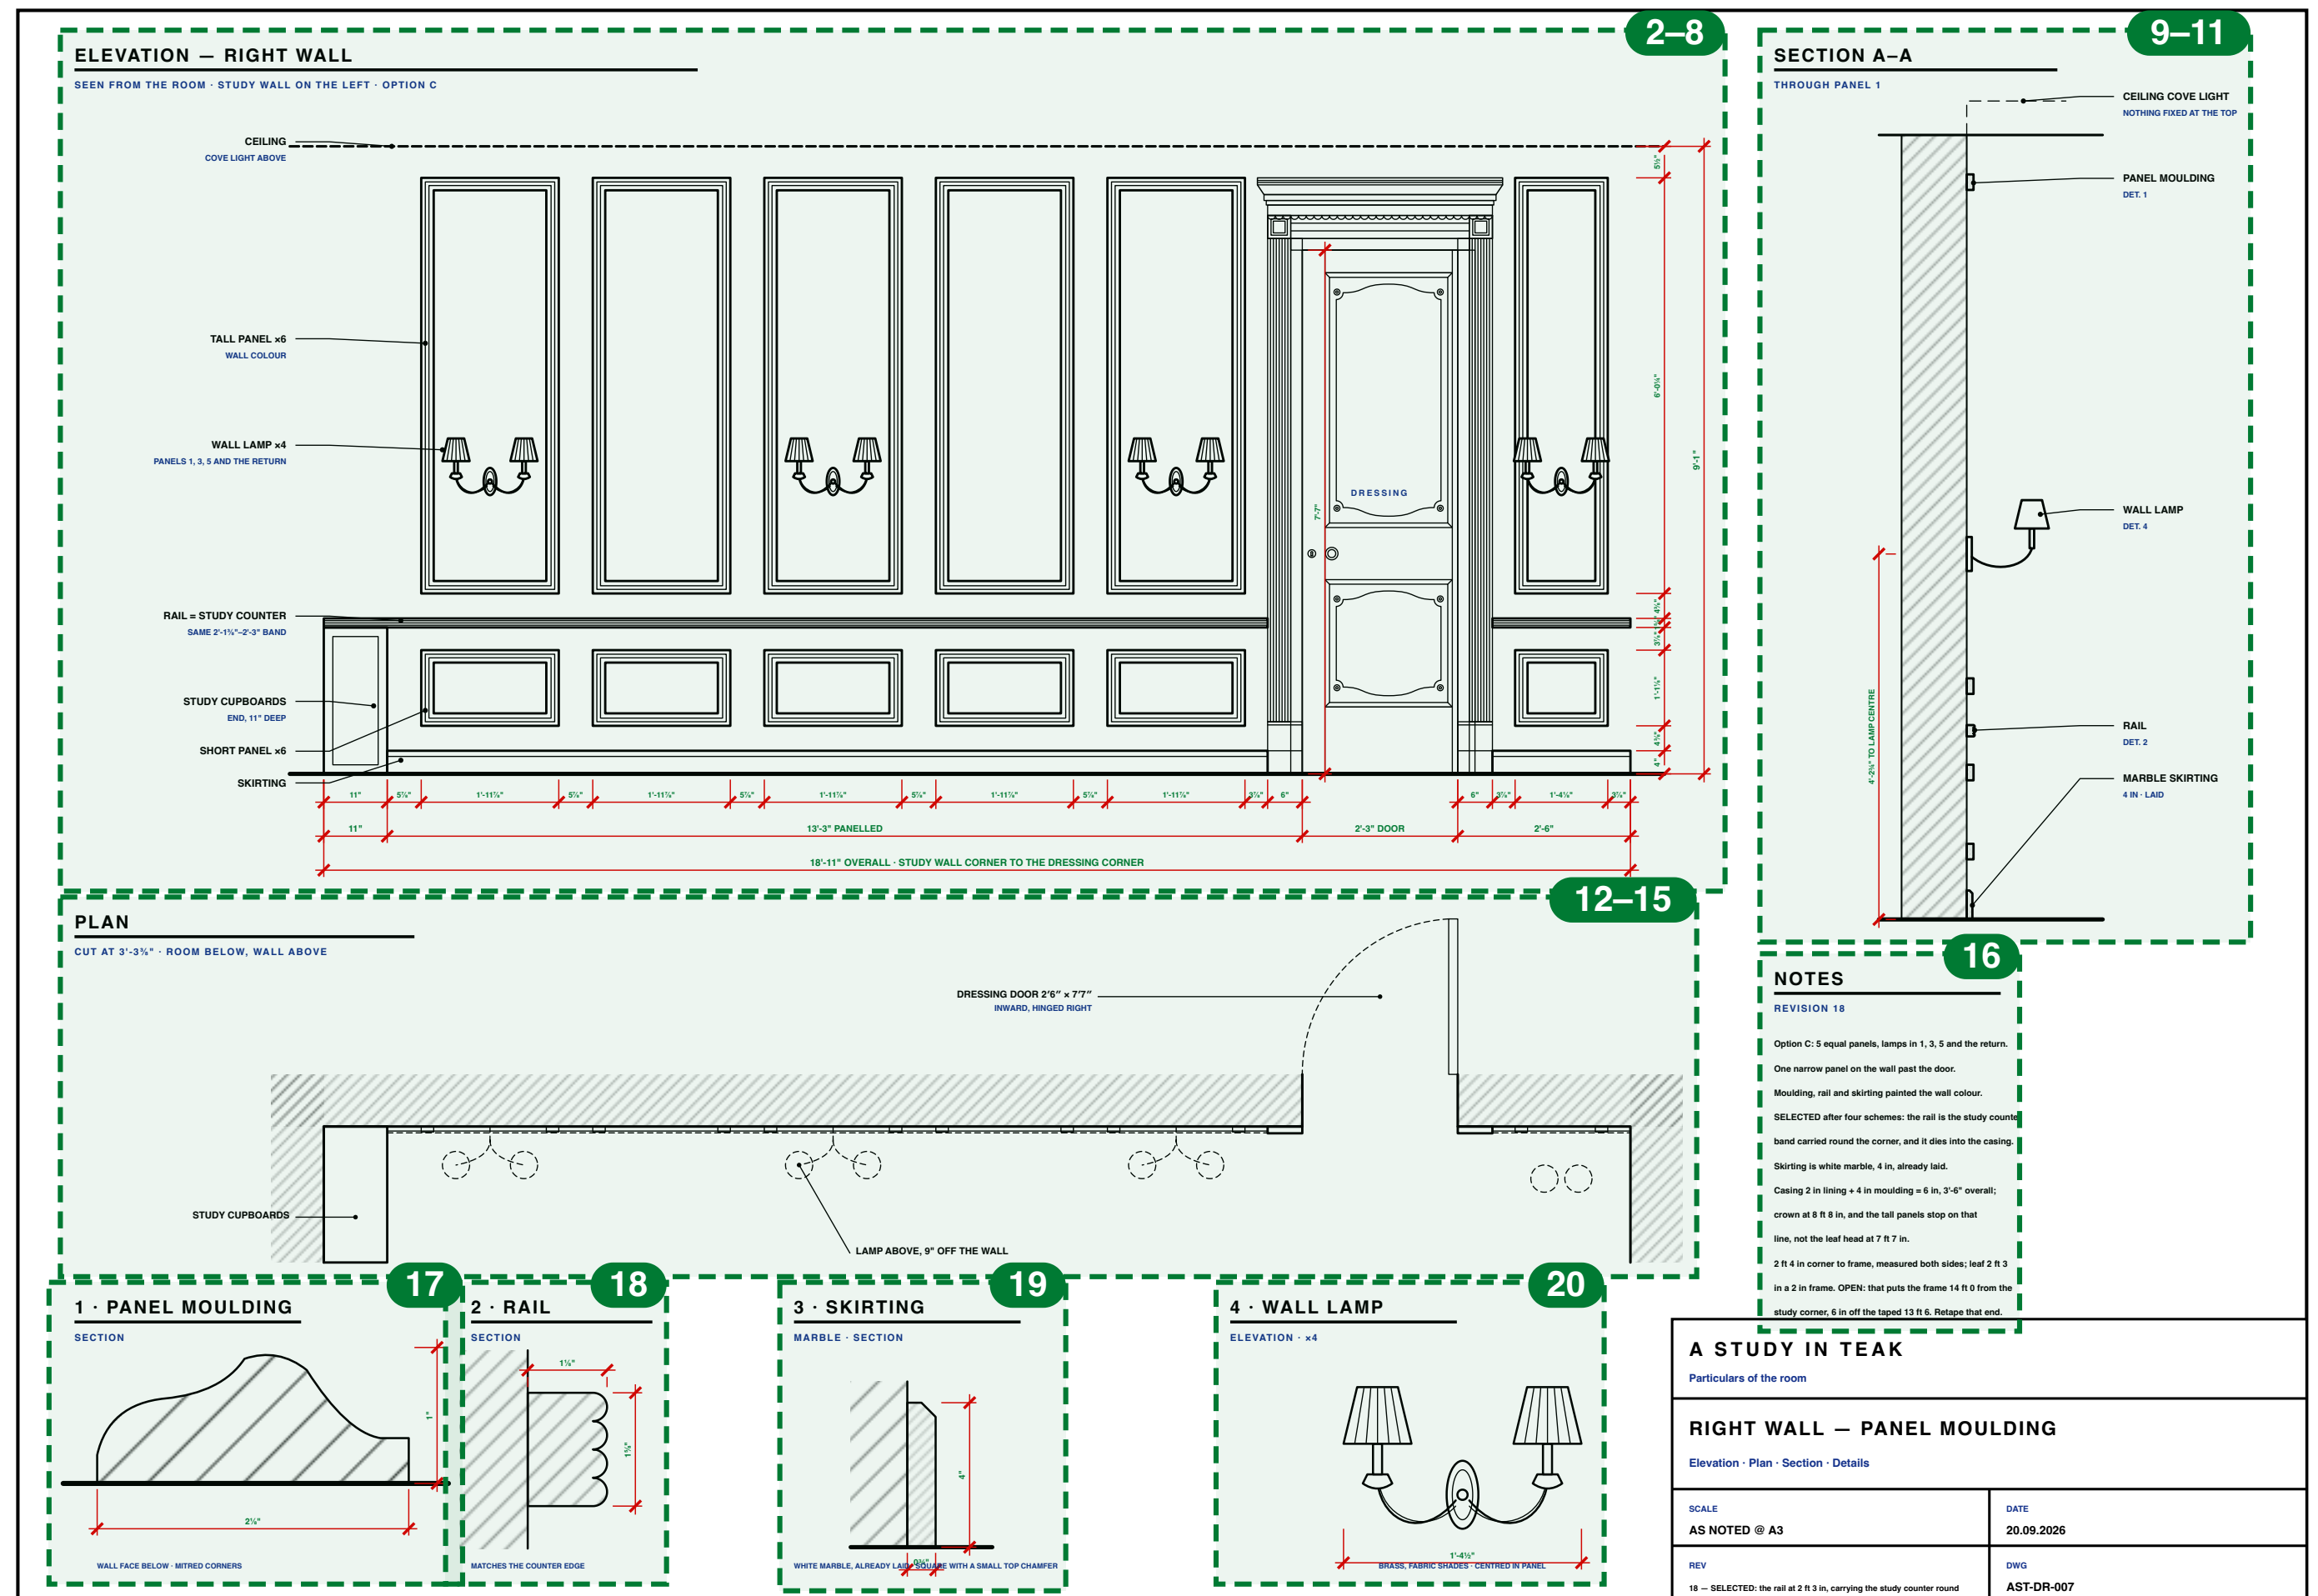


ELEVATION — RIGHT WALL


SEEN FROM THE ROOM · STUDY WALL ON THE LEFT · OPTION C

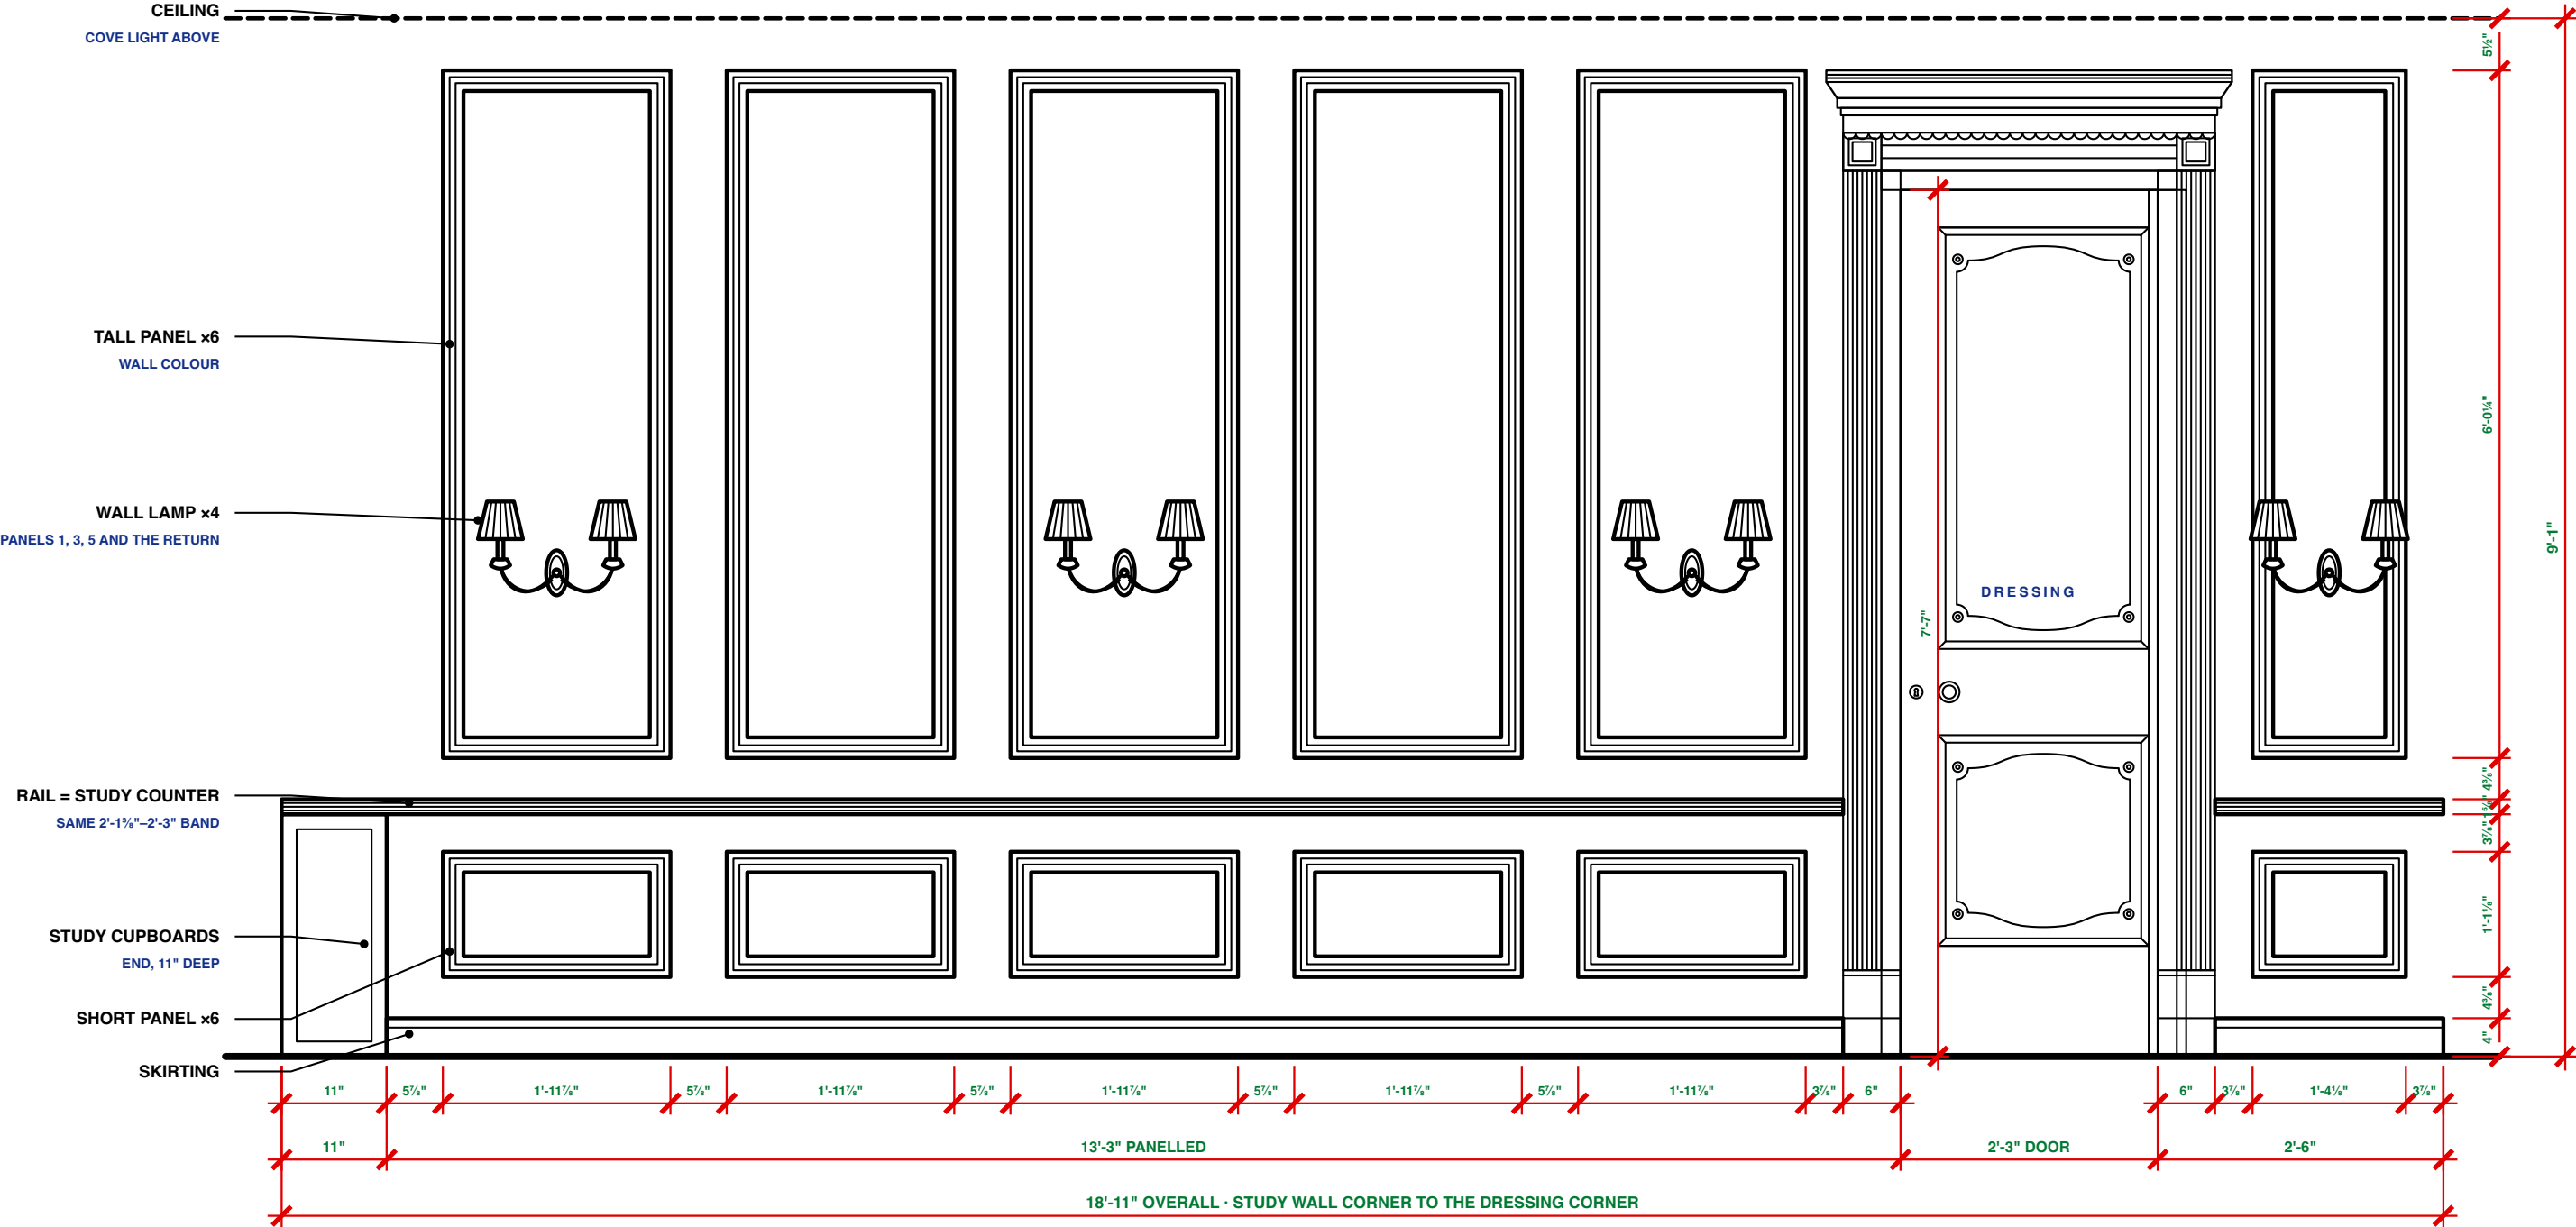

ELEVATION — RIGHT WALL


SEEN FROM THE ROOM · STUDY WALL ON THE LEFT · OPTION C

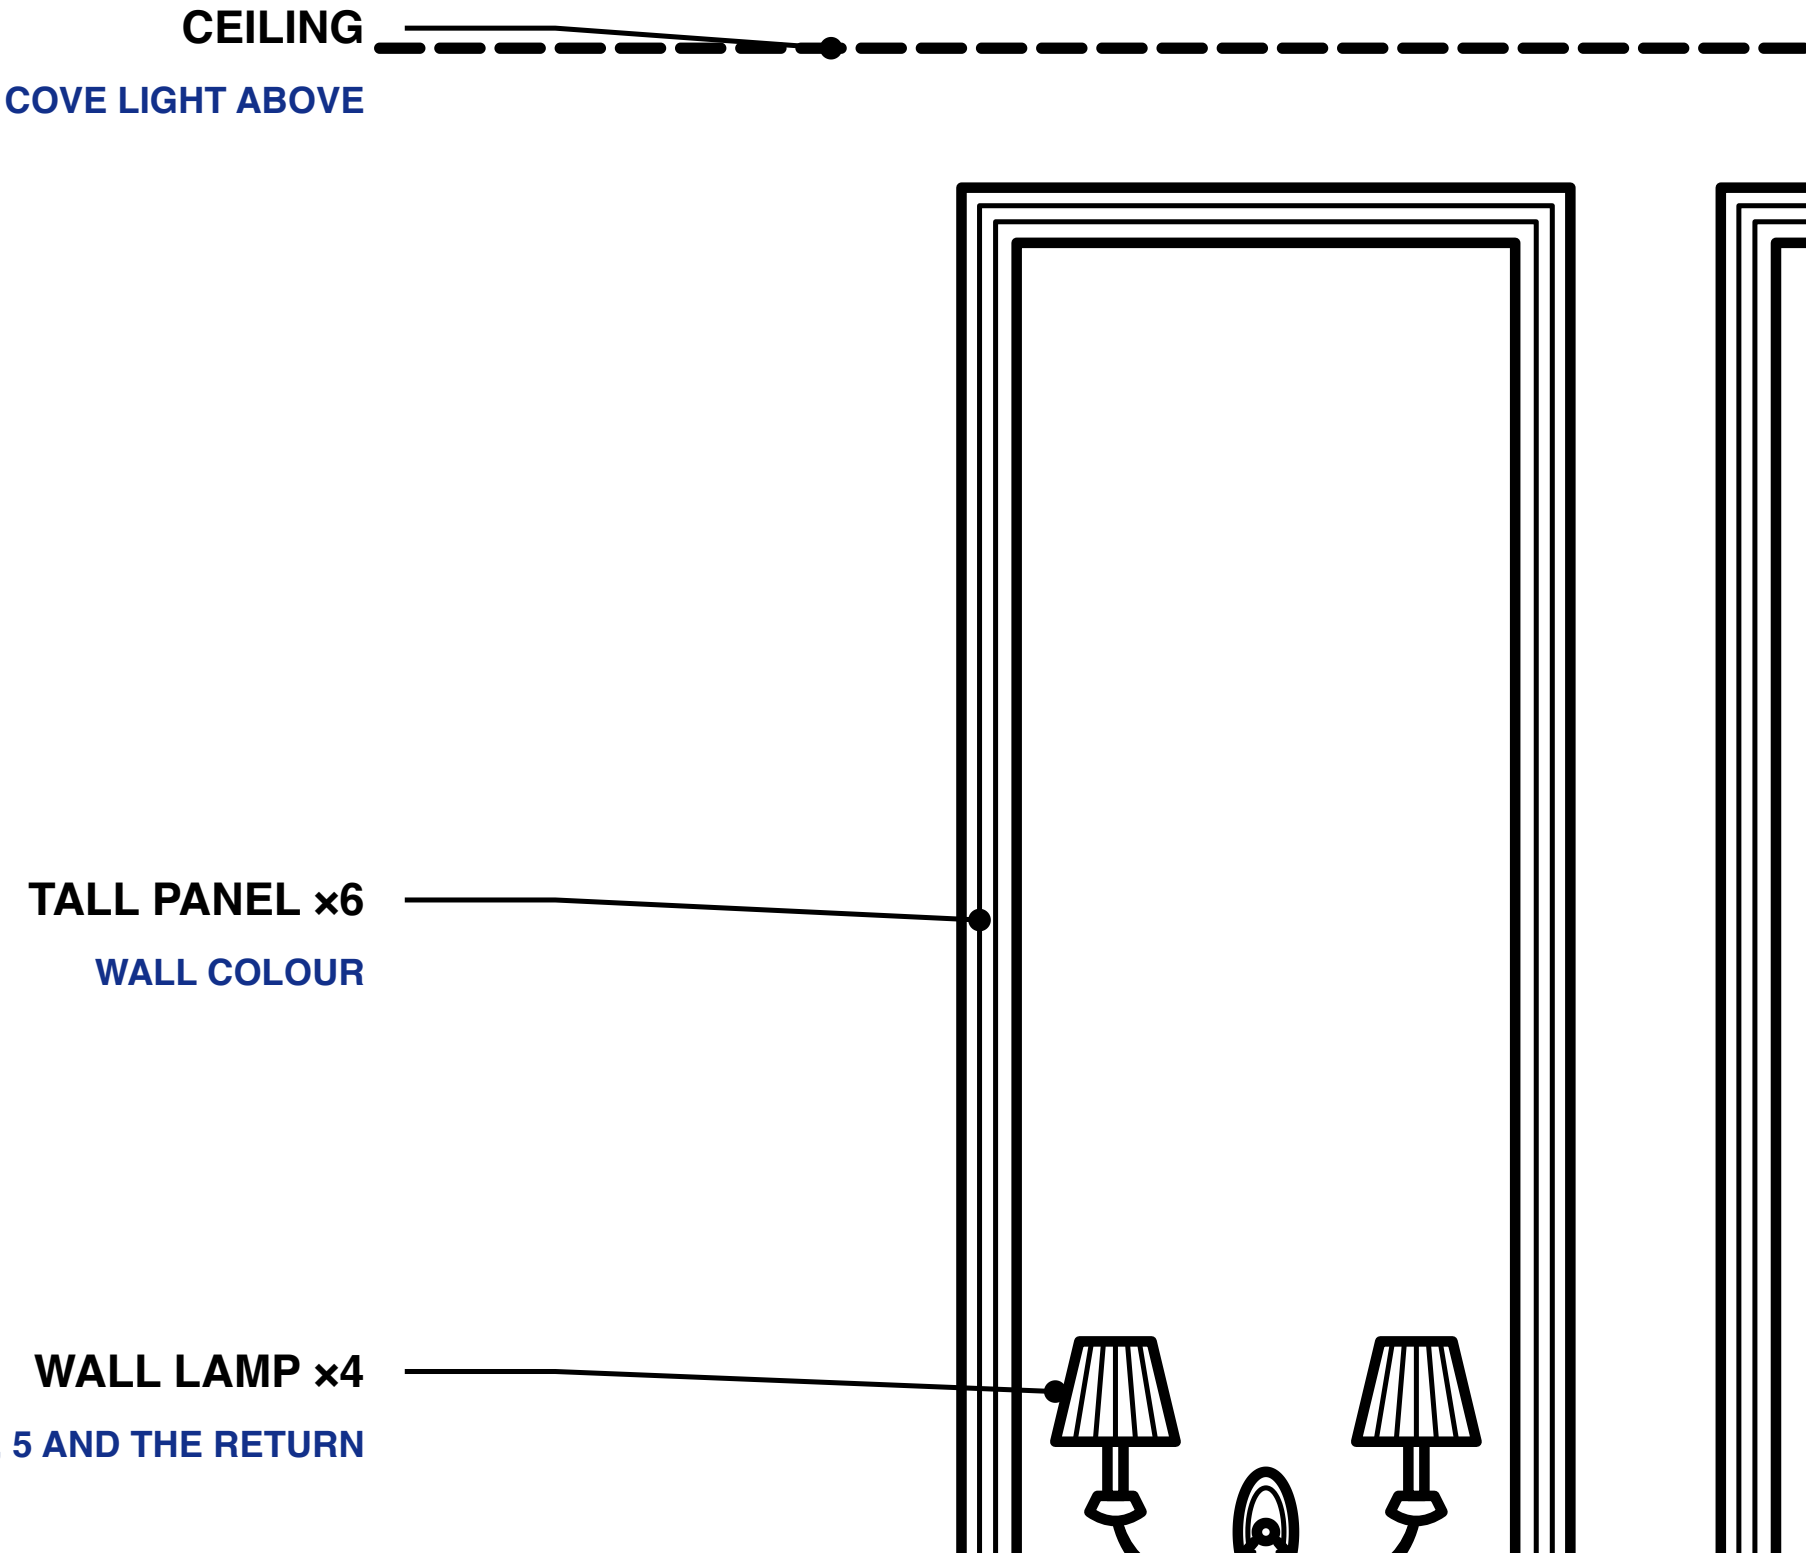


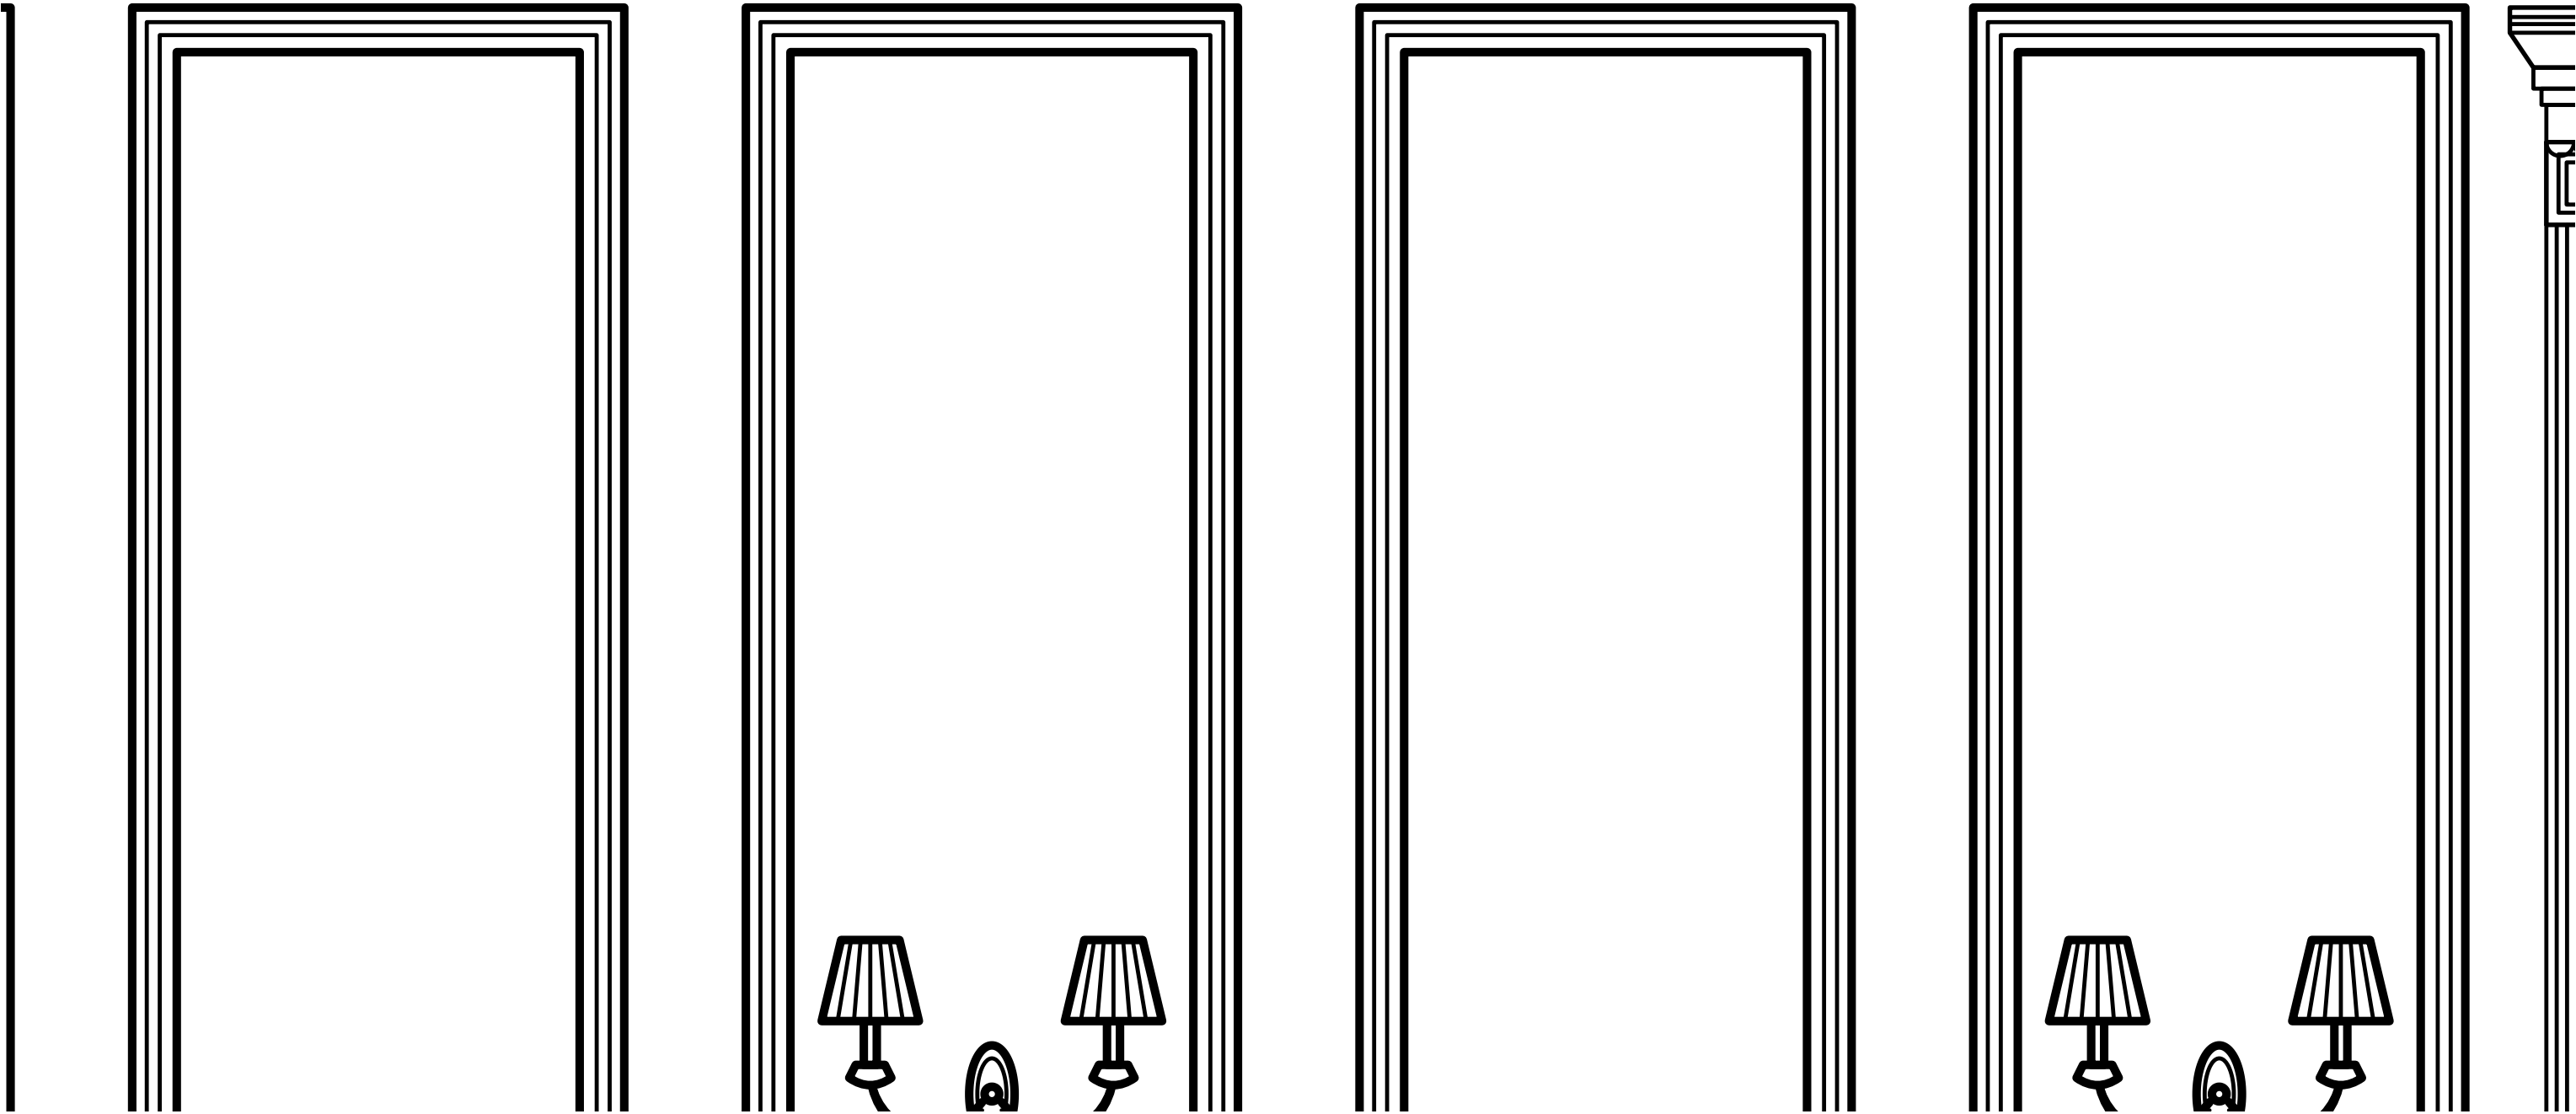

Aa note


All sizes in feet and inches. Enlarged — go by the written sizes, never measure the paper.

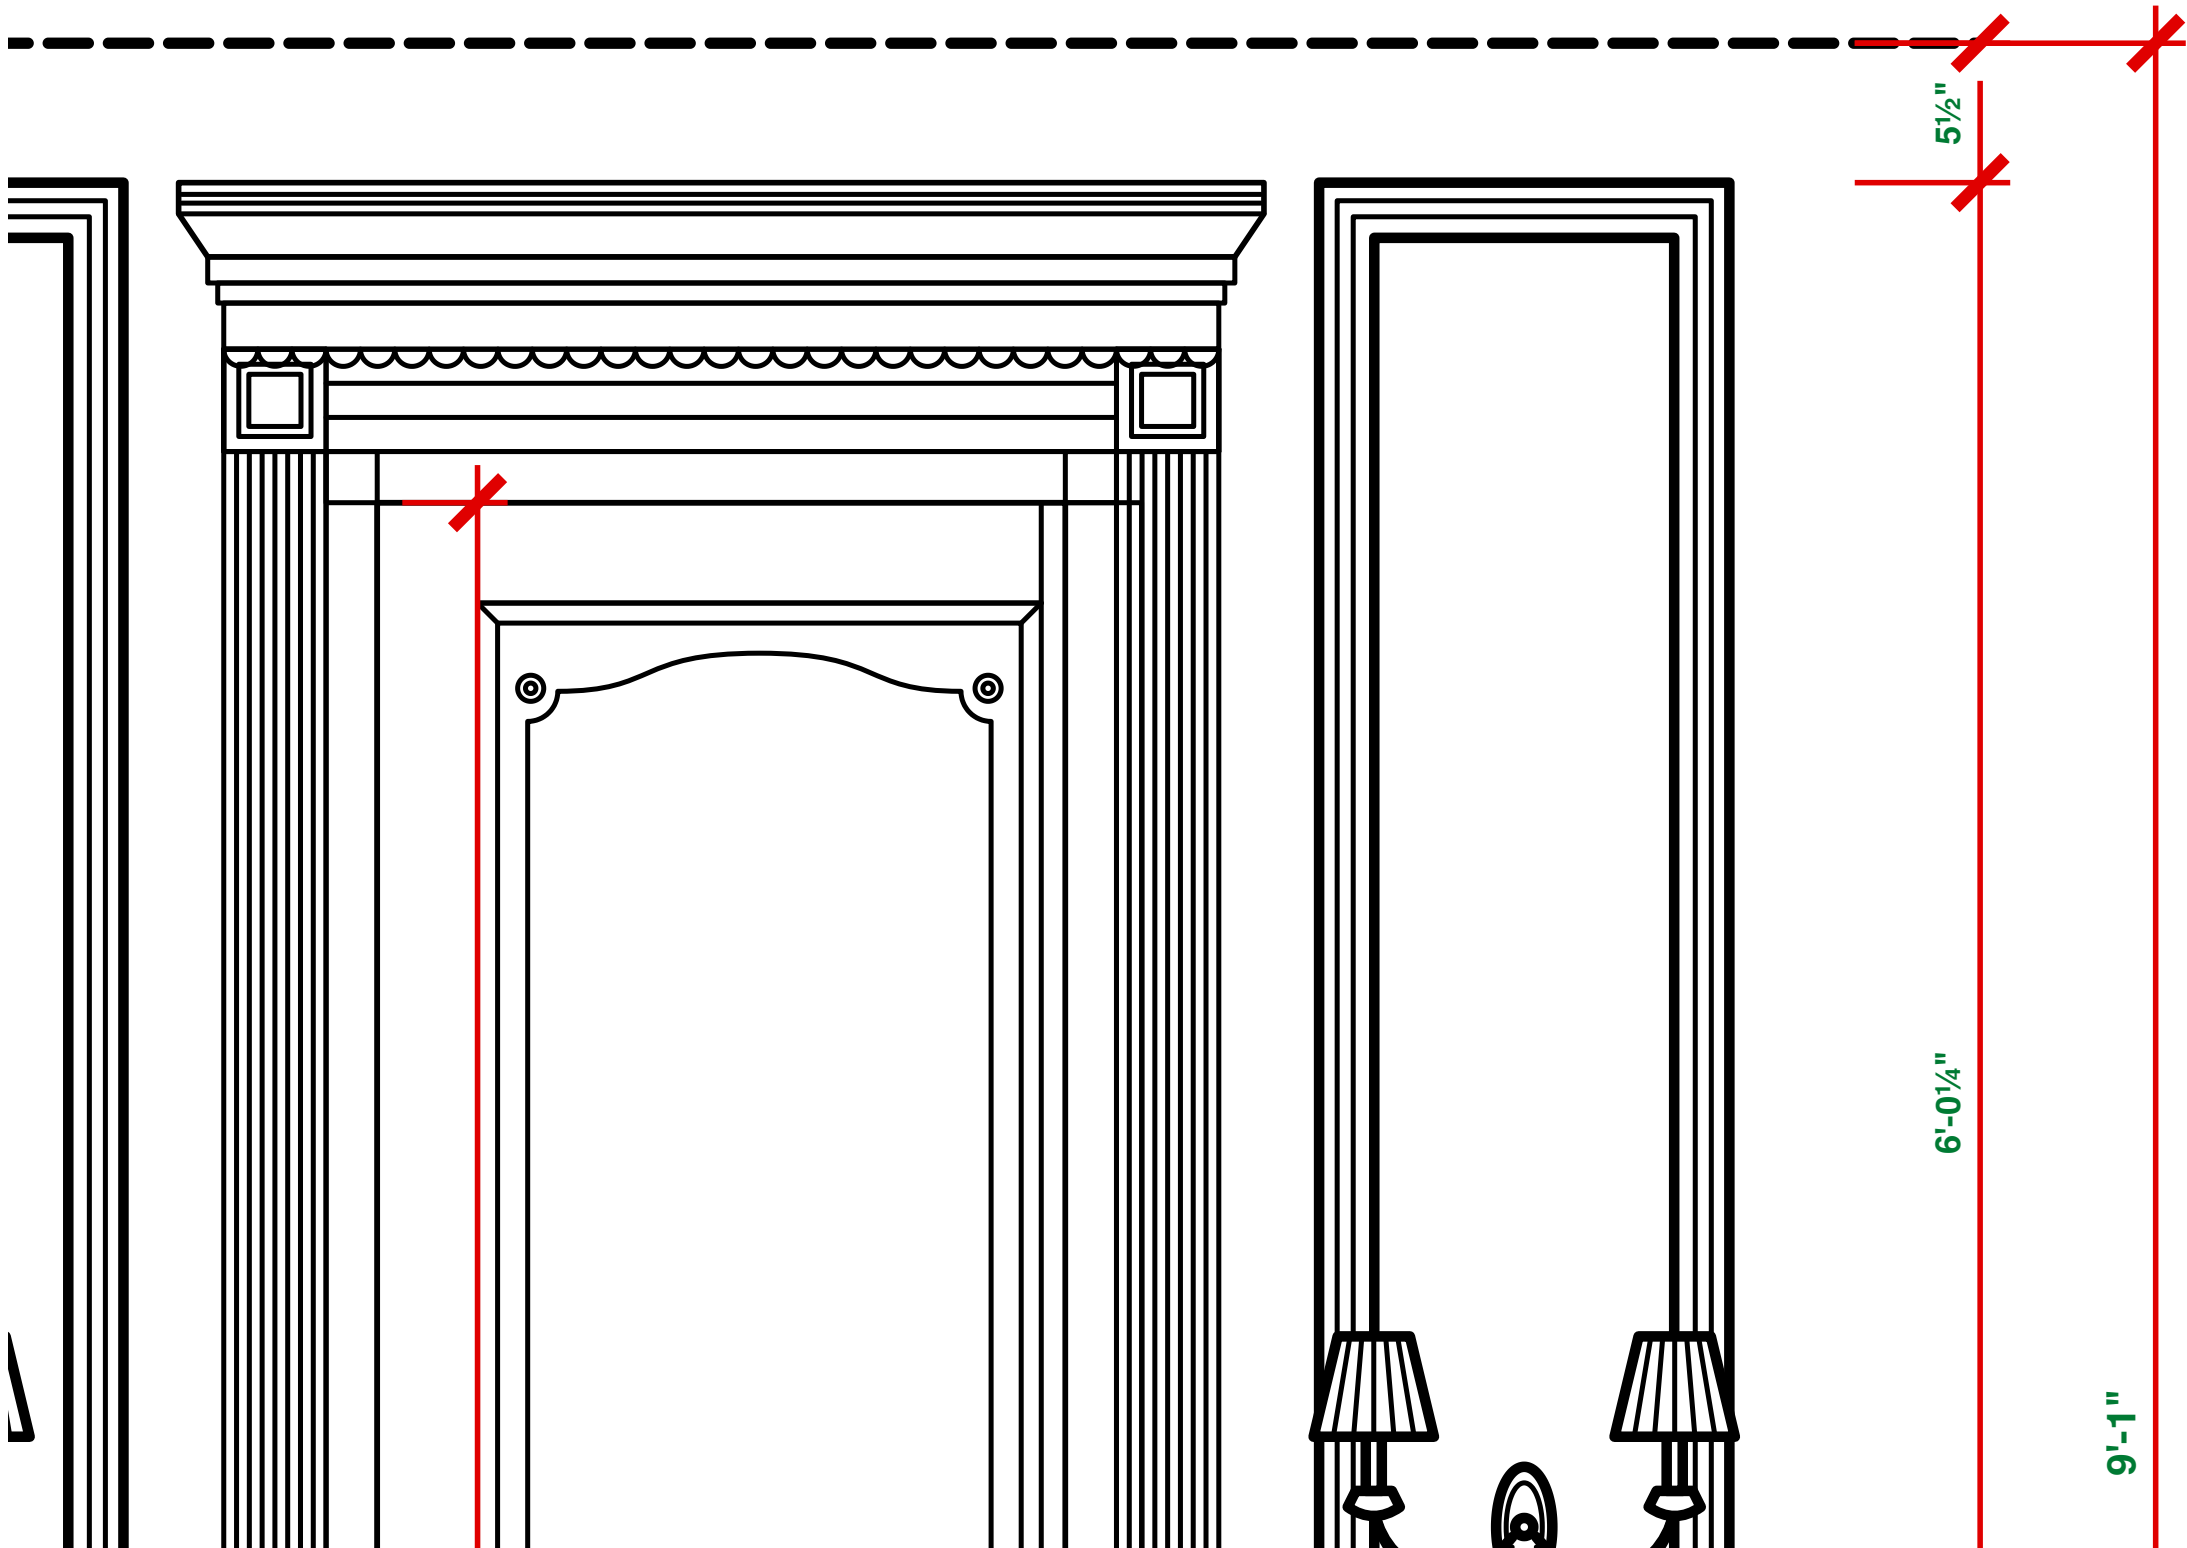

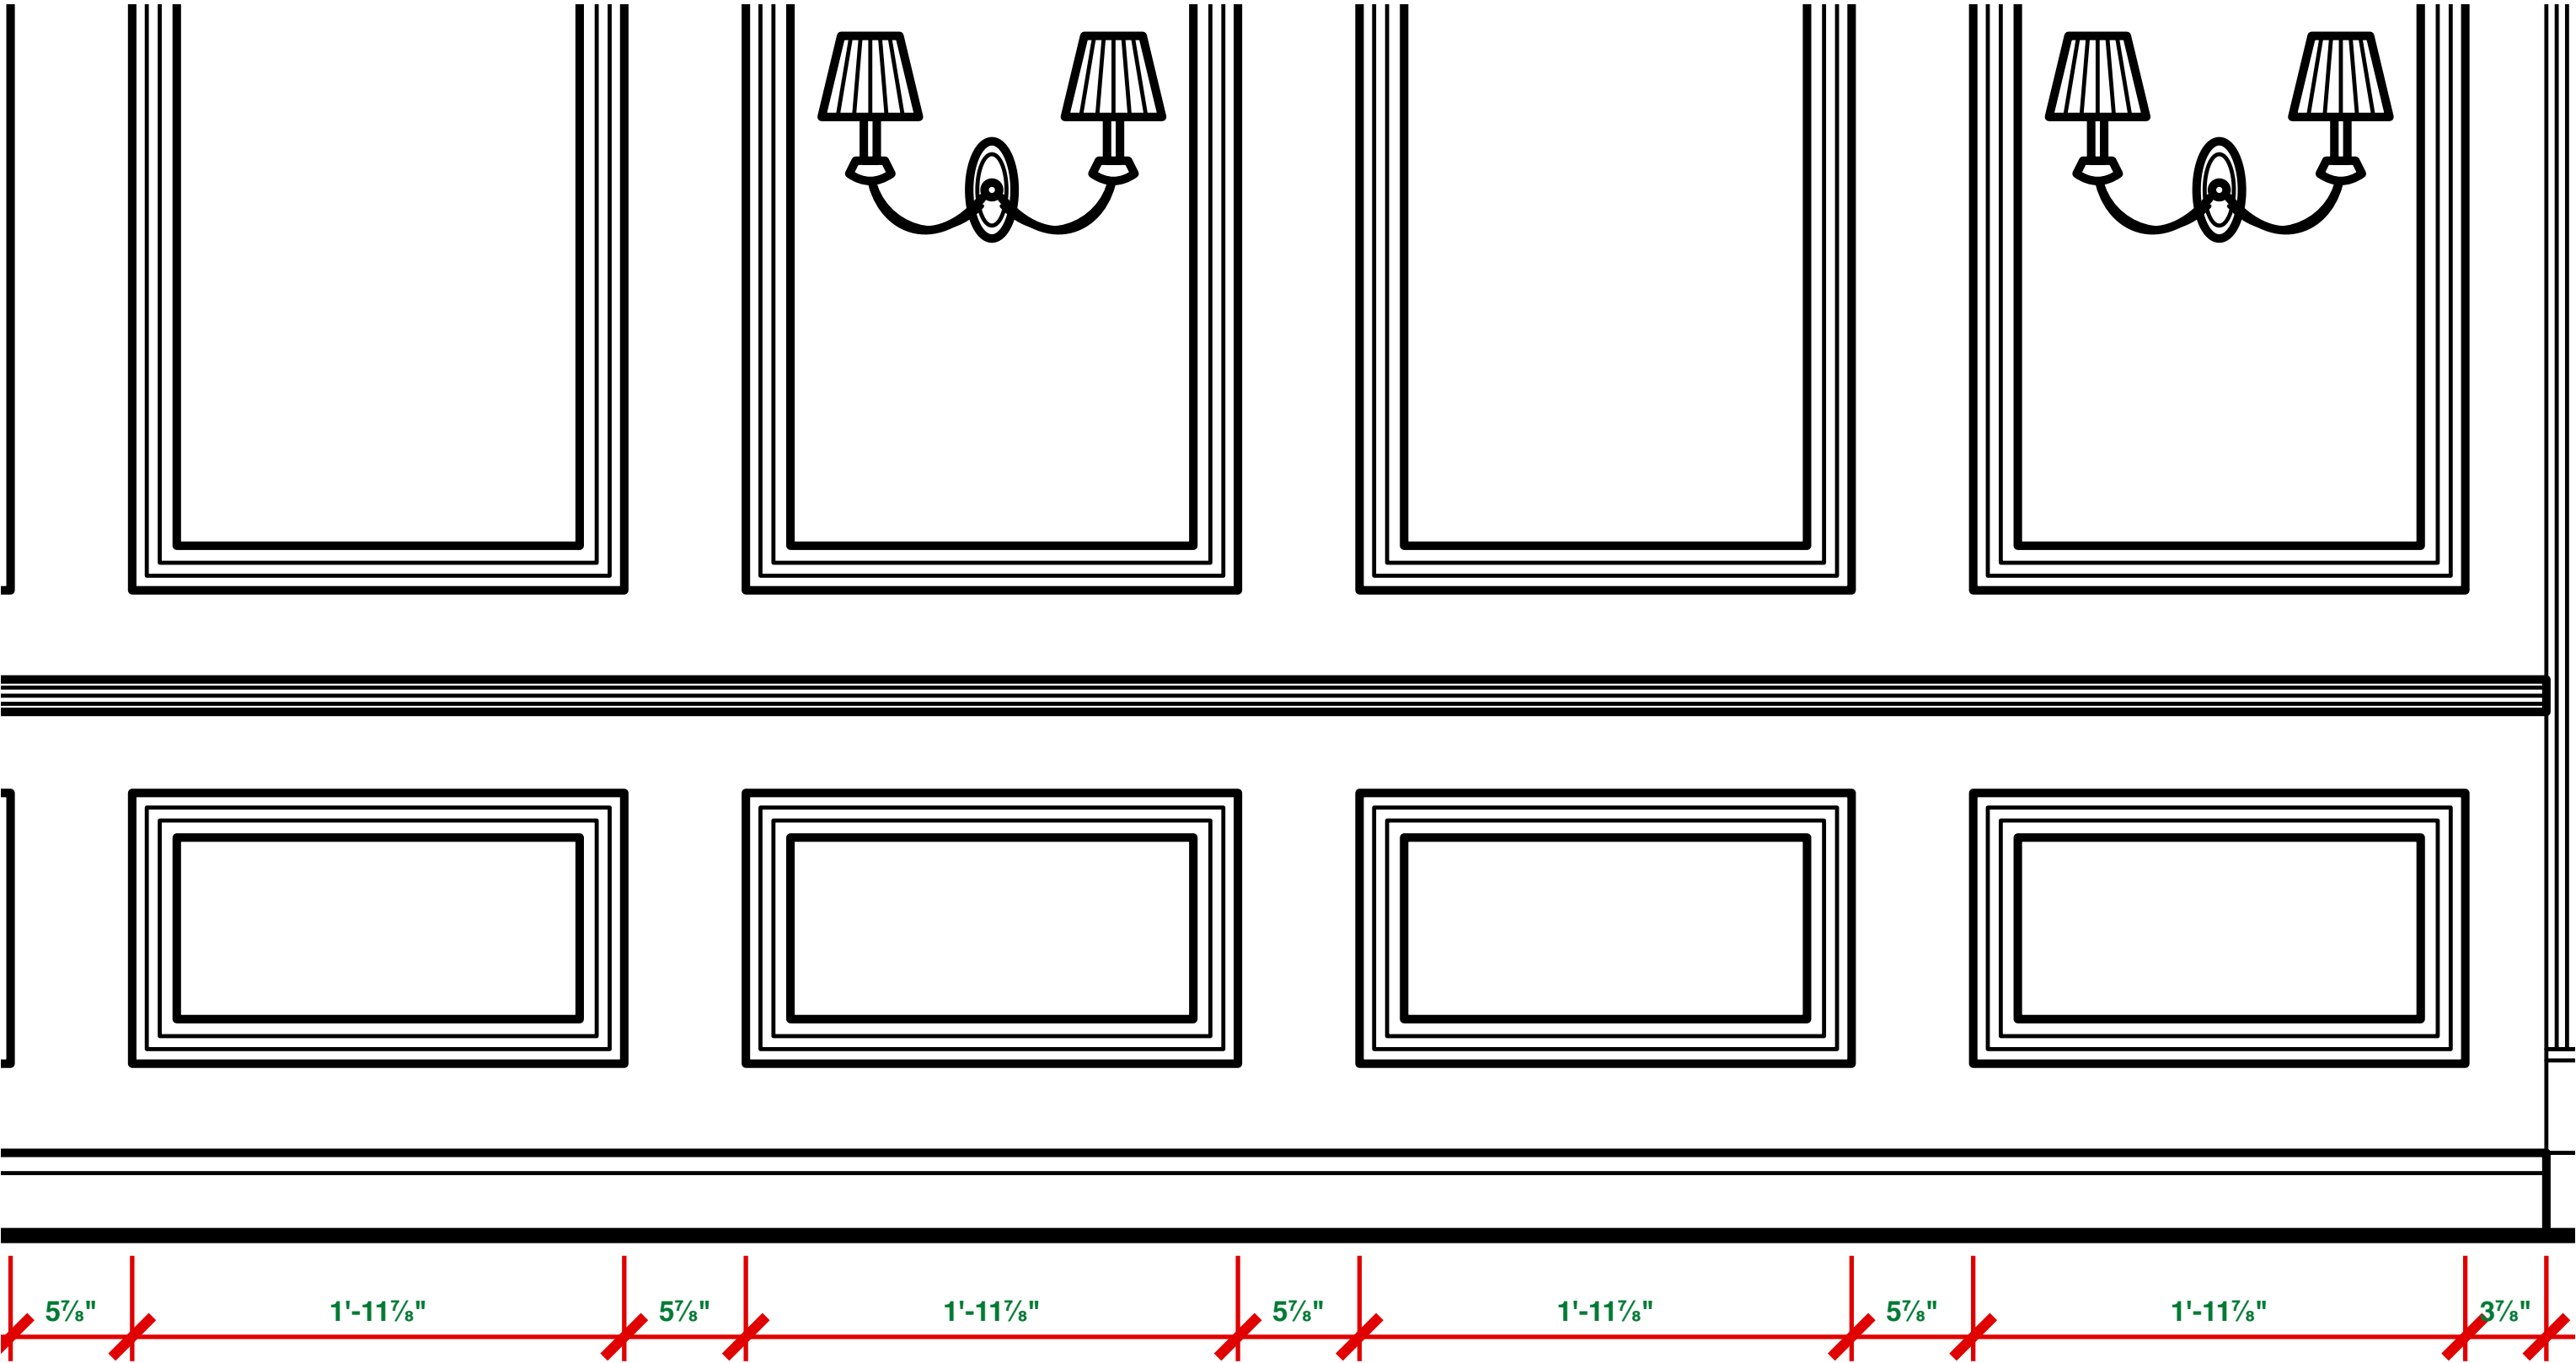


13'-3" PANELLED

18'-11" OVERALL · STUDY WALL CORNER TO THE DRESSING CORNER

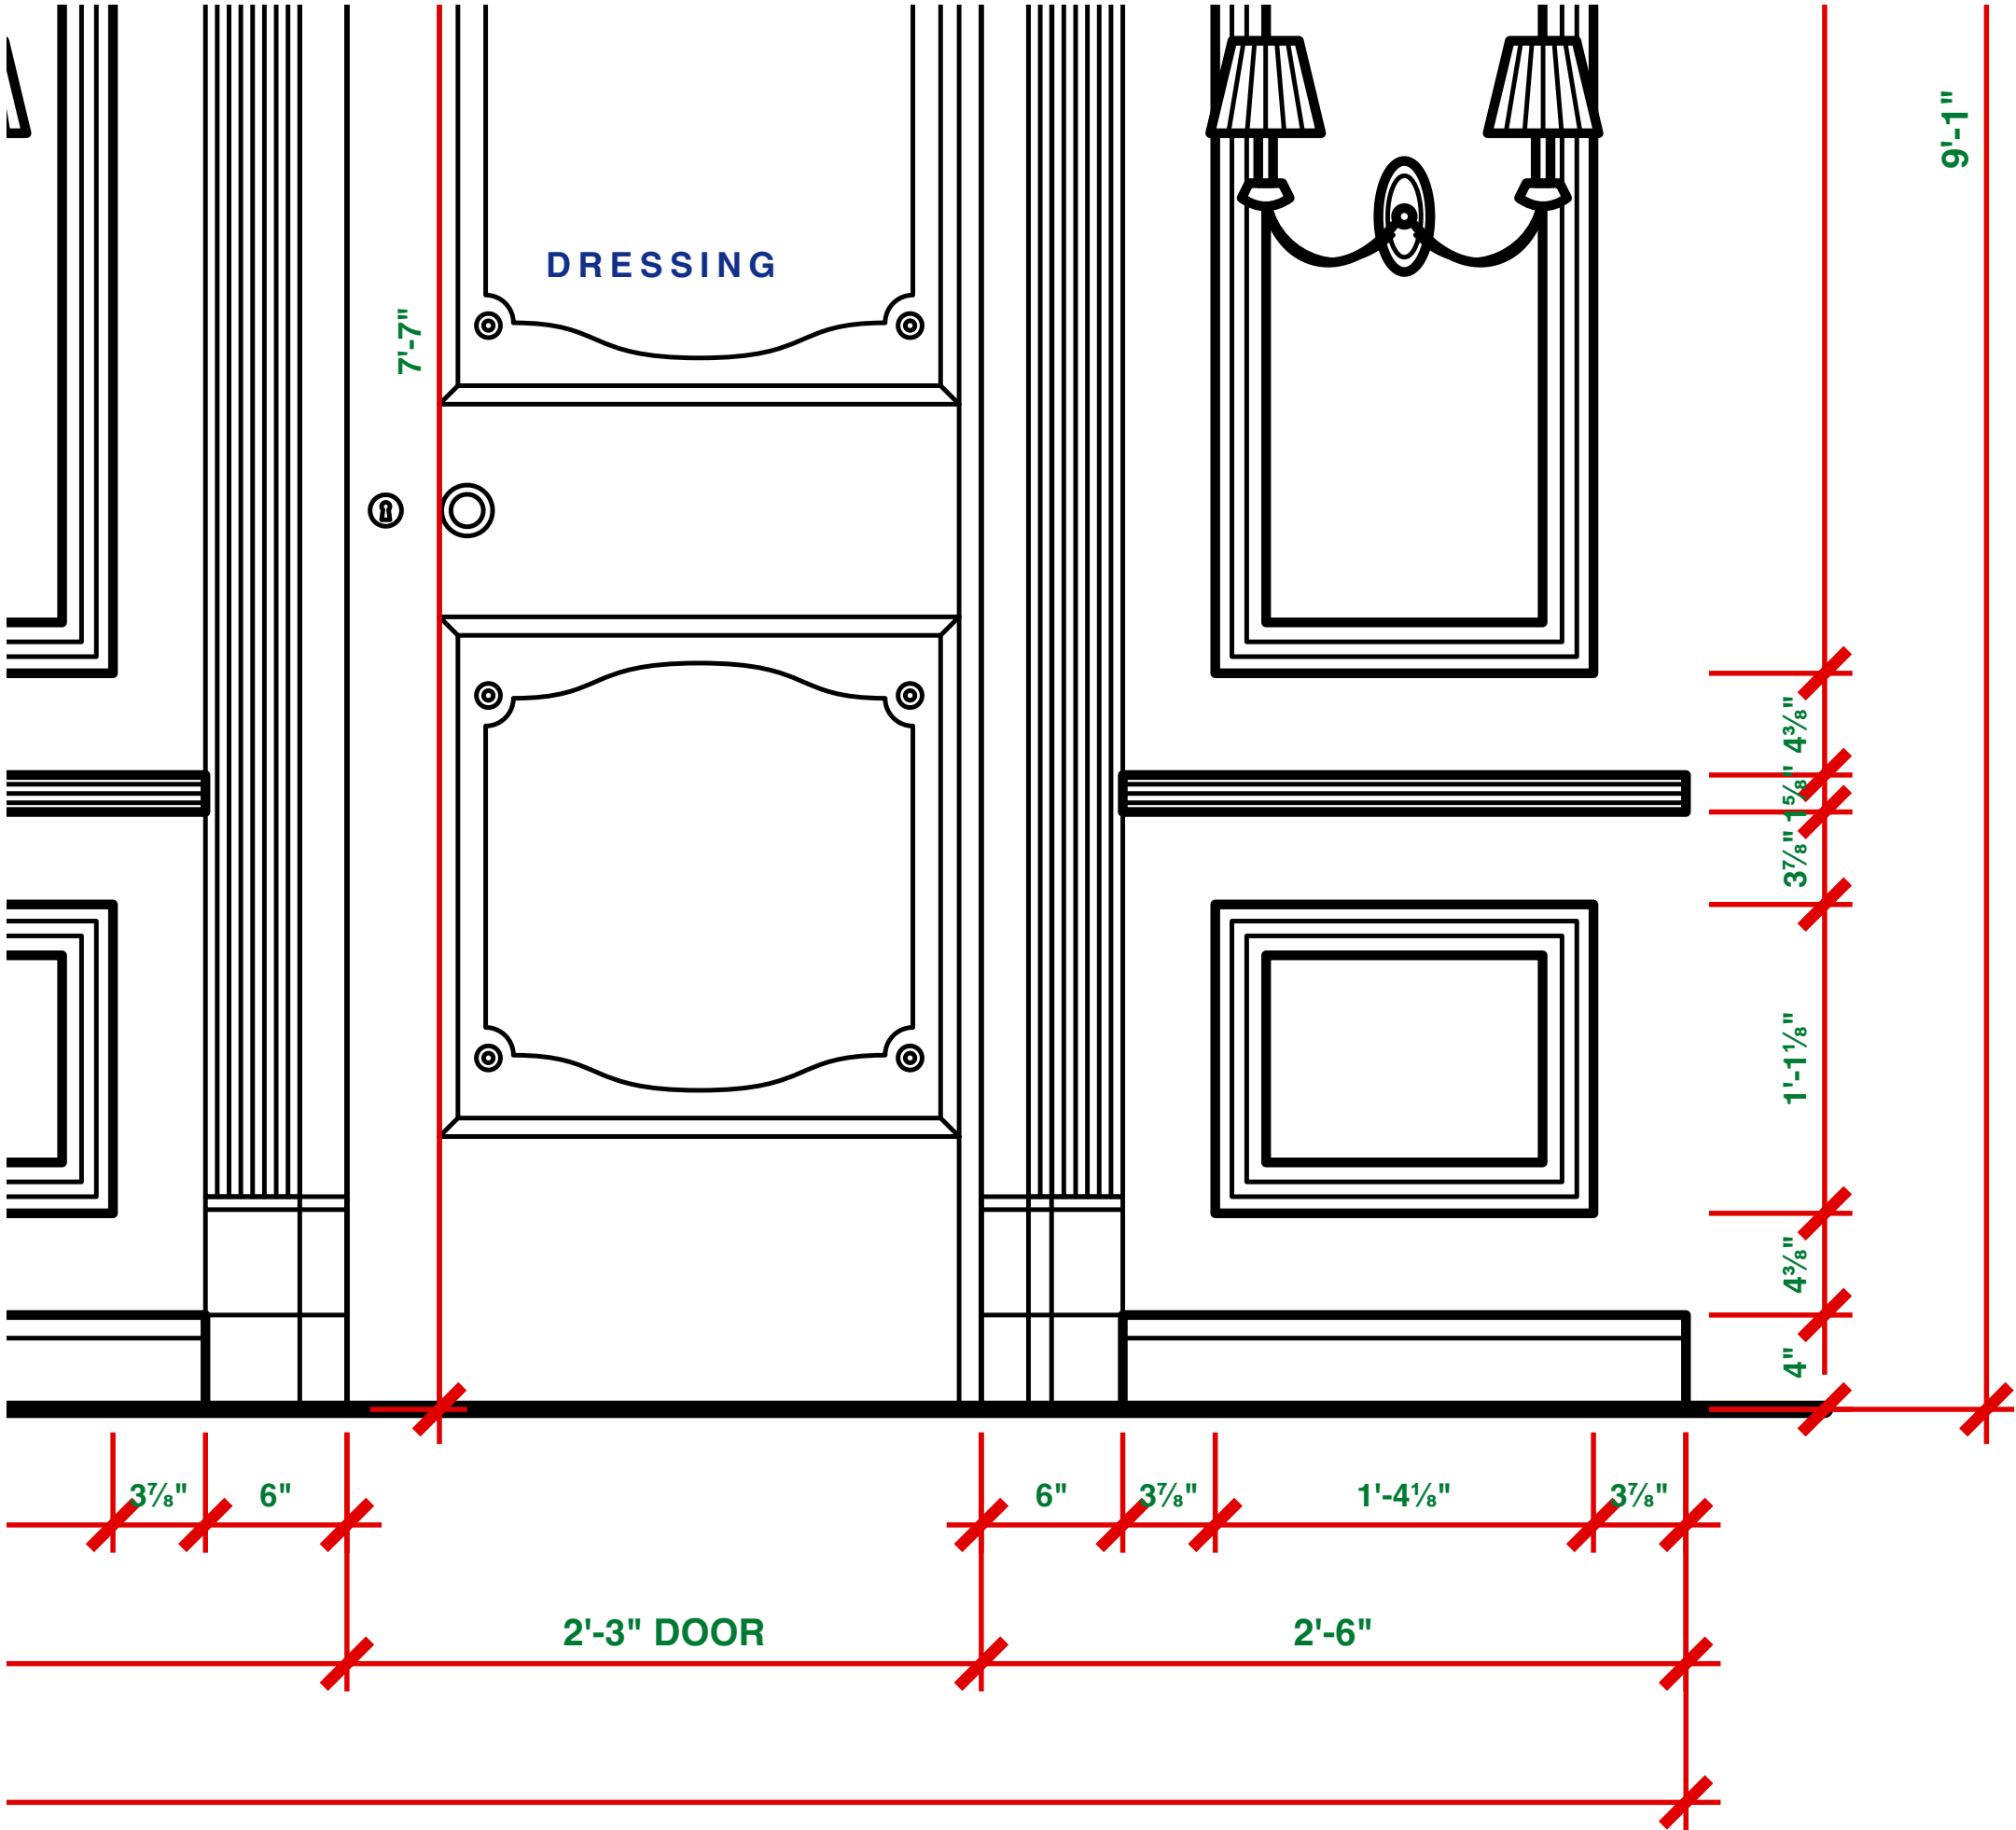


SECTION A-A


THROUGH PANEL 1

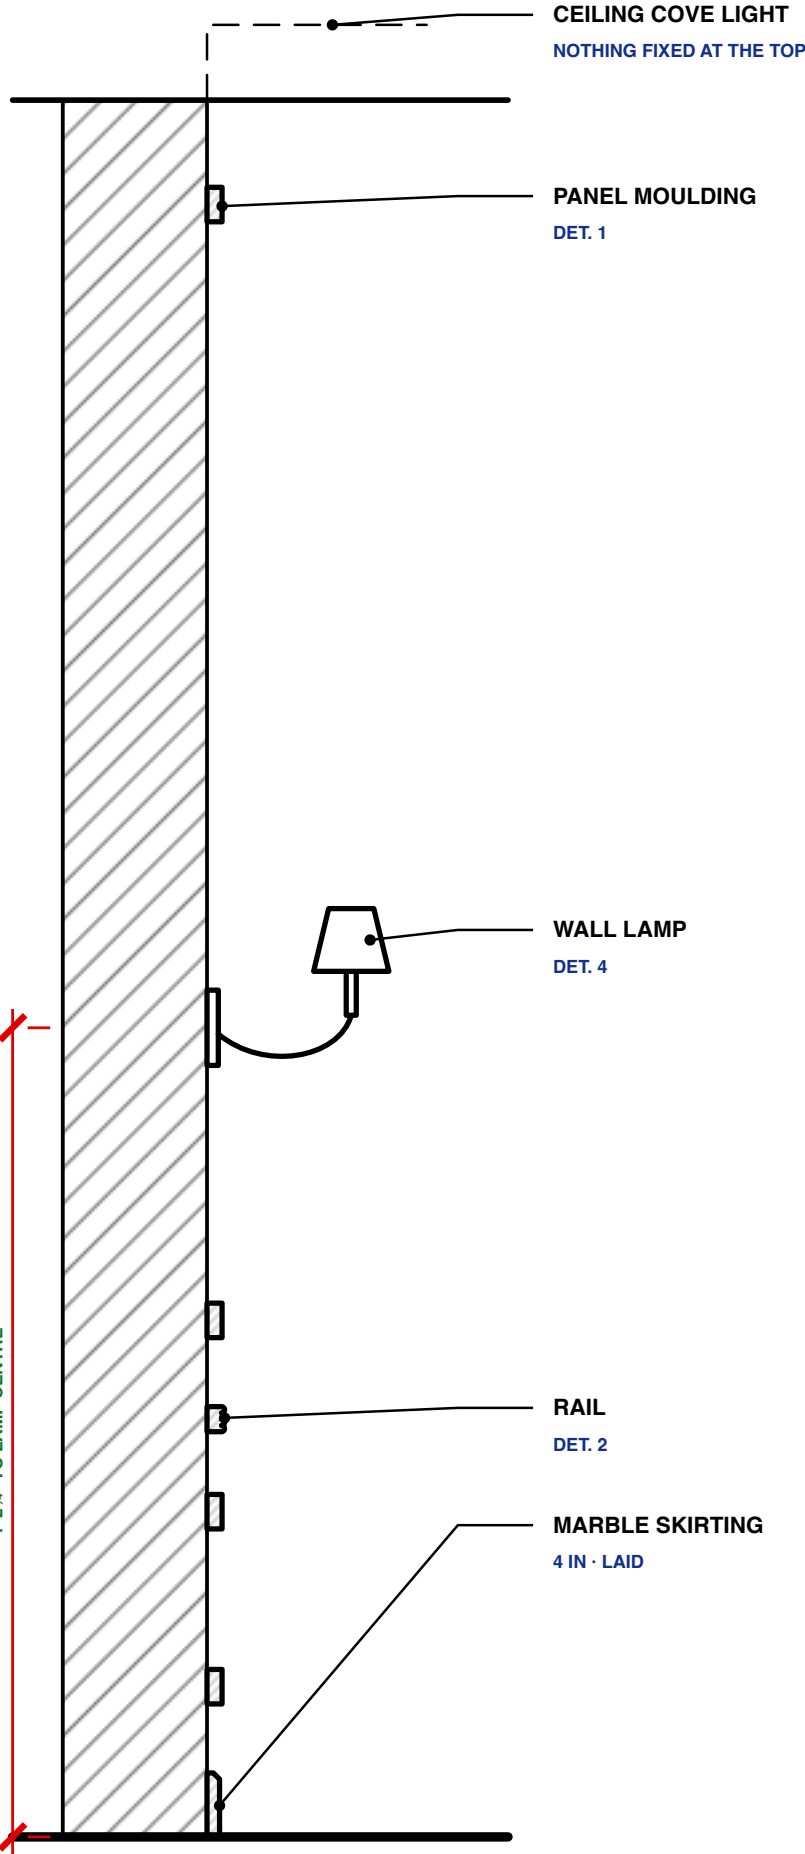

SECTION A–A


THROUGH PANEL 1

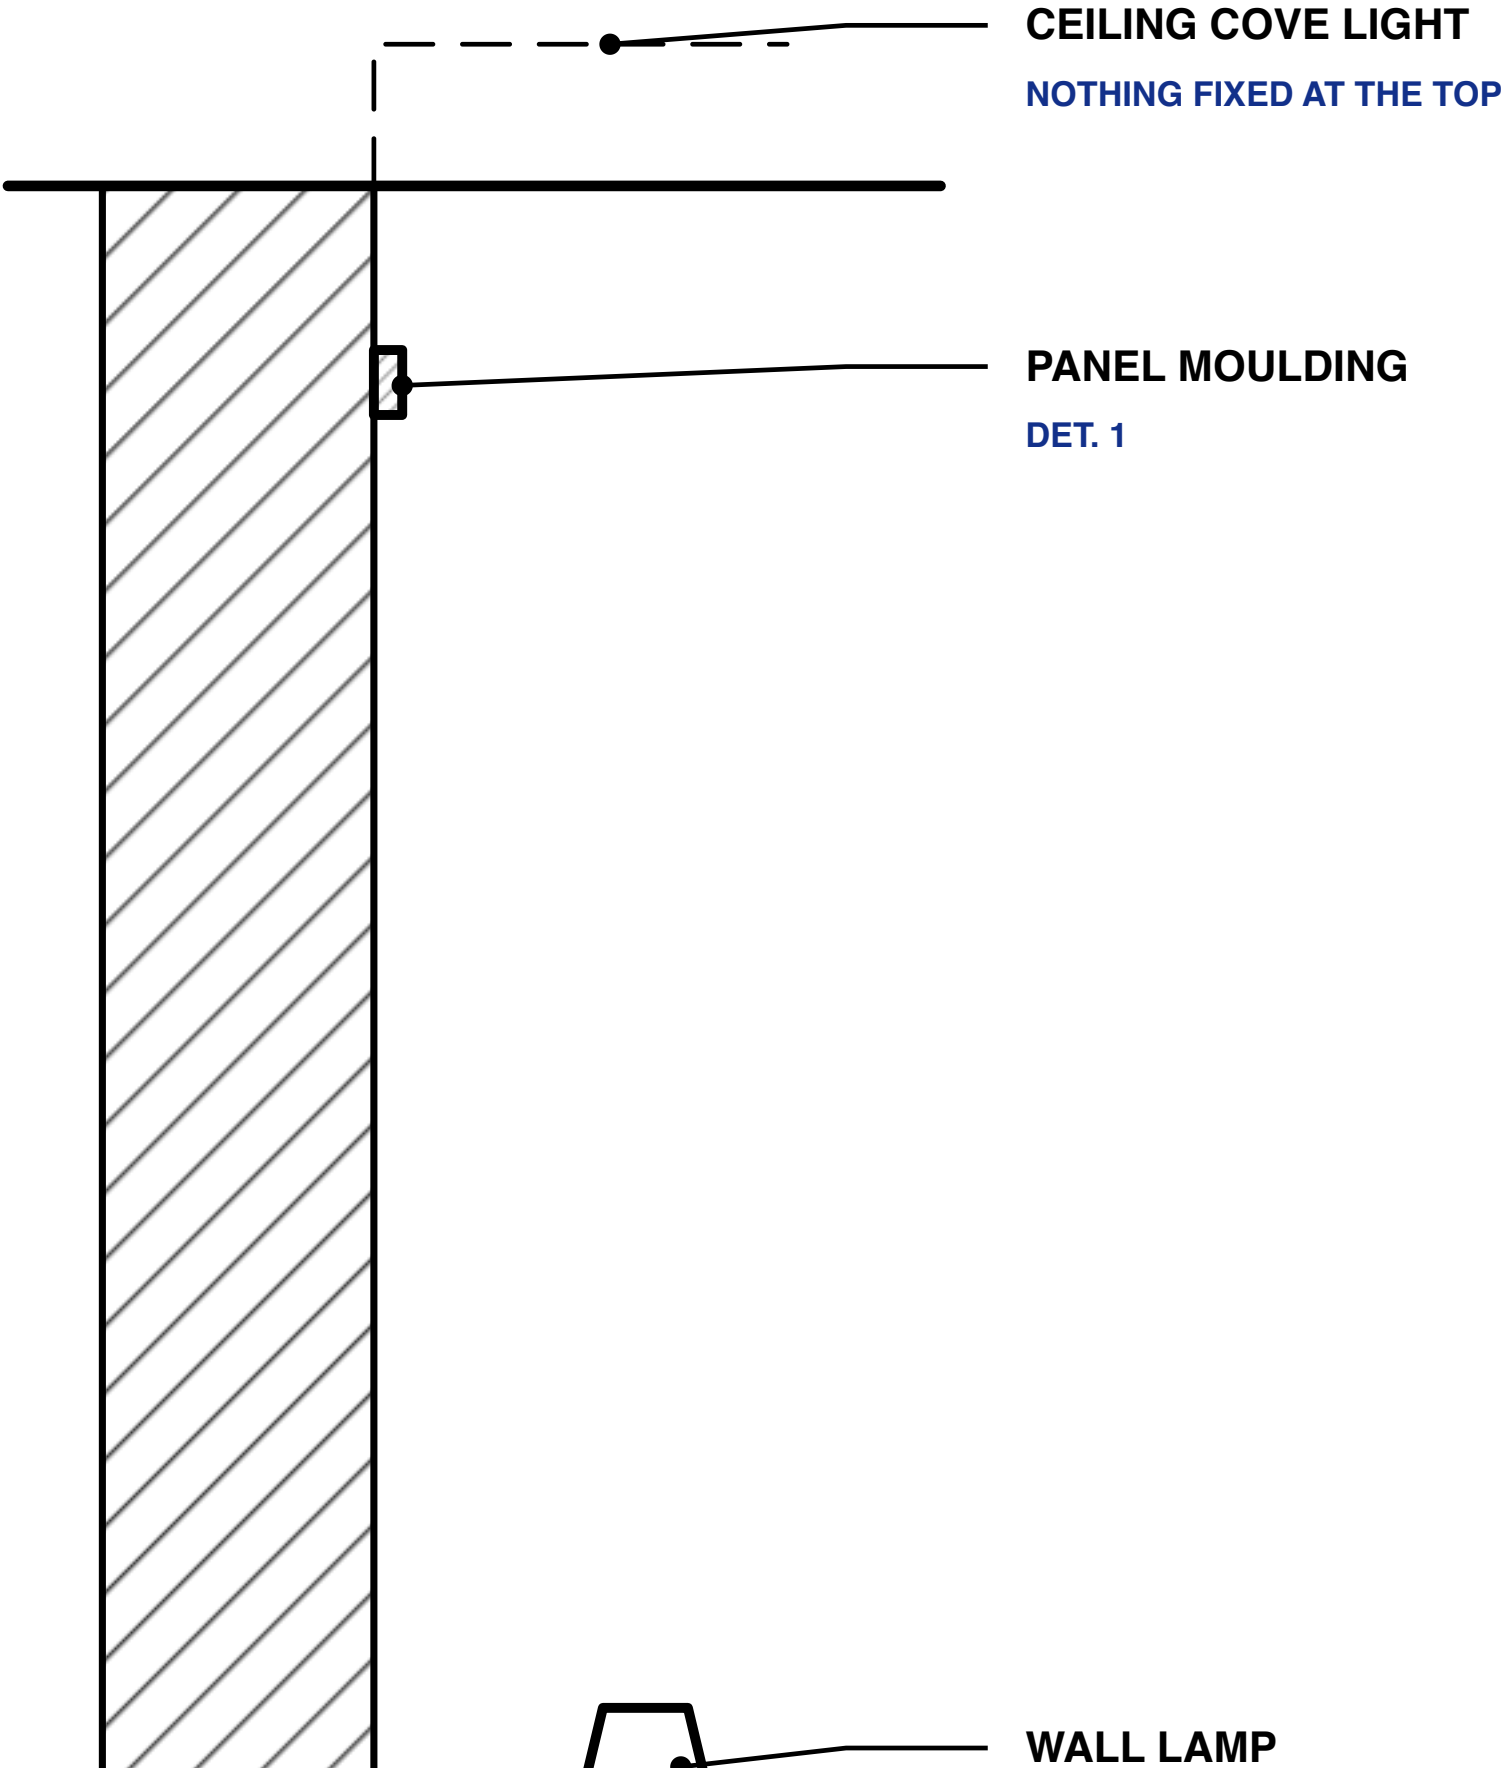

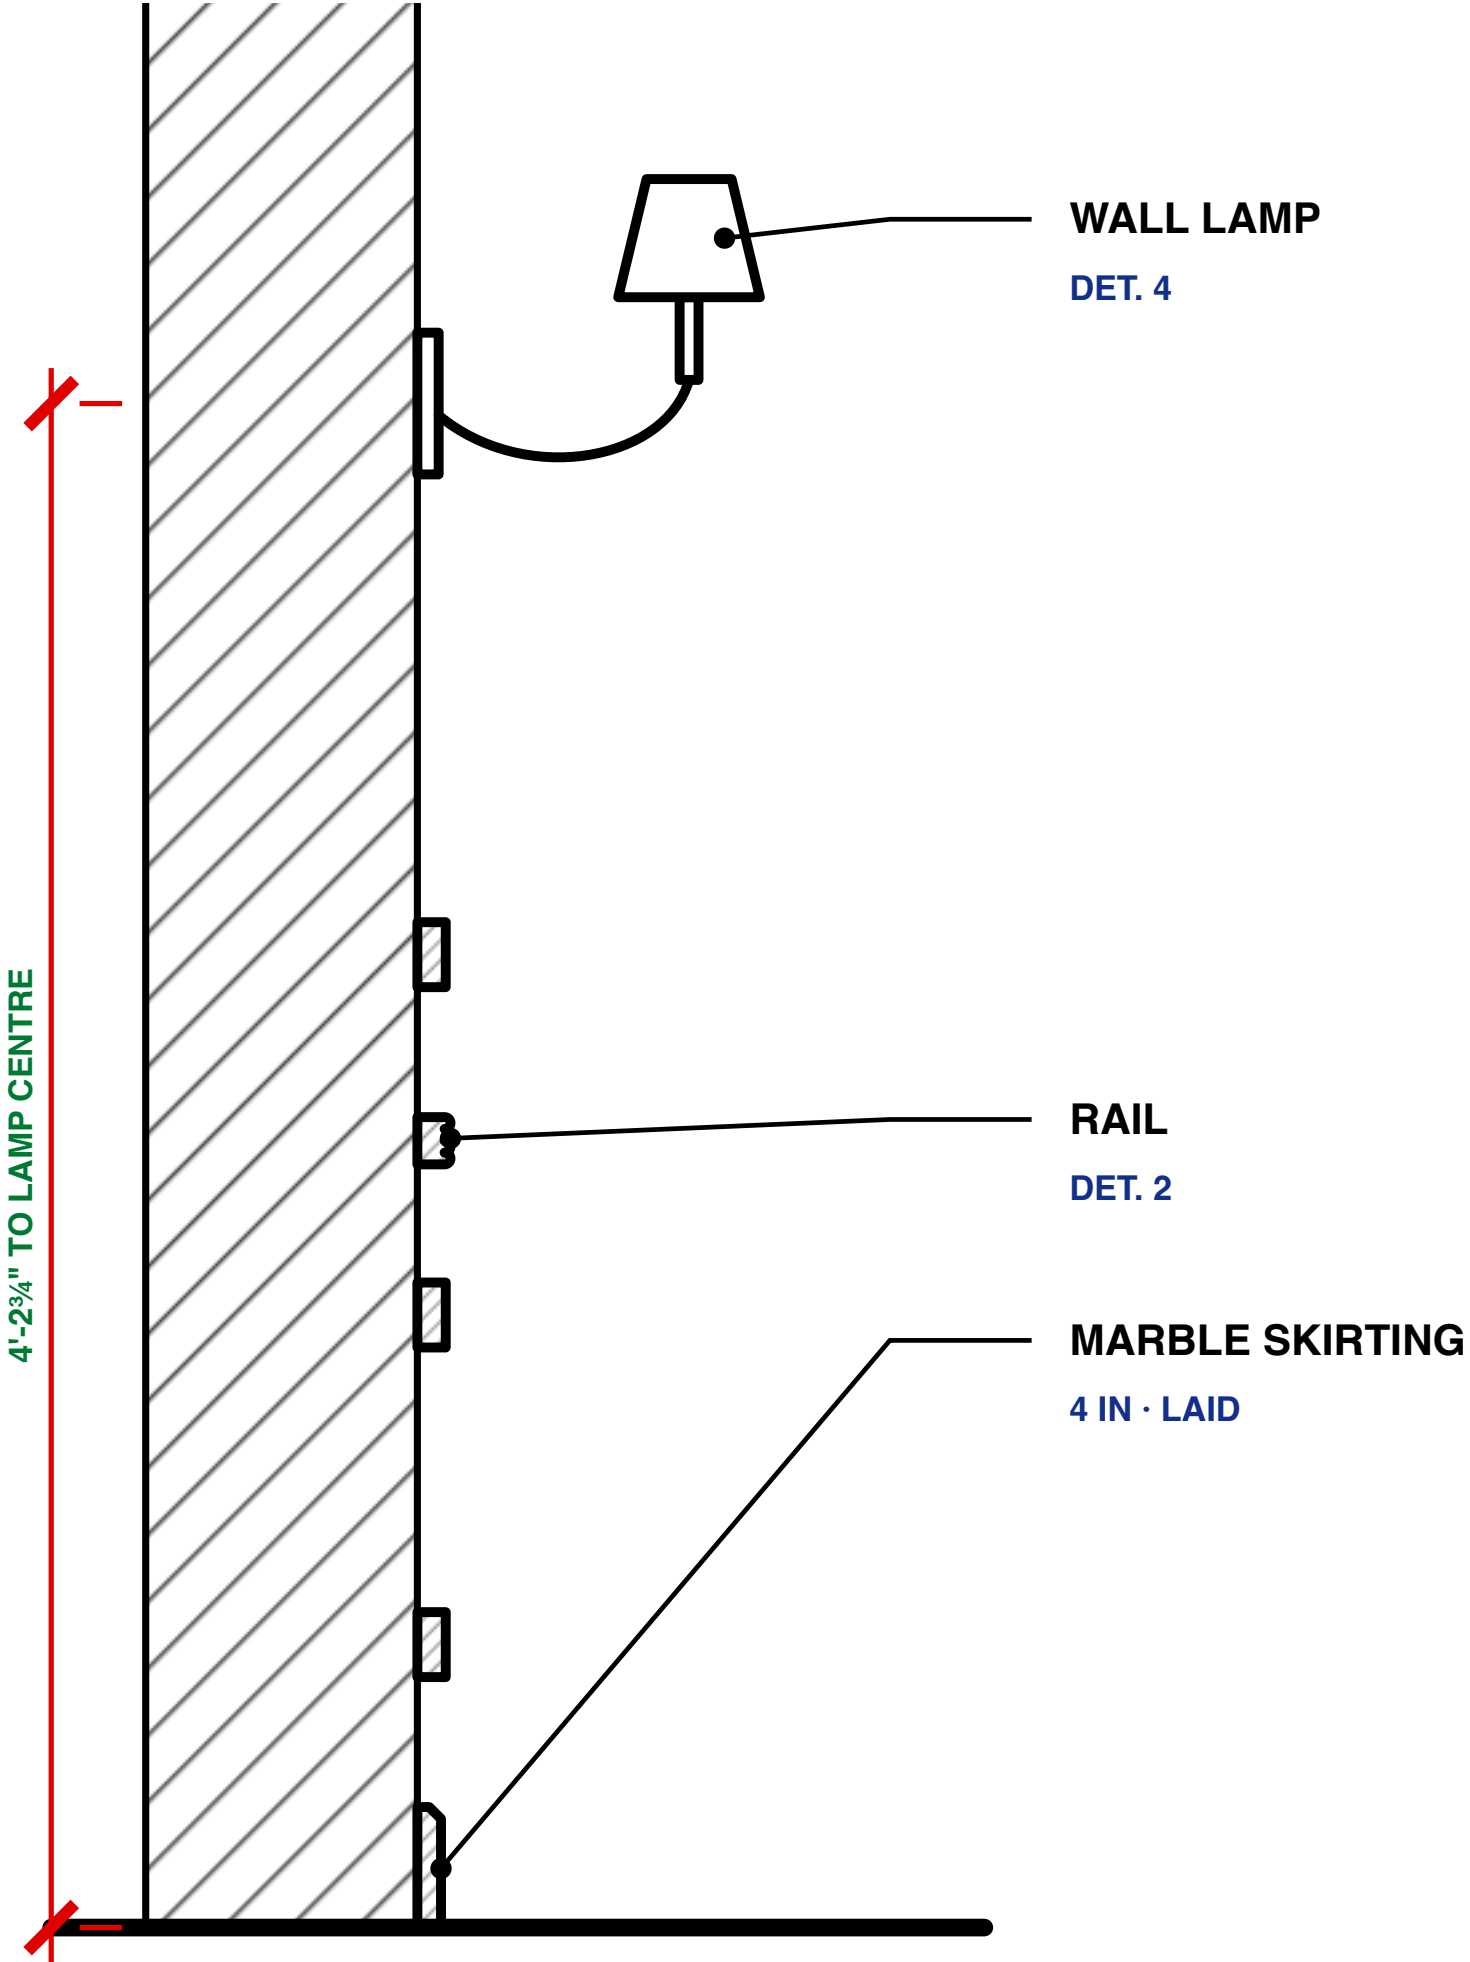


PLAN


CUT AT 3'-3 3/8" · ROOM BELOW, WALL ABOVE

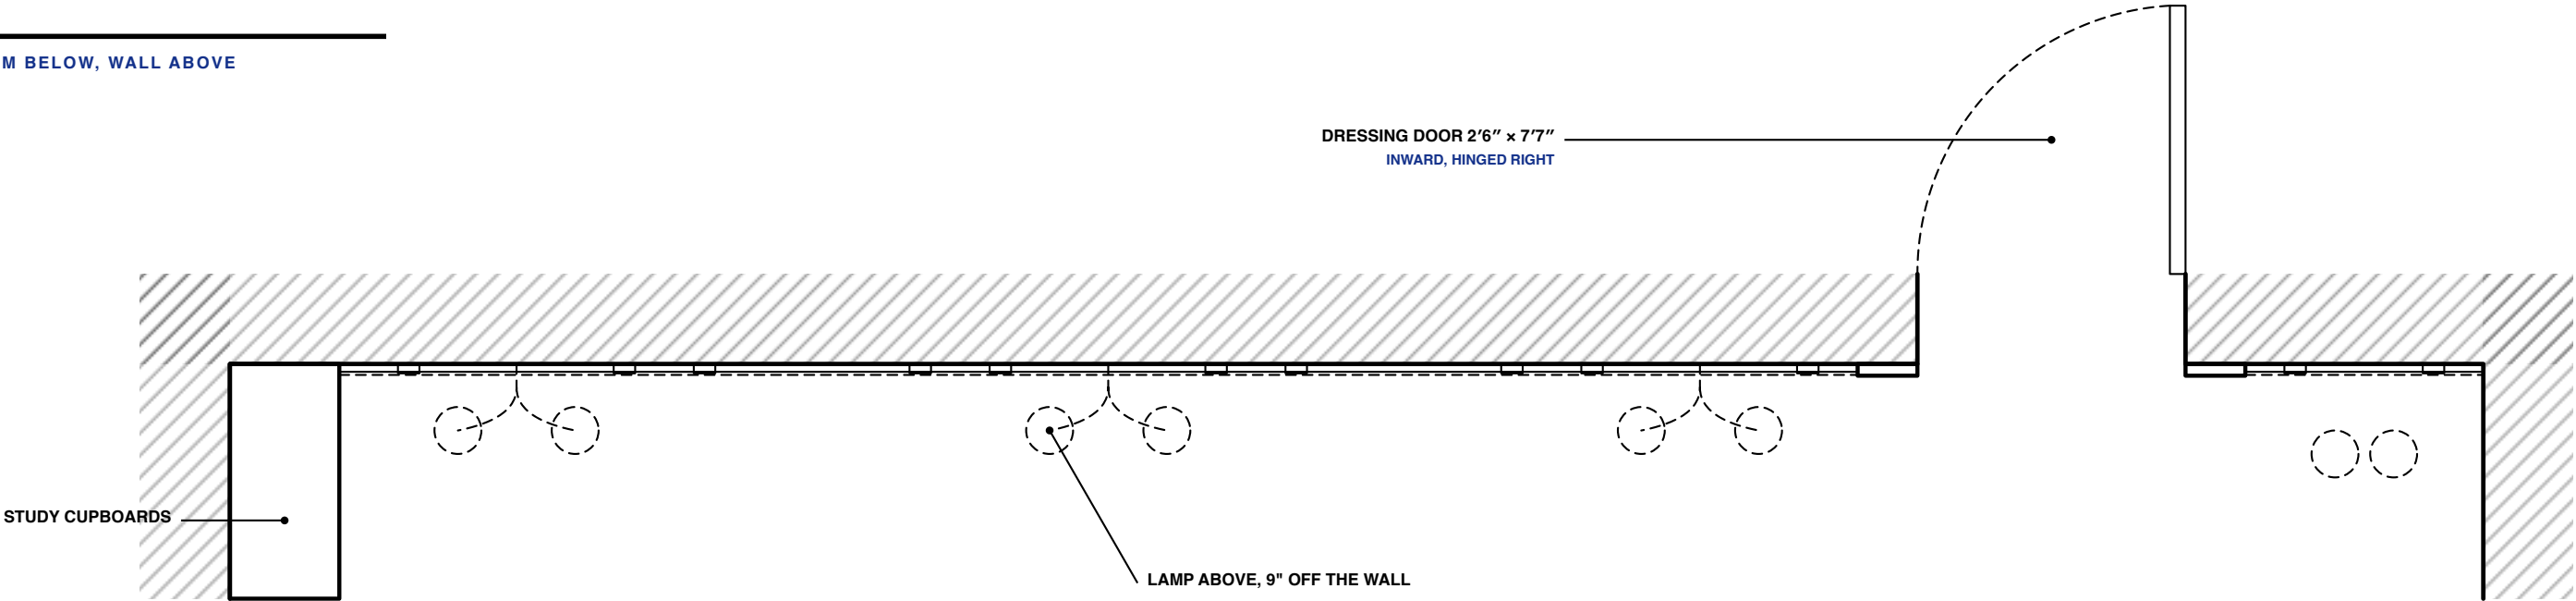

PLAN


CUT AT 3'-3 3/8" · ROOM BELOW, WALL ABOVE

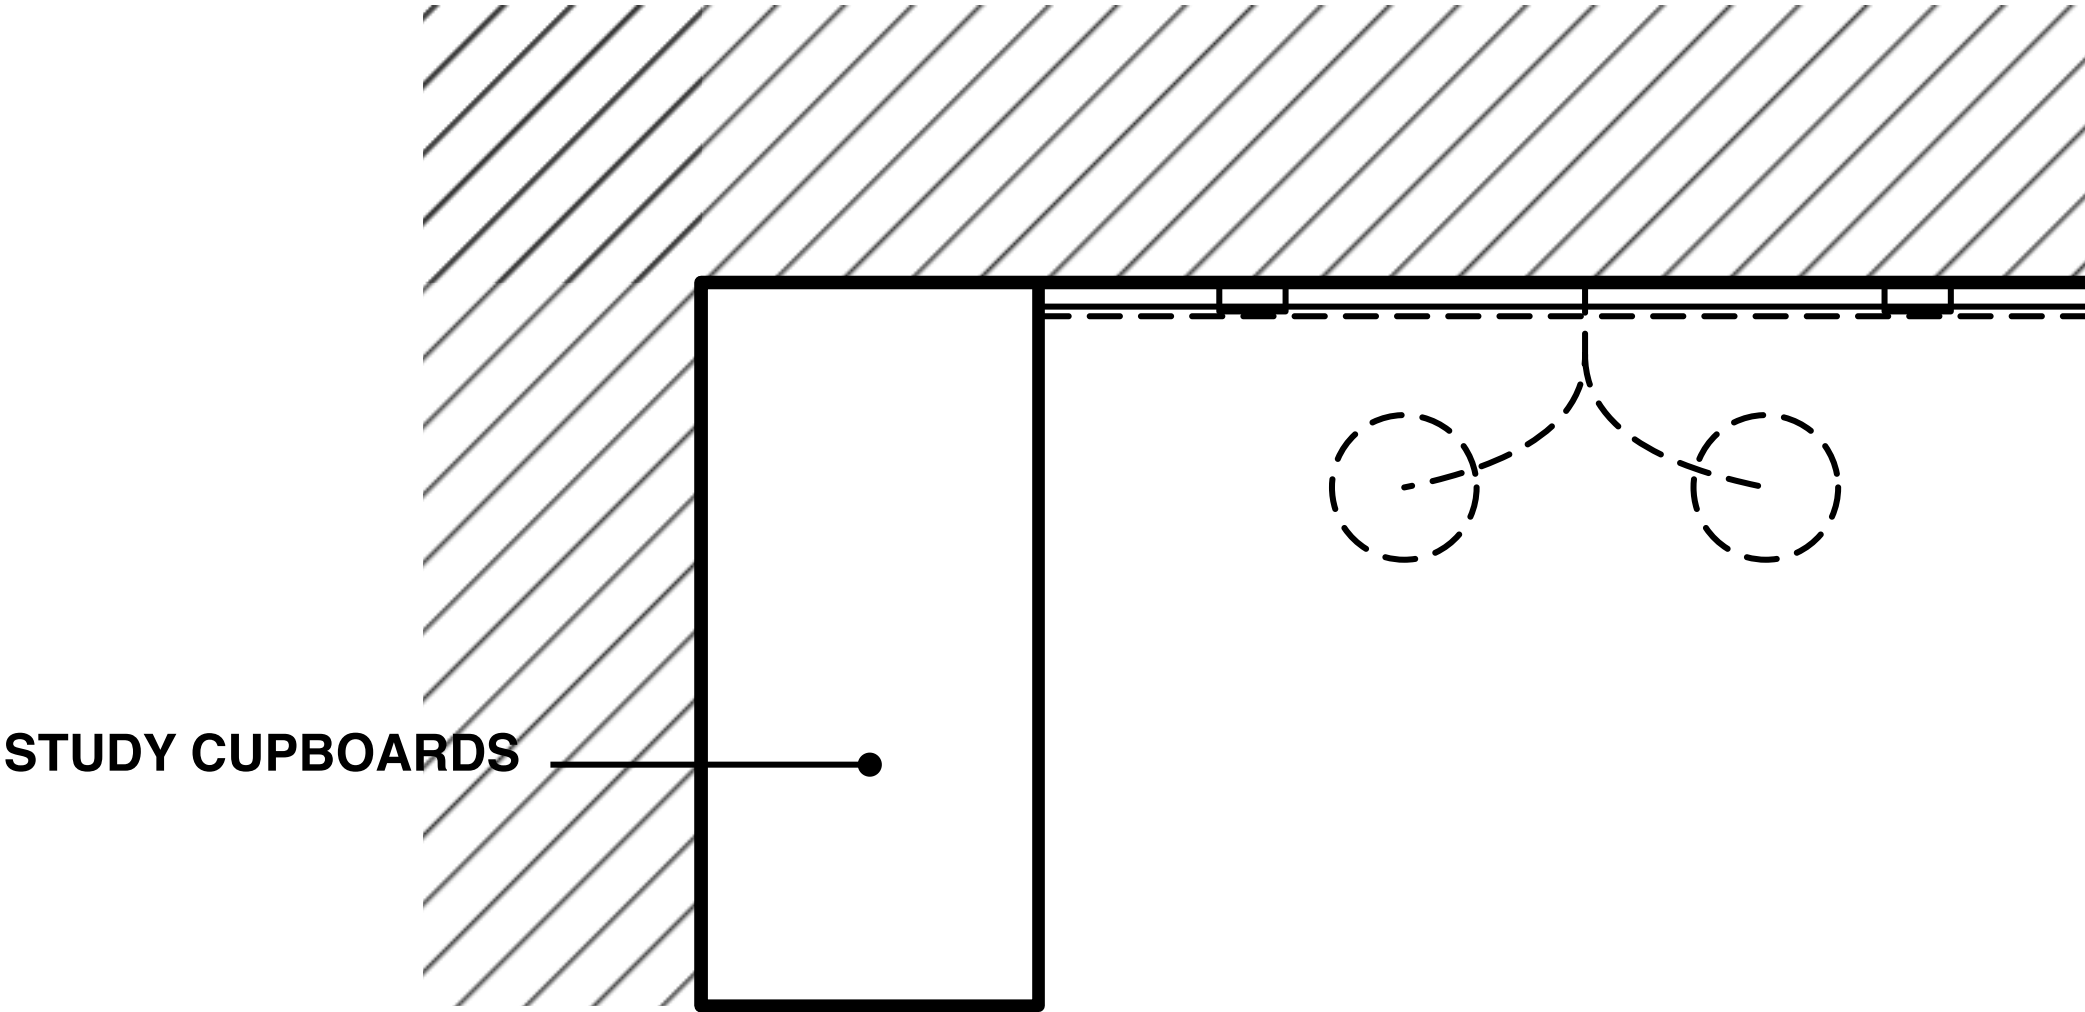

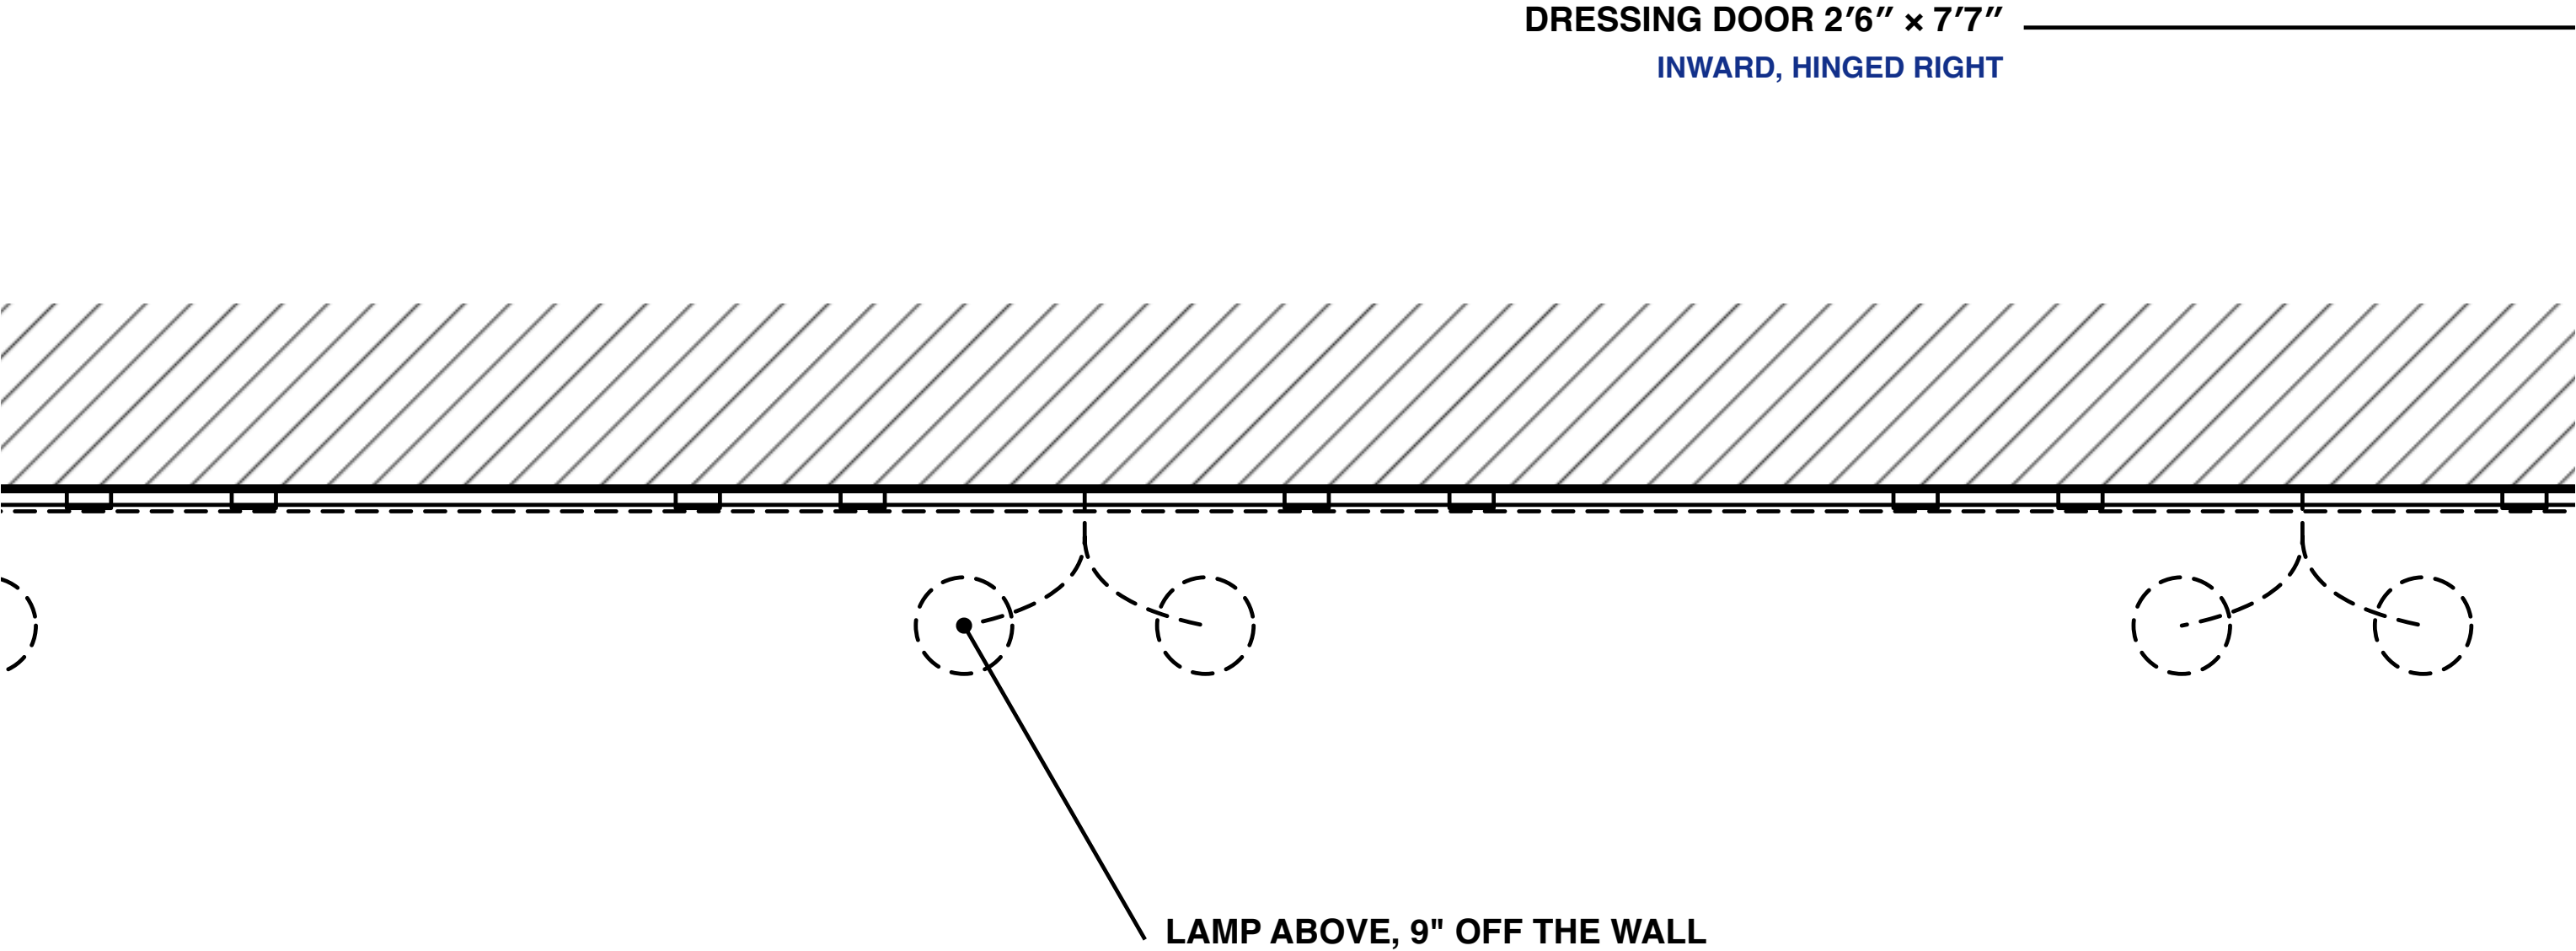

Aa note

All sizes in feet and inches. Enlarged — go by the written sizes, never measure the paper.

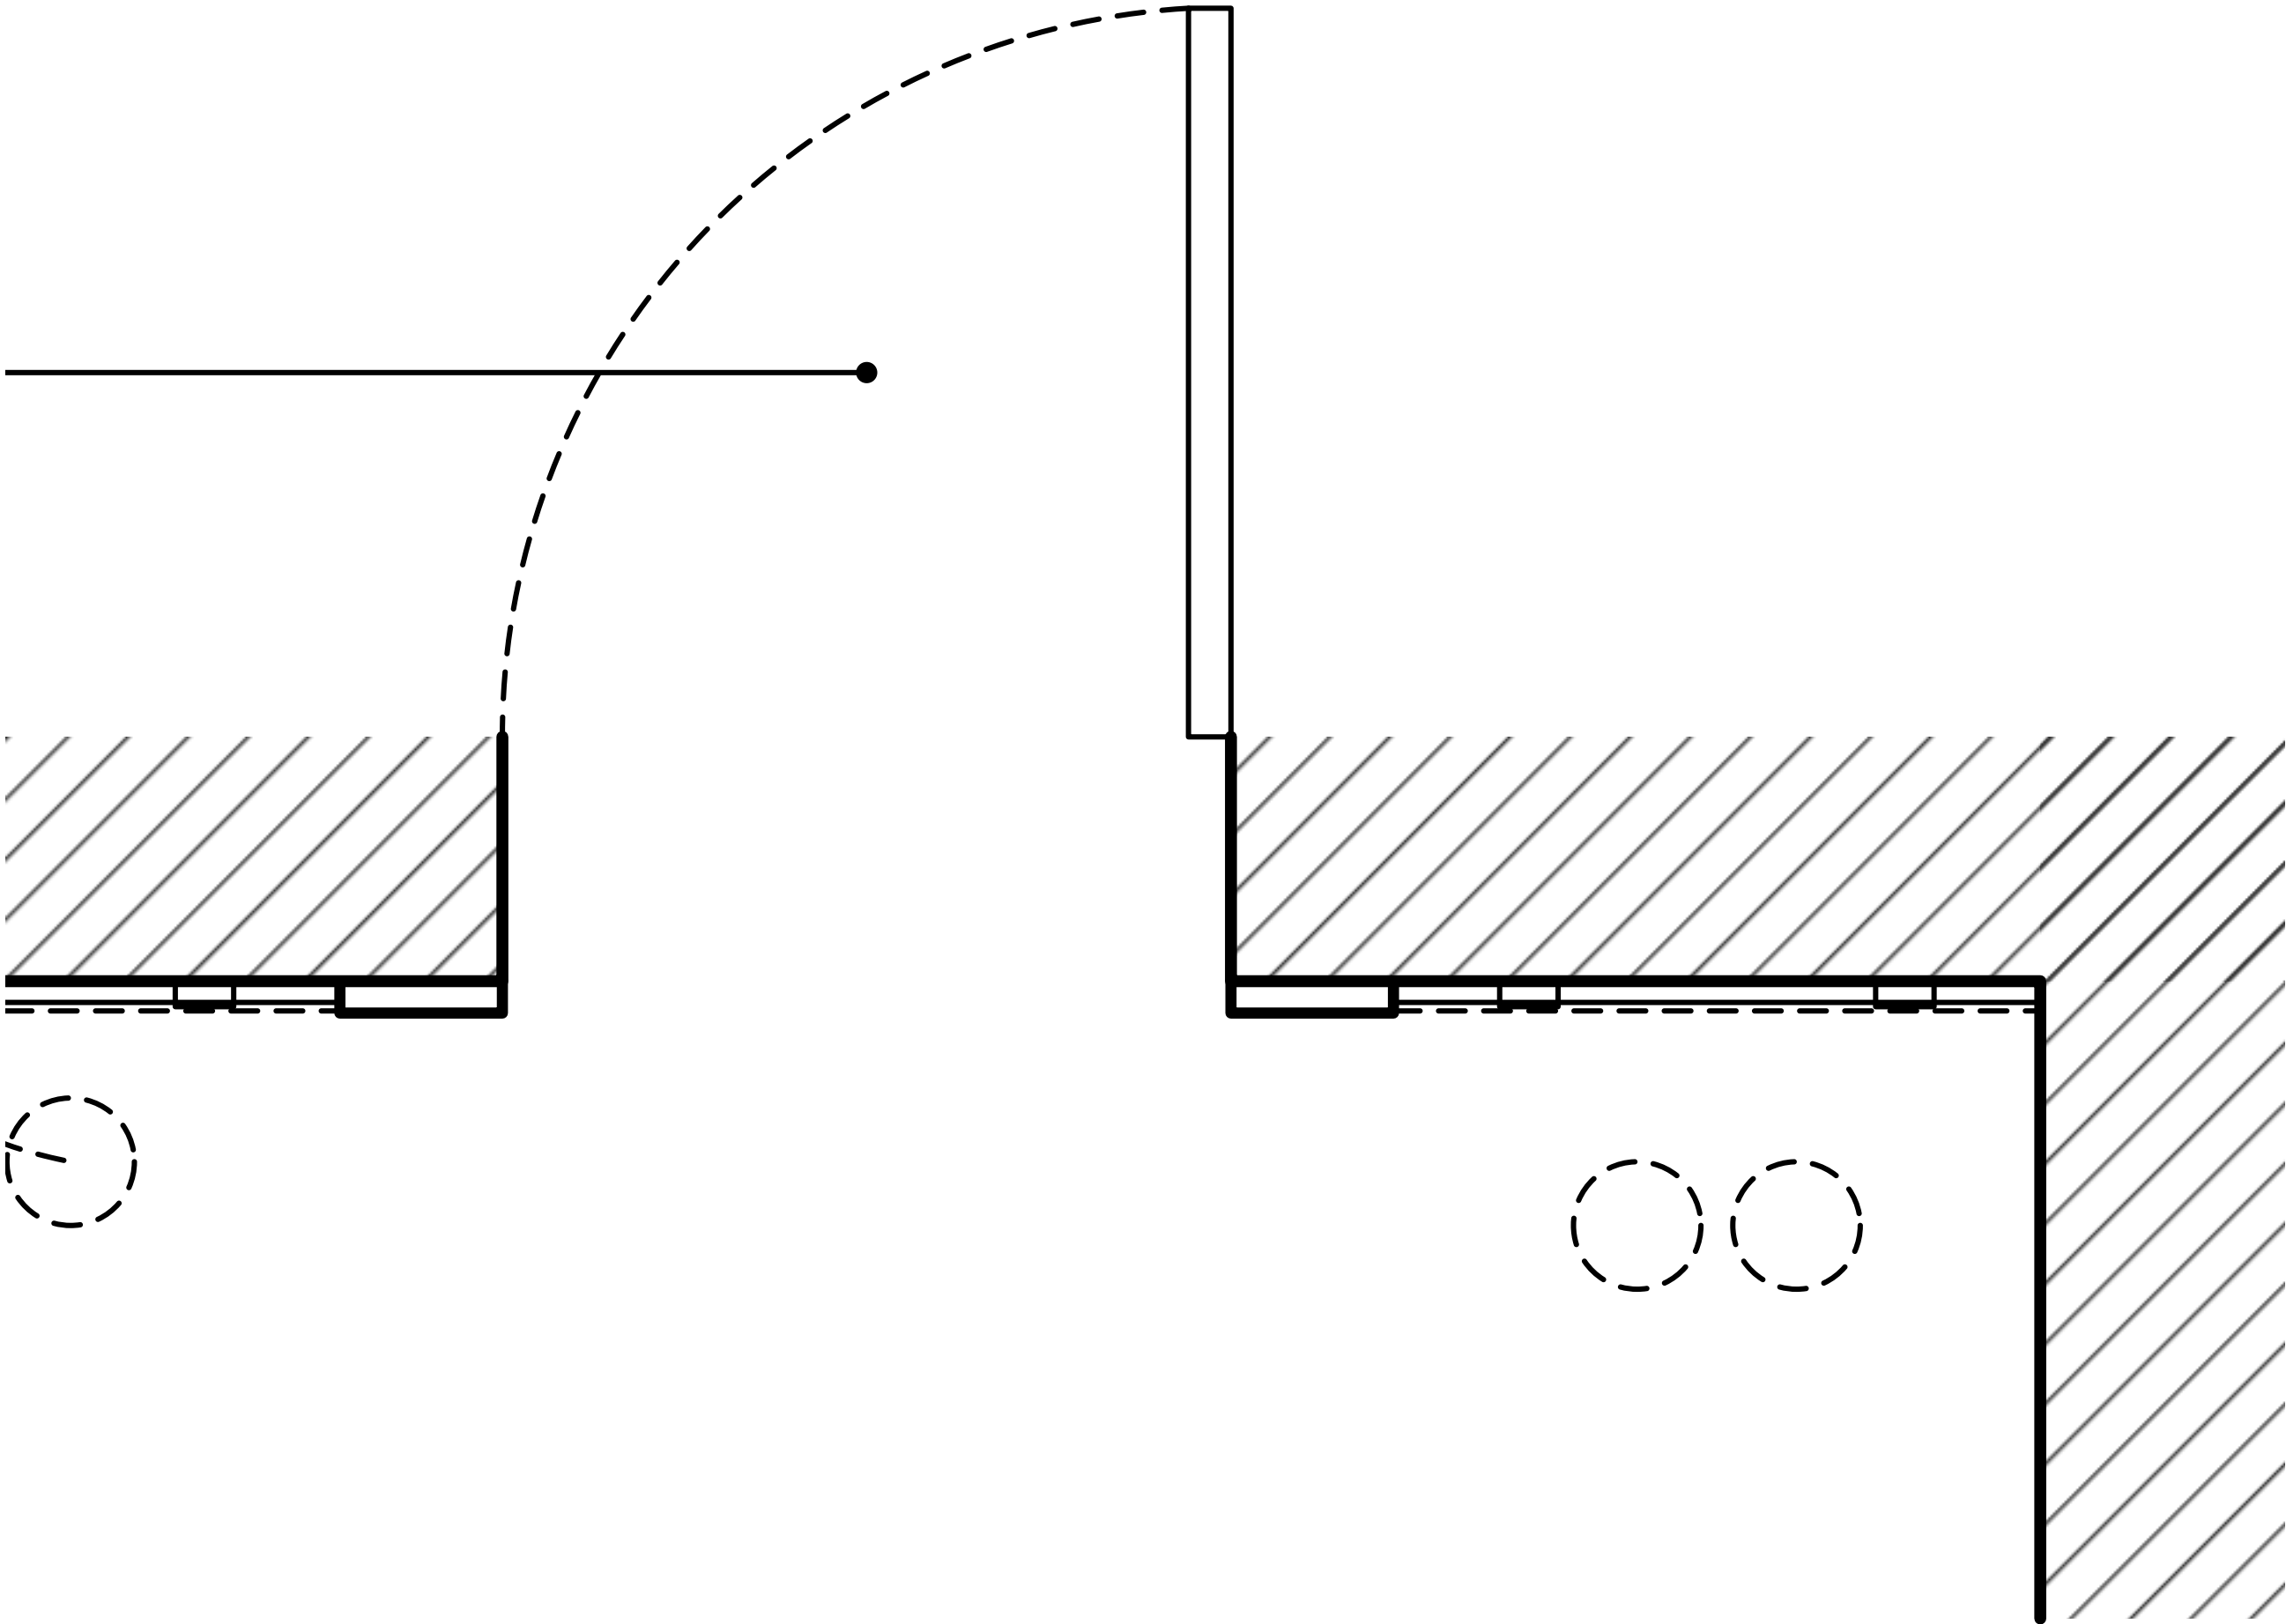

All sizes in feet and inches. Enlarged — go by the written sizes, never measure the paper.

NOTES

REVISION 18

Option C: 5 equal panels, lamps in 1, 3, 5 and the return.

One narrow panel on the wall past the door.

Moulding, rail and skirting painted the wall colour.

SELECTED after four schemes: the rail is the study counter

band carried round the corner, and it dies into the casing.

Skirting is white marble, 4 in, already laid.

Casing 2 in lining + 4 in moulding = 6 in, 3'-6" overall;

crown at 8 ft 8 in, and the tall panels stop on that

line, not the leaf head at 7 ft 7 in.


2 ft 4 in corner to frame, measured both sides; leaf 2 ft 3

in a 2 in frame. **OPEN:** that puts the frame 14 ft 0 from the

study corner, 6 in off the taped 13 ft 6. Retape that end.

1 · PANEL MOULDING


SECTION

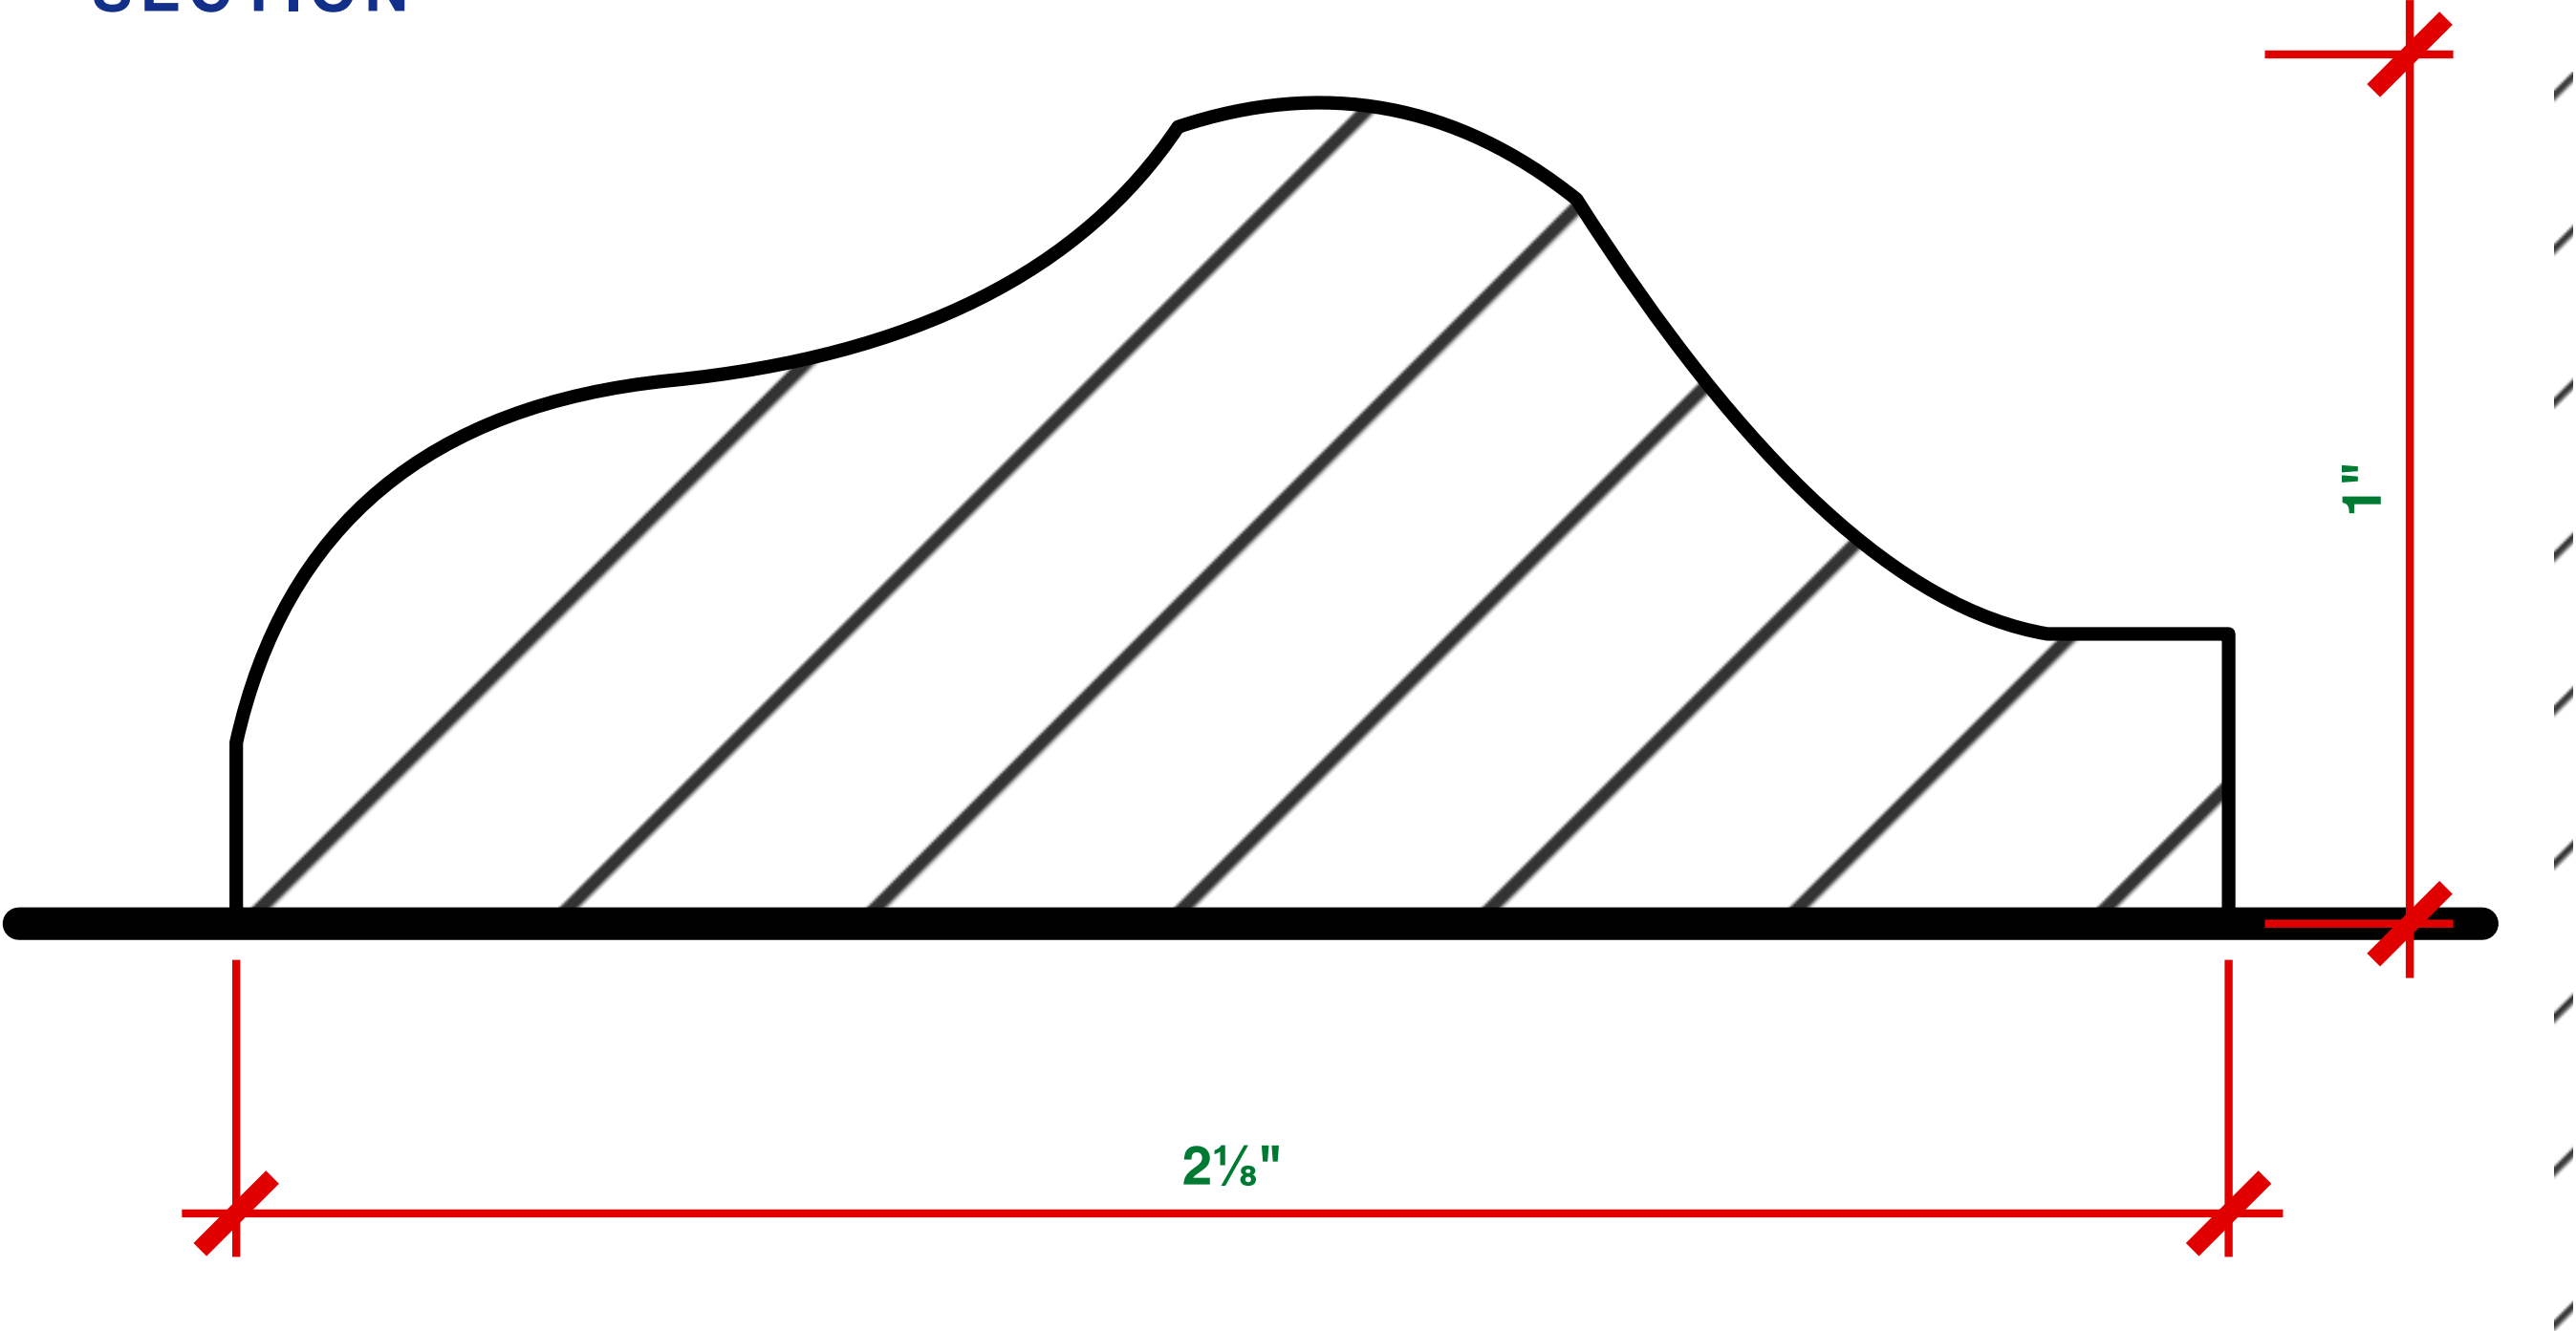

WALL FACE BELOW · MITRED CORNERS

2 · RAIL


SECTION

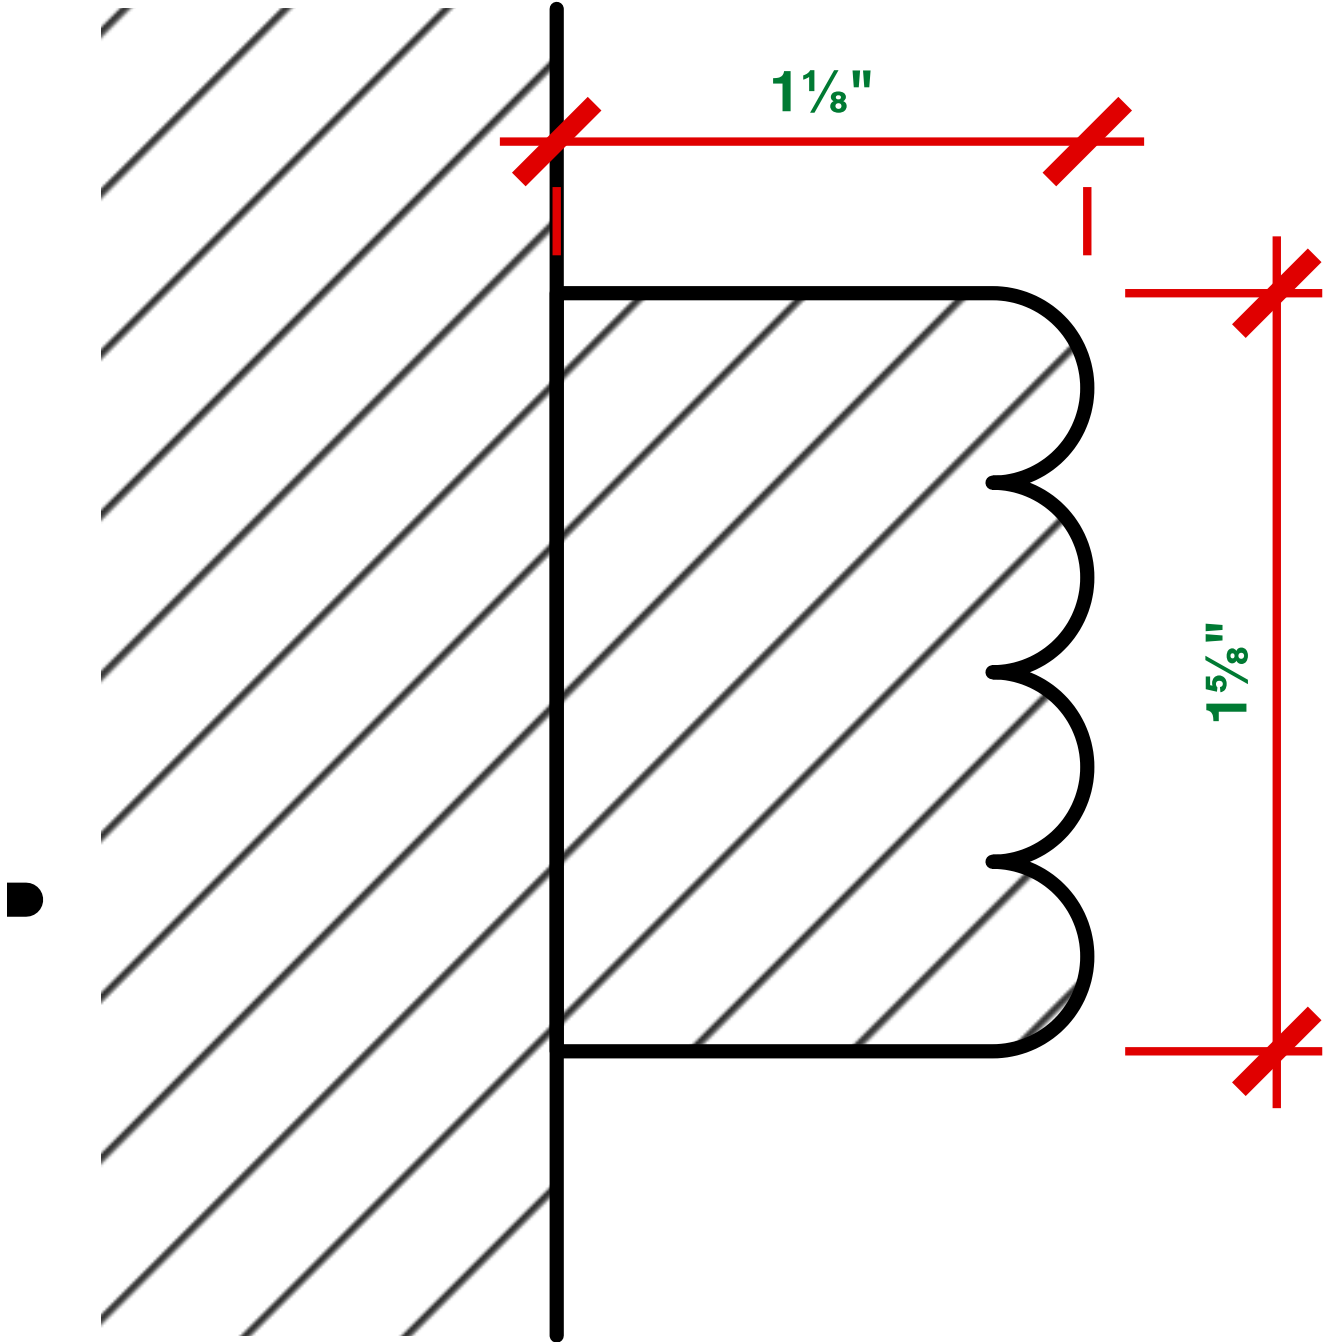

MATCHES THE COUNTER EDGE

3 · SKIRTING

MARBLE · SECTION

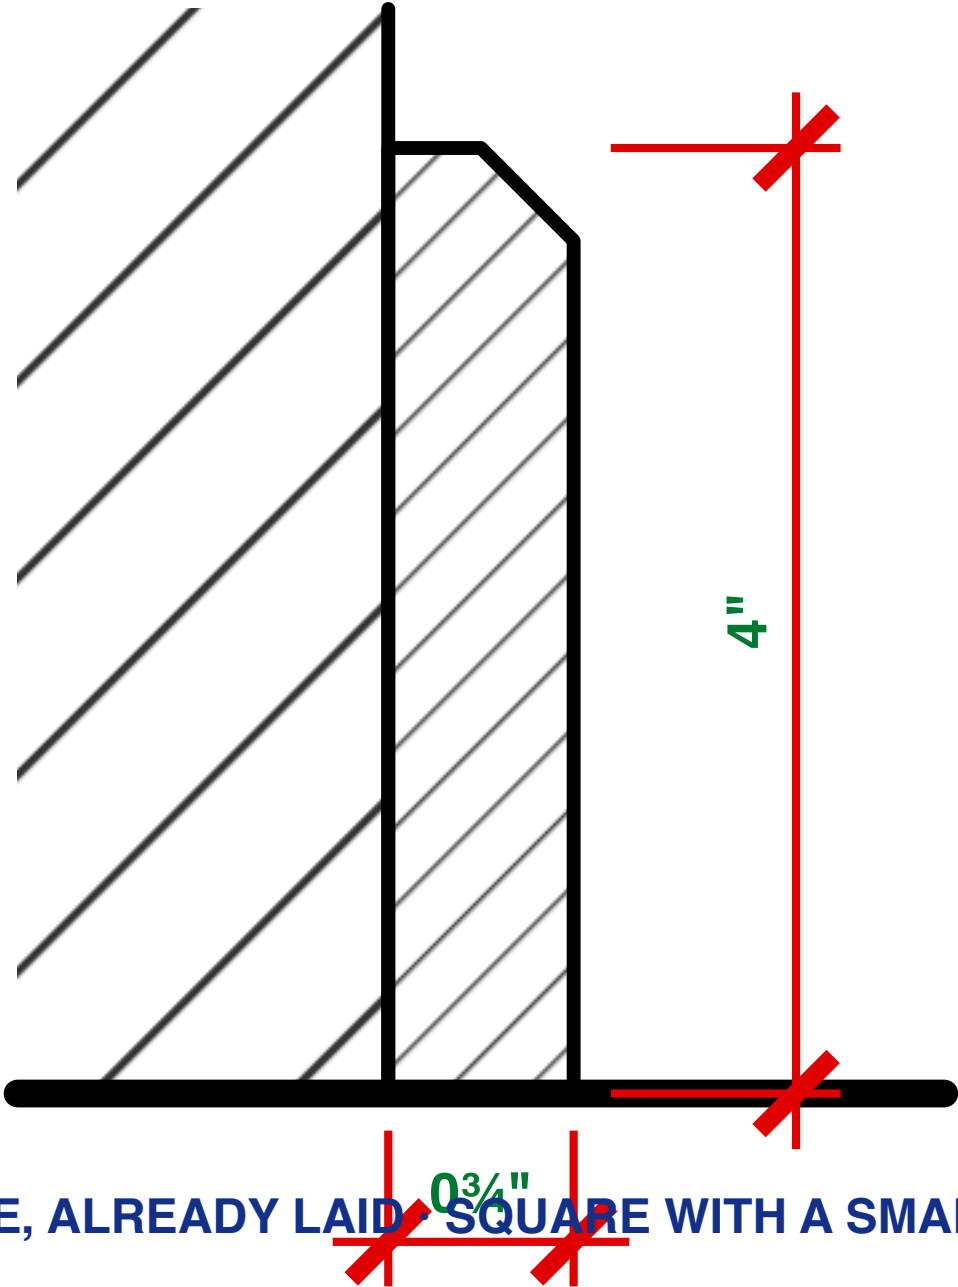

4 · WALL LAMP

ELEVATION · ×4

