


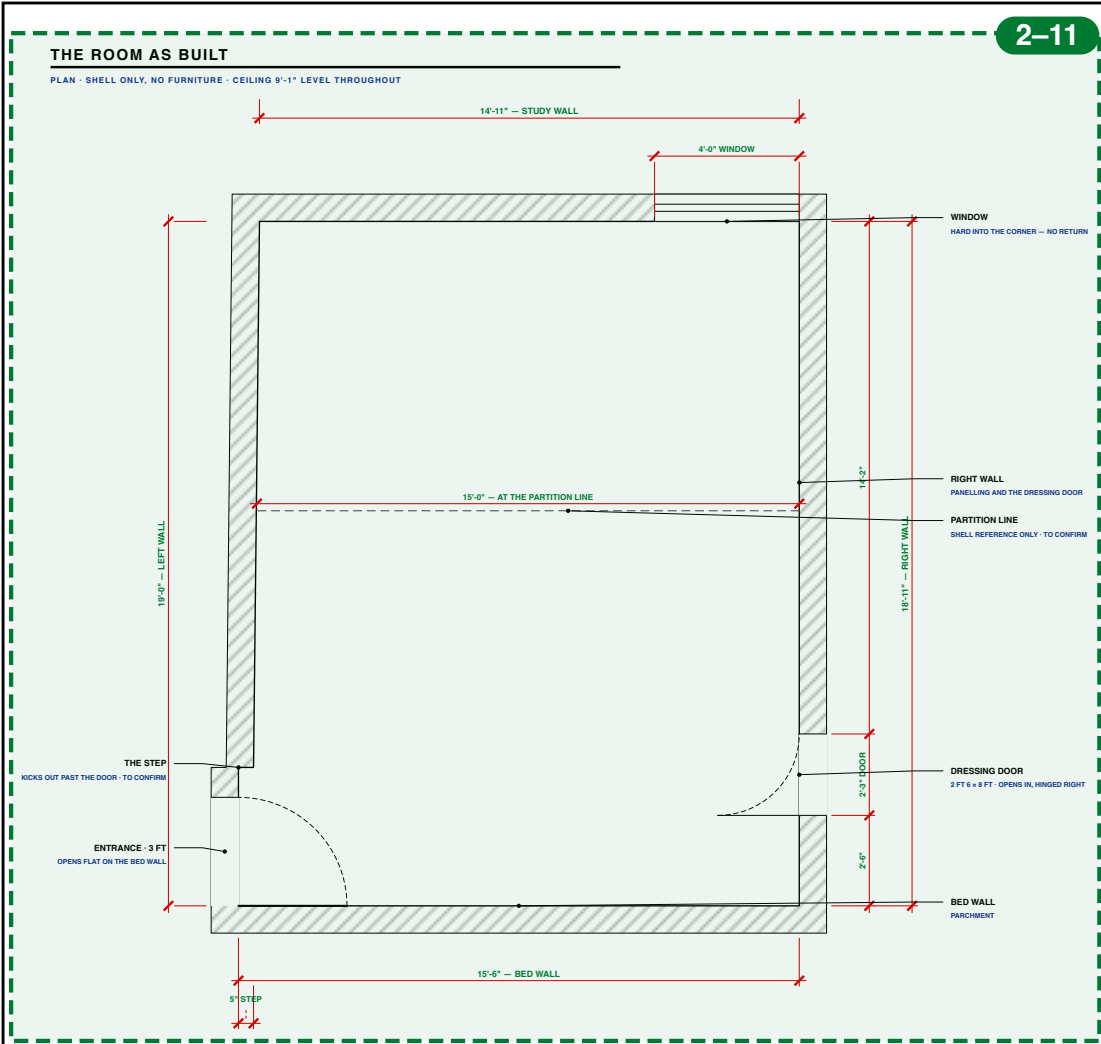

12-14

NOTES

REVISION 6

The room is not square. It widens about 2 in from the study wall to the bed wall — roughly half a degree.

Diagonals measured 24 ft 5 in and 23 ft 11 in.

Right wall — 13 ft 6 in to the door frame and 18 ft 11 in overall are drawn exactly; the 3 ft frame and 2 ft 4 in return do not both fit with a 2 in lining. See AST-DR-007.

The right wall is taken as the straight reference; the left wall carries the splay and the step.

Ceiling 9 ft 1 in, level throughout. The main room ceiling is plain, so the splay never shows from above.

Floor, marble border and skirting are laid. Skirting runs on three walls only: bed, left and right.

Every fitted piece to be built 0%–0¼" undersize and scribed on site to the wall it actually meets.

Furniture, partition and joinery are NOT shown.

Bathroom and dressing lie beyond the right wall — to come.

A STUDY IN TEAK

Particulars of the room


THE ROOM AS BUILT

Shell plan · measured on site

SCALE	DATE
1:40 @ A3	19.09.2026
REV	DWG
6 — the partition line at 11 ft from the bed wall, 8 ft from the study wall	AST-DR-000


THE ROOM AS BUILT


PLAN · SHELL ONLY, NO FURNITURE · CEILING 9'-1" LEVEL THROUGHOUT

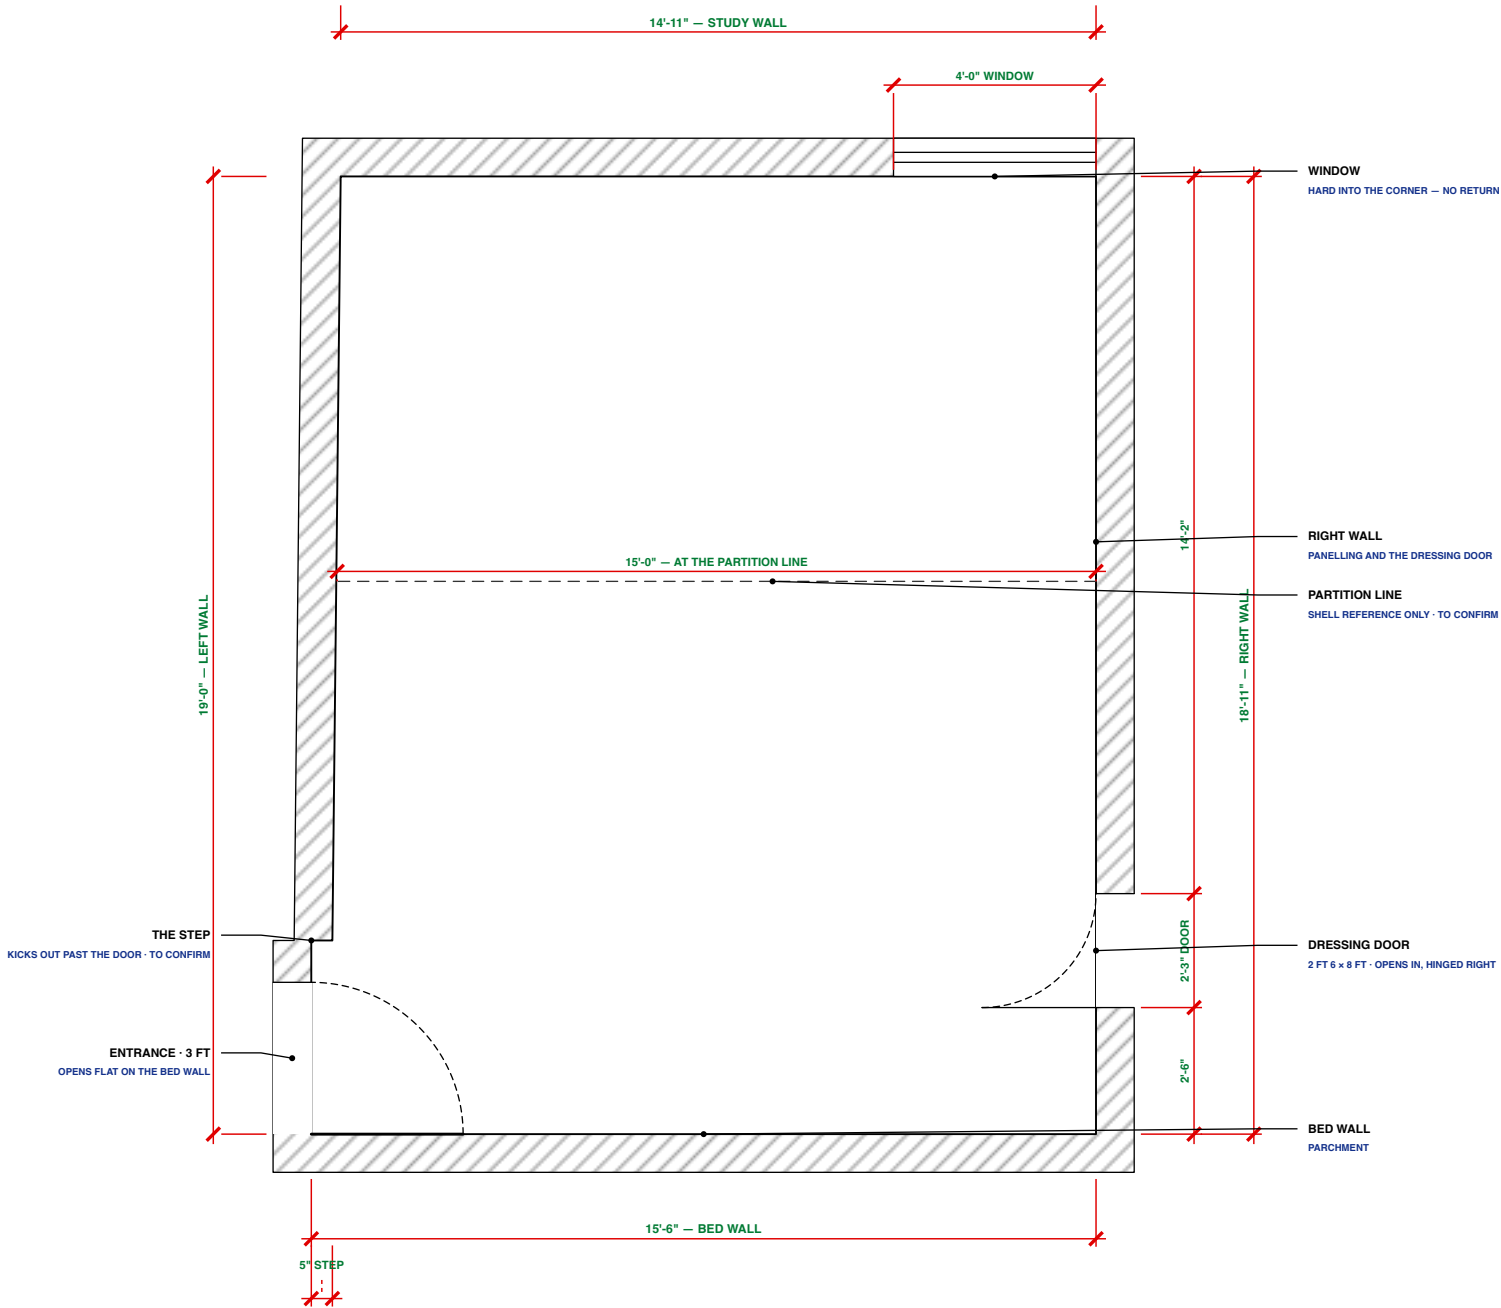


THE ROOM AS BUILT

PLAN · SHELL ONLY, NO FURNITURE · CEILING 9'-1" LEVEL THROUGHOUT

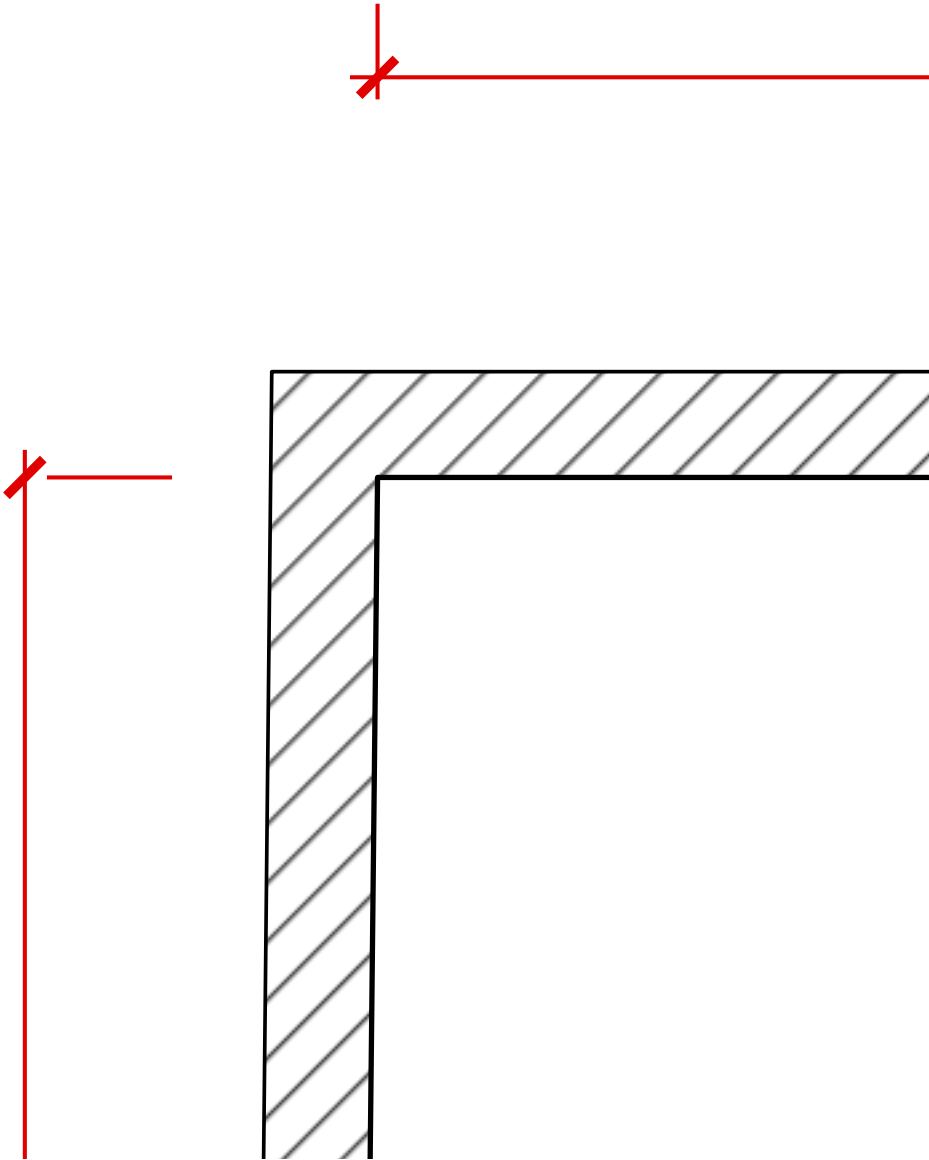


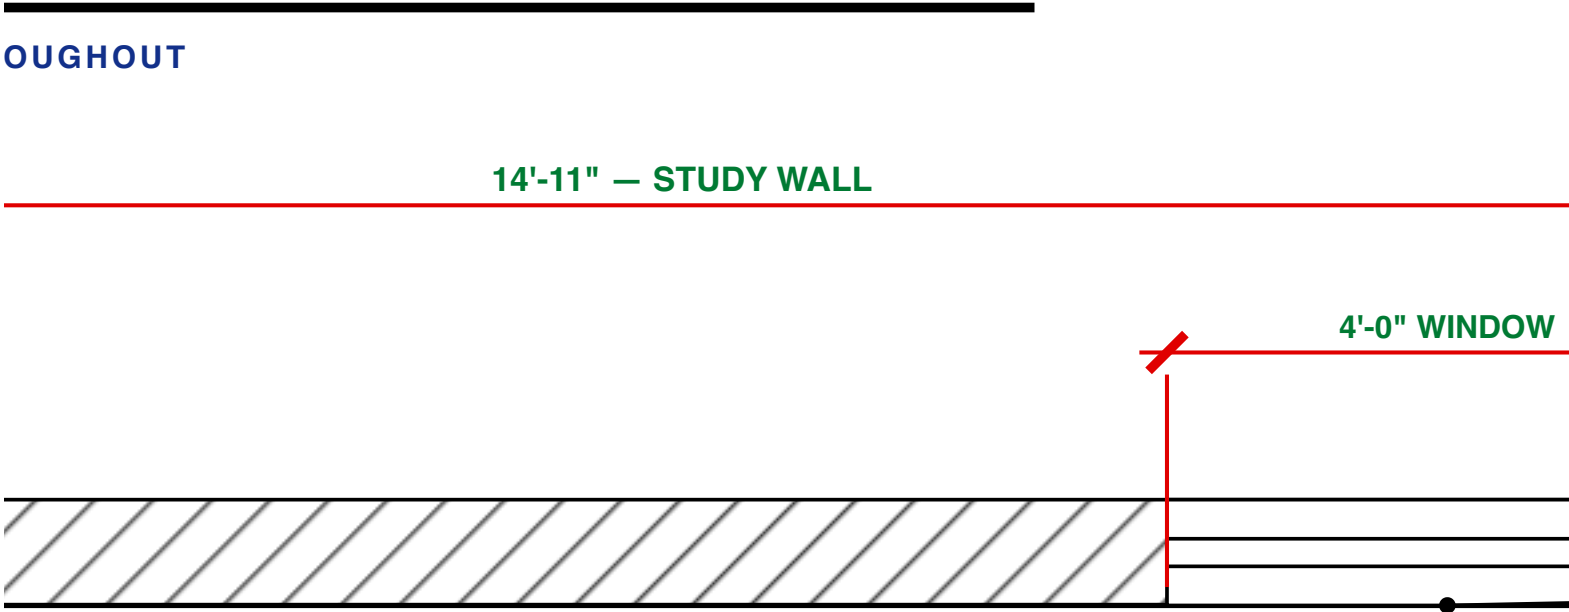

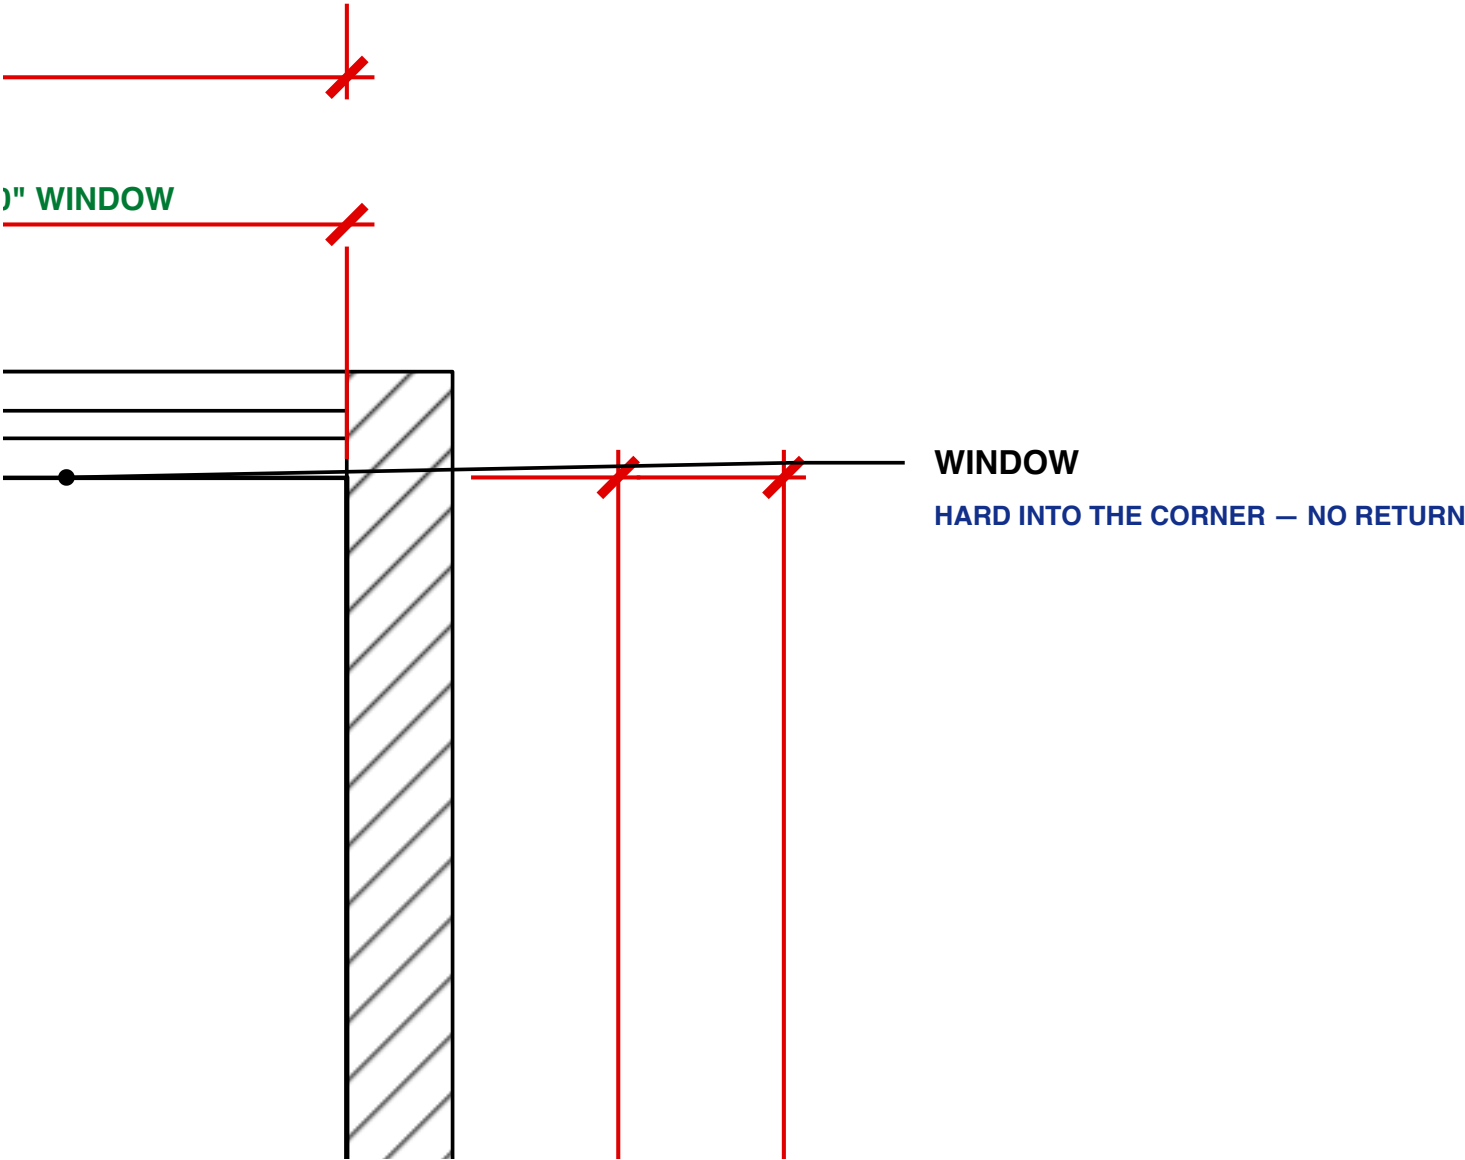

19'-0" — LEFT WALL



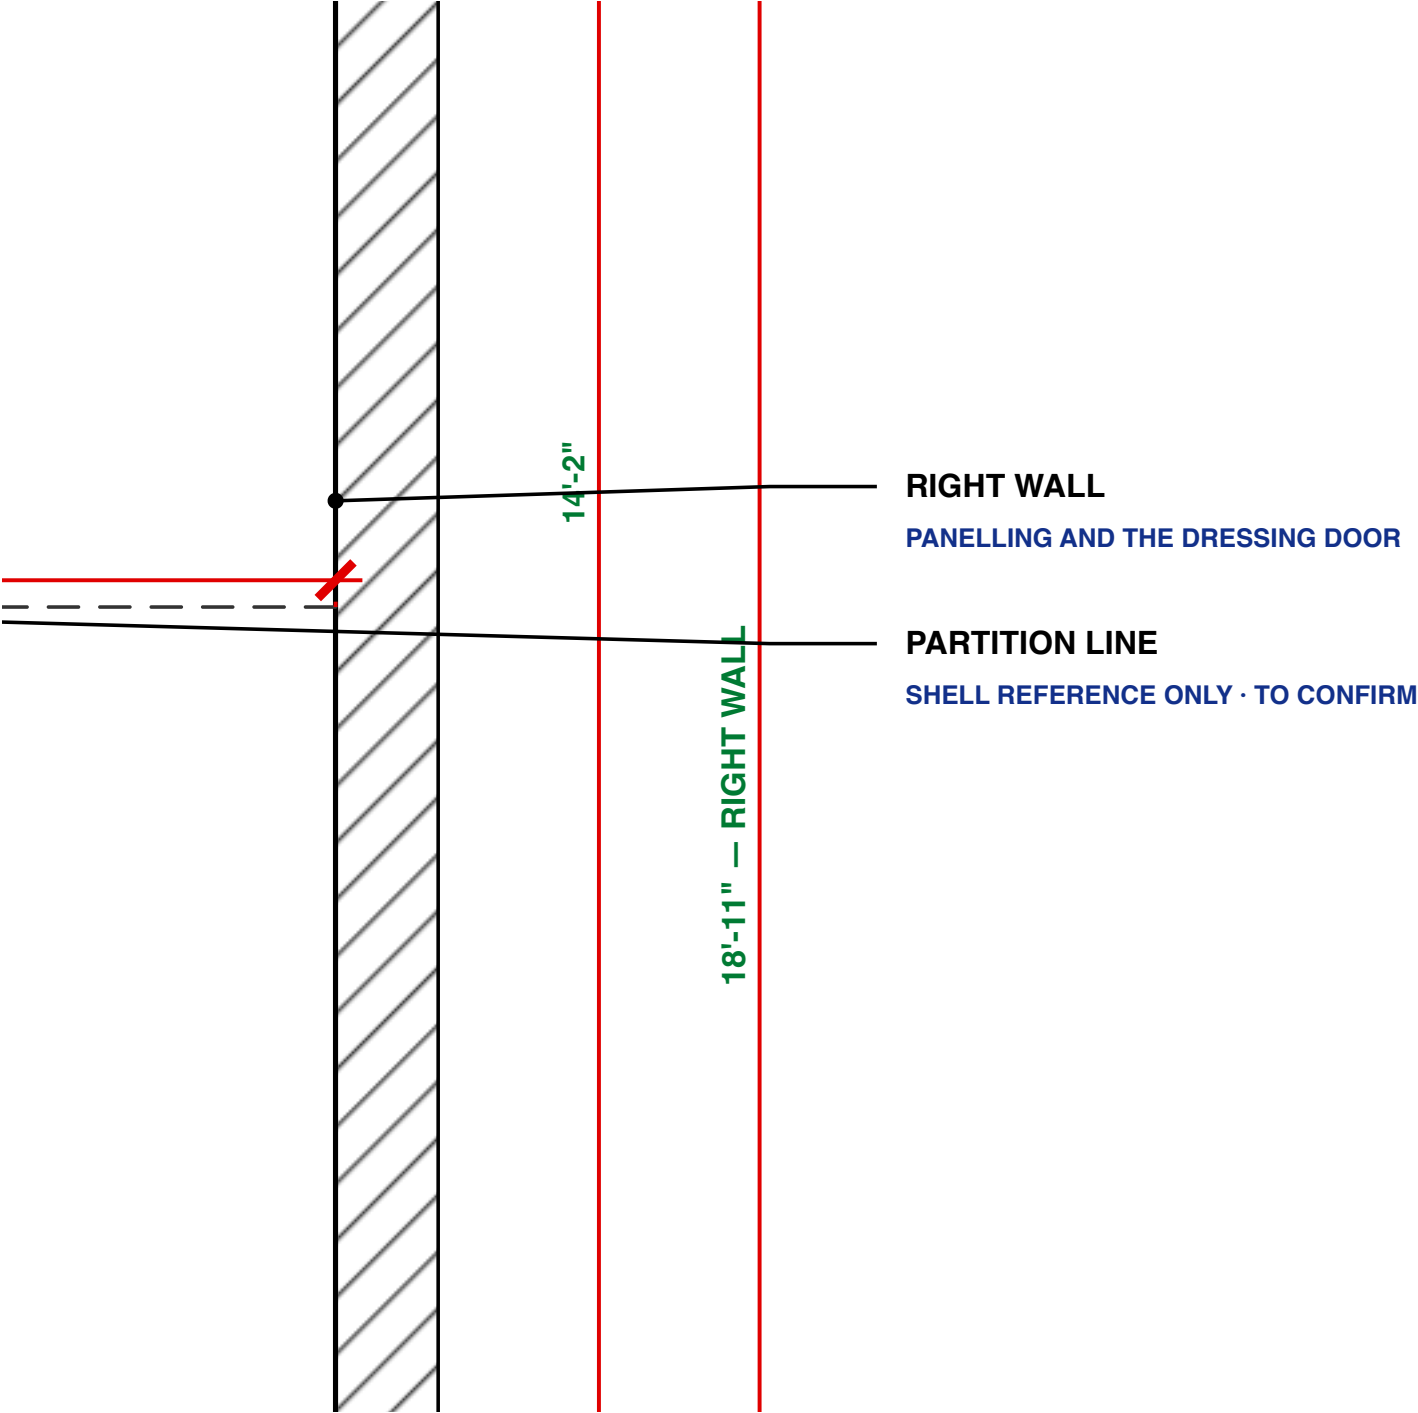

All sizes in feet and inches. Enlarged — go by the written sizes, never measure the paper.





THE STEP

ENTRANCE · 3 FT
OPENS FLAT ON THE BED WALL

ENTRANCE · 3 FT

5" STEP

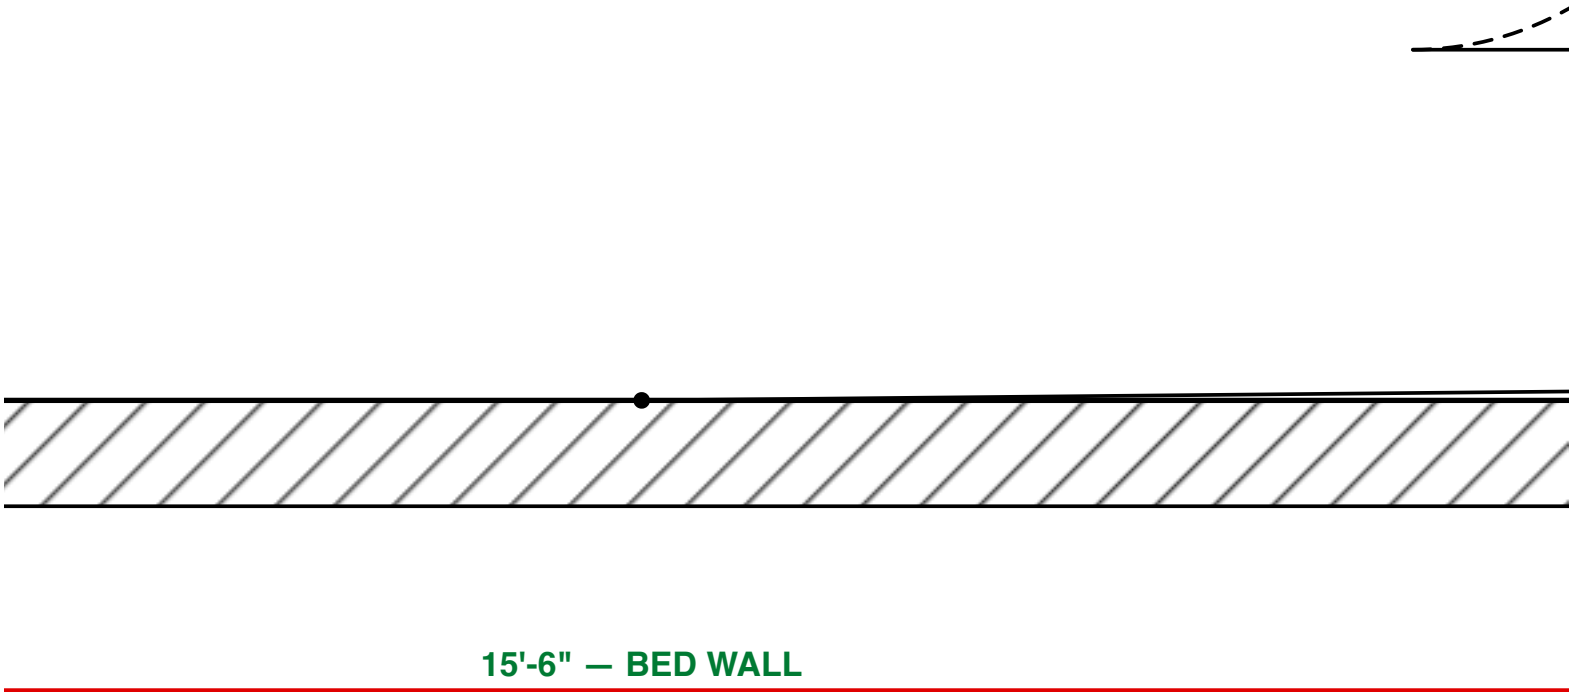

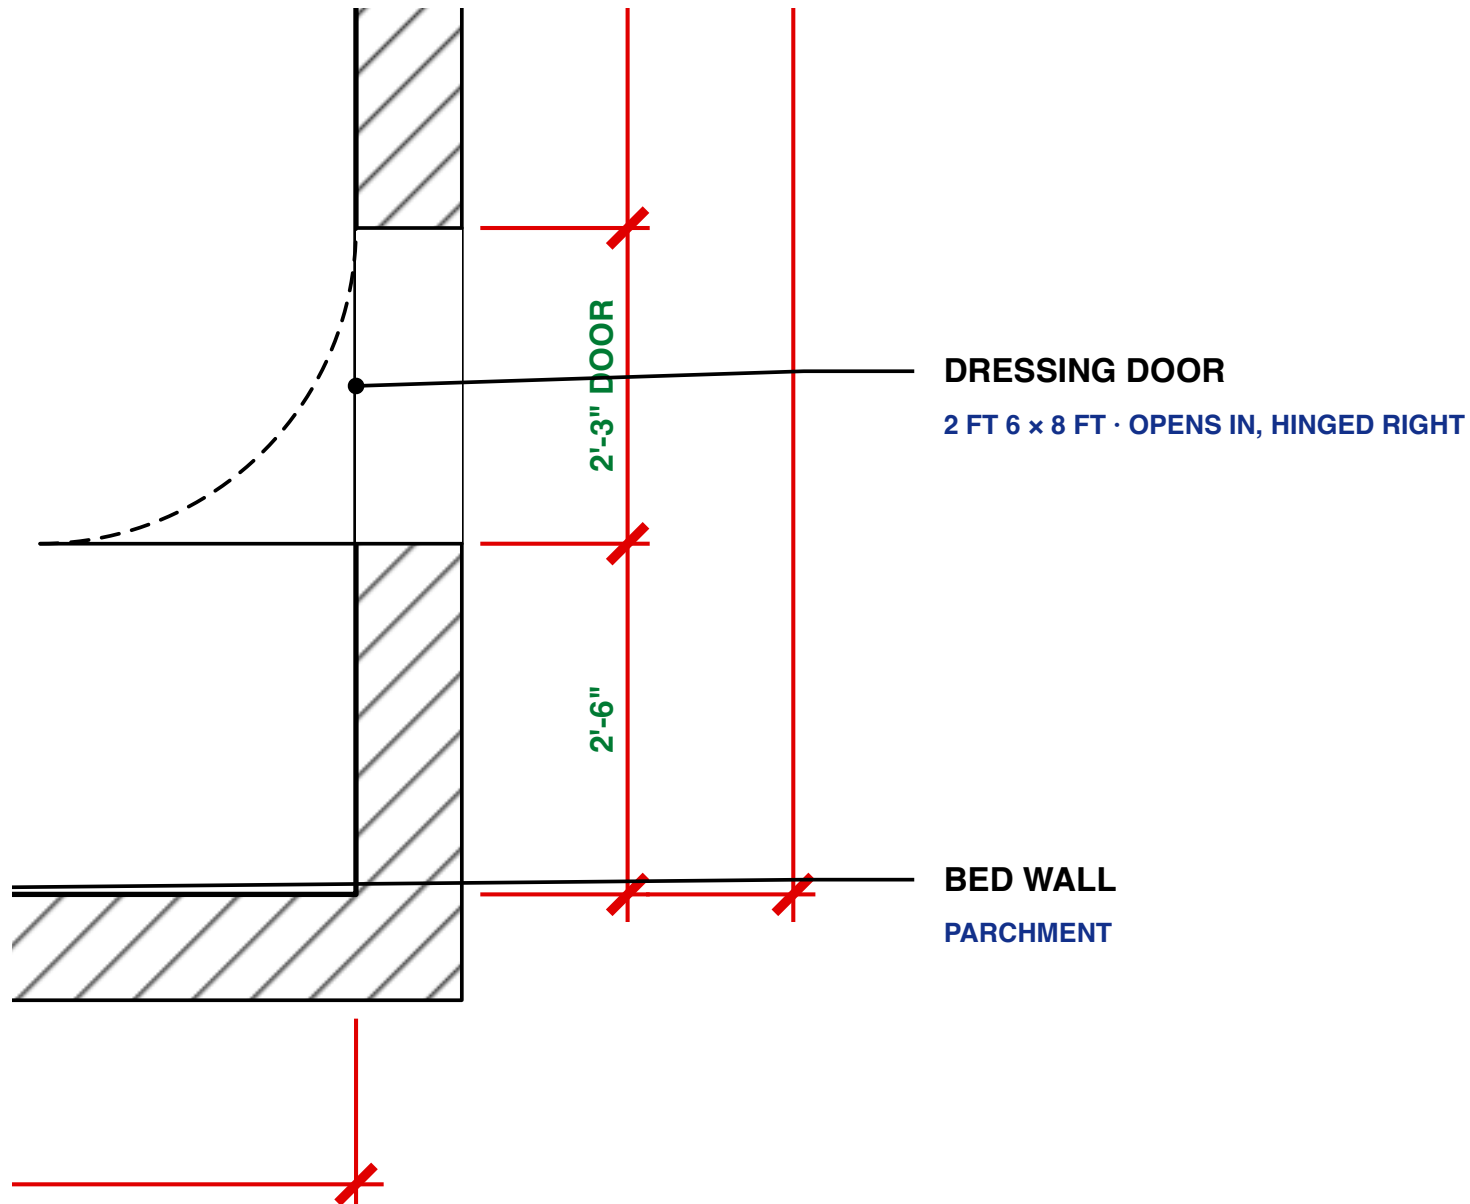

NOTES

REVISION 6

The room is not square. It widens about 2 in from the study wall to the bed wall — roughly half a degree.

Diagonals measured 24 ft 5 in and 23 ft 11 in.

Right wall — 13 ft 6 in to the door frame and 18 ft 11 in overall are drawn exactly; the 3 ft frame and 2 ft 4 in return do not both fit with a 2 in lining. See AST-DR-007.

The right wall is taken as the straight reference; the left wall carries the splay and the step.

Ceiling 9 ft 1 in, level throughout. The main room ceiling is plain, so the splay never shows from above.

Floor, marble border and skirting are laid. Skirting runs on three walls only: bed, left and right.

Every fitted piece to be built 0⁵/₈"–0³/₄" undersize and scribed on site to the wall it actually meets.

Furniture, partition and joinery are NOT shown.

Bathroom and dressing lie beyond the right wall — to come.

NOTES

REVISION 6

The room is not square. It widens about 2 in from the study wall to the bed wall — roughly half a degree.

Diagonals measured 24 ft 5 in and 23 ft 11 in.

Right wall — 13 ft 6 in to the door frame and 18 ft 11 in overall are drawn exactly; the 3 ft frame and 2 ft 4 in return do not both fit with a 2 in lining. See AST-DR-007.

The right wall is taken as the straight reference; the left wall carries the splay and the step.

The right wall is taken as the straight reference; the left wall carries the splay and the step.

Ceiling 9 ft 1 in, level throughout. The main room ceiling is plain, so the splay never shows from above.

Floor, marble border and skirting are laid. Skirting runs on three walls only: bed, left and right.

Every fitted piece to be built $0\frac{5}{8}$ "– $0\frac{3}{4}$ " undersize and scribed on site to the wall it actually meets.

Furniture, partition and joinery are NOT shown.

Bathroom and dressing lie beyond the right wall — to come.