

DRESSING DOOR




D2 · 2 FT 6 · THE CARVED HEAD

MAIN AND BATHROOM

D1 3 FT · D3 2 FT 6 · PLAIN CASING


1 · THE HEAD

DRESSING DOOR · LEFT END · LINING, MOULDING, SCALLOPS, CROWN

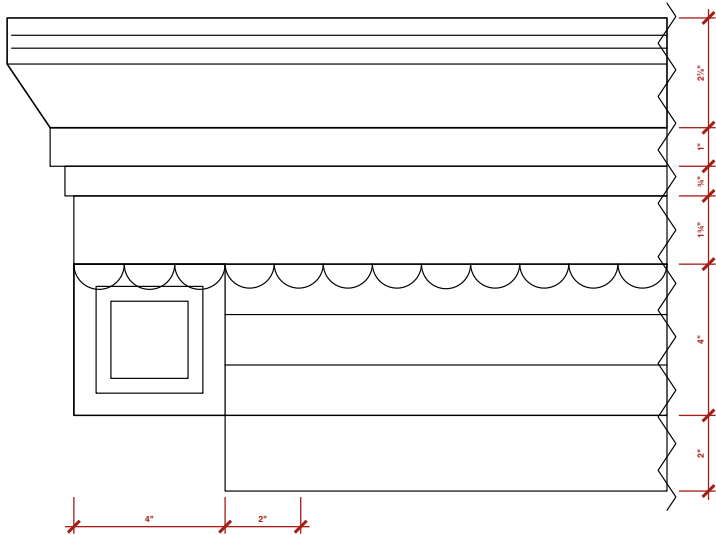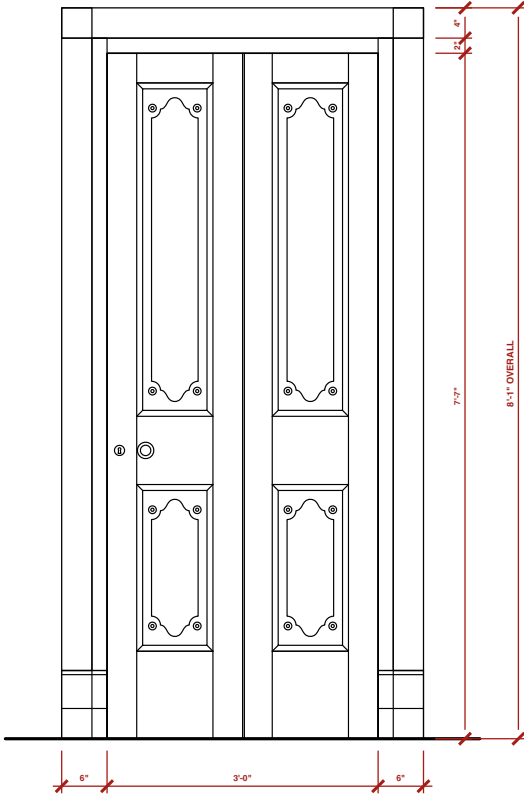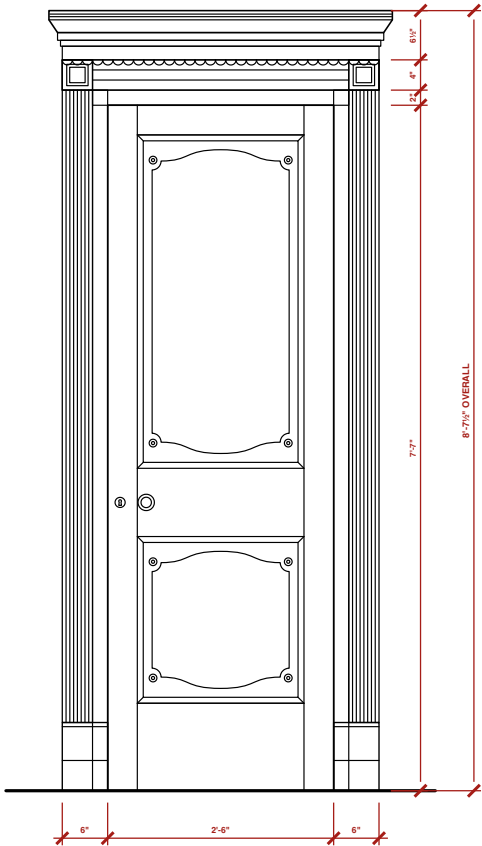

2 · SECTION

THROUGH THE HEAD

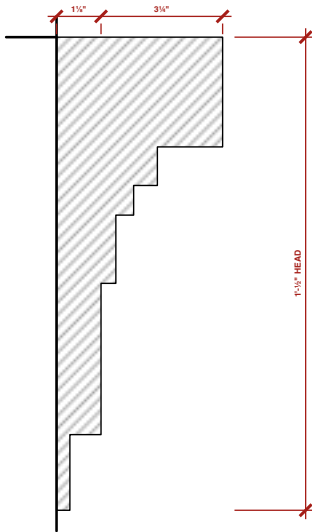


3 · JAMB

SECTION · 6 IN ON THE FACE



4 · PLINTH

AT THE FOOT

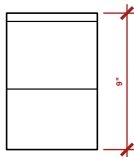

NOTES

REVISION 8

The lining is 2 in on the face. The moulding lays 4 in outside it, all round — so the jambs are 6 in wide, and over the opening the moulding head sits 6 in ABOVE the leaf, not on top of it.

The jambs are reeded. Across the head the moulding is STEPPED, not reeded — the reference has no reeding there.

A plinth block takes each jamb down over the marble skirting.

RELIEF

DATUM 0 = FACE OF THE PLASTER · LINING AND MOULDING ARE COMMON TO ALL THREE DOORS · THE REST IS THE DRESSING DOOR'S CARVED HEAD

Lining, 2 in on the face

Moulding, 4 in, reeded

Reed grooves in the moulding face

Corner block, flush with the moulding

Its sunk panel, two steps

1/4" OUT

1 1/2" OUT

3 IN

1 1/2" OUT

0 1/4" AND 0 1/2" IN

Scallop course

Scallops, cut back from its face

Small mouldings, over the scallops

Crown, the widest member

Plinth block, so the moulding dies on it

1 1/2" OUT

5 IN

2" AND 2 1/2" OUT

4 1/2" OUT

1 1/2" OUT

A STUDY IN TEAK

Particulars of the room

DOOR CASINGS

Carved head — dressing only · Plain elsewhere · Sections

SCALE

AS NOTED @ A3

DATE

19.09.2026

REV

8 — carved head: dressing door only

DWG

AST-DR-011

PROJECT

A Study in Teak — Door Casings

SHEET

General arrangement — the whole sheet

each view follows at its own scale, pages 2 to 8

SCALE

NTS

DATE

19.09.2026

REV



8

DRAWING

AST-DR-011 · 1 of 8

DRESSING DOOR

SCALE 1:15 @ A3 · D2 · 2 FT 6 · THE CARVED HEAD

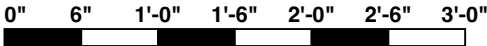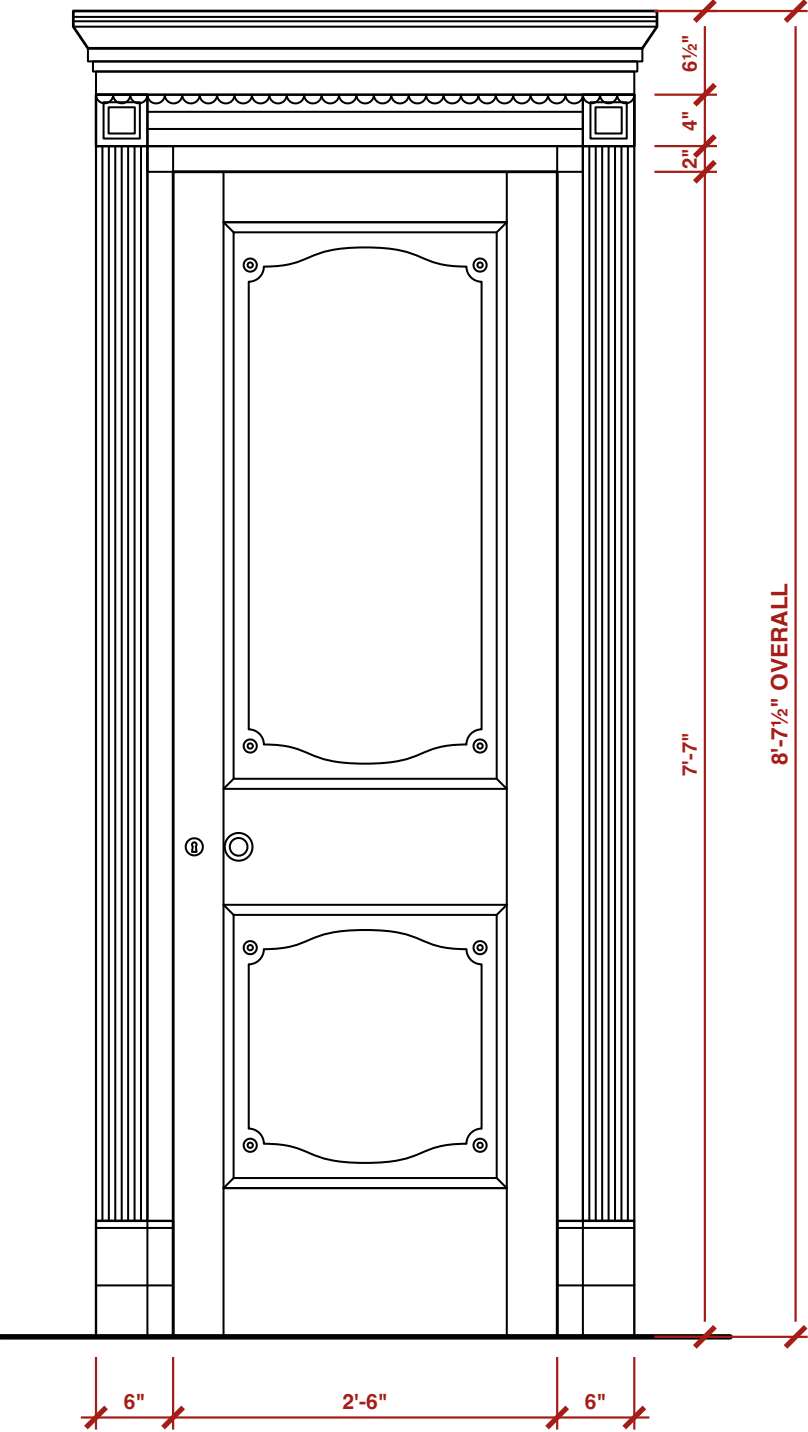

PROJECT
A Study in Teak — Door Casings

SHEET
Dressing door
Carved head — dressing only · Plain elsewhere · Sections

SCALE
1:15 @ A3



DATE
19.09.2026

REV
8

DRAWING
AST-DR-011 · 2 of 8

1 · THE HEAD



SCALE 1:3 (4" = 1'-0") @ A3 · DRESSING DOOR · LEFT END · LINING, MOULDING, SCALLOPS, CROWN

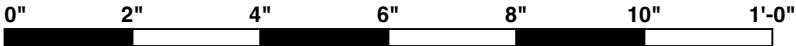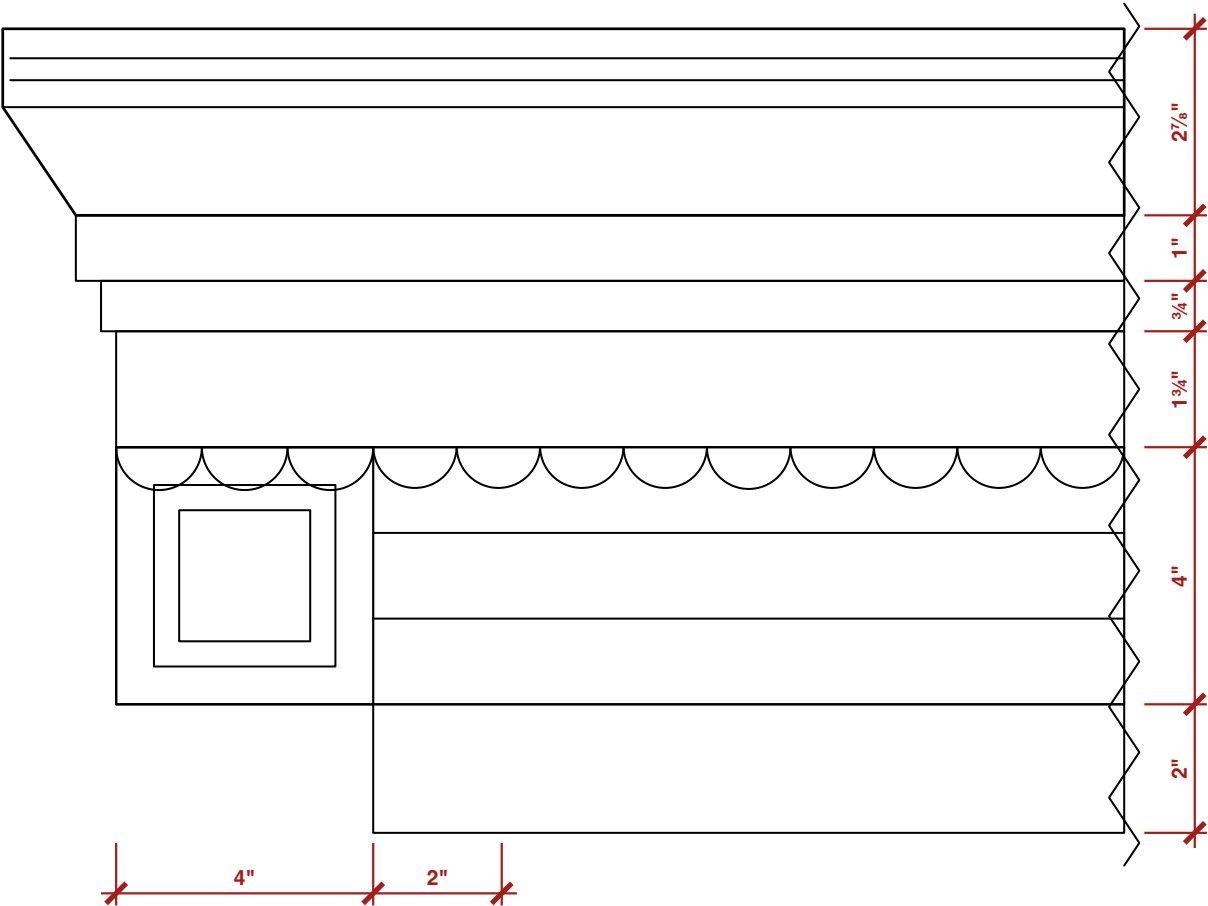

PROJECT	SHEET	SCALE	DATE	REV	DRAWING
A Study in Teak — Door Casings	1 · the head Carved head — dressing only · Plain elsewhere · Sections	1:3 @ A3	19.09.2026	8	AST-DR-011 · 3 of 8

2 · SECTION

SCALE 1:3 (4" = 1'-0") @ A3 · THROUGH THE HEA

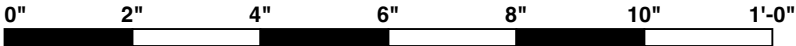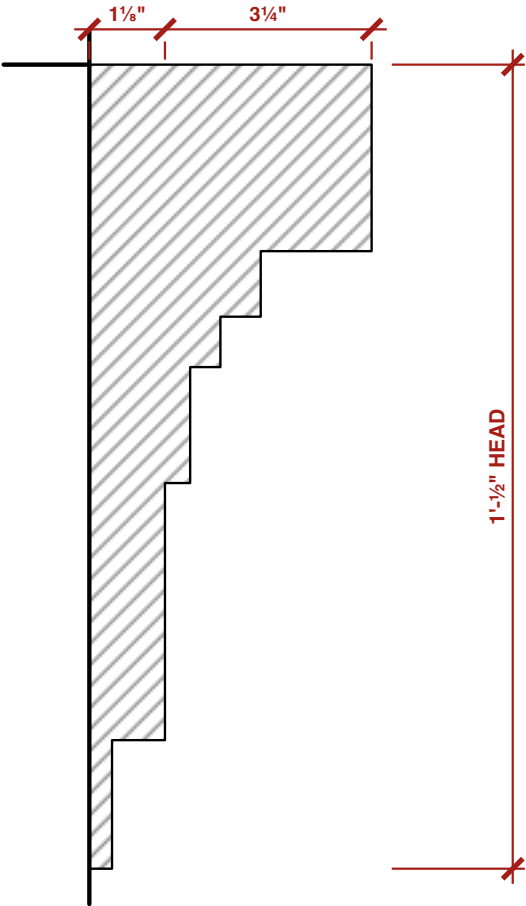

PROJECT
A Study in Teak — Door Casings

SHEET
2 · section
Carved head — dressing only · Plain elsewhere · Sections

SCALE
1:3 @ A3



DATE
19.09.2026

REV
8

DRAWING
AST-DR-011 · 4 of 8

3 · JAMB

SCALE 1:2 (6" = 1'-0") @ A3 · SECTION · 6 IN ON THE FAC

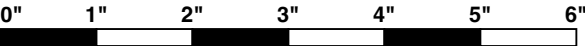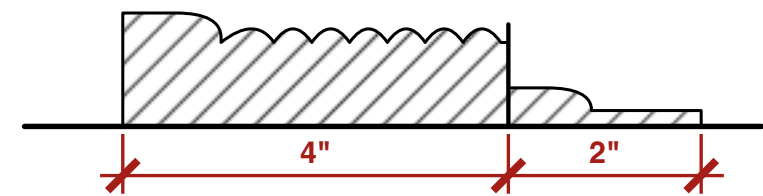

PROJECT
A Study in Teak — Door Casings

SHEET
3 · jamb
Carved head — dressing only · Plain elsewhere · Sections

SCALE
1:2 @ A3

DATE
19.09.2026

REV
8

DRAWING
AST-DR-011 · 5 of 8

NOTES

REVISION 8

The lining is 2 in on the face. The moulding lays 4 in outside it,
all round — so the jambs are 6 in wide, and over the opening the
moulding head sits 6 in ABOVE the leaf, not on top of it.



The jambs are reeded. Across the head the moulding is STEPPED,
not reeded — the reference has no reeding there.

A plinth block takes each jamb down over the marble skirting.

PROJECT A Study in Teak — Door Casings	SHEET Notes Carved head — dressing only · Plain elsewhere · Sections	SCALE NTS	DATE 19.09.2026	REV 8	DRAWING AST-DR-011 · 6 of 8
---	--	--------------	--------------------	----------	--------------------------------

4 · PLINTH

SCALE 1:4 (3" = 1'-0") @ A3 · AT THE FOOT

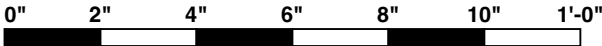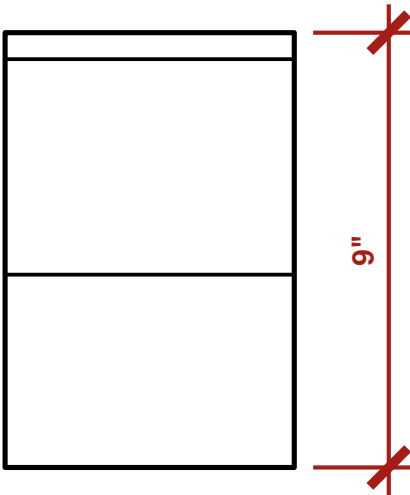

PROJECT
A Study in Teak — Door Casings

SHEET
4 · plinth
Carved head — dressing only · Plain elsewhere · Sections

SCALE
1:4 @ A3

DATE
19.09.2026

REV
8

DRAWING
AST-DR-011 · 7 of 8

RELIEF

DATUM 0 = FACE OF THE PLASTER · LINING AND MOULDING ARE COMMON TO ALL THREE DOORS · THE REST IS THE DRESSING DOOR'S CARVED HEAD

Lining, 2 in on the face	¼" OUT
Moulding, 4 in, reeded	1⅛" OUT
Reed grooves in the moulding face	
Corner block, flush with the moulding	1⅛" OUT
Its sunk panel, two steps	0¼" AND 0⅜" IN

PROJECT A Study in Teak — Door Casings	SHEET Relief Carved head — dressing only · Plain elsewhere · Sections	SCALE NTS	DATE 19.09.2026	REV 8	DRAWING AST-DR-011 · 8 of 8
---	---	--------------	--------------------	----------	--------------------------------