



FRONT ELEVATION — D2 · D3

7 ft 7 in x 2 ft 6 in · SINGLE LEAF

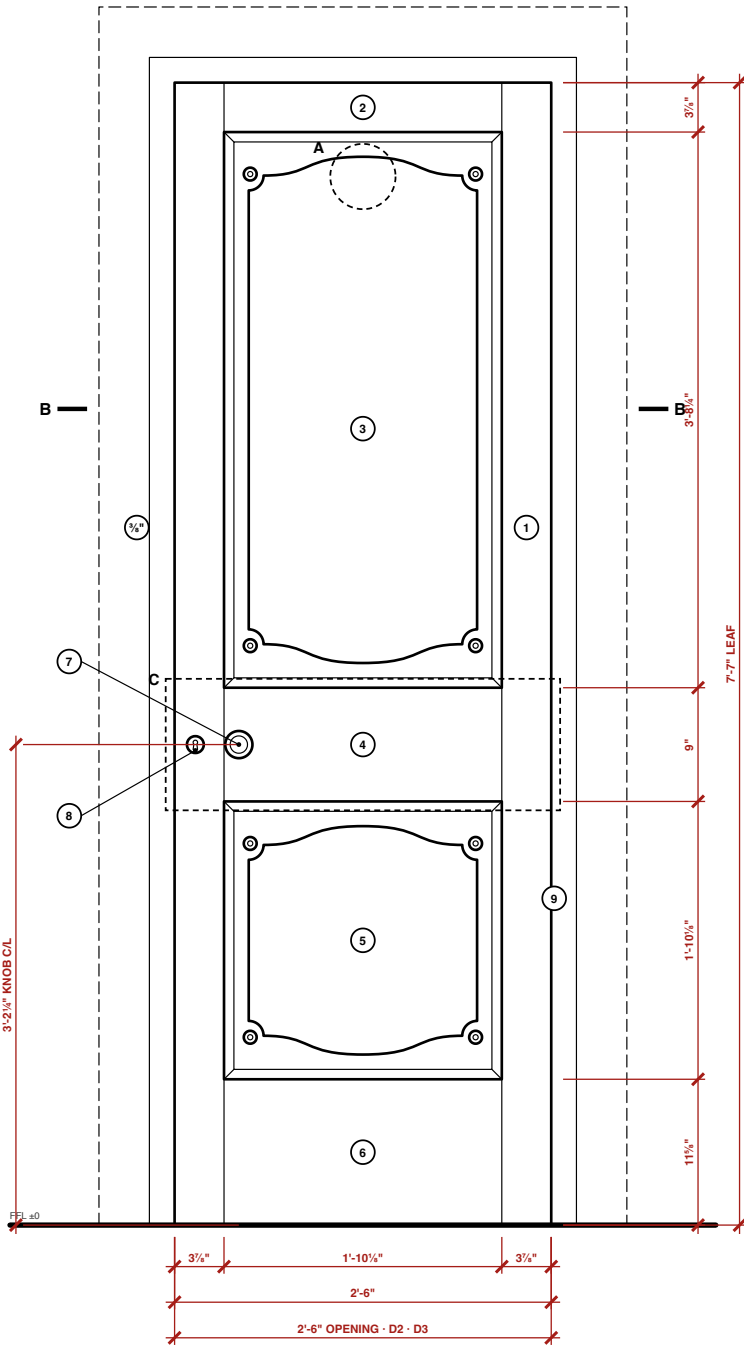


DETAIL A — PANEL HEAD

FOOT OF PANEL IS THE MIRROR

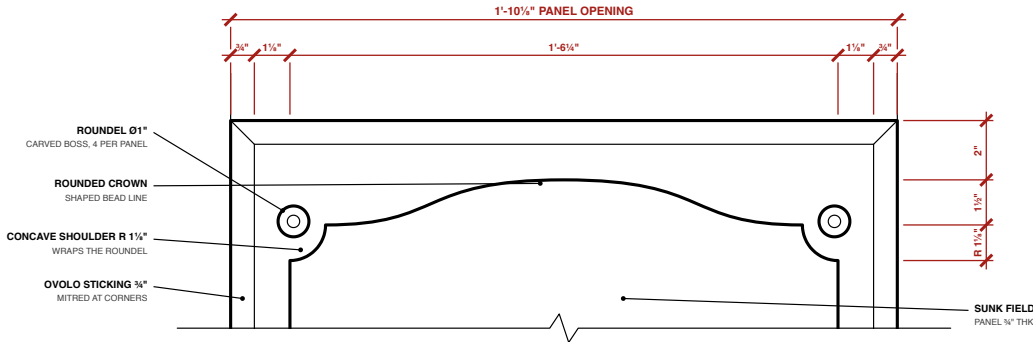


SECTION B-B

HORIZONTAL THROUGH UPPER PANELS

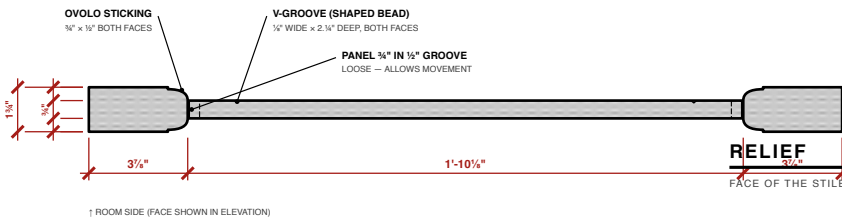

DETAIL C — LOCK RAIL

ACTIVE LEAF

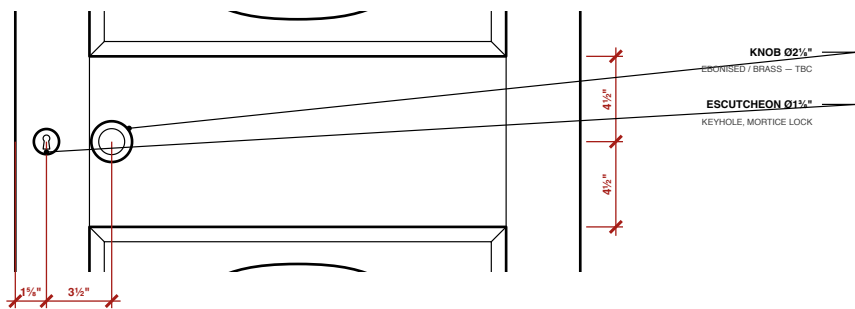

KEY

PARTS OF THE LEAF

- 1 Stile
- 2 Top rail
- 3 Upper panel — shaped bead, 4 roundels
- 4 Lock rail
- 5 Lower panel — same pattern
- 6 Bottom rail
- 7 Knob Ø2 1/4"
- 8 Keyhole escutcheon
- 9 Meeting bead (pair only)
- 1/4" Architrave — to design

NOTES

READ BEFORE MAKING

Dimensions in feet and inches. Do not scale.

Proportions taken from a film-still reference;

leaf size, opening and thickness are ASSUMED.

Knob centre lands 3'-1 1/4" above the floor — normal height.

D2 · D3 — DRESSING · BATHROOM, 7 ft 7 in x 2 ft 6 in.

Set out on the panel square. The 2 ft 6 in leaf gives a 1'-10 1/4" panel; the upper panel is two of those squares (3'-8 1/4"), the lower is one (1'-10 1/4"). Rails follow: top 3 1/4", lock 9", bottom 11 1/2". Knob centre 3'-2 1/4" above the floor.

Both widths take the identical rails and mouldings, so only the panel width changes — here 1'-10 1/4" per panel.

Solid teak frame. Veneer and polish per

Materials; polish to match the teak desk.

Casing: 2 in lining plus 4 in moulding over it, so the moulding head sits 6" above the leaf.

See AST-DR-011 (option A) and AST-DR-012 (option B).

Hinges and lock not yet designed.

RELIEF

FACE OF THE STILES AND RAILS = DATUM 0

Stiles and rails, 1 1/4" thick
Ovolo sticking, 1/4" wide
Panel, 3/4" thick, loose in a 1/2" groove
Panel field
Shaped bead line round the field
Roundel boss Ø1", four per panel
Mitres at the sticking corners
Knob Ø2 1/4" and escutcheon Ø1 1/4"

DATUM 0
WORKED ON THE FRAME EDGE
—
1/2" IN
2.5 IN
1/2" OUT
CUT, NOT SCRIBED
SURFACE

A STUDY IN TEAK

Particulars of the room

DOOR D2 · D3 — 7 FT 7 IN x 2 FT 6 IN

Elevation · Panel head · Section · Lock rail

SCALE

AS NOTED @ A3

DATE

17.09.2026

REV

6 — set out on the panel square: upper two squares, lower one

DWG

AST-DR-009

PROJECT

A Study in Teak — Door D2 · D3 — 7 ft 7 in x 2 ft ...

SHEET

General arrangement — the whole sheet

each view follows at its own scale, pages 2 to 7

SCALE

NTS

DATE

17.09.2026


REV

6

DRAWING

AST-DR-009 · 1 of 7

SCALE 1:3 (4" = 1'-0") @ A3 · FOOT OF PANEL IS THE MIRROR

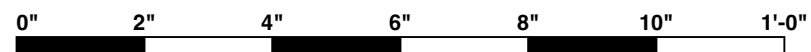

PROJECT	SHEET	SCALE	DATE	REV	DRAWING
A Study in Teak — Door D2 · D3 — 7 ft 7 in x 2 ft ...	Detail a — panel head Elevation · Panel head · Section · Lock rail	1:3 @ A3	17.09.2026	6	AST-DR-009 · 2 of 7

KEY

PARTS OF THE LEAF

- 1 Stile
- 2 Top rail
- 3 Upper panel — shaped bead, 4 roundels
- 4 Lock rail
- 5 Lower panel — same pattern
- 6 Bottom rail
- 7 Knob Ø2⅛"
- 8 Keyhole escutcheon
- 9 Meeting bead (pair only)
- 3/8" Architrave — to design

PROJECT
A Study in Teak — Door D2 · D3 — 7 ft 7 in × 2 ft ...

SHEET
Key
Elevation · Panel head · Section · Lock rail

SCALE
NTS

DATE
17.09.2026

REV
6

DRAWING
AST-DR-009 · 3 of 7

NOTES

READ BEFORE MAKING

Dimensions in feet and inches. Do not scale.

Proportions taken from a film-still reference;

leaf size, opening and thickness are ASSUMED.

Knob centre lands 3'-1³/₄" above the floor — normal height.

D2 · D3 — DRESSING · BATHROOM, 7 ft 7 in × 2 ft 6 in.

Set out on the panel square. The 2 ft 6 leaf gives a

1'-10¹/₈" panel; the upper panel is two of those squares

(3'-8¹/₄"), the lower is one (1'-10¹/₈"). Rails follow: top 3⁷/₈" ,

lock 9" , bottom 11⁵/₈" . Knob centre 3'-2¹/₄" above the floor.

Both widths take the identical rails and mouldings, so

only the panel width changes — here 1'-10¹/₈" per panel.

Solid teak frame. Veneer and polish per

Materials; polish to match the teak desk.

Casing: 2 in lining plus 4 in moulding over it, so the

moulding head sits 6" above the leaf.

See AST-DR-011 (option A) and AST-DR-012 (option B).

PROJECT

A Study in Teak — Door D2 · D3 — 7 ft 7 in × 2 ft ...

SHEET

Notes

Elevation · Panel head · Section · Lock rail

SCALE

NTS

DATE

17.09.2026

REV



6

DRAWING

AST-DR-009 · 4 of 7

SECTION B-B

SCALE 1:3 (4" = 1'-0") @ A3 · HORIZONTAL THROUGH UPPER PANELS

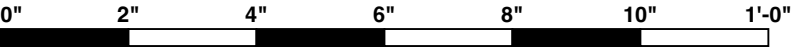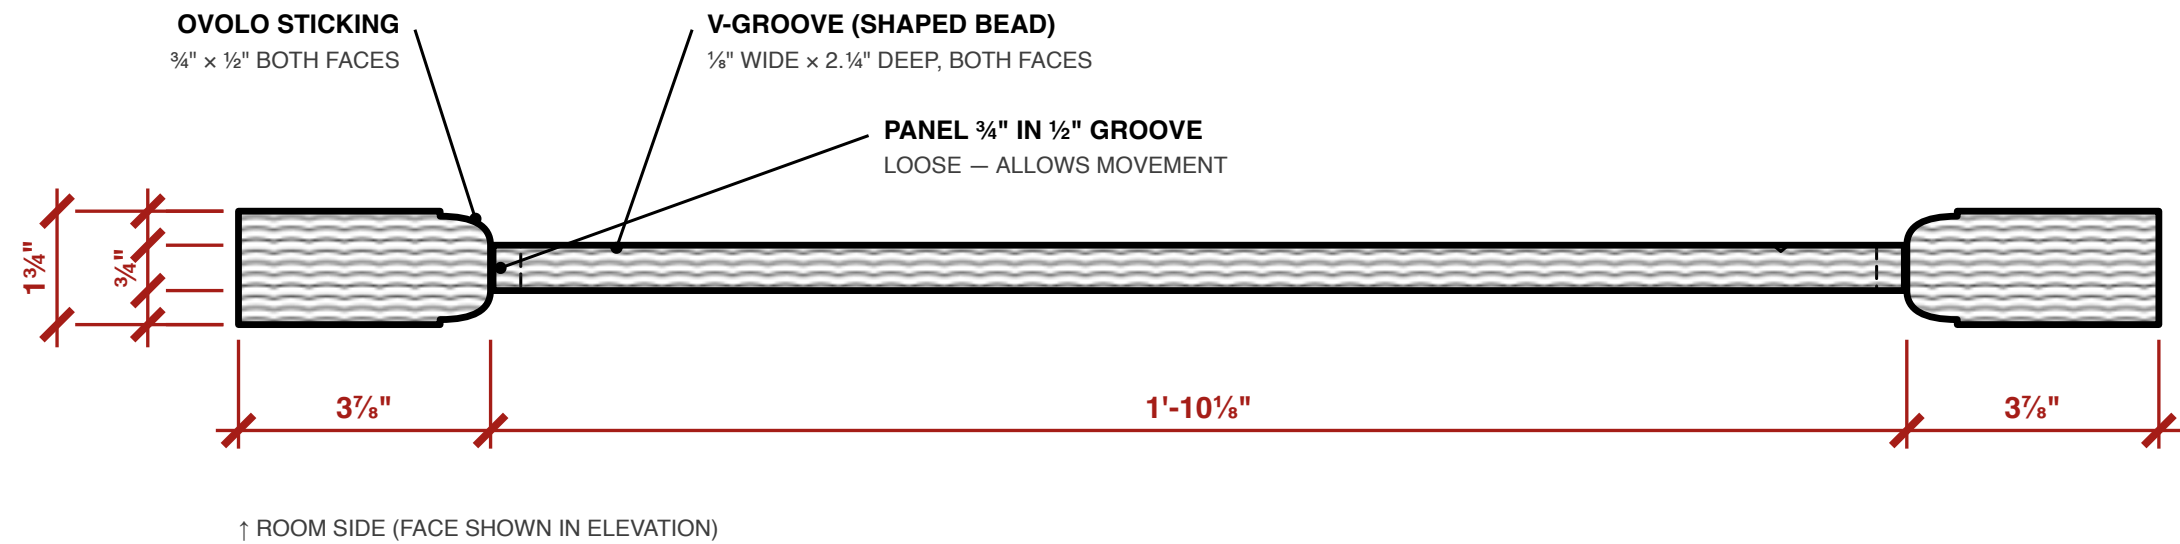

PROJECT
A Study in Teak — Door D2 · D3 — 7 ft 7 in $\times$ 2 ft ...

SHEET
Section B-B
Elevation · Panel head · Section · Lock rail

SCALE
1:3 @ A3

DATE
17.09.2026

REV
6

DRAWING
AST-DR-009 · 5 of 7

RELIEF

Hinges and lock not yet designed.



FACE OF THE STILES AND RAILS = DATUM 0

Stiles and rails, 1¾" thick	DATUM 0
Ovolo sticking, ¾" wide	WORKED ON THE FRAME EDGE
Panel, ¾" thick, loose in a ½" groove	—
Panel field	½" IN
Shaped bead line round the field	2.5 IN
Roundel boss Ø1", four per panel	⅛" OUT
Mitres at the sticking corners	CUT, NOT SCRIBED
Knob Ø2⅛" and escutcheon Ø1⅜"	SURFACE

PROJECT A Study in Teak — Door D2 · D3 — 7 ft 7 in × 2 ft ...	SHEET Relief Elevation · Panel head · Section · Lock rail	SCALE NTS	DATE 17.09.2026	REV 6	DRAWING AST-DR-009 · 6 of 7
--	---	--------------	--------------------	----------	--------------------------------

DETAIL C — LOCK RAIL

SCALE 1:4 (3" = 1'-0") @ A3 · ACTIVE LEAF

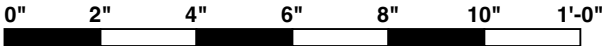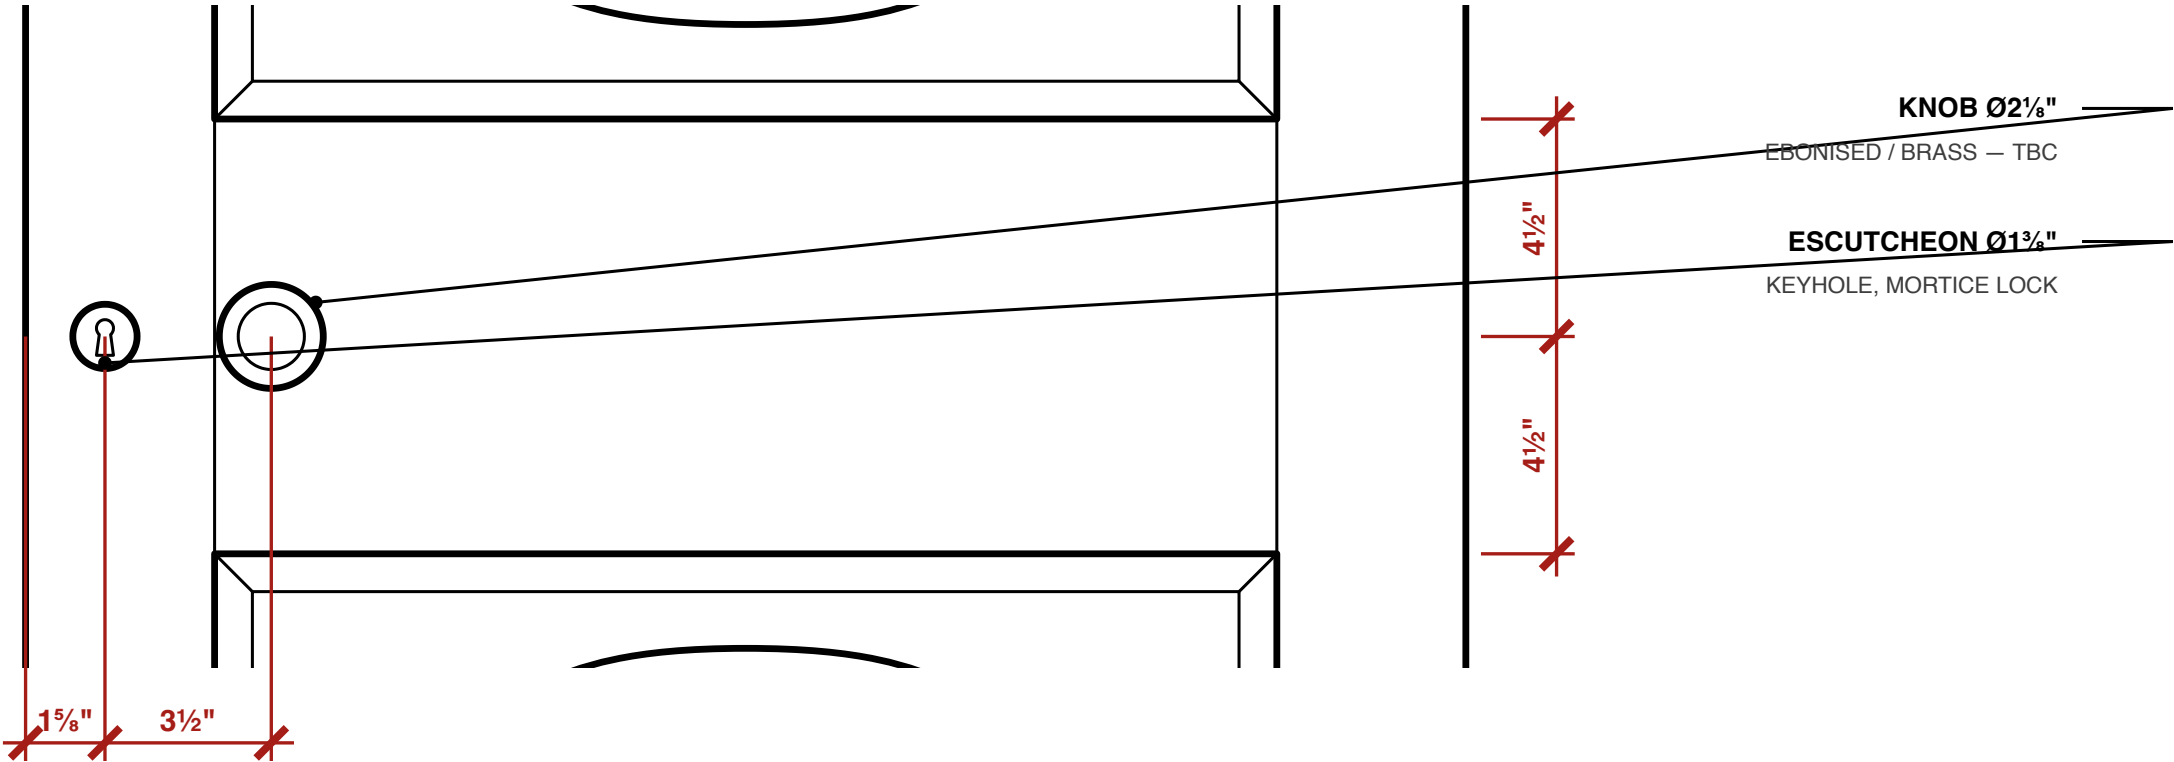

PROJECT
A Study in Teak — Door D2 · D3 — 7 ft 7 in × 2 ft ...

SHEET
Detail c — lock rail
Elevation · Panel head · Section · Lock rail

SCALE
1:4 @ A3

DATE
17.09.2026

REV
6

DRAWING
AST-DR-009 · 7 of 7