


DRESSING ROOM — SHELL AND LAYOUT

PLAN · COPIED FROM THE OWNER'S SKETCH — NOT YET A SITE MEASUREMENT

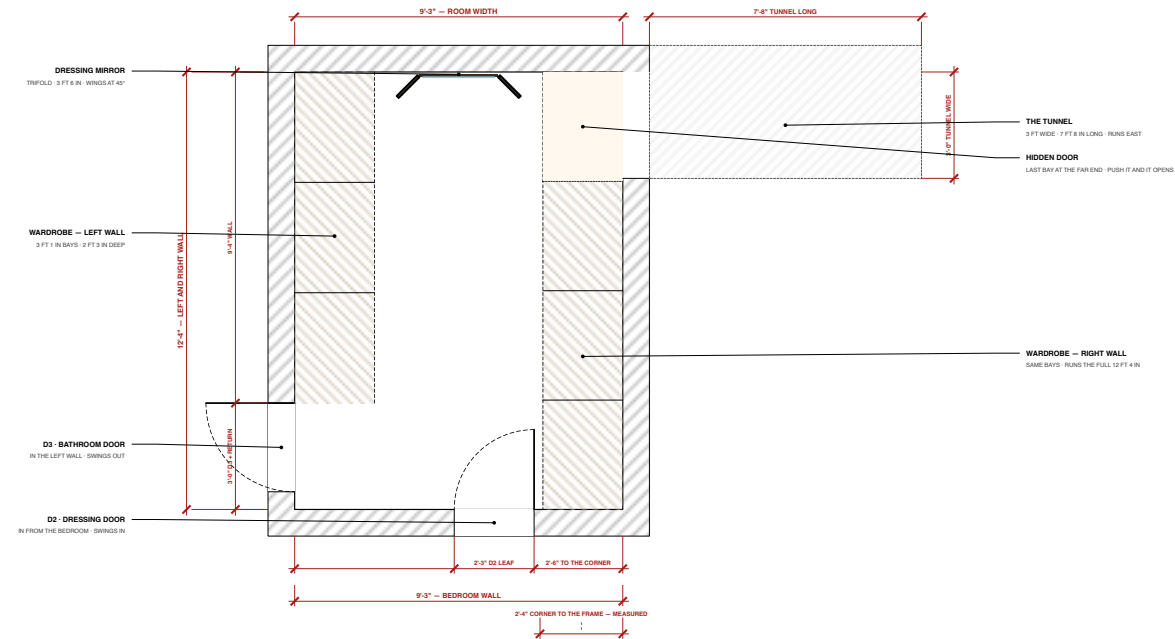

NOTES

REVISION 3

Third pass, and this one copies the sketch rather than interpreting it. The two earlier drawings both had the shape wrong: everything below is read straight off the owner's own clean drawing. The BEDROOM wall is the bottom wall here, 9' 3 in, and it carries D3, the existing dressing door in from the bedroom, 2' 4 in from the right-hand corner to the door FRAME — measured on both sides of the wall, and the figure that now governs. The sketch's 2' 0 in is superseded. The BATHROOM door, D3, is in the LEFT wall, at the bedroom end — not in the bedroom wall. The sketch runs 9' 4 in of wall down from the far corner and then opens the door. The TUNNEL runs EAST, straight out of the far end of the right wall, 3' 0 wide and 7' 8 in long, its far side flush with the far wall. The hidden door is the last wardrobe bay in front of it: built and shelved like every other bay, so from the room it reads as one more cupboard. Ceiling 9' 1 in, plain, over the left and right sides — the same height as the main room. A domed centre rises to 10' 0 in, so the wardrobes are capped at 9' 0 in, clear under it.

SETTLED — D2 sits 2' 4 in from the corner to its frame, on both sides of the wall. That closes this sheet against AST-DR-005 and AST-DR-007: this room's right-hand corner and the bedroom's bed wall corner are the same corner. Walls are taken at 9 in throughout. See AST-DR-024. OPEN — D2's width, 8 in down 2' 0 in, as the owner said, but the sketch's own 9' 4 in against 12' 4 in leaves 3' 0 in — so a 6 in return is shown into the corner. To confirm. SETTLED — the wardrobes are 2' 0 in deep, so the right-hand run reaches the bedroom wall and clears D2's frame, 2' 4 in in off that corner, by 1 in. OPEN — the left run is down stopping at D3. Whether it ends there or returns over the door is not decided. OPEN — where the tunnel leads, and what is at its far end. OPEN — the dome's own shape: how far along the room it runs, and its profile. The mirror is the confirmed infold, 3' 0 in across with its wings at 45° — see AST-DR-027.

A STUDY IN TEAK	
Particulars of the room	
DRESSING ROOM	
Shell and layout · third pass	
SCALE 1:35 @ A3	DATE 25.09.2026
REV	DWG AST-DR-023

PROJECT
A Study in Teak — Dressing Room

SHEET
General arrangement — the whole sheet
each view follows at its own scale, pages 2 to 3

SCALE
NTS



DATE
25.09.2026

REV
3

DRAWING
AST-DR-023 · 1 of 3

DRESSING ROOM — SHELL AND LAYOUT

SCALE 1:48 (1/4" = 1'-0") @ A4 · PLAN · COPIED FROM THE OWNER'S SKETCH — NOT YET A SITE MEASUREMENT

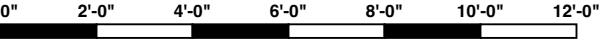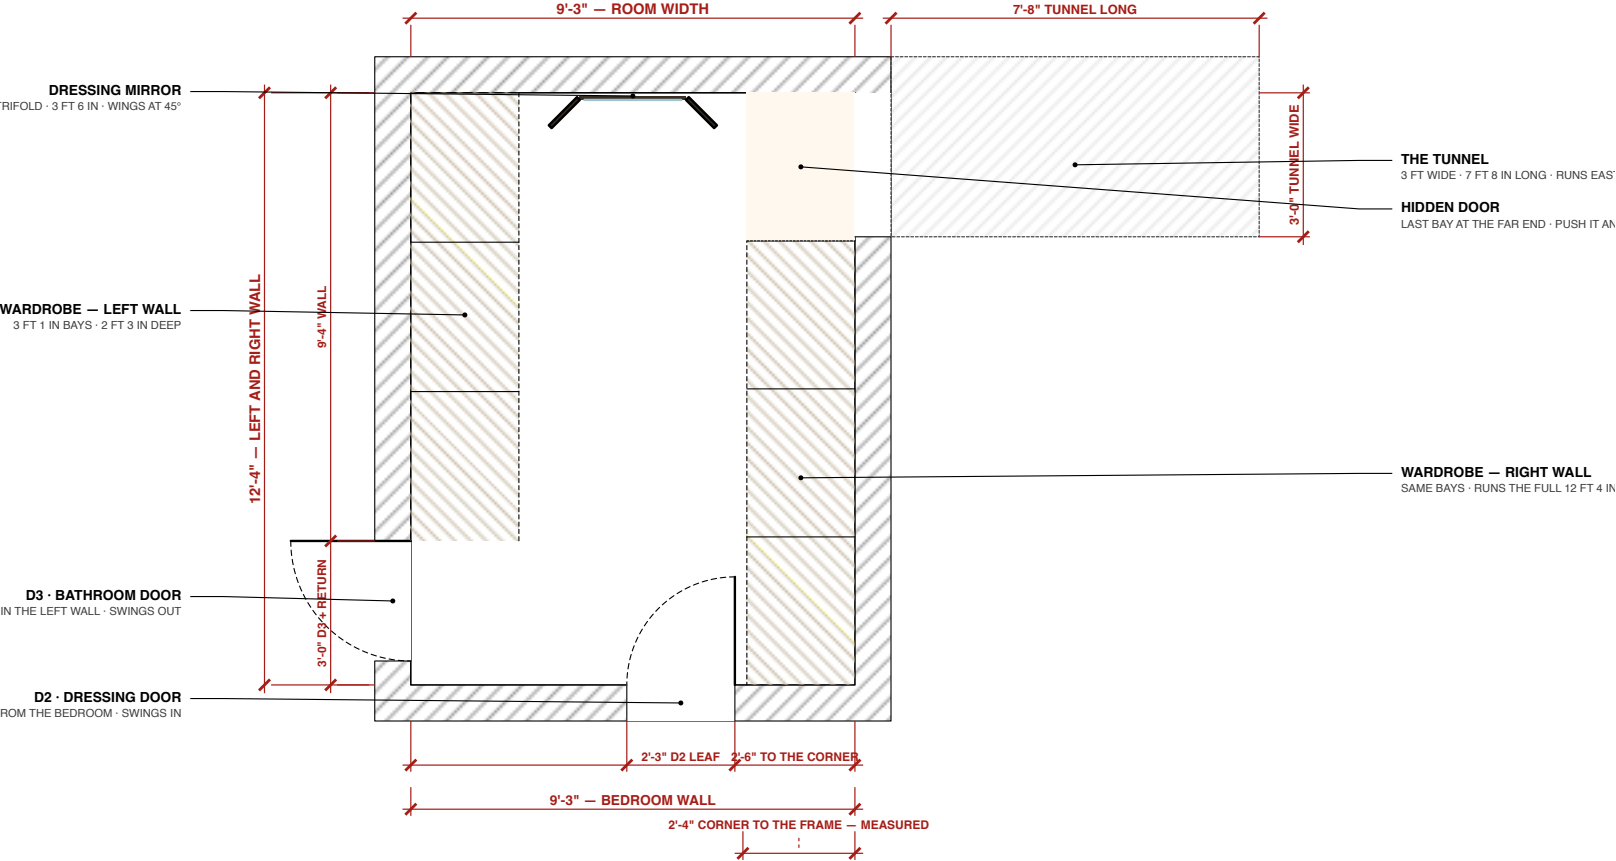

PROJECT A Study in Teak — Dressing Room	SHEET Dressing room — shell and layout Shell and layout · third pass	SCALE 1:48 @ A4	DATE 25.09.2026	REV 3	DRAWING AST-DR-023 · 2 of 3
--	--	--------------------	--------------------	----------	--------------------------------

NOTES

REVISION 3

Third pass, and this one copies the sketch rather than interpreting it. The two earlier drawings both had the shape wrong; everything below is read straight off the owner's own clean drawing. The BEDROOM wall is the bottom wall here, 9 ft 3 in, and it carries D2, the existing dressing door in from the bedroom, 2 ft 4 in from the right-hand corner to the door FRAME — measured on both sides of the wall, and the figure that now governs. The sketch's 2 ft 0 in is superseded. The BATHROOM door, D3, is in the LEFT wall, at the bedroom end — not in the bedroom wall. The sketch runs 9 ft 4 in of wall down from the far corner and then opens the door. The TUNNEL runs EAST, straight out of the far end of the right wall, 3 ft wide and 7 ft 8 in long, its far side flush with the far wall. The hidden door is the last wardrobe bay in front of it: built and shelved like every other bay, so from the room it reads as one more cupboard. Ceiling 9 ft 1 in, plain, over the left and right sides — the same height as the main room. A domed centre rises to 10 ft 0 in, so the wardrobes are capped at 9 ft 0 in, clear under it.

SETTLED — D2 sits 2 ft 4 in from the corner to its frame, on both sides of this sheet against AST-DR-000 and AST-DR-007: this room's right-hand bed-wall corner are the same corner. Walls are taken at 9 in through the corner. OPEN — D3's width. It is drawn 2 ft 6 in, as the owner said, but the sketch's 12 ft 4 in leaves 3 ft 0 in — so a 6 in return is shown into the corner. SETTLED — the wardrobes are 2 ft 3 in deep, so the right-hand run of wall clears D2's frame, 2 ft 4 in off that corner, by 1 in. OPEN — the left run is drawn stopping at D3. Whether it ends there or not is not decided. OPEN — where the tunnel leads, and what is at its far end. OPEN — the dome's own shape: how far along the room it runs, and how high. The mirror is the confirmed trifold, 3 ft 6 in across with its wings at 4

PROJECT A Study in Teak — Dressing Room	SHEET Notes Shell and layout · third pass	SCALE NTS	DATE 25.09.2026	REV 3	DRAWING AST-DR-023 · 3 of 3
--	---	--------------	--------------------	----------	--------------------------------