



ELEVATION — LEFT WALL

SEEN FROM THE ROOM - STUDY CORNER LEFT, BED CORNER RIGHT

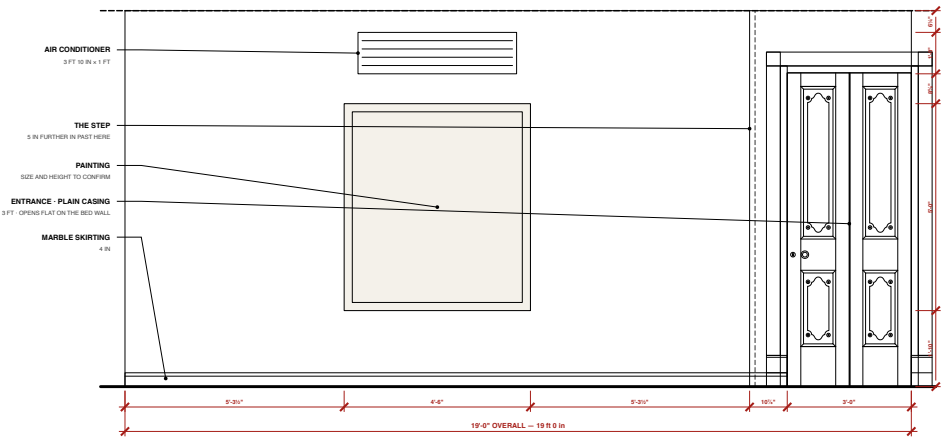

PLAN

CUT AT 3'-11 1/2" - ROOM BELOW THE WALL

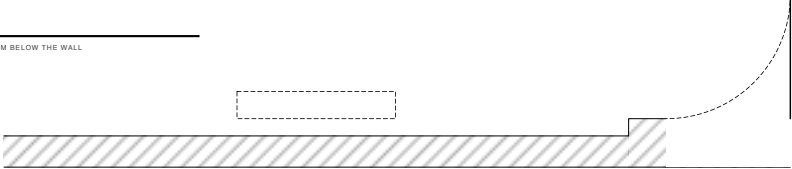

NOTES

REVISION 5

This wall stays plain. Paint, the marble skirting, one painting and the air conditioner over it — nothing is built into it and nothing is panelled. It is the quiet side of the room, opposite the panelled right wall, and it is the wall that carries the splay and the step, so anything fitted to it would have to be scuffed twice. The painting is centred on the 15 ft 1 1/2 in of wall before the step, the only uninterrupted run. Centre line 7 ft 8 1/2 in from the study corner, 1 ft 10 in off the floor.

OPEN — the painting is drawn 4 ft 6 in x 5 ft 0 in, centred at 4 ft 4 in. Still assumed. Send the real size and it is a one-time change. Sized to the wall it has: 8 1/2 in clear under the air conditioner, and 8 in wider than the unit, so the AC sits within its width. The air conditioner is 3 ft 10 in x 1 ft 0 in — MEASURED. Its depth (7 1/4 in) and its height off the ceiling (6 1/2 in) are still assumed. The AC needs a power point and a drain run before the wall is painted — decide the side the pipework leaves on. The entrance takes the PLAIN casing: same 2 in lining and 4 in moulding as every opening, running straight across the head and stopping. The carved head on AST-DR-011 is the DRESSING door's alone. OPEN — the profile of that 4 in plain band is not settled. Drawn flat.

A STUDY IN TEAK	
Particulars of the room	
LEFT WALL	
Elevation - Plan - The plain wall	
SCALE 1:30 @ A3	DATE 23.09.2026
REV 5 — the painting widened to 4 ft 6 in	DWG AST-DR-014

PROJECT
A Study in Teak — Left Wall

SHEET
General arrangement — the whole sheet
each view follows at its own scale, pages 2 to 4

SCALE
NTS



DATE
23.09.2026

REV
5

DRAWING
AST-DR-014 · 1 of 4

ELEVATION — LEFT WALL



SCALE 1:30 @ A4 · SEEN FROM THE ROOM · STUDY CORNER LEFT, BED CORNER RIGHT

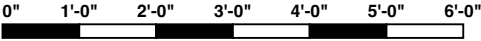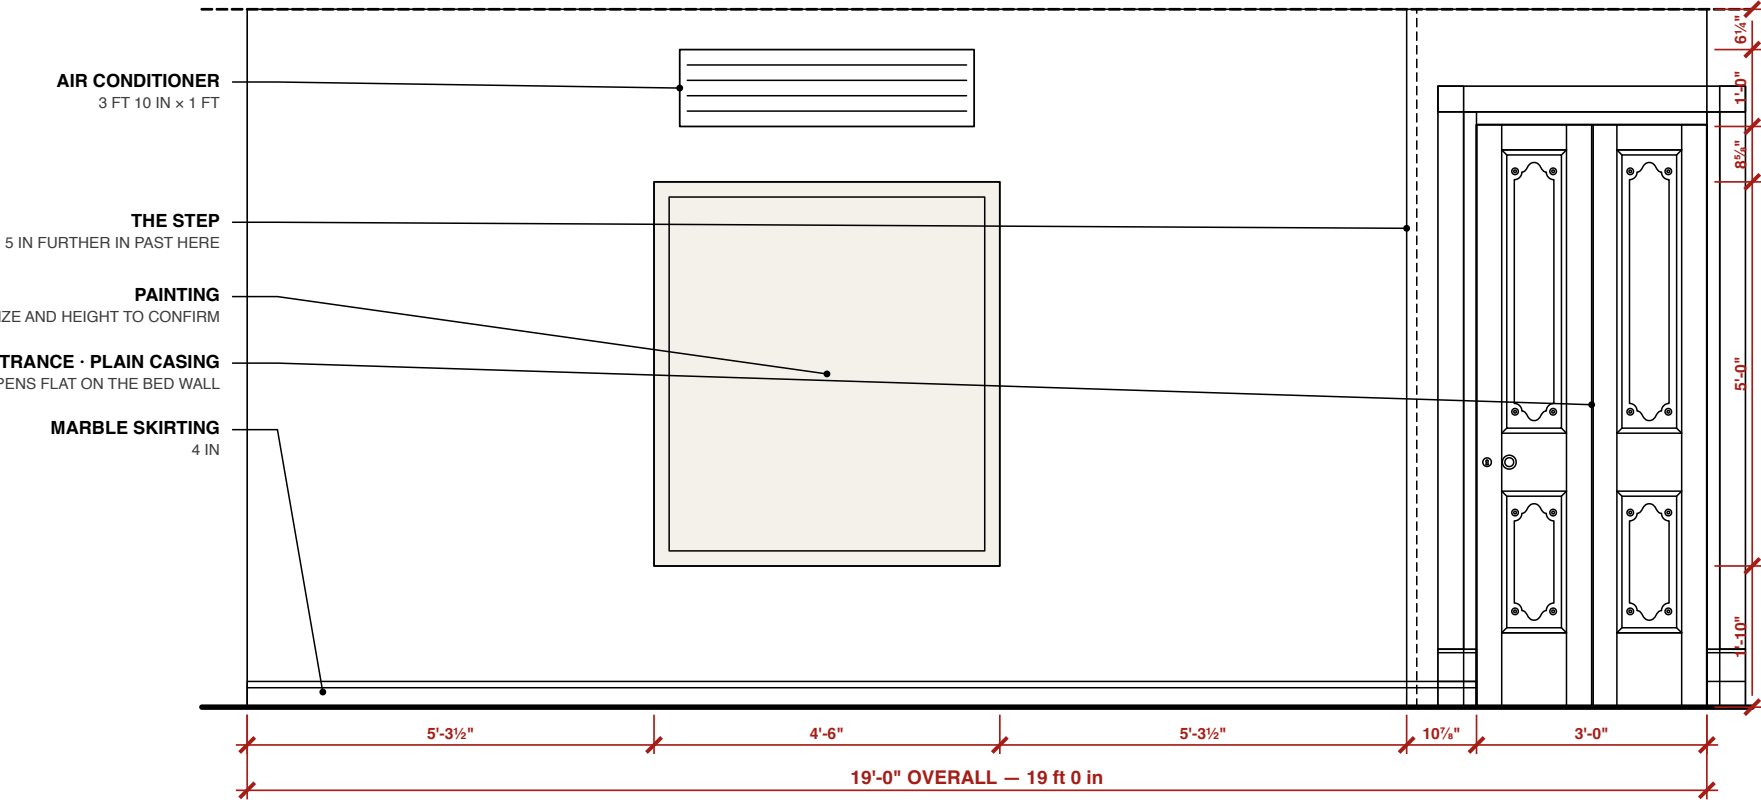

PROJECT	SHEET	SCALE	DATE	REV	DRAWING
A Study in Teak — Left Wall	Elevation — left wall Elevation · Plan · The plain wall	1:30 @ A4	23.09.2026	5	AST-DR-014 · 2 of 4

PLAN

SCALE 1:25 @ A4 · CUT AT 3'-11¼" · ROOM BELOW THE WALL

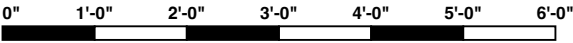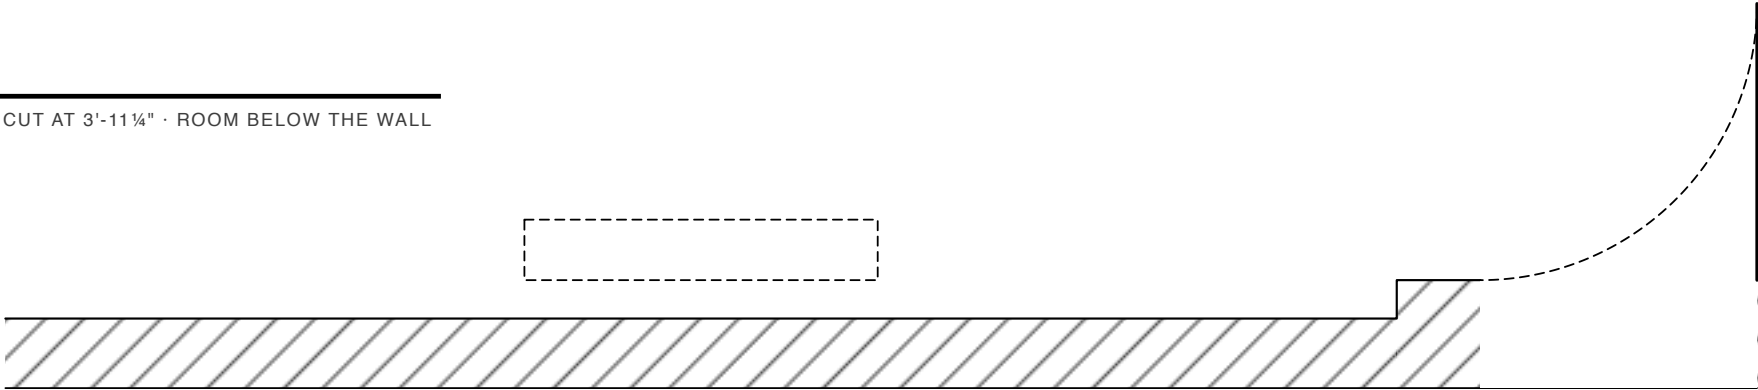

PROJECT A Study in Teak — Left Wall	SHEET Plan Elevation · Plan · The plain wall	SCALE 1:25 @ A4	DATE 23.09.2026	REV 5	DRAWING AST-DR-014 · 3 of 4
--	--	--------------------	--------------------	----------	--------------------------------

NOTES

REVISION 5

This wall stays plain. Paint, the marble skirting, one painting and the air conditioner over it — nothing is built into it and nothing is panelled.

It is the quiet side of the room, opposite the panelled right wall, and it is the wall that carries the splay and the step, so anything fitted to it would have to be scribed twice.

The painting is centred on the 15 ft 1⅝ in of wall before the step, the only uninterrupted run. Centre line 7 ft 6½ in from the study corner, 1 ft 10 in off the floor.

OPEN — the painting is drawn 4 ft 6 in x 5 ft 0 in, centred at 4 ft 4 in.

Still assumed. Send the real size and it is a one-line change.

Sized to the wall it has: 8⅝ in clear under the air conditioner, and 8 in wider than the unit, so the AC sits within its width.

The air conditioner is 3 ft 10 in x 1 ft 0 in — MEASURED. Its depth (7⅞ in) and its height off the ceiling (6¼ in) are still assumed.

The AC needs a power point and a drain run before the wall is painted — decide the side the pipework leaves on.

The entrance takes the PLAIN casing: same 2 in lining and 4 in moulding at every opening, running straight across the head and stopping. The carved head on AST-DR-011 is the DRESSING door's alone.

OPEN — the profile of that 4 in plain band is not settled. Drawn flat.

PROJECT A Study in Teak — Left Wall	SHEET Notes Elevation · Plan · The plain wall	SCALE NTS	DATE 23.09.2026	REV 5	DRAWING AST-DR-014 · 4 of 4
--	---	--------------	--------------------	----------	--------------------------------