



ELEVATION — RIGHT WALL

SEEN FROM THE ROOM - STUDY WALL ON THE LEFT - OPTION C

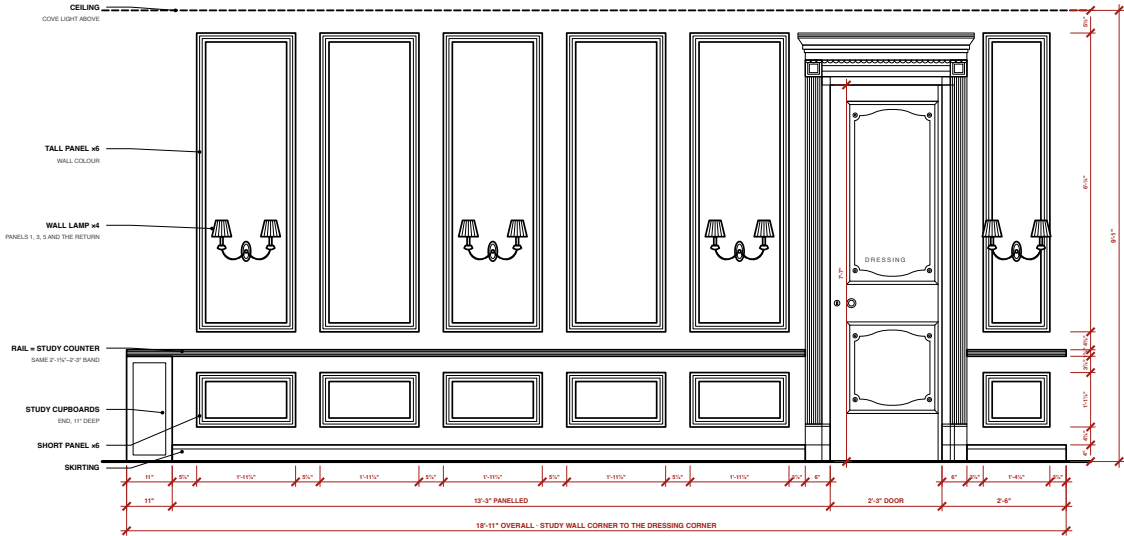


PLAN

CUT AT 3'-3 3/4" - ROOM BELOW, WALL ABOVE

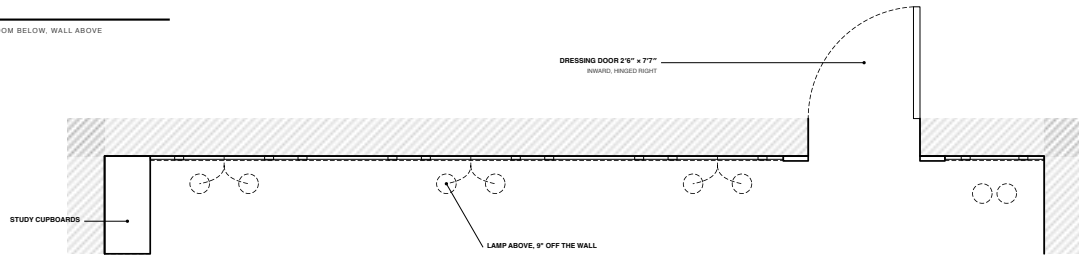

1 · PANEL MOULDING


SECTION

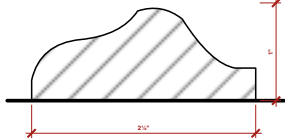

WALL FACE BELOW: MITRED CORNERS

2 · RAIL


SECTION

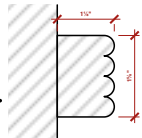

MATCHES THE COUNTER EDGE

3 · SKIRTING


MARBLE · SECTION

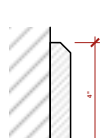

WHITE MARBLE, ALREADY LAPPED WITH A SMALL TOP CHAMFER

4 · WALL LAMP


ELEVATION - x/4

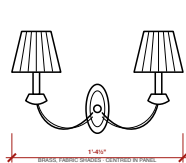

BROOK FABRIC COVERS: "DISTRICT" IN TEAK

SECTION A-A

THROUGH PANEL 1

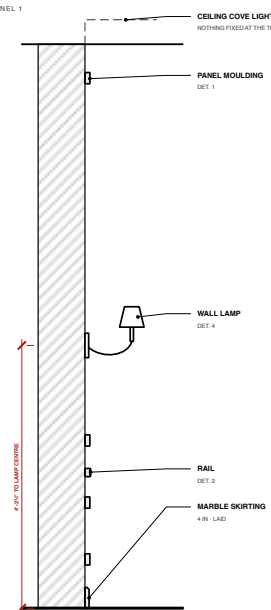

NOTES

REVISION: 18

Option C: 5 equal panels, lamps in 1, 3, 5 and the return.

One narrow panel on the wall past the door.

Moulding, rail and skirting painted the wall colour.

SELECTED after four schemes: the rail is the study counter

band carried round the corner, and it dies into the casing.

Skirting is white marble, 4 in, already laid.

Casing 2 in lining + 4 in moulding = 6 in, 3'-4" overall;

crown at 8 R 8 in, and the tall panels stop on that

line, not the leaf head at 7 R 7 in.

2 R 4 in corner to frame, measured both sides; leaf 2 R 3

in a 2 in frame. OPEN: that puts the frame 14 R 6 from the

study corner, 6 in off the lapped 13 R 6. Release that end.

A STUDY IN TEAK

Particulars of the room

RIGHT WALL — PANEL MOULDING

Elevation · Plan · Section · Details

SCALE

AS NOTED @ A3

DATE

20.09.2026

REV

18 — SELECTED: the rail at 2 R 3 in, carrying the study counter round

DWG

AST-DR-007

PROJECT
A Study in Teak — Right Wall — Panel Mou...

SHEET
General arrangement — the whole sheet
each view follows at its own scale, pages 2 to 9

SCALE
NTS



DATE
20.09.2026

REV
18

DRAWING
AST-DR-007 · 1 of 9

ELEVATION — RIGHT WALL



SCALE 1:30 @ A4 · SEEN FROM THE ROOM · STUDY WALL ON THE LEFT · OPTION C

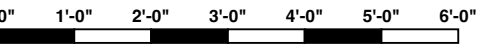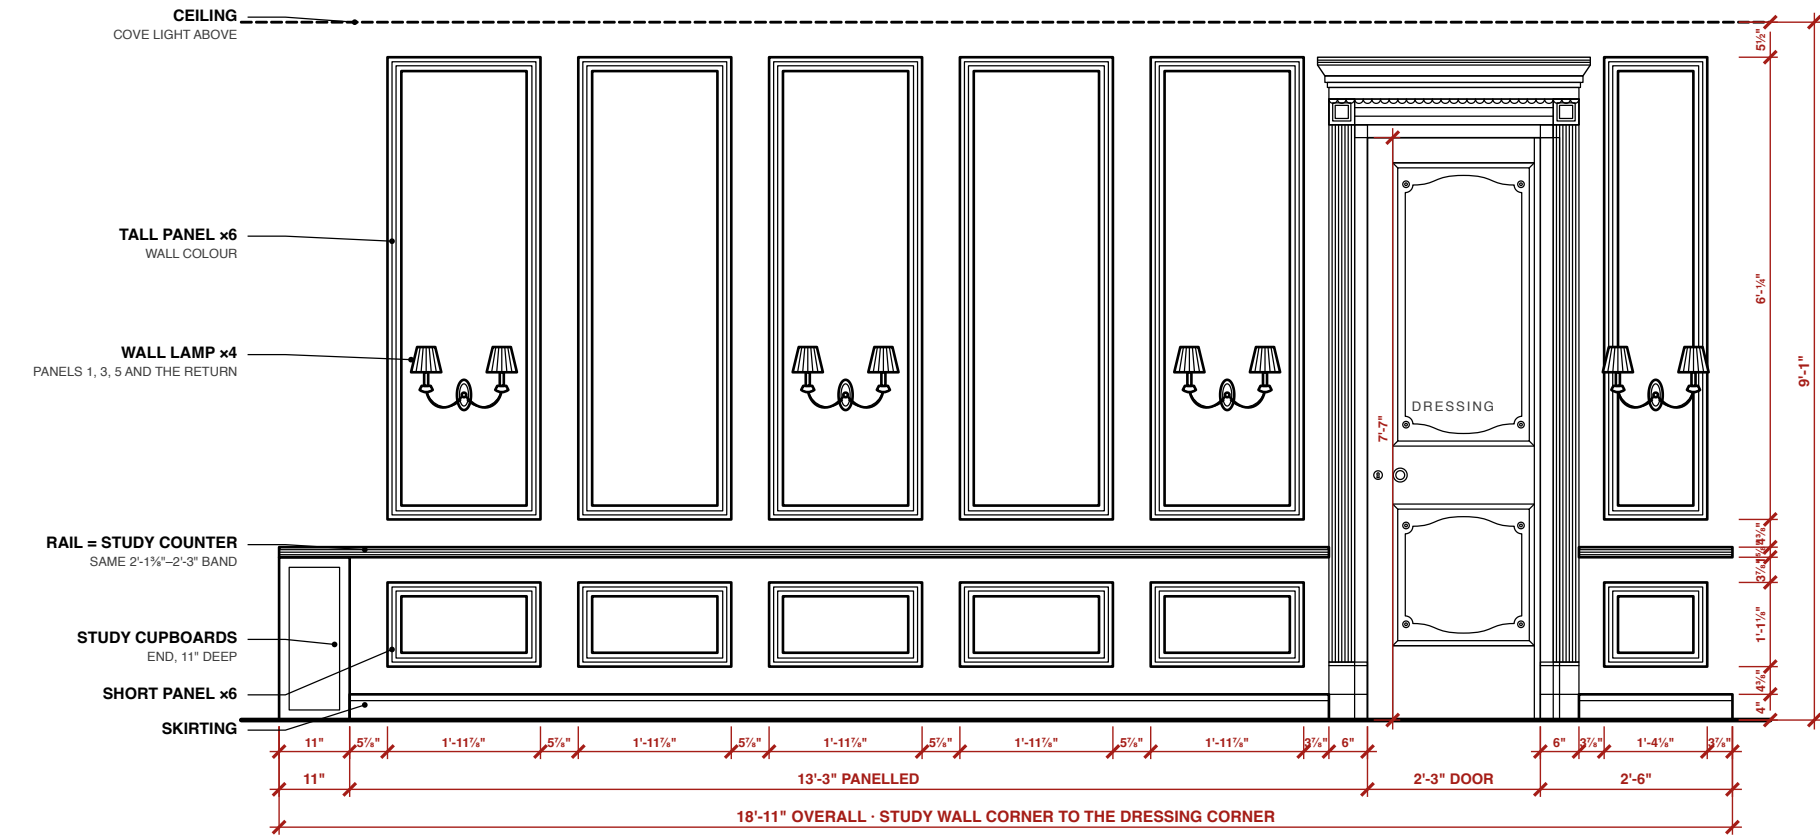

PROJECT	SHEET	SCALE	DATE	REV	DRAWING
A Study in Teak — Right Wall — Panel Mou...	Elevation — right wall Elevation · Plan · Section · Details	1:30 @ A4	20.09.2026	18	AST-DR-007 · 2 of 9

SECTION A-A



SCALE 1:24 (1/2" = 1'-0") @ A4 · THROUGH PANEL 1

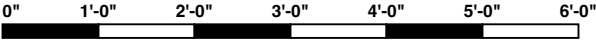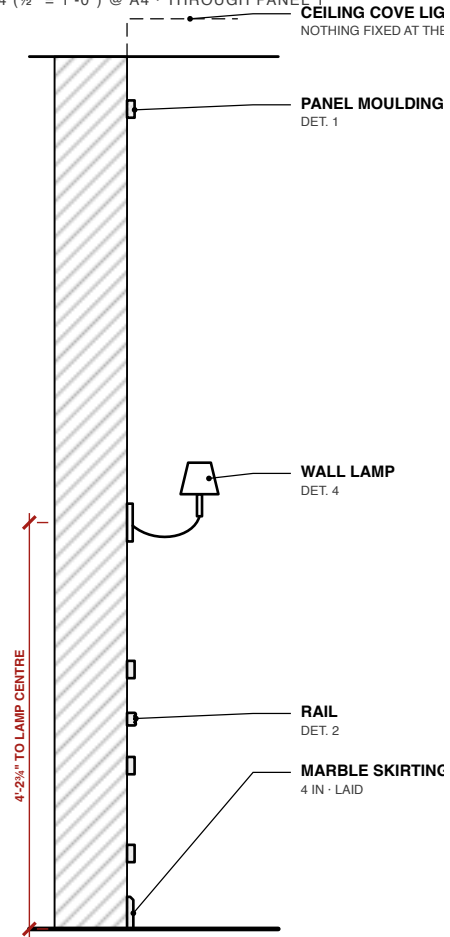

PROJECT A Study in Teak — Right Wall — Panel Mou...	SHEET Section A-A Elevation · Plan · Section · Details	SCALE 1:24 @ A4	DATE 20.09.2026	REV 18	DRAWING AST-DR-007 · 3 of 9
--	--	--------------------	--------------------	-----------	--------------------------------

PLAN

SCALE 1:30 @ A4 · CUT AT 3'-3¾" · ROOM BELOW, WALL ABOVE

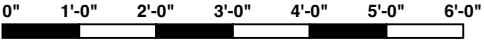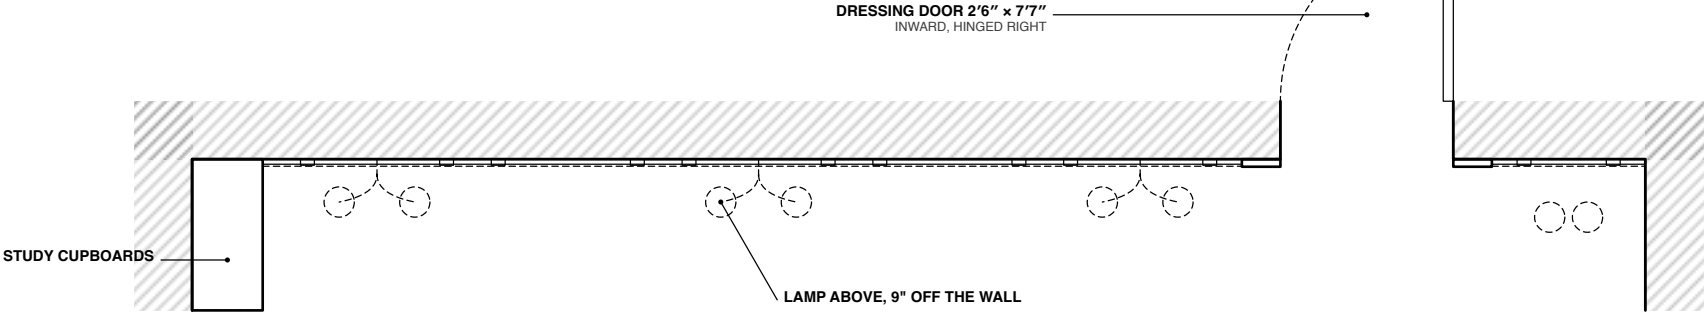

PROJECT
A Study in Teak — Right Wall — Panel Mou...

SHEET
Plan
Elevation · Plan · Section · Details

SCALE
1:30 @ A4

DATE
20.09.2026

REV
18

DRAWING
AST-DR-007 · 4 of 9

NOTES

REVISION 18

Option C: 5 equal panels, lamps in 1, 3, 5 and the return.

One narrow panel on the wall past the door.

Moulding, rail and skirting painted the wall colour.

SELECTED after four schemes: the rail is the study counter

band carried round the corner, and it dies into the casing.

Skirting is white marble, 4 in, already laid.

Casing 2 in lining + 4 in moulding = 6 in, 3'-6" overall;

crown at 8 ft 8 in, and the tall panels stop on that

line, not the leaf head at 7 ft 7 in.

2 ft 4 in corner to frame, measured both sides; leaf 2 ft 3


in a 2 in frame. OPEN: that puts the frame 14 ft 0 from the

study corner, 6 in off the taped 13 ft 6. Retape that end.


PROJECT	SHEET	SCALE	DATE	REV	DRAWING
A Study in Teak — Right Wall — Panel Mou...	Notes Elevation · Plan · Section · Details	NTS	20.09.2026	18	AST-DR-007 · 5 of 9

1 · PANEL MOULDING

SCALE 1:1 (FULL SIZE) @ A4 · SECTION

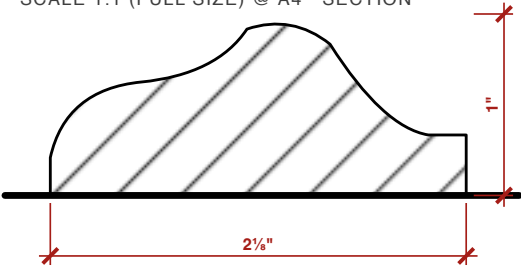


WALL FACE BELOW · MITRED CORNERS

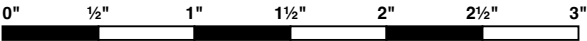


PROJECT	SHEET	SCALE	DATE	REV	DRAWING
A Study in Teak — Right Wall — Panel Mou...	1 · panel moulding Elevation · Plan · Section · Details	1:1 @ A4	20.09.2026	18	AST-DR-007 · 6 of 9

2 · RAIL

SCALE 1:1 (FULL SIZE) @ A4 · SEC

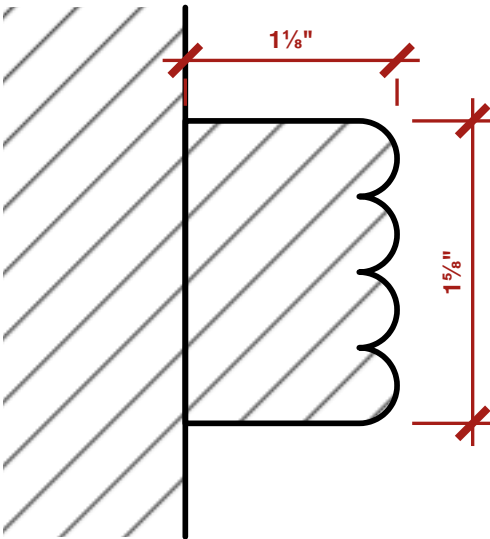

MATCHES THE COUNTER EDGE

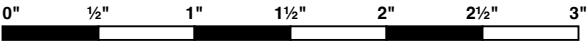

PROJECT
A Study in Teak — Right Wall — Panel Mou...

SHEET
2 · rail
Elevation · Plan · Section · Details

SCALE
1:1 @ A4



DATE
20.09.2026

REV
18

DRAWING
AST-DR-007 · 7 of 9

3 · SKIRTING



SCALE 1:2 (6" = 1'-0") @ A4 · MARBLE · SECTION

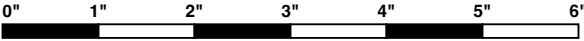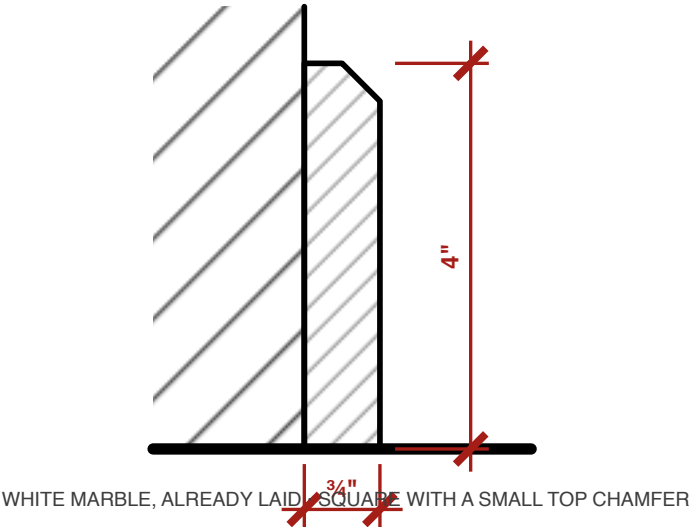

PROJECT	SHEET	SCALE	DATE	REV	DRAWING
A Study in Teak — Right Wall — Panel Mou...	3 · skirting Elevation · Plan · Section · Details	1:2 @ A4	20.09.2026	18	AST-DR-007 · 8 of 9

4 · WALL LAMP

SCALE 1:4 (3" = 1'-0") @ A4 · ELEVATION · x4

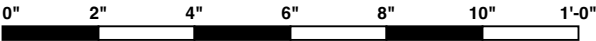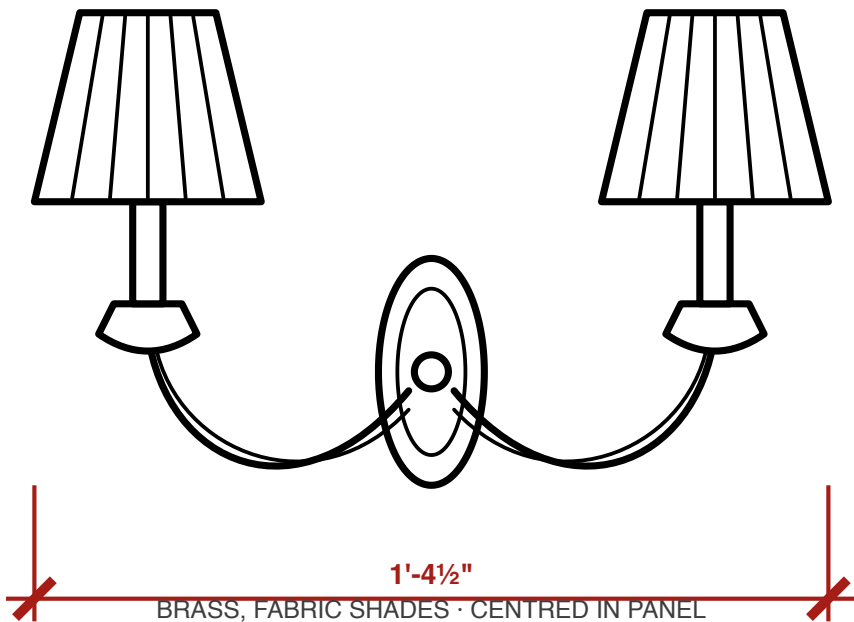

PROJECT	SHEET	SCALE	DATE	REV	DRAWING
A Study in Teak — Right Wall — Panel Mou...	4 · wall lamp Elevation · Plan · Section · Details	1:4 @ A4	20.09.2026	18	AST-DR-007 · 9 of 9