



ELEVATION — RIGHT WALL

SEEN FROM THE ROOM · STUDY WALL ON THE LEFT · OPTION C

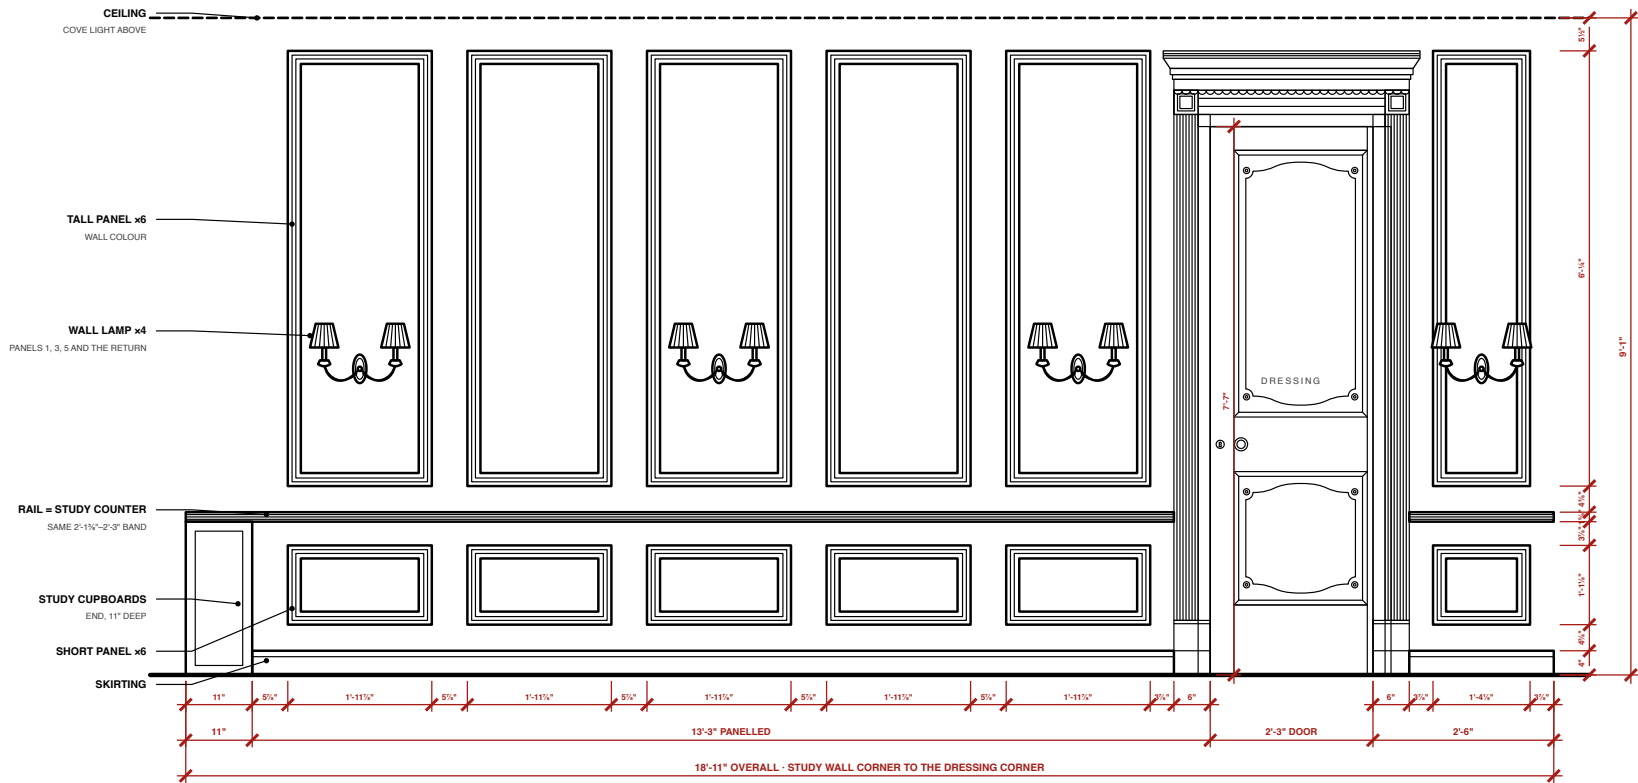

PLAN

CUT AT 3'-3 3/4" · ROOM BELOW, WALL ABOVE

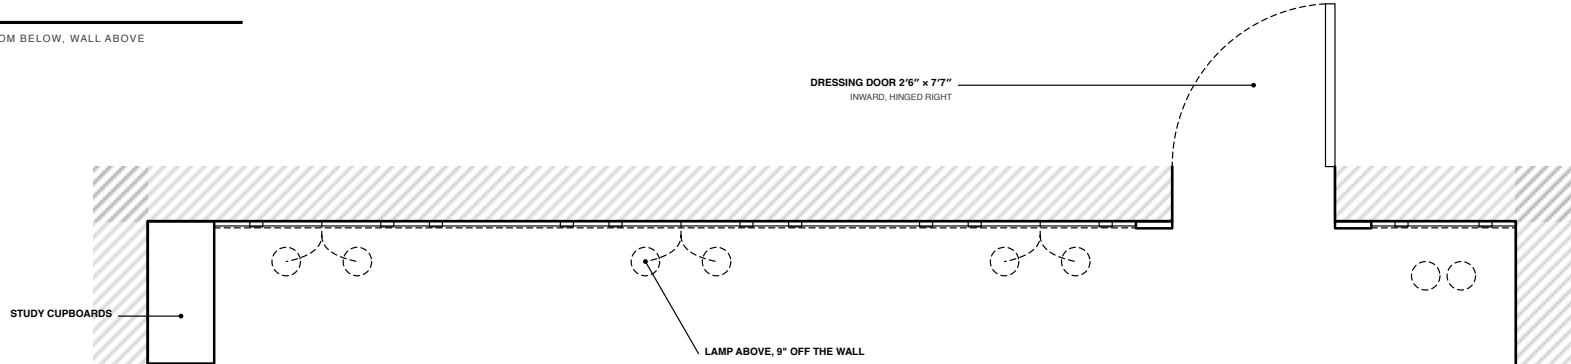

1 · PANEL MOULDING


SECTION



WALL FACE BELOW · MITRED CORNERS

2 · RAIL


SECTION

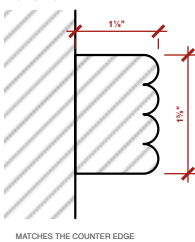

MATCHES THE COUNTER EDGE

3 · SKIRTING


MARBLE · SECTION

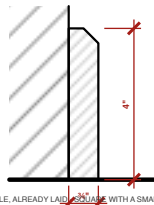

WHITE MARBLE, ALREADY LAID · 2 1/2" HIGH WITH A SMALL TOP CHAMFER


4 · WALL LAMP

ELEVATION · ×4

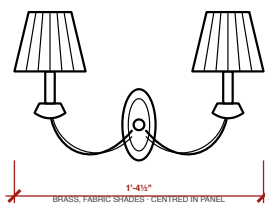

SECTION A-A

THROUGH PANEL 1

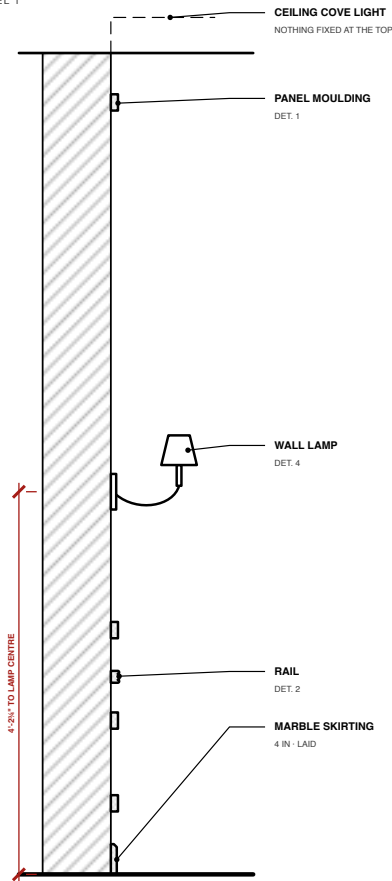

NOTES

REVISION 18

- Option C: 5 equal panels, lamps in 1, 3, 5 and the return.
One narrow panel on the wall past the door.
Moulding, rail and skirting painted the wall colour.
SELECTED after four schemes: the rail is the study counter band carried round the corner, and it dies into the casing.
Skirting is white marble, 4 in, already laid.
Casing 2 in lining + 4 in moulding = 6 in, 3'-6" overall;
crown at 8 ft 8 in, and the tall panels stop on that line, not the leaf head at 7 ft 7 in.
2 ft 4 in corner to frame, measured both sides; leaf 2 ft 3 in a 2 in frame. OPEN: that puts the frame 14 ft 0 in from the study corner, 6 in off the taped 13 ft 6. Retape that end.

A STUDY IN TEAK

Particulars of the room

RIGHT WALL — PANEL MOULDING

Elevation · Plan · Section · Details

SCALE
AS NOTED @ A3

DATE
20.09.2026

REV
18 — SELECTED: the rail at 2 ft 3 in, carrying the study counter round

DWG
AST-DR-007

PROJECT
A Study in Teak — Right Wall — Panel Moulding

SHEET
General arrangement — the whole sheet
each view follows at its own scale, pages 2 to 9

SCALE
NTS


DATE
20.09.2026

REV
18

DRAWING
AST-DR-007 · 1 of 9

SCALE 1:20 @ A3 · SEEN FROM THE ROOM · STUDY WALL ON THE LEFT · OPTION C

SCALE 1:20 @ A3 · SEEN FROM THE ROOM · STUDY WALL ON THE LEFT · OPTION C


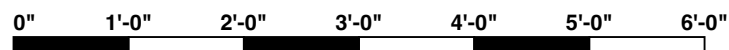


PROJECT	SHEET	SCALE	DATE	REV	DRAWING
A Study in Teak — Right Wall — Panel Moulding	Elevation — right wall Elevation · Plan · Section · Details	1:20 @ A3	20.09.2026	18	AST-DR-007 · 2 of 9

ALL DIMENSIONS IN FEET & INCHES. PRINT ON A3 AT 100% / "ACTUAL SIZE" – NOT "FIT TO PAGE" – AND CHECK THE SCALE BAR. DO NOT SCALE; WORK TO FIGURED DIMENSIONS. VERIFY ON SITE.

SECTION A-A

SCALE 1:15 @ A3 · THROUGH PANEL 1

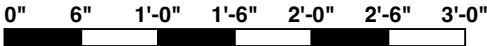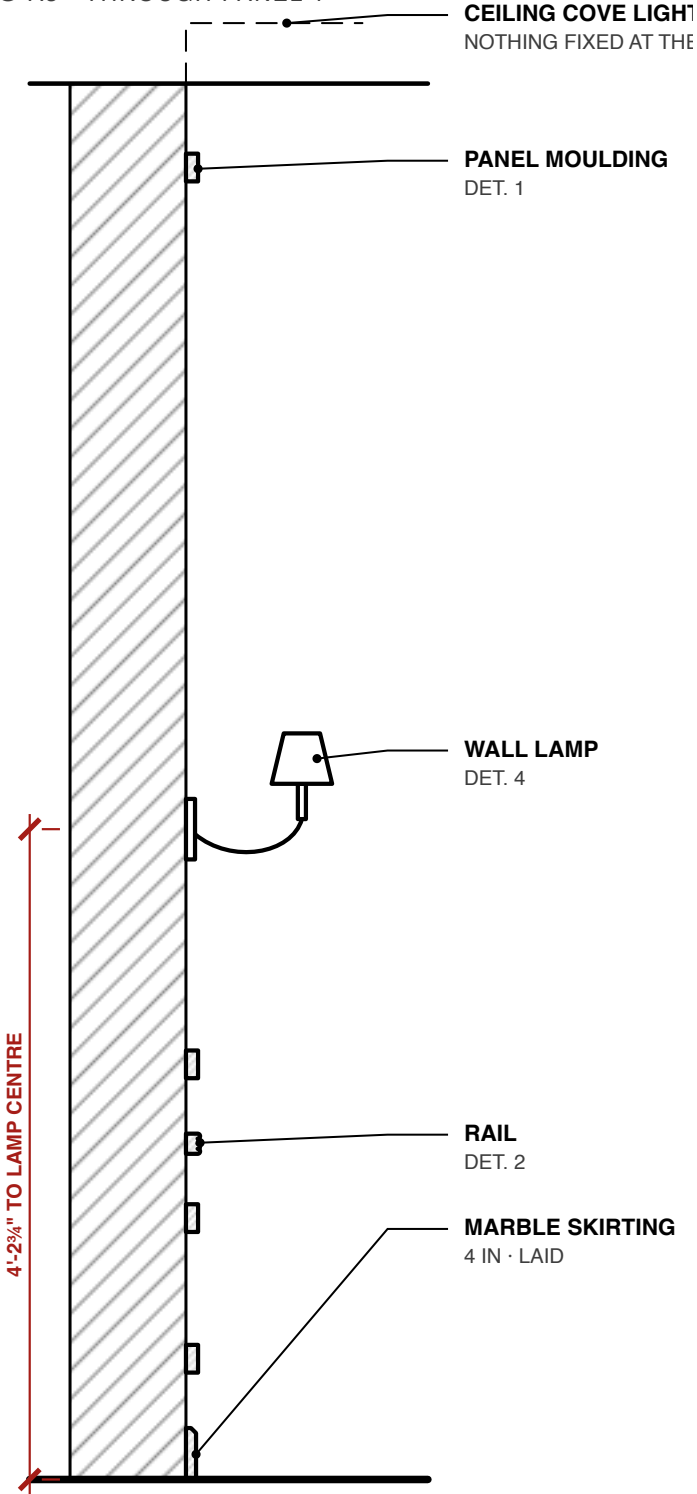

PROJECT
A Study in Teak — Right Wall — Panel Moulding

SHEET
Section A-A
Elevation · Plan · Section · Details

SCALE
1:15 @ A3



DATE
20.09.2026

REV
18

DRAWING
AST-DR-007 · 3 of 9

PLAN

SCALE 1:20 @ A3 · CUT AT 3'-3 3/8" · ROOM BELOW, WALL ABOVE

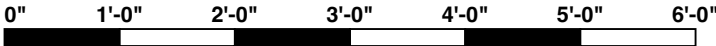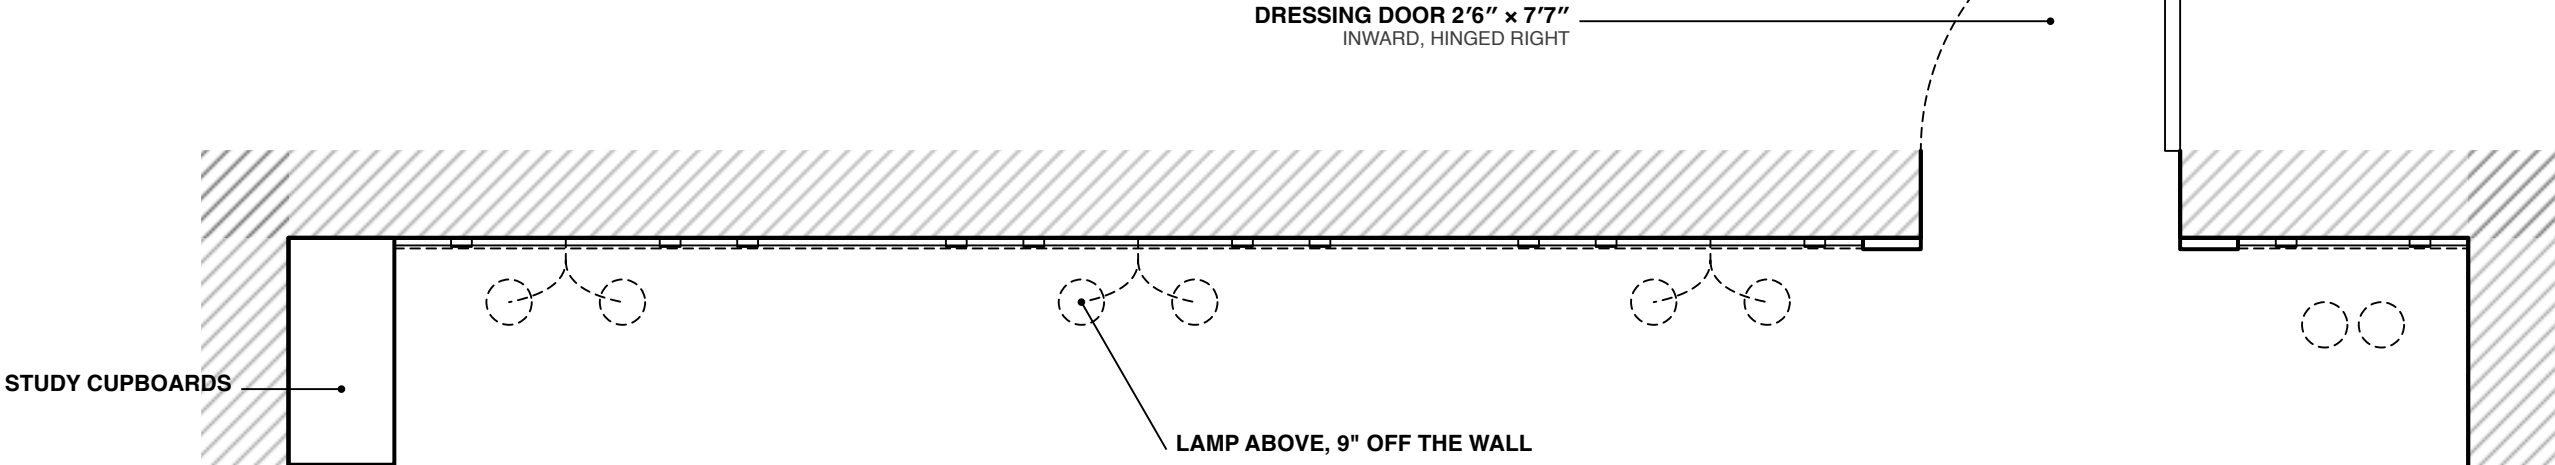

PROJECT
A Study in Teak — Right Wall — Panel Moulding

SHEET
Plan
Elevation · Plan · Section · Details

SCALE
1:20 @ A3

DATE
20.09.2026

REV
18

DRAWING
AST-DR-007 · 4 of 9

NOTES

REVISION 18

Option C: 5 equal panels, lamps in 1, 3, 5 and the return.

One narrow panel on the wall past the door.

Moulding, rail and skirting painted the wall colour.

SELECTED after four schemes: the rail is the study counter

band carried round the corner, and it dies into the casing.

Skirting is white marble, 4 in, already laid.

Casing 2 in lining + 4 in moulding = 6 in, 3'-6" overall;

crown at 8 ft 8 in, and the tall panels stop on that

line, not the leaf head at 7 ft 7 in.

2 ft 4 in corner to frame, measured both sides; leaf 2 ft 3


in a 2 in frame. OPEN: that puts the frame 14 ft 0 from the

study corner, 6 in off the taped 13 ft 6. Retape that end.


PROJECT A Study in Teak — Right Wall — Panel Moulding	SHEET Notes Elevation · Plan · Section · Details	SCALE NTS	DATE 20.09.2026	REV 18	DRAWING AST-DR-007 · 5 of 9
--	--	--------------	--------------------	-----------	--------------------------------

1 · PANEL MOULDING

SCALE 1:1 (FULL SIZE) @ A3 · SECTION

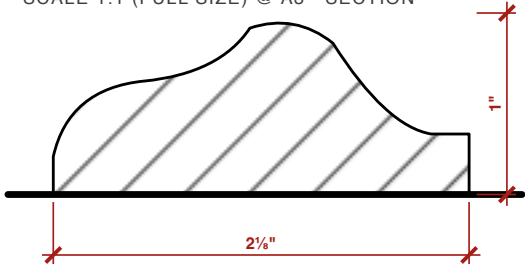

WALL FACE BELOW · MITRED CORNERS

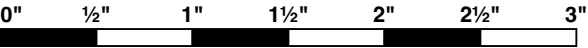

PROJECT
A Study in Teak — Right Wall — Panel Moulding

SHEET
1 · panel moulding
Elevation · Plan · Section · Details

SCALE
1:1 @ A3


DATE
20.09.2026

REV
18


DRAWING
AST-DR-007 · 6 of 9

2 · RAIL

SCALE 1:1 (FULL SIZE) @ A3 · SEC

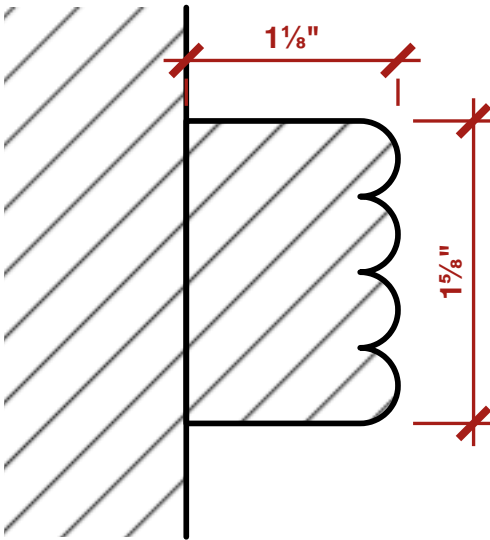

MATCHES THE COUNTER EDGE

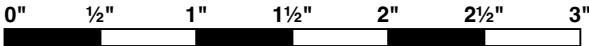

PROJECT
A Study in Teak — Right Wall — Panel Moulding

SHEET
2 · rail
Elevation · Plan · Section · Details

SCALE
1:1 @ A3



DATE
20.09.2026

REV
18

DRAWING
AST-DR-007 · 7 of 9

3 · SKIRTING

SCALE 1:2 (6" = 1'-0") @ A3 · MARBLE · SECTION

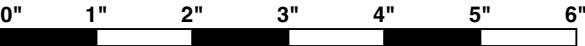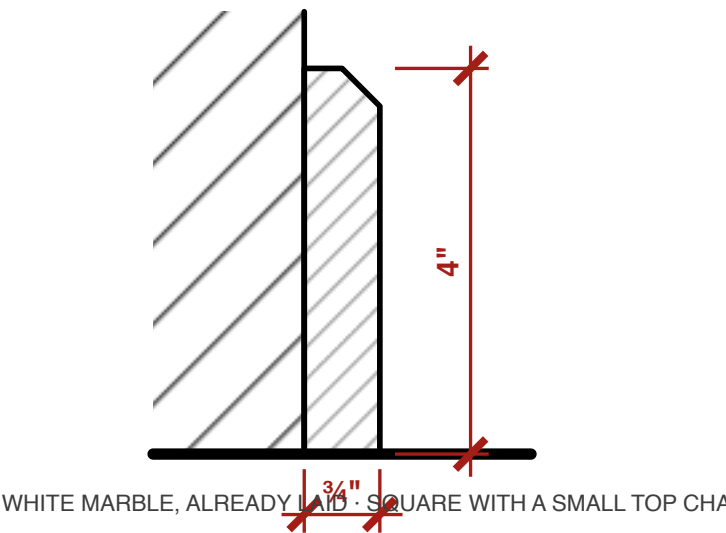

PROJECT
A Study in Teak — Right Wall — Panel Moulding

SHEET
3 · skirting
Elevation · Plan · Section · Details

SCALE
1:2 @ A3


DATE
20.09.2026

REV
18

DRAWING
AST-DR-007 · 8 of 9

4 · WALL LAMP

SCALE 1:4 (3" = 1'-0") @ A3 · ELEVATION · x4

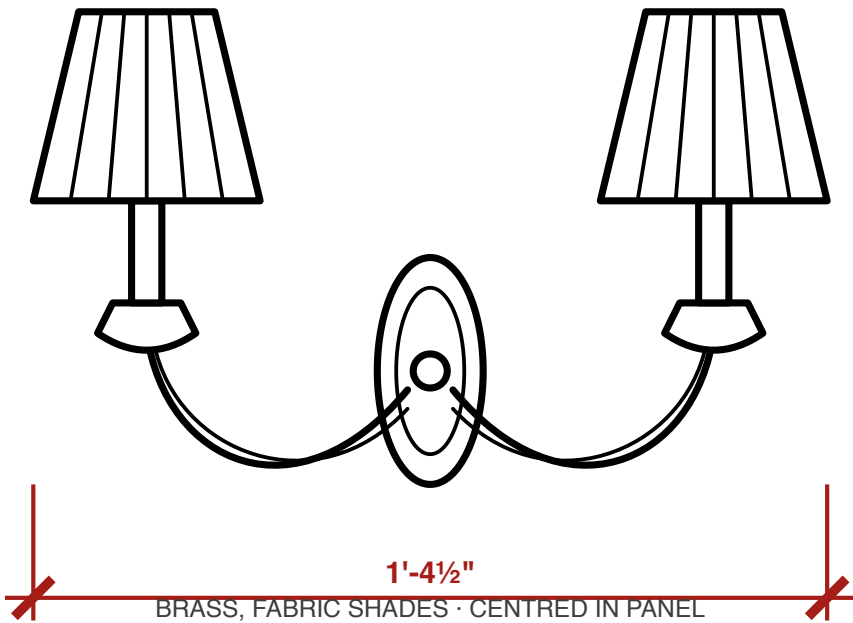

0" 2" 4" 6" 8" 10" 1'-0"

PROJECT
A Study in Teak — Right Wall — Panel Moulding

SHEET
4 · wall lamp
Elevation · Plan · Section · Details

SCALE
1:4 @ A3

DATE
20.09.2026

REV
18

DRAWING
AST-DR-007 · 9 of 9