



ELEVATION — STUDY WALL

BOOKCASE - PANEL FOR PAINTING - WINDOW

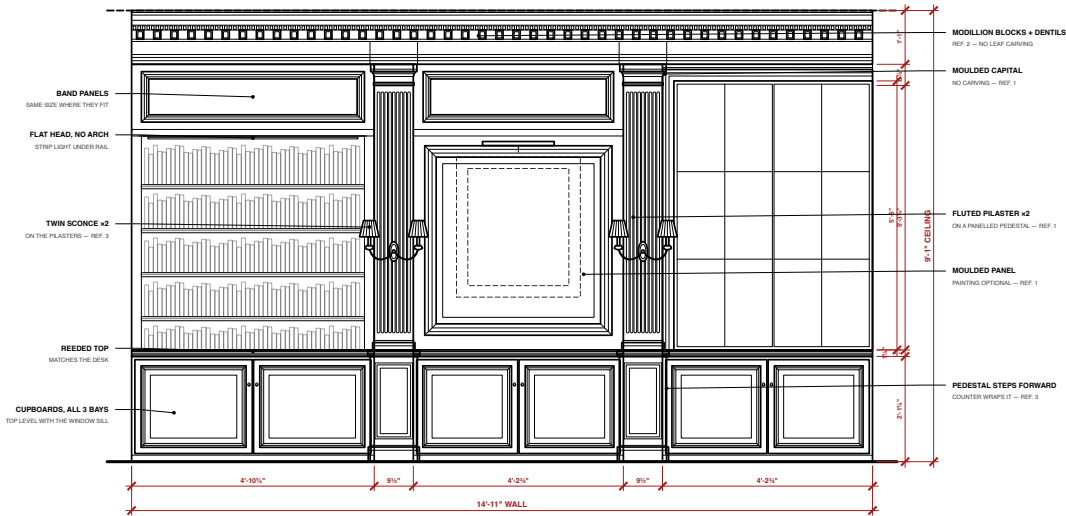


PLAN

CUT AT 3'-11 1/2" - ROOM BELOW, WALL ABOVE

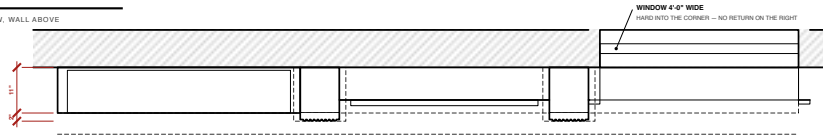

SECTION A-A

THROUGH BOOKCASE

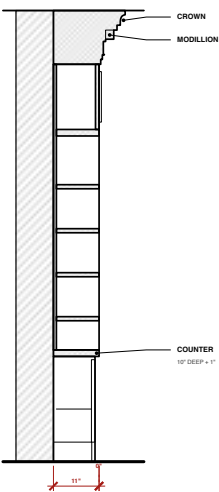

NOTES

REVISION 9

Wall 14 R 11 in, ceiling 9 R 1 in (measured).

Centre panel set equal to the window bay so the two pilasters frame a matched pair; the bookcase takes the remainder as the anchor at the end of the wall.

Window measured: 4 ft wide, 5 ft 5 in tall, hard into the right corner. Sill 2 ft 3 in - CONFIRMED.

OPEN: sill 2 ft 3 in + height 5 ft 5 in + your 1 ft 3 in to the ceiling makes 9 ft 11 in, two inches short of the 9 ft 11 ceiling. Sill and height are drawn as measured, so the head falls 1 ft 5 in down, not 1 ft 5 in. Lower it.

Counter top is set to the sill at 2'-3"; so the two are one surface; this datum runs on round to the right wall rail.

Cupboards under all three bays. Gold on handles only.

A STUDY IN TEAK

Particulars of the room

STUDY WALL — GENERAL ARRANGEMENT

Elevation - Plan - Section

SCALE AS NOTED @ A3	DATE 19.09.2026
REV 9 - sill datum confirmed at 686	DWG AST-DR-005

PROJECT
A Study in Teak — Study Wall — General A...

SHEET
General arrangement — the whole sheet
each view follows at its own scale, pages 2 to 5

SCALE
NTS



DATE
19.09.2026

REV
9

DRAWING
AST-DR-005 · 1 of 14

ELEVATION — STUDY WALL


SCALE 1:30 @ A4 · BOOKCASE · PANEL FOR PAINTING · WINDOW

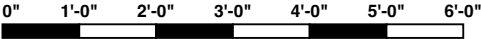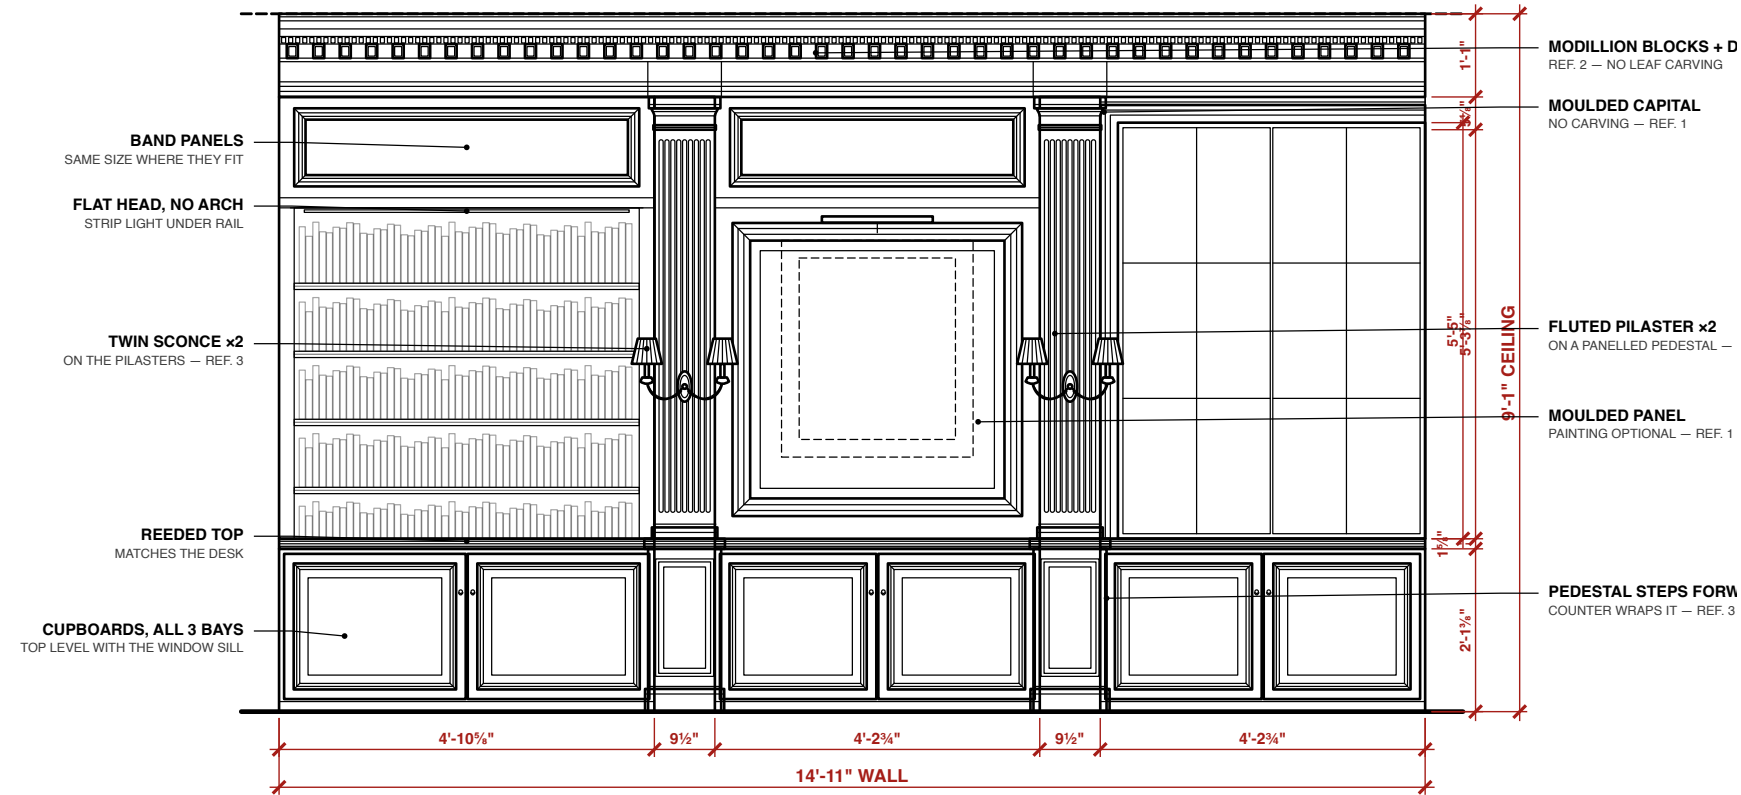

PROJECT	SHEET	SCALE	DATE	REV	DRAWING
A Study in Teak — Study Wall — General A...	Elevation — study wall Elevation · Plan · Section	1:30 @ A4	19.09.2026	9	AST-DR-005 · 2 of 14

SECTION A-A



SCALE 1:24 (1/2" = 1'-0") @ A4 · THROUGH BOOKCASE

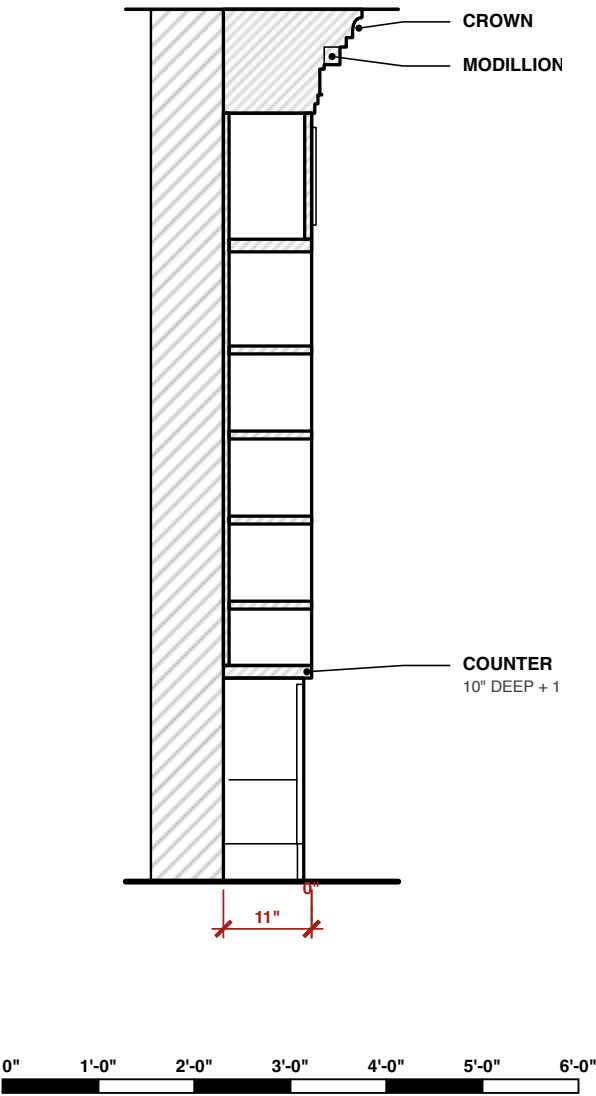

PROJECT	SHEET	SCALE	DATE	REV	DRAWING
A Study in Teak — Study Wall — General A...	Section A-A Elevation · Plan · Section	1:24 @ A4	19.09.2026	9	AST-DR-005 · 3 of 14

PLAN

SCALE 1:24 (1/2" = 1'-0") @ A4 · CUT AT 3'-11 1/4" · ROOM BELOW, WALL ABOVE

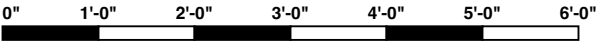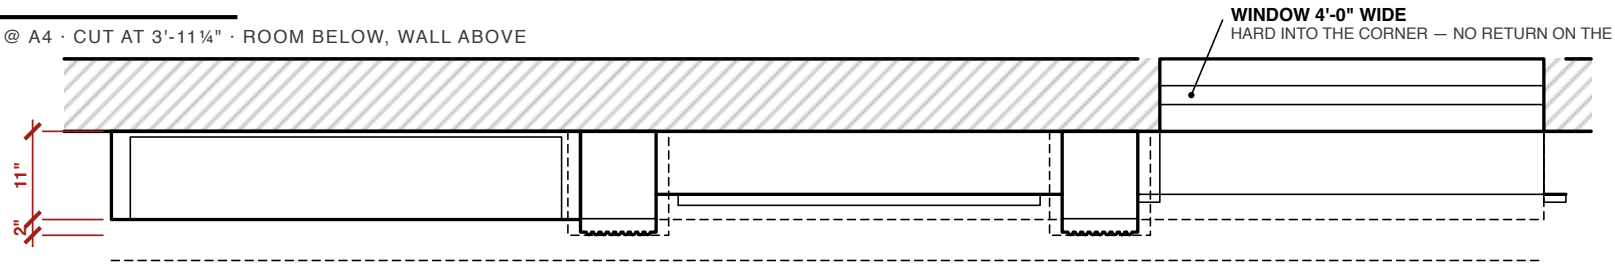

PROJECT
A Study in Teak — Study Wall — General A...

SHEET
Plan
Elevation · Plan · Section

SCALE
1:24 @ A4

DATE
19.09.2026

REV
9

DRAWING
AST-DR-005 · 4 of 14

NOTES

REVISION 9

Wall 14 ft 11 in, ceiling 9 ft 1 in (measured).

Centre panel set equal to the window bay so the two pilasters frame a matched pair; the bookcase takes the remainder as the anchor at the end of the wall.

Window measured: 4 ft wide, 5 ft 5 in tall, hard into the right corner. Sill 2 ft 3 in — CONFIRMED.

OPEN: sill 2 ft 3 + height 5 ft 5 + your 1 ft 3 to the ceiling makes 8 ft 11, two inches short of the 9 ft 1 ceiling. Sill and height are drawn as measured, so the head falls 1 ft 5 down, not 1 ft 3. Laser it.


Counter top is set to the sill at 2'-3", so the two are one surface; this datum runs on round to the right wall rail.

Cupboards under all three bays. Gold on handles only.

PROJECT A Study in Teak — Study Wall — General A...	SHEET Notes Elevation · Plan · Section	SCALE NTS	DATE 19.09.2026	REV 9	DRAWING AST-DR-005 · 5 of 14
--	--	--------------	--------------------	----------	---------------------------------


1 · PILASTER

CAPITAL AND BASE · ELEVATION · REF. 1

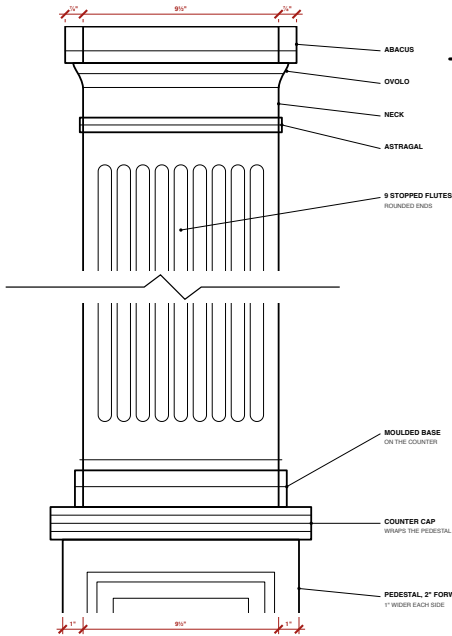


2 · PILASTER SECTION

PLAN

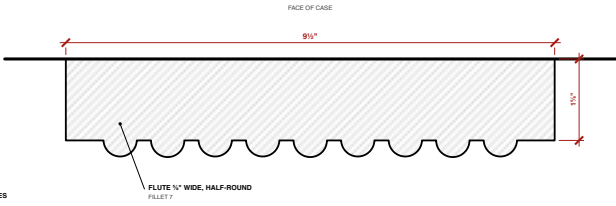


4 · MODILLION + DENTILS

FRONT · PLAIN

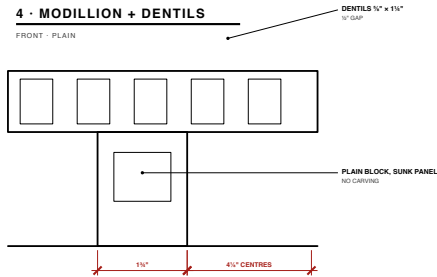


3 · CORNICE

SECTION

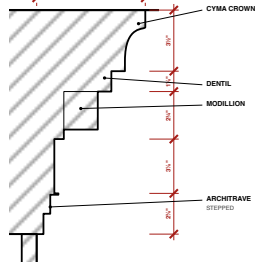


5 · PAINTING PANEL

BOLECTION Moulding · SECTION

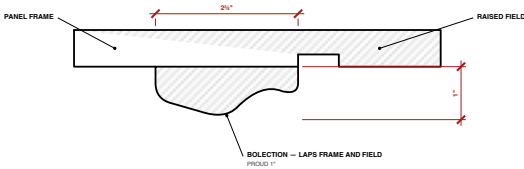


6 · BAND PANEL + SCONCE

ELEVATION · SAME PANEL OVER EVERY BAY

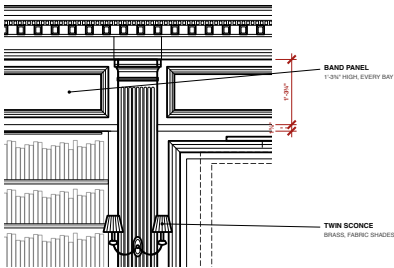

7 · COUNTER EDGE

SECTION · SAME REEDS AS THE DESK

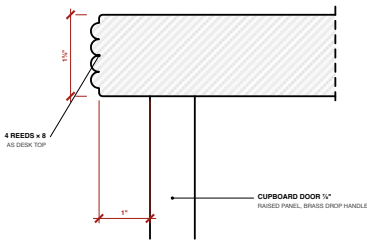

NOTES

DETAILS

No carving on pilasters or modillions — mouldings only.

Flute and modillion spacing to be set out on site as they finish asymmetrically on the wall.

Mock up profiles 3, 5 and 7 full size before cutting.

A STUDY IN TEAK

Particulars of the room

STUDY WALL — DETAILS

Plaster · Cornice · Modillon · Panel · Band · Counter

SCALE

AS NOTED @ A3

DATE

19.09.2026

REV

9 — sill datum confirmed at 686

DWG

AST-DR-006

PROJECT
A Study in Teak — Study Wall — Details

SHEET
General arrangement — the whole sheet
each view follows at its own scale, pages 7 to 14

SCALE
NTS



DATE
19.09.2026

REV
9

DRAWING
AST-DR-006 · 6 of 14

1 · PILASTER

SCALE 1:6 (2" = 1'-0") @ A4 · CAPITAL AND BASE · ELEVATION · REF. 1

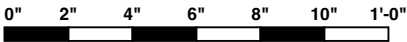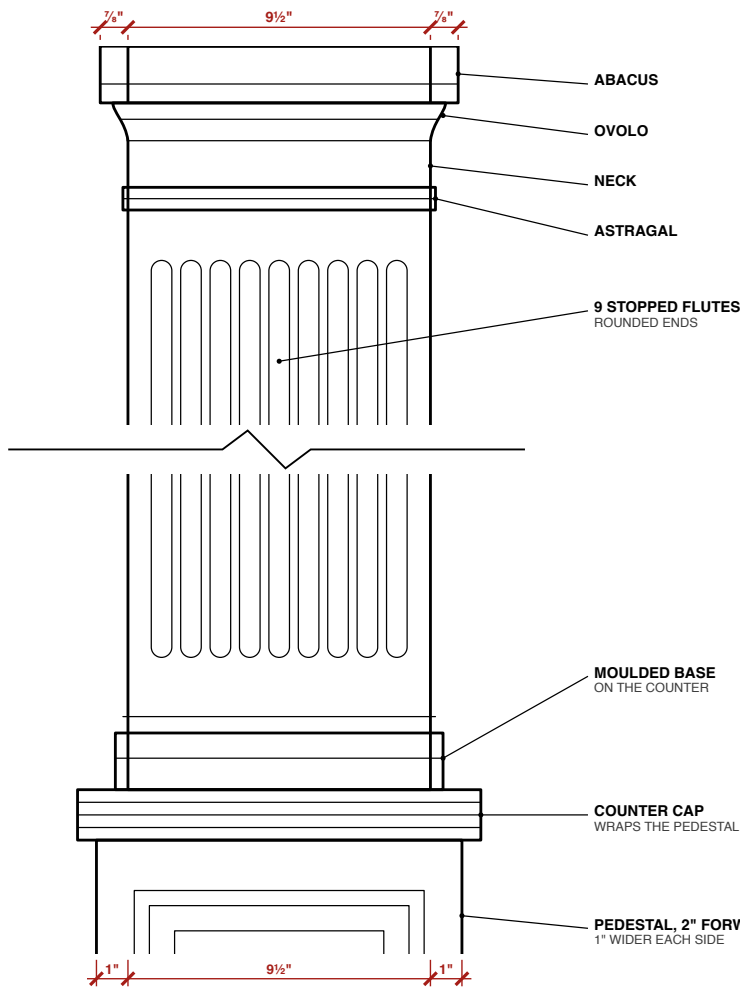

PROJECT
A Study in Teak — Study Wall — Details

SHEET
1 · pilaster
Pilaster · Cornice · Modillion · Panel · Band · Counter

SCALE
1:6 @ A4



DATE
19.09.2026

REV
9

DRAWING
AST-DR-006 · 7 of 14

2 · PILASTER SECTION

SCALE 1:2 (6" = 1'-0") @ A4 · PLAN

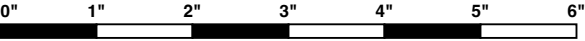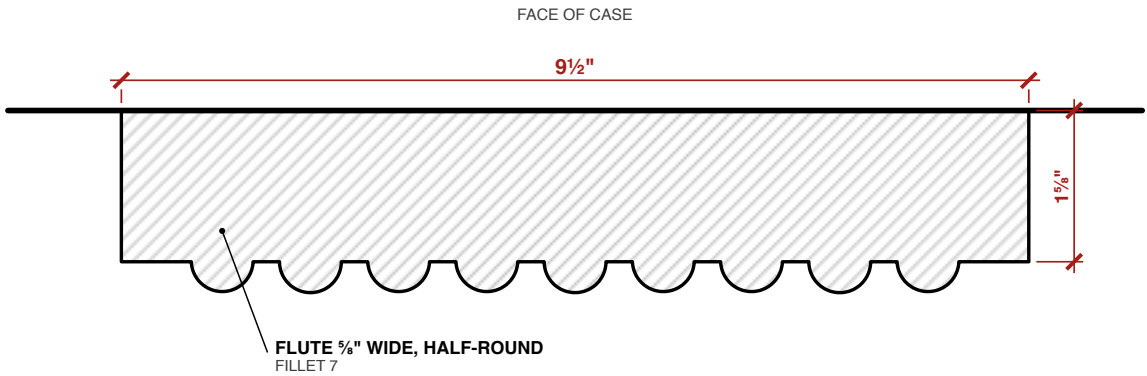

PROJECT
A Study in Teak — Study Wall — Details

SHEET
2 · pilaster section
Pilaster · Cornice · Modillion · Panel · Band · Counter

SCALE
1:2 @ A4


DATE
19.09.2026

REV
9

DRAWING
AST-DR-006 · 8 of 14

3 · CORNICE

SCALE 1:4 (3" = 1'-0") @ A4 · SECTION

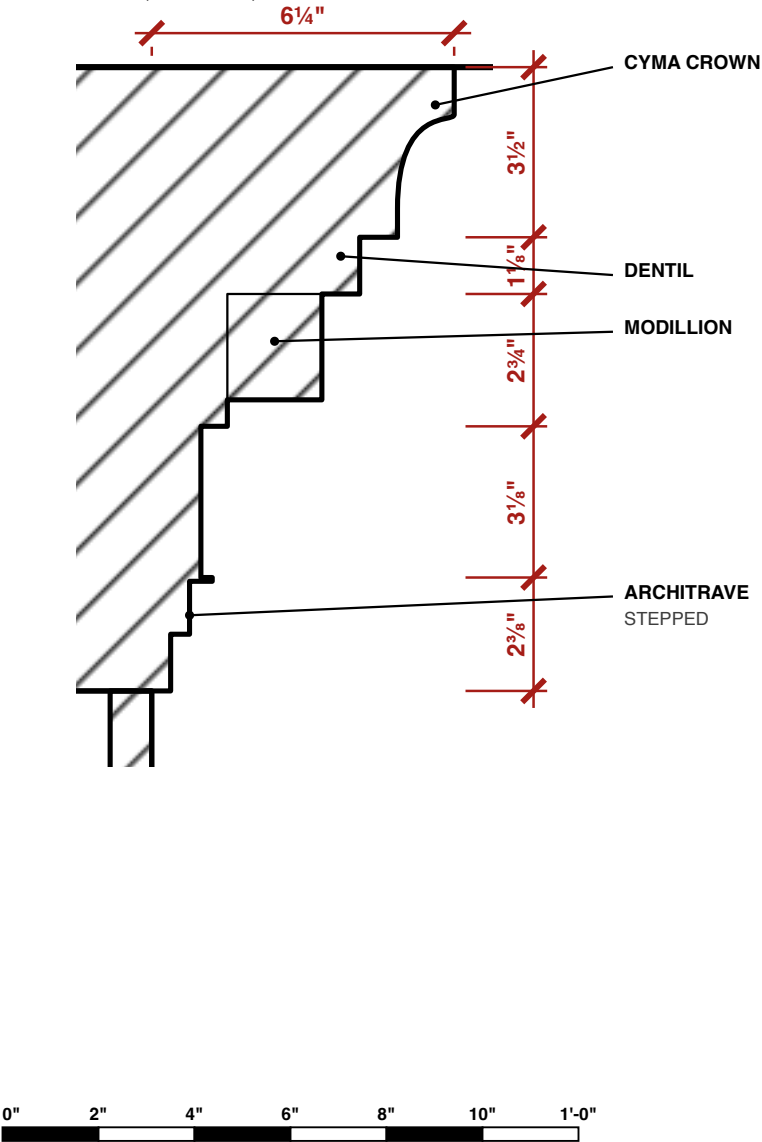

PROJECT
A Study in Teak — Study Wall — Details

SHEET
3 · cornice
Pilaster · Cornice · Modillion · Panel · Band · Counter

SCALE
1:4 @ A4

DATE
19.09.2026


REV
9

DRAWING
AST-DR-006 · 9 of 14

4 · MODILLION + DENTILS

SCALE 1:1 (FULL SIZE) @ A4 · FRONT · PLAIN


DENTILS 5/8" x 1 1/4"
1/2" GAP

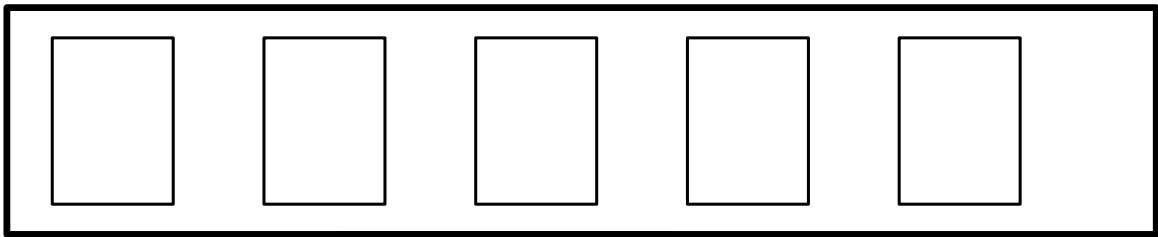

PLAIN BLOCK, SUNK PANEL
NO CARVING

1 3/4"

4 1/8" CENTRES

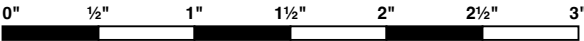

PROJECT
A Study in Teak — Study Wall — Details

SHEET
4 · modillion + dentils
Pilaster · Cornice · Modillion · Panel · Band · Counter

SCALE
1:1 @ A4



DATE
19.09.2026

REV
9

DRAWING
AST-DR-006 · 10 of 14

5 · PAINTING PANEL



SCALE 1:1 (FULL SIZE) @ A4 · BOLECTION MOULDING · SECTION

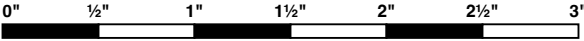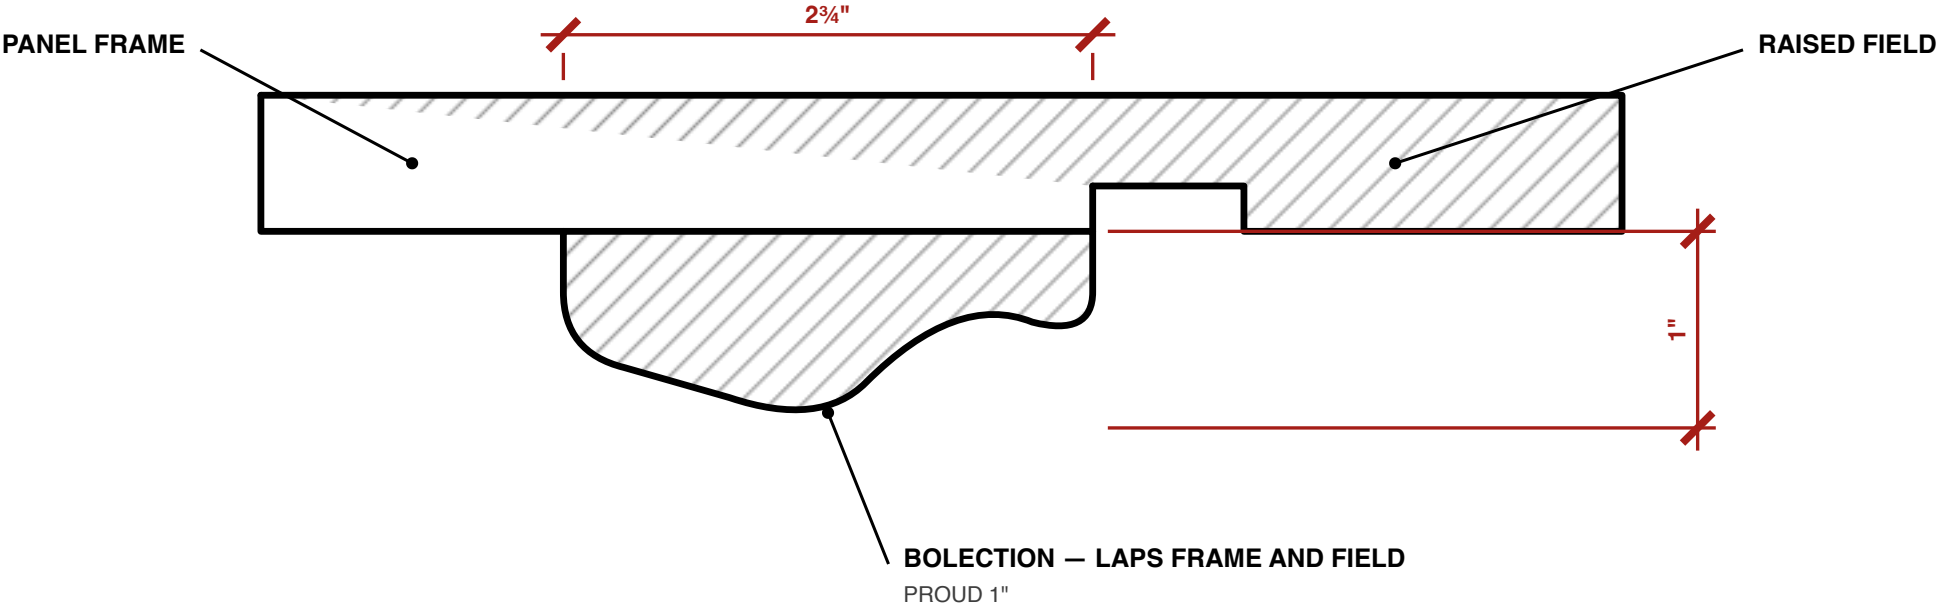

PROJECT	SHEET	SCALE	DATE	REV	DRAWING
A Study in Teak — Study Wall — Details	5 · painting panel Pilaster · Cornice · Modillion · Panel · Band · Counter	1:1 @ A4	19.09.2026	9	AST-DR-006 · 11 of 14

6 · BAND PANEL + SCONCE



SCALE 1:15 @ A4 · ELEVATION · SAME PANEL OVER EVERY BAY

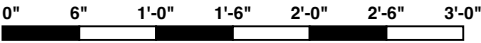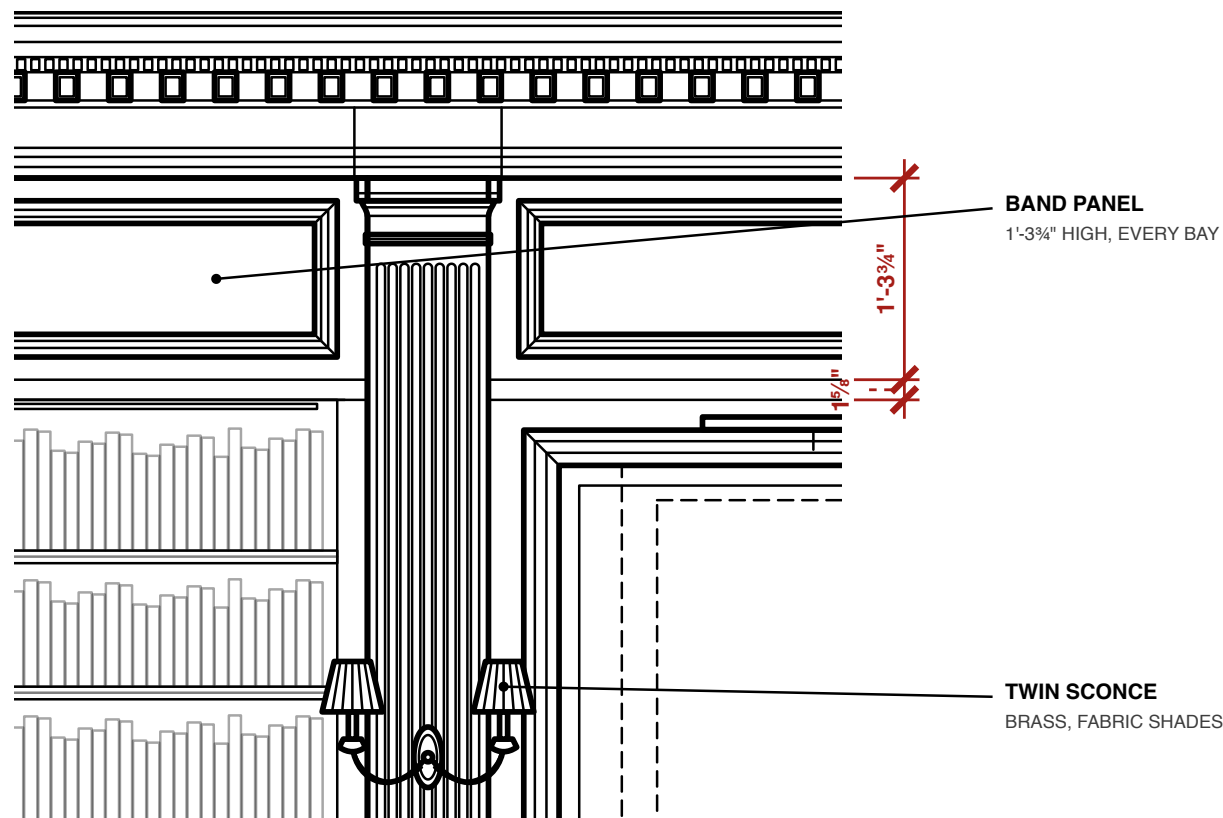

PROJECT	SHEET	SCALE	DATE	REV	DRAWING
A Study in Teak — Study Wall — Details	6 · band panel + sconce Pilaster · Cornice · Modillion · Panel · Band · Counter	1:15 @ A4	19.09.2026	9	AST-DR-006 · 12 of 14

7 · COUNTER EDGE

SCALE 1:2 (6" = 1'-0") @ A4 · SECTION · SAME REEDS AS THE DESK

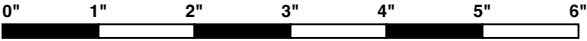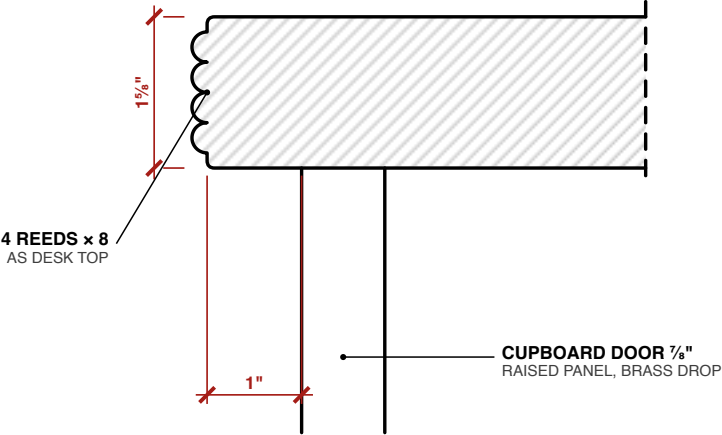

PROJECT
A Study in Teak — Study Wall — Details

SHEET
7 · counter edge
Pilaster · Cornice · Modillion · Panel · Band · Counter

SCALE
1:2 @ A4

DATE
19.09.2026

REV
9

DRAWING
AST-DR-006 · 13 of 14

NOTES

DETAILS

No carving on pilasters or modillions — mouldings only.

Flute and modillion spacing to be set out on site

so they finish symmetrically on the wall.

Mock up profiles 3, 5 and 7 full size before cutting.

PROJECT A Study in Teak — Study Wall — Details	SHEET Notes Pilaster · Cornice · Modillion · Panel · Band · Counter	SCALE NTS	DATE 19.09.2026	REV 9	DRAWING AST-DR-006 · 14 of 14
---	---	--------------	--------------------	----------	----------------------------------