



ELEVATION — STUDY WALL

BOOKCASE · PANEL FOR PAINTING · WINDOW

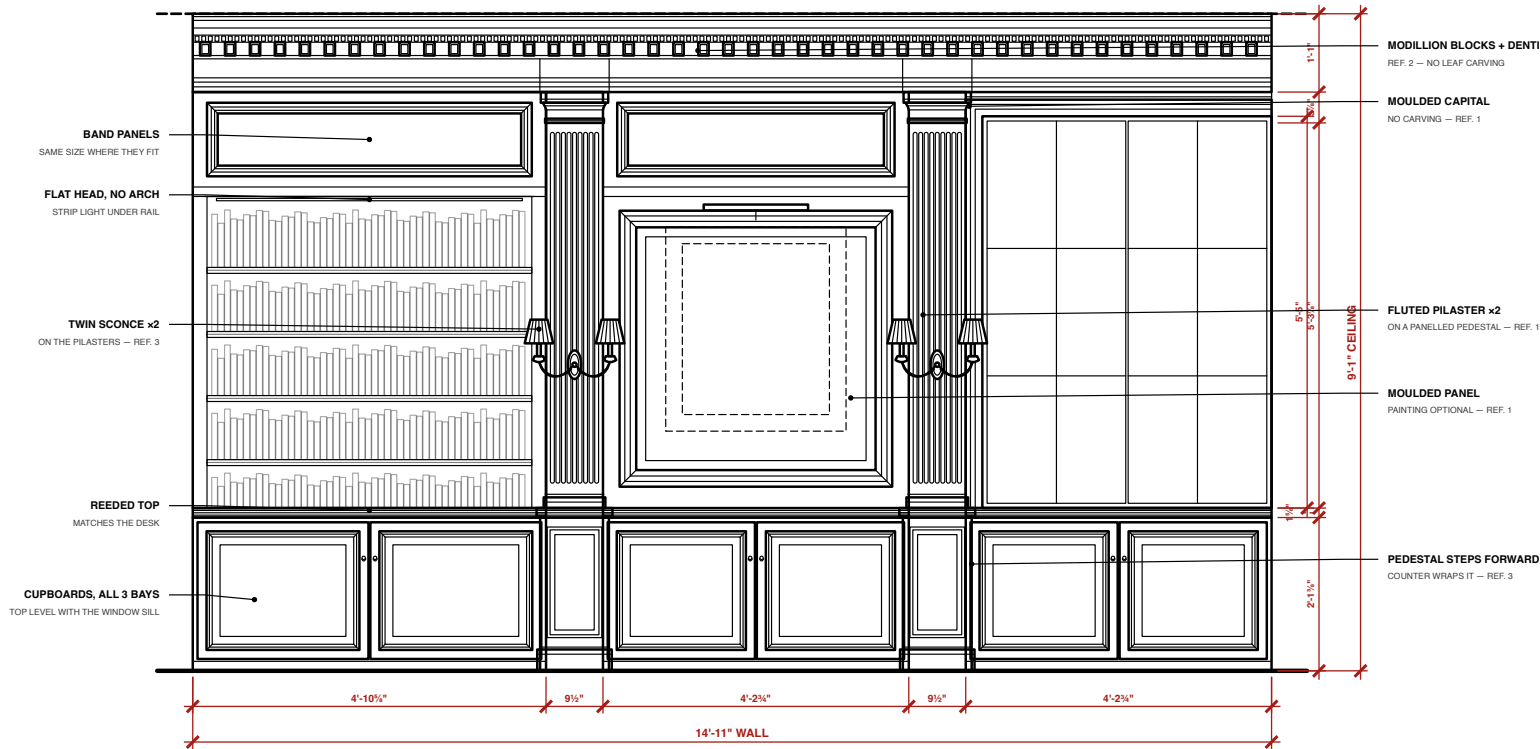


PLAN

CUT AT 3'-11 1/4" · ROOM BELOW, WALL ABOVE

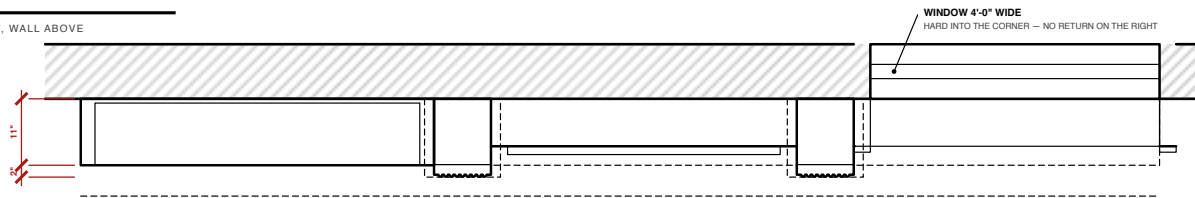

SECTION A-A

THROUGH BOOKCASE

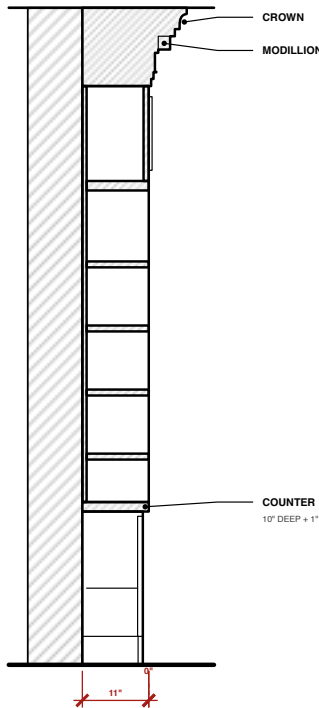

NOTES

REVISION 9

Wall 14 ft 11 in, ceiling 9 ft 1 in (measured).
Centre panel set equal to the window bay so the two pilasters frame a matched pair; the bookcase takes the remainder as the anchor at the end of the wall.
Window measured: 4 ft wide, 5 ft 5 in tall, hard into the right corner. Sill 2 ft 3 in — CONFIRMED.
OPEN: sill 2 ft 3 + height 5 ft 5 + your 1 ft 3 to the ceiling makes 8 ft 11, two inches short of the 9 ft 1 ceiling. Sill and height are drawn as measured, so the head falls 1 ft 5 down, not 1 ft 3. Laser it.
Counter top is set to the sill at 2'-3", so the two are one surface; this datum runs on round to the right wall rail.
Cupboards under all three bays. Gold on handles only.

A STUDY IN TEAK

Particulars of the room

STUDY WALL — GENERAL ARRANGEMENT

Elevation · Plan · Section

SCALE

AS NOTED @ A3

DATE

19.09.2026

REV

9 — sill datum confirmed at 686

DWG

AST-DR-005

PROJECT
A Study in Teak — Study Wall — General Arrange...

SHEET
General arrangement — the whole sheet
each view follows at its own scale, pages 2 to 5

SCALE
NTS



DATE
19.09.2026

REV
9

DRAWING
AST-DR-005 · 1 of 14

ELEVATION — STUDY WALL

SCALE 1:20 @ A3 · BOOKCASE · PANEL FOR PAINTING · WINDOW

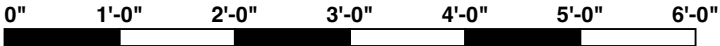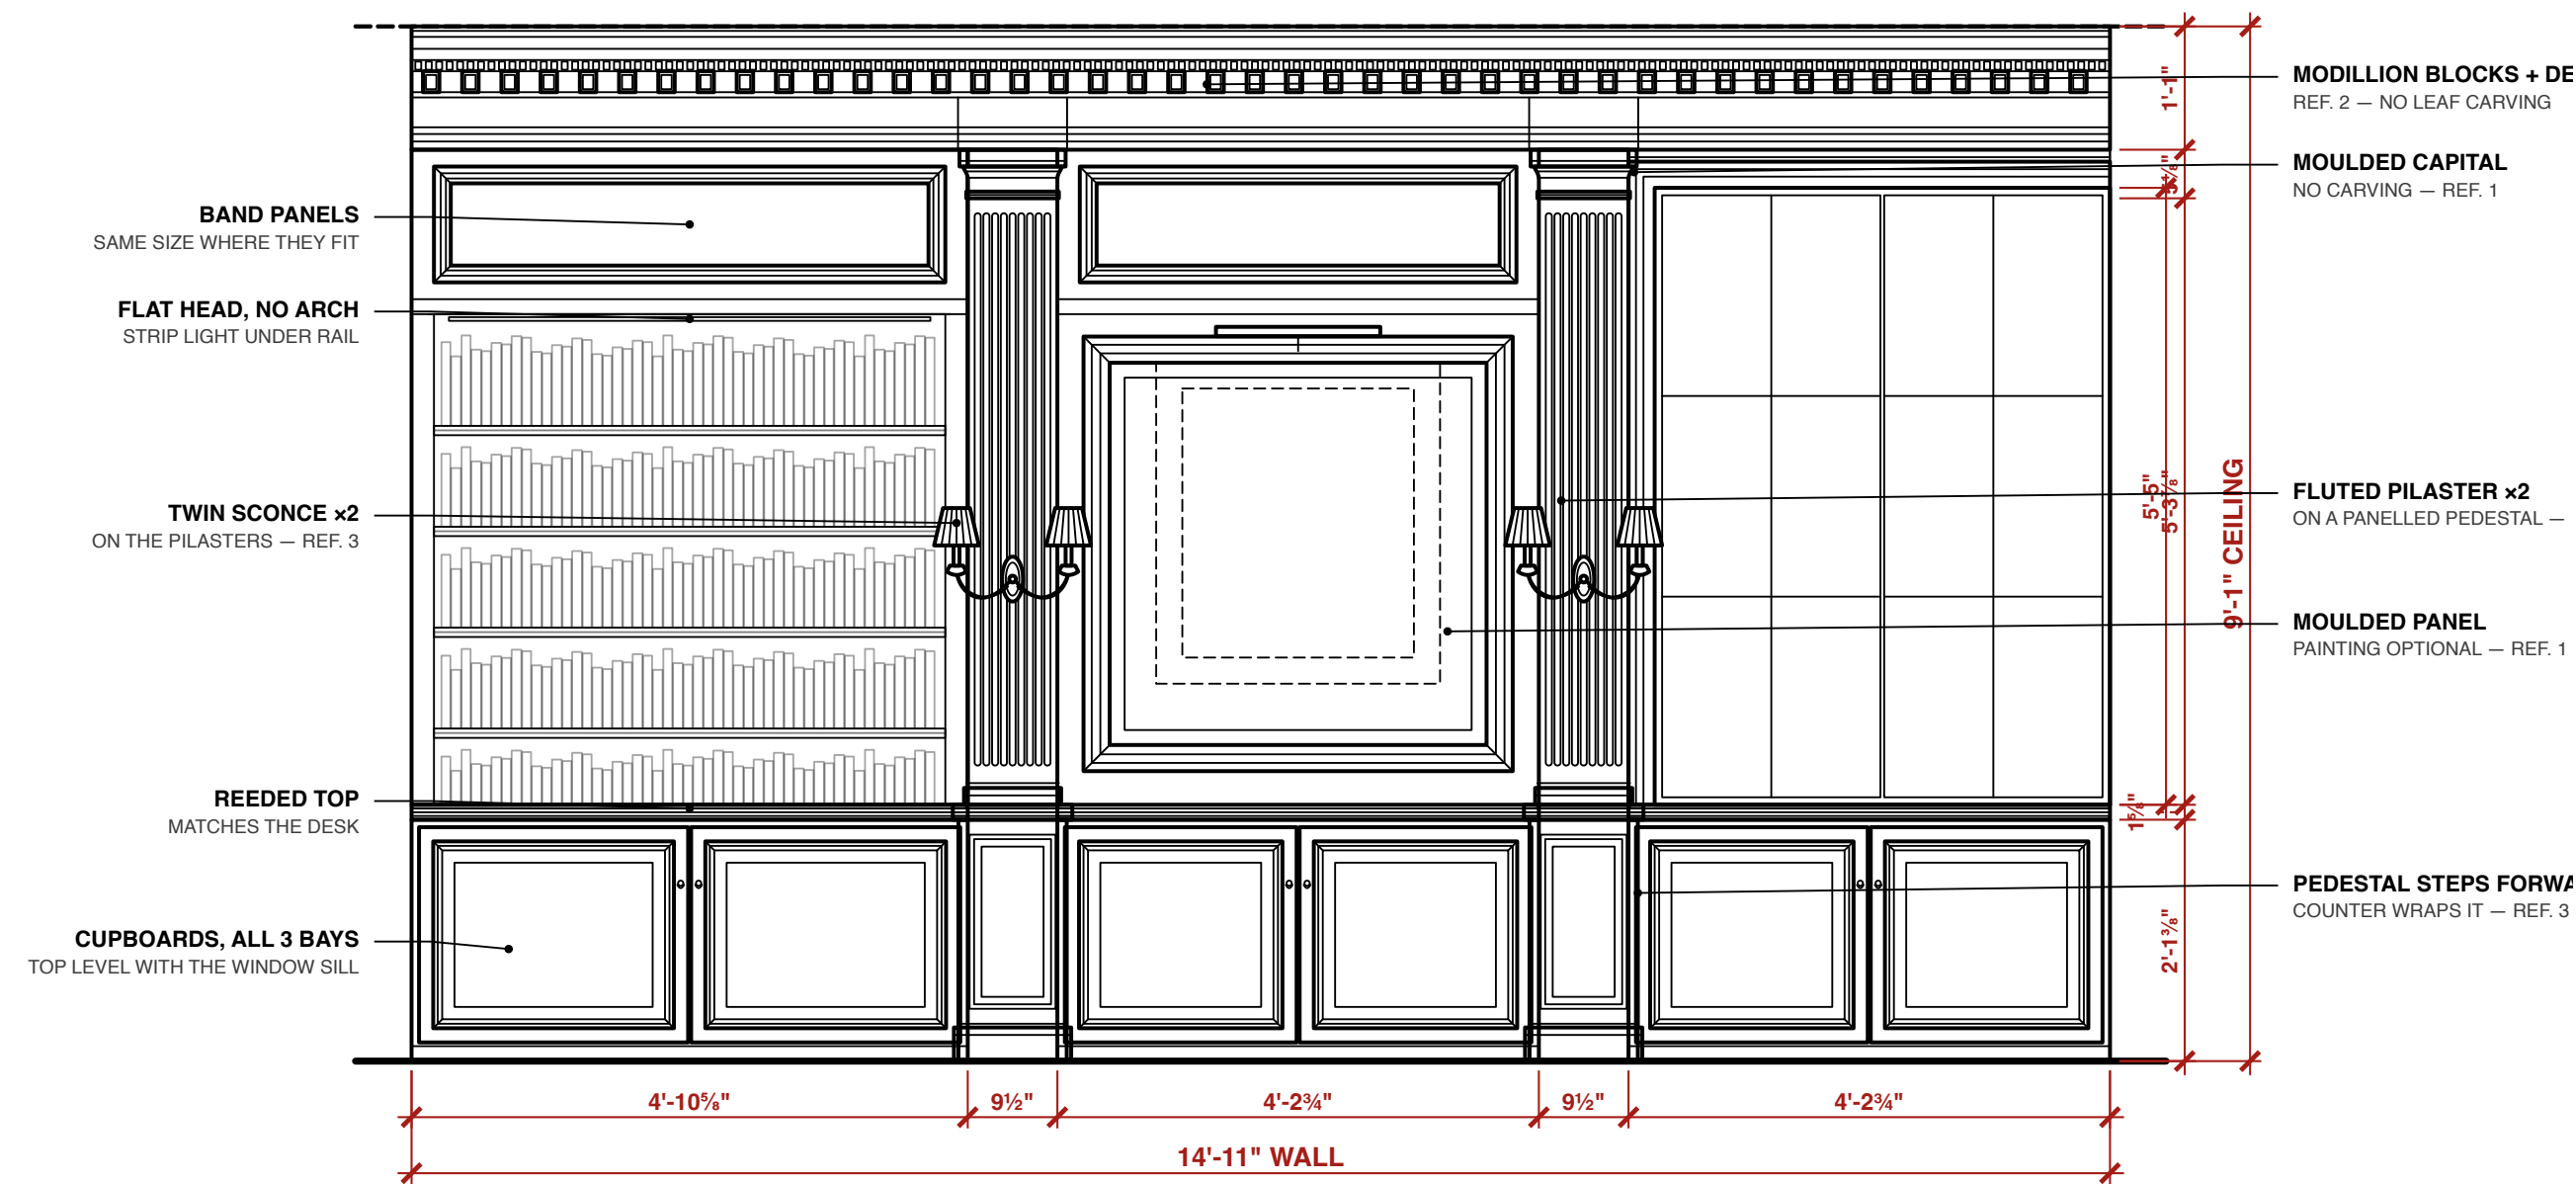

PROJECT
A Study in Teak — Study Wall — General Arrange...

SHEET
Elevation — study wall
Elevation · Plan · Section

SCALE
1:20 @ A3



DATE
19.09.2026

REV
9

DRAWING
AST-DR-005 · 2 of 14

SECTION A–A

SCALE 1:16 (3/4" = 1'-0") @ A3 · THROUGH BOOKCASE

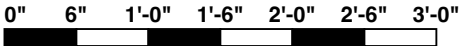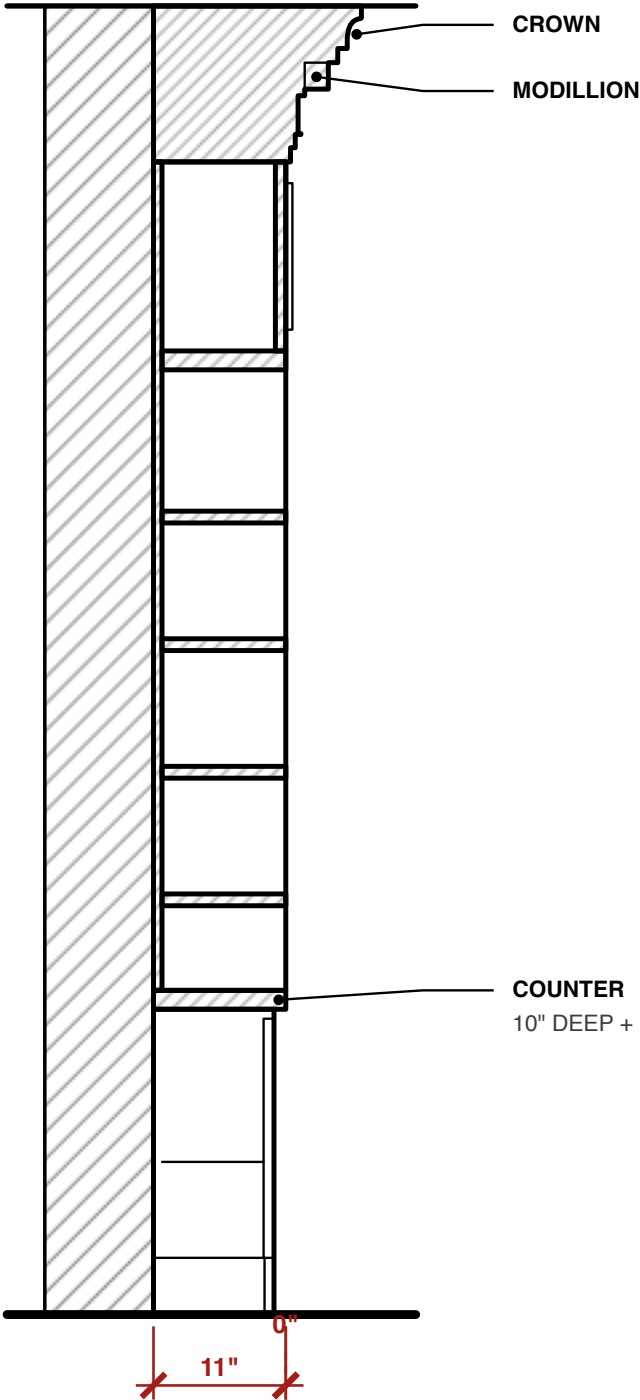

PROJECT
A Study in Teak — Study Wall — General Arrange...

SHEET
Section A–A
Elevation · Plan · Section

SCALE
1:16 @ A3



DATE
19.09.2026

REV
9

DRAWING
AST-DR-005 · 3 of 14

PLAN

SCALE 1:16 (3/4" = 1'-0") @ A3 · CUT AT 3'-11 1/4" · ROOM BELOW, WALL ABOVE

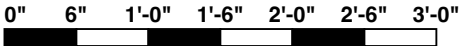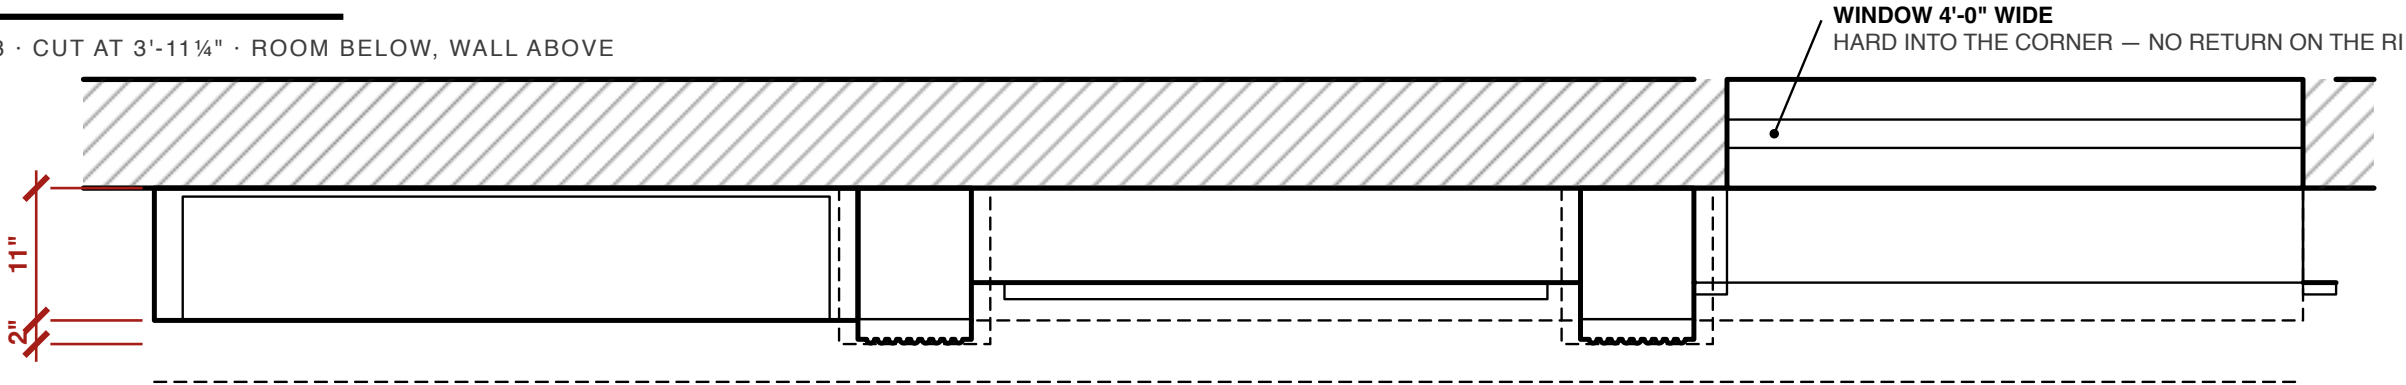

PROJECT
A Study in Teak — Study Wall — General Arrange...

SHEET
Plan
Elevation · Plan · Section

SCALE
1:16 @ A3

DATE
19.09.2026

REV
9

DRAWING
AST-DR-005 · 4 of 14

NOTES

REVISION 9

Wall 14 ft 11 in, ceiling 9 ft 1 in (measured).

Centre panel set equal to the window bay so the two pilasters frame a matched pair; the bookcase takes the remainder as the anchor at the end of the wall.

Window measured: 4 ft wide, 5 ft 5 in tall, hard into the right corner. Sill 2 ft 3 in — CONFIRMED.

OPEN: sill 2 ft 3 + height 5 ft 5 + your 1 ft 3 to the ceiling makes 8 ft 11, two inches short of the 9 ft 1 ceiling. Sill and height are drawn as measured, so the head falls 1 ft 5 down, not 1 ft 3. Laser it.


Counter top is set to the sill at 2'-3", so the two are one surface; this datum runs on round to the right wall rail.

Cupboards under all three bays. Gold on handles only.

PROJECT A Study in Teak — Study Wall — General Arrange...	SHEET Notes Elevation · Plan · Section	SCALE NTS	DATE 19.09.2026	REV 9	DRAWING AST-DR-005 · 5 of 14
--	--	--------------	--------------------	----------	---------------------------------


1 · PILASTER

CAPITAL AND BASE · ELEVATION · REF. 1

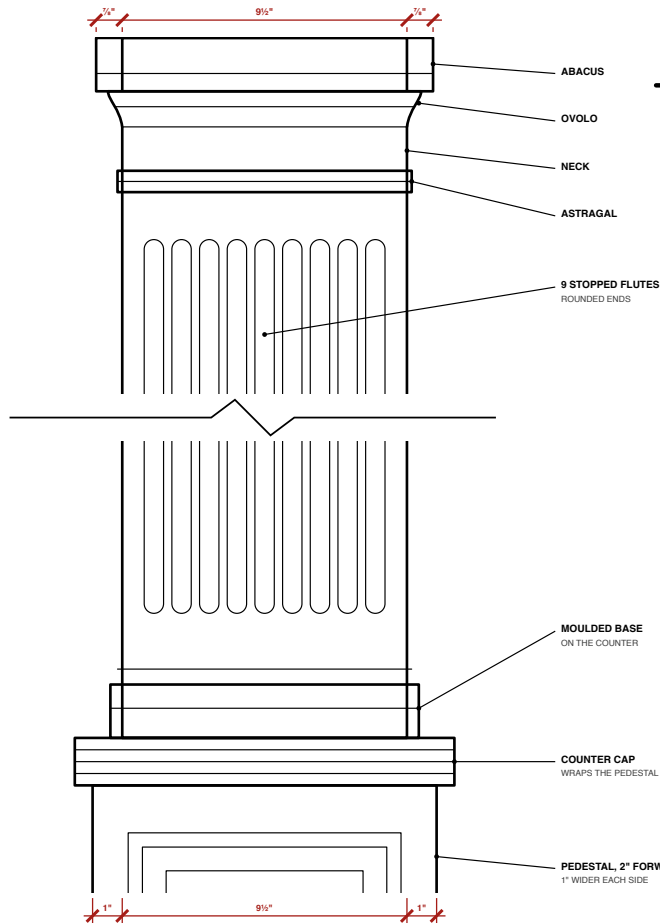


2 · PILASTER SECTION

PLAN

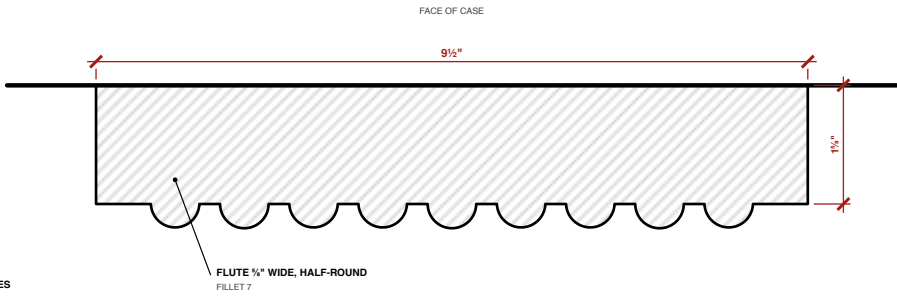


4 · MODILLION + DENTILS

FRONT · PLAIN

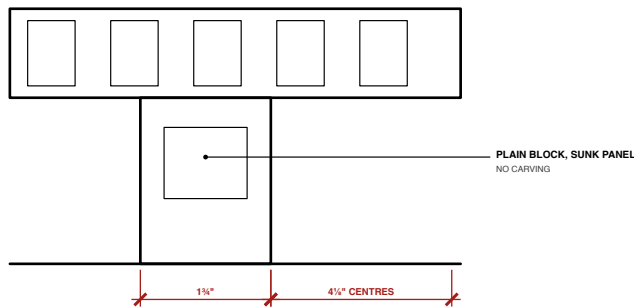


7 · COUNTER EDGE

SECTION · SAME REEDS AS THE DESK

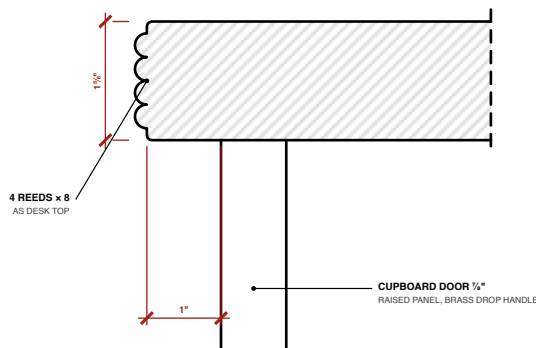


3 · CORNICE

SECTION

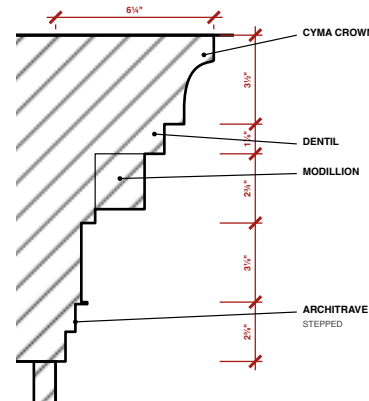

5 · PAINTING PANEL

BOLECTION MOULDING · SECTION

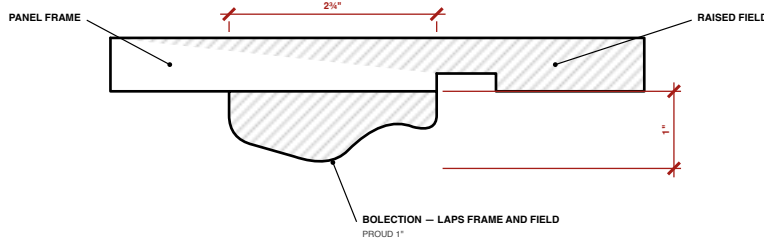

NOTES

DETAILS


No carving on pilasters or modillions — mouldings only.

Flute and modillion spacing to be set out on site
so they finish symmetrically on the wall.

Mock up profiles 3, 5 and 7 full size before cutting.

6 · BAND PANEL + SCONCE

ELEVATION · SAME PANEL OVER EVERY BAY

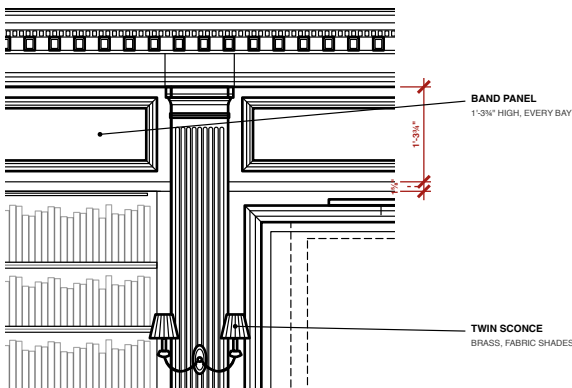

A STUDY IN TEAK

Particulars of the room

STUDY WALL — DETAILS

Pilaster · Cornice · Modillion · Panel · Band · Counter

SCALE

AS NOTED @ A3

DATE

19.09.2026

REV

9 — slll datum confirmed at 686

DWG

AST-DR-006

PROJECT

A Study in Teak — Study Wall — Details

SHEET

General arrangement — the whole sheet

each view follows at its own scale, pages 7 to 14

SCALE

NTS

DATE

19.09.2026

REV



9

DRAWING

AST-DR-006 · 6 of 14

1 · PILASTER

SCALE 1:4 (3" = 1'-0") @ A3 · CAPITAL AND BASE · ELEVATION · REF. 1

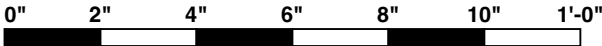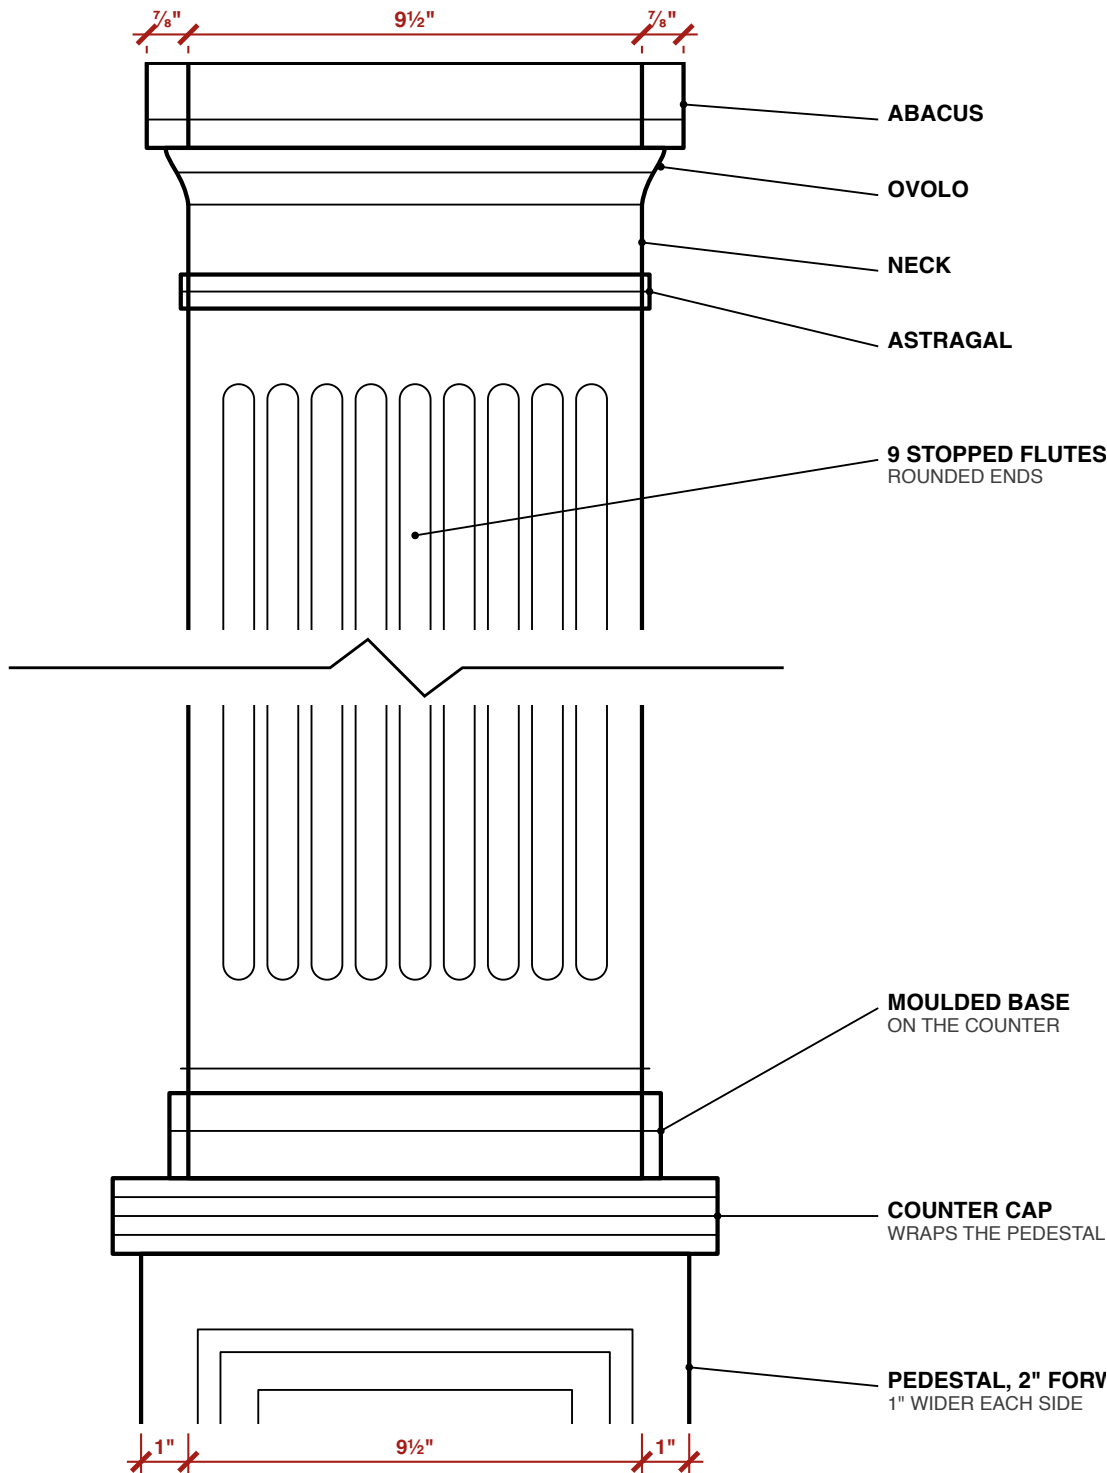

PROJECT
A Study in Teak — Study Wall — Details

SHEET
1 · pilaster
Pilaster · Cornice · Modillion · Panel · Band · Counter

SCALE
1:4 @ A3



DATE
19.09.2026

REV
9

DRAWING
AST-DR-006 · 7 of 14

2 · PILASTER SECTION

SCALE 1:1 (FULL SIZE) @ A3 · PLAN

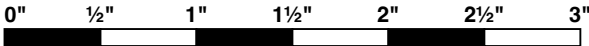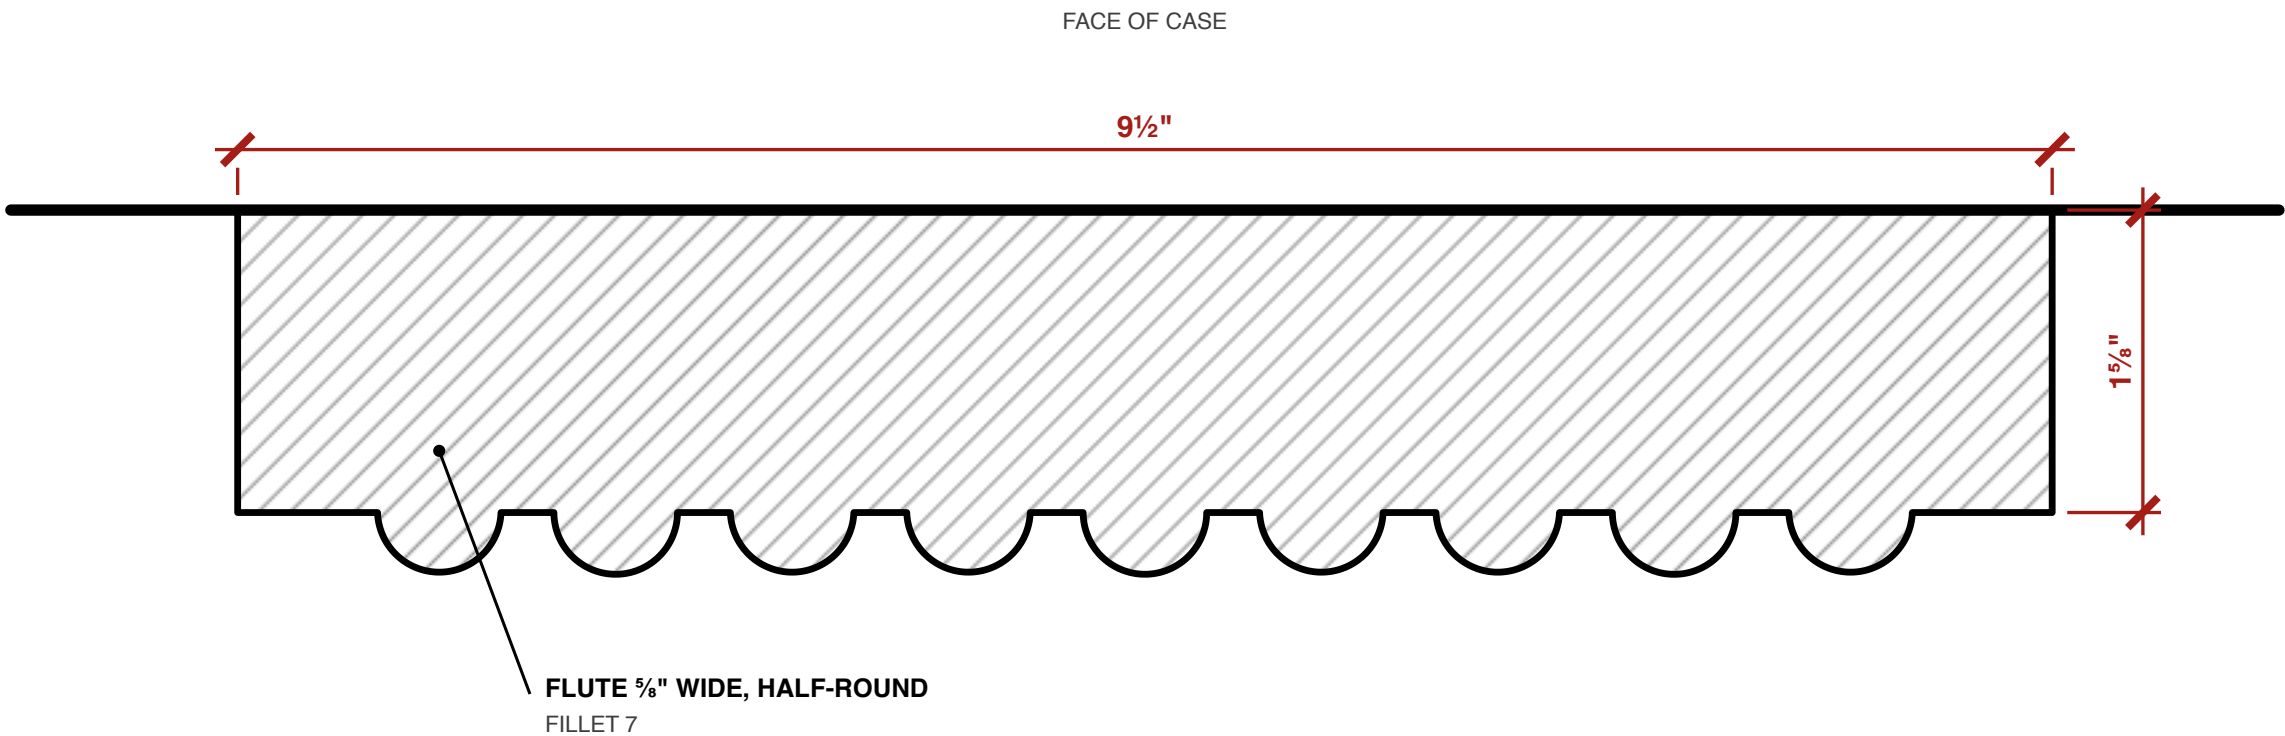

PROJECT
A Study in Teak — Study Wall — Details

SHEET
2 · pilaster section
Pilaster · Cornice · Modillion · Panel · Band · Counter

SCALE
1:1 @ A3



DATE
19.09.2026

REV
9

DRAWING
AST-DR-006 · 8 of 14

3 · CORNICE

SCALE 1:3 (4" = 1'-0") @ A3 · SECTION

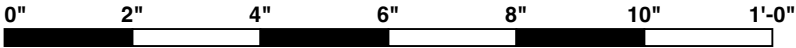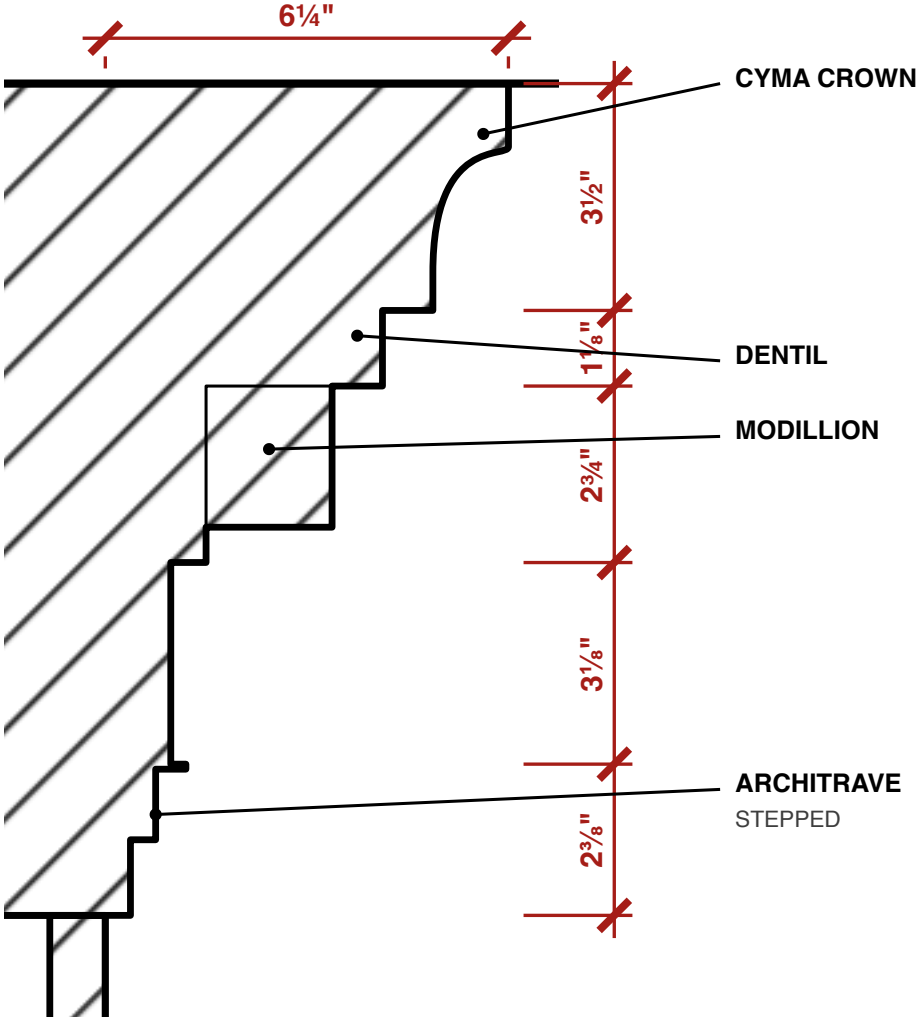

PROJECT
A Study in Teak — Study Wall — Details

SHEET
3 · cornice
Pilaster · Cornice · Modillion · Panel · Band · Counter

SCALE
1:3 @ A3

DATE
19.09.2026


REV
9

DRAWING
AST-DR-006 · 9 of 14


4 · MODILLION + DENTILS

SCALE 1:1 (FULL SIZE) @ A3 · FRONT · PLAIN

DENTILS $\frac{5}{8}$ " x $1\frac{1}{4}$ "
 $\frac{1}{2}$ " GAP

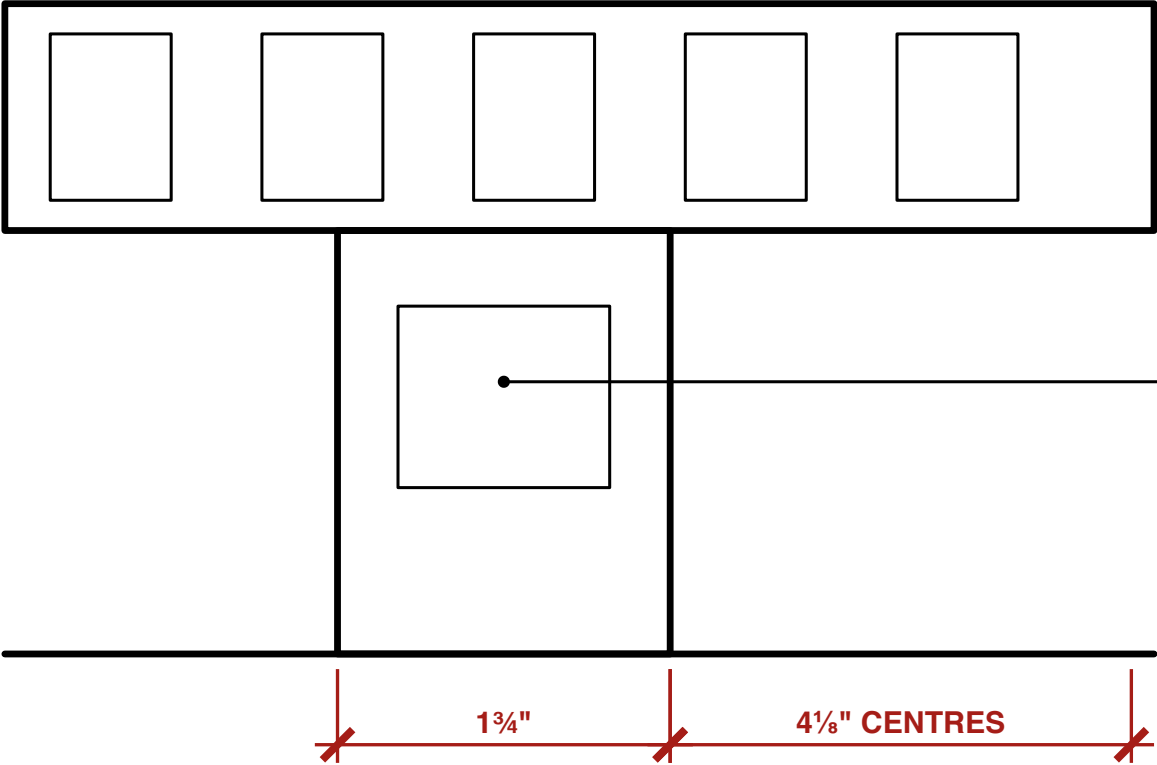

PLAIN BLOCK, SUNK PANEL
NO CARVING

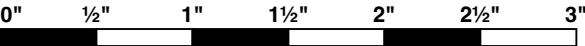

PROJECT
A Study in Teak — Study Wall — Details

SHEET
4 · modillion + dentils
Pilaster · Cornice · Modillion · Panel · Band · Counter

SCALE
1:1 @ A3



DATE
19.09.2026

REV
9

DRAWING
AST-DR-006 · 10 of 14

5 · PAINTING PANEL

SCALE 1:1 (FULL SIZE) @ A3 · BOLECTION MOULDING · SECTION

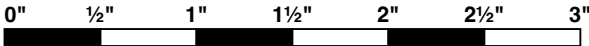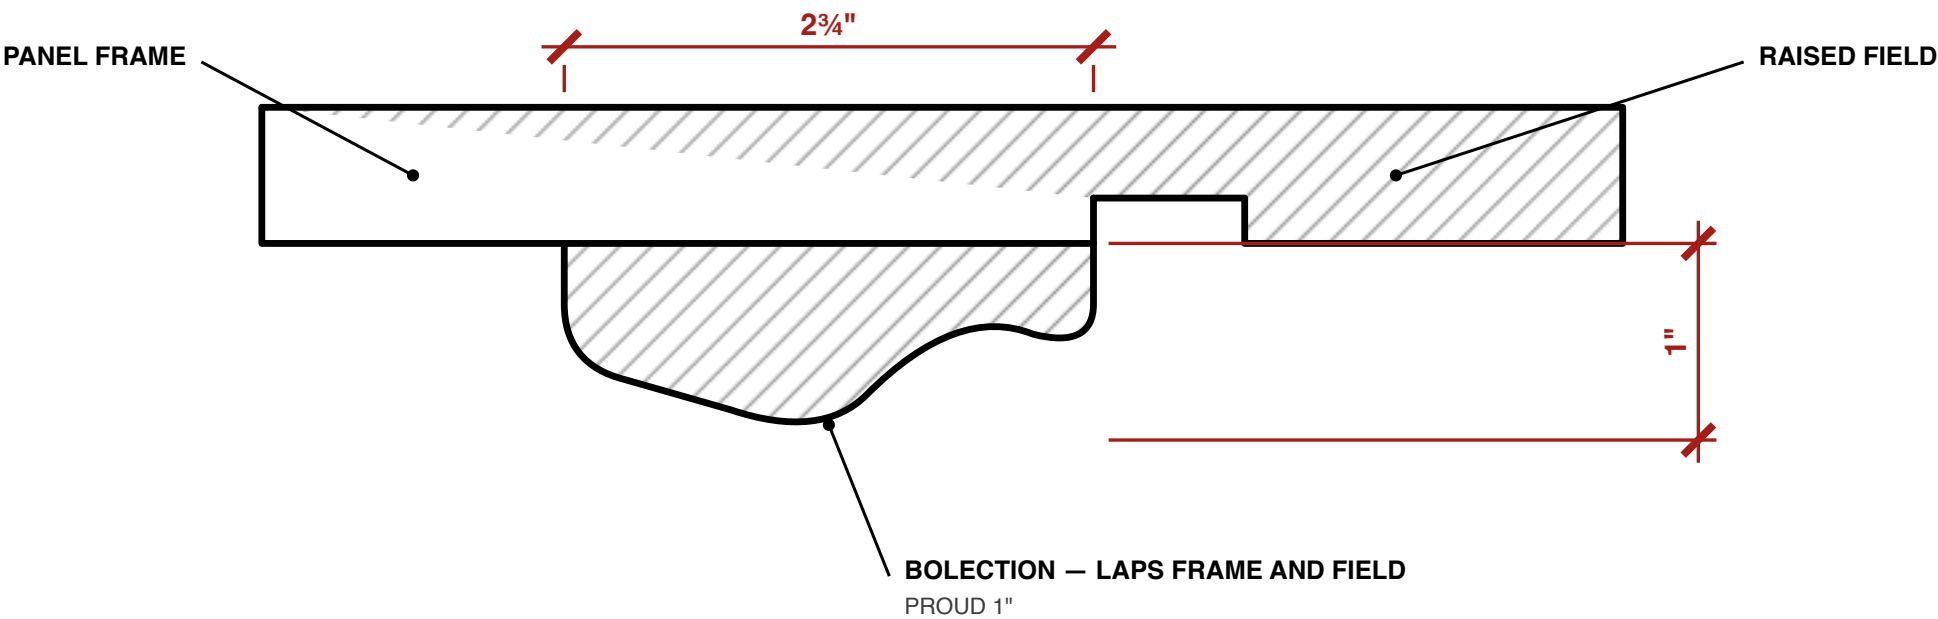

PROJECT
A Study in Teak — Study Wall — Details

SHEET
5 · painting panel
Pilaster · Cornice · Modillion · Panel · Band · Counter

SCALE
1:1 @ A3


DATE
19.09.2026

REV
9

DRAWING
AST-DR-006 · 11 of 14

6 · BAND PANEL + SCONCE

SCALE 1:10 @ A3 · ELEVATION · SAME PANEL OVER EVERY BAY

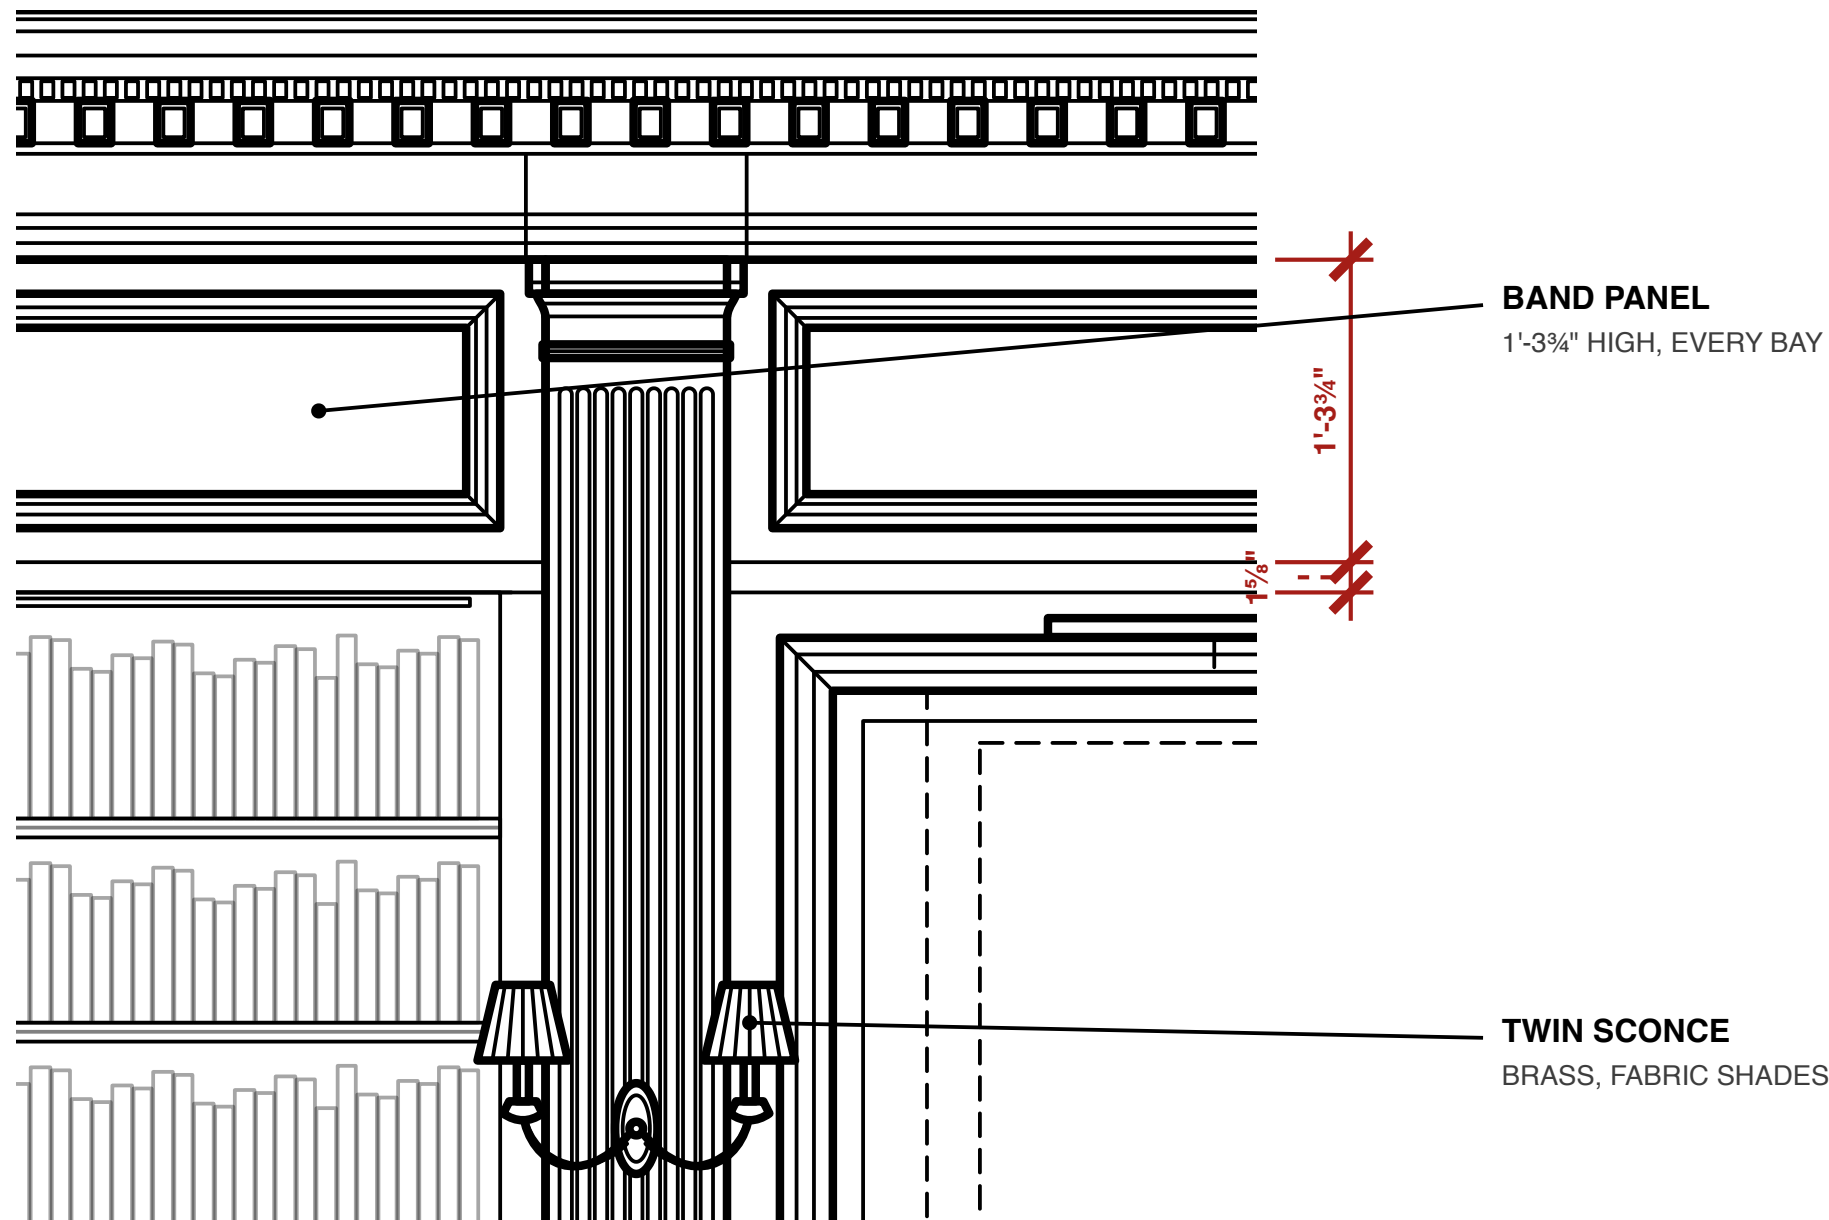

0" 6" 1'-0" 1'-6" 2'-0" 2'-6" 3'-0"

PROJECT
A Study in Teak — Study Wall — Details

SHEET
6 · band panel + sconce
Pilaster · Cornice · Modillion · Panel · Band · Counter

SCALE
1:10 @ A3



DATE
19.09.2026

REV
9

DRAWING
AST-DR-006 · 12 of 14

7 · COUNTER EDGE

SCALE 1:1 (FULL SIZE) @ A3 · SECTION · SAME REEDS AS THE DESK

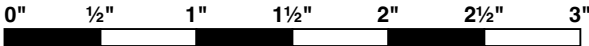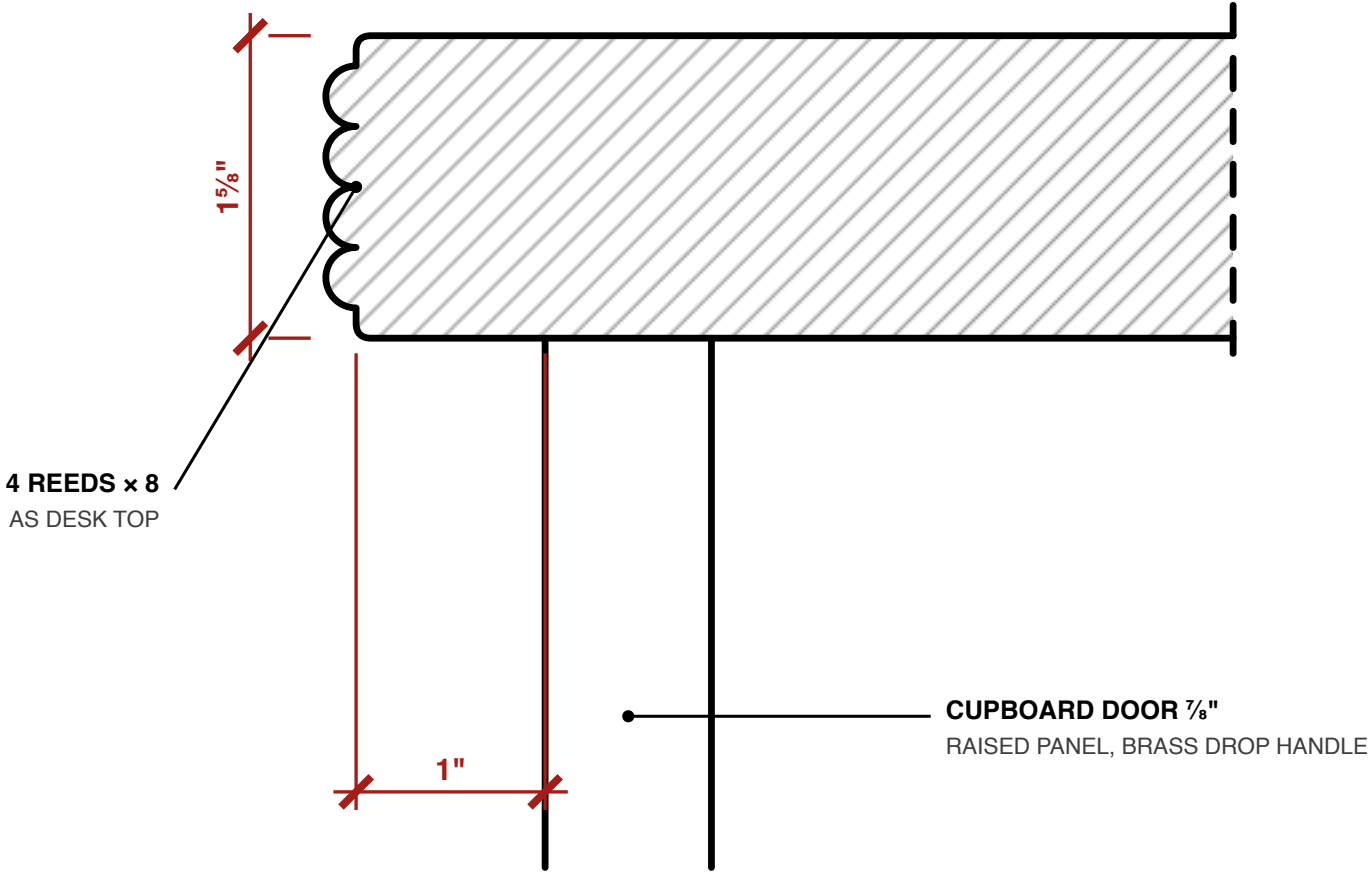

PROJECT
A Study in Teak — Study Wall — Details

SHEET
7 · counter edge
Pilaster · Cornice · Modillion · Panel · Band · Counter

SCALE
1:1 @ A3

DATE
19.09.2026

REV
9

DRAWING
AST-DR-006 · 13 of 14

NOTES

DETAILS

No carving on pilasters or modillions — mouldings only.

Flute and modillion spacing to be set out on site

so they finish symmetrically on the wall.

Mock up profiles 3, 5 and 7 full size before cutting.

PROJECT A Study in Teak — Study Wall — Details	SHEET Notes Pilaster · Cornice · Modillion · Panel · Band · Counter	SCALE NTS	DATE 19.09.2026	REV 9	DRAWING AST-DR-006 · 14 of 14
---	---	--------------	--------------------	----------	----------------------------------