



FRONT

MARBLE THE FULL 5 FT - THE BOWL SITS UNDER THE FAUCET, 6 IN RIGHT OF CENTRE

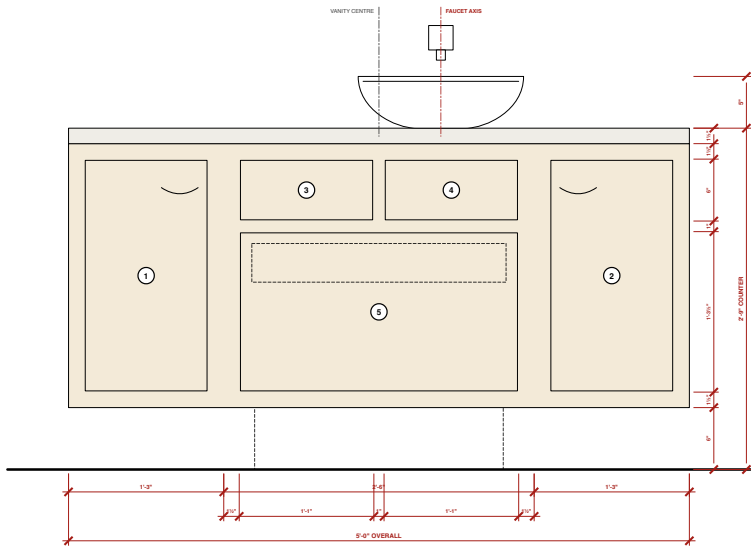

PLAN

FROM ABOVE - WALL AT THE TOP

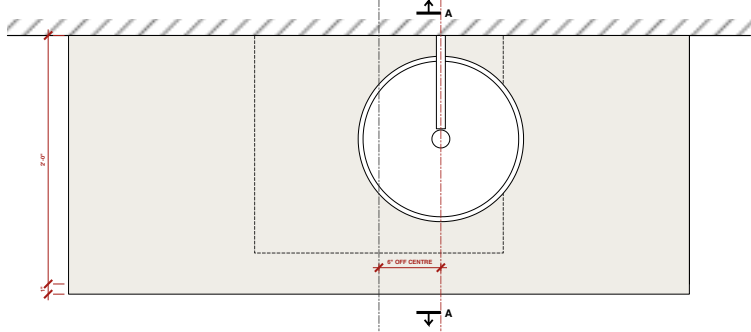

SECTION KEY

- A** Hanging cleat
B Big drawer, U-box
C Waste Ø11" and P-trap
D Support, set back 2"
E Wall support
F Ply sub-top
G Inner drawer


NOTES

REVISION 1
Symmetric about the vanity's centre — except the bowl, which has to sit under the faucet, 6" right of it.
The waste drops through the right-hand TOP drawer as well as the big one: both are U-boxes (see section).

OPEN — bowl Ø11" x 5" and the spout are assumed.
With the bowl on a 2'-0" counter its rim is at 2'-2".
OPEN — the support's design: reference photos to come.


SECTION A-A

ON THE FAUCET AXIS

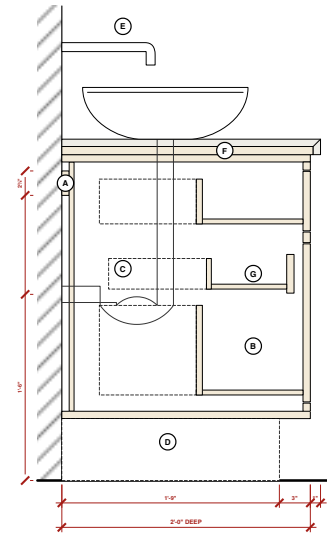


DETAIL 2 - THE BIG DRAWER

PLAN - INNER DRAWER DASHED

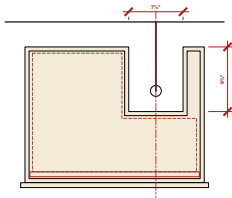

DETAIL 1 - THE MARBLE EDGE

SECTION

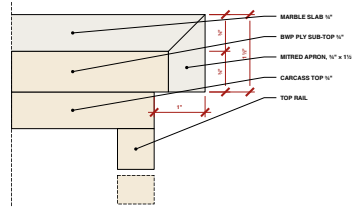

FRONTS

SIZES ARE THE FRONT ITSELF - 1/4" GAP ALL ROUND

No.	DETAIL	W x H	FT-IN
1	Door, cup pull	11 1/2" x 1'-0 1/2"	11 1/2" x 1'-0 1/2"
2	Door, cup pull	11 1/2" x 1'-0 1/2"	11 1/2" x 1'-0 1/2"
3	Top drawer, push-open	1'-0 1/2" x 5 1/2"	1'-0 1/2" x 5 1/2"
4	Top drawer, push-open	1'-0 1/2" x 5 1/2"	1'-0 1/2" x 5 1/2"
5	Big drawer, U-box, push-open	2'-0 1/2" x 1'-0 1/2"	2'-0 1/2" x 1'-0 1/2"
5a	Inner drawer, finger scoop	2'-0 1/2" x 3 1/2"	2'-0 1/2" x 3 1/2"

MATERIALS

THE ROOM'S PALETTE — NOTHING NEW

Top Ridge-gold marble, the bathroom stone, 1 1/2" slab on a 1/2" BWP sub-top, mitred 1 1/2" apron, polished.
Carcass 1/2" BWP / marine ply, tank veneer both faces. Every edge sealed — 3 stands in a wet room.
Fronts 1/2" BWP, tank veneer, 1/2" solid tank lipping.
Runners Undermount, full extension. Drawers push-to-open — no handles on them: the doors keep cup pulls.
Fittings Chrome — already bought. Door cup pulls to match.
Hanging 1/2" ply cleat on the wall, 2'-0 1/2" - 2'-0 1/2" high.
Inter A U-box on its own runners, above the big drawer's low sides — see AST-DR-022.

A STUDY IN TEAK

Particulars of the room

VANITY — NORMAL

Marble full length · Door · Drawers · Door

SCALE AS NOTED @ A3	DATE 23.09.2026
REV 1 — as sketched	DWG AST-DR-019

PROJECT

A Study in Teak — Vanity — Normal

SHEET

General arrangement — the whole sheet

each view follows at its own scale, pages 2 to 10

SCALE

NTS

DATE

23.09.2026


REV

1

DRAWING

AST-DR-019 · 1 of 10



SCALE 1:10 @ A4 · MARBLE THE FULL 5 FT · THE BOWL SITS UNDER THE FAUCET, 6 IN RIGHT OF CENTRE

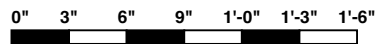

PROJECT	SHEET	SCALE	DATE	REV	DRAWING
A Study in Teak — Vanity — Normal	Front Marble full length · Door · Drawers · Door	1:10 @ A4	23.09.2026	1	AST-DR-019 · 2 of 10

SECTION A-A

SCALE 1:10 @ A4 · ON THE FAUCET AXIS

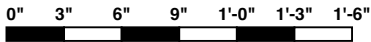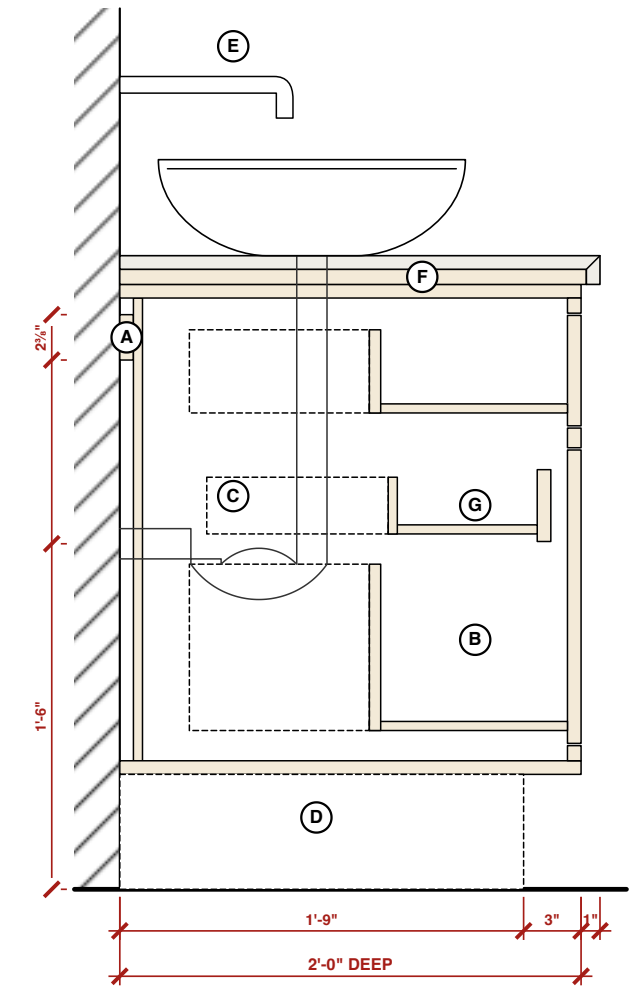

PROJECT
A Study in Teak — Vanity — Normal

SHEET
Section A-A
Marble full length · Door · Drawers · Door

SCALE
1:10 @ A4


DATE
23.09.2026

REV
1

DRAWING
AST-DR-019 · 3 of 10

DETAIL 1 · THE MARBLE EDGE

SCALE 1:1 (FULL SIZE) @ A4 · SECTION

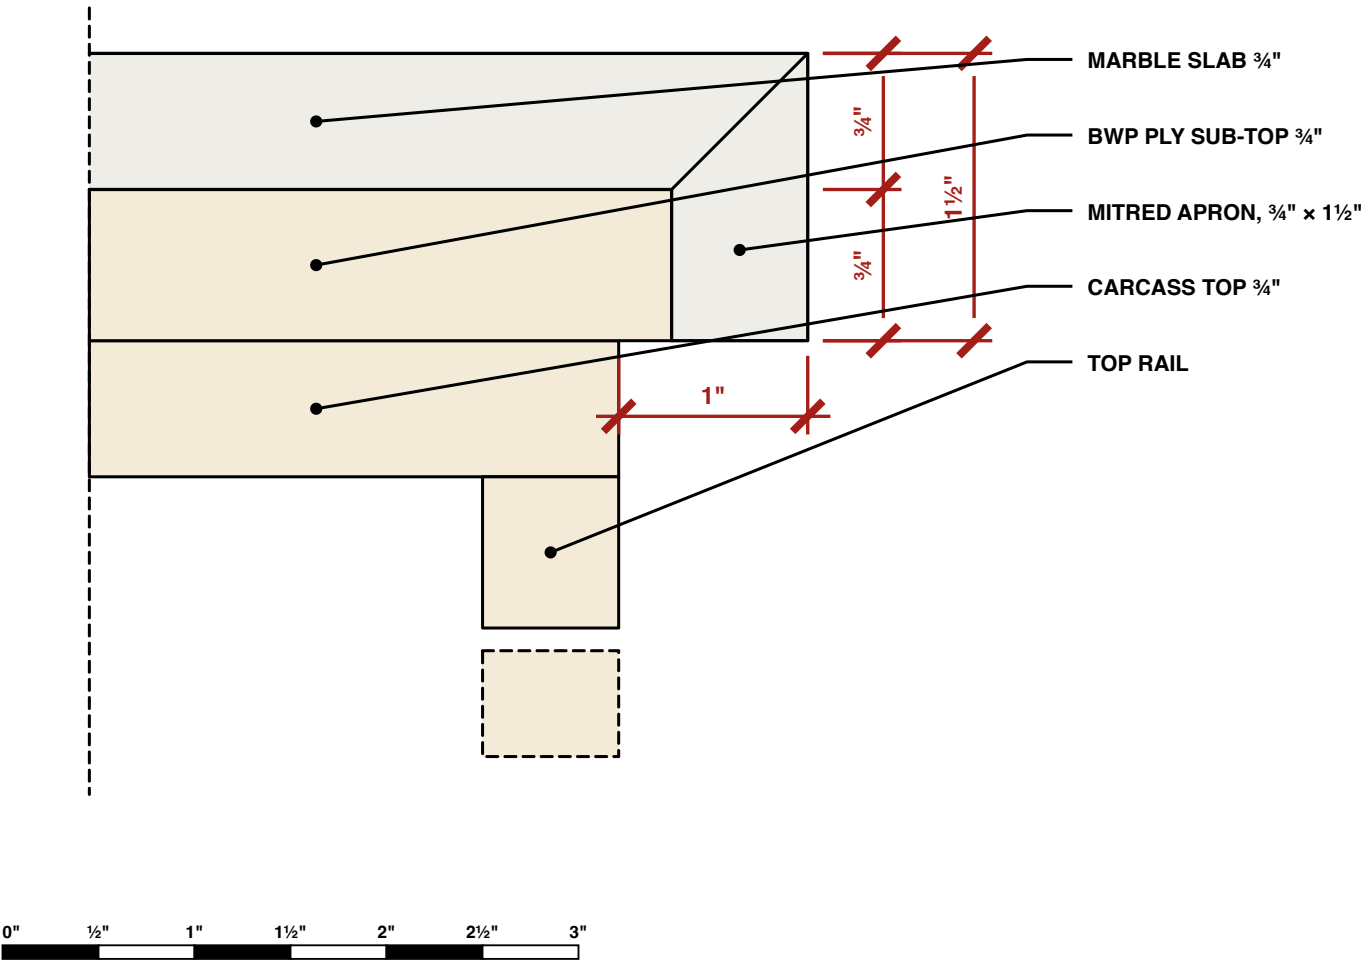

PROJECT A Study in Teak — Vanity — Normal	SHEET Detail 1 · the marble edge Marble full length · Door · Drawers · Door	SCALE 1:1 @ A4	DATE 23.09.2026	REV 1	DRAWING AST-DR-019 · 4 of 10
--	---	-------------------	--------------------	----------	---------------------------------

FRONTS

SIZES ARE THE FRONT ITSELF · 1⁄8" GAP ALL ROUND

No.	WHAT	W × H	FT-IN
1	Door, cup pull	11¾" × 1'-10¼"	11¾" × 1'-10¼"
2	Door, cup pull	11¾" × 1'-10¼"	11¾" × 1'-10¼"
3	Top drawer, push-open	1'-¾" × 5¾"	1'-¾" × 5¾"
4	Top drawer, push-open	1'-¾" × 5¾"	1'-¾" × 5¾"
5	Big drawer, U-box, push-open	2'-2¾" × 1'-3¼"	2'-2¾" × 1'-3¼"
5a	Inner drawer, finger scoop	2'-5⁄8" × 3¾"	2'-5⁄8" × 3¾"

PROJECT A Study in Teak — Vanity — Normal	SHEET Fronts Marble full length · Door · Drawers · Door	SCALE NTS	DATE 23.09.2026	REV 1	DRAWING AST-DR-019 · 5 of 10
--	---	--------------	--------------------	----------	---------------------------------

MATERIALS



THE ROOM'S PALETTE — NOTHING NEW

Top	Beige-gold marble, the bathroom stone. ¾" slab on a ¾" BWP sub-top, mitred 1½" apron, polished.
Carcass	¾" BWP / marine ply, teak veneer both faces. Every edge sealed — it stands in a wet room.
Fronts	¾" BWP, teak veneer, ¼" solid teak lipping.
Runners	Undermount, full extension. Drawers push-to-open — no handles on them; the doors keep cup pulls.
Fittings	Chrome — already bought. Door cup pulls to match.
Hanging	¾" ply cleat on the wall, 2'-3½"—2'-5⅞" high.
Inner	A U-box on its own runners, above the big drawer's low sides — see AST-DR-022.

PROJECT A Study in Teak — Vanity — Normal	SHEET Materials Marble full length · Door · Drawers · Door	SCALE NTS	DATE 23.09.2026	REV 1	DRAWING AST-DR-019 · 6 of 10
--	--	--------------	--------------------	----------	---------------------------------

PLAN



SCALE 1:8 (1½" = 1'-0") @ A4 · FROM ABOVE · WALL AT THE TOP

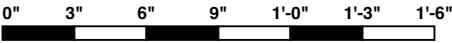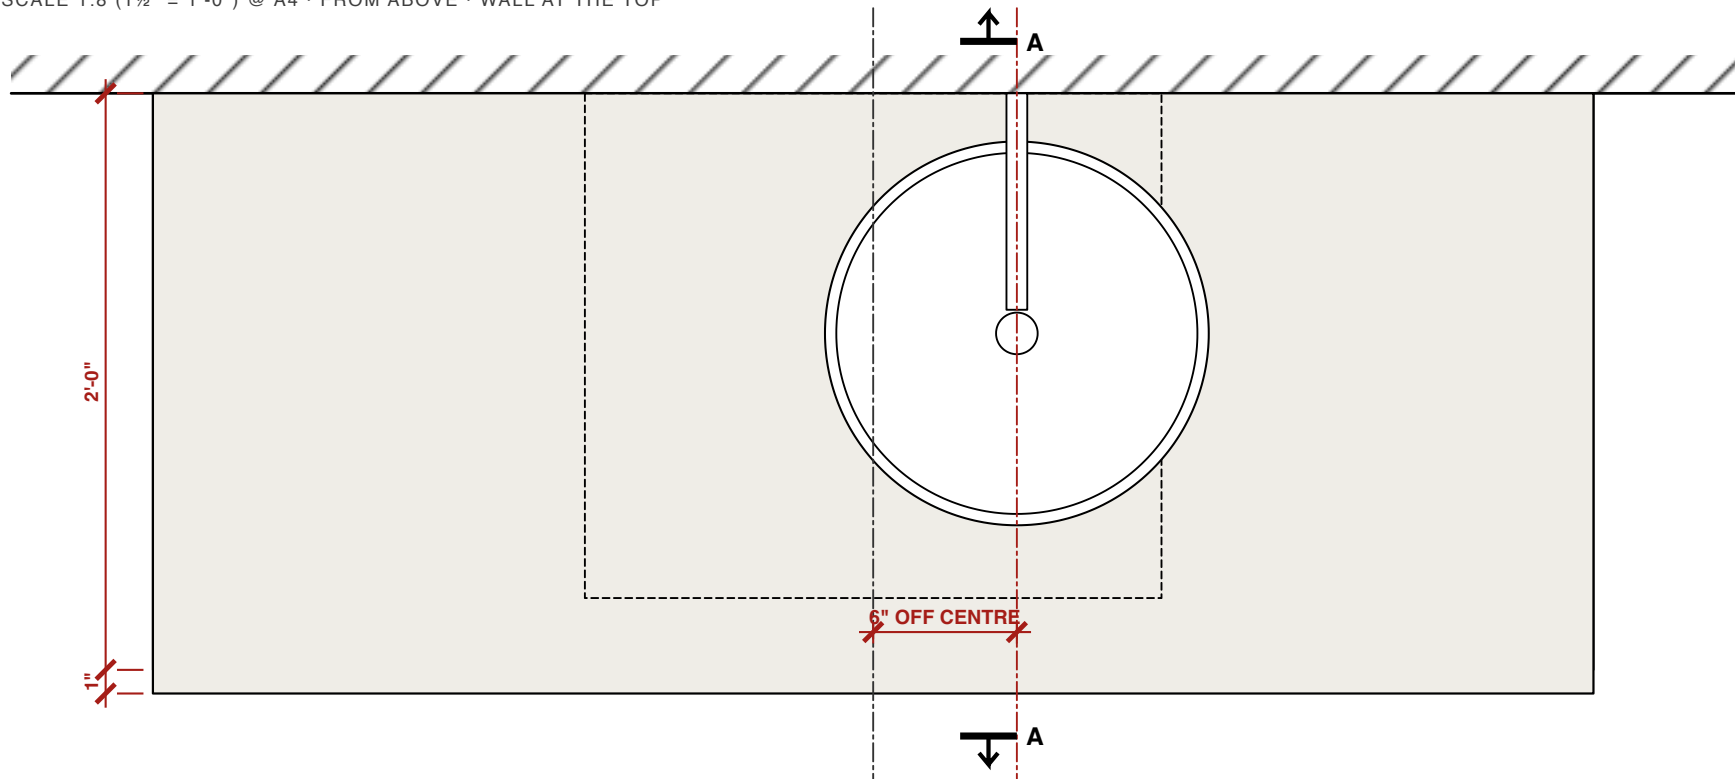

PROJECT	SHEET	SCALE	DATE	REV	DRAWING
A Study in Teak — Vanity — Normal	Plan Marble full length · Door · Drawers · Door	1:8 @ A4	23.09.2026	1	AST-DR-019 · 7 of 10

DETAIL 2 · THE BIG DRAWER

SCALE 1:8 (1½" = 1'-0") @ A4 · PLAN · INNER DRAWER DASHED

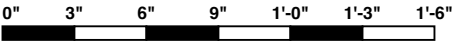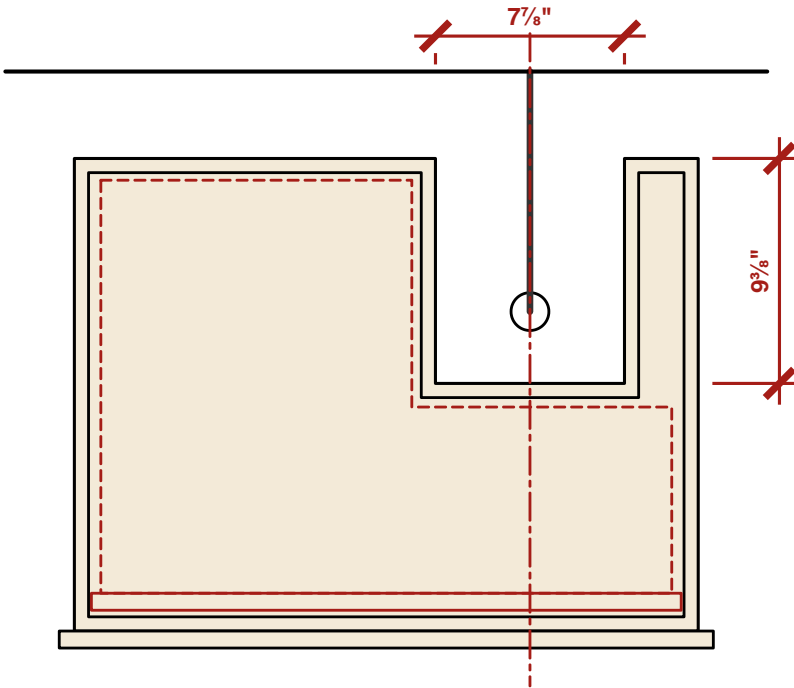

PROJECT
A Study in Teak — Vanity — Normal

SHEET
Detail 2 · the big drawer
Marble full length · Door · Drawers · Door

SCALE
1:8 @ A4

DATE
23.09.2026

REV
1

DRAWING
AST-DR-019 · 8 of 10

SECTION KEY

- A

Hanging cleat
- B

Big drawer, U-box
- C

Waste Ø1⁵/₈" and P-trap
- D

Support, set back 3"
- E

Wall spout
- F

Ply sub-top
- G

Inner drawer

PROJECT A Study in Teak — Vanity — Normal	SHEET Section key Marble full length · Door · Drawers · Door	SCALE NTS	DATE 23.09.2026	REV 1	DRAWING AST-DR-019 · 9 of 10
--	--	--------------	--------------------	----------	---------------------------------

NOTES

REVISION 1

Symmetric about the vanity's centre — except the bowl,
which has to sit under the faucet, 6" right of it.

The waste drops through the right-hand TOP drawer as
well as the big one: both are U-boxes (see section).

OPEN — bowl Ø1'-4" x 5" and the spout are assumed.

With the bowl on a 2'-9" counter its rim is at 3'-2".

OPEN — the support's design: reference photos to come.

PROJECT	SHEET	SCALE	DATE	REV	DRAWING
A Study in Teak — Vanity — Normal	Notes Marble full length · Door · Drawers · Door	NTS	23.09.2026	1	AST-DR-019 · 10 of 10