



FRONT

A 1 FT VENEER CUPBOARD LEFT · 4 FT OF MARBLE CENTRED ON THE FAUCET

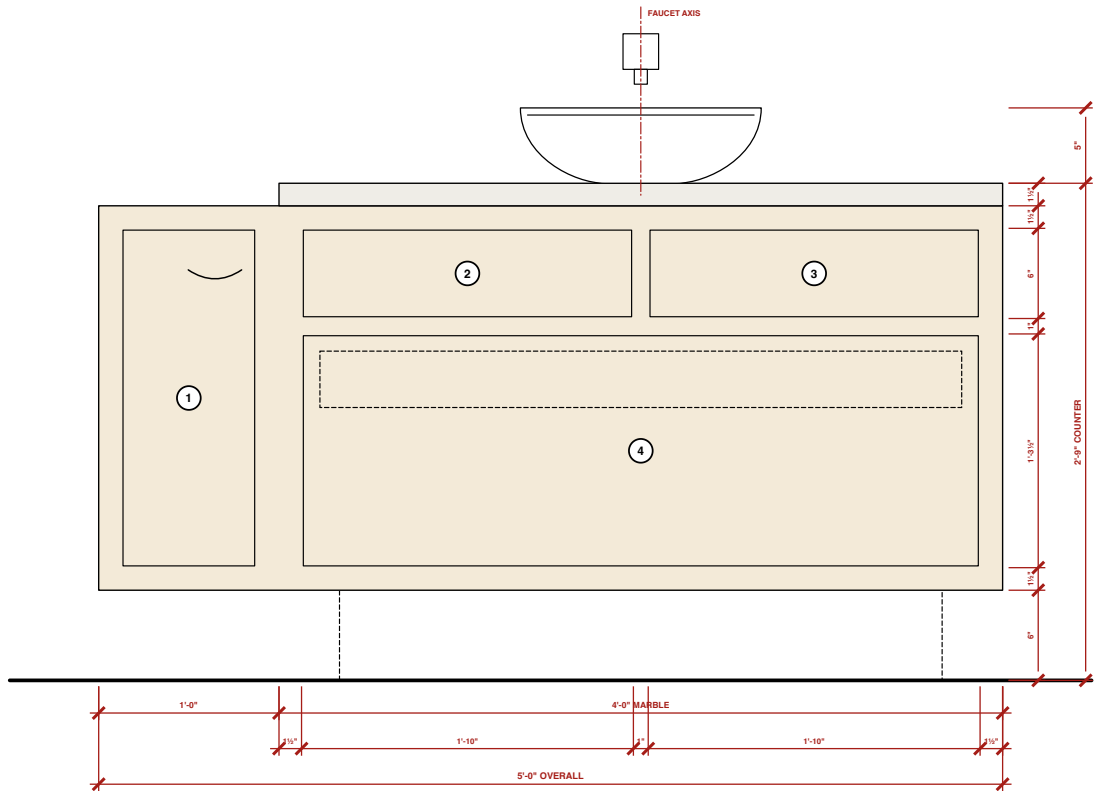

PLAN

FROM ABOVE · WALL AT THE TOP

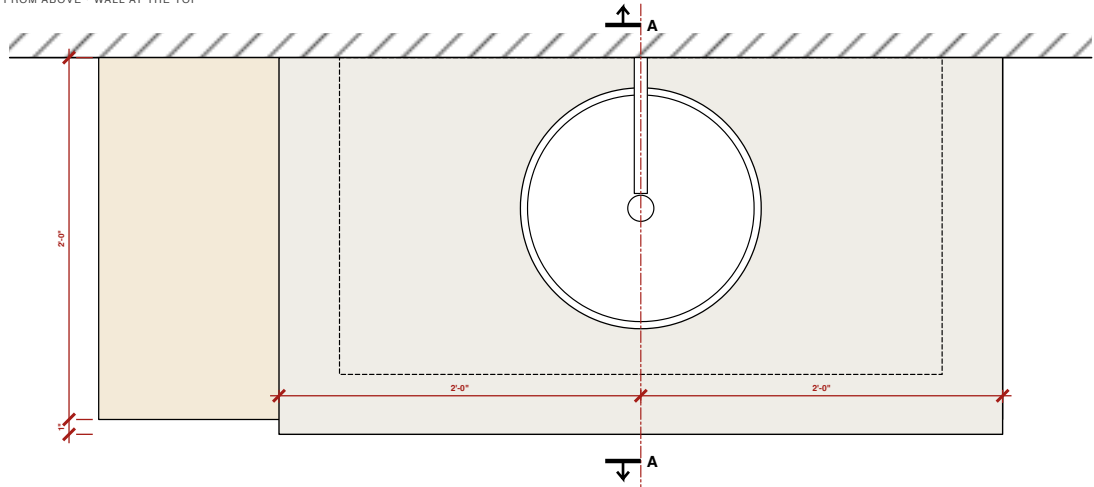

SECTION KEY

- (A) Hanging cleat

(D) Support, set back 3"

(G) Inner drawer
- (B) Big drawer, U-box

(E) Wall spout
- (C) Waste Ø1½" and P-trap

(F) Ply sub-top

NOTES

REVISION 1

Taking 1 ft off the left moves the marble's centre 6 in right — onto the faucet. Bowl, drawer split and support all sit on that one line. The top drawers split on it, so the waste drops between them: only the big one is a U.


OPEN — bowl Ø1'-4" x 5" and the spout are assumed.

With the bowl on a 2'-9" counter its rim is at 3'-2".

OPEN — the support's design: reference photos to come.


SECTION A-A

ON THE FAUCET AXIS

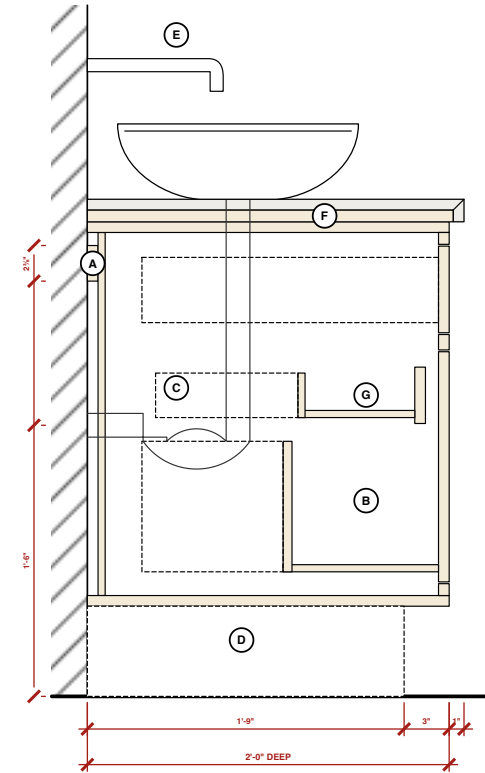


DETAIL 2 · THE BIG DRAWER

PLAN · INNER DRAWER DASHED

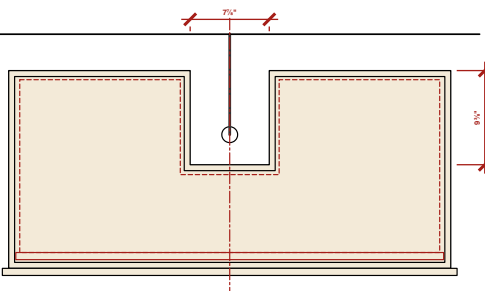

DETAIL 1 · THE MARBLE EDGE

SECTION

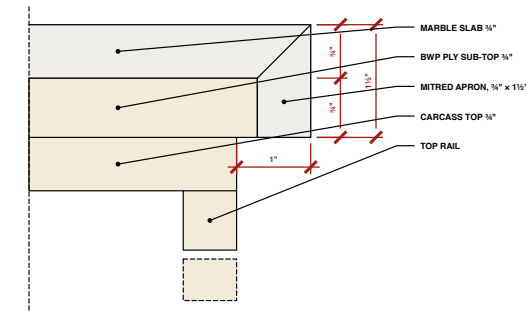

FRONTS

SIZES ARE THE FRONT ITSELF · ¼" GAP ALL ROUND

No.	WHAT	W x H	FT-IN
1	Door, cup pull	8½" x 1'-10¼"	8½" x 1'-10¼"
2	Top drawer, push-open	1'-9¼" x 5¼"	1'-9¼" x 5¼"
3	Top drawer, push-open	1'-9¼" x 5¼"	1'-9¼" x 5¼"
4	Big drawer, U-box, push-open	3'-8¼" x 1'-3¼"	3'-8¼" x 1'-3¼"
4a	Inner drawer, finger scoop	3'-6½" x 3¼"	3'-6½" x 3¼"

MATERIALS

THE ROOM'S PALETTE — NOTHING NEW

Top	Beige-gold marble, the bathroom stone. ¾" slab on a ¾" BWP sub-top, mitred 1½" apron, polished.
Carcass	¾" BWP / marine ply, teak veneer both faces. Every edge sealed — it stands in a wet room.
Fronts	¾" BWP; teak veneer, ½" solid teak lipping.
Ledge	The 1 ft veneer top: solid teak nosing, sealed like a worktop. Marble stops at the bank.
Runners	Undermount, full extension. Drawers push-to-open — no handles on them; the doors keep cup pulls.
Fittings	Chrome — already bought. Door cup pulls to match.
Hanging	¾" ply cleat on the wall, 2'-3½"-2'-5½" high.
Inner	A U-box on its own runners, above the big drawer's low sides — see AST-DR-022.

A STUDY IN TEAK

Particulars of the room

VANITY — SCHEME B

1 ft cupboard left · 4 ft marble on the faucet

SCALE AS NOTED @ A3	DATE 23.09.2026
REV 1 — as sketched	DWG AST-DR-020

PROJECT

A Study in Teak — Vanity — Scheme B

SHEET

General arrangement — the whole sheet

each view follows at its own scale, pages 2 to 10

SCALE

NTS

DATE

23.09.2026

REV



1

DRAWING

AST-DR-020 · 1 of 10

FRONT

SCALE 1:8 (1½" = 1'-0") @ A3 · A 1 FT VENEER CUPBOARD LEFT · 4 FT OF MARBLE CENTRED ON THE FAUCET

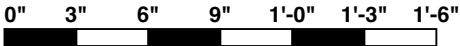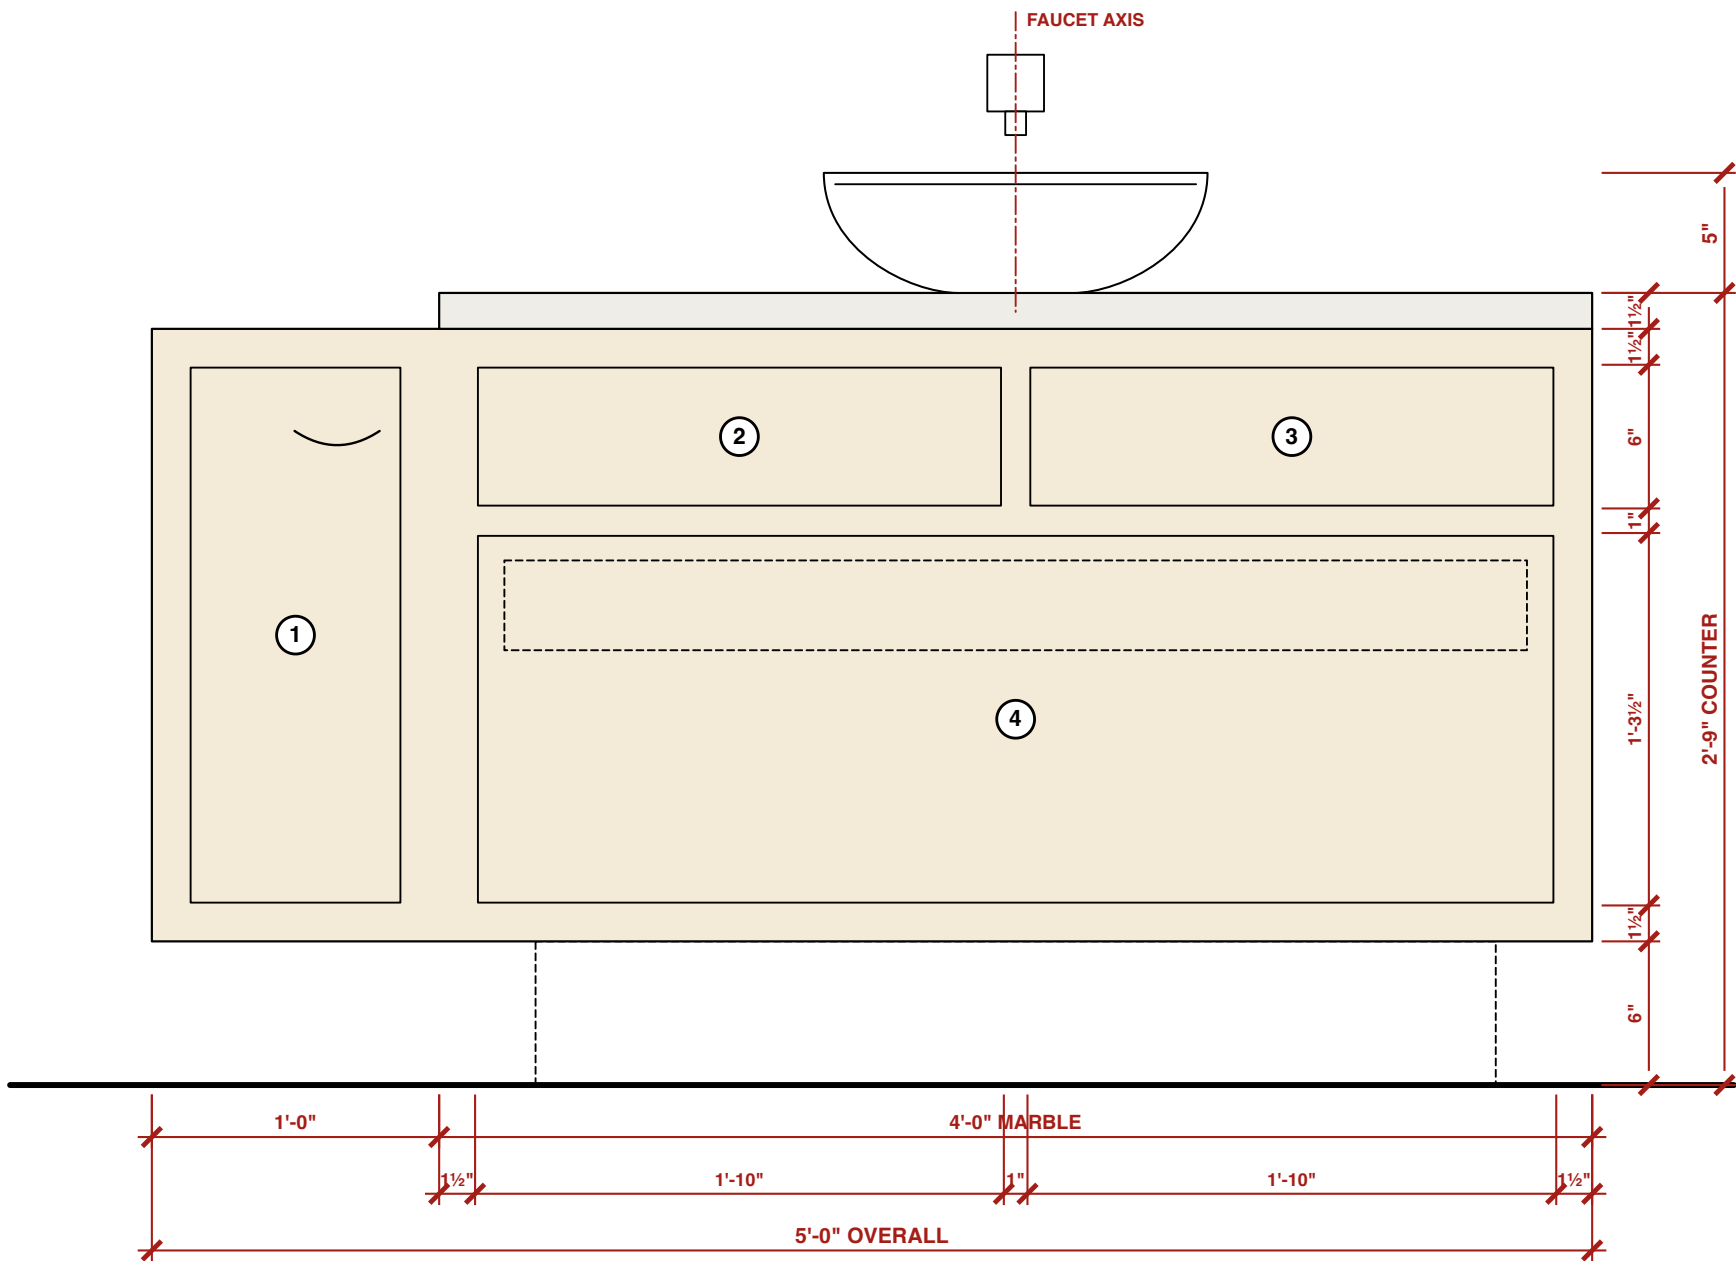

PROJECT
A Study in Teak — Vanity — Scheme B

SHEET
Front
1 ft cupboard left · 4 ft marble on the faucet

SCALE
1:8 @ A3



DATE
23.09.2026

REV
1

DRAWING
AST-DR-020 · 2 of 10

SECTION A-A

SCALE 1:8 (1½" = 1'-0") @ A3 · ON THE FAUCET AXIS

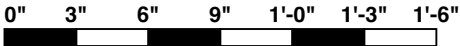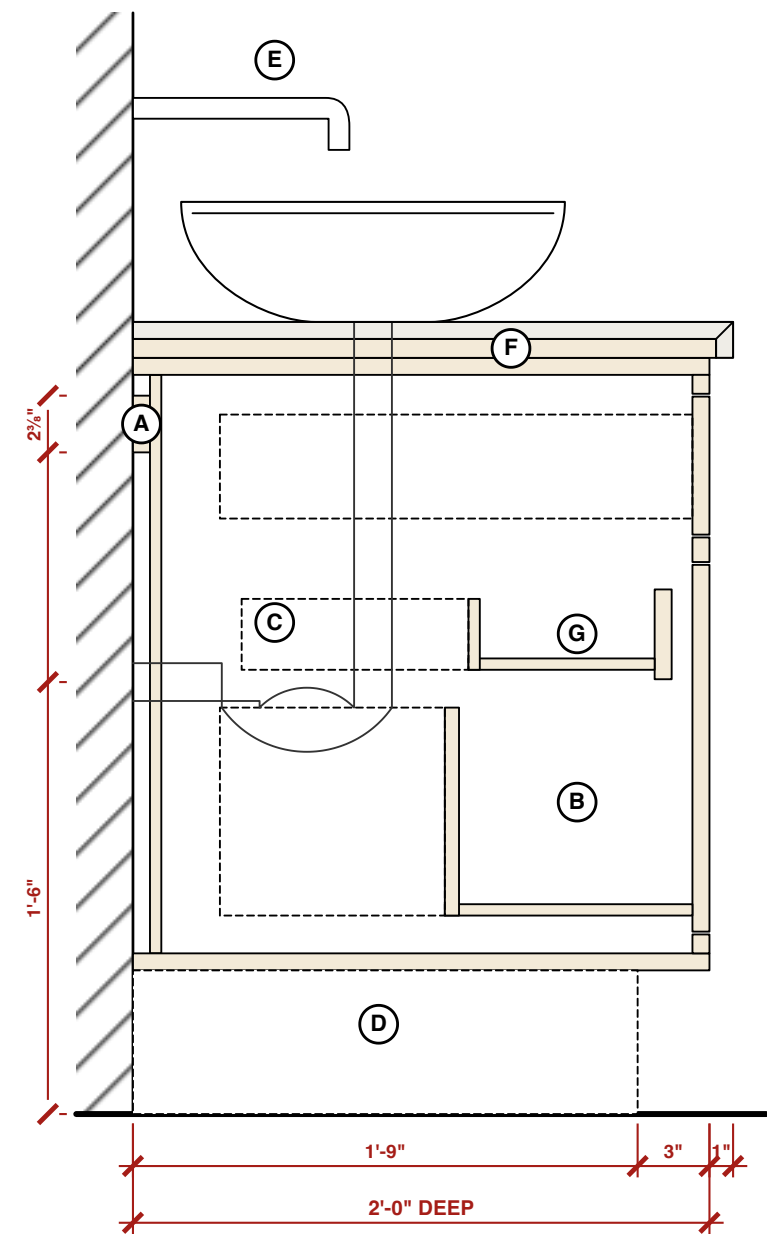

PROJECT
A Study in Teak — Vanity — Scheme B

SHEET
Section A-A
1 ft cupboard left · 4 ft marble on the faucet

SCALE
1:8 @ A3



DATE
23.09.2026

REV
1

DRAWING
AST-DR-020 · 3 of 10

DETAIL 1 · THE MARBLE EDGE

SCALE 1:1 (FULL SIZE) @ A3 · SECTION

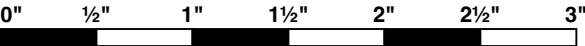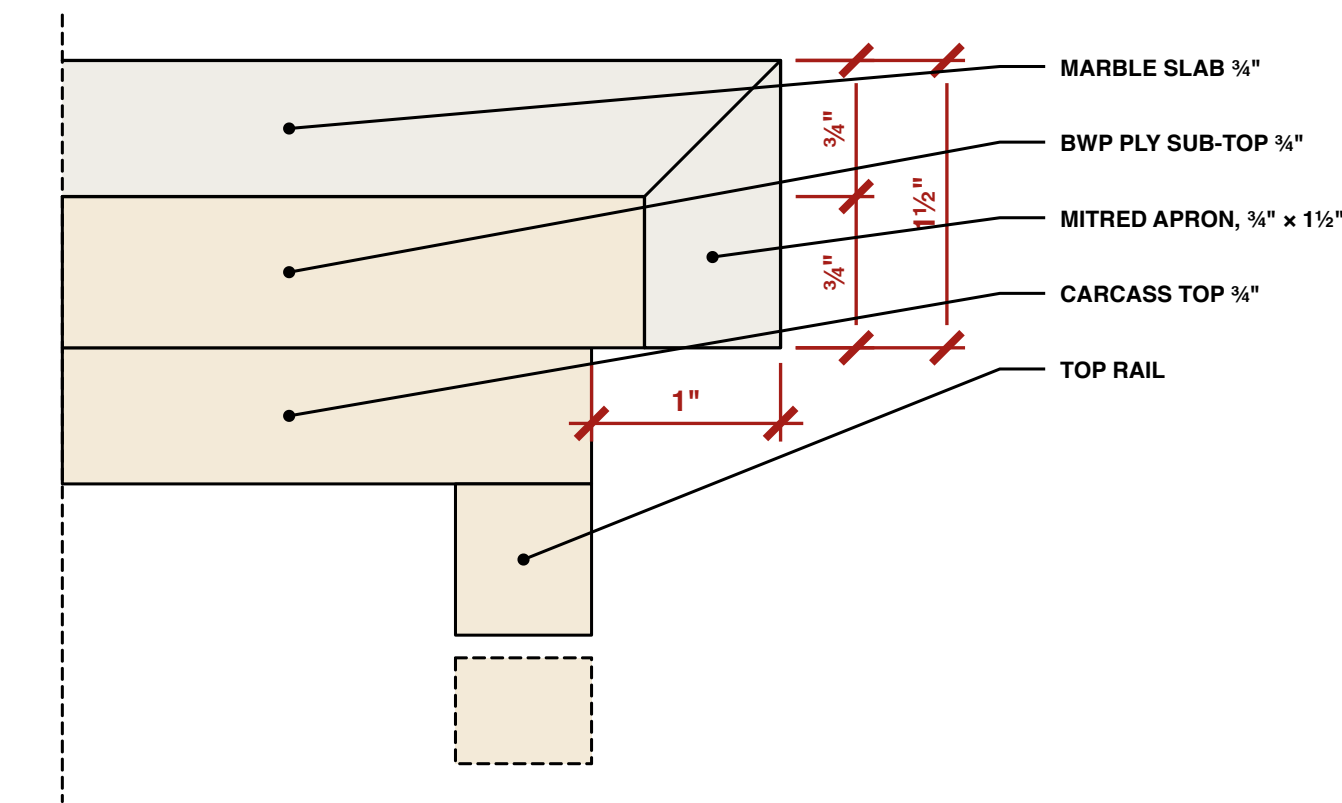

PROJECT	SHEET	SCALE	DATE	REV	DRAWING
A Study in Teak — Vanity — Scheme B	Detail 1 · the marble edge 1 ft cupboard left · 4 ft marble on the faucet	1:1 @ A3	23.09.2026	1	AST-DR-020 · 4 of 10

FRONTS

SIZES ARE THE FRONT ITSELF · 1⁄8" GAP ALL ROUND

No.	WHAT	W × H	FT-IN
1	Door, cup pull	8¾" × 1'-10¼"	8¾" × 1'-10¼"
2	Top drawer, push-open	1'-9¾" × 5¾"	1'-9¾" × 5¾"
3	Top drawer, push-open	1'-9¾" × 5¾"	1'-9¾" × 5¾"
4	Big drawer, U-box, push-open	3'-8¾" × 1'-3¼"	3'-8¾" × 1'-3¼"
4a	Inner drawer, finger scoop	3'-6⅝" × 3¾"	3'-6⅝" × 3¾"

PROJECT A Study in Teak — Vanity — Scheme B	SHEET Fronts 1 ft cupboard left · 4 ft marble on the faucet	SCALE NTS	DATE 23.09.2026	REV 1	DRAWING AST-DR-020 · 5 of 10
--	---	--------------	--------------------	----------	---------------------------------

MATERIALS



THE ROOM'S PALETTE — NOTHING NEW

Top	Beige-gold marble, the bathroom stone. ¾" slab on a ¾" BWP sub-top, mitred 1½" apron, polished.
Carcass	¾" BWP / marine ply, teak veneer both faces. Every edge sealed — it stands in a wet room.
Fronts	¾" BWP, teak veneer, ¼" solid teak lipping.
Ledge	The 1 ft veneer top: solid teak nosing, sealed like a worktop. Marble stops at the bank.
Runners	Undermount, full extension. Drawers push-to-open — no handles on them; the doors keep cup pulls.
Fittings	Chrome — already bought. Door cup pulls to match.
Hanging	¾" ply cleat on the wall, 2'-3½"—2'-5⅞" high.
Inner	A U-box on its own runners, above the big drawer's low sides — see AST-DR-022.

PROJECT A Study in Teak — Vanity — Scheme B	SHEET Materials 1 ft cupboard left · 4 ft marble on the faucet	SCALE NTS	DATE 23.09.2026	REV 1	DRAWING AST-DR-020 · 6 of 10
--	--	--------------	--------------------	----------	---------------------------------

PLAN



SCALE 1:5 @ A3 · FROM ABOVE · WALL AT THE TOP

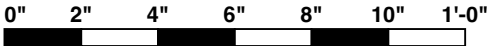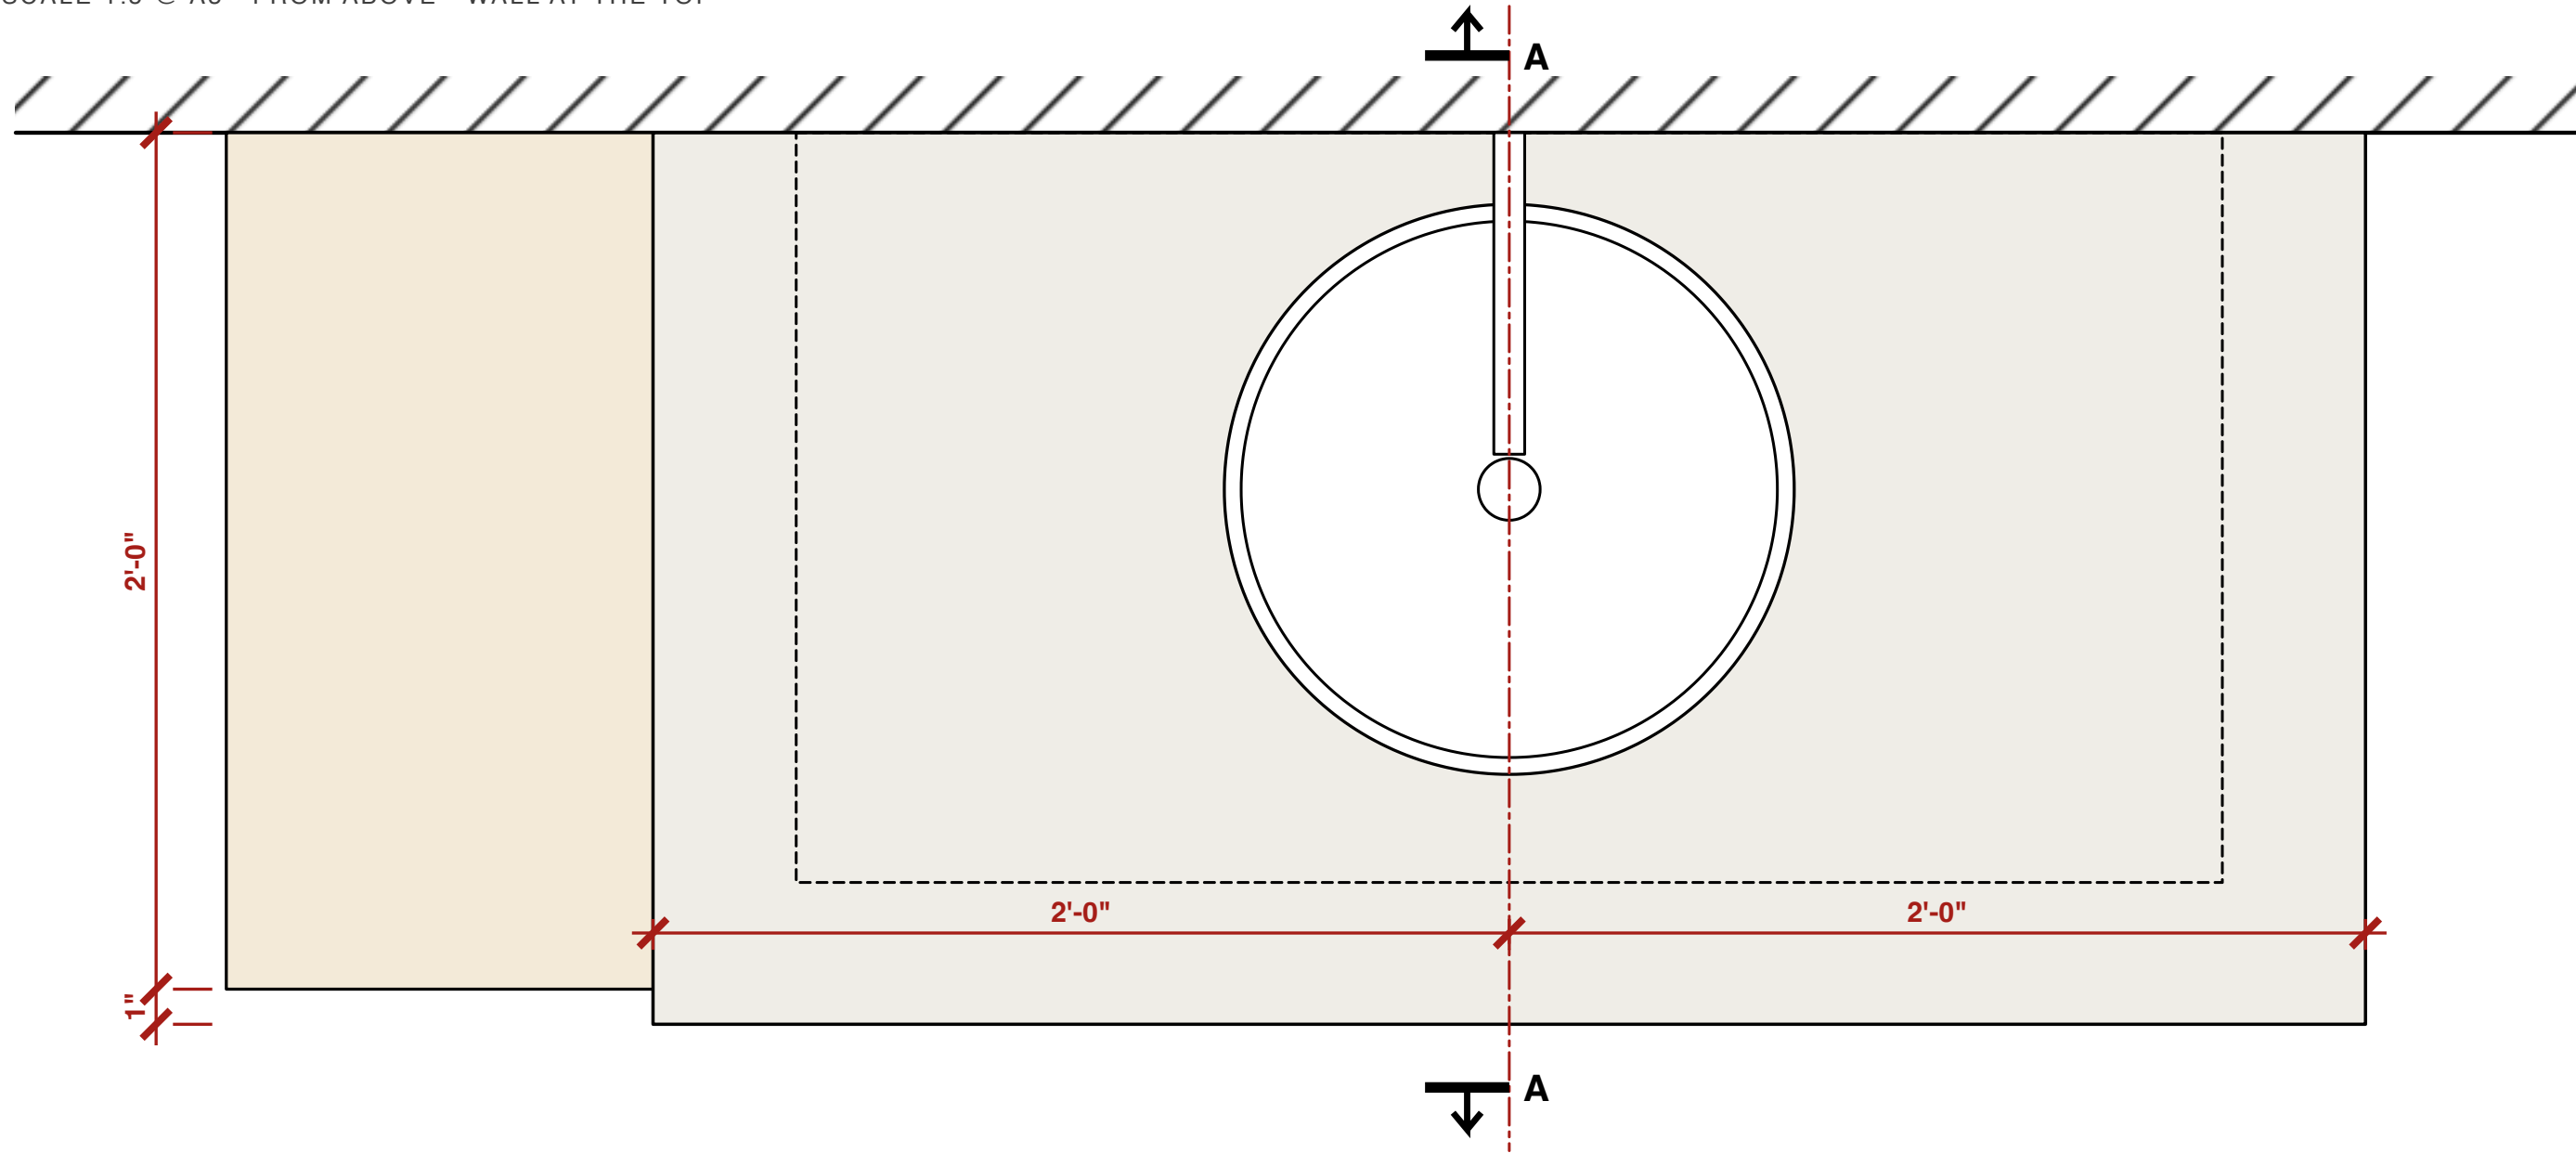

PROJECT A Study in Teak — Vanity — Scheme B	SHEET Plan 1 ft cupboard left · 4 ft marble on the faucet	SCALE 1:5 @ A3	DATE 23.09.2026	REV 1	DRAWING AST-DR-020 · 7 of 10
--	---	-------------------	--------------------	----------	---------------------------------

DETAIL 2 · THE BIG DRAWER

SCALE 1:5 @ A3 · PLAN · INNER DRAWER DASHED

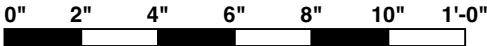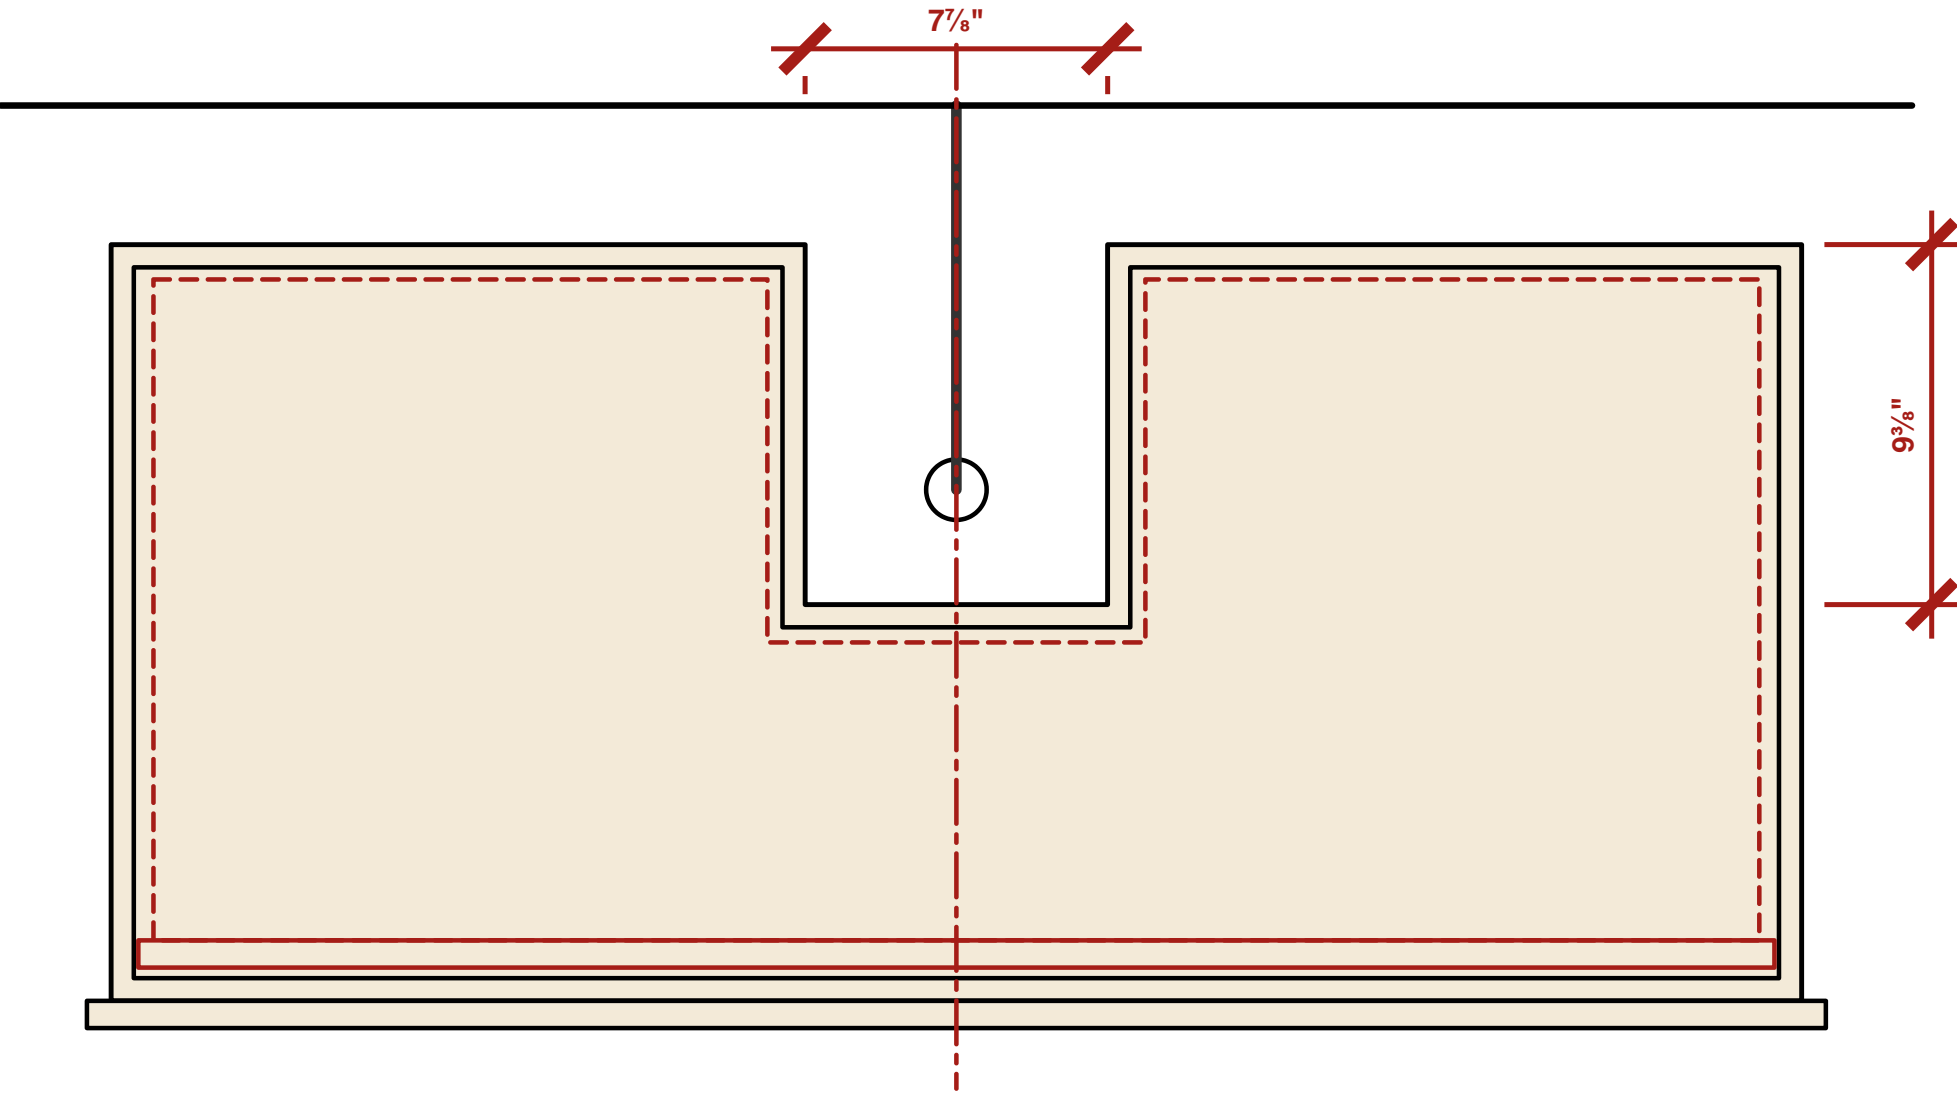

PROJECT	SHEET	SCALE	DATE	REV	DRAWING
A Study in Teak — Vanity — Scheme B	Detail 2 · the big drawer 1 ft cupboard left · 4 ft marble on the faucet	1:5 @ A3	23.09.2026	1	AST-DR-020 · 8 of 10

SECTION KEY

- A

Hanging cleat
- B

Big drawer, U-box
- C

Waste Ø1⁵/₈" and P-trap
- D

Support, set back 3"
- E

Wall spout
- F

Ply sub-top
- G

Inner drawer

PROJECT A Study in Teak — Vanity — Scheme B	SHEET Section key 1 ft cupboard left · 4 ft marble on the faucet	SCALE NTS	DATE 23.09.2026	REV 1	DRAWING AST-DR-020 · 9 of 10
--	--	--------------	--------------------	----------	---------------------------------

NOTES

REVISION 1

Taking 1 ft off the left moves the marble's centre 6 in
right — onto the faucet. Bowl, drawer split and support
all sit on that one line. The top drawers split on it,
so the waste drops between them: only the big one is a U.

OPEN — bowl Ø1'-4" × 5" and the spout are assumed.

With the bowl on a 2'-9" counter its rim is at 3'-2".

OPEN — the support's design: reference photos to come.

PROJECT A Study in Teak — Vanity — Scheme B	SHEET Notes 1 ft cupboard left · 4 ft marble on the faucet	SCALE NTS	DATE 23.09.2026	REV 1	DRAWING AST-DR-020 · 10 of 10
--	--	--------------	--------------------	----------	----------------------------------