



FRONT

CHOSEN · 1 FT 6 LEFT, 6 IN RIGHT · 3 FT MARBLE BANK ON THE FAUCET, DOWN TO THE FLOOR

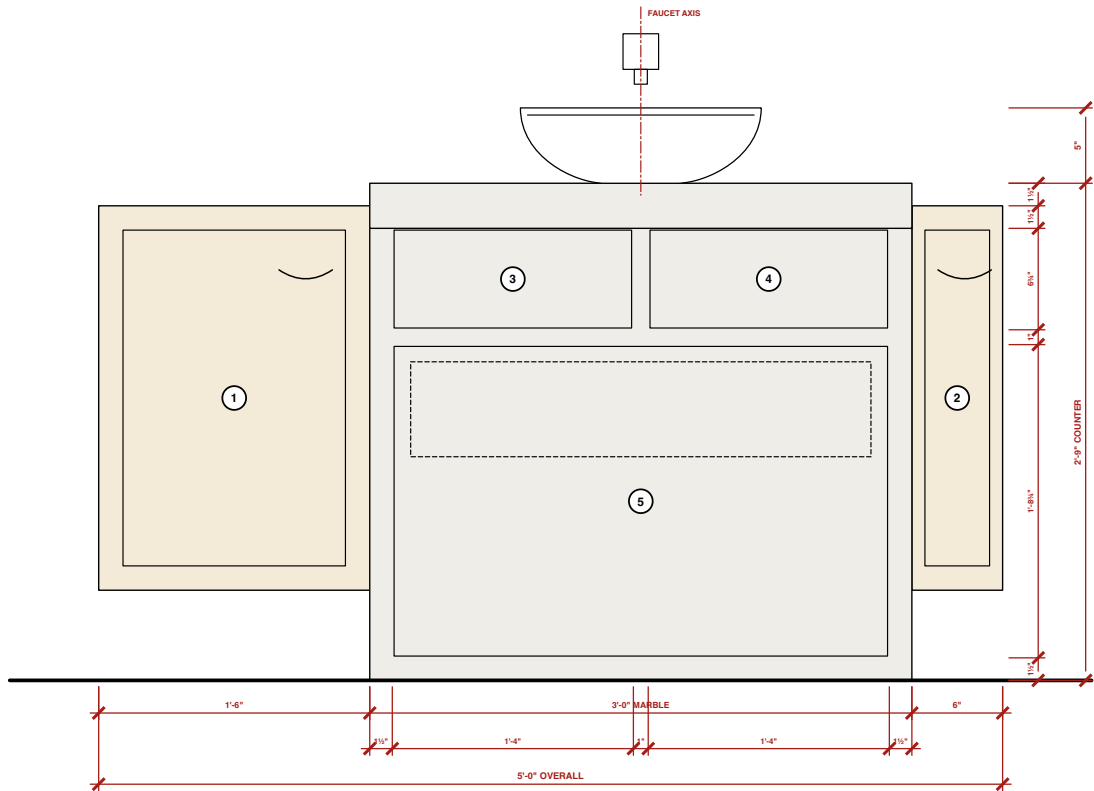

PLAN

FROM ABOVE · WALL AT THE TOP

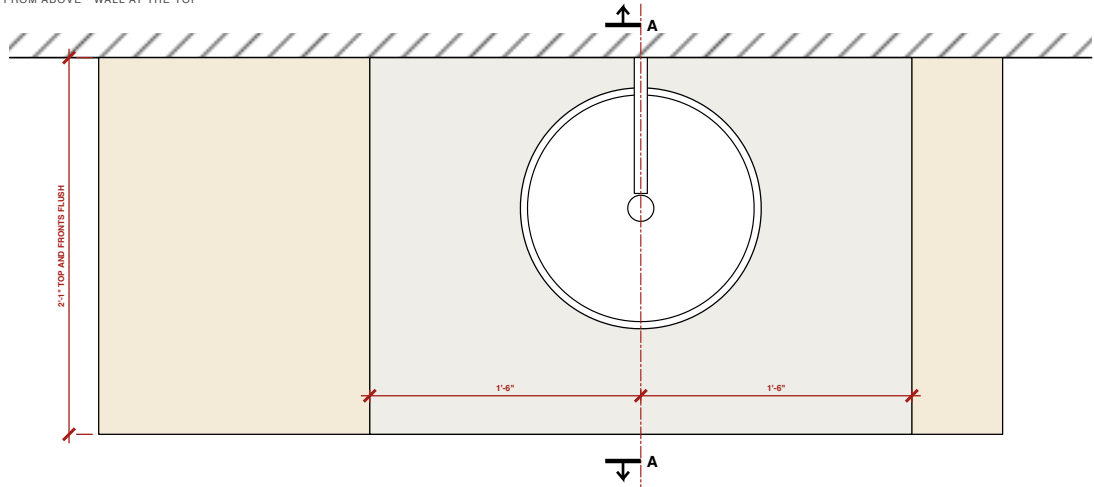

SECTION KEY

- (A) Hanging cleat (B) Big drawer, U-box (C) Waste Ø1½" and P-trap
(E) Wall spout (F) Ply sub-top (G) Inner drawer

NOTES

REVISION 3

The marble bank now runs to the floor and is the support.

Top drawers: 6½ in front, Drawer within: a 5½ in box.

The big drawer takes the rest: 20½ in front, 12¼ in clear

under the inner drawer for tall bottles.


OPEN — bowl Ø1'-4" x 5" and the spout are assumed.

OPEN — marble front thickness and how it is bonded to the
drawer boxes: stone supplier to confirm.

Rev 3: top and front meet in one mitred corner, flush.


SECTION A-A

ON THE FAUCET AXIS

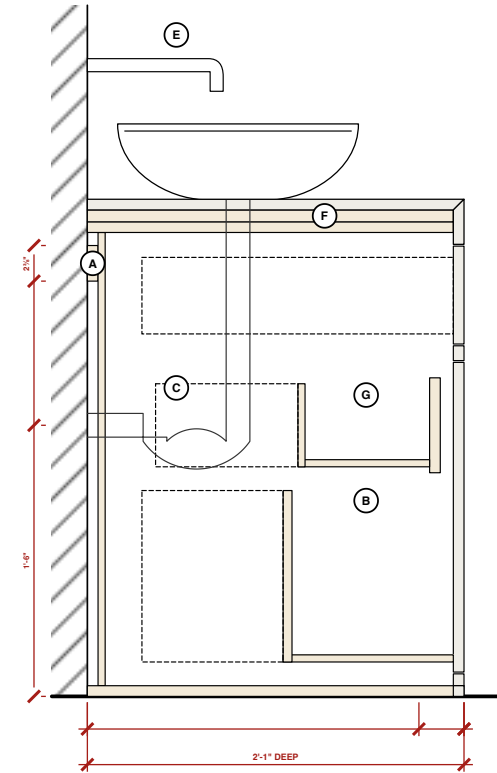


DETAIL 2 · THE BIG DRAWER

PLAN · INNER DRAWER DASHED

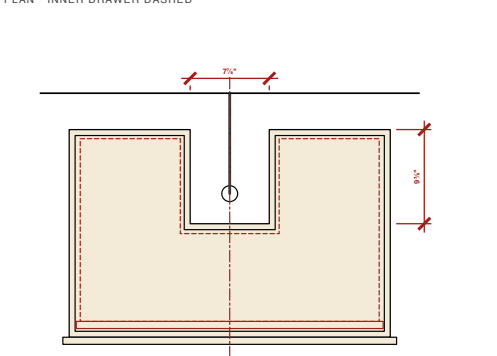

DETAIL 1 · THE MARBLE EDGE

SECTION · ONE MITRED CORNER, FRONTS FLUSH

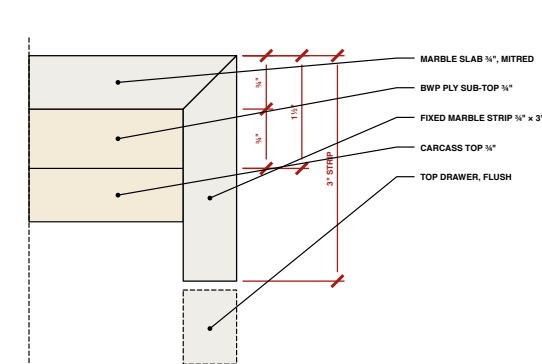

FRONTS

SIZES ARE THE FRONT ITSELF · ¼" GAP ALL ROUND

No.	WHAT	W x H	FT-IN
1	Pull-out cabinet, cup pull	1'-2¼" x 1'-10¼"	1'-2¾" x 1'-10¼"
2	Pull-out cabinet, cup pull	4¼" x 1'-10¼"	4¼" x 1'-10¼"
3	Top drawer, push-open · marble	1'-3¼" x 6¼"	1'-3¾" x 6¼"
4	Top drawer, push-open · marble	1'-3¼" x 6¼"	1'-3¾" x 6¼"
5	Big drawer, U-box, push-open · marble	2'-8¼" x 1'-8½"	2'-8¾" x 1'-8½"
5a	Inner drawer, finger scoop	2'-6½" x 6¼"	2'-6¾" x 6¼"

MATERIALS

THE ROOM'S PALETTE — NOTHING NEW

Top	Beige-gold marble, the bathroom stone. ½" slab on a ½" BWP sub-top, mitred at the front edge into a fixed ½" marble strip: one corner, fronts flush.
Bank	The same beige marble on the face frame and on every drawer front, floor to counter. It stands on the floor and carries the top — no support. Two pull-out cabinets, 9292 cream but veneer, high gloss, ½" BWP, edges sealed. 6 in off the floor.
Ends	The two veneer tops: solid nosing, sealed.
Ledges	Drawers: undermount, push-to-open. Pull-outs: heavy full-extension runners, cup pull.
Runners	Chrome — already bought.
Fittings	U-box, 5½ in deep, on its own runners — AST-DR-022.
Inner	

A STUDY IN TEAK

Particulars of the room

VANITY — SCHEME C

Chosen · marble bank to the floor · pull-outs each end

SCALE AS NOTED @ A3	DATE 02.10.2026
REV 3 — one mitred corner, fronts flush with the top	DWG AST-DR-021

PROJECT

A Study in Teak — Vanity — Scheme C

SHEET

General arrangement — the whole sheet

each view follows at its own scale, pages 2 to 10

SCALE

NTS

DATE

02.10.2026

REV



3

DRAWING

AST-DR-021 · 1 of 18

FRONT



SCALE 1:8 (1½" = 1'-0") @ A3 · CHOSEN · 1 FT 6 LEFT, 6 IN RIGHT · 3 FT MARBLE BANK ON THE FAUCET, DOWN TO THE FLOOR

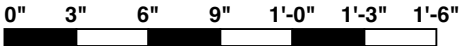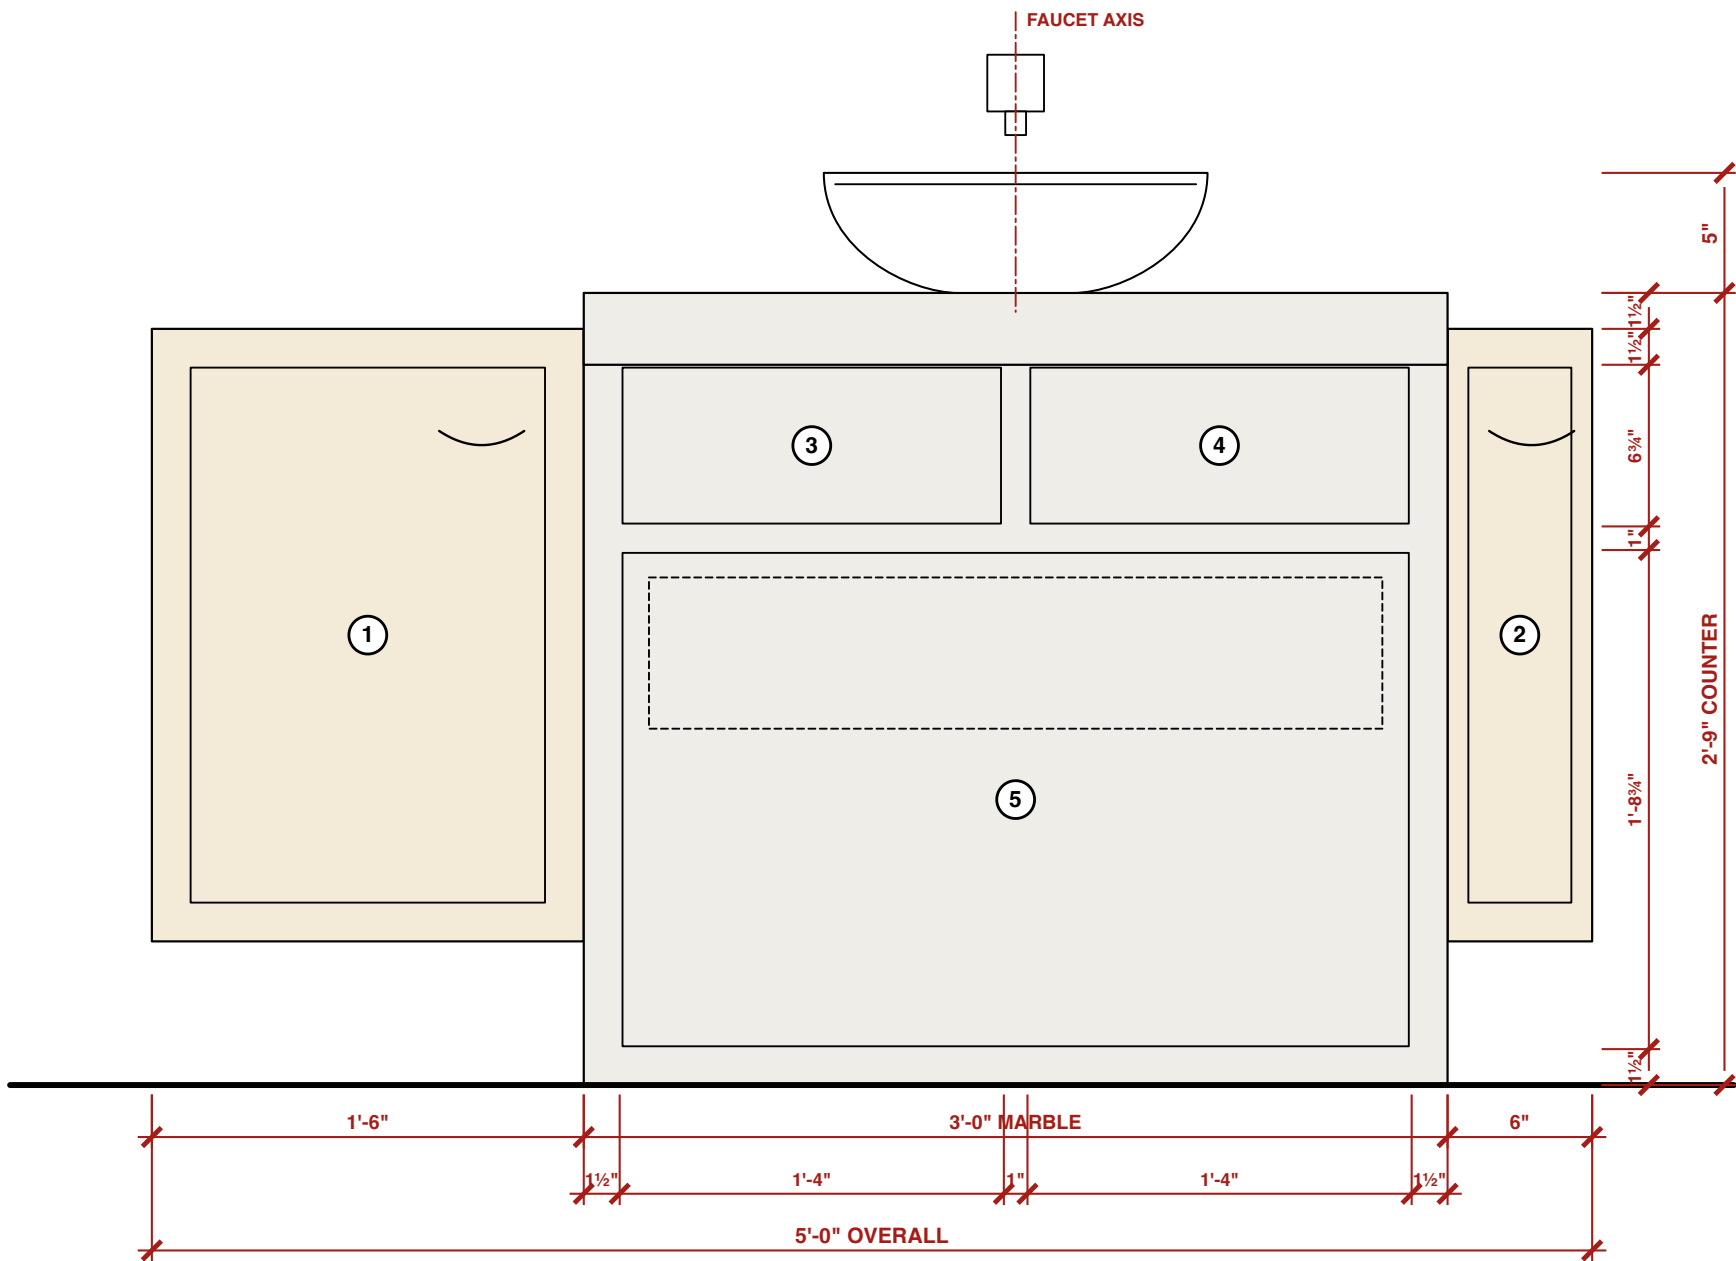

PROJECT A Study in Teak — Vanity — Scheme C	SHEET Front Chosen · marble bank to the floor · pull-outs each end	SCALE 1:8 @ A3	DATE 02.10.2026	REV 3	DRAWING AST-DR-021 · 2 of 18
--	--	-------------------	--------------------	----------	---------------------------------

SECTION A-A

SCALE 1:8 (1½" = 1'-0") @ A3 · ON THE FAUCET AXIS

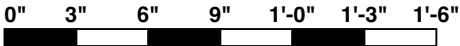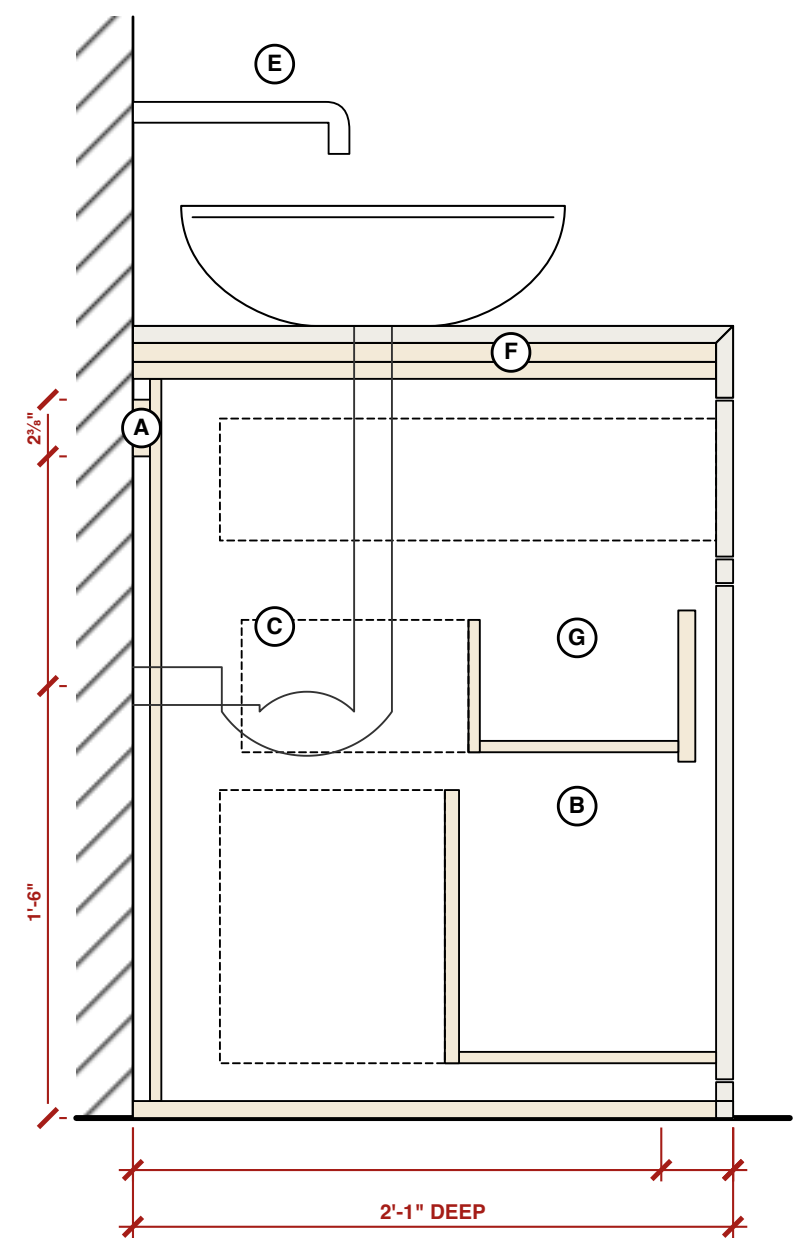

PROJECT
A Study in Teak — Vanity — Scheme C

SHEET
Section A-A
Chosen · marble bank to the floor · pull-outs each end

SCALE
1:8 @ A3



DATE
02.10.2026

REV
3

DRAWING
AST-DR-021 · 3 of 18

DETAIL 1 · THE MARBLE EDGE

SCALE 1:1 (FULL SIZE) @ A3 · SECTION · ONE MITRED CORNER, FRONTS FLUSH

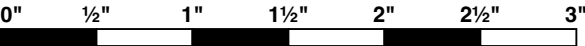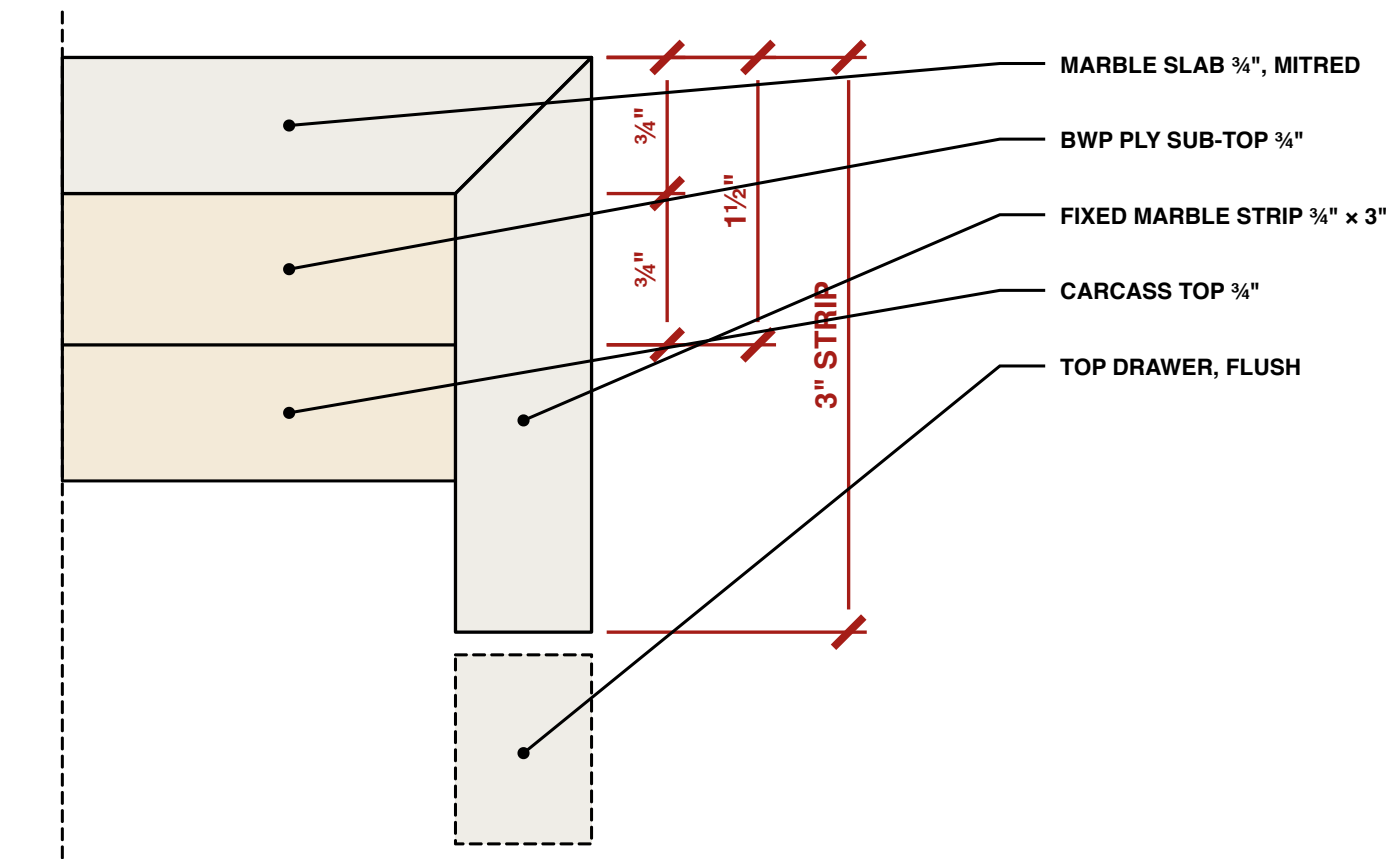

PROJECT A Study in Teak — Vanity — Scheme C	SHEET Detail 1 · the marble edge Chosen · marble bank to the floor · pull-outs each end	SCALE 1:1 @ A3	DATE 02.10.2026	REV 3	DRAWING AST-DR-021 · 4 of 18
---	--	--------------------------------------	---------------------------------------	-----------------------------	--

FRONTS

SIZES ARE THE FRONT ITSELF · 1⁄8" GAP ALL ROUND

No.	WHAT	W × H	FT-IN
1	Pull-out cabinet, cup pull	1'-2¾" × 1'-10¼"	1'-2¾" × 1'-10¼"
2	Pull-out cabinet, cup pull	4¼" × 1'-10¼"	4¼" × 1'-10¼"
3	Top drawer, push-open · marble	1'-3¾" × 6½"	1'-3¾" × 6½"
4	Top drawer, push-open · marble	1'-3¾" × 6½"	1'-3¾" × 6½"
5	Big drawer, U-box, push-open · marble	2'-8¾" × 1'-8½"	2'-8¾" × 1'-8½"
5a	Inner drawer, finger scoop	2'-6½" × 6¼"	2'-6½" × 6¼"

PROJECT A Study in Teak — Vanity — Scheme C	SHEET Fronts Chosen · marble bank to the floor · pull-outs each end	SCALE NTS	DATE 02.10.2026	REV 3	DRAWING AST-DR-021 · 5 of 18
--	---	--------------	--------------------	----------	---------------------------------

MATERIALS



THE ROOM'S PALETTE — NOTHING NEW

Top	Beige-gold marble, the bathroom stone. ¾" slab on a ¾" BWP sub-top, mitred at the front edge into a fixed ¾" marble strip: one corner, fronts flush.
Bank	The same beige marble on the face frame and on every drawer front, floor to counter. It stands on the floor and carries the top — no support.
Ends	Two pull-out cabinets, 9292 cream burl veneer, high gloss, ¾" BWP, edges sealed. 6 in off the floor.
Ledges	The two veneer tops: solid nosing, sealed.
Runners	Drawers: undermount, push-to-open. Pull-outs: heavy full-extension runners, cup pull.
Fittings	Chrome — already bought.
Inner	U-box, 5½ in deep, on its own runners — AST-DR-022.

PROJECT A Study in Teak — Vanity — Scheme C	SHEET Materials Chosen · marble bank to the floor · pull-outs each end	SCALE NTS	DATE 02.10.2026	REV 3	DRAWING AST-DR-021 · 6 of 18
--	--	--------------	--------------------	----------	---------------------------------

PLAN



SCALE 1:5 @ A3 · FROM ABOVE · WALL AT THE TOP

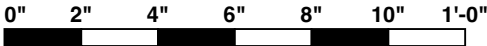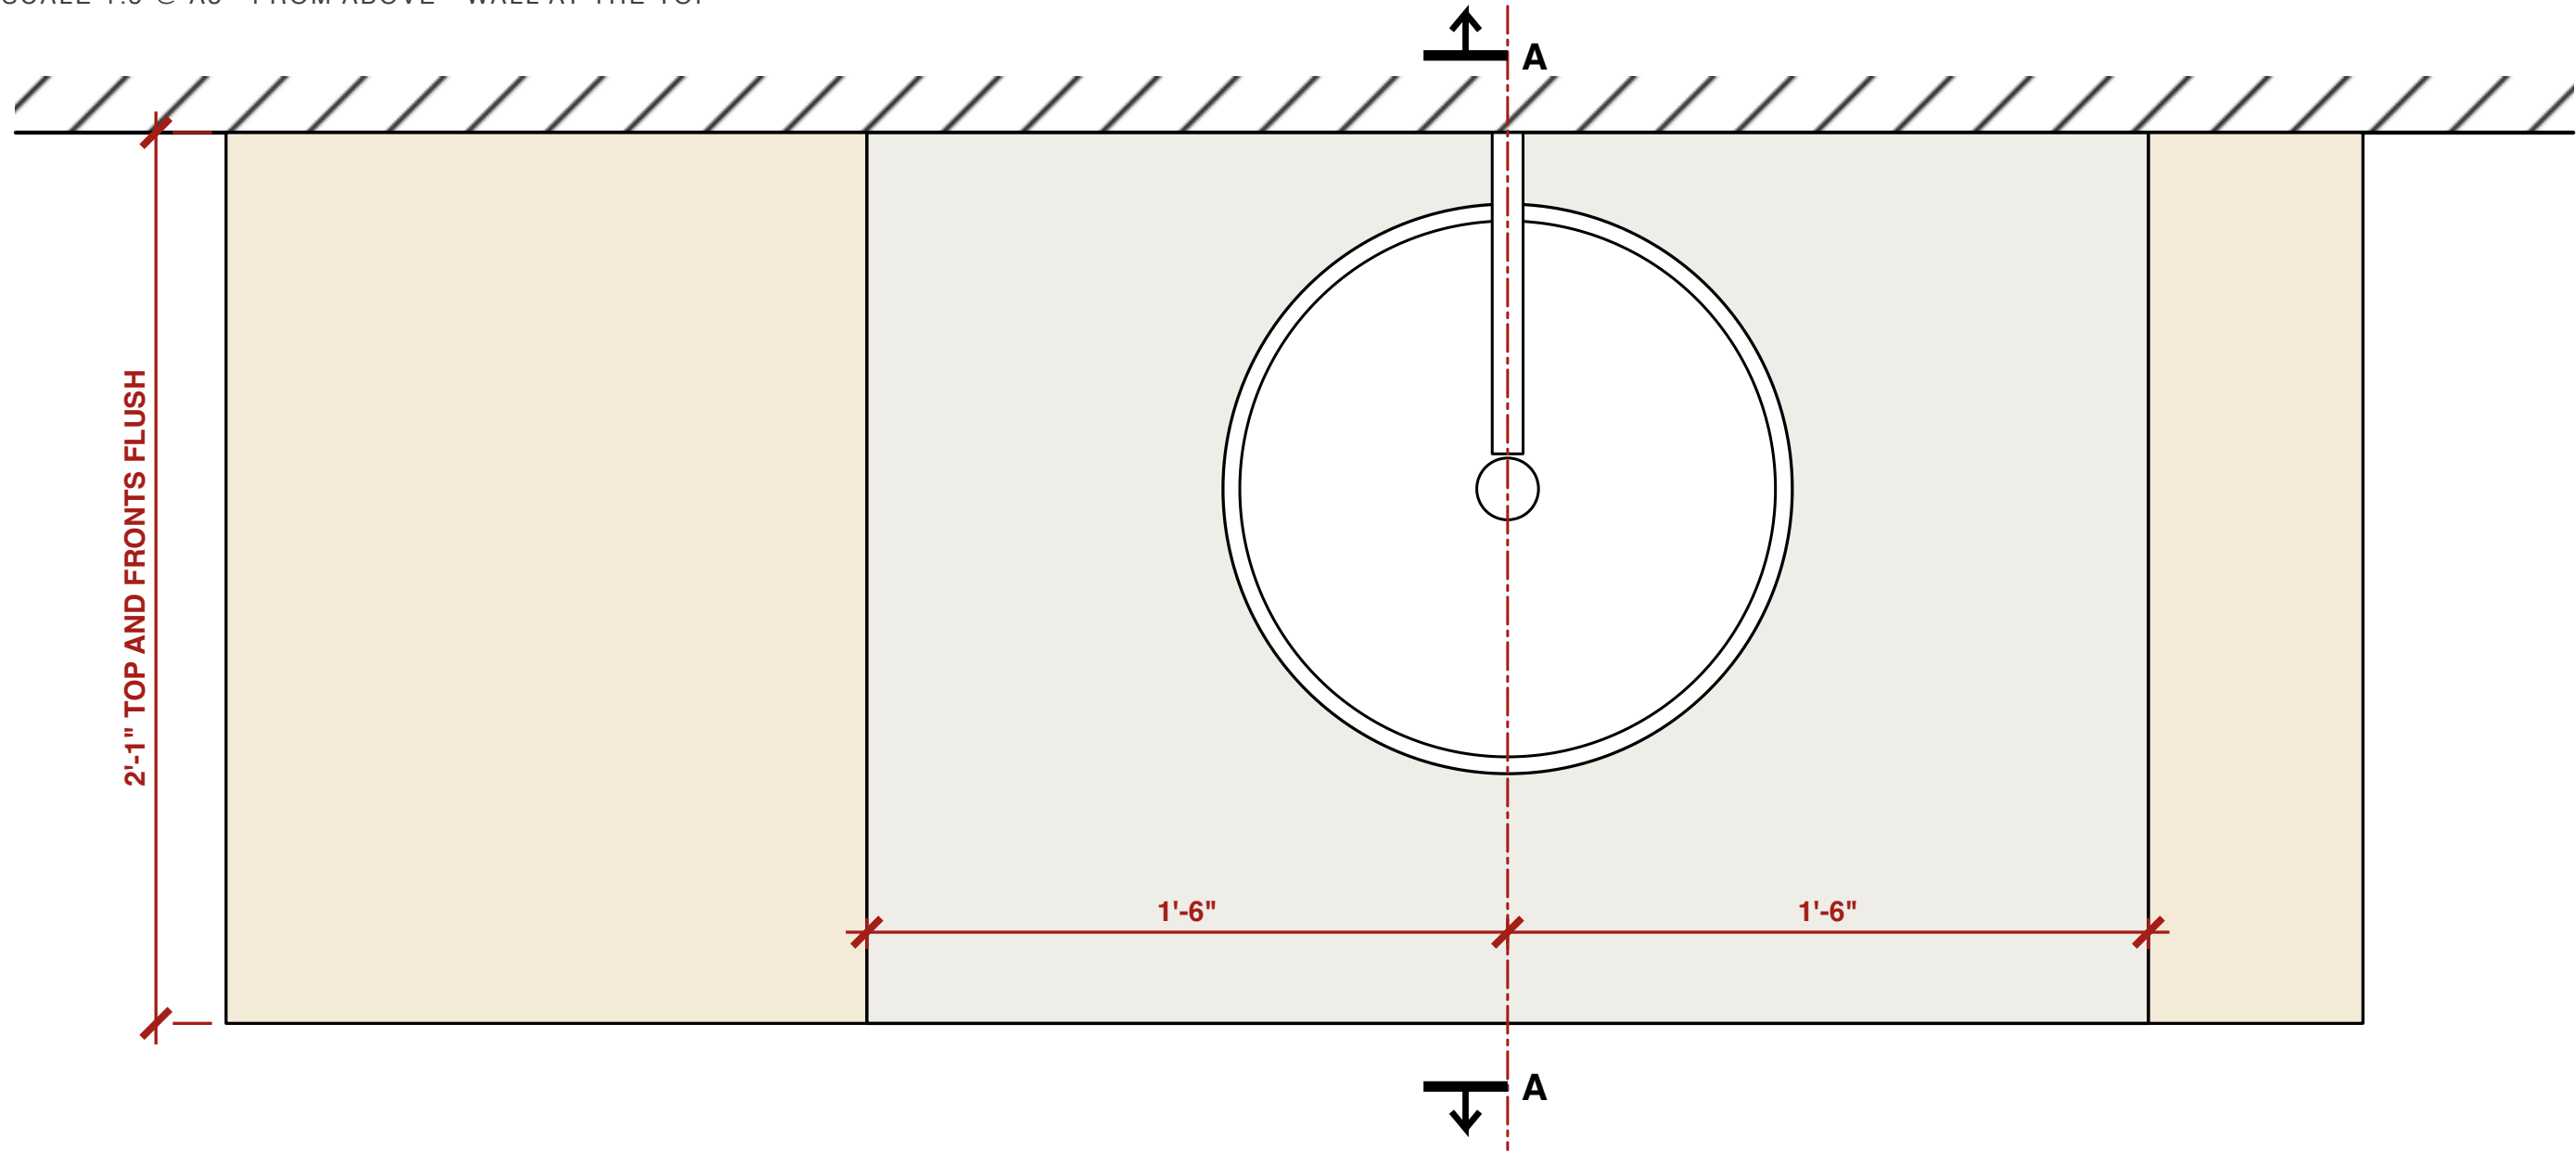

PROJECT A Study in Teak — Vanity — Scheme C	SHEET Plan Chosen · marble bank to the floor · pull-outs each end	SCALE 1:5 @ A3	DATE 02.10.2026	REV 3	DRAWING AST-DR-021 · 7 of 18
--	---	-------------------	--------------------	----------	---------------------------------

DETAIL 2 · THE BIG DRAWER

SCALE 1:5 @ A3 · PLAN · INNER DRAWER DASHED

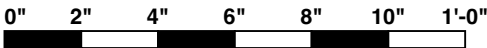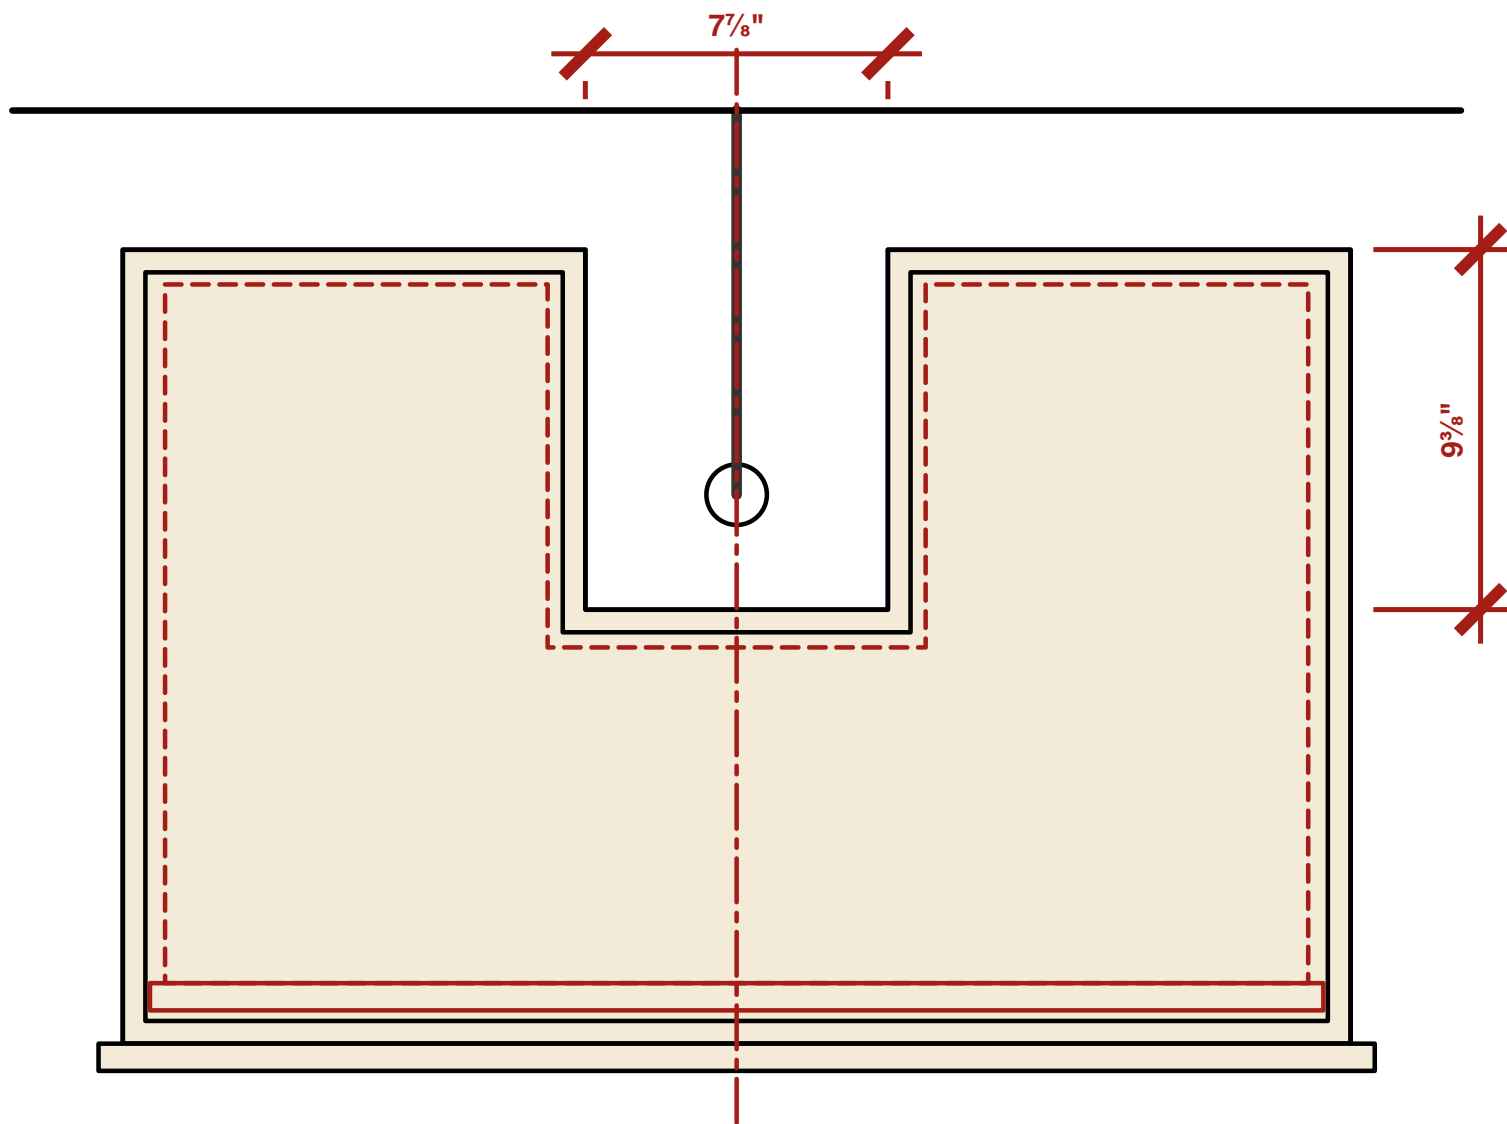

PROJECT
A Study in Teak — Vanity — Scheme C

SHEET
Detail 2 · the big drawer
Chosen · marble bank to the floor · pull-outs each end

SCALE
1:5 @ A3

DATE
02.10.2026

REV
3

DRAWING
AST-DR-021 · 8 of 18

SECTION KEY

- A

Hanging cleat
- B

Big drawer, U-box
- C

Waste Ø1⁵/₈" and P-trap
- E

Wall spout
- F

Ply sub-top
- G

Inner drawer

PROJECT A Study in Teak — Vanity — Scheme C	SHEET Section key Chosen · marble bank to the floor · pull-outs each end	SCALE NTS	DATE 02.10.2026	REV 3	DRAWING AST-DR-021 · 9 of 18
--	--	--------------	--------------------	----------	---------------------------------

NOTES

REVISION 3

The marble bank now runs to the floor and is the support.

Top drawers: 6½ in fronts. Drawer within: a 5½ in box.

The big drawer takes the rest: 20½ in front, 12¾ in clear

under the inner drawer for tall bottles.

OPEN — bowl Ø1'-4" × 5" and the spout are assumed.

OPEN — marble front thickness and how it is bonded to the

drawer boxes: stone supplier to confirm.

Rev 3: top and front meet in one mitred corner, flush.

PROJECT
A Study in Teak — Vanity — Scheme C

SHEET
Notes
Chosen · marble bank to the floor · pull-outs each end

SCALE
NTS


DATE
02.10.2026

REV
3

DRAWING
AST-DR-021 · 10 of 18


1 · CLOSED

SECTION THROUGH ONE ARM · SCHEME C, CHOSEN — BANK TO THE FLOOR

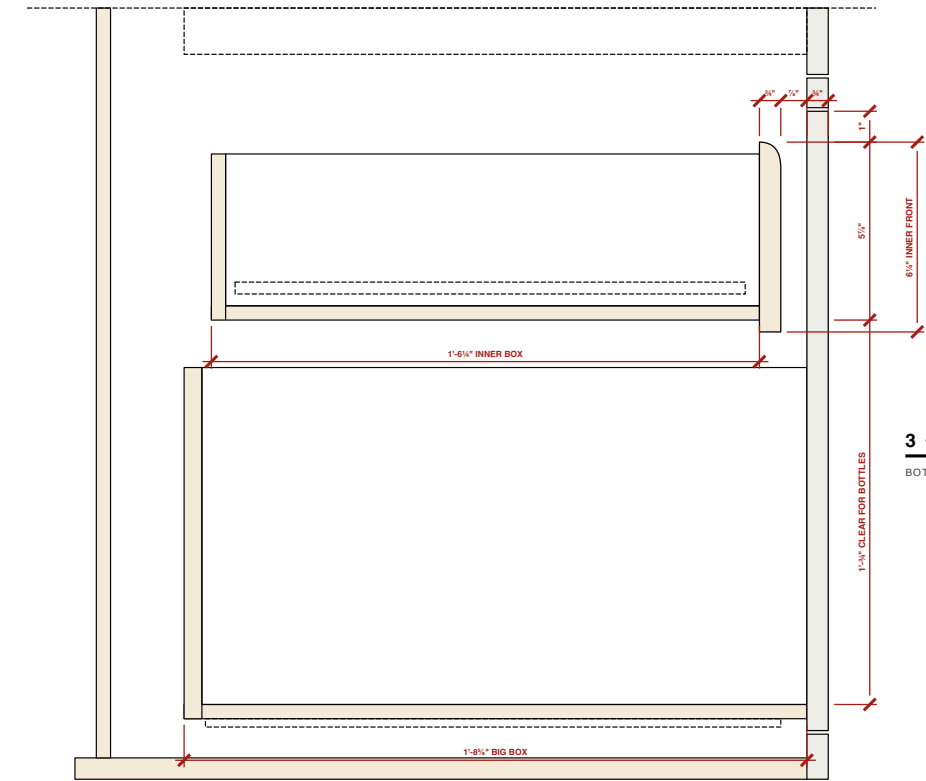


4 · FRONT

THE INNER DRAWER HIDES BEHIND THE BIG FRONT · MARBLE BANK, FLOOR TO COUNTER

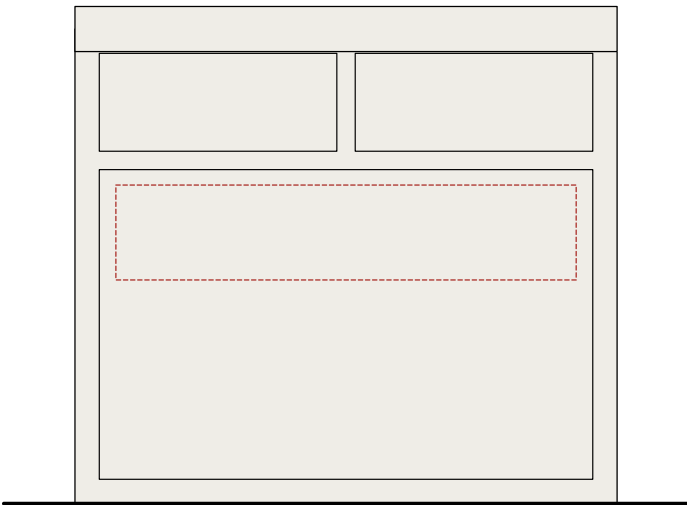


2 · OPEN

BIG DRAWER OUT · INNER ONE PULLED OUT BEHIND ITS FRONT

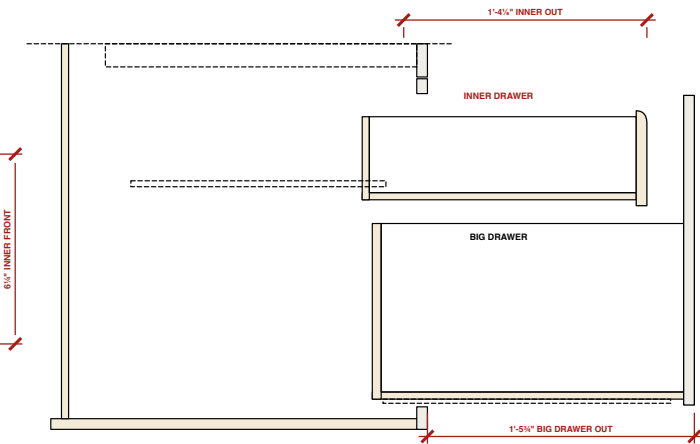

3 · PLAN

BOTH DRAWERS SHUT · THE PIPE DROPS THROUGH BOTH NOTCHES

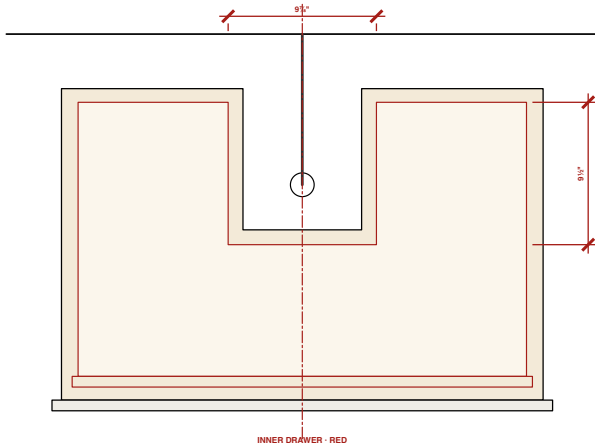

SIZES

THE SAME DRAWER IN ALL THREE SCHEMES

SCHEME	BIG FRONT	INNER FRONT	INNER BOX W
Normal	2'-2 3/4" x 1'-3 3/4"	2'-5 1/4" x 3 1/4"	1'-11 3/4" · L
B	3'-3 3/4" x 1'-3 3/4"	3'-6 1/4" x 3 1/4"	3'-5 3/4" · U
C	2'-8 3/4" x 1'-8 1/4"	2'-6 1/4" x 6 1/4"	2'-5 3/4" · U

Scheme C (chosen): inner box 1'-6 1/4" deep, 5 1/4" high, 1/2" ply, notch 9/16" wide.

HARDWARE

Big drawer	Undermount runners, full extension, push-to-open. Its sides stop at 1'-1 1/4" to pass under the inner.
Inner drawer	Side-mounted runners 1'-3 1/4", full extension, on the carcass partitions at 1'-4 1/4"-1'-4 1/2". Independent.
Inner front	1/4" BWP, teak veneer both faces, top edge scooped for a finger. No handle.

NOTES

REVISION 2

Open the big drawer: the inner one stays put. Pull it and it comes out 1'-4 1/4" behind the big front, over the bottles — the tray in the kitchen drawer photographed.

Both are U-boxes. The waste pipe drops through their notches whichever drawer is shut; neither may be solid across the back.

It can never pass the big front — that front is solid. Shut, it stands 1/4" behind it.

Below the inner drawer: 1'-3/4" clear — tall bottles stand.

Normal version: the pipe is off centre, which leaves the inner drawer a 1" right arm. Too thin to keep — that arm is left off and the inner drawer is an L.

A STUDY IN TEAK

Particulars of the room

VANITY — DRAWER WITHIN

The big drawer, and a drawer inside it

SCALE AS NOTED @ A3	DATE 30.09.2026
REV 2 — scheme C: 5 1/4" in inner box, bank to the floor	DWG AST-DR-022

PROJECT
A Study in Teak — Vanity — Drawer Within

SHEET
General arrangement — the whole sheet
each view follows at its own scale, pages 12 to 18

SCALE
NTS



DATE
30.09.2026

REV
2

DRAWING
AST-DR-022 · 11 of 18

1 · CLOSED

SCALE 1:4 (3" = 1'-0") @ A3 · SECTION THROUGH ONE ARM · SCHEME C, CHOSEN — BANK TO THE FLOOR

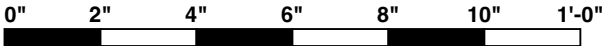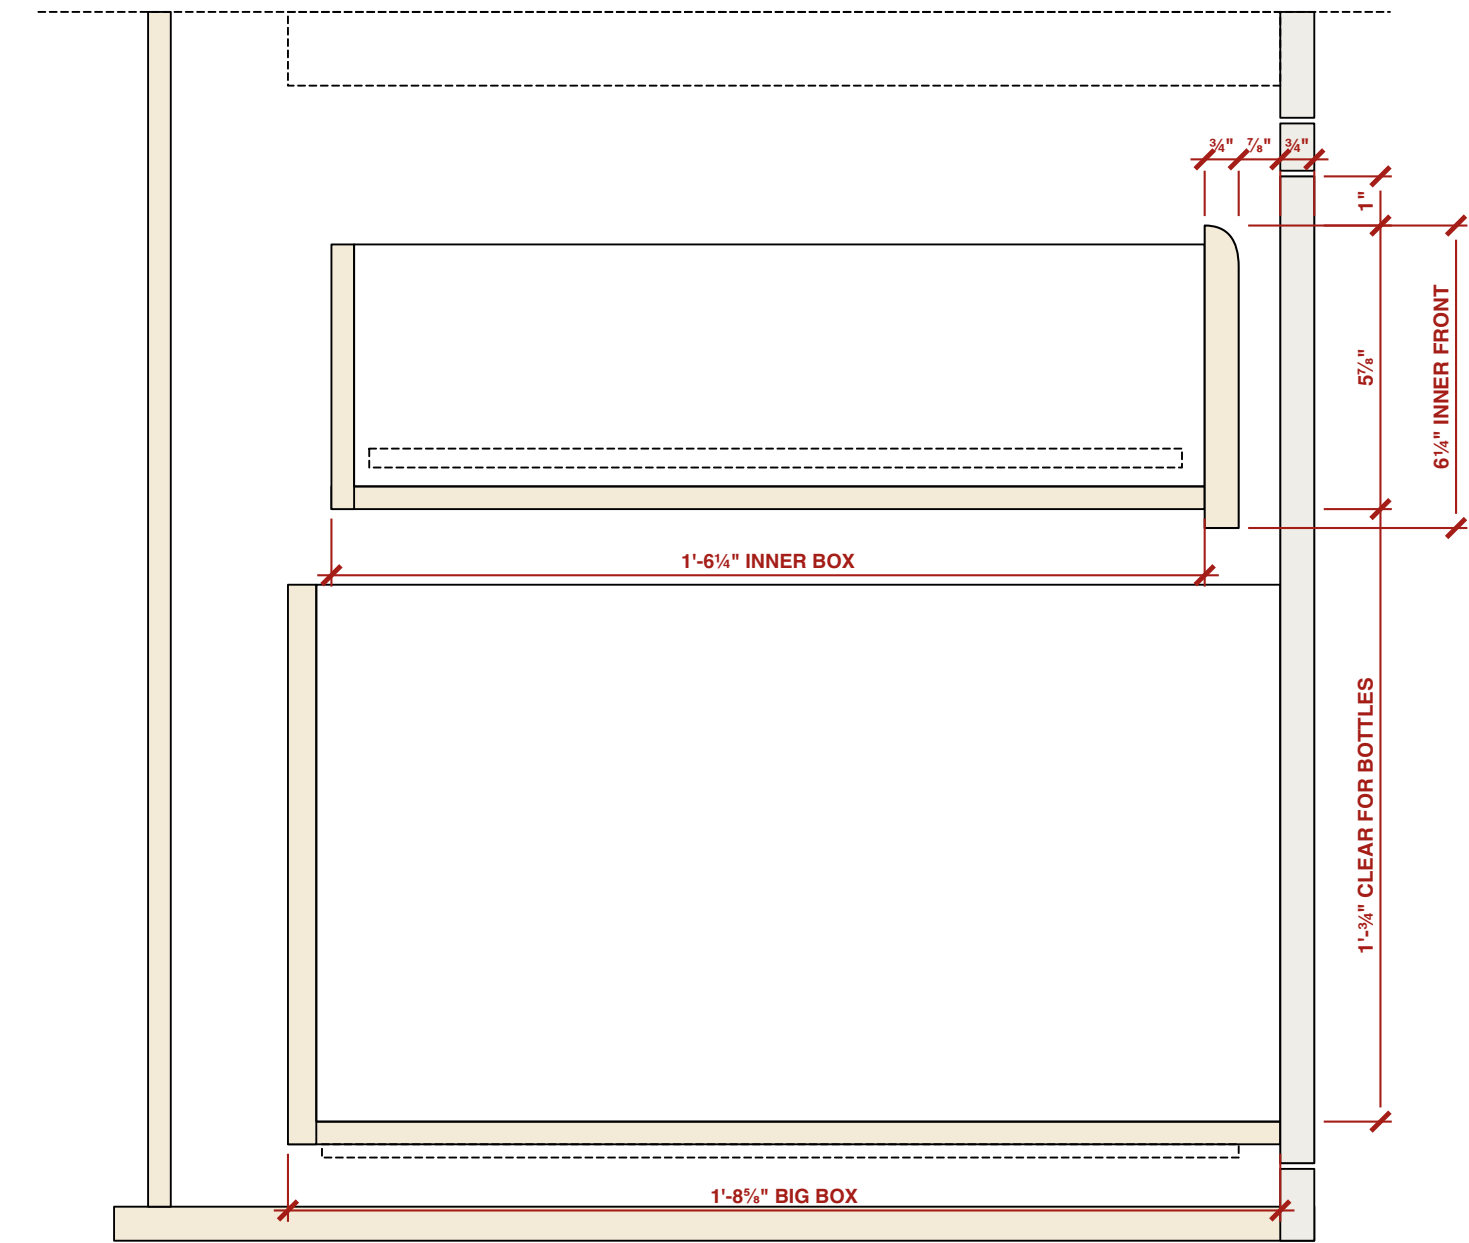

PROJECT
A Study in Teak — Vanity — Drawer Within

SHEET
1 · closed
The big drawer, and a drawer inside it

SCALE
1:4 @ A3



DATE
30.09.2026

REV
2

DRAWING
AST-DR-022 · 12 of 18

2 · OPEN

SCALE 1:4 (3" = 1'-0") @ A3 · BIG DRAWER OUT · INNER ONE PULLED OUT BEHIND ITS FRONT

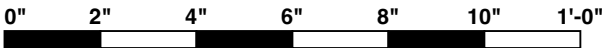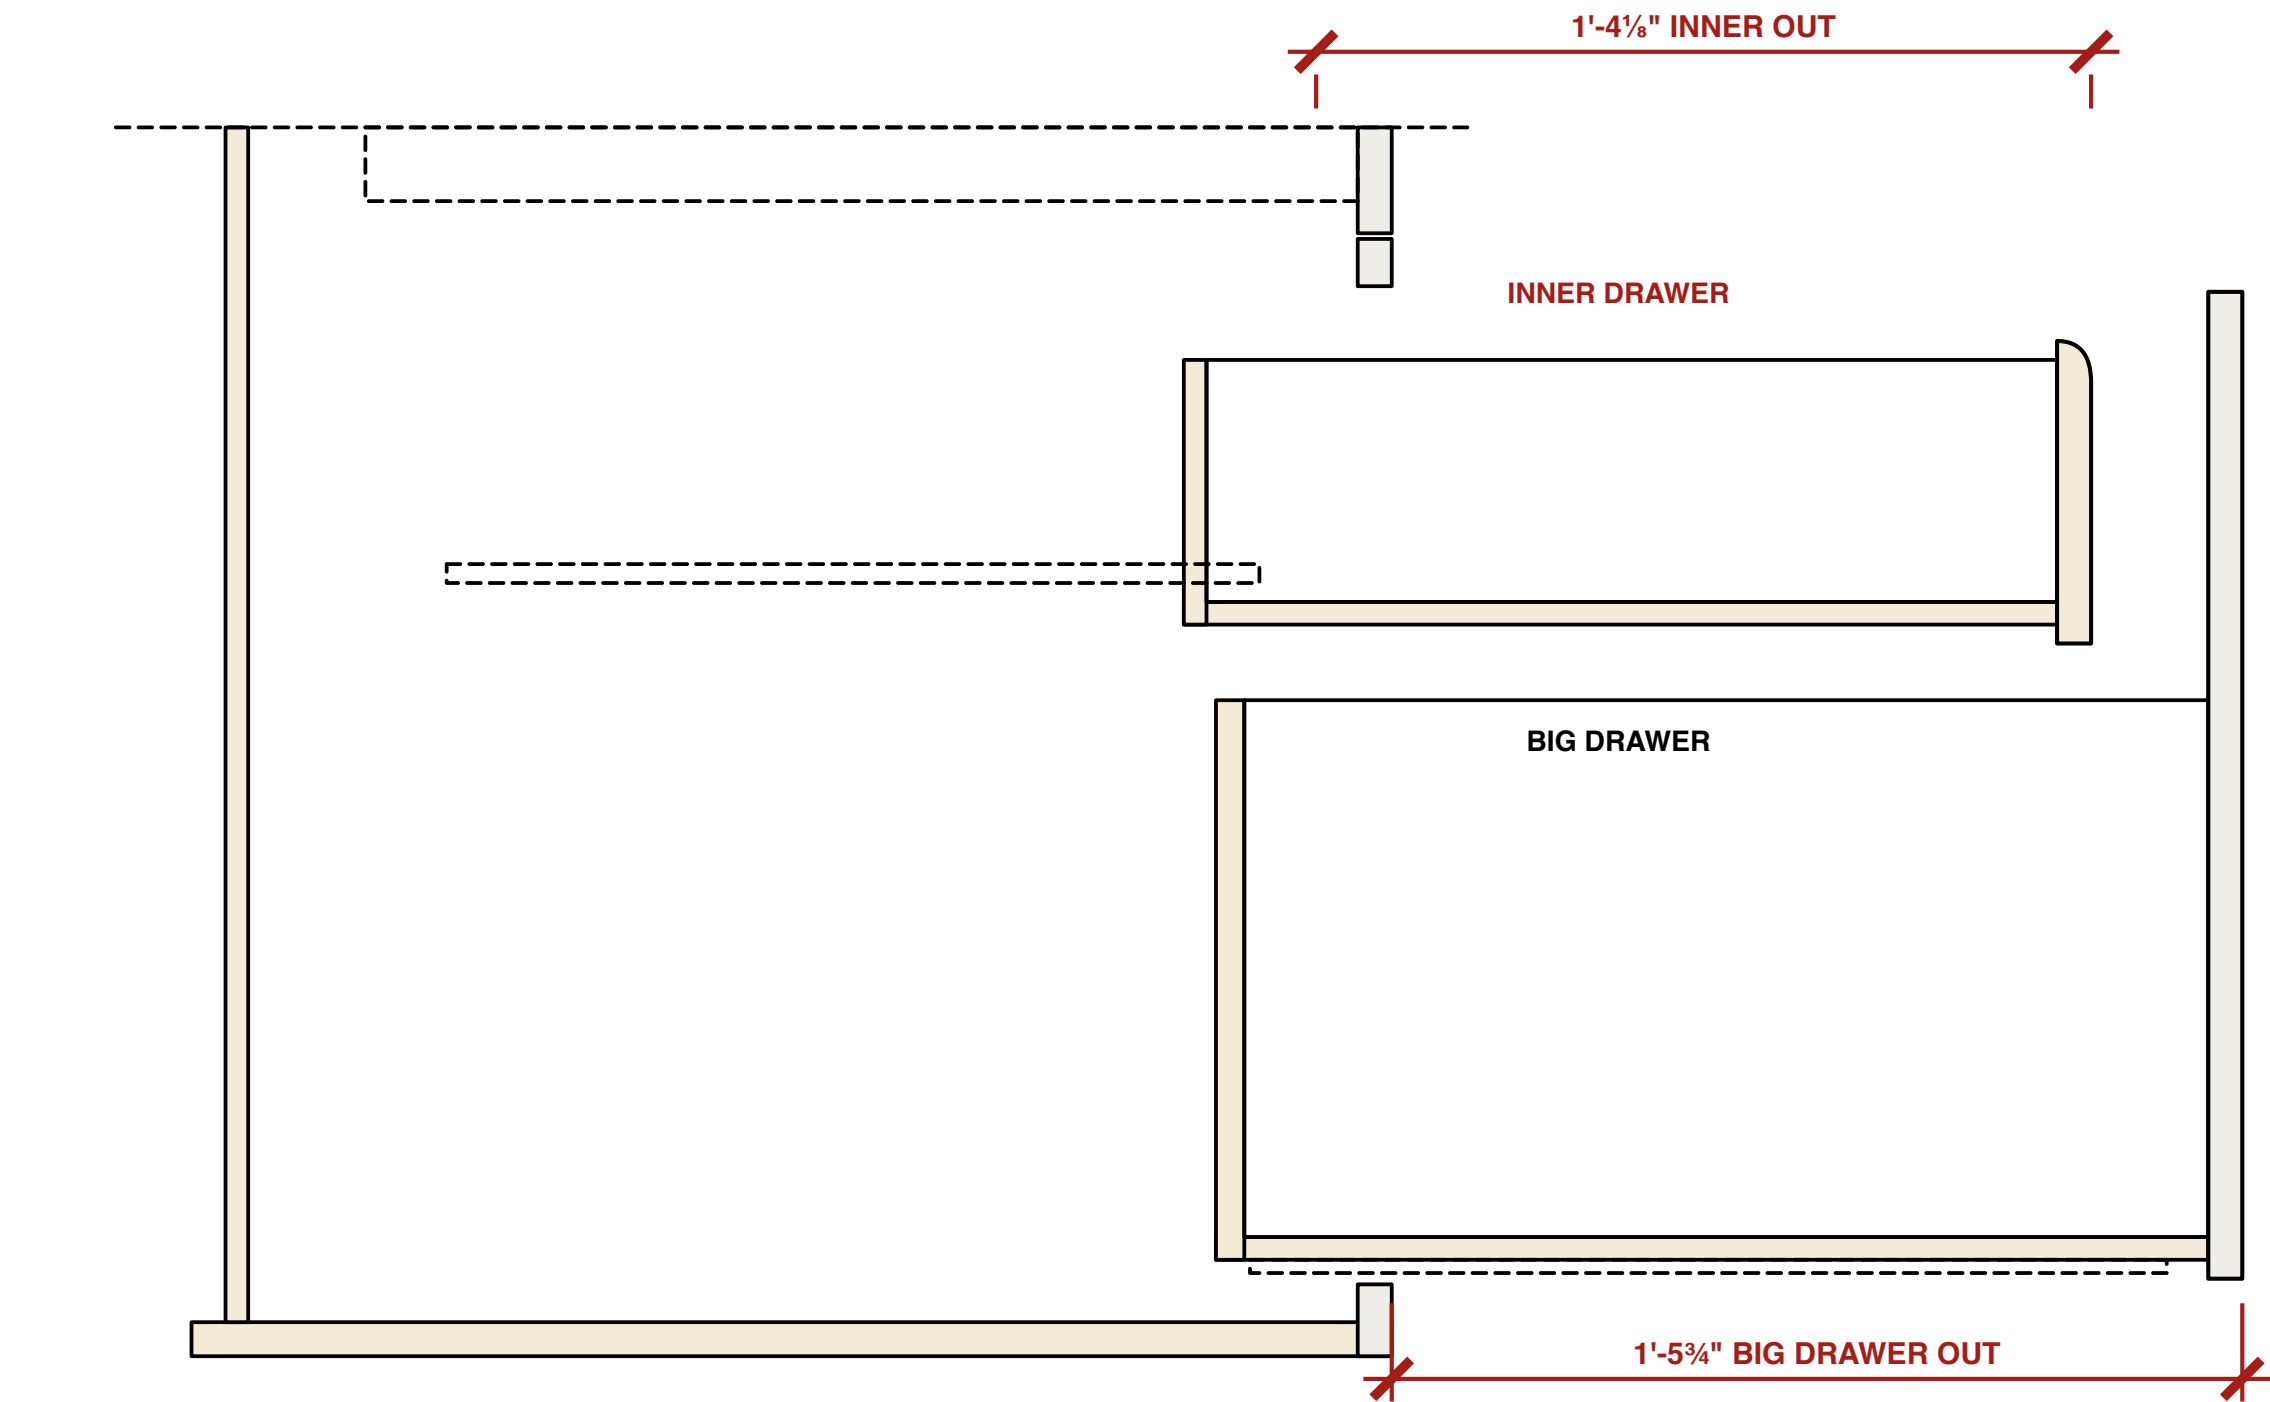

PROJECT
A Study in Teak — Vanity — Drawer Within

SHEET
2 · open
The big drawer, and a drawer inside it

SCALE
1:4 @ A3

DATE
30.09.2026

REV
2

DRAWING
AST-DR-022 · 13 of 18

SIZES

THE SAME DRAWER IN ALL THREE SCHEMES

SCHEME	BIG FRONT	INNER FRONT	INNER BOX W
Normal	2'-2¾" × 1'-3¼"	2'-⅝" × 3¾"	1'-11¾" · L
B	3'-8¾" × 1'-3¼"	3'-6⅝" × 3¾"	3'-5¾" · U
C	2'-8¾" × 1'-8½"	2'-6½" × 6¼"	2'-5¾" · U

Scheme C (chosen): inner box 1'-6¼" deep, 5½" high, ½" ply; notch 9⅞" wide.



PROJECT A Study in Teak — Vanity — Drawer Within	SHEET Sizes The big drawer, and a drawer inside it	SCALE NTS	DATE 30.09.2026	REV 2	DRAWING AST-DR-022 · 14 of 18
---	--	--------------	--------------------	----------	----------------------------------

HARDWARE

Big drawer	Undermount runners, full extension, push-to-open. Its sides stop at 1'-1 ⁵ / ₈ " to pass under the inner.
Inner drawer	Side-mounted runners 1'-3 ³ / ₄ ", full extension, on the carcass partitions at 1'-4 ¹ / ₈ "–1'-4 ¹ / ₂ ". Independent.
Inner front	³ / ₄ " BWP, teak veneer both faces, top edge scooped for a finger. No handle.

3 · PLAN

SCALE 1:4 (3" = 1'-0") @ A3 · BOTH DRAWERS SHUT · THE PIPE DROPS THROUGH BOTH NOTCHES

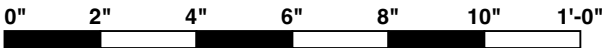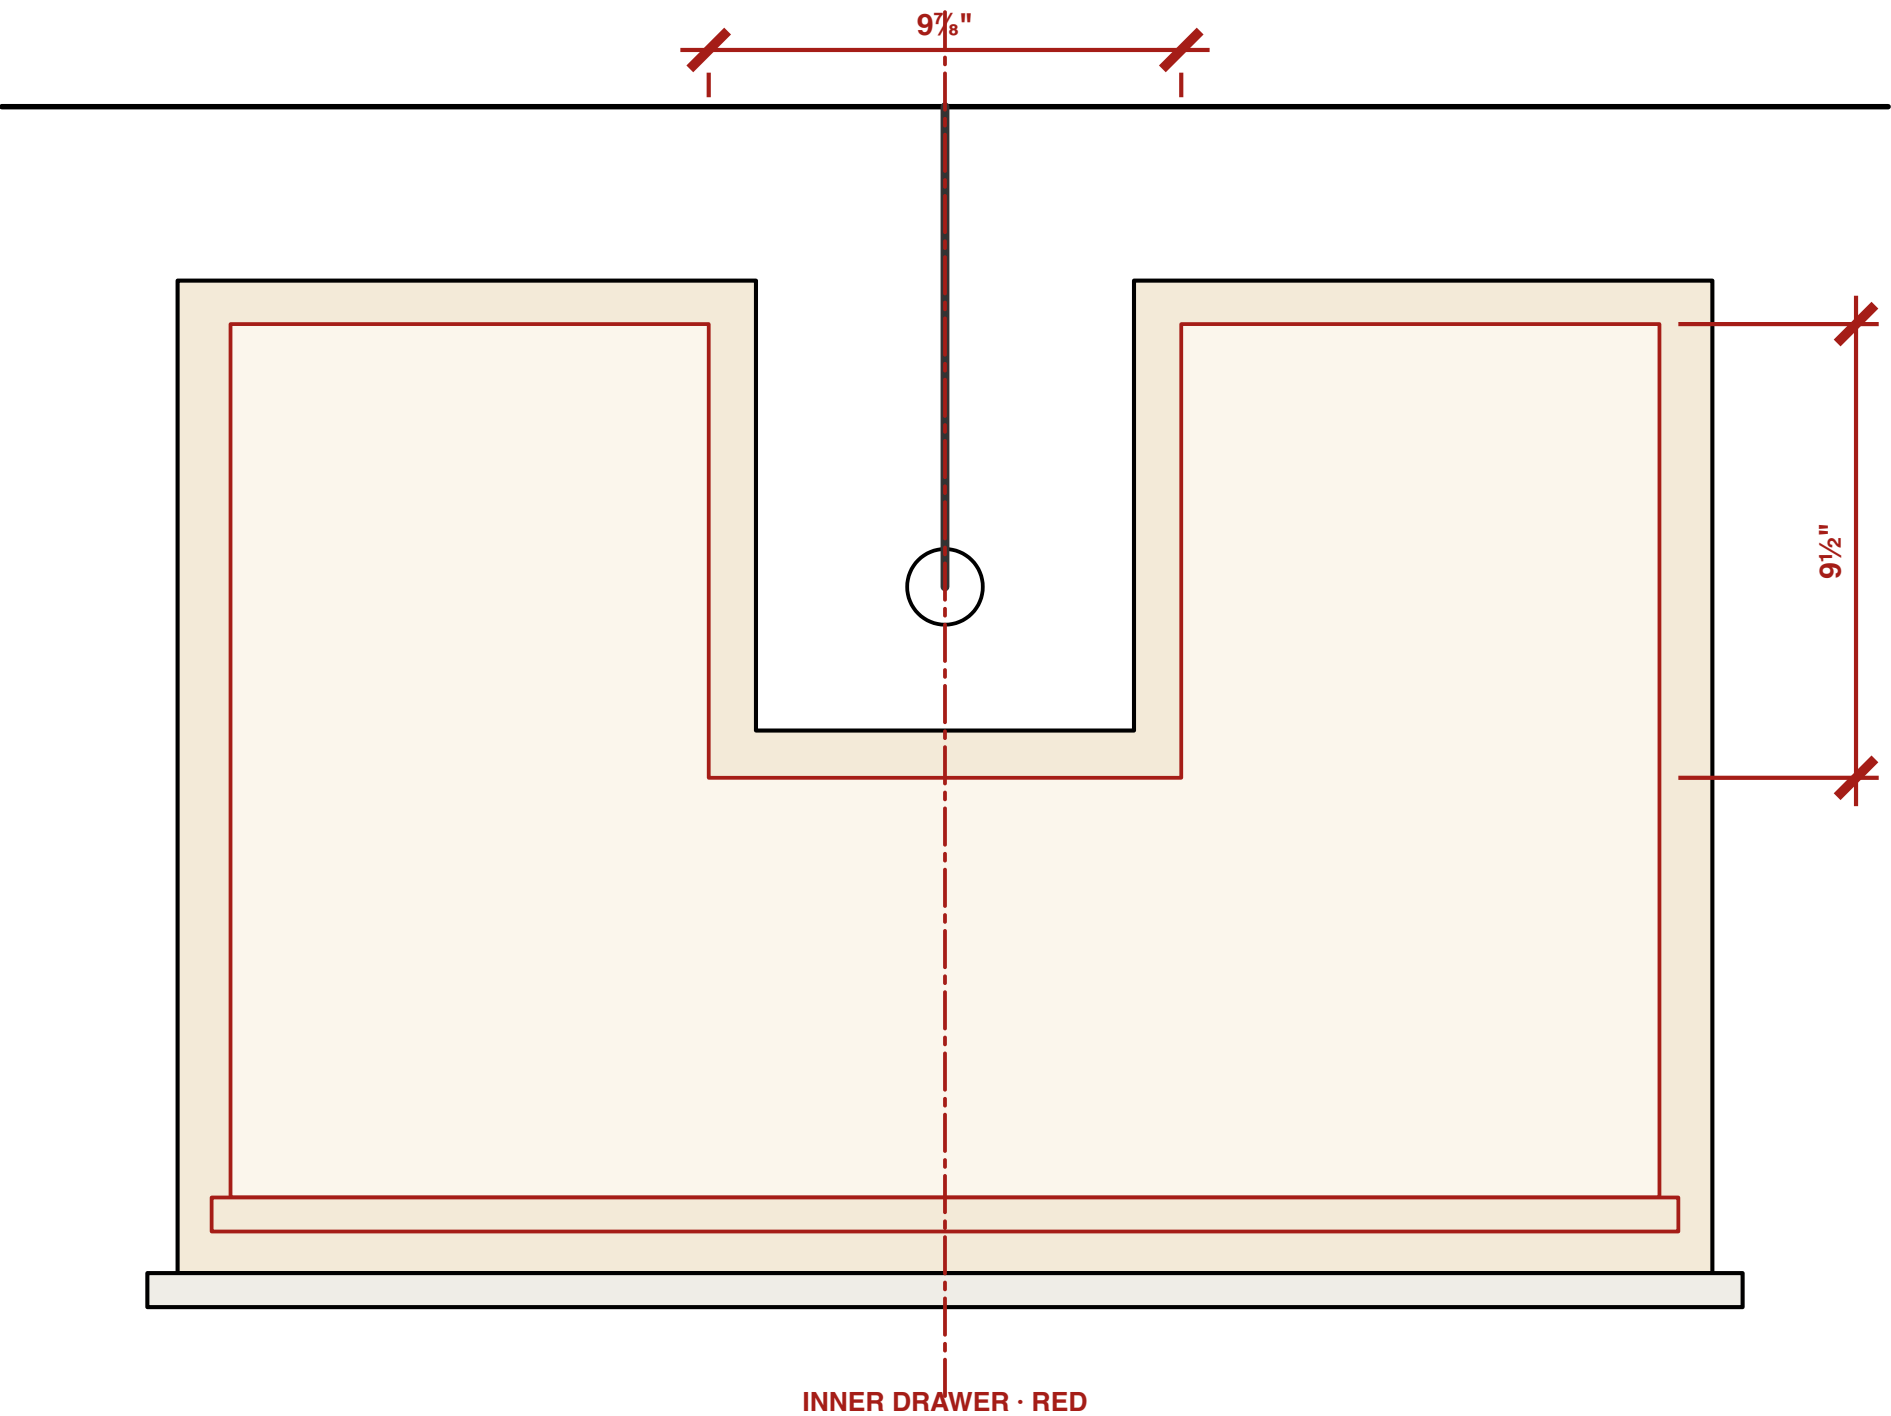

PROJECT
A Study in Teak — Vanity — Drawer Within

SHEET
3 · plan
The big drawer, and a drawer inside it

SCALE
1:4 @ A3

DATE
30.09.2026

REV
2

DRAWING
AST-DR-022 · 16 of 18

NOTES

REVISION 2

Open the big drawer: the inner one stays put. Pull it
and it comes out 1'-4¹/₈" behind the big front, over the
bottles — the tray in the kitchen drawer photographed.

Both are U-boxes. The waste pipe drops through their
notches whichever drawer is shut; neither may be solid
across the back.

It can never pass the big front — that front is solid.



Shut, it stands 7⁷/₈" behind it.

Below the inner drawer: 1'-3³/₄" clear — tall bottles stand.

Normal version: the pipe is off centre, which leaves
the inner drawer a 1" right arm. Too thin to keep — that
arm is left off and the inner drawer is an L.

4 · FRONT

SCALE 1:5 @ A3 · THE INNER DRAWER HIDES BEHIND THE BIG FRONT · MARBLE BANK, FLOOR TO COUNTER

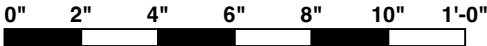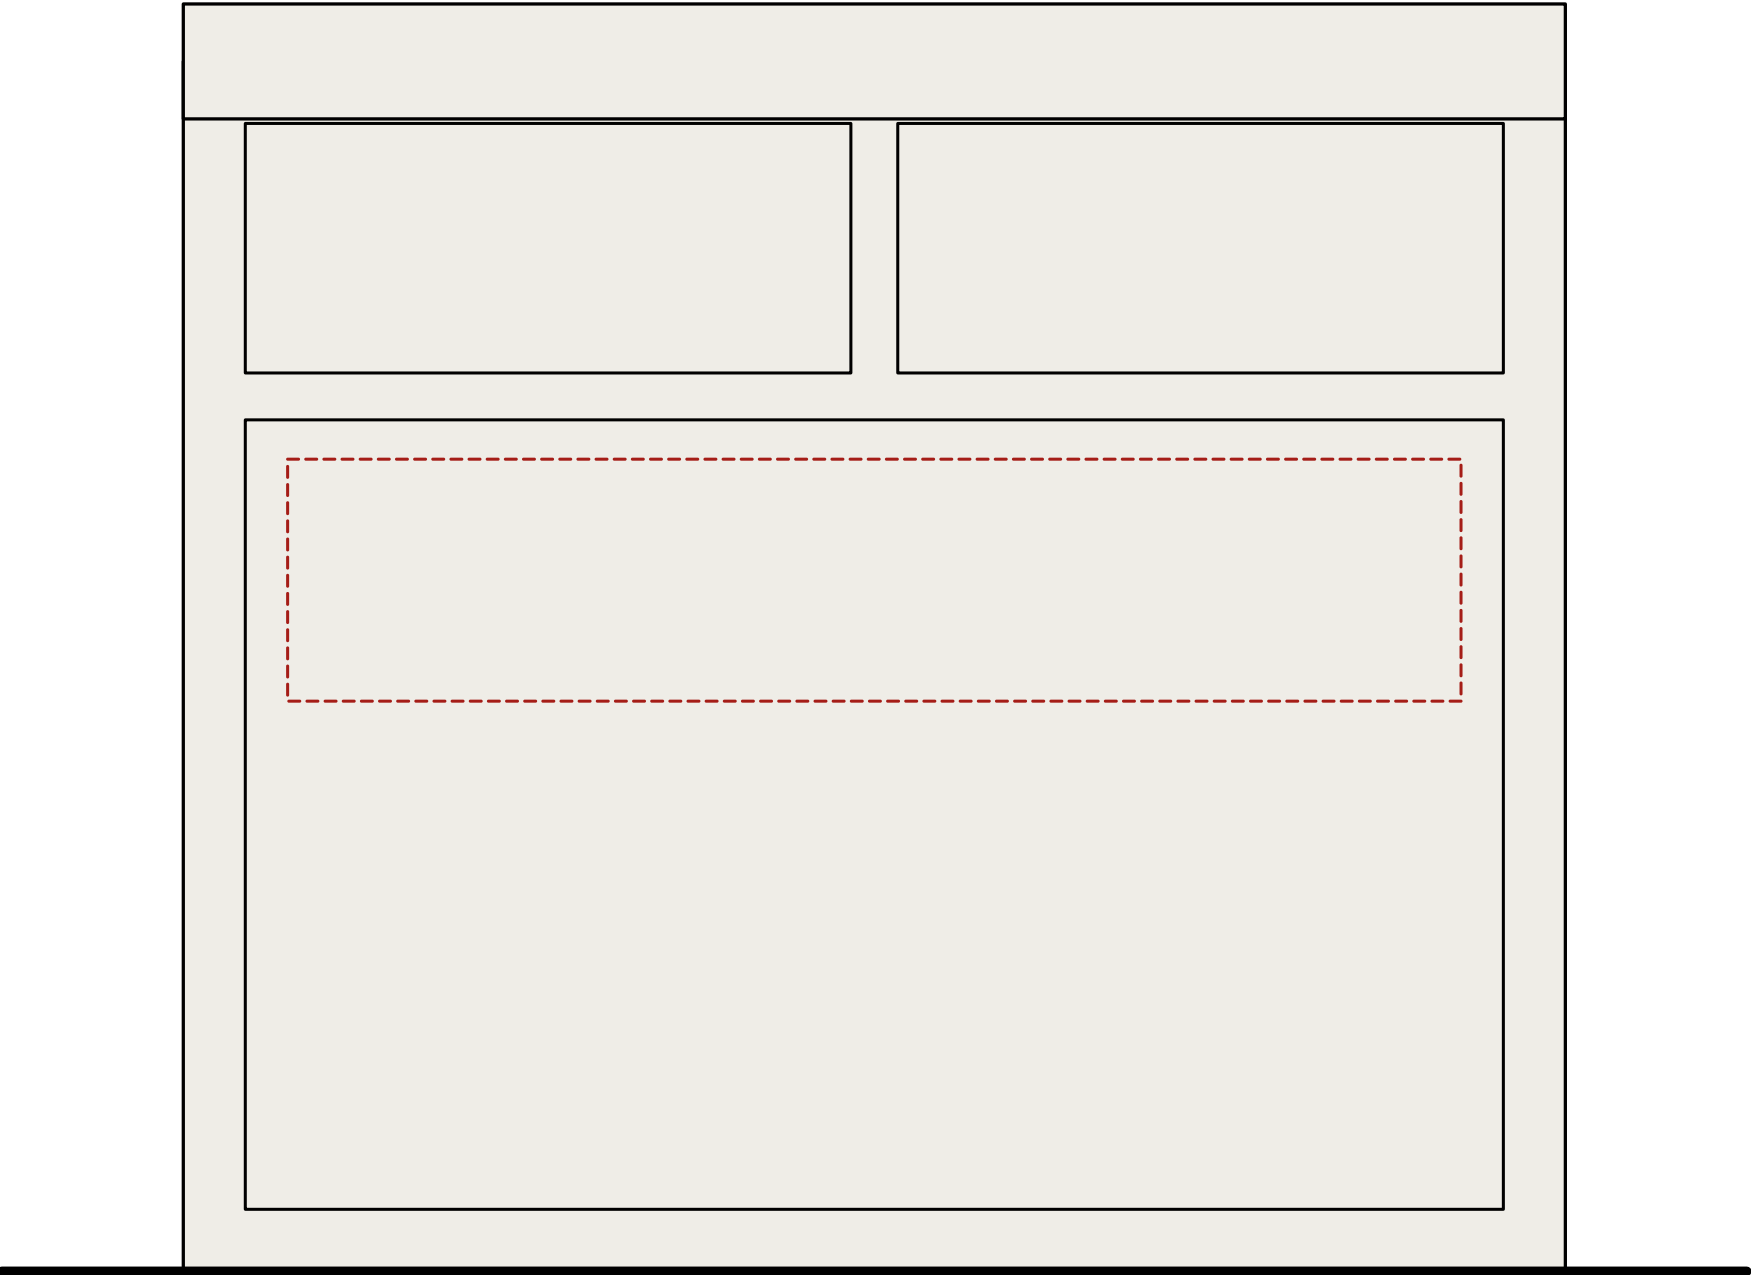

PROJECT
A Study in Teak — Vanity — Drawer Within

SHEET
4 · front
The big drawer, and a drawer inside it

SCALE
1:5 @ A3

DATE
30.09.2026

REV
2

DRAWING
AST-DR-022 · 18 of 18