



FRONT

MARBLE THE FULL 5 FT · THE BOWL SITS UNDER THE FAUCET, 6 IN RIGHT OF CENTRE

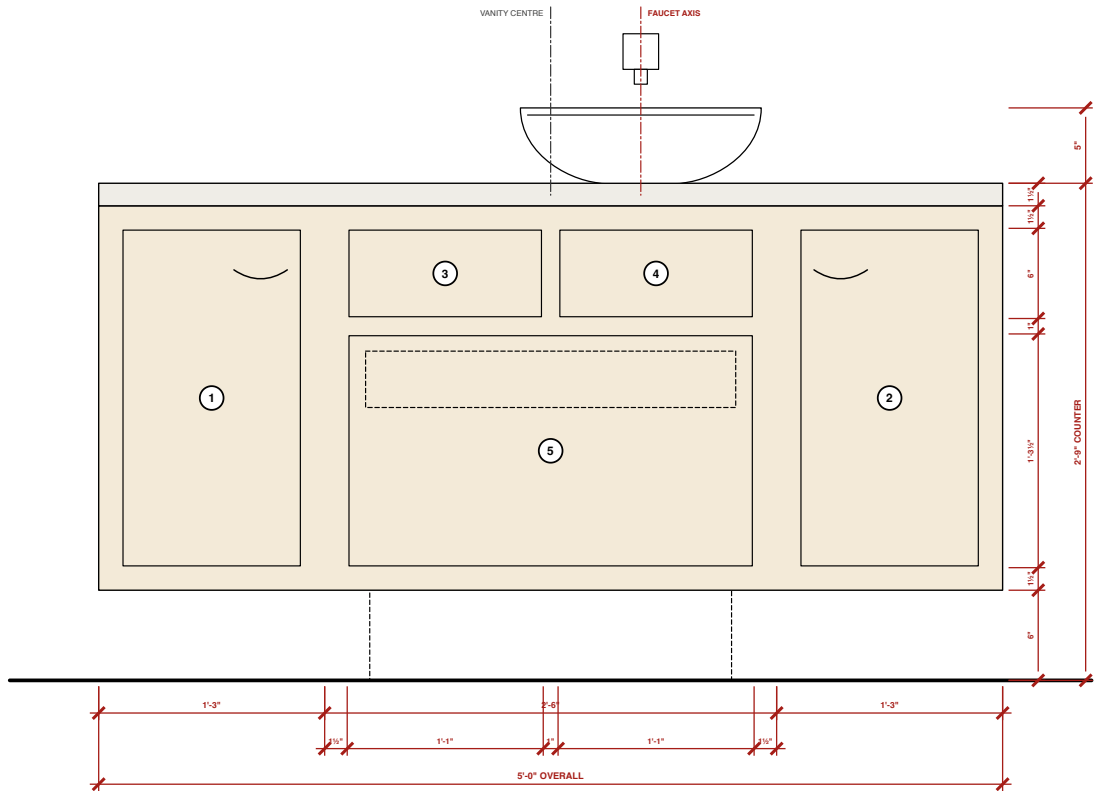

PLAN

FROM ABOVE · WALL AT THE TOP

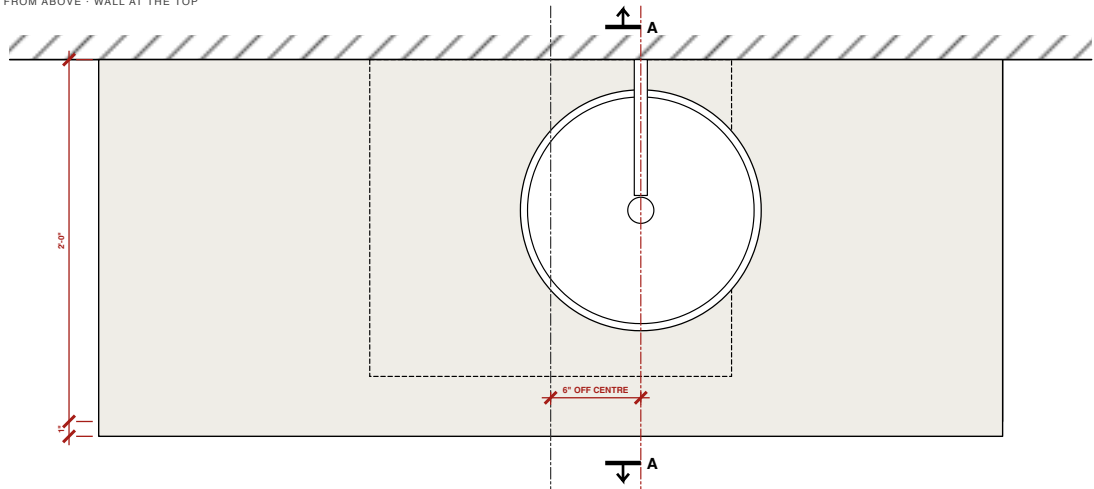

SECTION KEY

- (A) Hanging cleat (B) Big drawer, U-box (C) Waste Ø1½" and P-trap (D) Support, set back 3" (E) Wall spout (F) Ply sub-top (G) Inner drawer

NOTES


REVISION 1

Symmetric about the vanity's centre — except the bowl, which has to sit under the faucet, 6" right of it.
The waste drops through the right-hand TOP drawer as well as the big one: both are U-boxes (see section).

OPEN — bowl Ø1'-4" x 5" and the spout are assumed.
With the bowl on a 2'-9" counter its rim is at 3'-2".
OPEN — the support's design: reference photos to come.


SECTION A-A

ON THE FAUCET AXIS

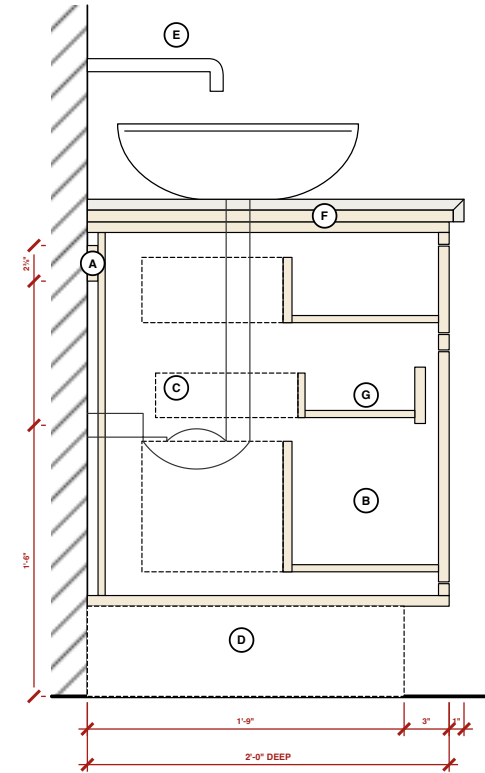


DETAIL 2 · THE BIG DRAWER

PLAN · INNER DRAWER DASHED

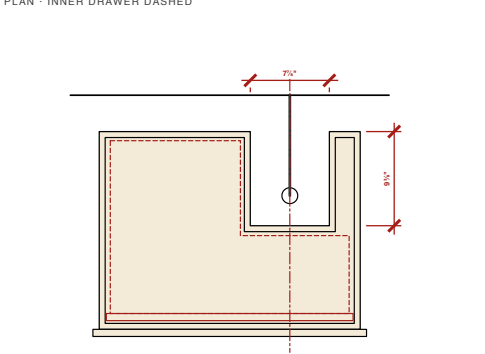

DETAIL 1 · THE MARBLE EDGE

SECTION

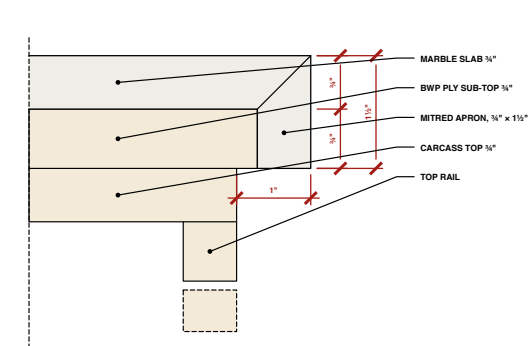

FRONTS

SIZES ARE THE FRONT ITSELF · ¼" GAP ALL ROUND

No.	WHAT	W x H	FT-IN
1	Door, cup pull	11¼" x 1'-10¼"	11¼" x 1'-10¼"
2	Door, cup pull	11¼" x 1'-10¼"	11¼" x 1'-10¼"
3	Top drawer, push-open	1'-½" x 5½"	1'-½" x 5½"
4	Top drawer, push-open	1'-½" x 5½"	1'-½" x 5½"
5	Big drawer, U-box, push-open	2'-2¼" x 1'-3¼"	2'-2¼" x 1'-3¼"
5a	Inner drawer, finger scoop	2'-½" x 3¼"	2'-½" x 3¼"

MATERIALS

THE ROOM'S PALETTE — NOTHING NEW

Top	Beige-gold marble, the bathroom stone. ½" slab on a ¼" BWP sub-top, mitred 1½" apron, polished.
Carcass	¾" BWP / marine ply, teak veneer both faces. Every edge sealed — it stands in a wet room.
Fronts	¾" BWP, teak veneer, ¼" solid teak flipping.
Runners	Undermount, full extension. Drawers push-to-open — no handles on them; the doors keep cup pulls.
Fittings	Chrome — already bought. Door cup pulls to match.
Hanging	¾" ply cleat on the wall, 2'-3½"-2'-5¼" high.
Inner	A U-box on its own runners, above the big drawer's low sides — see AST-DR-022.

A STUDY IN TEAK

Particulars of the room

VANITY — NORMAL

Marble full length · Door · Drawers · Door

SCALE AS NOTED @ A3	DATE 23.09.2026
REV 1 — as sketched	DWG AST-DR-019

PROJECT
A Study in Teak — Vanity — Normal

SHEET
General arrangement — the whole sheet
each view follows at its own scale, pages 2 to 10

SCALE
NTS

DATE
23.09.2026

REV
1

DRAWING
AST-DR-019 · 1 of 10

SCALE 1:8 (1½" = 1'-0") @ A3 · MARBLE THE FULL 5 FT · THE BOWL SITS UNDER THE FAUCET, 6 IN RIGHT OF CENTRE

Technical drawing of a vanity unit showing front and side elevations with dimensions and labels.

Front Elevation:

- Overall width: 5'-0" OVERALL
- Overall height: 2'-9" COUNTER
- Labels: 1 (Left cabinet door), 2 (Right cabinet door), 3 (Left drawer), 4 (Right drawer), 5 (Central cabinet door)
- Dimensions (from left to right): 1'-3", 1 1/2", 1'-1", 1", 1'-1", 1 1/2", 1'-3"
- Dimensions (from top to bottom): 5", 1 1/2", 1 1/2", 6", 1", 1 1/2", 1'-3 1/2", 6", 1 1/2"

Side Elevation:

- Overall width: 5'-0" OVERALL
- Overall height: 2'-9" COUNTER
- Labels: 1 (Left cabinet door), 2 (Right cabinet door), 3 (Left drawer), 4 (Right drawer), 5 (Central cabinet door)
- Dimensions (from left to right): 1'-3", 1 1/2", 1'-1", 1", 1'-1", 1 1/2", 1'-3"
- Dimensions (from top to bottom): 5", 1 1/2", 1 1/2", 6", 1", 1 1/2", 1'-3 1/2", 6", 1 1/2"



Labels:

- VANITY CENTRE
- FAUCET AXIS



SECTION A-A

SCALE 1:8 (1½" = 1'-0") @ A3 · ON THE FAUCET AXIS

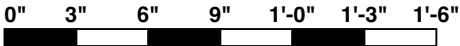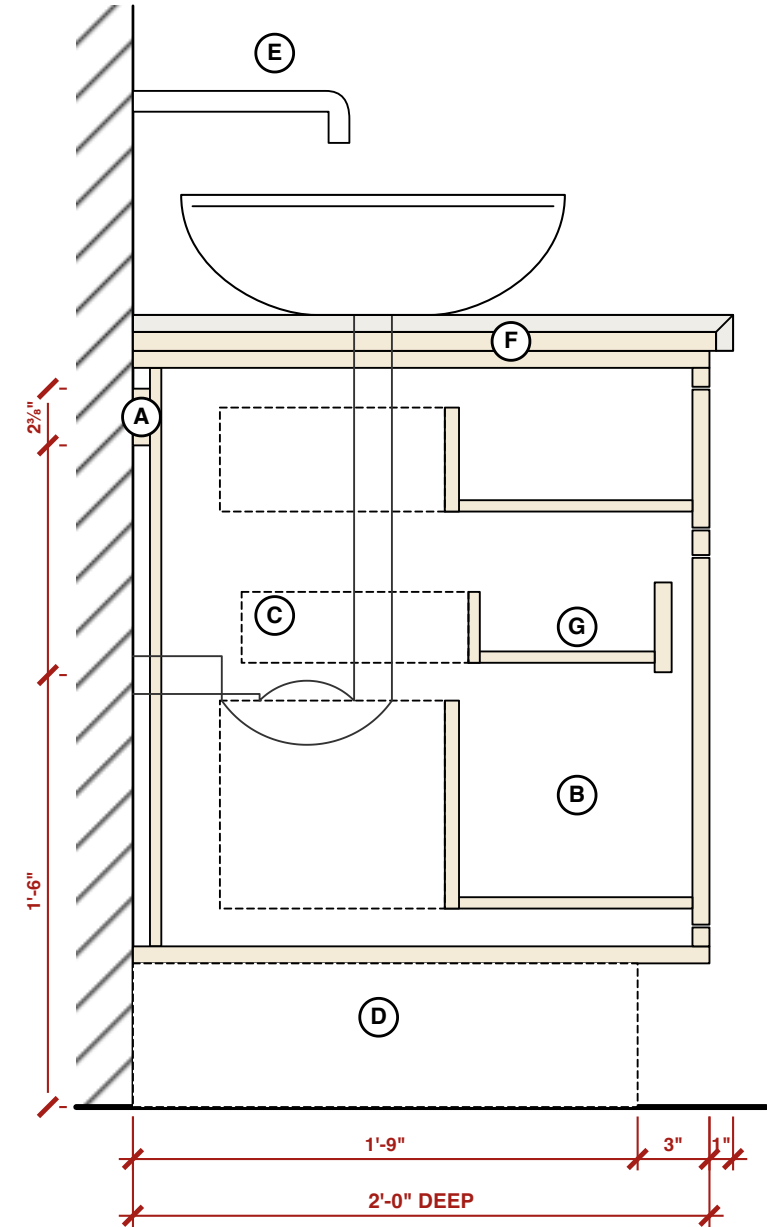

PROJECT
A Study in Teak — Vanity — Normal

SHEET
Section A-A
Marble full length · Door · Drawers · Door

SCALE
1:8 @ A3



DATE
23.09.2026

REV
1

DRAWING
AST-DR-019 · 3 of 10

DETAIL 1 · THE MARBLE EDGE

SCALE 1:1 (FULL SIZE) @ A3 · SECTION

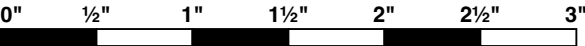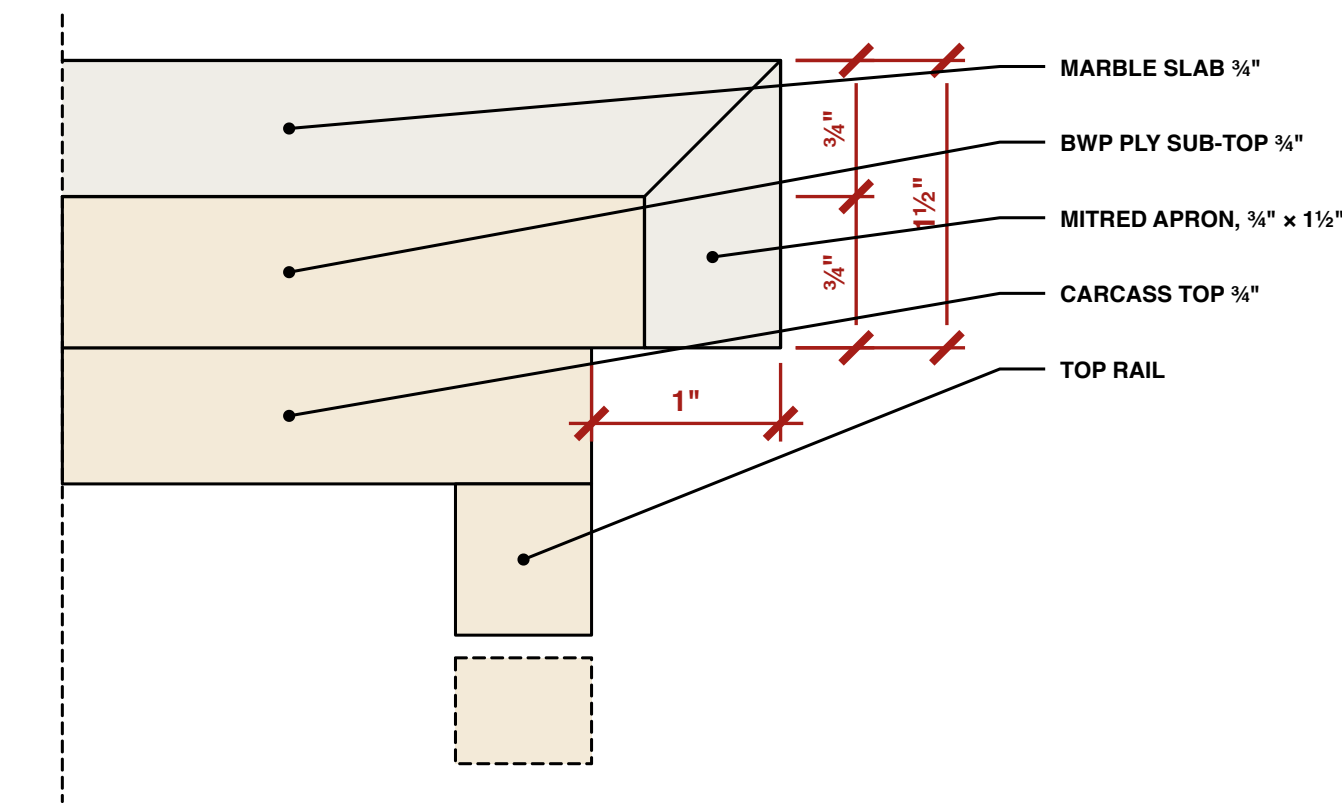

PROJECT
A Study in Teak — Vanity — Normal

SHEET
Detail 1 · the marble edge
Marble full length · Door · Drawers · Door

SCALE
1:1 @ A3

DATE
23.09.2026

REV
1

DRAWING
AST-DR-019 · 4 of 10

FRONTS

SIZES ARE THE FRONT ITSELF · 1⁄8" GAP ALL ROUND

No.	WHAT	W × H	FT-IN
1	Door, cup pull	11¾" × 1'-10¼"	11¾" × 1'-10¼"
2	Door, cup pull	11¾" × 1'-10¼"	11¾" × 1'-10¼"
3	Top drawer, push-open	1'-¾" × 5¾"	1'-¾" × 5¾"
4	Top drawer, push-open	1'-¾" × 5¾"	1'-¾" × 5¾"
5	Big drawer, U-box, push-open	2'-2¾" × 1'-3¼"	2'-2¾" × 1'-3¼"
5a	Inner drawer, finger scoop	2'-5⁄8" × 3¾"	2'-5⁄8" × 3¾"

PROJECT A Study in Teak — Vanity — Normal	SHEET Fronts Marble full length · Door · Drawers · Door	SCALE NTS	DATE 23.09.2026	REV 1	DRAWING AST-DR-019 · 5 of 10
--	---	--------------	--------------------	----------	---------------------------------

MATERIALS



THE ROOM'S PALETTE — NOTHING NEW

Top	Beige-gold marble, the bathroom stone. ¾" slab on a ¾" BWP sub-top, mitred 1½" apron, polished.
Carcass	¾" BWP / marine ply, teak veneer both faces. Every edge sealed — it stands in a wet room.
Fronts	¾" BWP, teak veneer, ¼" solid teak lipping.
Runners	Undermount, full extension. Drawers push-to-open — no handles on them; the doors keep cup pulls.
Fittings	Chrome — already bought. Door cup pulls to match.
Hanging	¾" ply cleat on the wall, 2'-3½"—2'-5⅞" high.
Inner	A U-box on its own runners, above the big drawer's low sides — see AST-DR-022.

PROJECT A Study in Teak — Vanity — Normal	SHEET Materials Marble full length · Door · Drawers · Door	SCALE NTS	DATE 23.09.2026	REV 1	DRAWING AST-DR-019 · 6 of 10
--	--	--------------	--------------------	----------	---------------------------------

PLAN



SCALE 1:5 @ A3 · FROM ABOVE · WALL AT THE TOP

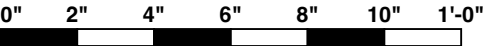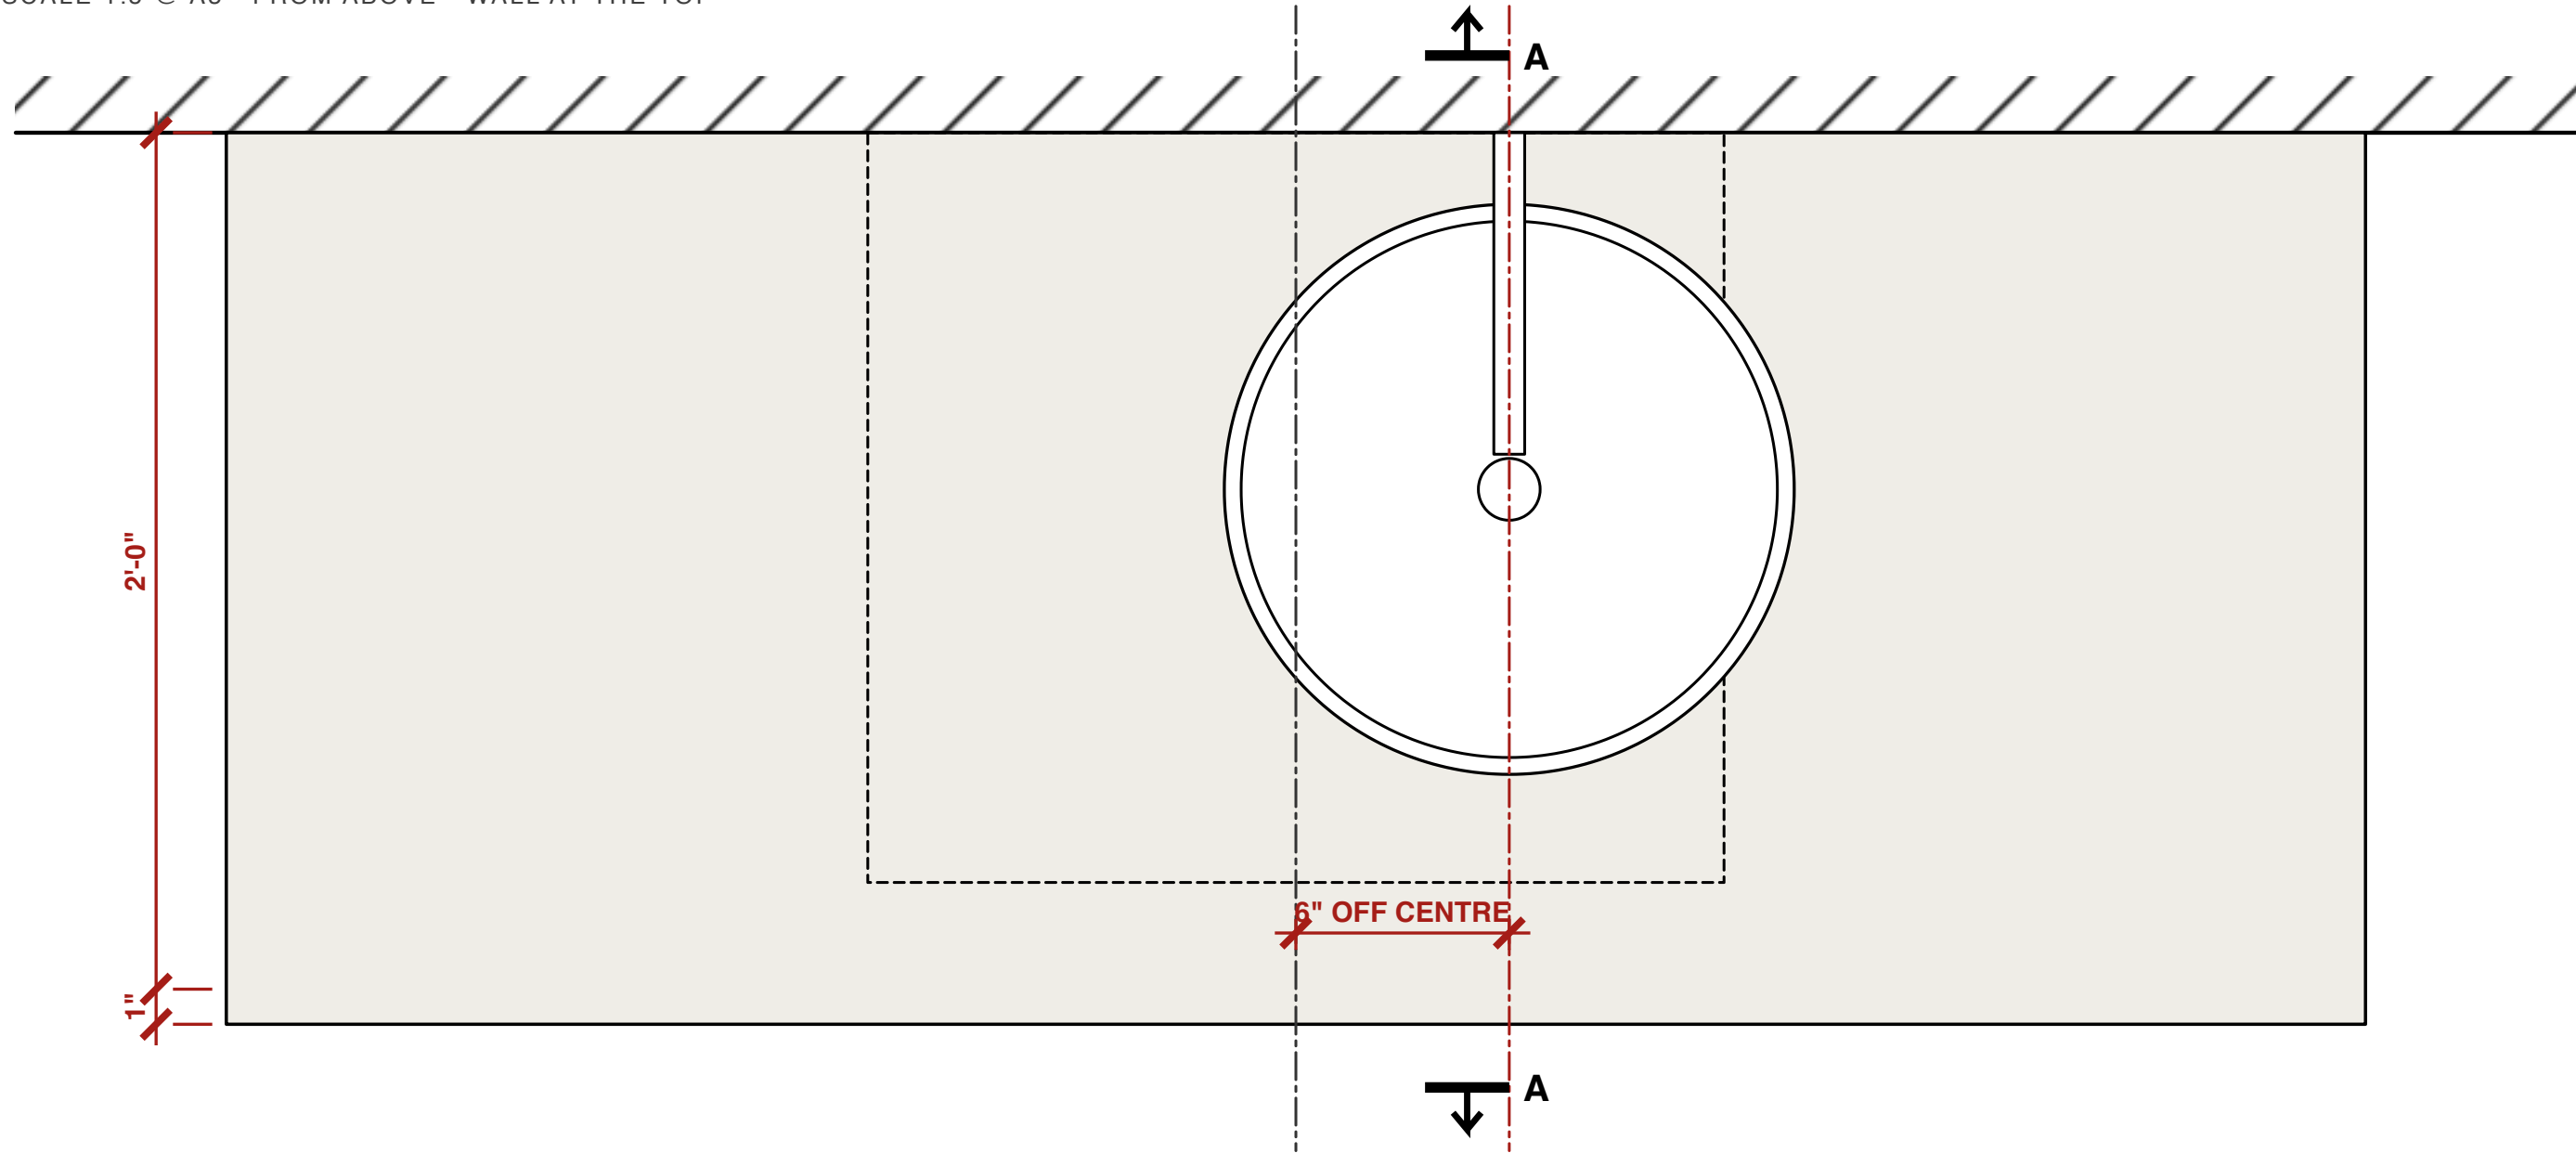

PROJECT A Study in Teak — Vanity — Normal	SHEET Plan Marble full length · Door · Drawers · Door	SCALE 1:5 @ A3	DATE 23.09.2026	REV 1	DRAWING AST-DR-019 · 7 of 10
--	---	-------------------	--------------------	----------	---------------------------------

DETAIL 2 · THE BIG DRAWER

SCALE 1:5 @ A3 · PLAN · INNER DRAWER DASHED

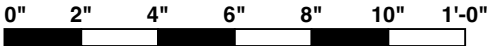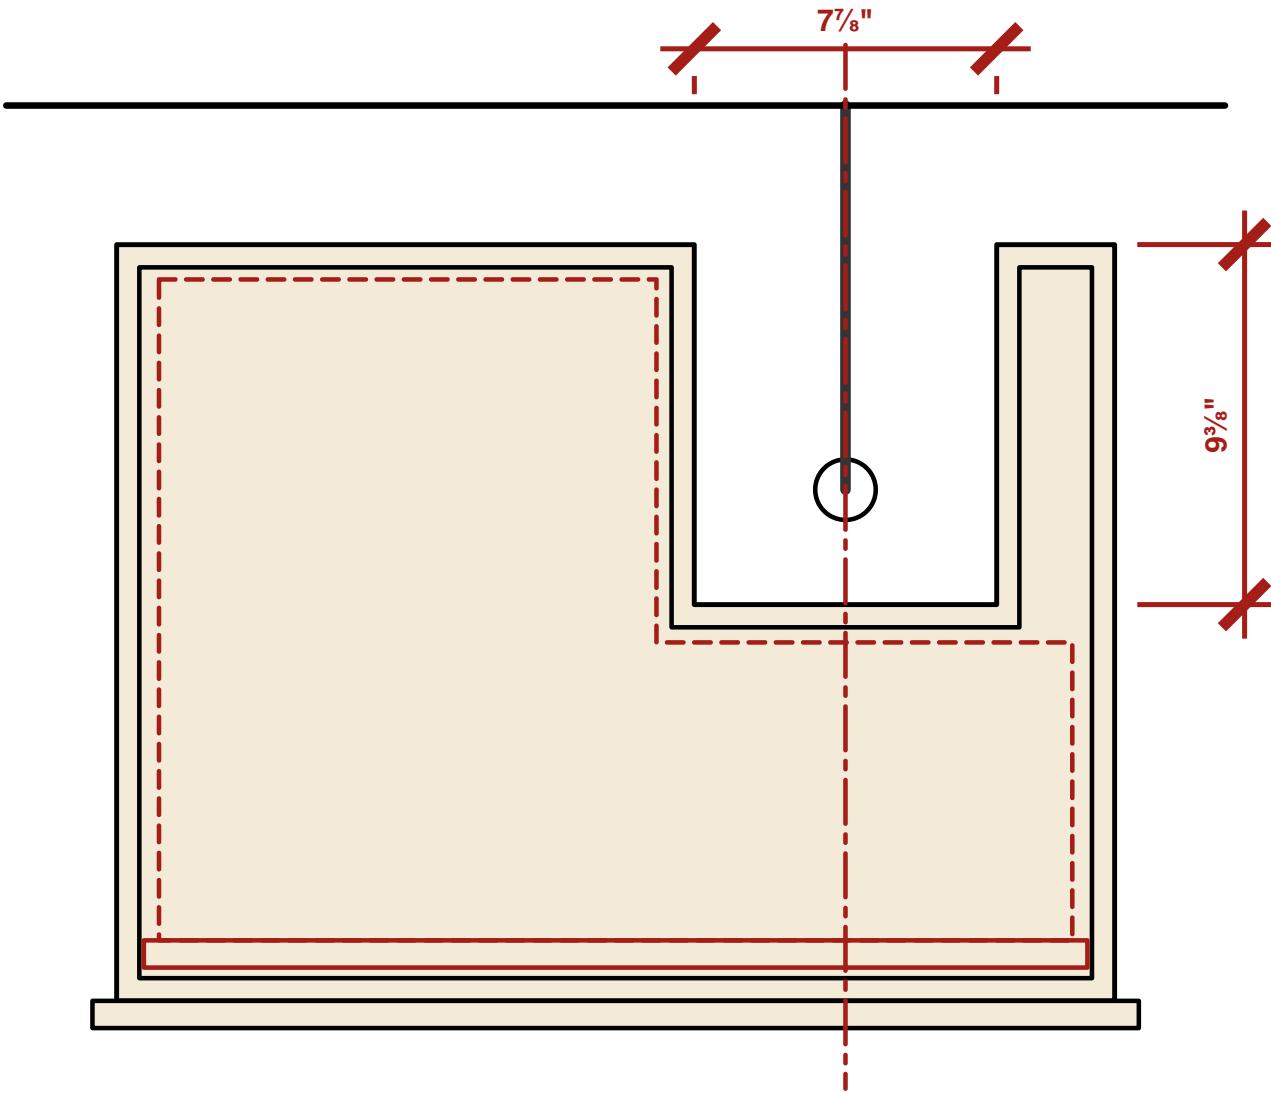

PROJECT	SHEET	SCALE	DATE	REV	DRAWING
A Study in Teak — Vanity — Normal	Detail 2 · the big drawer Marble full length · Door · Drawers · Door	1:5 @ A3	23.09.2026	1	AST-DR-019 · 8 of 10

SECTION KEY

- A

Hanging cleat
- B

Big drawer, U-box
- C

Waste Ø1⁵/₈" and P-trap
- D

Support, set back 3"
- E

Wall spout
- F

Ply sub-top
- G

Inner drawer

PROJECT A Study in Teak — Vanity — Normal	SHEET Section key Marble full length · Door · Drawers · Door	SCALE NTS	DATE 23.09.2026	REV 1	DRAWING AST-DR-019 · 9 of 10
--	--	--------------	--------------------	----------	---------------------------------

NOTES

REVISION 1

Symmetric about the vanity's centre — except the bowl, which has to sit under the faucet, 6" right of it.

The waste drops through the right-hand TOP drawer as well as the big one: both are U-boxes (see section).

OPEN — bowl Ø1'-4" × 5" and the spout are assumed.

With the bowl on a 2'-9" counter its rim is at 3'-2".

OPEN — the support's design: reference photos to come.

PROJECT A Study in Teak — Vanity — Normal	SHEET Notes Marble full length · Door · Drawers · Door	SCALE NTS	DATE 23.09.2026	REV 1	DRAWING AST-DR-019 · 10 of 10
--	--	--------------	--------------------	----------	----------------------------------