



ELEVATION — STUDY WALL

BOOKCASE · PANEL FOR PAINTING · WINDOW

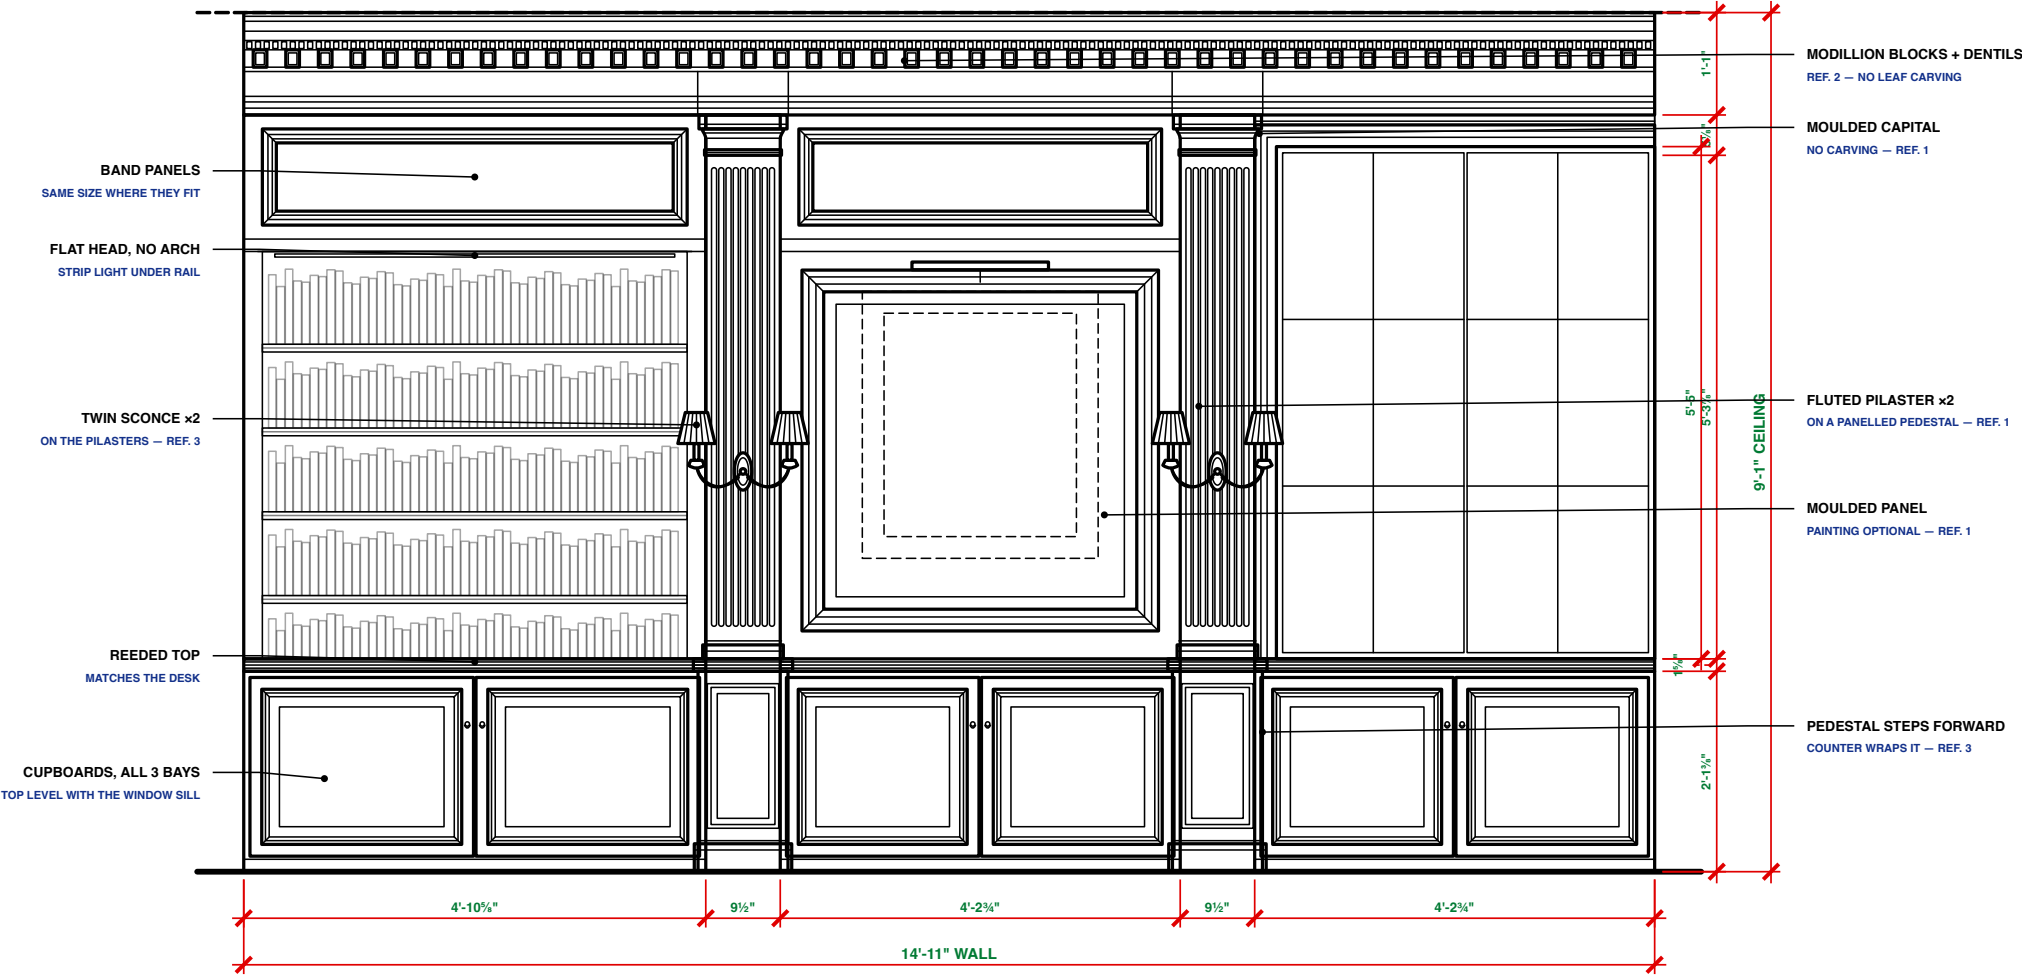


SECTION A-A

THROUGH BOOKCASE

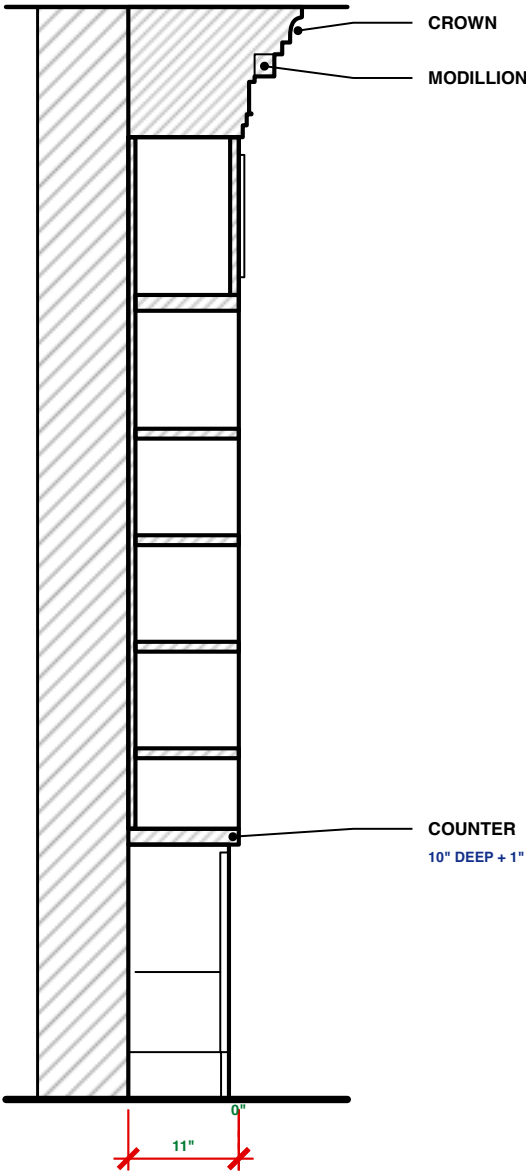

PLAN

CUT AT 3'-11 1/4" · ROOM BELOW, WALL ABOVE

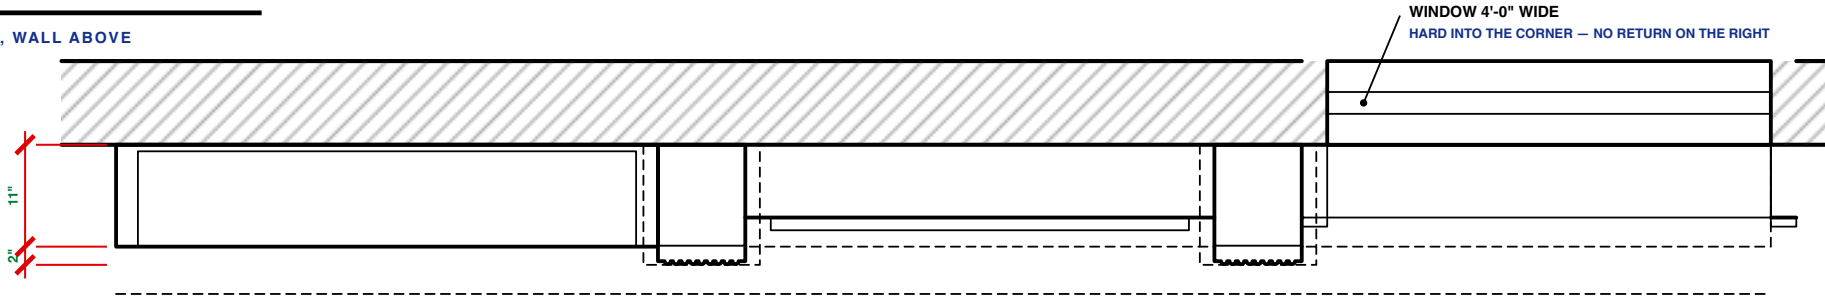

NOTES

REVISION 9

Wall 14 ft 11 in, ceiling 9 ft 1 in (measured).


Centre panel set equal to the window bay so the two pilasters frame a matched pair; the bookcase takes the remainder as the anchor at the end of the wall.

Window measured: 4 ft wide, 5 ft 5 in tall, hard into the right corner. Sill 2 ft 3 in — CONFIRMED.

OPEN: sill 2 ft 3 + height 5 ft 5 + your 1 ft 3 to the ceiling makes 8 ft 11, two inches short of the 9 ft 1 ceiling. Sill and height are drawn as measured, so the head falls 1 ft 5 down, not 1 ft 3. Laser it.

Counter top is set to the sill at 2'-3", so the two are one surface; this datum runs on round to the right wall rail.


Cupboards under all three bays. Gold on handles only.

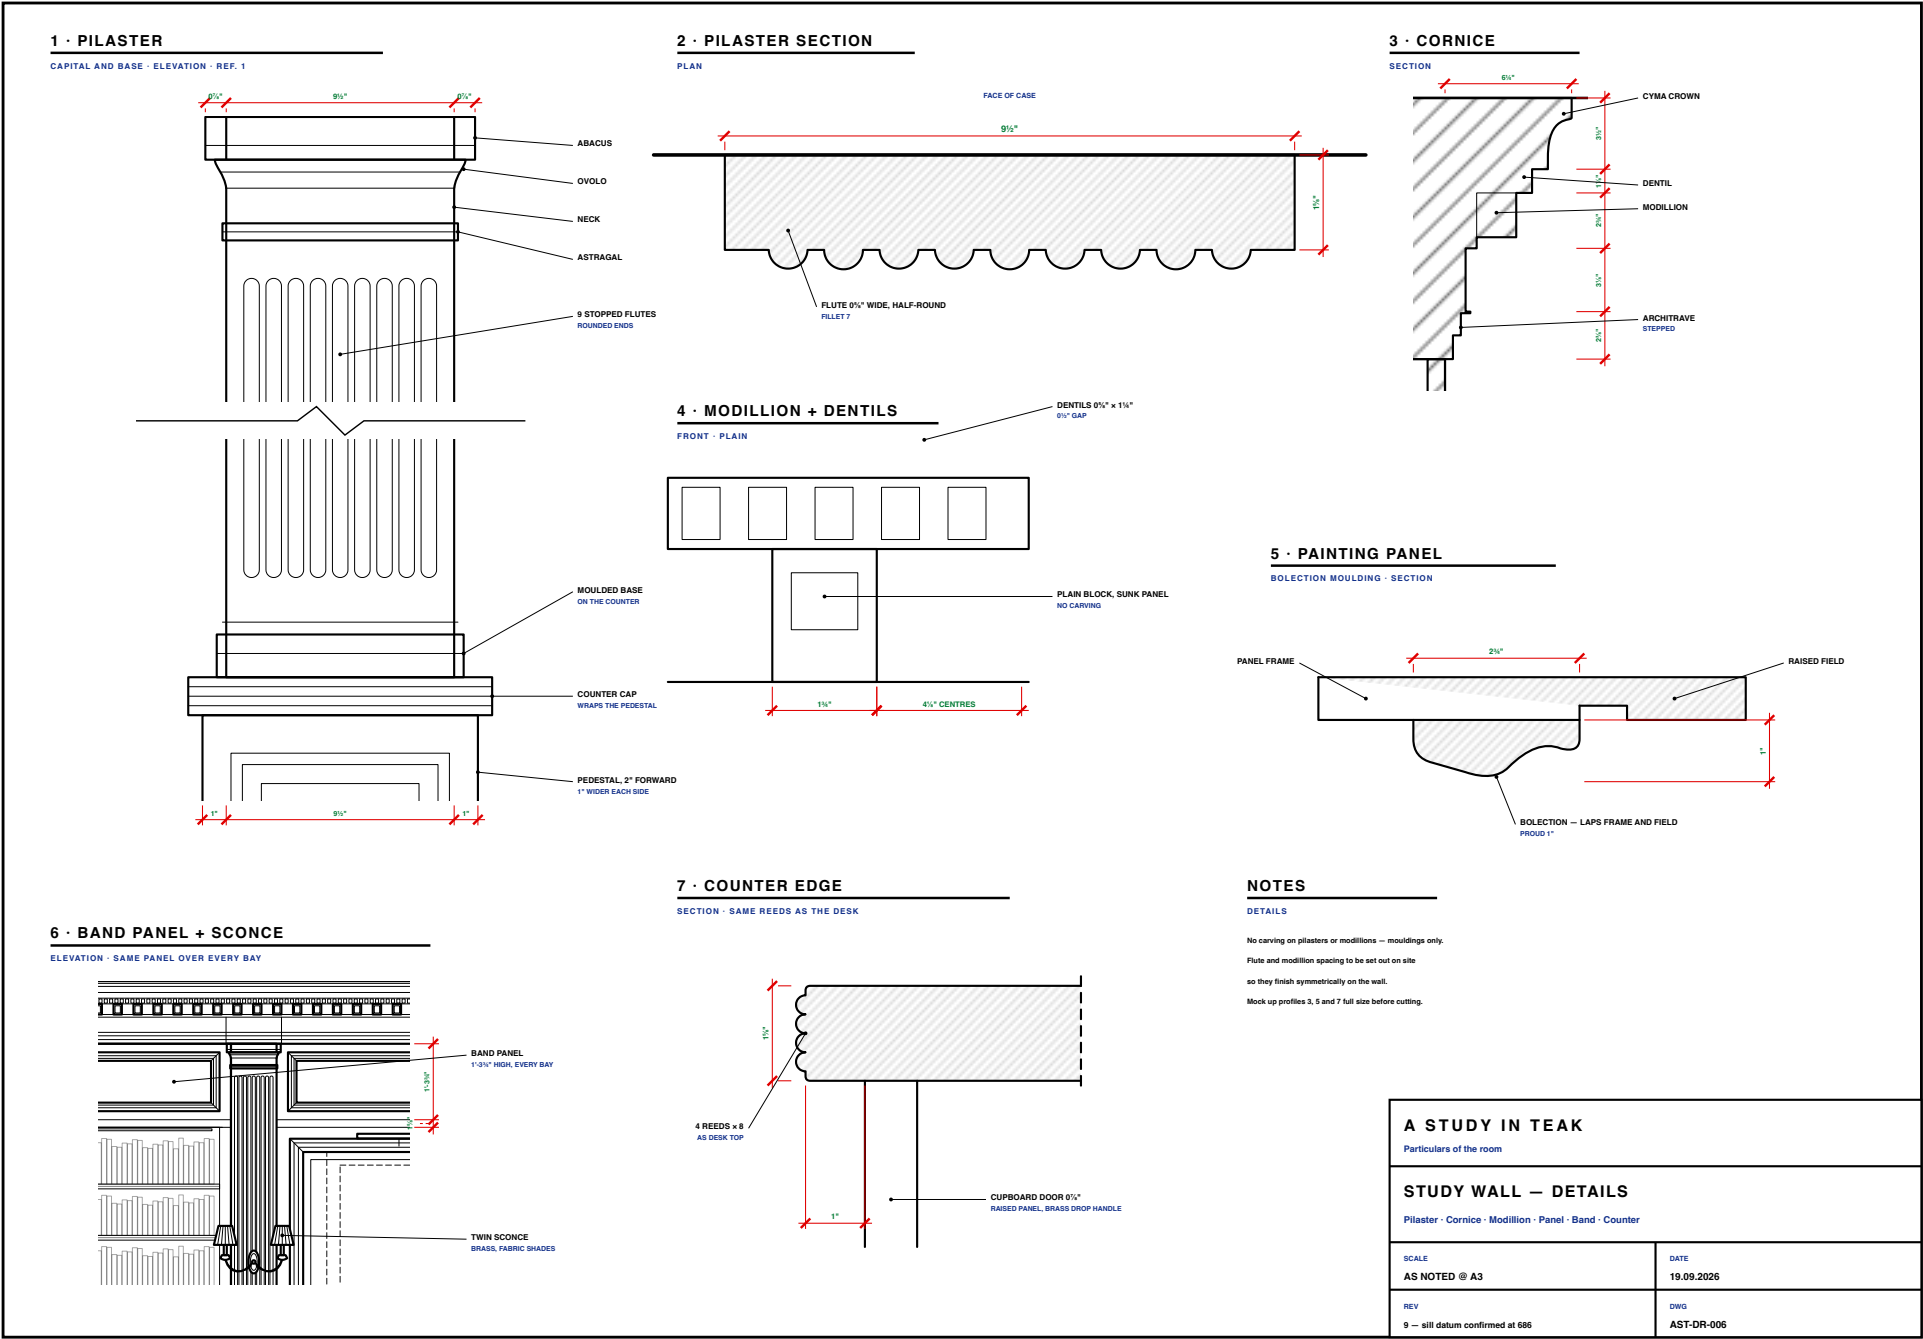

1 · PILASTER

CAPITAL AND BASE · ELEVATION · REF. 1

2
PI

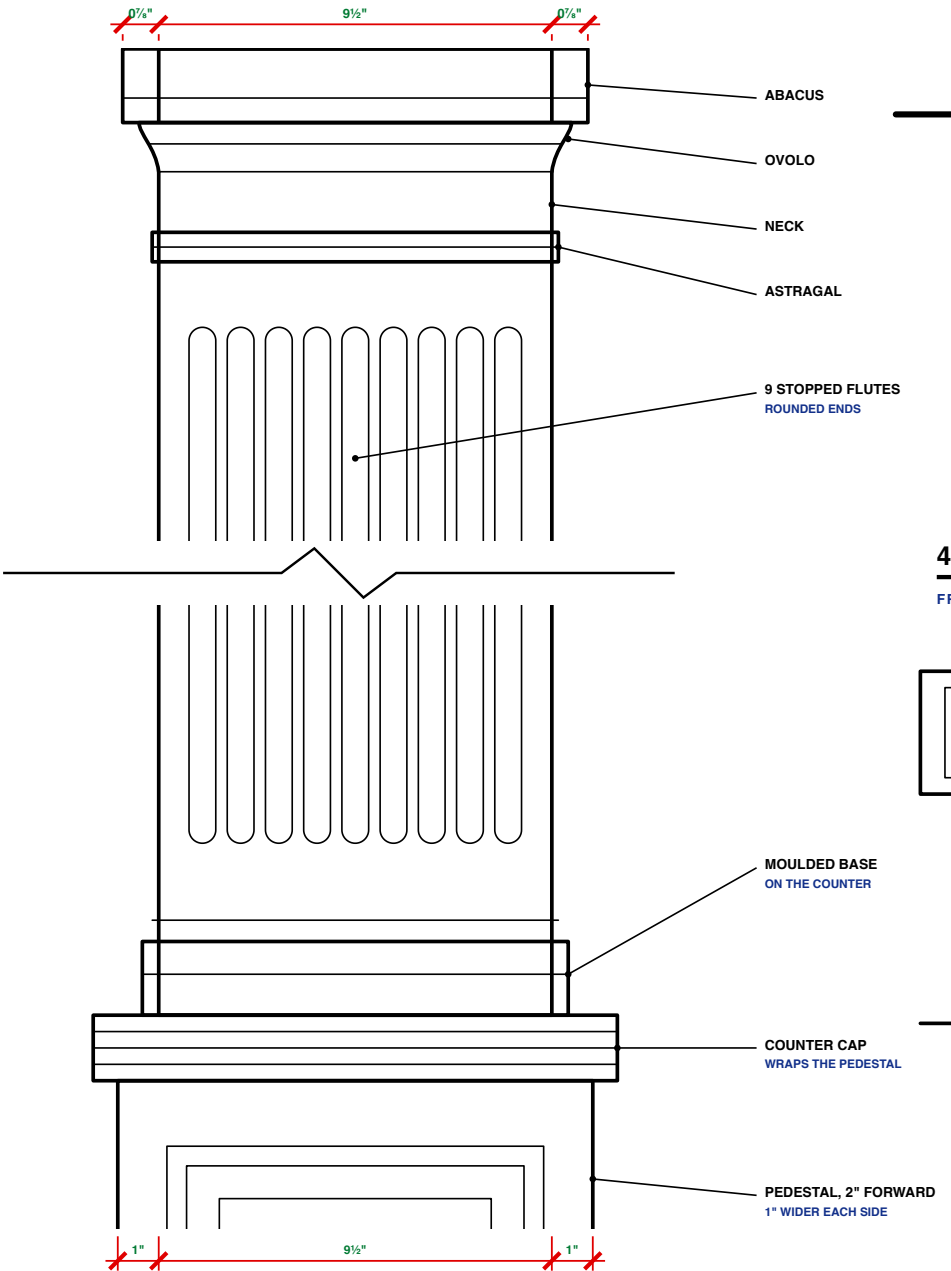


4
FF

2 · PILASTER SECTION

PLAN


FACE OF CASE

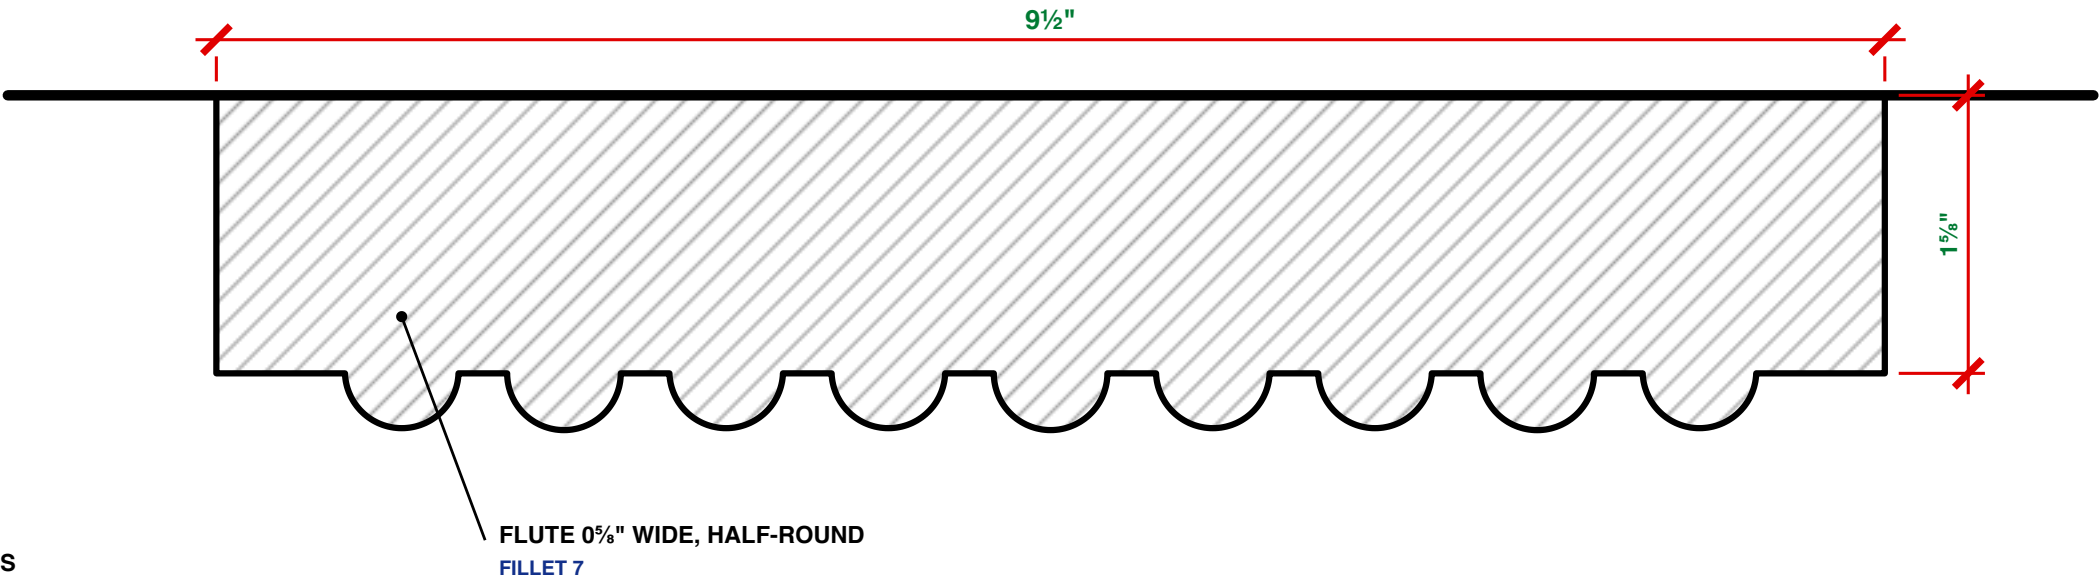

FLUTE 0 5/8" WIDE, HALF-ROUND
FILLET 7

3 · CORNICE


SECTION

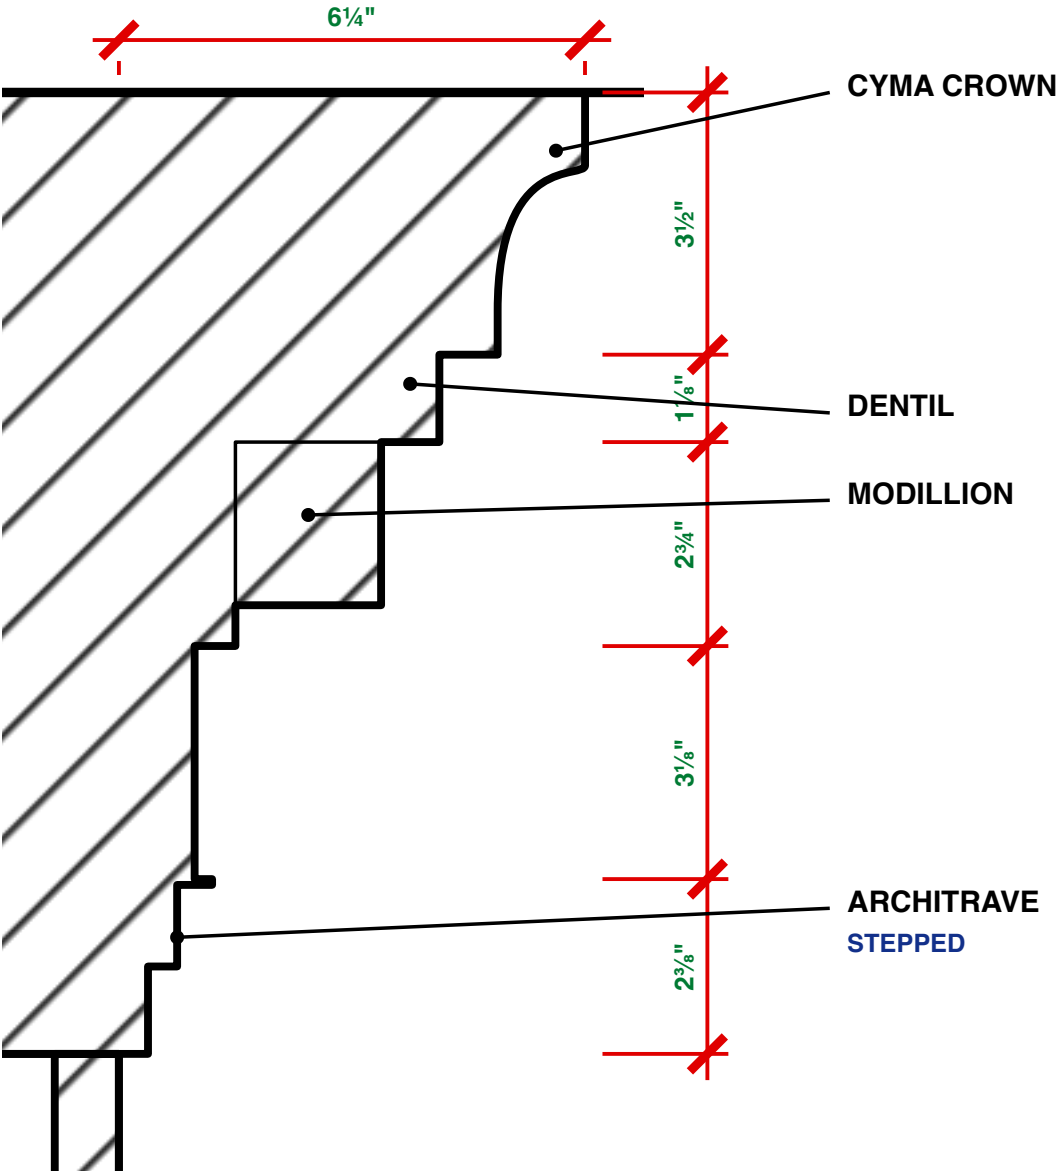

4 · MODILLION + DENTILS

FRONT · PLAIN


DENTILS 0⁵/₈" × 1¹/₄"
0¹/₂" GAP

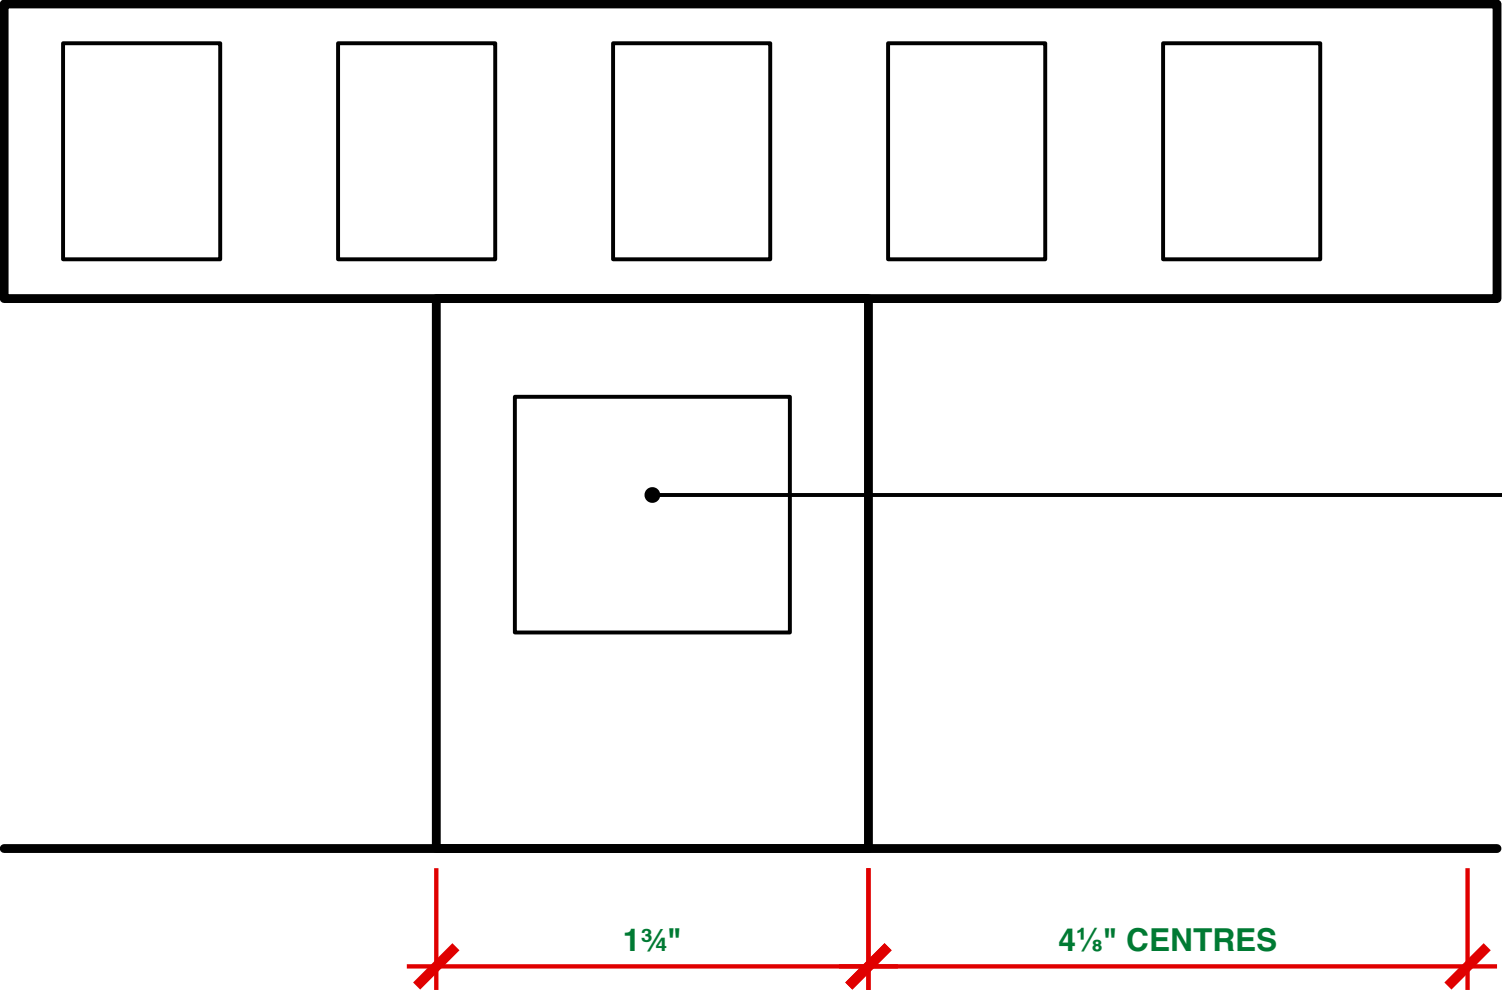

PLAIN BLOCK, SUNK PANEL
NO CARVING


5 · PAINTING PANEL

BOLECTION MOULDING · SECTION

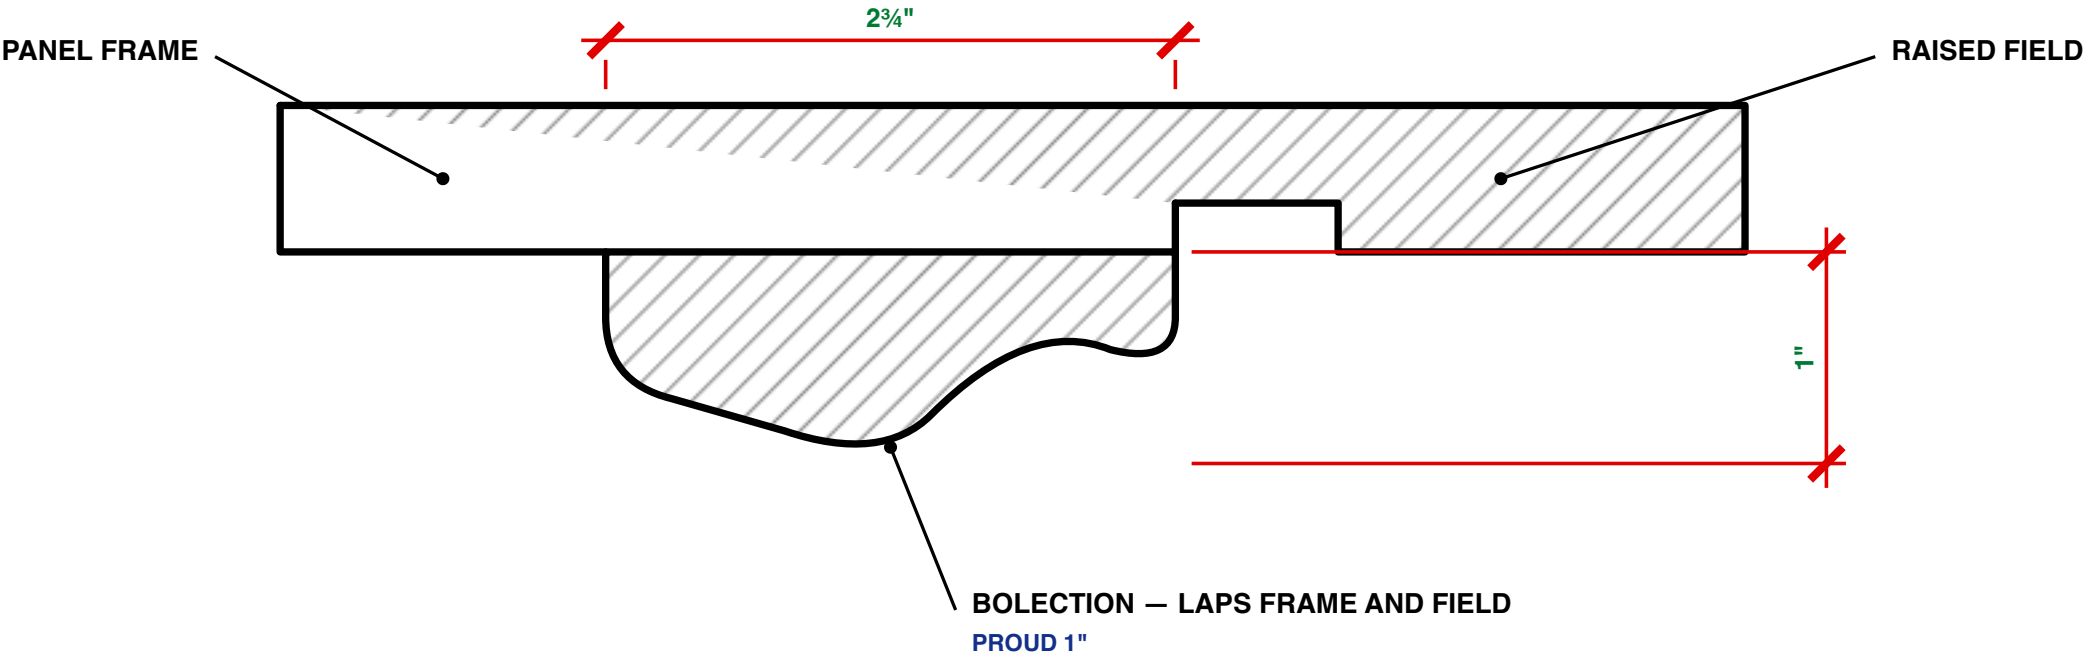


6 · BAND PANEL + SCONCE

ELEVATION · SAME PANEL OVER EVERY BAY

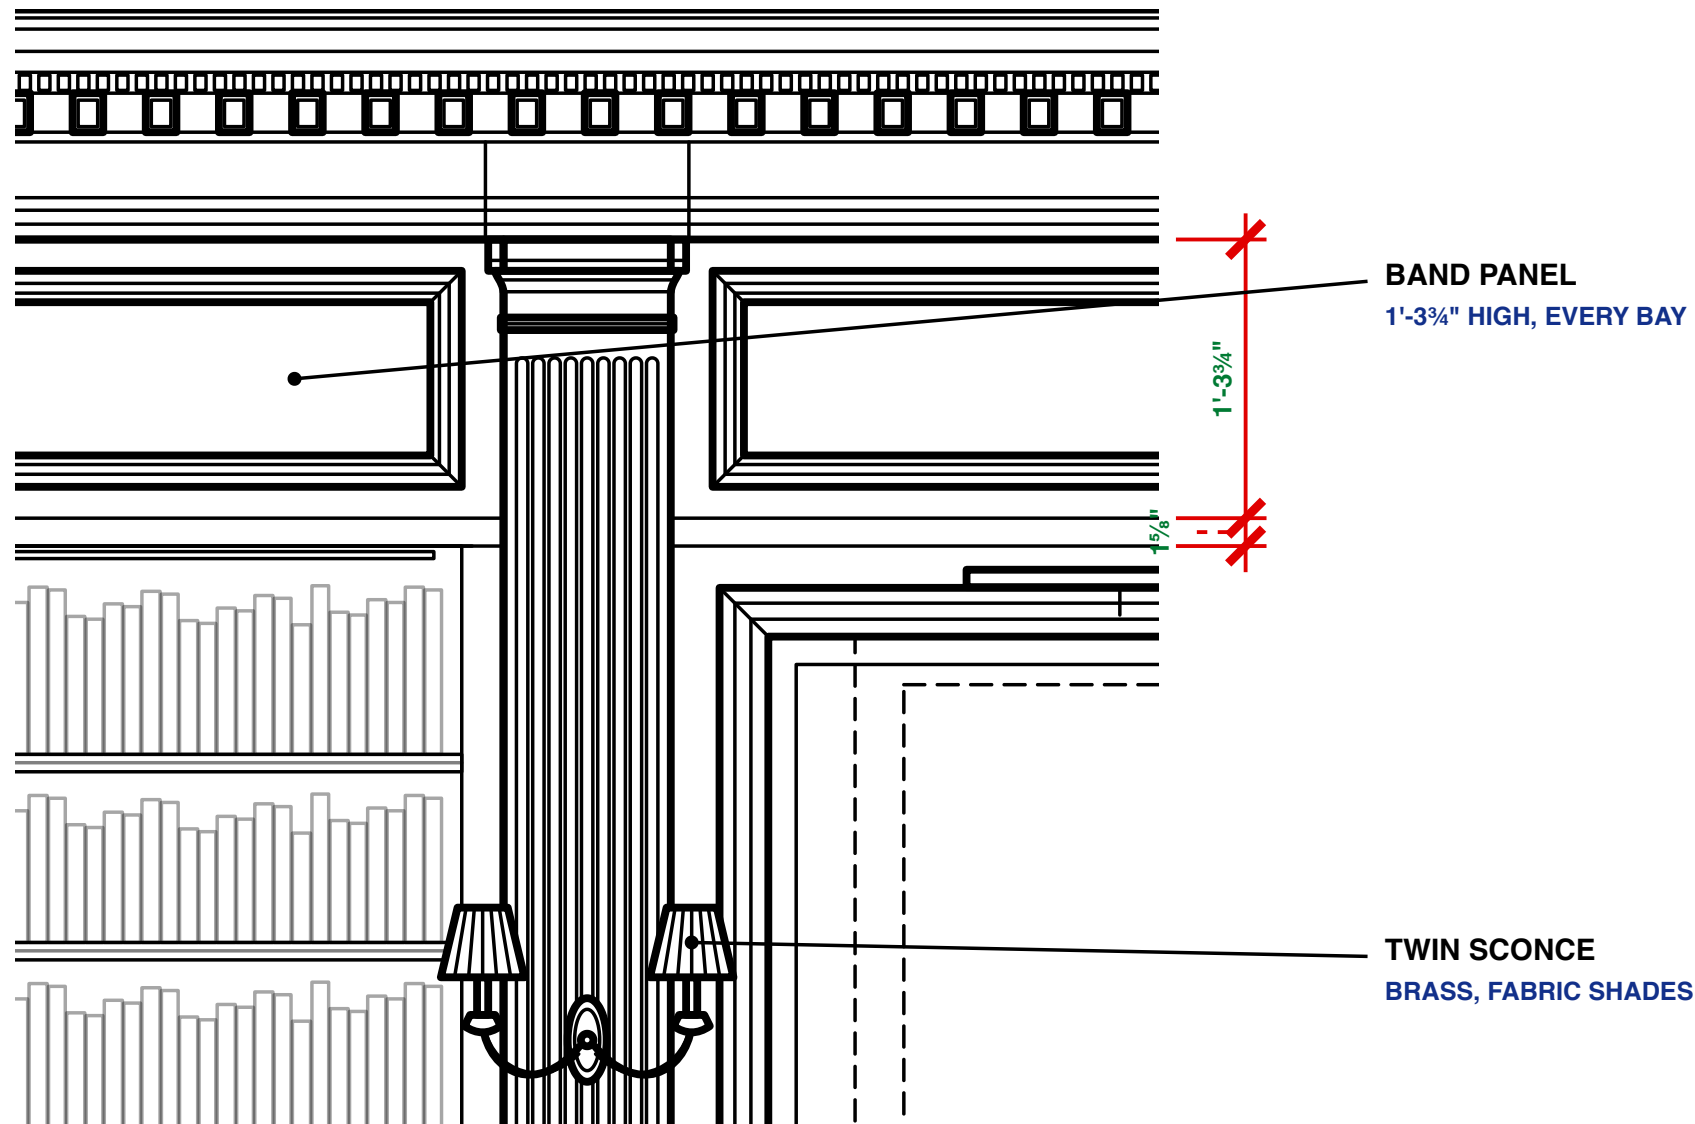

7 · COUNTER EDGE

SECTION · SAME REEDS AS THE DESK

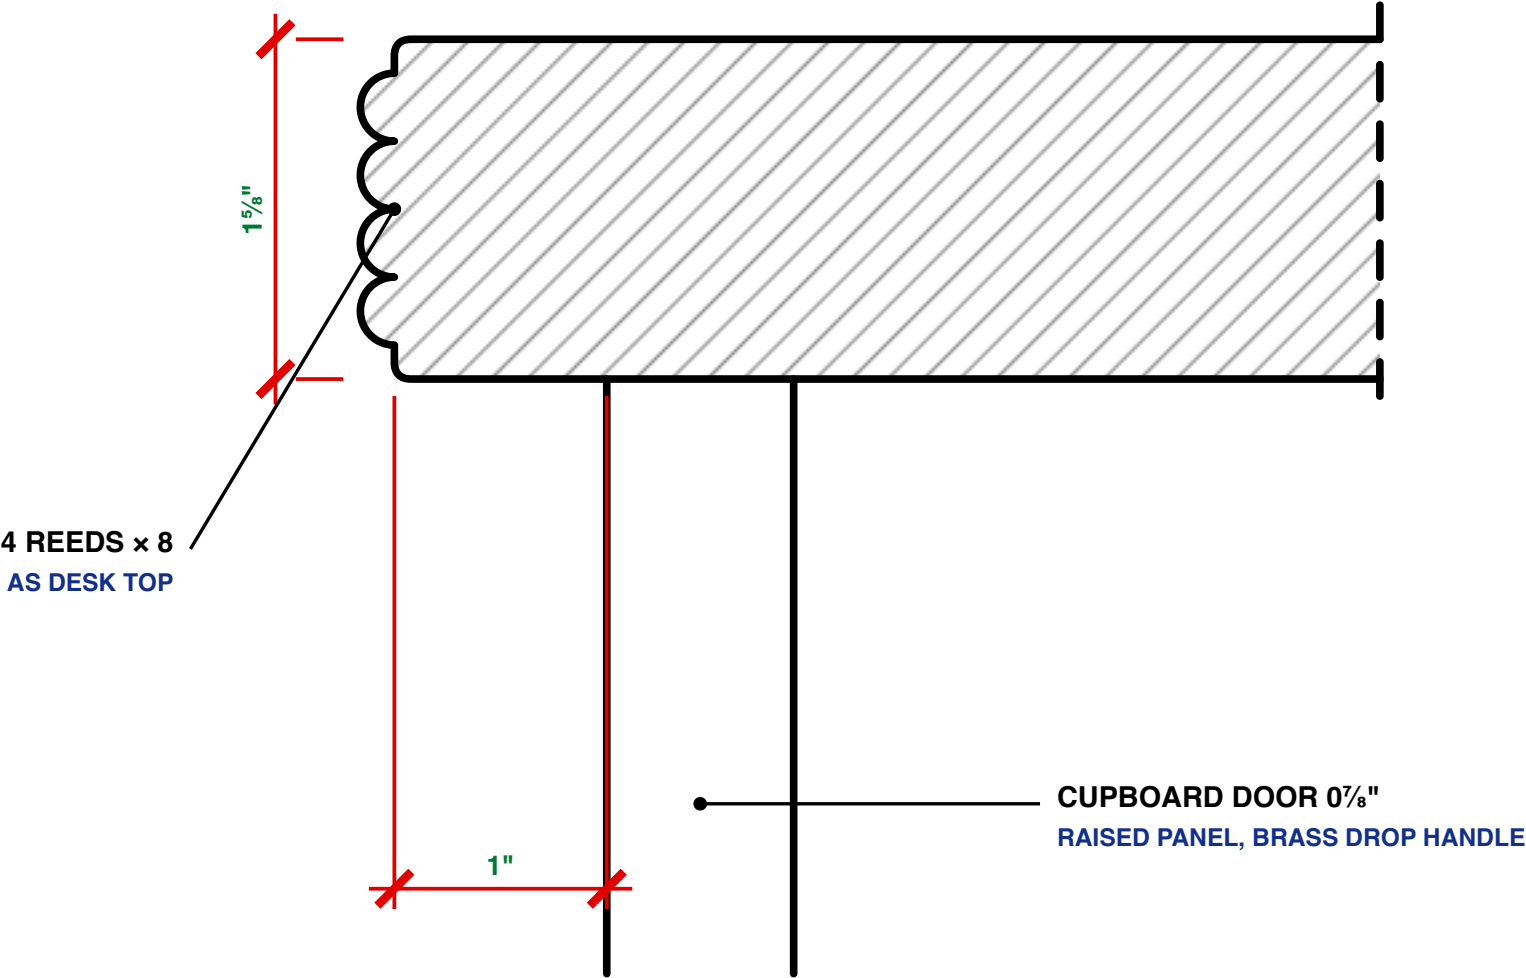

NOTES

DETAILS

No carving on pilasters or modillions — mouldings only.

Flute and modillion spacing to be set out on site

so they finish symmetrically on the wall.

Mock up profiles 3, 5 and 7 full size before cutting.